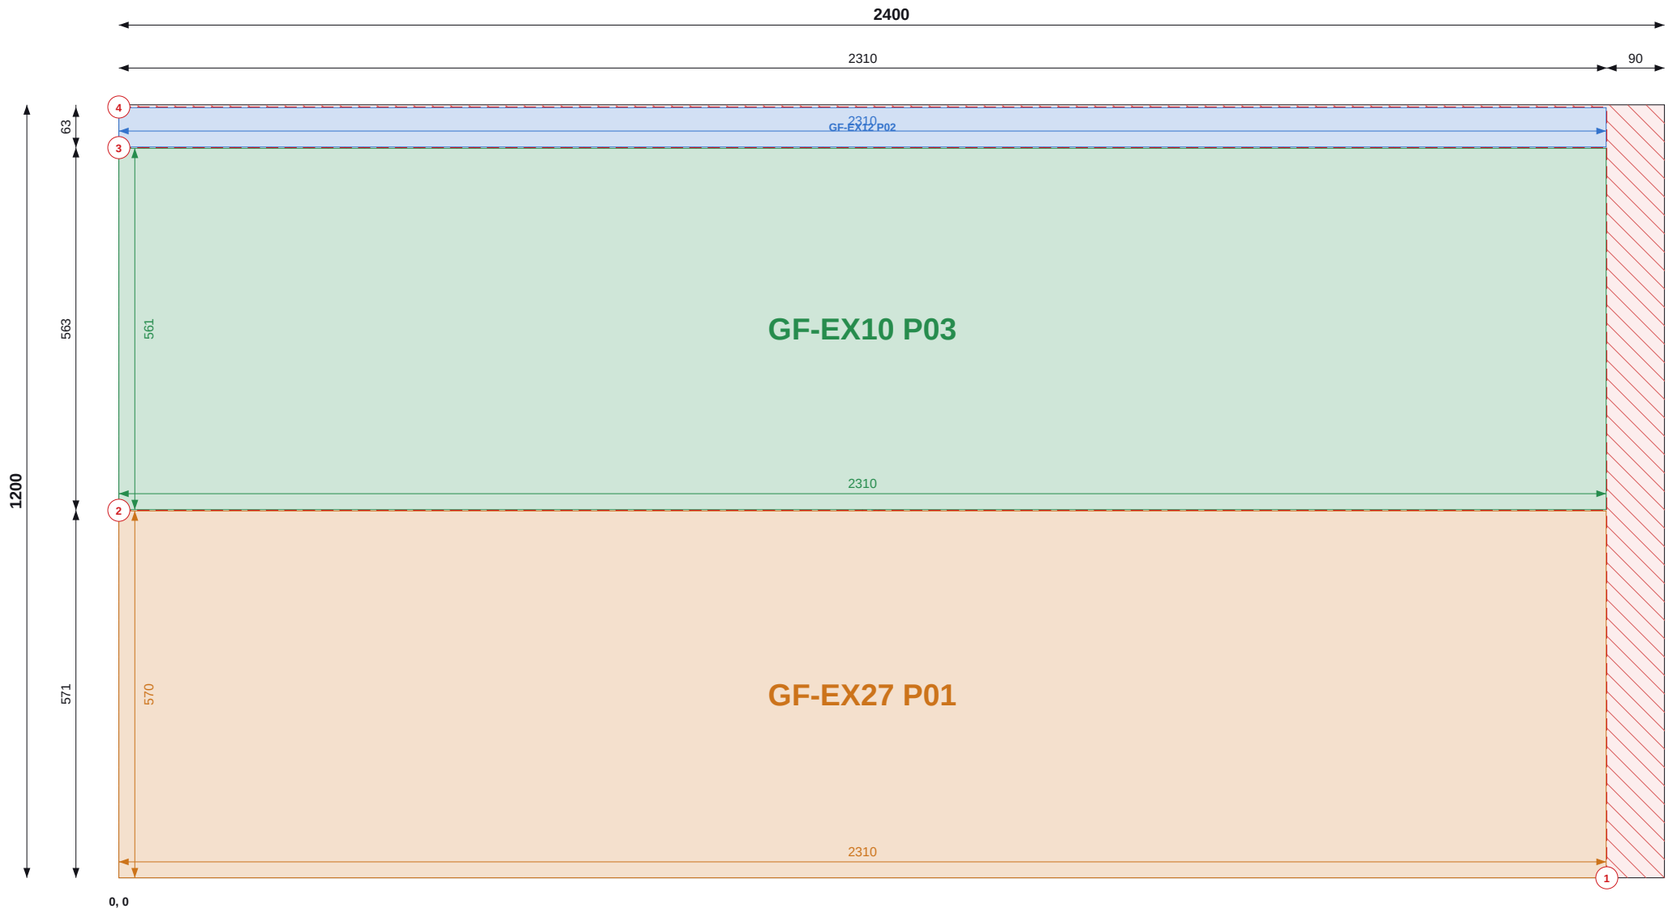


Top / left chains = saw cut positions (to cut centres). Coloured = part size and position.

SHEET 1 OF 33

THIS SHEET

Item	Value
Parts	3
Used / waste	95.6% / 0.13 m2
Reusable offcuts	0
Saw cuts / shared	4 / 2

PIECES (POSITION = BOTTOM-LEFT CORNER)

Label	Size	X, Y
GF-EX12 P02	61 x 2310	0, 1135
GF-EX10 P03	561 x 2310	0, 572
GF-EX27 P01	570 x 2310	0, 0

GROUND FLOOR TOTALS

Item	Value
Sheets / pieces	33 / 224
Yield / waste	92.8% / 6.83 m2
Saw cuts / shared / on stock edge	277 / 191 / 192

NOTES

1. Cut from PIR 120mm 1200x2400, 2mm saw kerf. Viewed on the face; dimensions from the sheet's bottom-left corner (0,0). Red numbered lines = saw cuts in order, each edge to edge.
2. Coloured dimensions belong to the part of that colour: its width and height, and its position from the sheet edges. Raked parts: corner coordinates at each corner.
3. Red hatch = waste. Labels = panel + piece mark on the manufacture drawing.

REVISIONS

REV	DATE	DESCRIPTION
C01	14.09.26	Construction issue
C02	14.09.26	Roof trusses revised; SP diagonals added

TLS TIMBER FRAME
Design & Manufacture
Scan: 3D model + drawings

CLIENT	PROJECT
MP Adams	MP Adams Plot 4, Eckington

DRAWING TITLE


PIR CUTTING - GROUND FLOOR - SHEET 1 OF 33

PIR 120mm 1200x2400 | Ground Floor

SCALE	SIZE	DATE	DRAWN
NTS	A3	14.09.26	TS

STATUS	DRAWING No.	REV
CONSTRUCTION	P4-CP-PIR-01 / 01	C02

Do not scale. All dimensions in mm. Check all dimensions on site.

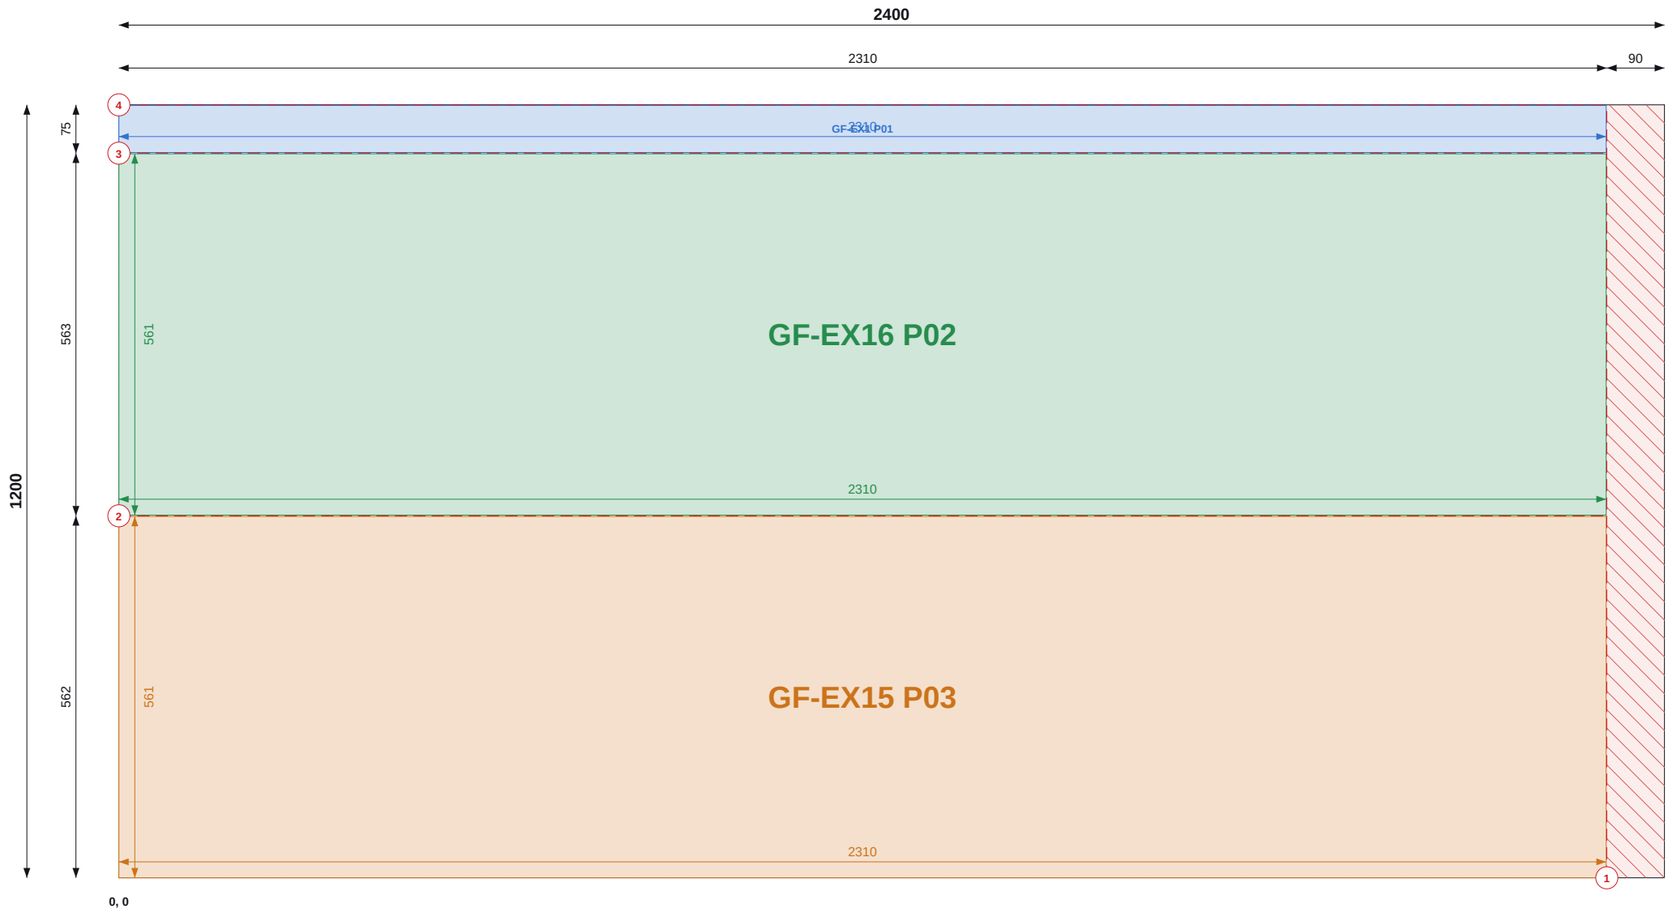

Top / left chains = saw cut positions (to cut centres). Coloured = part size and position.

SHEET 2 OF 33

THIS SHEET

Item	Value
Parts	3
Used / waste	95.8% / 0.12 m2
Reusable offcuts	0
Saw cuts / shared	4 / 2

PIECES (POSITION = BOTTOM-LEFT CORNER)

Label	Size	X, Y
GF-EX1 P01	73 x 2310	0, 1126
GF-EX16 P02	561 x 2310	0, 563
GF-EX15 P03	561 x 2310	0, 0

NOTES

1. Cut from PIR 120mm 1200x2400, 2mm saw kerf. Viewed on the face; dimensions from the sheet's bottom-left corner (0,0). Red numbered lines = saw cuts in order, each edge to edge.
2. Coloured dimensions belong to the part of that colour: its width and height, and its position from the sheet edges. Raked parts: corner coordinates at each corner.
3. Red hatch = waste. Labels = panel + piece mark on the manufacture drawing.

REVISIONS

REV	DATE	DESCRIPTION
C01	14.09.26	Construction issue
C02	14.09.26	Roof trusses revised; SP diagonals added

TLS TIMBER FRAME DESIGN SUITE

TLS TIMBER FRAME

Design & Manufacture

Scan: 3D model + drawings

CLIENT	PROJECT
MP Adams	MP Adams Plot 4, Eckington

DRAWING TITLE


PIR CUTTING - GROUND FLOOR - SHEET 2 OF 33

PIR 120mm 1200x2400 | Ground Floor

SCALE	SIZE	DATE	DRAWN
NTS	A3	14.09.26	TS

STATUS	DRAWING No.	REV
CONSTRUCTION	P4-CP-PIR-01 / 02	C02

Do not scale. All dimensions in mm. Check all dimensions on site.

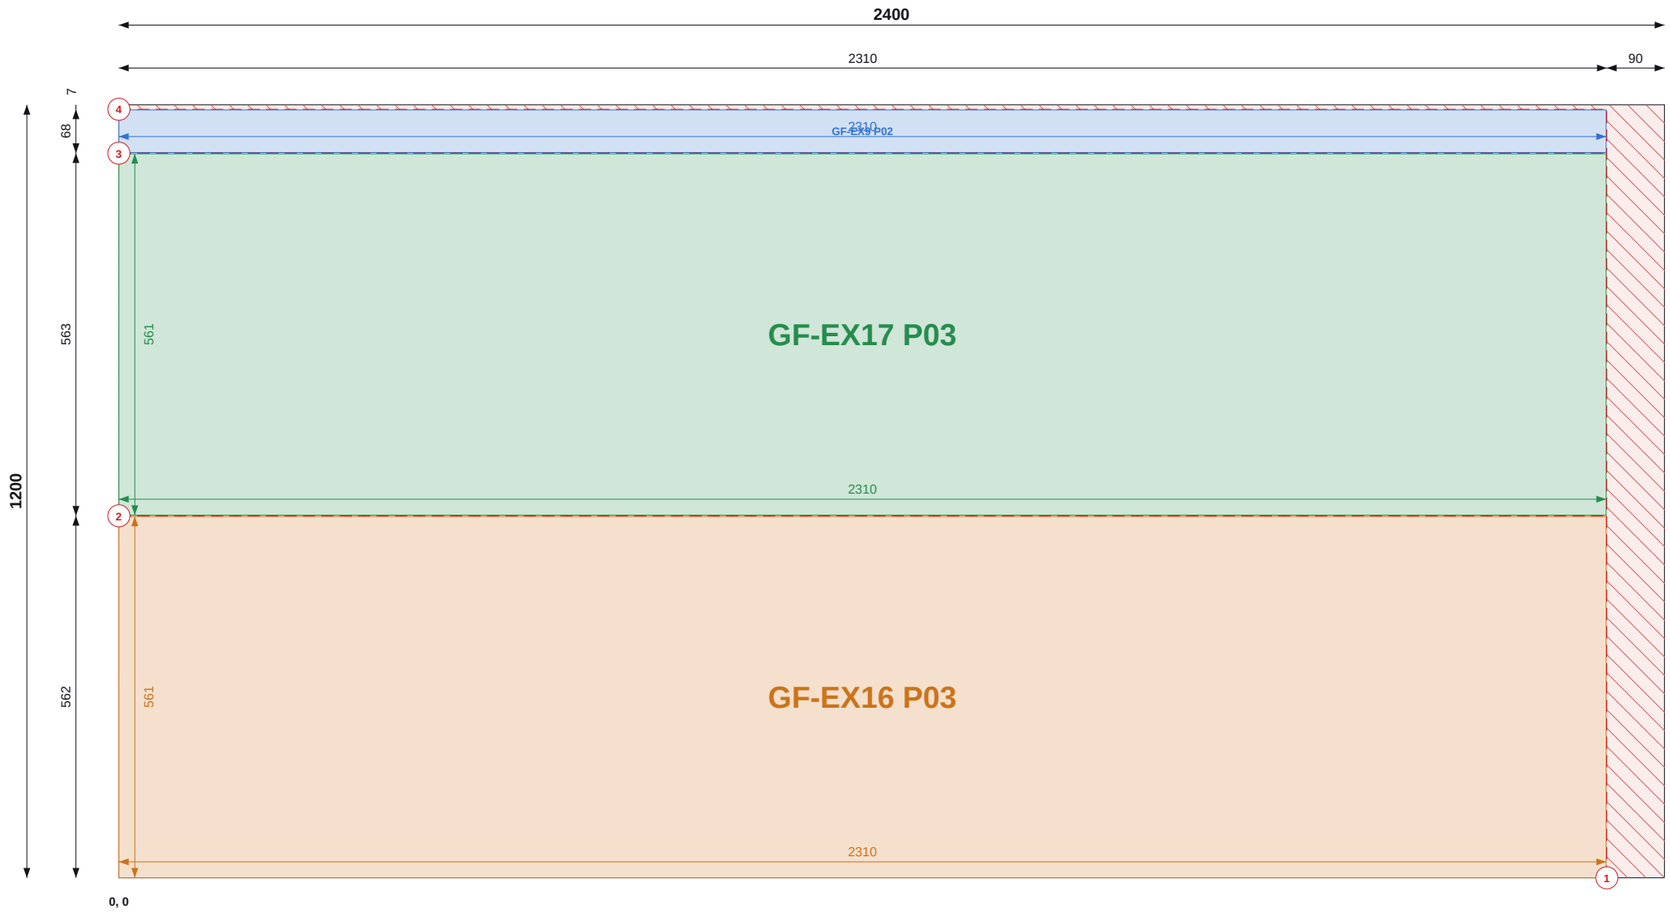

Top / left chains = saw cut positions (to cut centres). Coloured = part size and position.

SHEET 3 OF 33

THIS SHEET

Item	Value
Parts	3
Used / waste	95.3% / 0.14 m2
Reusable offcuts	0
Saw cuts / shared	4 / 2

PIECES (POSITION = BOTTOM-LEFT CORNER)

Label	Size	X, Y
GF-EX9 P02	66 x 2310	0, 1126
GF-EX17 P03	561 x 2310	0, 563
GF-EX16 P03	561 x 2310	0, 0

NOTES

1. Cut from PIR 120mm 1200x2400, 2mm saw kerf. Viewed on the face; dimensions from the sheet's bottom-left corner (0,0). Red numbered lines = saw cuts in order, each edge to edge.
2. Coloured dimensions belong to the part of that colour: its width and height, and its position from the sheet edges. Raked parts: corner coordinates at each corner.
3. Red hatch = waste. Labels = panel + piece mark on the manufacture drawing.

REVISIONS

REV	DATE	DESCRIPTION
C01	14.09.26	Construction issue
C02	14.09.26	Roof trusses revised; SP diagonals added

TLS TIMBER FRAME DESIGN SUITE

TLS TIMBER FRAME

Design & Manufacture

Scan: 3D model + drawings

CLIENT	PROJECT
MP Adams	MP Adams Plot 4, Eckington

DRAWING TITLE


PIR CUTTING - GROUND FLOOR - SHEET 3 OF 33

PIR 120mm 1200x2400 | Ground Floor

SCALE	SIZE	DATE	DRAWN
NTS	A3	14.09.26	TS

STATUS	DRAWING No.	REV
CONSTRUCTION	P4-CP-PIR-01 / 03	C02

Do not scale. All dimensions in mm. Check all dimensions on site.

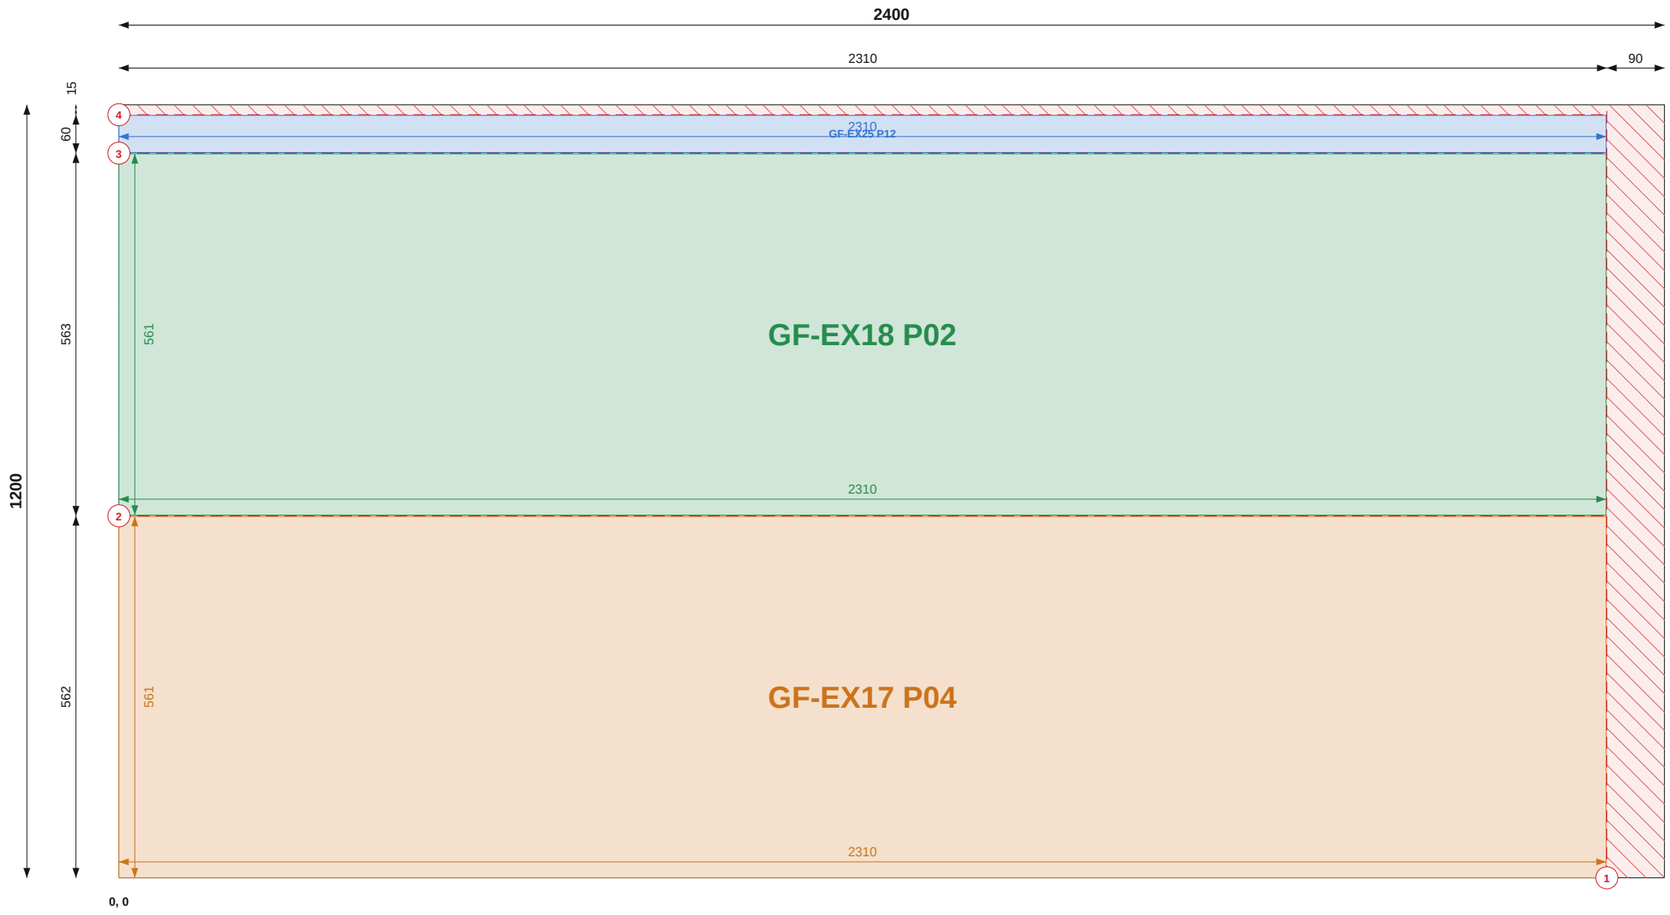

Top / left chains = saw cut positions (to cut centres). Coloured = part size and position.

SHEET 4 OF 33

THIS SHEET

Item	Value
Parts	3
Used / waste	94.6% / 0.16 m2
Reusable offcuts	0
Saw cuts / shared	4 / 2

PIECES (POSITION = BOTTOM-LEFT CORNER)

Label	Size	X, Y
GF-EX25 P12	58 x 2310	0, 1126
GF-EX18 P02	561 x 2310	0, 563
GF-EX17 P04	561 x 2310	0, 0

NOTES

1. Cut from PIR 120mm 1200x2400, 2mm saw kerf. Viewed on the face; dimensions from the sheet's bottom-left corner (0,0). Red numbered lines = saw cuts in order, each edge to edge.
2. Coloured dimensions belong to the part of that colour: its width and height, and its position from the sheet edges. Raked parts: corner coordinates at each corner.
3. Red hatch = waste. Labels = panel + piece mark on the manufacture drawing.

REVISIONS

REV	DATE	DESCRIPTION
C01	14.09.26	Construction issue
C02	14.09.26	Roof trusses revised; SP diagonals added

TLS TIMBER FRAME
Design & Manufacture
Scan: 3D model + drawings


CLIENT	PROJECT
MP Adams	MP Adams Plot 4, Eckington

DRAWING TITLE
PIR CUTTING - GROUND FLOOR - SHEET 4 OF 33
PIR 120mm 1200x2400 | Ground Floor

SCALE	SIZE	DATE	DRAWN
NTS	A3	14.09.26	TS

STATUS	DRAWING No.	REV
CONSTRUCTION	P4-CP-PIR-01 / 04	C02

Do not scale. All dimensions in mm. Check all dimensions on site.

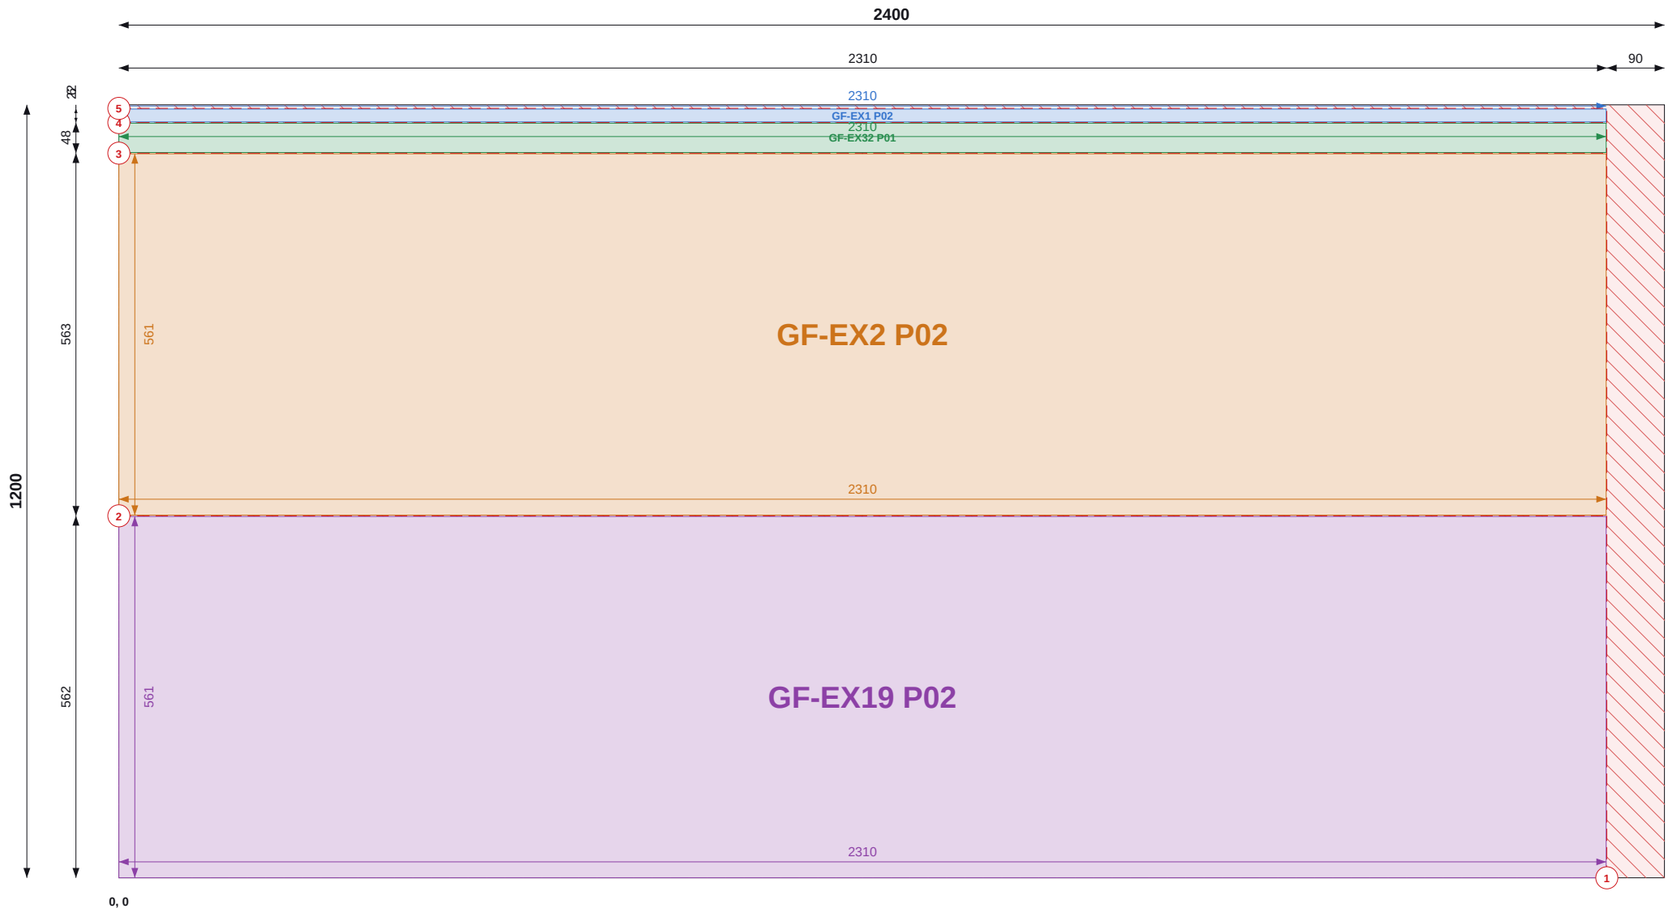

Top / left chains = saw cut positions (to cut centres). Coloured = part size and position.

SHEET 5 OF 33

THIS SHEET

Item	Value
Parts	4
Used / waste	95.2% / 0.14 m2
Reusable offcuts	0
Saw cuts / shared	5 / 3

PIECES (POSITION = BOTTOM-LEFT CORNER)

Label	Size	X, Y
GF-EX1 P02	20 x 2310	0, 1174
GF-EX32 P01	46 x 2310	0, 1126
GF-EX2 P02	561 x 2310	0, 563
GF-EX19 P02	561 x 2310	0, 0

NOTES

1. Cut from PIR 120mm 1200x2400, 2mm saw kerf. Viewed on the face; dimensions from the sheet's bottom-left corner (0,0). Red numbered lines = saw cuts in order, each edge to edge.
2. Coloured dimensions belong to the part of that colour: its width and height, and its position from the sheet edges. Raked parts: corner coordinates at each corner.
3. Red hatch = waste. Labels = panel + piece mark on the manufacture drawing.

REVISIONS

REV	DATE	DESCRIPTION
C01	14.09.26	Construction issue
C02	14.09.26	Roof trusses revised; SP diagonals added

TLS TIMBER FRAME
Design & Manufacture
Scan: 3D model + drawings

CLIENT	PROJECT
MP Adams	MP Adams Plot 4, Eckington

DRAWING TITLE


PIR CUTTING - GROUND FLOOR - SHEET 5 OF 33

PIR 120mm 1200x2400 | Ground Floor

SCALE	SIZE	DATE	DRAWN
NTS	A3	14.09.26	TS

STATUS	DRAWING No.	REV
CONSTRUCTION	P4-CP-PIR-01 / 05	C02

Do not scale. All dimensions in mm. Check all dimensions on site.

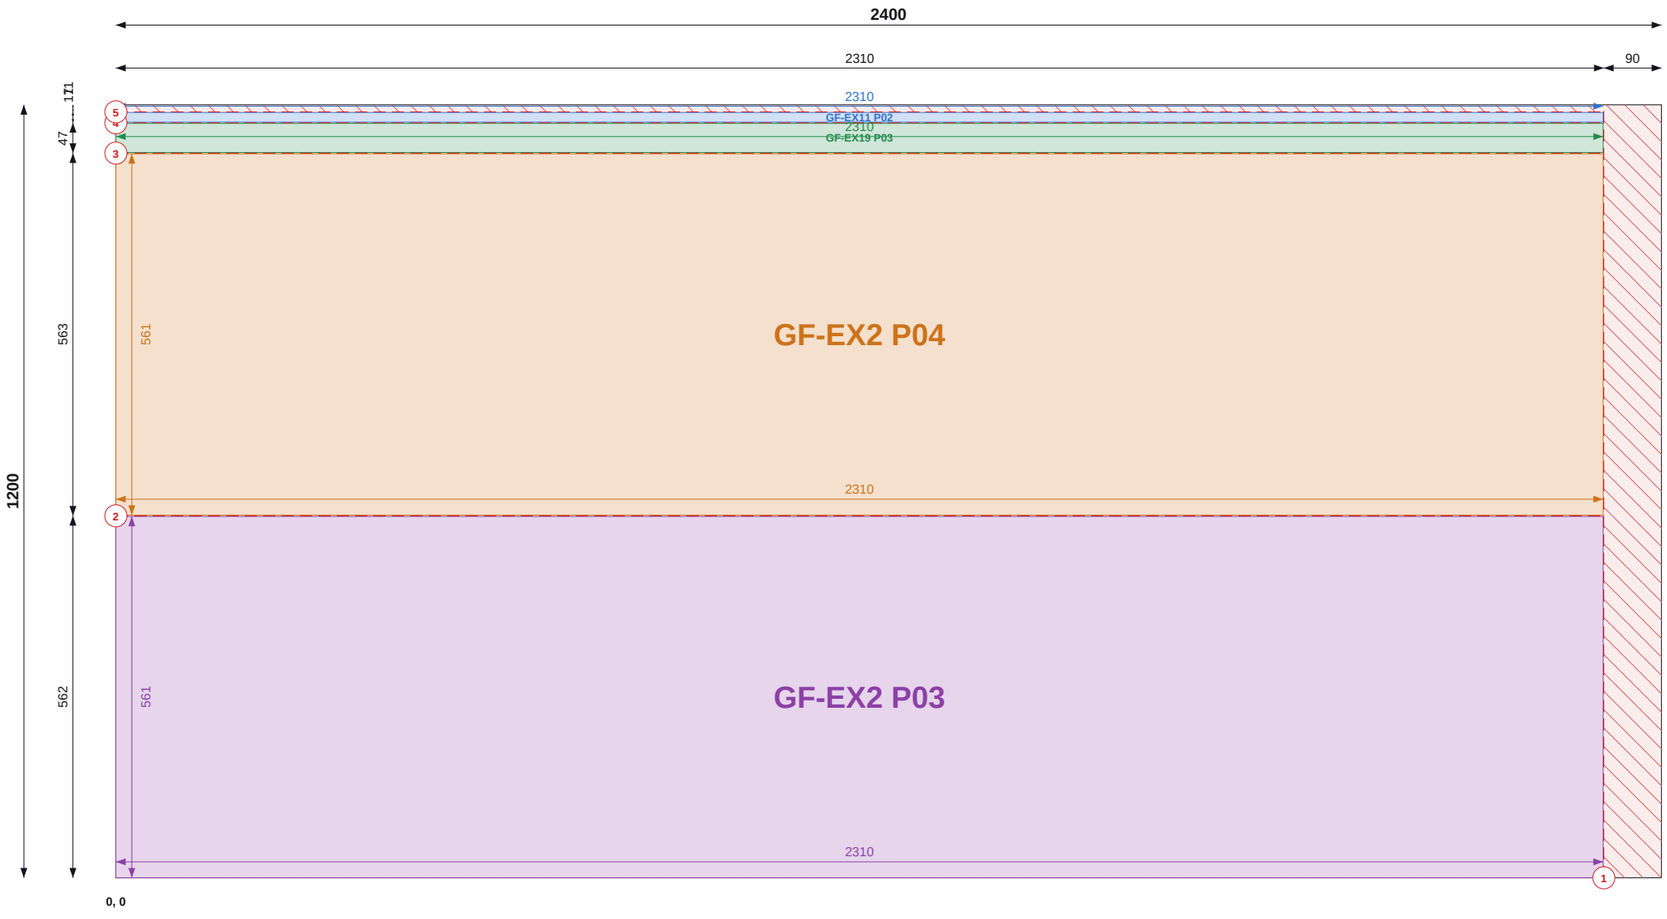

Top / left chains = saw cut positions (to cut centres). Coloured = part size and position.

SHEET 6 OF 33

THIS SHEET

Item	Value
Parts	4
Used / waste	94.8% / 0.15 m2
Reusable offcuts	0
Saw cuts / shared	5 / 3

PIECES (POSITION = BOTTOM-LEFT CORNER)

Label	Size	X, Y
GF-EX11 P02	15 x 2310	0, 1173
GF-EX19 P03	45 x 2310	0, 1126
GF-EX2 P04	561 x 2310	0, 563
GF-EX2 P03	561 x 2310	0, 0

NOTES

1. Cut from PIR 120mm 1200x2400, 2mm saw kerf. Viewed on the face; dimensions from the sheet's bottom-left corner (0,0). Red numbered lines = saw cuts in order, each edge to edge.
2. Coloured dimensions belong to the part of that colour: its width and height, and its position from the sheet edges. Raked parts: corner coordinates at each corner.
3. Red hatch = waste. Labels = panel + piece mark on the manufacture drawing.

REVISIONS

REV	DATE	DESCRIPTION
C01	14.09.26	Construction issue
C02	14.09.26	Roof trusses revised; SP diagonals added

TLS TIMBER FRAME
Design & Manufacture
Scan: 3D model + drawings

CLIENT	PROJECT
MP Adams	MP Adams Plot 4, Eckington

DRAWING TITLE


PIR CUTTING - GROUND FLOOR - SHEET 6 OF 33

PIR 120mm 1200x2400 | Ground Floor

SCALE	SIZE	DATE	DRAWN
NTS	A3	14.09.26	TS

STATUS	DRAWING No.	REV
CONSTRUCTION	P4-CP-PIR-01 / 06	C02

Do not scale. All dimensions in mm. Check all dimensions on site.

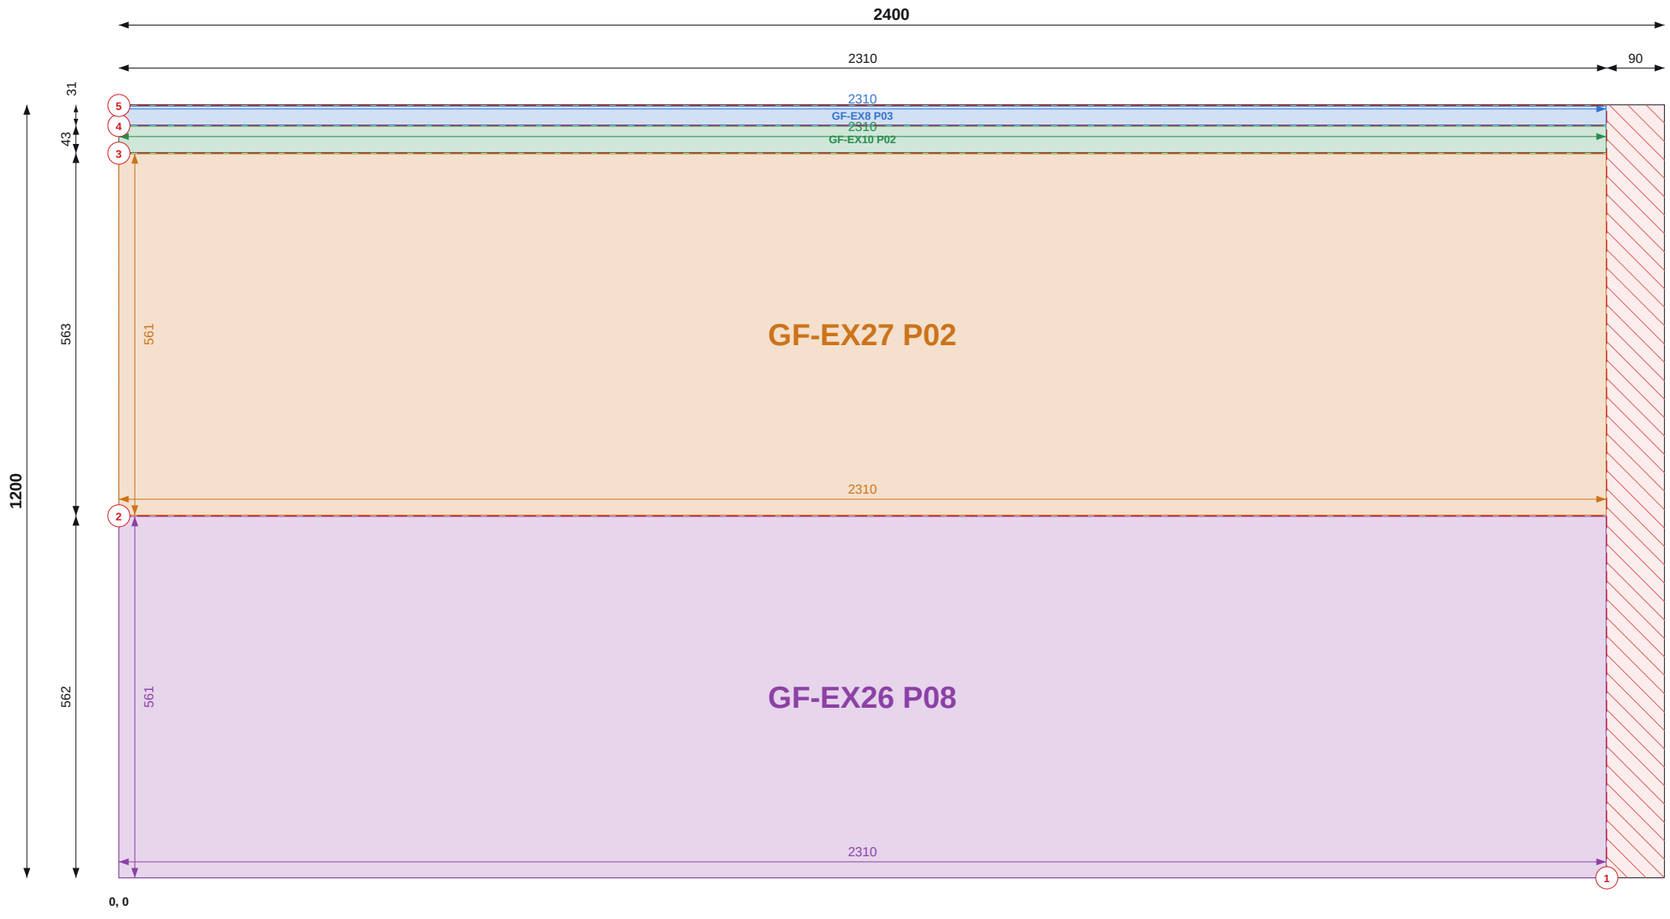

Top / left chains = saw cut positions (to cut centres). Coloured = part size and position.

SHEET 7 OF 33

THIS SHEET

Item	Value
Parts	4
Used / waste	95.6% / 0.13 m2
Reusable offcuts	0
Saw cuts / shared	5 / 3

PIECES (POSITION = BOTTOM-LEFT CORNER)

Label	Size	X, Y
GF-EX8 P03	29 x 2310	0, 1169
GF-EX10 P02	41 x 2310	0, 1126
GF-EX27 P02	561 x 2310	0, 563
GF-EX26 P08	561 x 2310	0, 0

NOTES

1. Cut from PIR 120mm 1200x2400, 2mm saw kerf. Viewed on the face; dimensions from the sheet's bottom-left corner (0,0). Red numbered lines = saw cuts in order, each edge to edge.
2. Coloured dimensions belong to the part of that colour: its width and height, and its position from the sheet edges. Raked parts: corner coordinates at each corner.
3. Red hatch = waste. Labels = panel + piece mark on the manufacture drawing.

REVISIONS

REV	DATE	DESCRIPTION
C01	14.09.26	Construction issue
C02	14.09.26	Roof trusses revised; SP diagonals added

TLS TIMBER FRAME
Design & Manufacture
Scan: 3D model + drawings

CLIENT	PROJECT
MP Adams	MP Adams Plot 4, Eckington

DRAWING TITLE


PIR CUTTING - GROUND FLOOR - SHEET 7 OF 33

PIR 120mm 1200x2400 | Ground Floor

SCALE	SIZE	DATE	DRAWN
NTS	A3	14.09.26	TS

STATUS	DRAWING No.	REV
CONSTRUCTION	P4-CP-PIR-01 / 07	C02

Do not scale. All dimensions in mm. Check all dimensions on site.

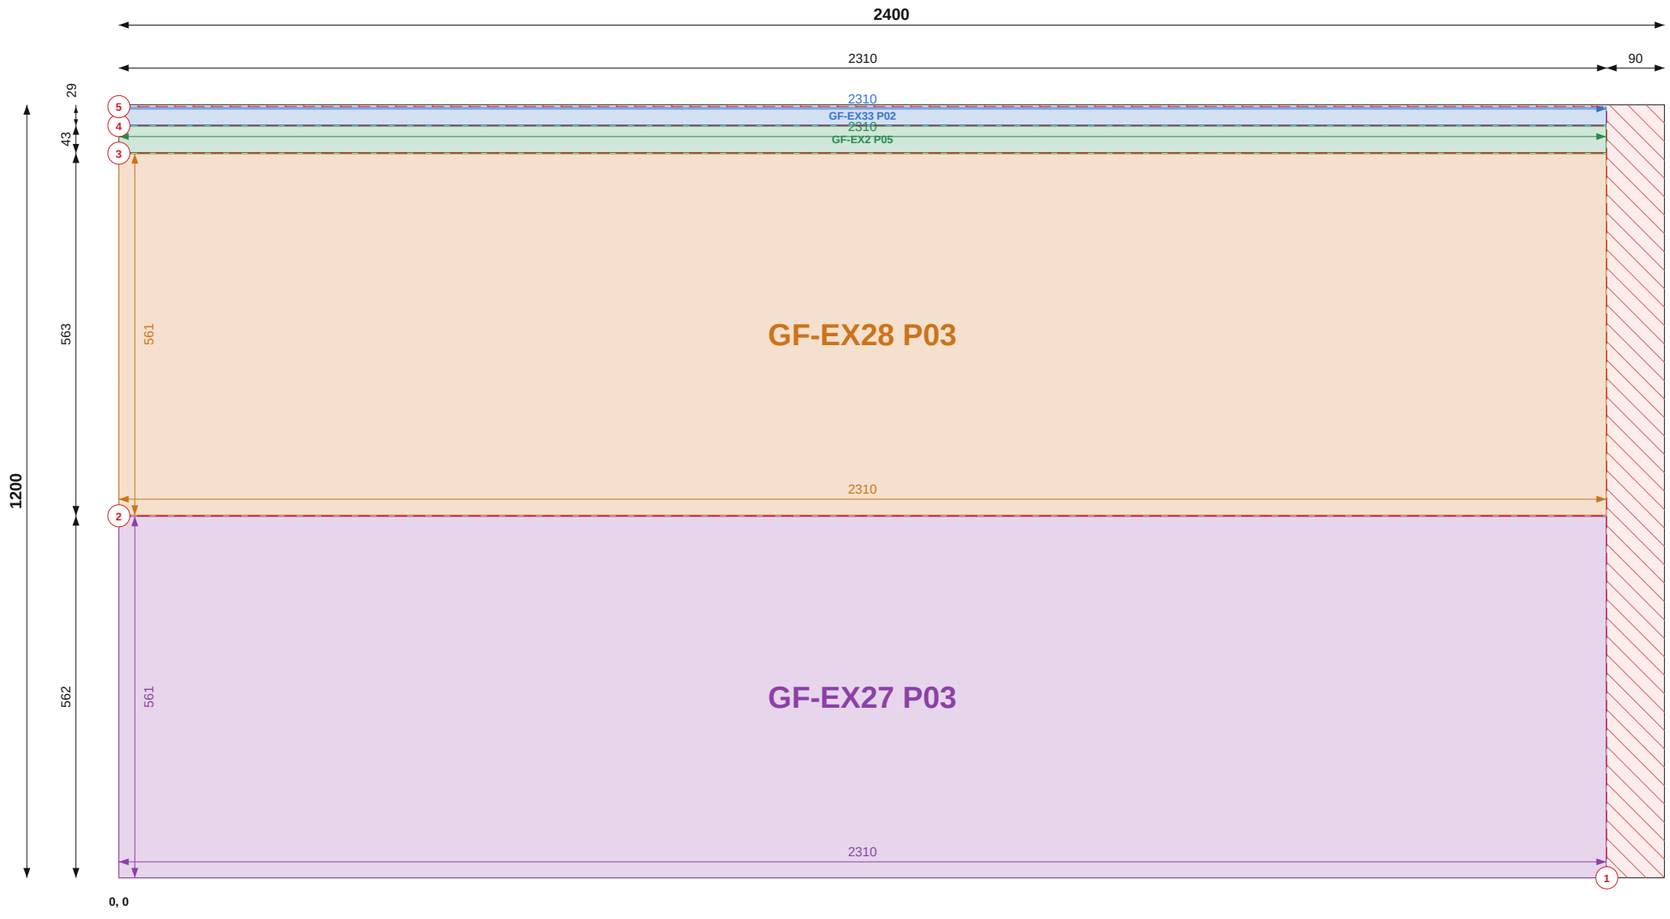

Top / left chains = saw cut positions (to cut centres). Coloured = part size and position.

SHEET 8 OF 33

THIS SHEET

Item	Value
Parts	4
Used / waste	95.4% / 0.13 m2
Reusable offcuts	0
Saw cuts / shared	5 / 3

PIECES (POSITION = BOTTOM-LEFT CORNER)

Label	Size	X, Y
GF-EX33 P02	27 x 2310	0, 1169
GF-EX2 P05	41 x 2310	0, 1126
GF-EX28 P03	561 x 2310	0, 563
GF-EX27 P03	561 x 2310	0, 0

NOTES

1. Cut from PIR 120mm 1200x2400, 2mm saw kerf. Viewed on the face; dimensions from the sheet's bottom-left corner (0,0). Red numbered lines = saw cuts in order, each edge to edge.
2. Coloured dimensions belong to the part of that colour: its width and height, and its position from the sheet edges. Raked parts: corner coordinates at each corner.
3. Red hatch = waste. Labels = panel + piece mark on the manufacture drawing.

REVISIONS

REV	DATE	DESCRIPTION
C01	14.09.26	Construction issue
C02	14.09.26	Roof trusses revised; SP diagonals added

TLS TIMBER FRAME
Design & Manufacture
Scan: 3D model + drawings

CLIENT	PROJECT
MP Adams	MP Adams Plot 4, Eckington

DRAWING TITLE


PIR CUTTING - GROUND FLOOR - SHEET 8 OF 33

PIR 120mm 1200x2400 | Ground Floor

SCALE	SIZE	DATE	DRAWN
NTS	A3	14.09.26	TS

STATUS	DRAWING No.	REV
CONSTRUCTION	P4-CP-PIR-01 / 08	C02

Do not scale. All dimensions in mm. Check all dimensions on site.

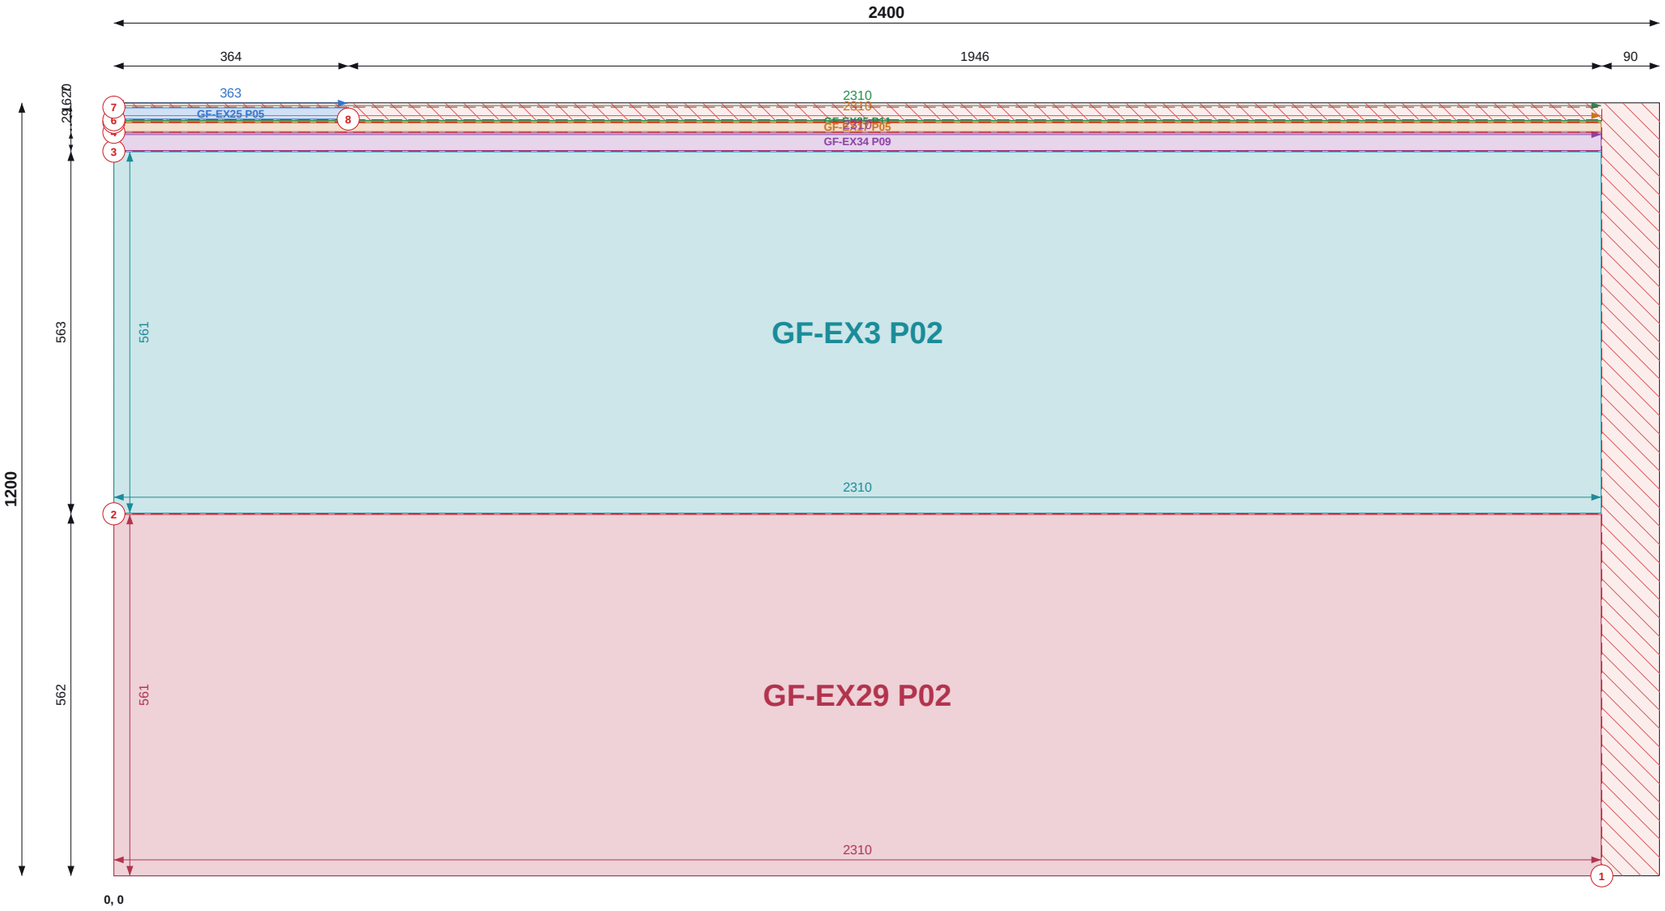

Top / left chains = saw cut positions (to cut centres). Coloured = part size and position.

Do not scale. All dimensions in mm. Check all dimensions on site.

SHEET 9 OF 33

THIS SHEET

Item	Value
Parts	6
Used / waste	93.6% / 0.18 m2
Reusable offcuts	0
Saw cuts / shared	8 / 5

PIECES (POSITION = BOTTOM-LEFT CORNER)

Label	Size	X, Y
GF-EX25 P05	363 x 18	0, 1175
GF-EX25 P11	2 x 2310	0, 1171
GF-EX17 P05	14 x 2310	0, 1155
GF-EX34 P09	27 x 2310	0, 1126
GF-EX3 P02	561 x 2310	0, 563
GF-EX29 P02	561 x 2310	0, 0

NOTES

1. Cut from PIR 120mm 1200x2400, 2mm saw kerf. Viewed on the face; dimensions from the sheet's bottom-left corner (0,0). Red numbered lines = saw cuts in order, each edge to edge.
2. Coloured dimensions belong to the part of that colour: its width and height, and its position from the sheet edges. Raked parts: corner coordinates at each corner.
3. Red hatch = waste. Labels = panel + piece mark on the manufacture drawing.

REVISIONS

REV	DATE	DESCRIPTION
C01	14.09.26	Construction issue
C02	14.09.26	Roof trusses revised; SP diagonals added

TLS TIMBER FRAME
Design & Manufacture
Scan: 3D model + drawings

CLIENT	PROJECT
MP Adams	MP Adams Plot 4, Eckington


DRAWING TITLE

PIR CUTTING - GROUND FLOOR - SHEET 9 OF 33

PIR 120mm 1200x2400 | Ground Floor

SCALE	SIZE	DATE	DRAWN
NTS	A3	14.09.26	TS

STATUS	DRAWING No.	REV
CONSTRUCTION	P4-CP-PIR-01 / 09	C02

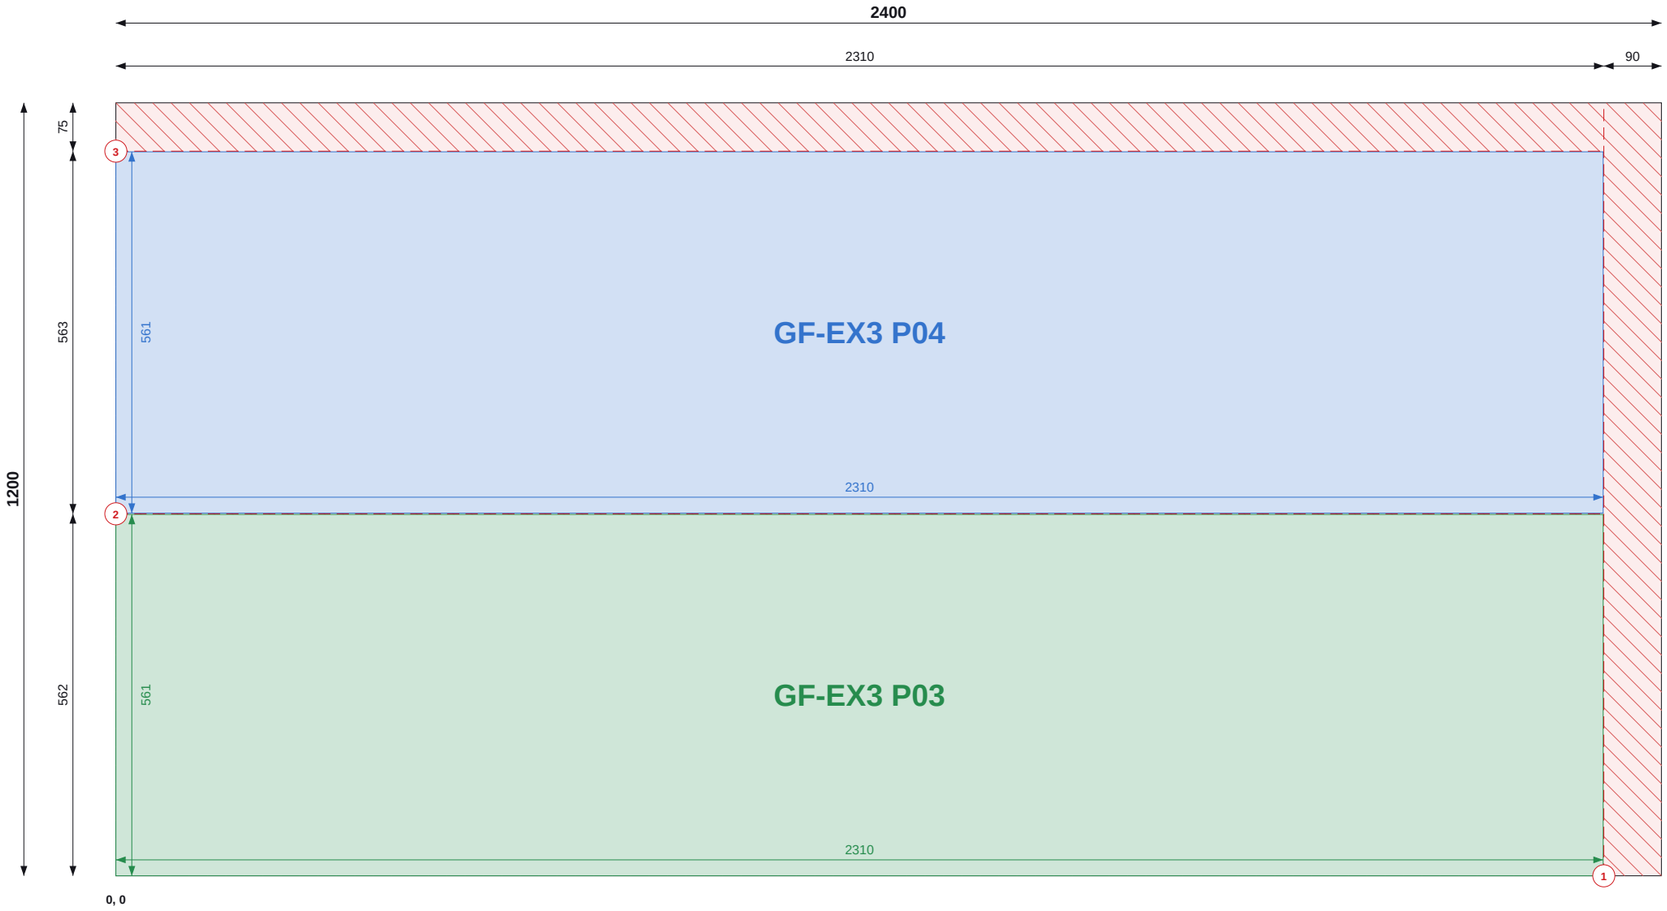

Top / left chains = saw cut positions (to cut centres). Coloured = part size and position.

Do not scale. All dimensions in mm. Check all dimensions on site.

SHEET 10 OF 33

THIS SHEET

Item	Value
Parts	2
Used / waste	90.0% / 0.29 m2
Reusable offcuts	0
Saw cuts / shared	3 / 1

PIECES (POSITION = BOTTOM-LEFT CORNER)

Label	Size	X, Y
GF-EX3 P04	561 x 2310	0, 563
GF-EX3 P03	561 x 2310	0, 0

NOTES

1. Cut from PIR 120mm 1200x2400, 2mm saw kerf. Viewed on the face; dimensions from the sheet's bottom-left corner (0,0). Red numbered lines = saw cuts in order, each edge to edge.
2. Coloured dimensions belong to the part of that colour: its width and height, and its position from the sheet edges. Raked parts: corner coordinates at each corner.
3. Red hatch = waste. Labels = panel + piece mark on the manufacture drawing.

REVISIONS

REV	DATE	DESCRIPTION
C01	14.09.26	Construction issue
C02	14.09.26	Roof trusses revised; SP diagonals added

TLS TIMBER FRAME
Design & Manufacture
Scan: 3D model + drawings

CLIENT	PROJECT
MP Adams	MP Adams Plot 4, Eckington


DRAWING TITLE

PIR CUTTING - GROUND FLOOR - SHEET 10 OF 33

PIR 120mm 1200x2400 | Ground Floor

SCALE	SIZE	DATE	DRAWN
NTS	A3	14.09.26	TS

STATUS	DRAWING No.	REV
CONSTRUCTION	P4-CP-PIR-01 / 10	C02

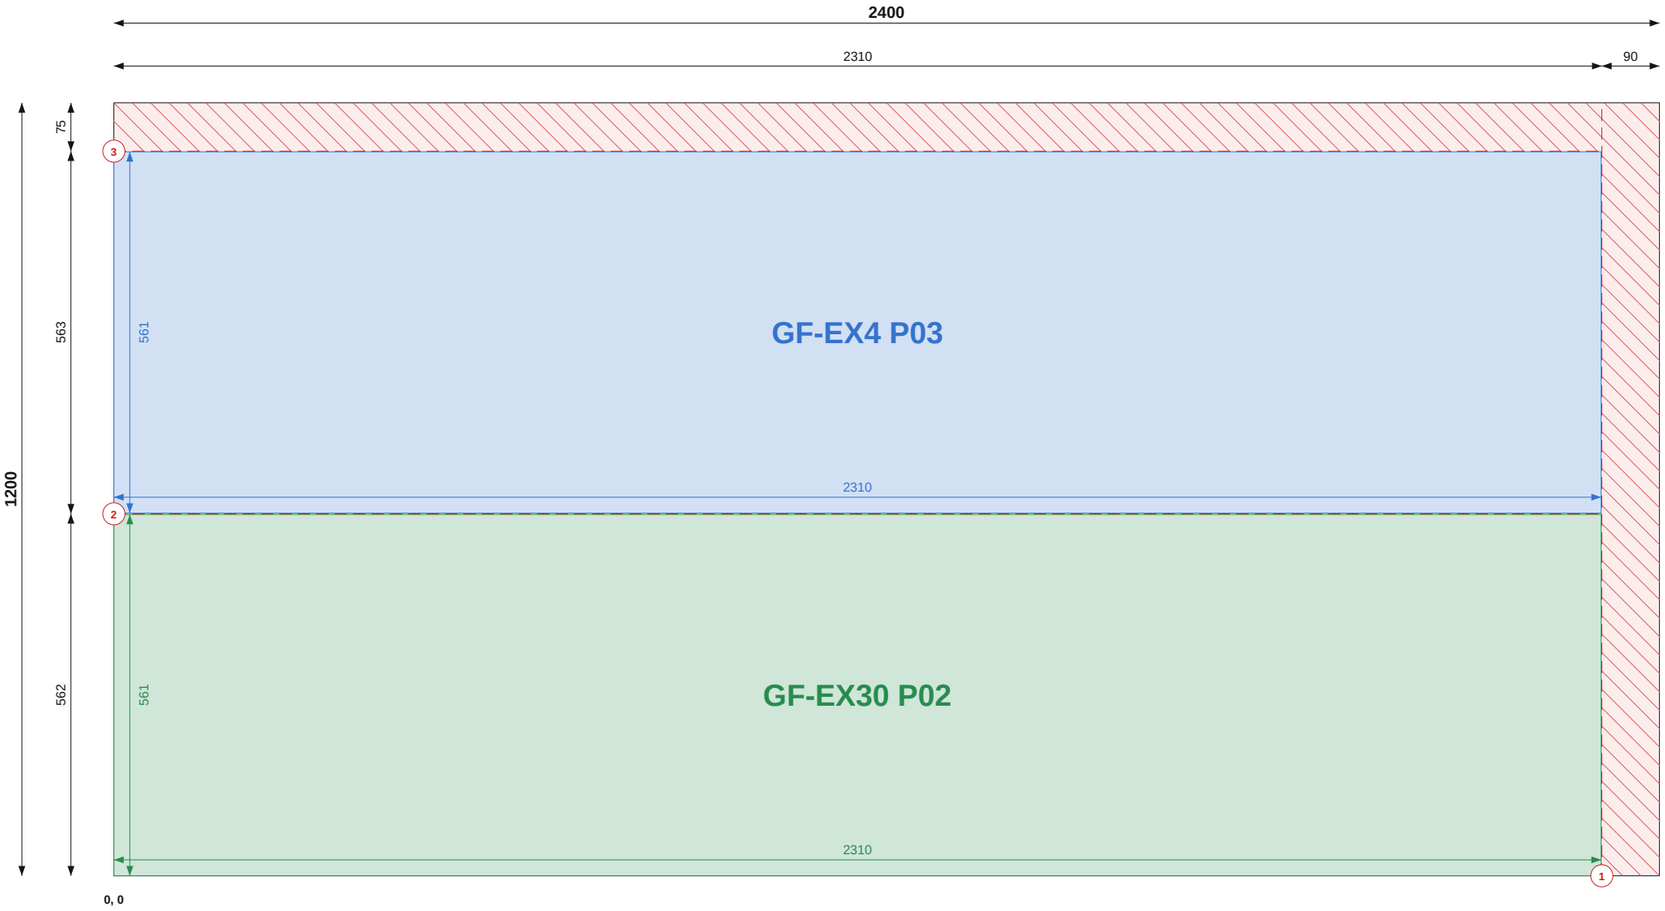

Top / left chains = saw cut positions (to cut centres). Coloured = part size and position.

SHEET 11 OF 33

THIS SHEET

Item	Value
Parts	2
Used / waste	90.0% / 0.29 m2
Reusable offcuts	0
Saw cuts / shared	3 / 1

PIECES (POSITION = BOTTOM-LEFT CORNER)

Label	Size	X, Y
GF-EX4 P03	561 x 2310	0, 563
GF-EX30 P02	561 x 2310	0, 0

NOTES

1. Cut from PIR 120mm 1200x2400, 2mm saw kerf. Viewed on the face; dimensions from the sheet's bottom-left corner (0,0). Red numbered lines = saw cuts in order, each edge to edge.
2. Coloured dimensions belong to the part of that colour: its width and height, and its position from the sheet edges. Raked parts: corner coordinates at each corner.
3. Red hatch = waste. Labels = panel + piece mark on the manufacture drawing.

REVISIONS

REV	DATE	DESCRIPTION
C01	14.09.26	Construction issue
C02	14.09.26	Roof trusses revised; SP diagonals added

TLS TIMBER FRAME
Design & Manufacture
Scan: 3D model + drawings

CLIENT	PROJECT
MP Adams	MP Adams Plot 4, Eckington

DRAWING TITLE


PIR CUTTING - GROUND FLOOR - SHEET 11 OF 33

PIR 120mm 1200x2400 | Ground Floor

SCALE	SIZE	DATE	DRAWN
NTS	A3	14.09.26	TS

STATUS	DRAWING No.	REV
CONSTRUCTION	P4-CP-PIR-01 / 11	C02

Do not scale. All dimensions in mm. Check all dimensions on site.

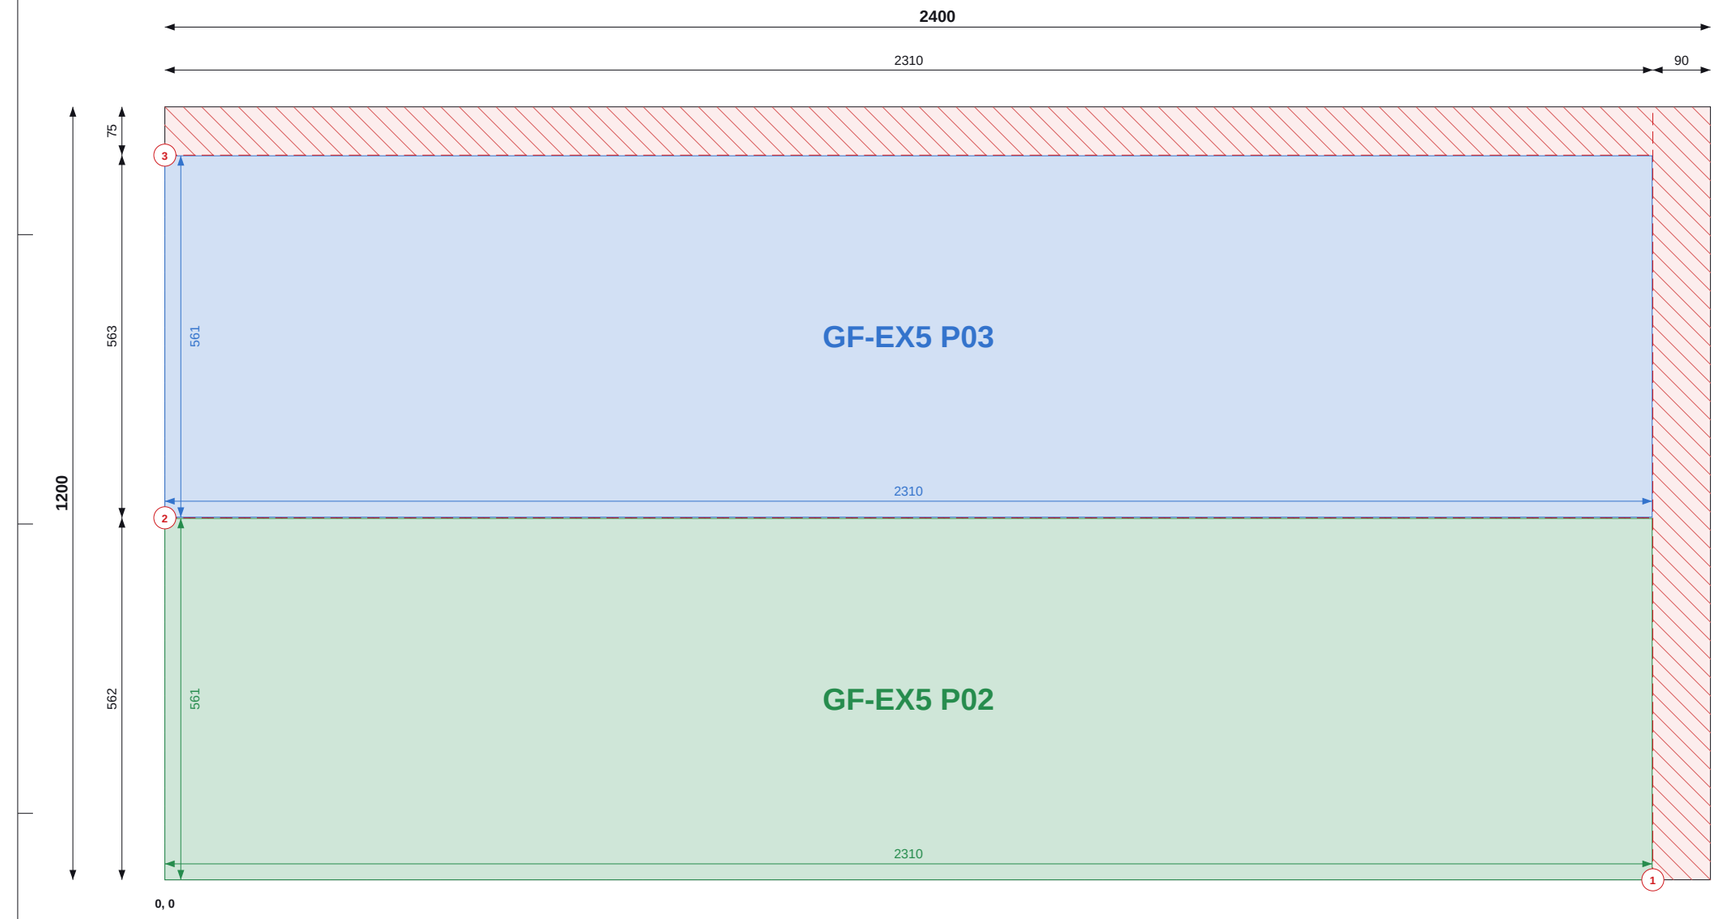

Top / left chains = saw cut positions (to cut centres). Coloured = part size and position.

SHEET 12 OF 33

THIS SHEET

Item	Value
Parts	2
Used / waste	90.0% / 0.29 m2
Reusable offcuts	0
Saw cuts / shared	3 / 1

PIECES (POSITION = BOTTOM-LEFT CORNER)

Label	Size	X, Y
GF-EX5 P03	561 x 2310	0, 563
GF-EX5 P02	561 x 2310	0, 0

NOTES

1. Cut from PIR 120mm 1200x2400, 2mm saw kerf. Viewed on the face; dimensions from the sheet's bottom-left corner (0,0). Red numbered lines = saw cuts in order, each edge to edge.
2. Coloured dimensions belong to the part of that colour: its width and height, and its position from the sheet edges. Raked parts: corner coordinates at each corner.
3. Red hatch = waste. Labels = panel + piece mark on the manufacture drawing.

REVISIONS

REV	DATE	DESCRIPTION
C01	14.09.26	Construction issue
C02	14.09.26	Roof trusses revised; SP diagonals added

TLS TIMBER FRAME
Design & Manufacture
Scan: 3D model + drawings

CLIENT	PROJECT
MP Adams	MP Adams Plot 4, Eckington

DRAWING TITLE


PIR CUTTING - GROUND FLOOR - SHEET 12 OF 33

PIR 120mm 1200x2400 | Ground Floor

SCALE	SIZE	DATE	DRAWN
NTS	A3	14.09.26	TS

STATUS	DRAWING No.	REV
CONSTRUCTION	P4-CP-PIR-01 / 12	C02

Do not scale. All dimensions in mm. Check all dimensions on site.

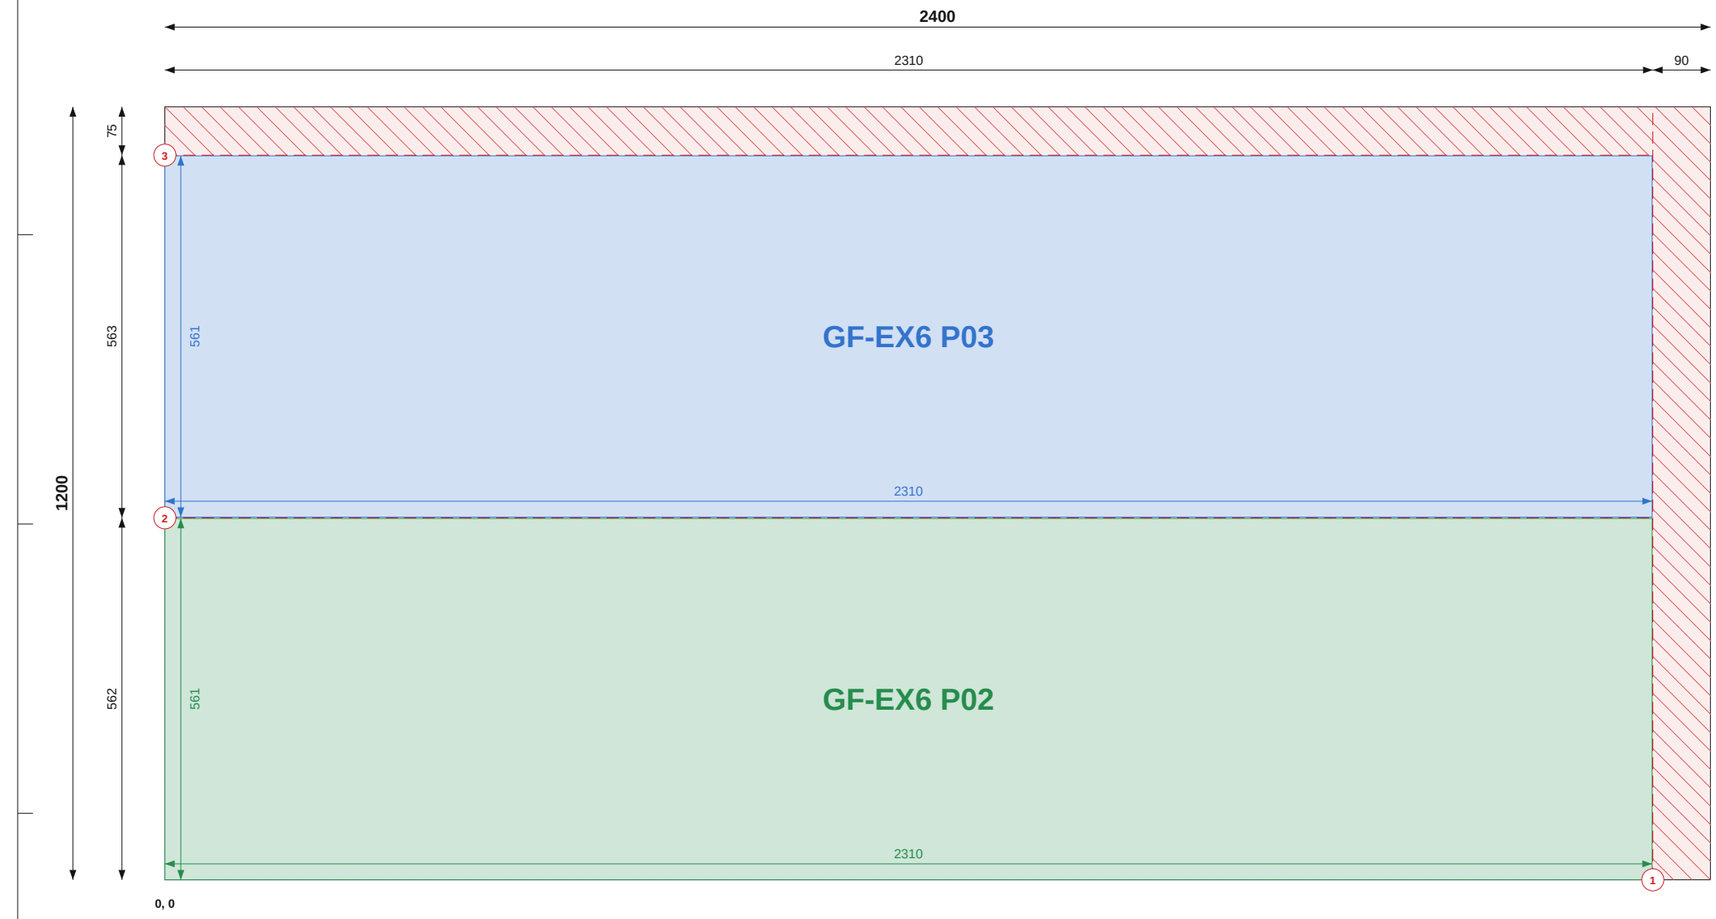

Top / left chains = saw cut positions (to cut centres). Coloured = part size and position.

Do not scale. All dimensions in mm. Check all dimensions on site.

SHEET 13 OF 33

THIS SHEET

Item	Value
Parts	2
Used / waste	90.0% / 0.29 m2
Reusable offcuts	0
Saw cuts / shared	3 / 1

PIECES (POSITION = BOTTOM-LEFT CORNER)

Label	Size	X, Y
GF-EX6 P03	561 x 2310	0, 563
GF-EX6 P02	561 x 2310	0, 0

NOTES

1. Cut from PIR 120mm 1200x2400, 2mm saw kerf. Viewed on the face; dimensions from the sheet's bottom-left corner (0,0). Red numbered lines = saw cuts in order, each edge to edge.
2. Coloured dimensions belong to the part of that colour: its width and height, and its position from the sheet edges. Raked parts: corner coordinates at each corner.
3. Red hatch = waste. Labels = panel + piece mark on the manufacture drawing.

REVISIONS

REV	DATE	DESCRIPTION
C01	14.09.26	Construction issue
C02	14.09.26	Roof trusses revised; SP diagonals added

TLS TIMBER FRAME
Design & Manufacture
Scan: 3D model + drawings

CLIENT	PROJECT
MP Adams	MP Adams Plot 4, Eckington


DRAWING TITLE

PIR CUTTING - GROUND FLOOR - SHEET 13 OF 33

PIR 120mm 1200x2400 | Ground Floor

SCALE	SIZE	DATE	DRAWN
NTS	A3	14.09.26	TS

STATUS	DRAWING No.	REV
CONSTRUCTION	P4-CP-PIR-01 / 13	C02

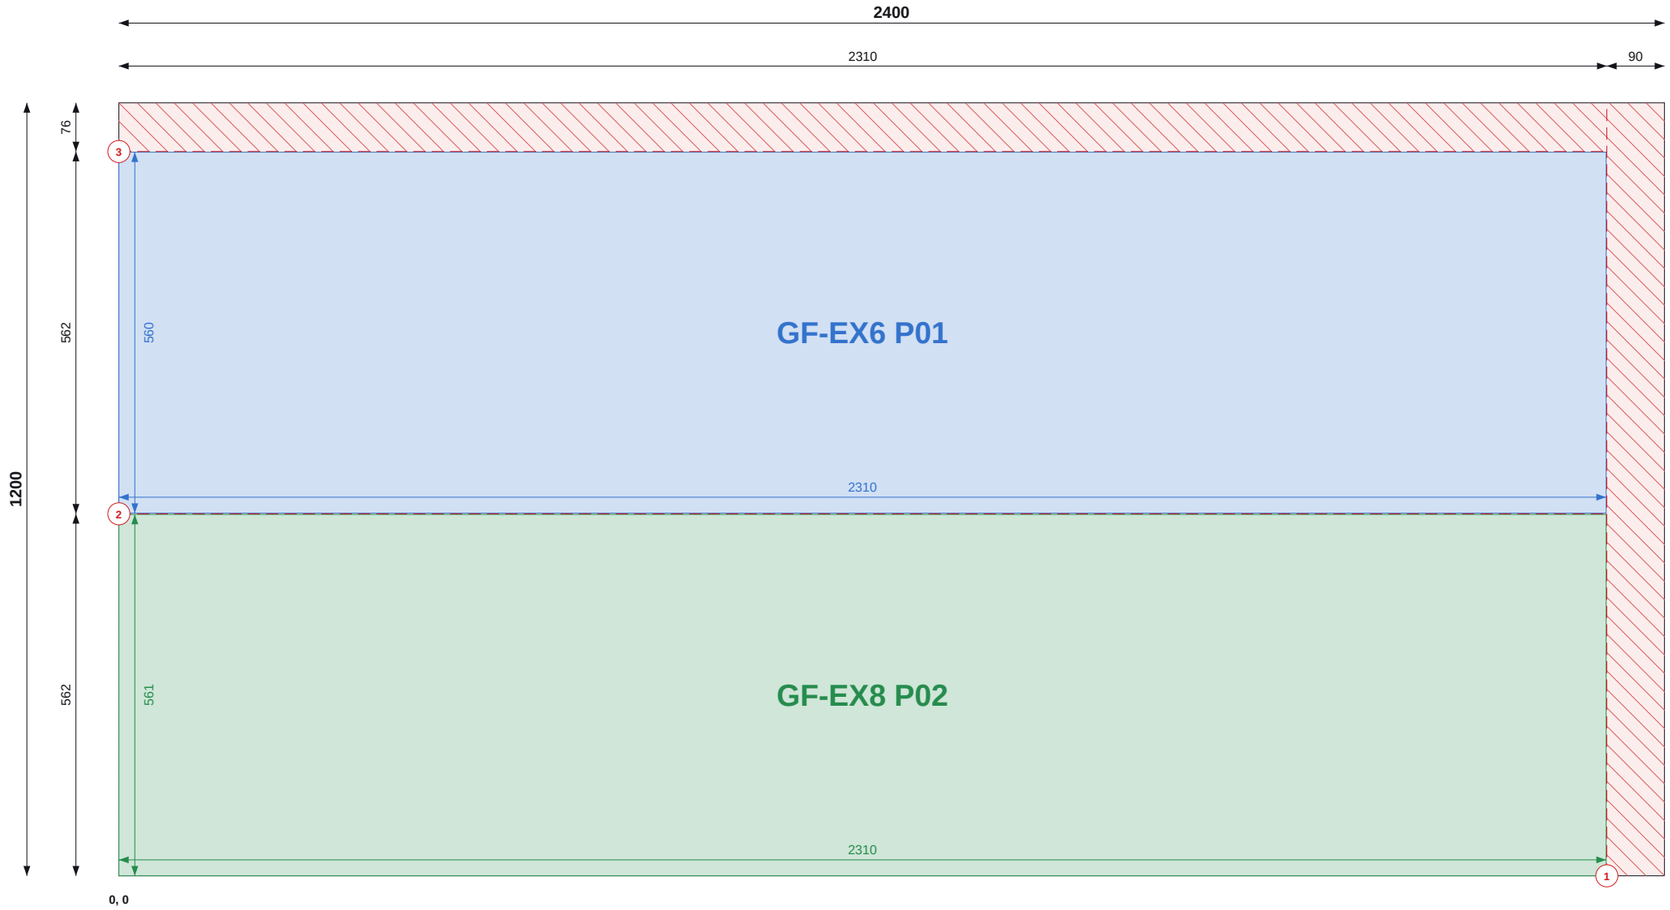

Top / left chains = saw cut positions (to cut centres). Coloured = part size and position.

SHEET 14 OF 33

THIS SHEET

Item	Value
Parts	2
Used / waste	89.9% / 0.29 m2
Reusable offcuts	0
Saw cuts / shared	3 / 1

PIECES (POSITION = BOTTOM-LEFT CORNER)

Label	Size	X, Y
GF-EX6 P01	560 x 2310	0, 563
GF-EX8 P02	561 x 2310	0, 0

NOTES

1. Cut from PIR 120mm 1200x2400, 2mm saw kerf. Viewed on the face; dimensions from the sheet's bottom-left corner (0,0). Red numbered lines = saw cuts in order, each edge to edge.
2. Coloured dimensions belong to the part of that colour: its width and height, and its position from the sheet edges. Raked parts: corner coordinates at each corner.
3. Red hatch = waste. Labels = panel + piece mark on the manufacture drawing.

REVISIONS

REV	DATE	DESCRIPTION
C01	14.09.26	Construction issue
C02	14.09.26	Roof trusses revised; SP diagonals added

TLS TIMBER FRAME
Design & Manufacture
Scan: 3D model + drawings

CLIENT	PROJECT
MP Adams	MP Adams Plot 4, Eckington

DRAWING TITLE


PIR CUTTING - GROUND FLOOR - SHEET 14 OF 33

PIR 120mm 1200x2400 | Ground Floor

SCALE	SIZE	DATE	DRAWN
NTS	A3	14.09.26	TS

STATUS	DRAWING No.	REV
CONSTRUCTION	P4-CP-PIR-01 / 14	C02

Do not scale. All dimensions in mm. Check all dimensions on site.

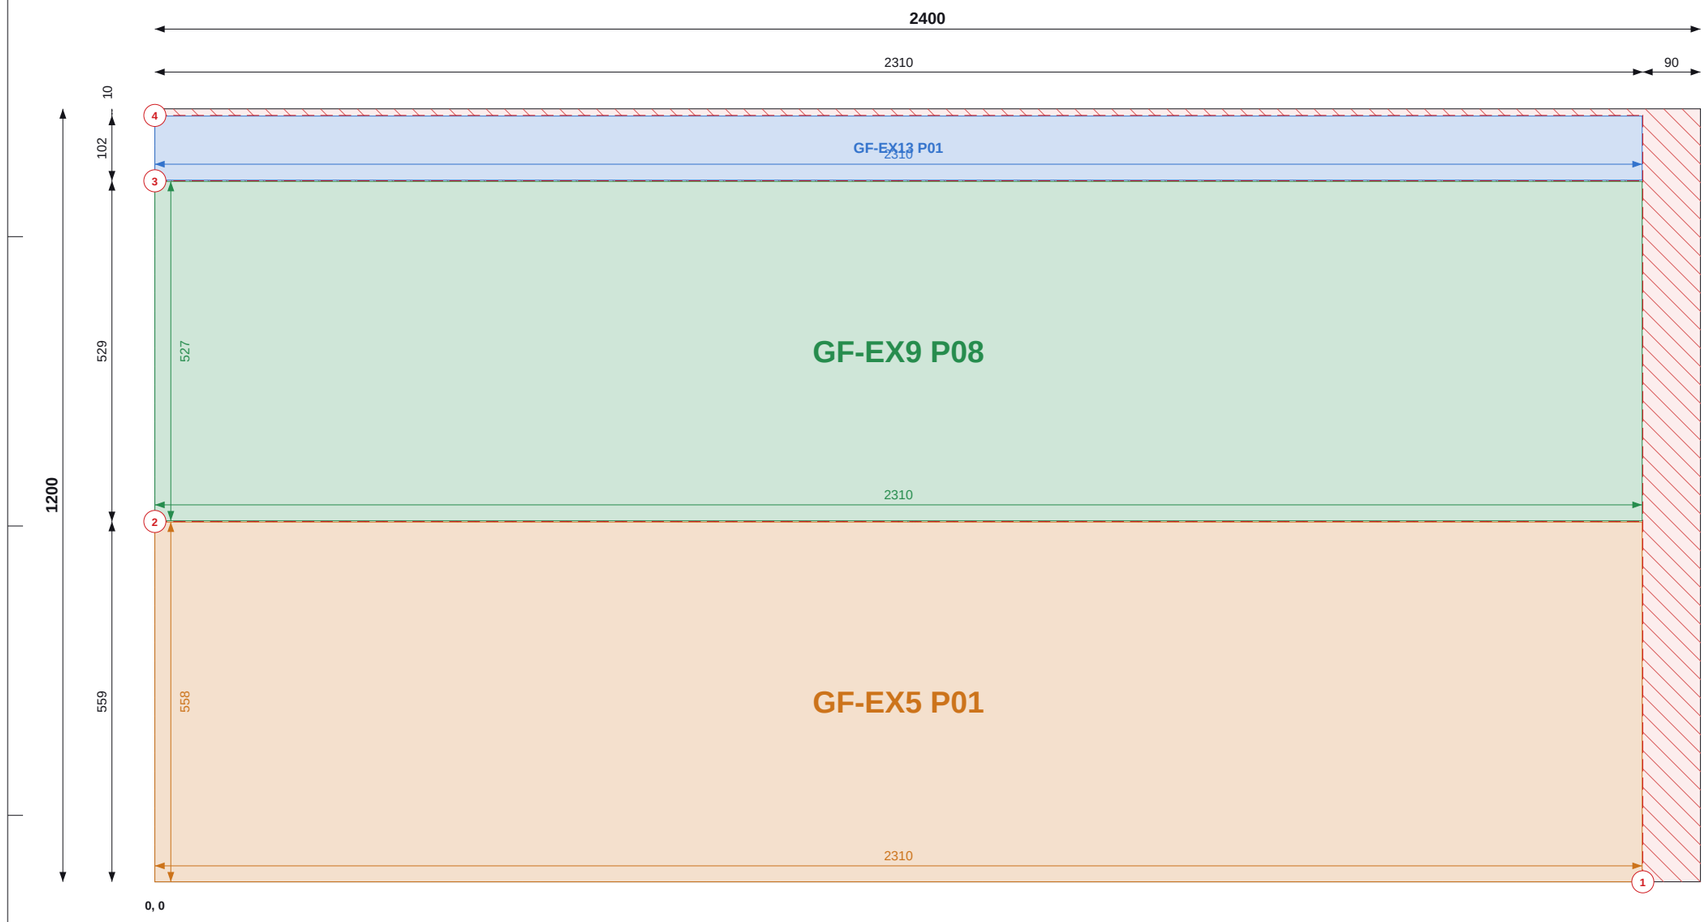

Top / left chains = saw cut positions (to cut centres). Coloured = part size and position.

SHEET 15 OF 33

THIS SHEET

Item	Value
Parts	3
Used / waste	95.0% / 0.14 m2
Reusable offcuts	0
Saw cuts / shared	4 / 2

PIECES (POSITION = BOTTOM-LEFT CORNER)

Label	Size	X, Y
GF-EX13 P01	99 x 2310	0, 1089
GF-EX9 P08	527 x 2310	0, 560
GF-EX5 P01	558 x 2310	0, 0

NOTES

1. Cut from PIR 120mm 1200x2400, 2mm saw kerf. Viewed on the face; dimensions from the sheet's bottom-left corner (0,0). Red numbered lines = saw cuts in order, each edge to edge.
2. Coloured dimensions belong to the part of that colour: its width and height, and its position from the sheet edges. Raked parts: corner coordinates at each corner.
3. Red hatch = waste. Labels = panel + piece mark on the manufacture drawing.

REVISIONS

REV	DATE	DESCRIPTION
C01	14.09.26	Construction issue
C02	14.09.26	Roof trusses revised; SP diagonals added

TLS TIMBER FRAME DESIGN SUITE

TLS TIMBER FRAME

Design & Manufacture

Scan: 3D model + drawings

CLIENT	PROJECT
MP Adams	MP Adams Plot 4, Eckington

DRAWING TITLE


PIR CUTTING - GROUND FLOOR - SHEET 15 OF 33

PIR 120mm 1200x2400 | Ground Floor

SCALE	SIZE	DATE	DRAWN
NTS	A3	14.09.26	TS

STATUS	DRAWING No.	REV
CONSTRUCTION	P4-CP-PIR-01 / 15	C02

Do not scale. All dimensions in mm. Check all dimensions on site.

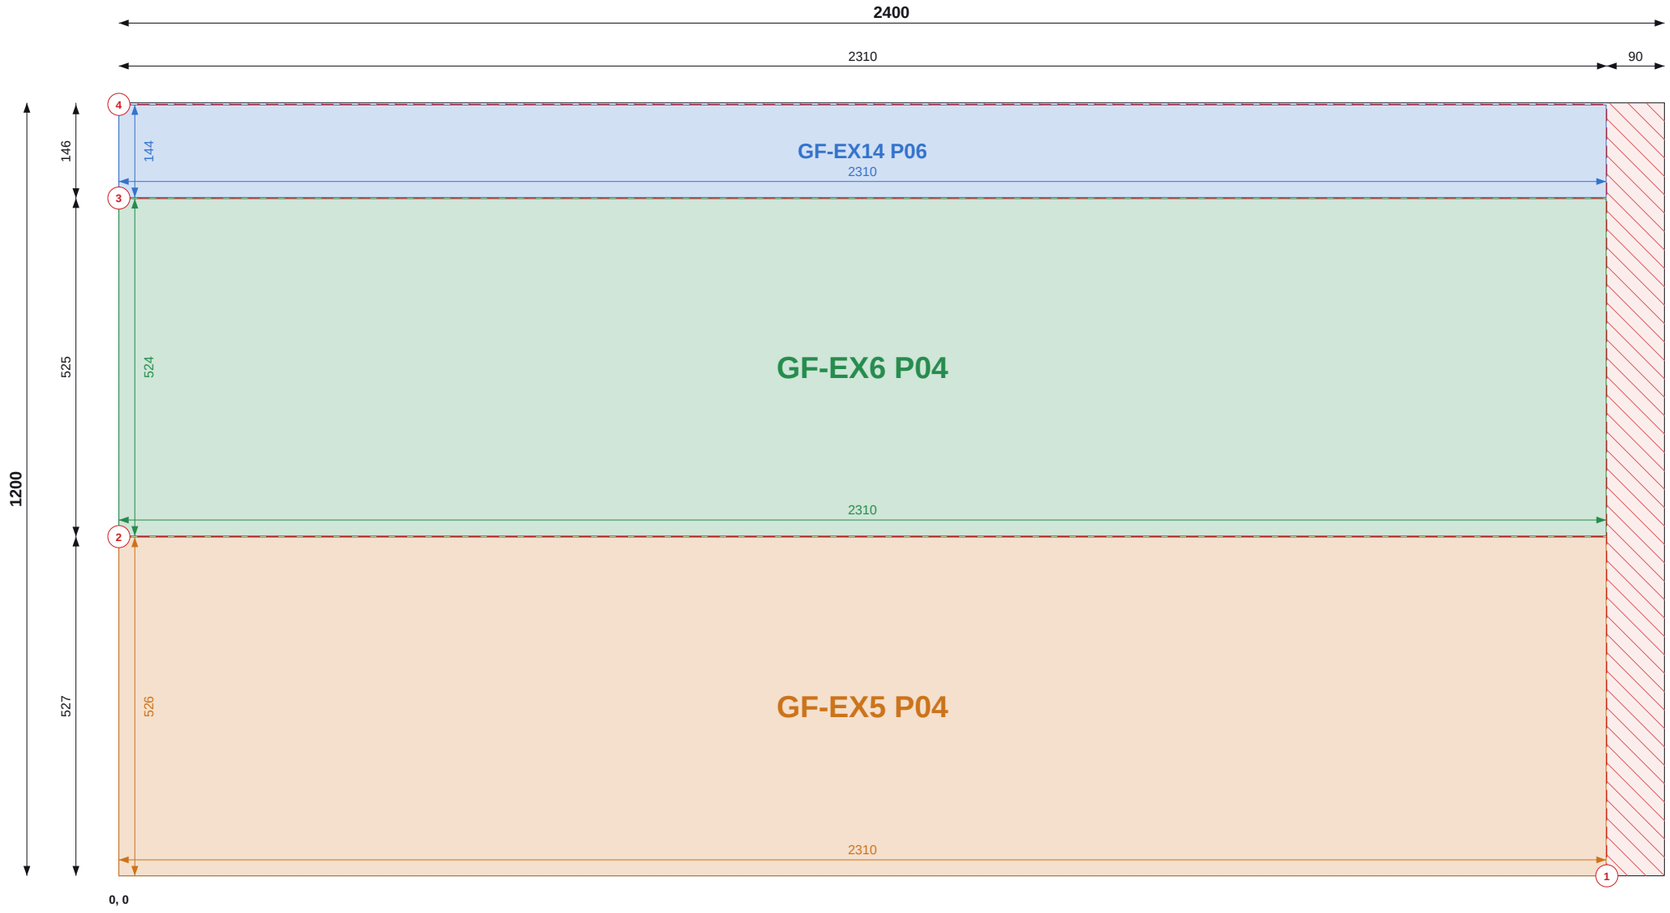

Top / left chains = saw cut positions (to cut centres). Coloured = part size and position.

Do not scale. All dimensions in mm. Check all dimensions on site.

SHEET 16 OF 33

THIS SHEET

Item	Value
Parts	3
Used / waste	95.6% / 0.13 m2
Reusable offcuts	0
Saw cuts / shared	4 / 2

PIECES (POSITION = BOTTOM-LEFT CORNER)

Label	Size	X, Y
GF-EX14 P06	144 x 2310	0, 1053
GF-EX6 P04	524 x 2310	0, 528
GF-EX5 P04	526 x 2310	0, 0

NOTES

1. Cut from PIR 120mm 1200x2400, 2mm saw kerf. Viewed on the face; dimensions from the sheet's bottom-left corner (0,0). Red numbered lines = saw cuts in order, each edge to edge.
2. Coloured dimensions belong to the part of that colour: its width and height, and its position from the sheet edges. Raked parts: corner coordinates at each corner.
3. Red hatch = waste. Labels = panel + piece mark on the manufacture drawing.

REVISIONS

REV	DATE	DESCRIPTION
C01	14.09.26	Construction issue
C02	14.09.26	Roof trusses revised; SP diagonals added

TLS TIMBER FRAME
Design & Manufacture
Scan: 3D model + drawings

CLIENT	PROJECT
MP Adams	MP Adams Plot 4, Eckington


DRAWING TITLE

PIR CUTTING - GROUND FLOOR - SHEET 16 OF 33

PIR 120mm 1200x2400 | Ground Floor

SCALE	SIZE	DATE	DRAWN
NTS	A3	14.09.26	TS

STATUS	DRAWING No.	REV
CONSTRUCTION	P4-CP-PIR-01 / 16	C02

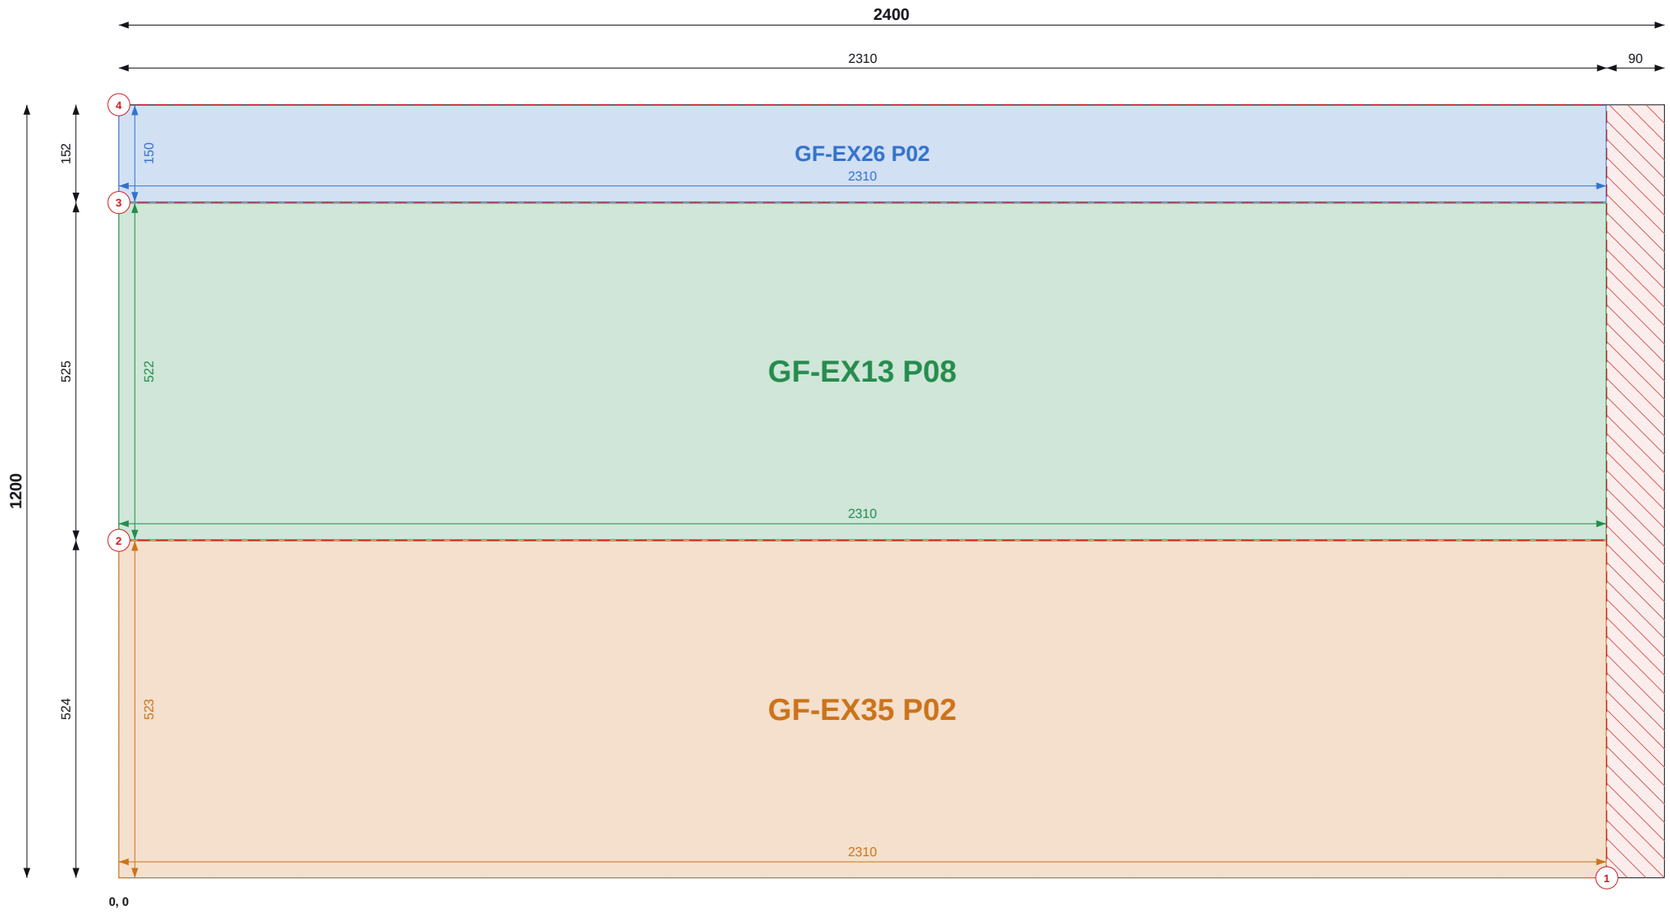

Top / left chains = saw cut positions (to cut centres). Coloured = part size and position.

SHEET 17 OF 33

THIS SHEET

Item	Value
Parts	3
Used / waste	95.9% / 0.12 m2
Reusable offcuts	0
Saw cuts / shared	4 / 2

PIECES (POSITION = BOTTOM-LEFT CORNER)

Label	Size	X, Y
GF-EX26 P02	150 x 2310	0, 1049
GF-EX13 P08	522 x 2310	0, 525
GF-EX35 P02	523 x 2310	0, 0

NOTES

1. Cut from PIR 120mm 1200x2400, 2mm saw kerf. Viewed on the face; dimensions from the sheet's bottom-left corner (0,0). Red numbered lines = saw cuts in order, each edge to edge.
2. Coloured dimensions belong to the part of that colour: its width and height, and its position from the sheet edges. Raked parts: corner coordinates at each corner.
3. Red hatch = waste. Labels = panel + piece mark on the manufacture drawing.

REVISIONS

REV	DATE	DESCRIPTION
C01	14.09.26	Construction issue
C02	14.09.26	Roof trusses revised; SP diagonals added

TLS TIMBER FRAME
Design & Manufacture
Scan: 3D model + drawings

CLIENT	PROJECT
MP Adams	MP Adams Plot 4, Eckington

DRAWING TITLE


PIR CUTTING - GROUND FLOOR - SHEET 17 OF 33

PIR 120mm 1200x2400 | Ground Floor

SCALE	SIZE	DATE	DRAWN
NTS	A3	14.09.26	TS

STATUS	DRAWING No.	REV
CONSTRUCTION	P4-CP-PIR-01 / 17	C02

Do not scale. All dimensions in mm. Check all dimensions on site.

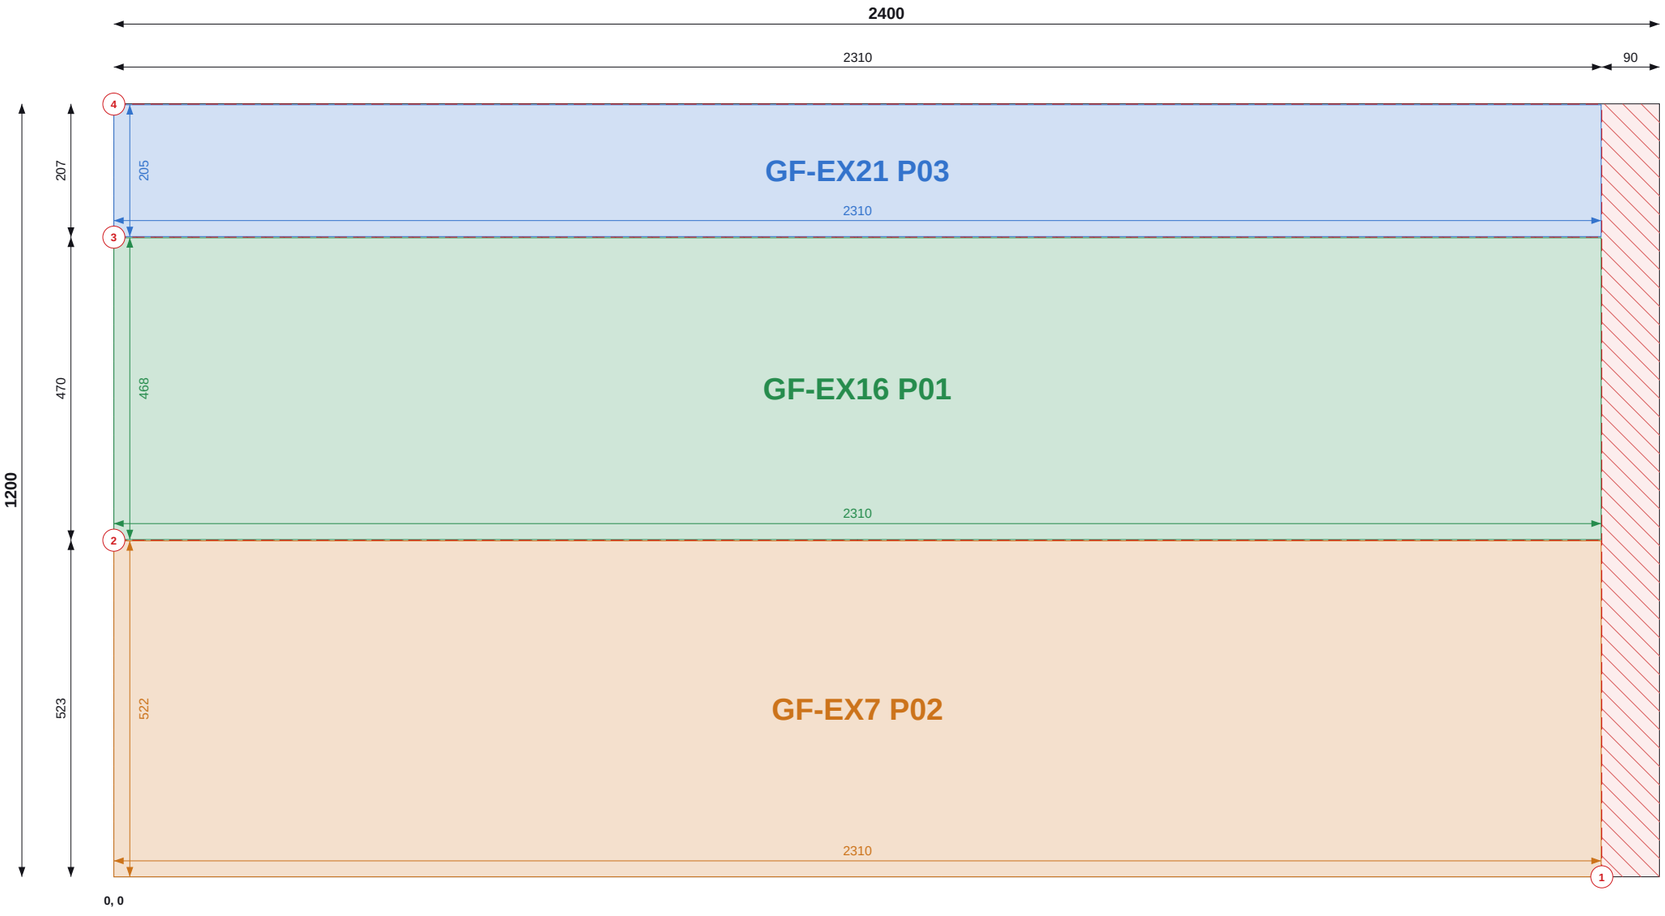

Top / left chains = saw cut positions (to cut centres). Coloured = part size and position.

SHEET 18 OF 33

THIS SHEET

Item	Value
Parts	3
Used / waste	95.8% / 0.12 m2
Reusable offcuts	0
Saw cuts / shared	4 / 2

PIECES (POSITION = BOTTOM-LEFT CORNER)

Label	Size	X, Y
GF-EX21 P03	205 x 2310	0, 994
GF-EX16 P01	468 x 2310	0, 524
GF-EX7 P02	522 x 2310	0, 0

NOTES

1. Cut from PIR 120mm 1200x2400, 2mm saw kerf. Viewed on the face; dimensions from the sheet's bottom-left corner (0,0). Red numbered lines = saw cuts in order, each edge to edge.
2. Coloured dimensions belong to the part of that colour: its width and height, and its position from the sheet edges. Raked parts: corner coordinates at each corner.
3. Red hatch = waste. Labels = panel + piece mark on the manufacture drawing.

REVISIONS

REV	DATE	DESCRIPTION
C01	14.09.26	Construction issue
C02	14.09.26	Roof trusses revised; SP diagonals added

TLS TIMBER FRAME
Design & Manufacture
Scan: 3D model + drawings

CLIENT	PROJECT
MP Adams	MP Adams Plot 4, Eckington

DRAWING TITLE


PIR CUTTING - GROUND FLOOR - SHEET 18 OF 33

PIR 120mm 1200x2400 | Ground Floor

SCALE	SIZE	DATE	DRAWN
NTS	A3	14.09.26	TS

STATUS	DRAWING No.	REV
CONSTRUCTION	P4-CP-PIR-01 / 18	C02

Do not scale. All dimensions in mm. Check all dimensions on site.

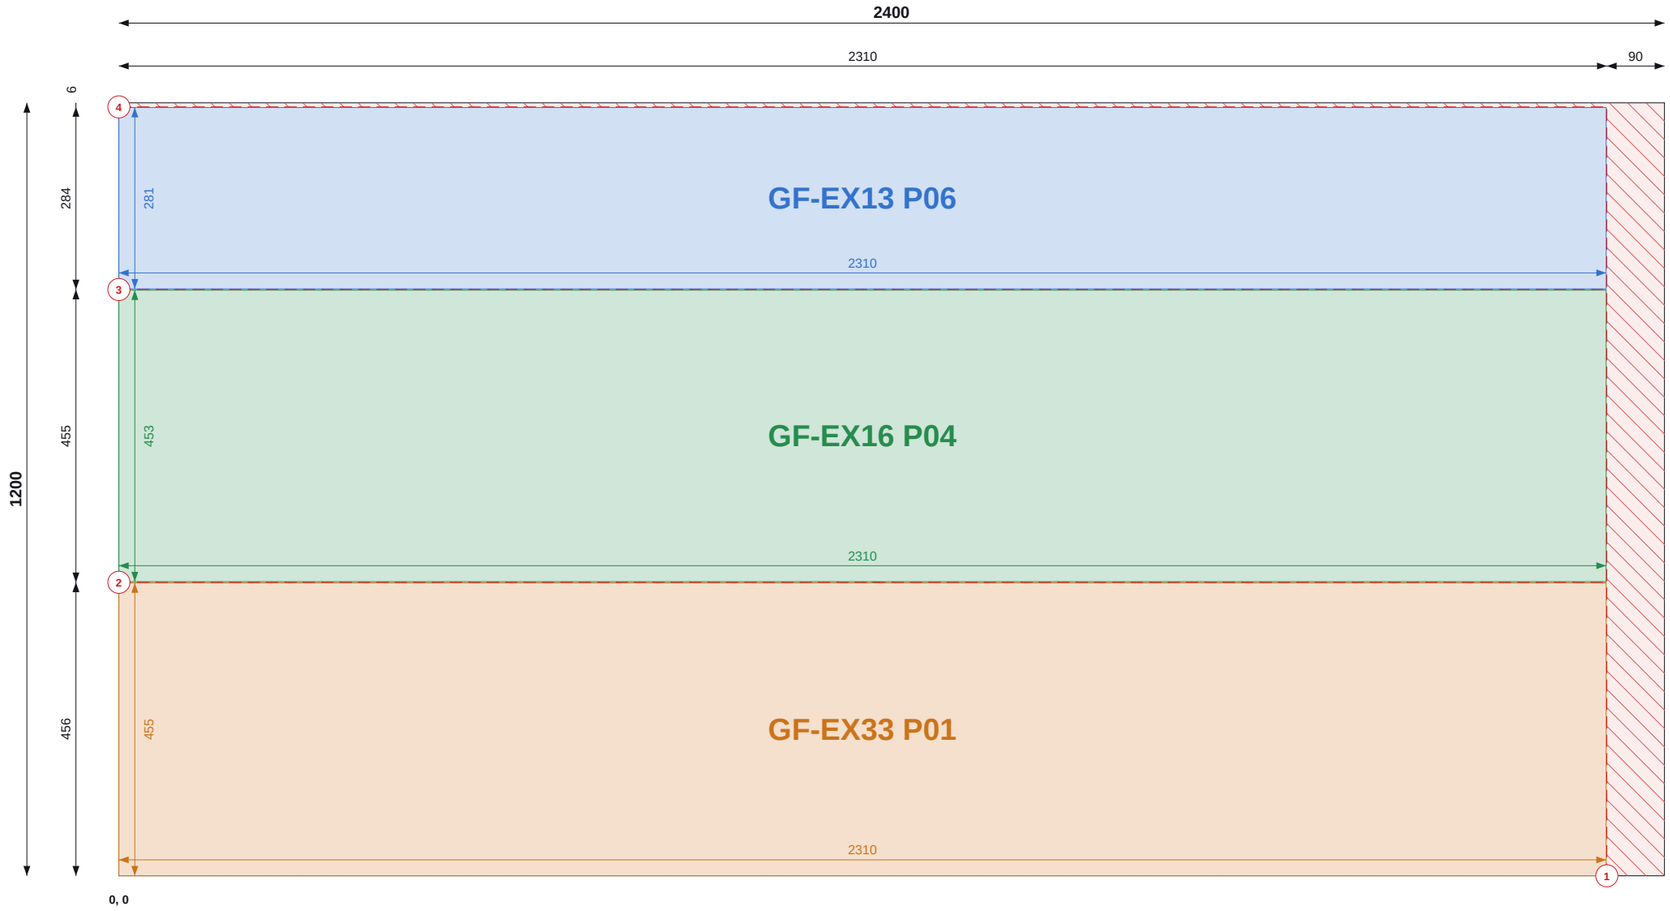

Top / left chains = saw cut positions (to cut centres). Coloured = part size and position.

Do not scale. All dimensions in mm. Check all dimensions on site.

SHEET 19 OF 33

THIS SHEET

Item	Value
Parts	3
Used / waste	95.3% / 0.13 m2
Reusable offcuts	0
Saw cuts / shared	4 / 2

PIECES (POSITION = BOTTOM-LEFT CORNER)

Label	Size	X, Y
GF-EX13 P06	281 x 2310	0, 911
GF-EX16 P04	453 x 2310	0, 457
GF-EX33 P01	455 x 2310	0, 0

NOTES

1. Cut from PIR 120mm 1200x2400, 2mm saw kerf. Viewed on the face; dimensions from the sheet's bottom-left corner (0,0). Red numbered lines = saw cuts in order, each edge to edge.
2. Coloured dimensions belong to the part of that colour: its width and height, and its position from the sheet edges. Raked parts: corner coordinates at each corner.
3. Red hatch = waste. Labels = panel + piece mark on the manufacture drawing.

REVISIONS

REV	DATE	DESCRIPTION
C01	14.09.26	Construction issue
C02	14.09.26	Roof trusses revised; SP diagonals added

TLS TIMBER FRAME
Design & Manufacture
Scan: 3D model + drawings

CLIENT	PROJECT
MP Adams	MP Adams Plot 4, Eckington


DRAWING TITLE

PIR CUTTING - GROUND FLOOR - SHEET 19 OF 33

PIR 120mm 1200x2400 | Ground Floor

SCALE	SIZE	DATE	DRAWN
NTS	A3	14.09.26	TS

STATUS	DRAWING No.	REV
CONSTRUCTION	P4-CP-PIR-01 / 19	C02

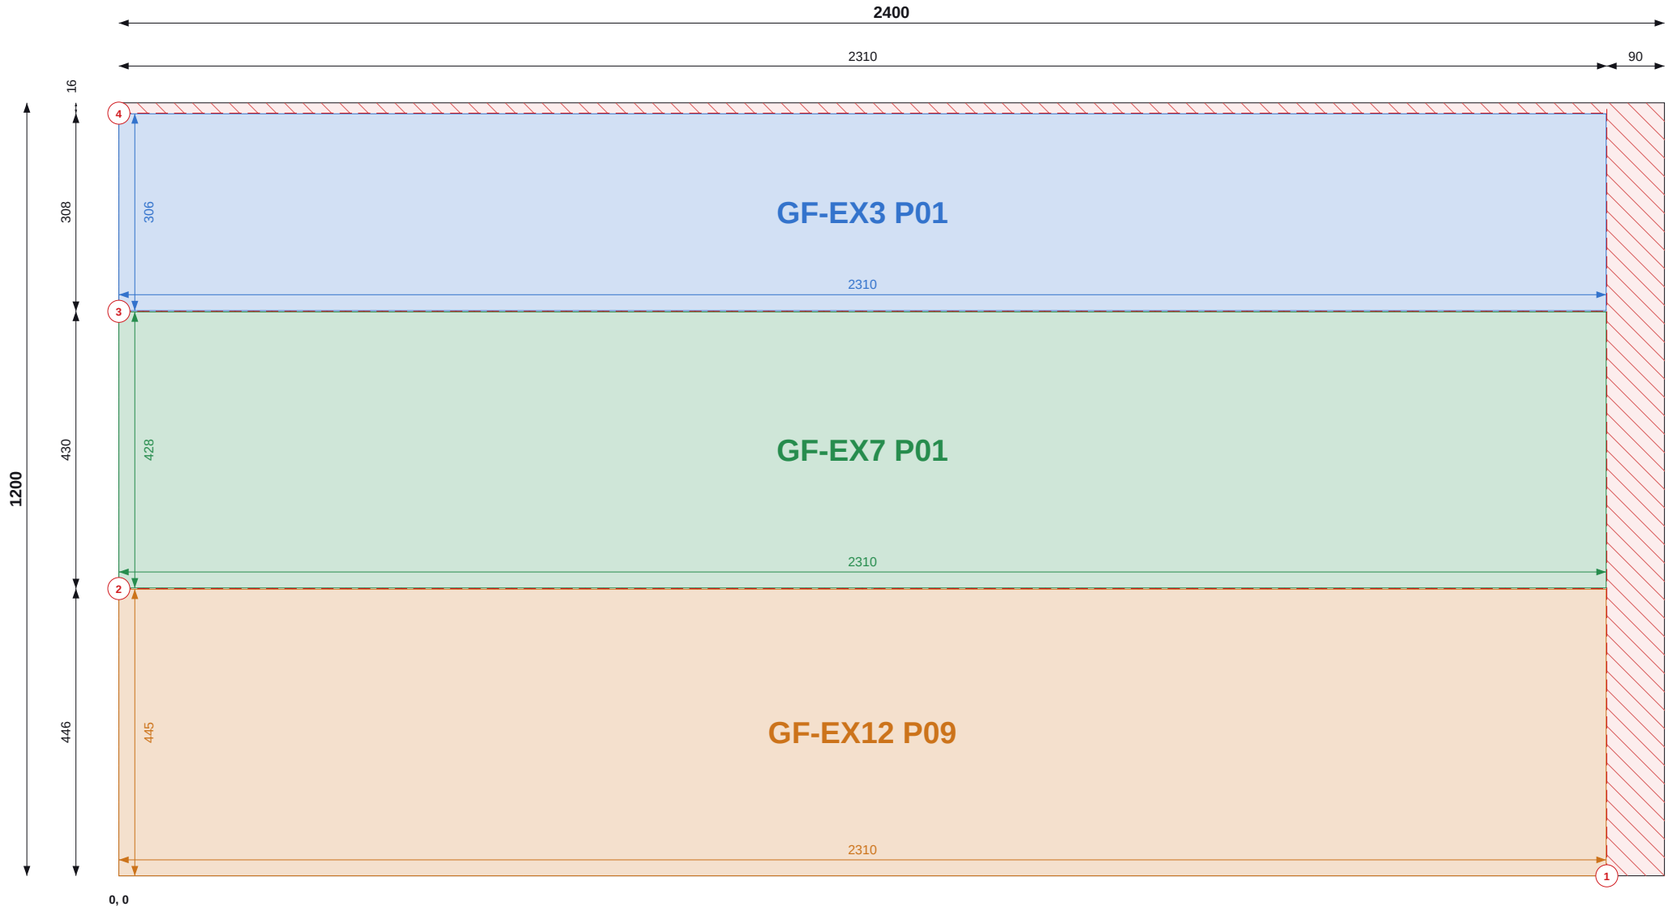

Top / left chains = saw cut positions (to cut centres). Coloured = part size and position.

Do not scale. All dimensions in mm. Check all dimensions on site.

SHEET 20 OF 33

THIS SHEET

Item	Value
Parts	3
Used / waste	94.5% / 0.16 m2
Reusable offcuts	0
Saw cuts / shared	4 / 2

PIECES (POSITION = BOTTOM-LEFT CORNER)

Label	Size	X, Y
GF-EX3 P01	306 x 2310	0, 877
GF-EX7 P01	428 x 2310	0, 447
GF-EX12 P09	445 x 2310	0, 0

NOTES

1. Cut from PIR 120mm 1200x2400, 2mm saw kerf. Viewed on the face; dimensions from the sheet's bottom-left corner (0,0). Red numbered lines = saw cuts in order, each edge to edge.
2. Coloured dimensions belong to the part of that colour: its width and height, and its position from the sheet edges. Raked parts: corner coordinates at each corner.
3. Red hatch = waste. Labels = panel + piece mark on the manufacture drawing.

REVISIONS

REV	DATE	DESCRIPTION
C01	14.09.26	Construction issue
C02	14.09.26	Roof trusses revised; SP diagonals added

TLS TIMBER FRAME
Design & Manufacture
Scan: 3D model + drawings

CLIENT	PROJECT
MP Adams	MP Adams Plot 4, Eckington


DRAWING TITLE

PIR CUTTING - GROUND FLOOR - SHEET 20 OF 33

PIR 120mm 1200x2400 | Ground Floor

SCALE	SIZE	DATE	DRAWN
NTS	A3	14.09.26	TS

STATUS	DRAWING No.	REV
CONSTRUCTION	P4-CP-PIR-01 / 20	C02

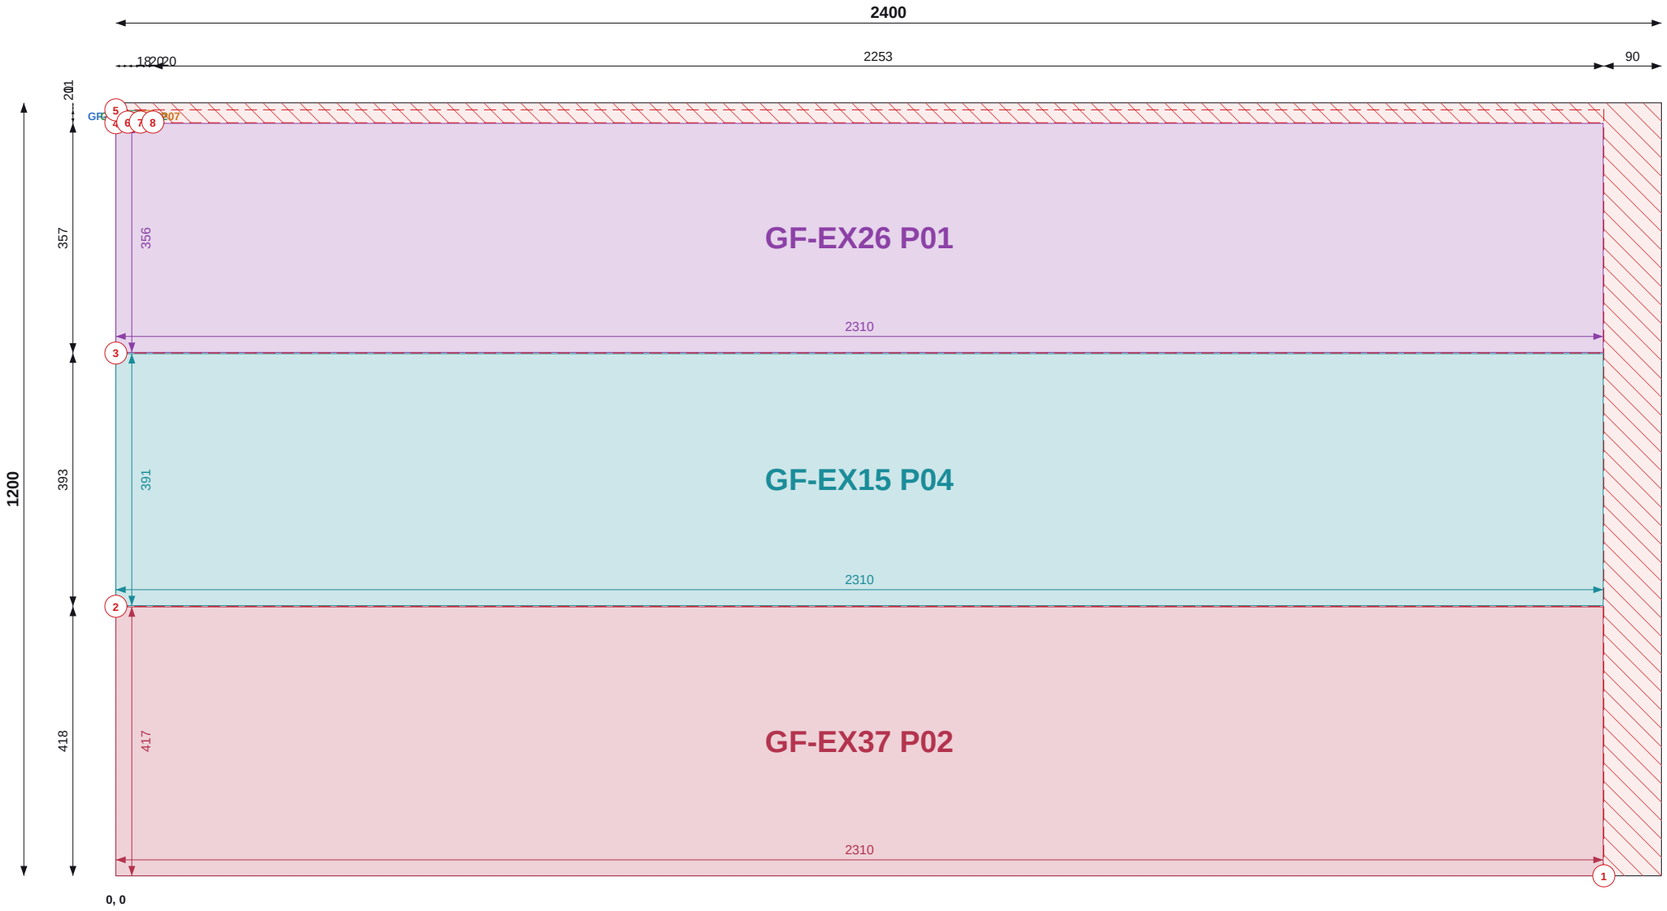

Top / left chains = saw cut positions (to cut centres). Coloured = part size and position.

Do not scale. All dimensions in mm. Check all dimensions on site.

SHEET 21 OF 33

THIS SHEET

Item	Value
Parts	6
Used / waste	93.4% / 0.19 m2
Reusable offcuts	0
Saw cuts / shared	8 / 5

PIECES (POSITION = BOTTOM-LEFT CORNER)

Label	Size	X, Y
GF-EX25 P10	18 x 18	0, 1170
GF-EX32 P02	18 x 18	20, 1170
GF-EX32 P07	18 x 18	39, 1170
GF-EX26 P01	356 x 2310	0, 813
GF-EX15 P04	391 x 2310	0, 419
GF-EX37 P02	417 x 2310	0, 0

NOTES

1. Cut from PIR 120mm 1200x2400, 2mm saw kerf. Viewed on the face; dimensions from the sheet's bottom-left corner (0,0). Red numbered lines = saw cuts in order, each edge to edge.
2. Coloured dimensions belong to the part of that colour: its width and height, and its position from the sheet edges. Raked parts: corner coordinates at each corner.
3. Red hatch = waste. Labels = panel + piece mark on the manufacture drawing.

REVISIONS

REV	DATE	DESCRIPTION
C01	14.09.26	Construction issue
C02	14.09.26	Roof trusses revised; SP diagonals added

TLS TIMBER FRAME
Design & Manufacture
Scan: 3D model + drawings

CLIENT	PROJECT
MP Adams	MP Adams Plot 4, Eckington


DRAWING TITLE

PIR CUTTING - GROUND FLOOR - SHEET 21 OF 33

PIR 120mm 1200x2400 | Ground Floor

SCALE	SIZE	DATE	DRAWN
NTS	A3	14.09.26	TS

STATUS	DRAWING No.	REV
CONSTRUCTION	P4-CP-PIR-01 / 21	C02

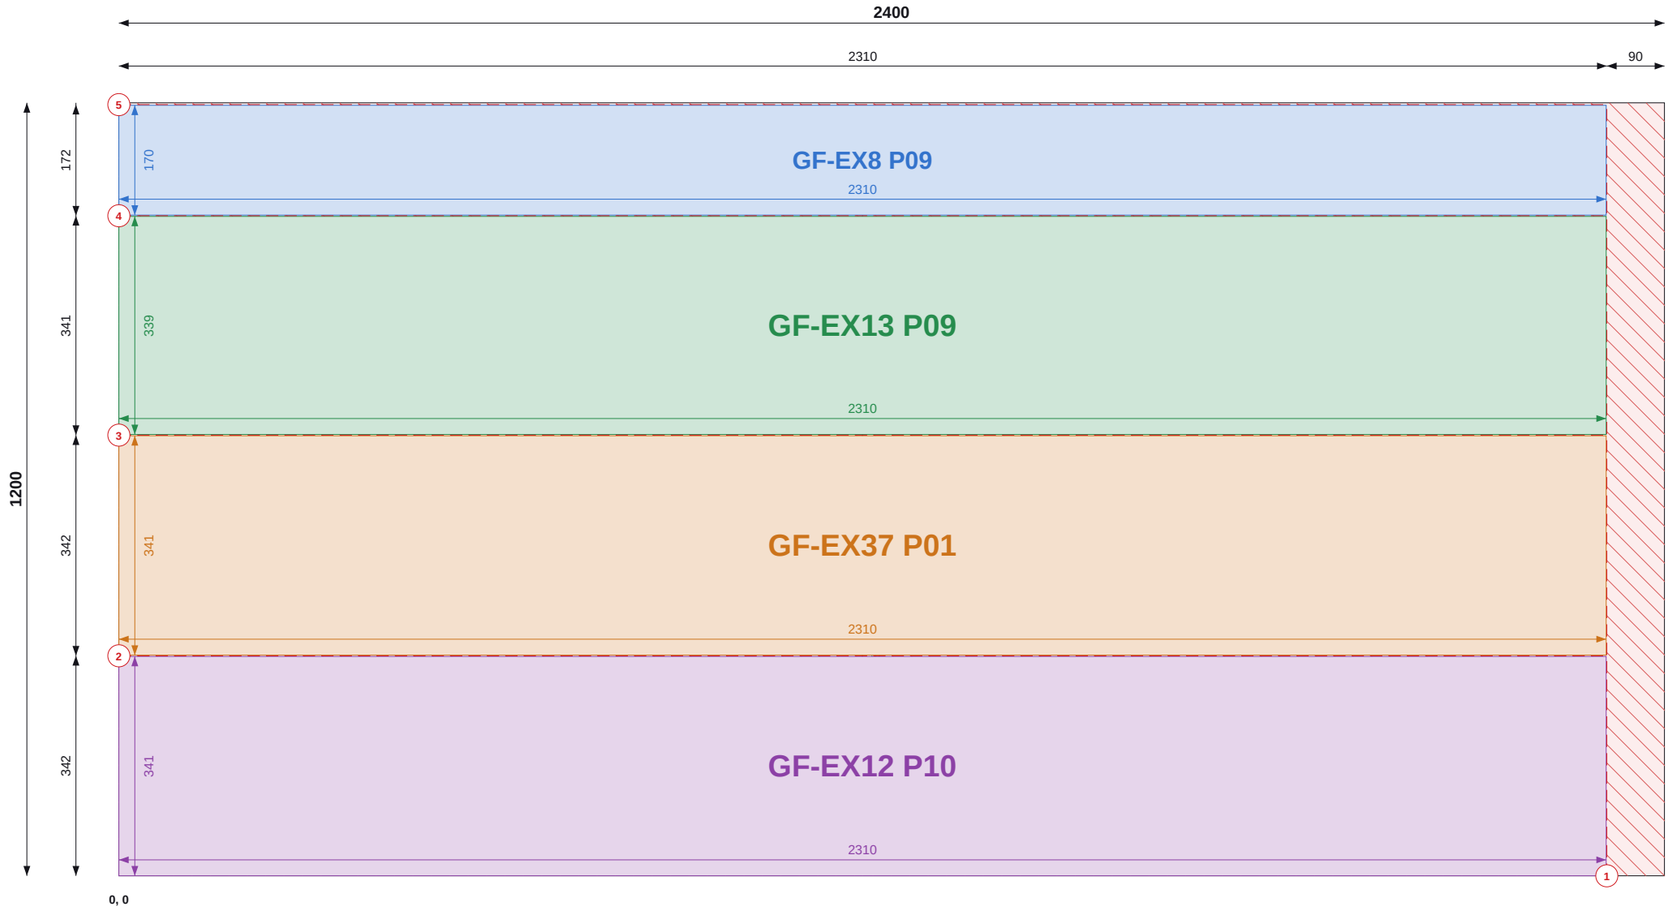

Top / left chains = saw cut positions (to cut centres). Coloured = part size and position.

SHEET 22 OF 33

THIS SHEET

Item	Value
Parts	4
Used / waste	95.4% / 0.13 m2
Reusable offcuts	0
Saw cuts / shared	5 / 3

PIECES (POSITION = BOTTOM-LEFT CORNER)

Label	Size	X, Y
GF-EX8 P09	170 x 2310	0, 1026
GF-EX13 P09	339 x 2310	0, 685
GF-EX37 P01	341 x 2310	0, 343
GF-EX12 P10	341 x 2310	0, 0

NOTES

1. Cut from PIR 120mm 1200x2400, 2mm saw kerf. Viewed on the face; dimensions from the sheet's bottom-left corner (0,0). Red numbered lines = saw cuts in order, each edge to edge.
2. Coloured dimensions belong to the part of that colour: its width and height, and its position from the sheet edges. Raked parts: corner coordinates at each corner.
3. Red hatch = waste. Labels = panel + piece mark on the manufacture drawing.

REVISIONS

REV	DATE	DESCRIPTION
C01	14.09.26	Construction issue
C02	14.09.26	Roof trusses revised; SP diagonals added

TLS TIMBER FRAME
Design & Manufacture
Scan: 3D model + drawings

CLIENT	PROJECT
MP Adams	MP Adams Plot 4, Eckington

DRAWING TITLE


PIR CUTTING - GROUND FLOOR - SHEET 22 OF 33

PIR 120mm 1200x2400 | Ground Floor

SCALE	SIZE	DATE	DRAWN
NTS	A3	14.09.26	TS

STATUS	DRAWING No.	REV
CONSTRUCTION	P4-CP-PIR-01 / 22	C02

Do not scale. All dimensions in mm. Check all dimensions on site.

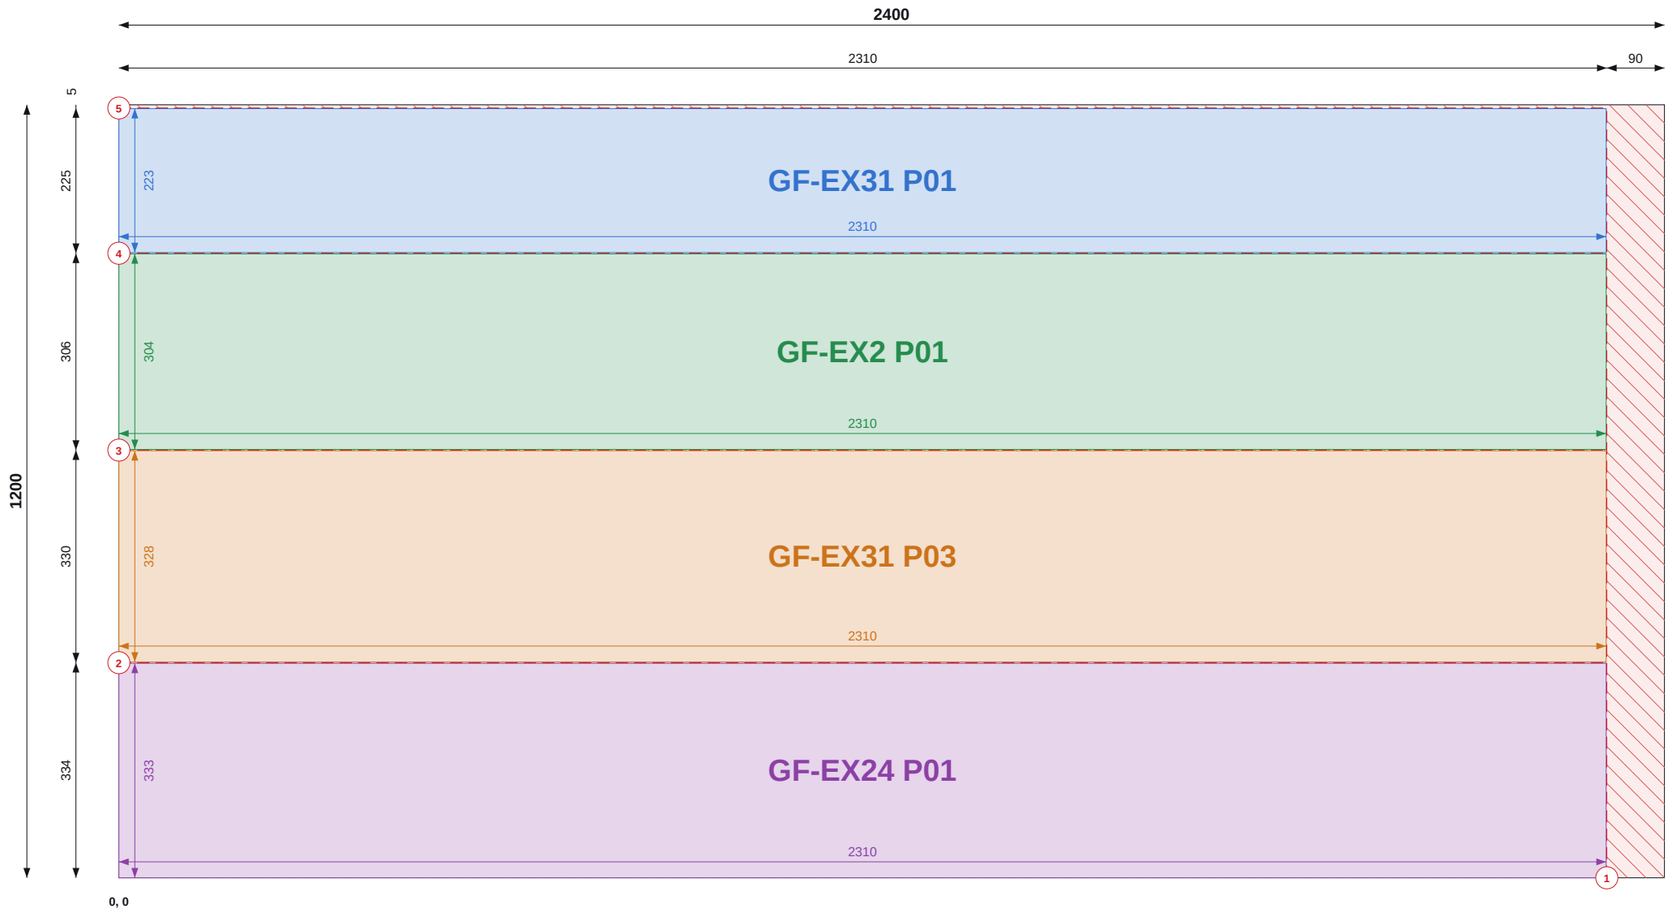

Top / left chains = saw cut positions (to cut centres). Coloured = part size and position.

SHEET 23 OF 33

THIS SHEET

Item	Value
Parts	4
Used / waste	95.3% / 0.14 m2
Reusable offcuts	0
Saw cuts / shared	5 / 3

PIECES (POSITION = BOTTOM-LEFT CORNER)

Label	Size	X, Y
GF-EX31 P01	223 x 2310	0, 971
GF-EX2 P01	304 x 2310	0, 665
GF-EX31 P03	328 x 2310	0, 335
GF-EX24 P01	333 x 2310	0, 0

NOTES

1. Cut from PIR 120mm 1200x2400, 2mm saw kerf. Viewed on the face; dimensions from the sheet's bottom-left corner (0,0). Red numbered lines = saw cuts in order, each edge to edge.
2. Coloured dimensions belong to the part of that colour: its width and height, and its position from the sheet edges. Raked parts: corner coordinates at each corner.
3. Red hatch = waste. Labels = panel + piece mark on the manufacture drawing.

REVISIONS

REV	DATE	DESCRIPTION
C01	14.09.26	Construction issue
C02	14.09.26	Roof trusses revised; SP diagonals added

TLS TIMBER FRAME
Design & Manufacture
Scan: 3D model + drawings

CLIENT	PROJECT
MP Adams	MP Adams Plot 4, Eckington

DRAWING TITLE


PIR CUTTING - GROUND FLOOR - SHEET 23 OF 33

PIR 120mm 1200x2400 | Ground Floor

SCALE	SIZE	DATE	DRAWN
NTS	A3	14.09.26	TS

STATUS	DRAWING No.	REV
CONSTRUCTION	P4-CP-PIR-01 / 23	C02

Do not scale. All dimensions in mm. Check all dimensions on site.

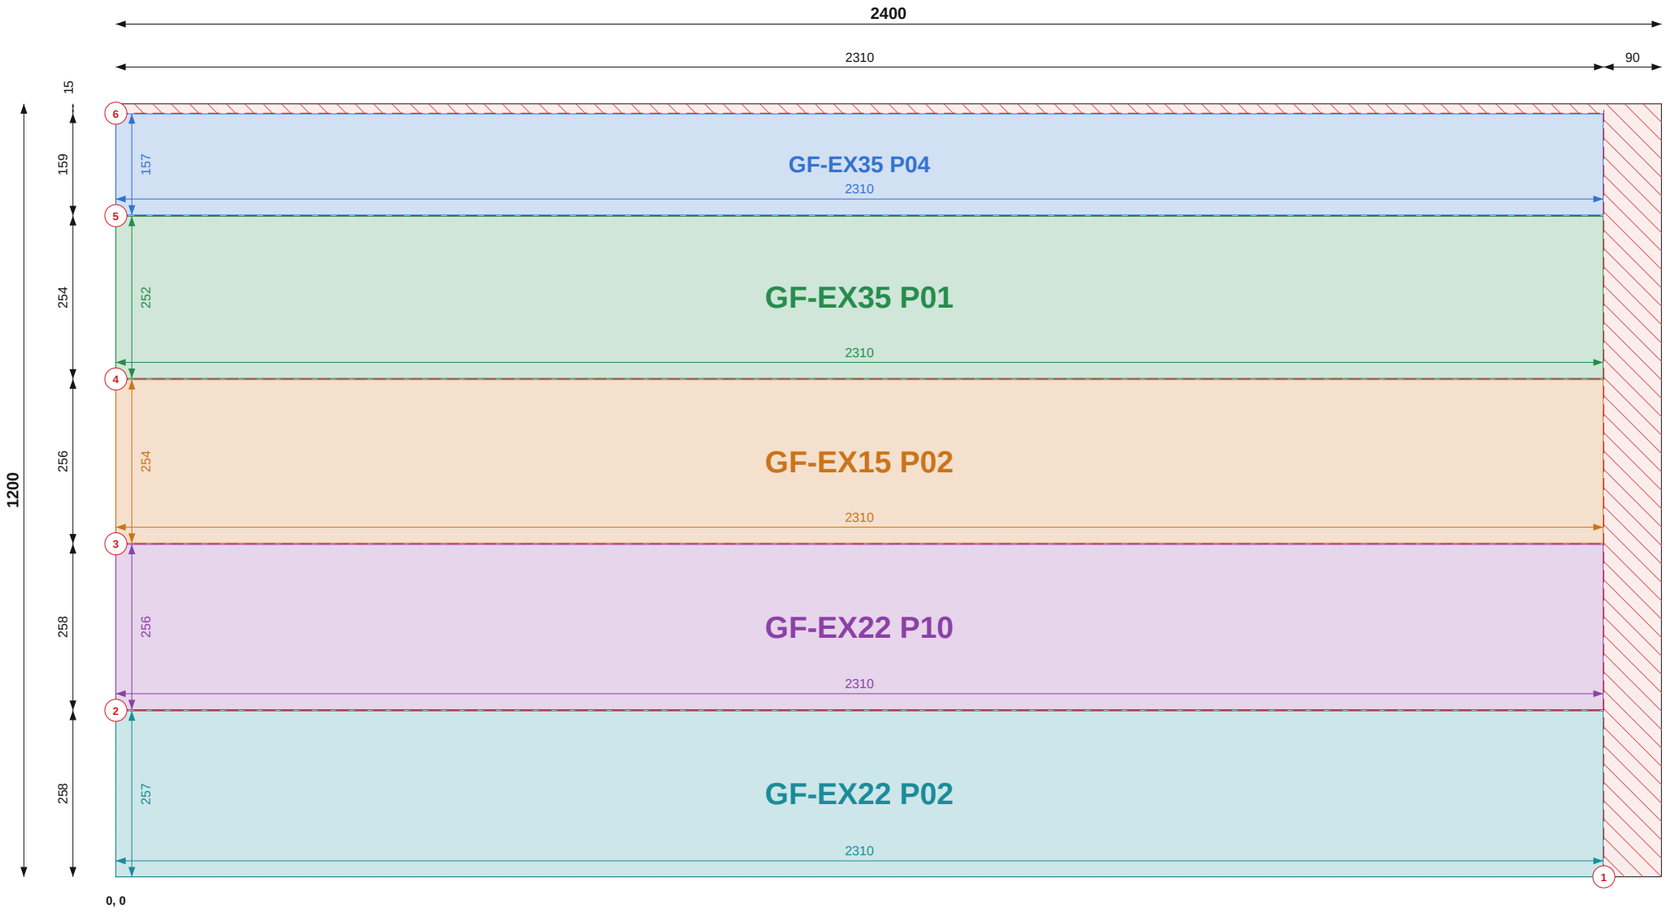

Top / left chains = saw cut positions (to cut centres). Coloured = part size and position.

Do not scale. All dimensions in mm. Check all dimensions on site.

SHEET 24 OF 33

THIS SHEET

Item	Value
Parts	5
Used / waste	94.3% / 0.16 m2
Reusable offcuts	0
Saw cuts / shared	6 / 4

PIECES (POSITION = BOTTOM-LEFT CORNER)

Label	Size	X, Y
GF-EX35 P04	157 x 2310	0, 1027
GF-EX35 P01	252 x 2310	0, 774
GF-EX15 P02	254 x 2310	0, 518
GF-EX22 P10	256 x 2310	0, 259
GF-EX22 P02	257 x 2310	0, 0

NOTES

1. Cut from PIR 120mm 1200x2400, 2mm saw kerf. Viewed on the face; dimensions from the sheet's bottom-left corner (0,0). Red numbered lines = saw cuts in order, each edge to edge.
2. Coloured dimensions belong to the part of that colour: its width and height, and its position from the sheet edges. Raked parts: corner coordinates at each corner.
3. Red hatch = waste. Labels = panel + piece mark on the manufacture drawing.

REVISIONS

REV	DATE	DESCRIPTION
C01	14.09.26	Construction issue
C02	14.09.26	Roof trusses revised; SP diagonals added

TLS TIMBER FRAME DESIGN SUITE

TLS TIMBER FRAME

Design & Manufacture

Scan: 3D model + drawings

CLIENT	PROJECT
MP Adams	MP Adams Plot 4, Eckington


DRAWING TITLE

PIR CUTTING - GROUND FLOOR - SHEET 24 OF 33

PIR 120mm 1200x2400 | Ground Floor

SCALE	SIZE	DATE	DRAWN
NTS	A3	14.09.26	TS

STATUS	DRAWING No.	REV
CONSTRUCTION	P4-CP-PIR-01 / 24	C02

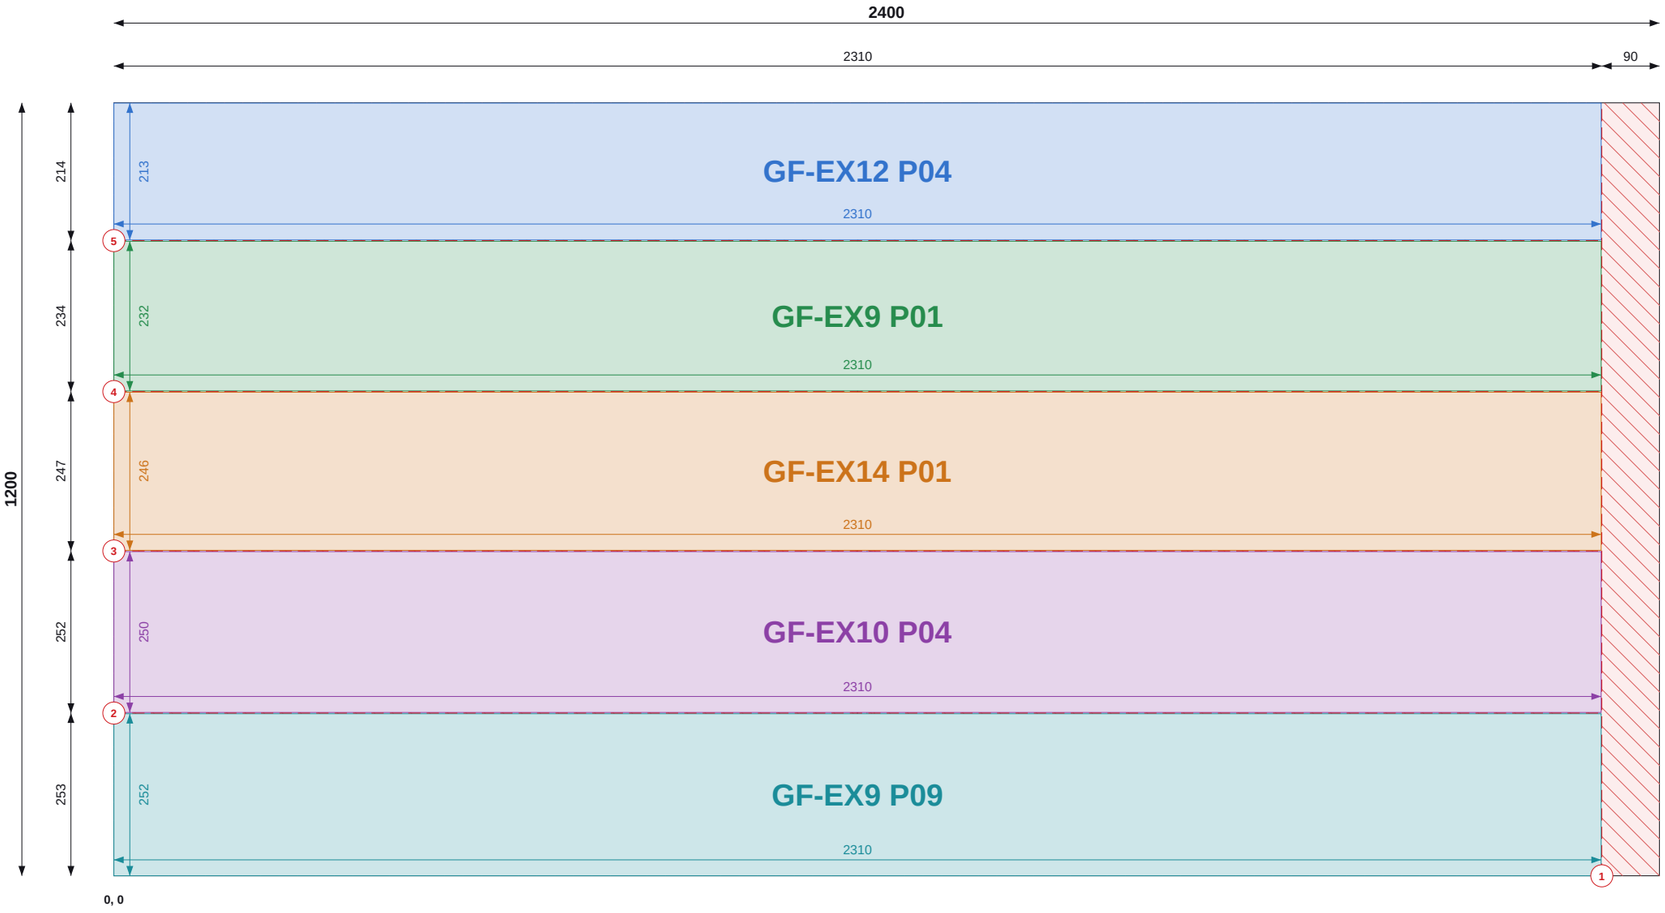

Top / left chains = saw cut positions (to cut centres). Coloured = part size and position.

Do not scale. All dimensions in mm. Check all dimensions on site.

SHEET 25 OF 33

THIS SHEET

Item	Value
Parts	5
Used / waste	95.6% / 0.13 m2
Reusable offcuts	0
Saw cuts / shared	5 / 4

PIECES (POSITION = BOTTOM-LEFT CORNER)

Label	Size	X, Y
GF-EX12 P04	213 x 2310	0, 987
GF-EX9 P01	232 x 2310	0, 753
GF-EX14 P01	246 x 2310	0, 505
GF-EX10 P04	250 x 2310	0, 254
GF-EX9 P09	252 x 2310	0, 0

NOTES

1. Cut from PIR 120mm 1200x2400, 2mm saw kerf. Viewed on the face; dimensions from the sheet's bottom-left corner (0,0). Red numbered lines = saw cuts in order, each edge to edge.
2. Coloured dimensions belong to the part of that colour: its width and height, and its position from the sheet edges. Raked parts: corner coordinates at each corner.
3. Red hatch = waste. Labels = panel + piece mark on the manufacture drawing.

REVISIONS

REV	DATE	DESCRIPTION
C01	14.09.26	Construction issue
C02	14.09.26	Roof trusses revised; SP diagonals added

TLS TIMBER FRAME
Design & Manufacture
Scan: 3D model + drawings


CLIENT	PROJECT
MP Adams	MP Adams Plot 4, Eckington

DRAWING TITLE
PIR CUTTING - GROUND FLOOR - SHEET 25 OF 33

PIR 120mm 1200x2400 | Ground Floor

SCALE	SIZE	DATE	DRAWN
NTS	A3	14.09.26	TS

STATUS	DRAWING No.	REV
CONSTRUCTION	P4-CP-PIR-01 / 25	C02

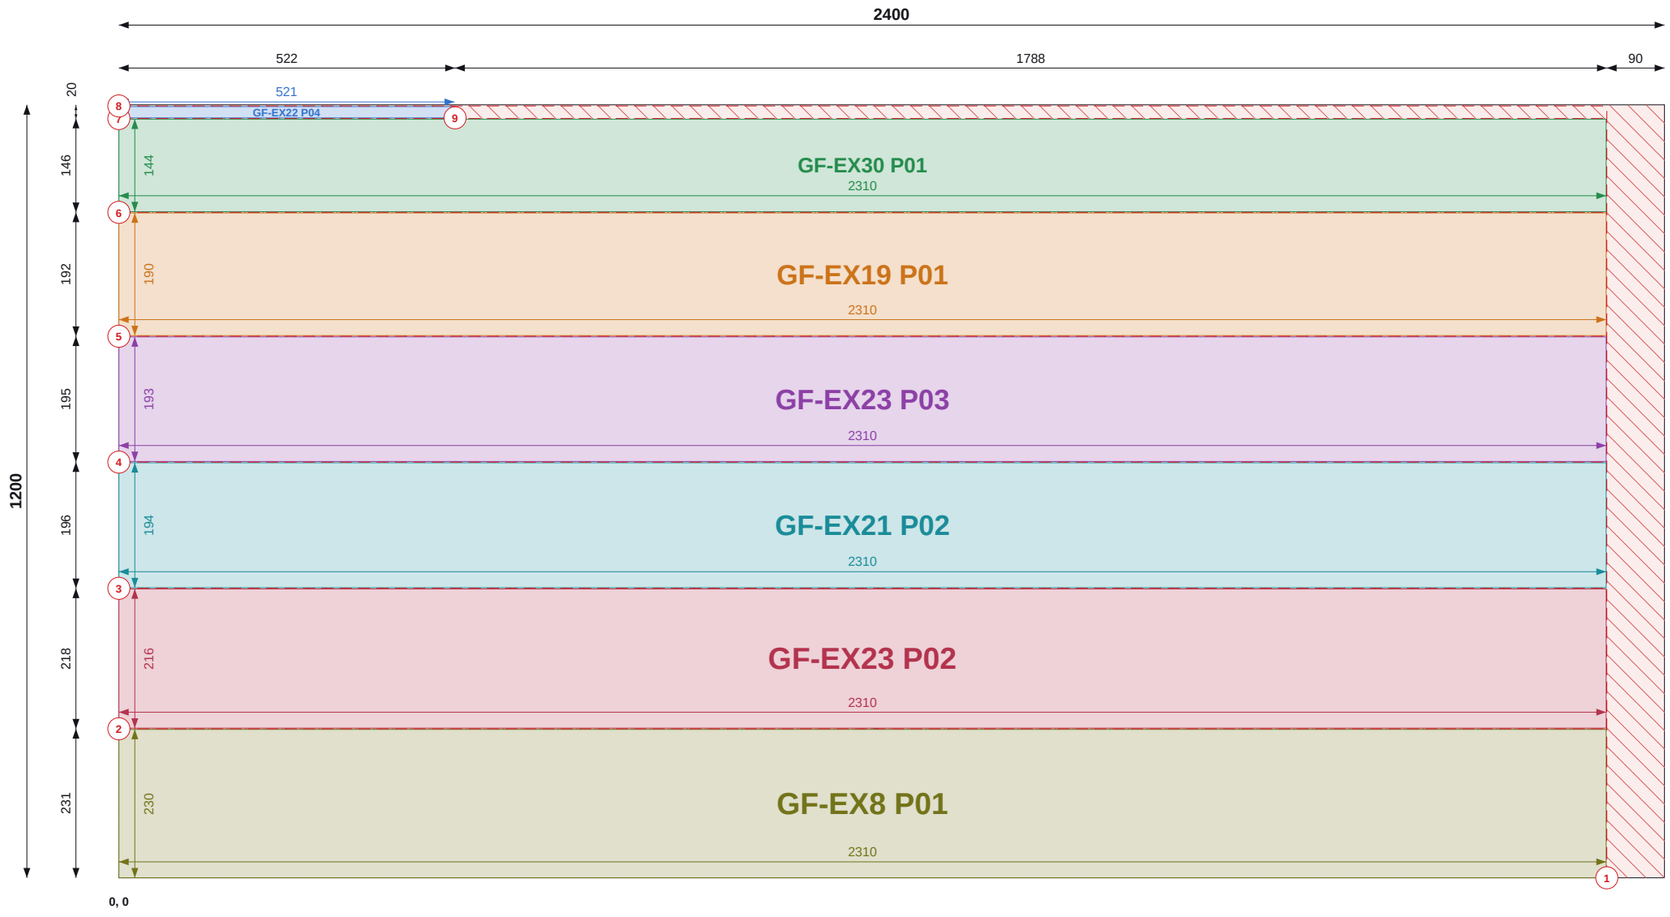

Top / left chains = saw cut positions (to cut centres). Coloured = part size and position.

SHEET 26 OF 33

THIS SHEET

Item	Value
Parts	7
Used / waste	94.0% / 0.17 m2
Reusable offcuts	0
Saw cuts / shared	9 / 6

PIECES (POSITION = BOTTOM-LEFT CORNER)

Label	Size	X, Y
GF-EX22 P04	521 x 18	0, 1180
GF-EX30 P01	144 x 2310	0, 1034
GF-EX19 P01	190 x 2310	0, 842
GF-EX23 P03	193 x 2310	0, 646
GF-EX21 P02	194 x 2310	0, 450
GF-EX23 P02	216 x 2310	0, 232
GF-EX8 P01	230 x 2310	0, 0

NOTES

1. Cut from PIR 120mm 1200x2400, 2mm saw kerf. Viewed on the face; dimensions from the sheet's bottom-left corner (0,0). Red numbered lines = saw cuts in order, each edge to edge.
2. Coloured dimensions belong to the part of that colour: its width and height, and its position from the sheet edges. Raked parts: corner coordinates at each corner.
3. Red hatch = waste. Labels = panel + piece mark on the manufacture drawing.

REVISIONS

REV	DATE	DESCRIPTION
C01	14.09.26	Construction issue
C02	14.09.26	Roof trusses revised; SP diagonals added

TLS TIMBER FRAME
Design & Manufacture
Scan: 3D model + drawings

CLIENT	PROJECT
MP Adams	MP Adams Plot 4, Eckington

DRAWING TITLE


PIR CUTTING - GROUND FLOOR - SHEET 26 OF 33

PIR 120mm 1200x2400 | Ground Floor

SCALE	SIZE	DATE	DRAWN
NTS	A3	14.09.26	TS

STATUS	DRAWING No.	REV
CONSTRUCTION	P4-CP-PIR-01 / 26	C02

Do not scale. All dimensions in mm. Check all dimensions on site.

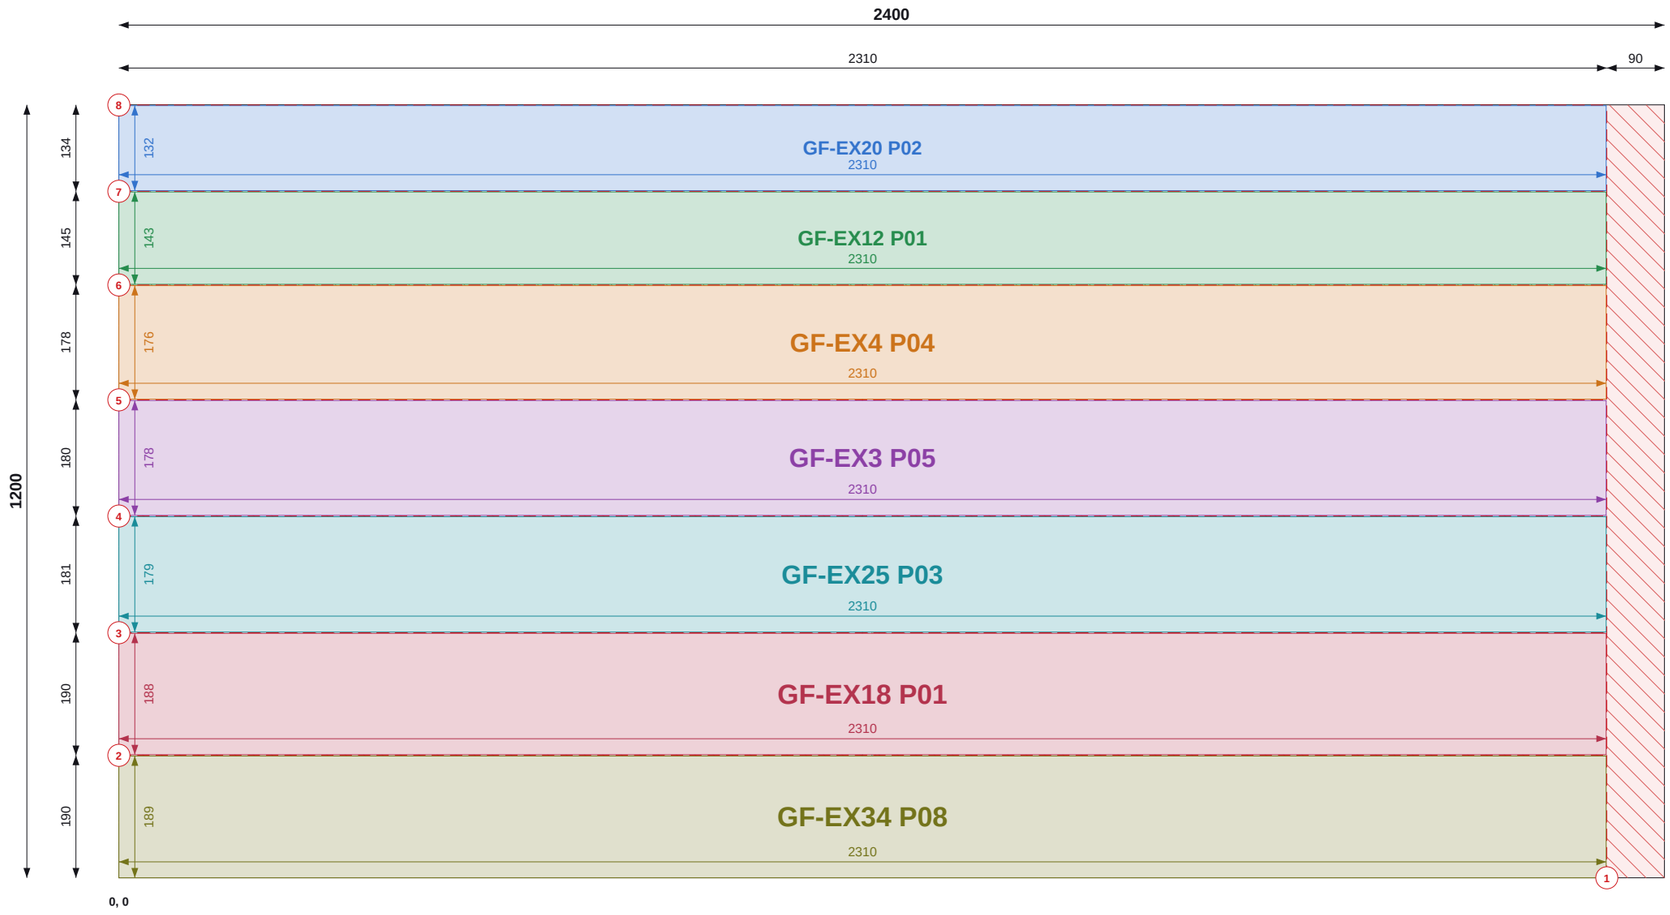

Top / left chains = saw cut positions (to cut centres). Coloured = part size and position.

SHEET 27 OF 33

THIS SHEET

Item	Value
Parts	7
Used / waste	95.2% / 0.14 m2
Reusable offcuts	0
Saw cuts / shared	8 / 6

PIECES (POSITION = BOTTOM-LEFT CORNER)

Label	Size	X, Y
GF-EX20 P02	132 x 2310	0, 1067
GF-EX12 P01	143 x 2310	0, 921
GF-EX4 P04	176 x 2310	0, 743
GF-EX3 P05	178 x 2310	0, 563
GF-EX25 P03	179 x 2310	0, 381
GF-EX18 P01	188 x 2310	0, 191
GF-EX34 P08	189 x 2310	0, 0

NOTES

1. Cut from PIR 120mm 1200x2400, 2mm saw kerf. Viewed on the face; dimensions from the sheet's bottom-left corner (0,0). Red numbered lines = saw cuts in order, each edge to edge.
2. Coloured dimensions belong to the part of that colour: its width and height, and its position from the sheet edges. Raked parts: corner coordinates at each corner.
3. Red hatch = waste. Labels = panel + piece mark on the manufacture drawing.

REVISIONS

REV	DATE	DESCRIPTION
C01	14.09.26	Construction issue
C02	14.09.26	Roof trusses revised; SP diagonals added

TLS TIMBER FRAME
Design & Manufacture
Scan: 3D model + drawings

CLIENT	PROJECT
MP Adams	MP Adams Plot 4, Eckington

DRAWING TITLE


PIR CUTTING - GROUND FLOOR - SHEET 27 OF 33

PIR 120mm 1200x2400 | Ground Floor

SCALE	SIZE	DATE	DRAWN
NTS	A3	14.09.26	TS

STATUS	DRAWING No.	REV
CONSTRUCTION	P4-CP-PIR-01 / 27	C02

Do not scale. All dimensions in mm. Check all dimensions on site.

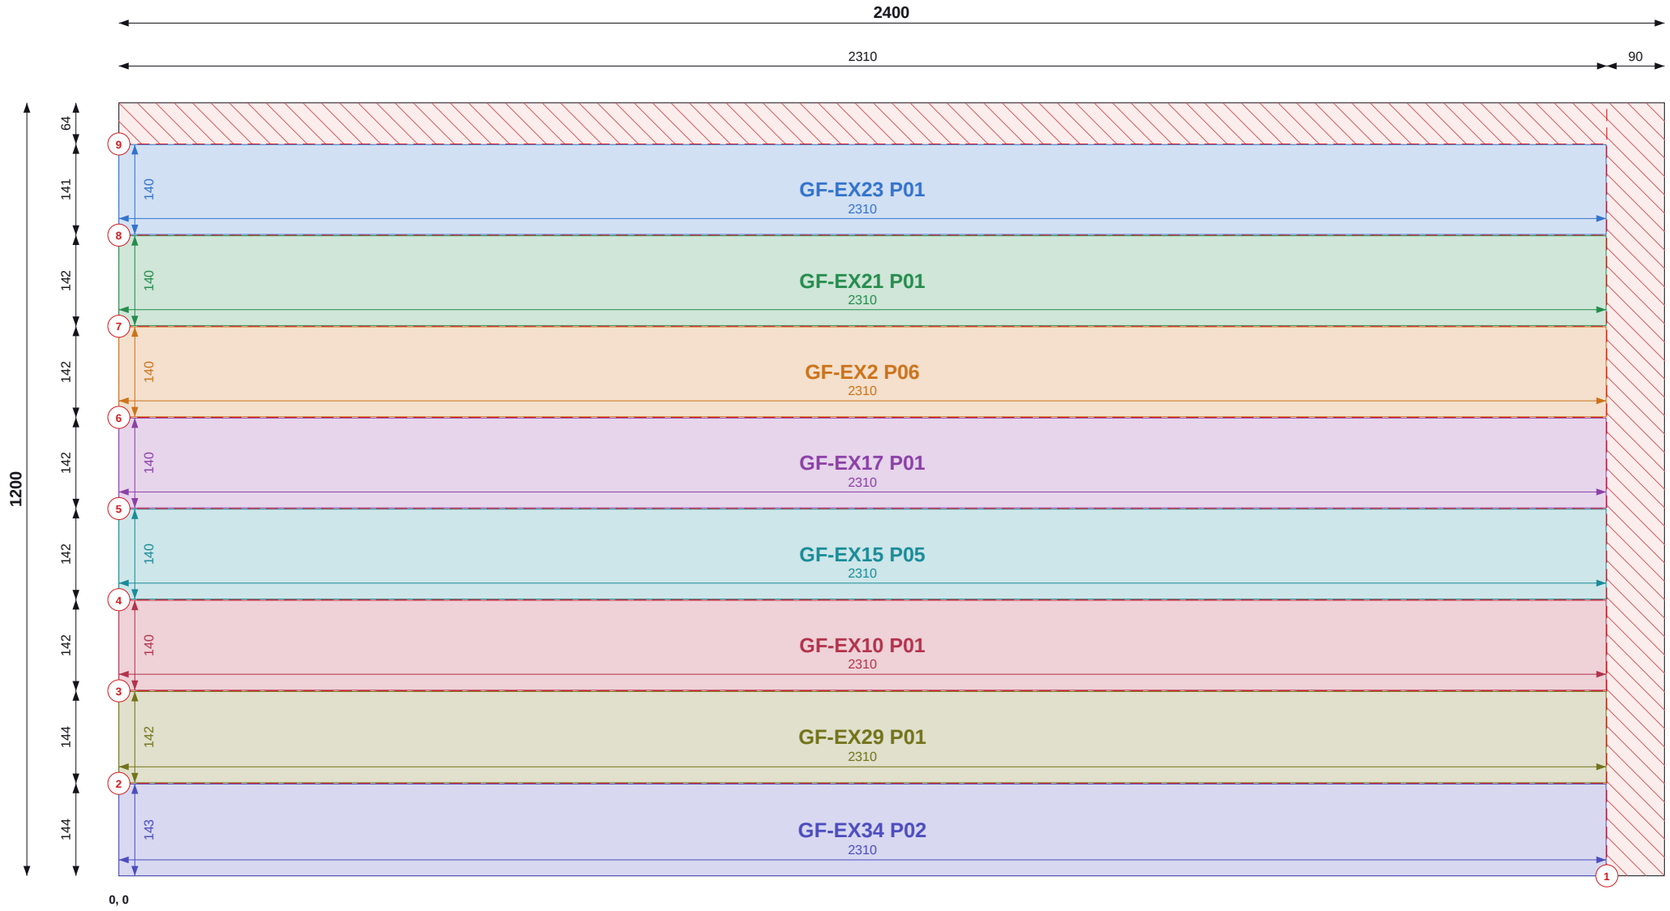

Top / left chains = saw cut positions (to cut centres). Coloured = part size and position.

SHEET 28 OF 33

THIS SHEET

Item	Value
Parts	8
Used / waste	89.9% / 0.29 m2
Reusable offcuts	0
Saw cuts / shared	9 / 7

PIECES (POSITION = BOTTOM-LEFT CORNER)

Label	Size	X, Y
GF-EX23 P01	140 x 2310	0, 996
GF-EX21 P01	140 x 2310	0, 854
GF-EX2 P06	140 x 2310	0, 713
GF-EX17 P01	140 x 2310	0, 571
GF-EX15 P05	140 x 2310	0, 430
GF-EX10 P01	140 x 2310	0, 288
GF-EX29 P01	142 x 2310	0, 145
GF-EX34 P02	143 x 2310	0, 0

NOTES

1. Cut from PIR 120mm 1200x2400, 2mm saw kerf. Viewed on the face; dimensions from the sheet's bottom-left corner (0,0). Red numbered lines = saw cuts in order, each edge to edge.
2. Coloured dimensions belong to the part of that colour: its width and height, and its position from the sheet edges. Raked parts: corner coordinates at each corner.
3. Red hatch = waste. Labels = panel + piece mark on the manufacture drawing.

REVISIONS

REV	DATE	DESCRIPTION
C01	14.09.26	Construction issue
C02	14.09.26	Roof trusses revised; SP diagonals added

TLS TIMBER FRAME
Design & Manufacture
Scan: 3D model + drawings

CLIENT	PROJECT
MP Adams	MP Adams Plot 4, Eckington


DRAWING TITLE
PIR CUTTING - GROUND FLOOR - SHEET 28 OF 33

PIR 120mm 1200x2400 | Ground Floor

SCALE	SIZE	DATE	DRAWN
NTS	A3	14.09.26	TS

STATUS	DRAWING No.	REV
CONSTRUCTION	P4-CP-PIR-01 / 28	C02

Do not scale. All dimensions in mm. Check all dimensions on site.

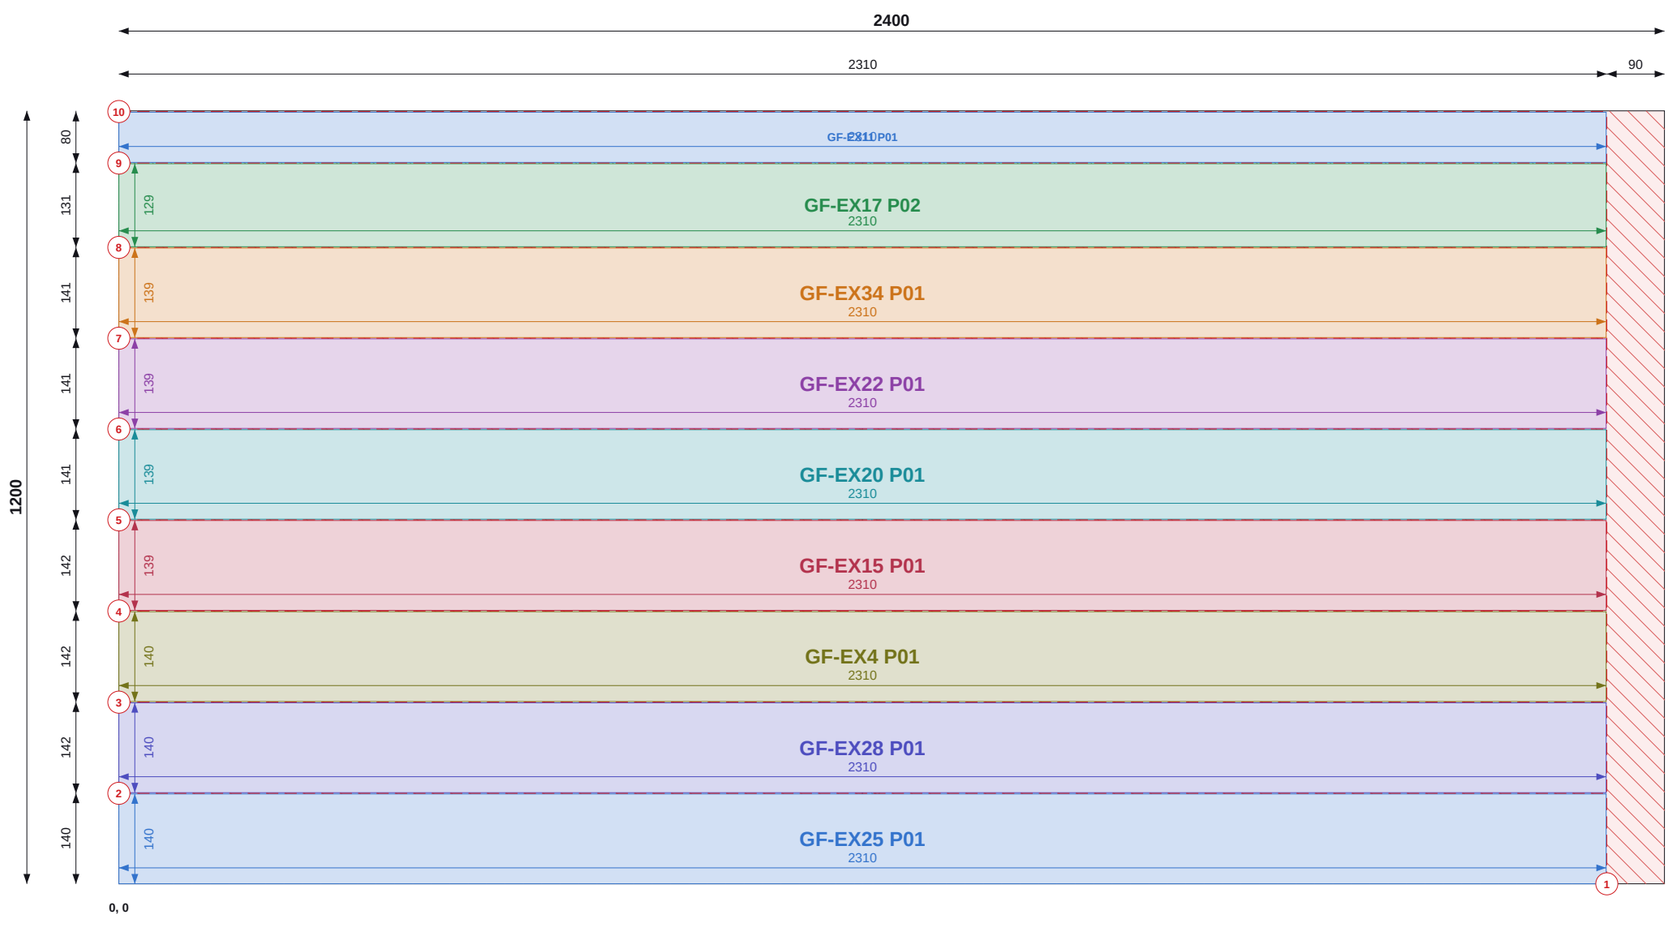

Top / left chains = saw cut positions (to cut centres). Coloured = part size and position.

SHEET 29 OF 33

THIS SHEET

Item	Value
Parts	9
Used / waste	94.8% / 0.15 m2
Reusable offcuts	0
Saw cuts / shared	10 / 8

PIECES (POSITION = BOTTOM-LEFT CORNER)

Label	Size	X, Y
GF-EX11 P01	78 x 2310	0, 1120
GF-EX17 P02	129 x 2310	0, 989
GF-EX34 P01	139 x 2310	0, 848
GF-EX22 P01	139 x 2310	0, 707
GF-EX20 P01	139 x 2310	0, 566
GF-EX15 P01	139 x 2310	0, 425
GF-EX4 P01	140 x 2310	0, 283
GF-EX28 P01	140 x 2310	0, 142
GF-EX25 P01	140 x 2310	0, 0

NOTES

1. Cut from PIR 120mm 1200x2400, 2mm saw kerf. Viewed on the face; dimensions from the sheet's bottom-left corner (0,0). Red numbered lines = saw cuts in order, each edge to edge.
2. Coloured dimensions belong to the part of that colour: its width and height, and its position from the sheet edges. Raked parts: corner coordinates at each corner.
3. Red hatch = waste. Labels = panel + piece mark on the manufacture drawing.

REVISIONS

REV	DATE	DESCRIPTION
C01	14.09.26	Construction issue
C02	14.09.26	Roof trusses revised; SP diagonals added

TLS TIMBER FRAME DESIGN SUITE

TLS TIMBER FRAME

Design & Manufacture

Scan: 3D model + drawings

CLIENT	PROJECT
MP Adams	MP Adams Plot 4, Eckington

DRAWING TITLE

PIR CUTTING - GROUND FLOOR - SHEET 29 OF 33

PIR 120mm 1200x2400 | Ground Floor

SCALE	SIZE	DATE	DRAWN
NTS	A3	14.09.26	TS

STATUS	DRAWING No.	REV
CONSTRUCTION	P4-CP-PIR-01 / 29	C02

Do not scale. All dimensions in mm. Check all dimensions on site.



Top / left chains = saw cut positions (to cut centres). Coloured = part size and position.

Do not scale. All dimensions in mm. Check all dimensions on site.

SHEET 30 OF 33

THIS SHEET

Item	Value
Parts	11
Used / waste	94.5% / 0.16 m2
Reusable offcuts	0
Saw cuts / shared	12 / 10

PIECES (POSITION = BOTTOM-LEFT CORNER)

Label	Size	X, Y
GF-EX30 P03	92 x 2310	0, 1107
GF-EX32 P08	98 x 2310	0, 1006
GF-EX28 P09	98 x 2310	0, 906
GF-EX19 P09	98 x 2310	0, 805
GF-EX36 P07	99 x 2310	0, 705
GF-EX30 P09	99 x 2310	0, 604
GF-EX28 P04	99 x 2310	0, 503
GF-EX4 P02	114 x 2310	0, 387
GF-EX28 P02	126 x 2310	0, 259
GF-EX27 P04	126 x 2310	0, 130
GF-EX26 P09	128 x 2310	0, 0

NOTES

1. Cut from PIR 120mm 1200x2400, 2mm saw kerf. Viewed on the face; dimensions from the sheet's bottom-left corner (0,0). Red numbered lines = saw cuts in order, each edge to edge.
2. Coloured dimensions belong to the part of that colour: its width and height, and its position from the sheet edges. Raked parts: corner coordinates at each corner.
3. Red hatch = waste. Labels = panel + piece mark on the manufacture drawing.

REVISIONS

REV	DATE	DESCRIPTION
C01	14.09.26	Construction issue
C02	14.09.26	Roof trusses revised; SP diagonals added

TLS TIMBER FRAME
Design & Manufacture
Scan: 3D model + drawings

CLIENT	PROJECT
MP Adams	MP Adams Plot 4, Eckington


DRAWING TITLE

PIR CUTTING - GROUND FLOOR - SHEET 30 OF 33

PIR 120mm 1200x2400 | Ground Floor

SCALE	SIZE	DATE	DRAWN
NTS	A3	14.09.26	TS

STATUS	DRAWING No.	REV
CONSTRUCTION	P4-CP-PIR-01 / 30	C02

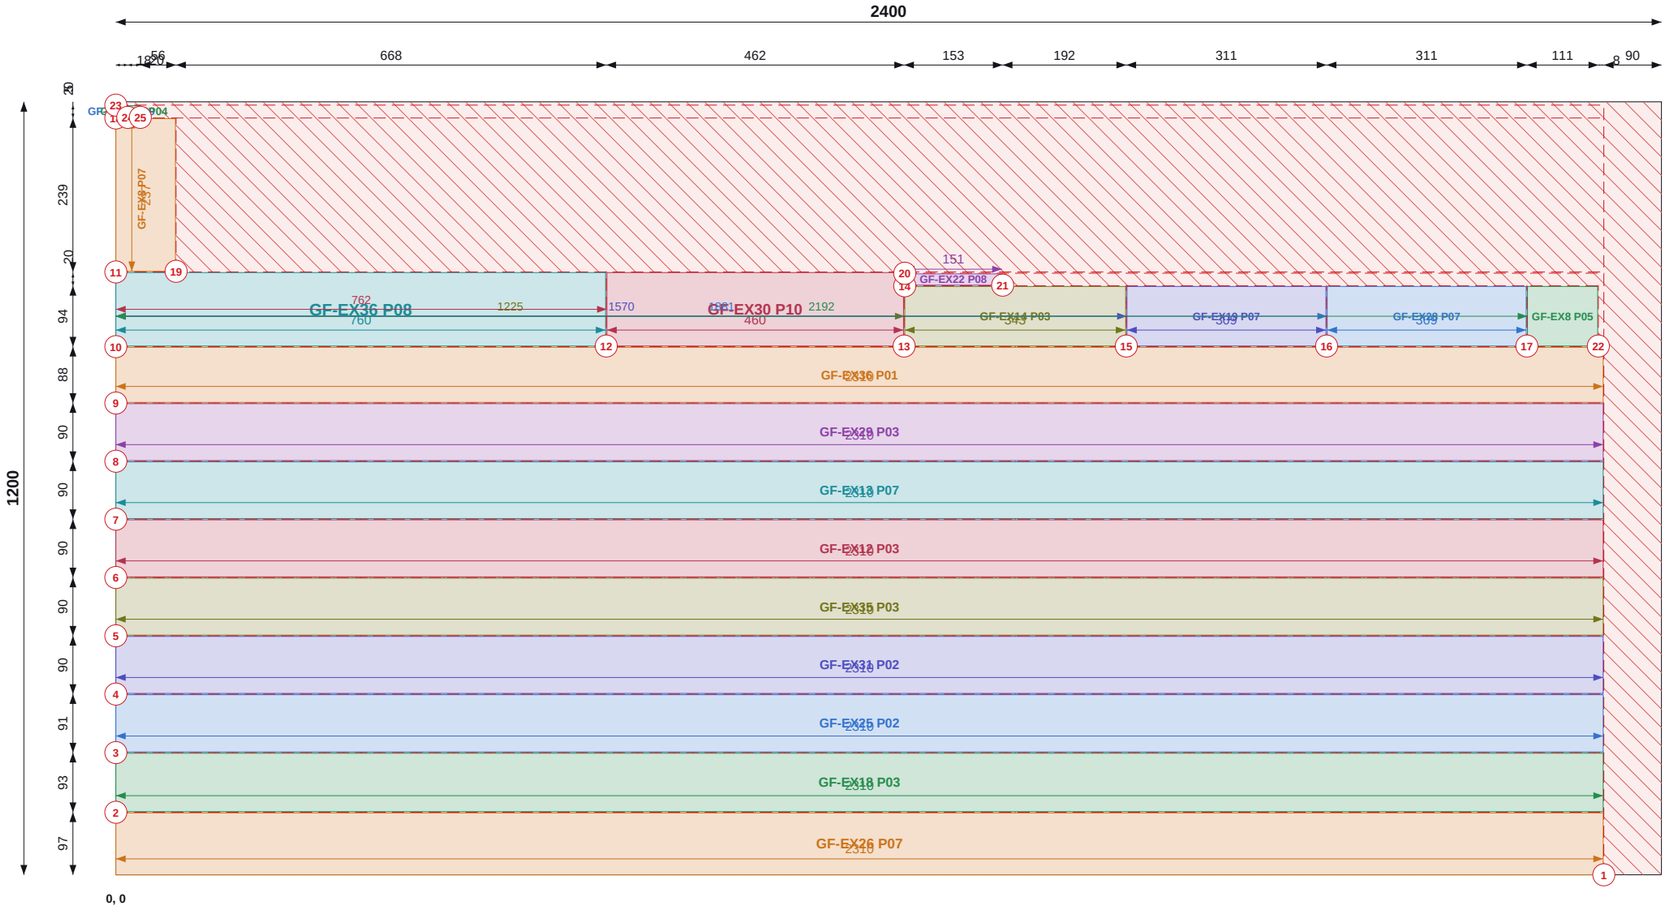

Top / left chains = saw cut positions (to cut centres). Coloured = part size and position.

Do not scale. All dimensions in mm. Check all dimensions on site.

SHEET 31 OF 33

THIS SHEET

Item	Value
Parts	19
Used / waste	73.5% / 0.76 m2
Reusable offcuts	0
Saw cuts / shared	25 / 18

PIECES (POSITION = BOTTOM-LEFT CORNER)

Label	Size	X, Y
GF-EX22 P09	18 x 18	0, 1176
GF-EX25 P04	18 x 18	20, 1176
GF-EX8 P07	237 x 93	0, 937
GF-EX22 P08	151 x 18	1225, 915
GF-EX36 P08	114 x 760	0, 821
GF-EX30 P10	114 x 460	762, 821
GF-EX14 P03	343 x 93	1225, 821
GF-EX19 P07	309 x 93	1570, 821
GF-EX28 P07	309 x 93	1881, 821
GF-EX8 P05	109 x 93	2192, 821
GF-EX36 P01	86 x 2310	0, 733
GF-EX29 P03	88 x 2310	0, 643
GF-EX13 P07	88 x 2310	0, 553
GF-EX12 P03	88 x 2310	0, 463
GF-EX35 P03	89 x 2310	0, 372
GF-EX31 P02	89 x 2310	0, 282
GF-EX25 P02	89 x 2310	0, 191
GF-EX18 P03	91 x 2310	0, 98
GF-EX26 P07	96 x 2310	0, 0

NOTES

1. Cut from PIR 120mm 1200x2400, 2mm saw kerf. Viewed on the face; dimensions from the sheet's bottom-left corner (0,0). Red numbered lines = saw cuts in order, each edge to edge.
2. Coloured dimensions belong to the part of that colour: its width and height, and its position from the sheet edges. Raked parts: corner coordinates at each corner.
3. Red hatch = waste. Labels = panel + piece mark on the manufacture drawing.

REVISIONS

REV	DATE	DESCRIPTION
C01	14.09.26	Construction issue
C02	14.09.26	Roof trusses revised; SP diagonals added

TLS TIMBER FRAME
Design & Manufacture
Scan: 3D model + drawings


CLIENT	PROJECT
MP Adams	MP Adams Plot 4, Eckington

DRAWING TITLE
PIR CUTTING - GROUND FLOOR - SHEET 31 OF 33

PIR 120mm 1200x2400 | Ground Floor

SCALE	SIZE	DATE	DRAWN
NTS	A3	14.09.26	TS

STATUS	DRAWING No.	REV
CONSTRUCTION	P4-CP-PIR-01 / 31	C02

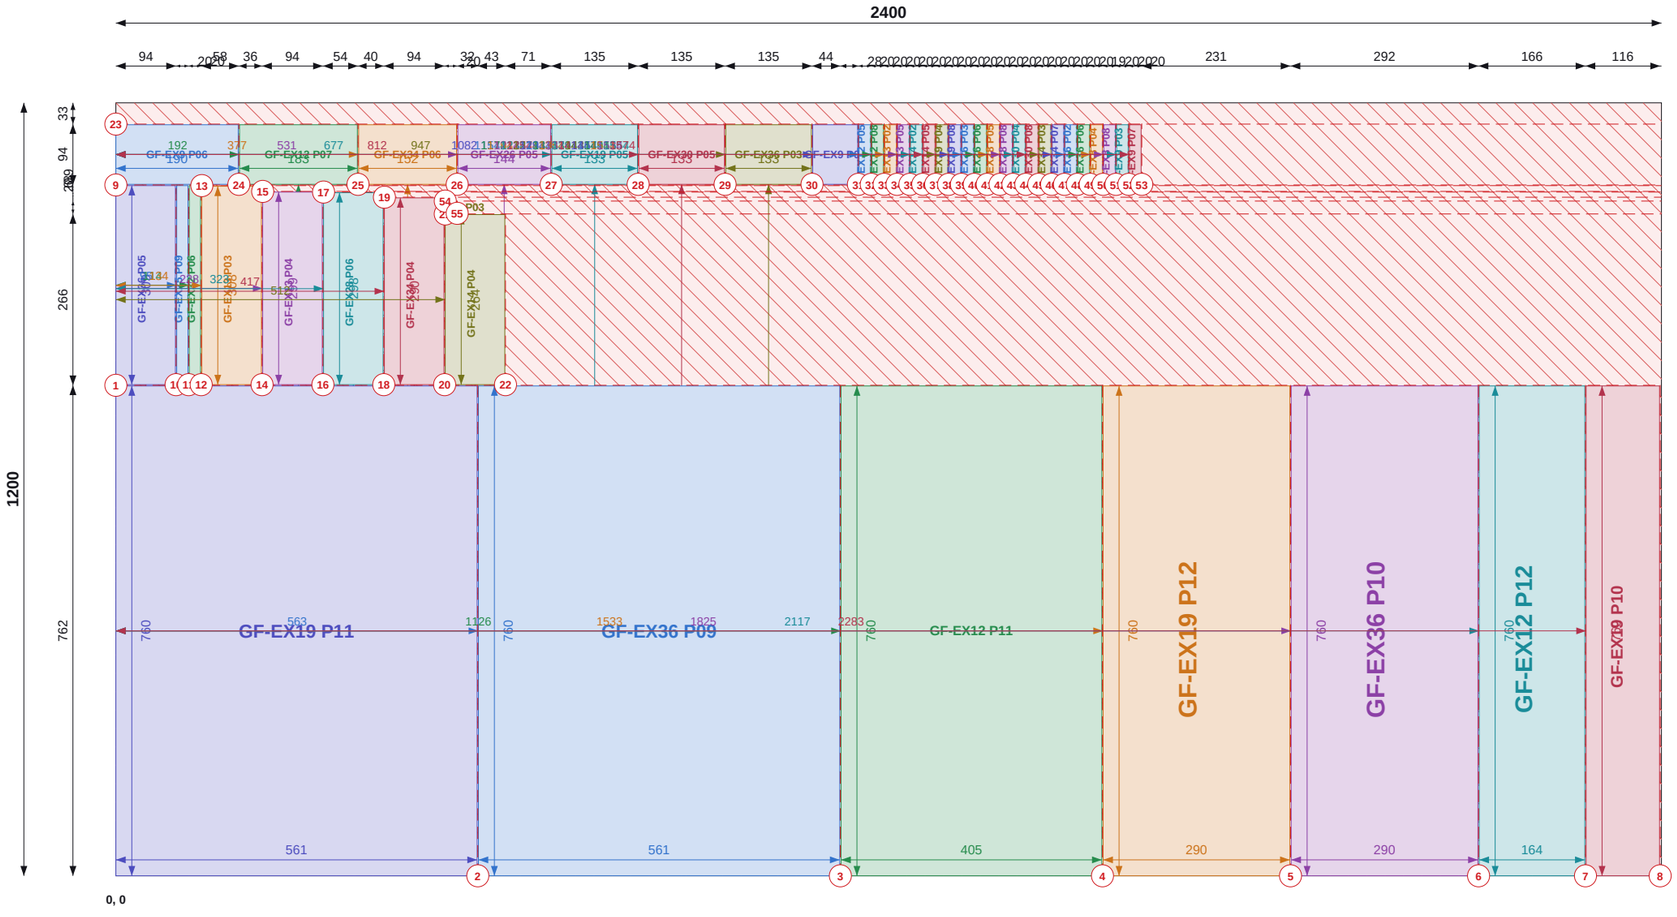

Top / left chains = saw cut positions (to cut centres). Coloured = part size and position.

SHEET 32 OF 33

THIS SHEET

Item	Value
Parts	46
Used / waste	74.0% / 0.75 m2
Reusable offcuts	0
Saw cuts / shared	55 / 45

PIECES (POSITION = BOTTOM-LEFT CORNER)

Label	Size	X, Y
GF-EX9 P06	190 x 93	0, 1074
GF-EX12 P07	183 x 93	192, 1074
GF-EX34 P06	152 x 93	377, 1074
GF-EX26 P05	144 x 93	531, 1074
GF-EX19 P05	133 x 93	677, 1074
GF-EX30 P05	133 x 93	812, 1074
GF-EX36 P03	133 x 93	947, 1074
GF-EX9 P04	70 x 93	1082, 1074
GF-EX12 P05	18 x 93	1154, 1074
GF-EX12 P08	18 x 93	1174, 1074
GF-EX13 P02	18 x 93	1194, 1074
GF-EX13 P05	18 x 93	1214, 1074
GF-EX14 P02	18 x 93	1234, 1074
GF-EX14 P05	18 x 93	1254, 1074
GF-EX19 P04	18 x 93	1274, 1074
GF-EX19 P08	18 x 93	1294, 1074
GF-EX26 P03	18 x 93	1314, 1074
GF-EX26 P06	18 x 93	1334, 1074
GF-EX28 P05	18 x 93	1354, 1074
GF-EX28 P08	18 x 93	1374, 1074
GF-EX30 P04	18 x 93	1394, 1074
GF-EX30 P08	18 x 93	1414, 1074
GF-EX34 P03	18 x 93	1434, 1074
GF-EX34 P07	18 x 93	1454, 1074
GF-EX36 P02	18 x 93	1474, 1074
GF-EX36 P06	18 x 93	1494, 1074
GF-EX8 P04	18 x 93	1514, 1074
GF-EX8 P08	18 x 93	1534, 1074
GF-EX9 P03	18 x 93	1554, 1074
GF-EX9 P07	18 x 93	1574, 1074
GF-EX22 P03	18 x 18	512, 1028
GF-EX36 P05	309 x 93	0, 762
GF-EX25 P09	309 x 18	95, 762
GF-EX32 P06	309 x 18	114, 762
GF-EX13 P03	308 x 93	134, 762
GF-EX13 P04	299 x 93	228, 762
GF-EX28 P06	298 x 93	323, 762
GF-EX34 P04	290 x 93	417, 762
GF-EX14 P04	264 x 93	512, 762
GF-EX19 P11	561 x 760	0, 0
GF-EX36 P09	561 x 760	563, 0
GF-EX12 P11	405 x 760	1126, 0
GF-EX19 P12	290 x 760	1533, 0
GF-EX36 P10	290 x 760	1825, 0
GF-EX12 P12	164 x 760	2117, 0
GF-EX19 P10	114 x 760	2283, 0

NOTES

1. Cut from PIR 120mm 1200x2400, 2mm saw kerf. Viewed on the face; dimensions from the sheet's bottom-left corner (0,0). Red numbered lines = saw cuts in order, each edge to edge.
2. Coloured dimensions belong to the part of that colour: its width and height, and its position from the sheet edges. Raked parts: corner coordinates at each corner.
3. Red hatch = waste. Labels = panel + piece mark on the manufacture drawing.

REVISIONS

REV	DATE	DESCRIPTION
C01	14.09.26	Construction issue
C02	14.09.26	Roof trusses revised; SP diagonals added

TLS TIMBER FRAME
Design & Manufacture
Scan: 3D model + drawings

CLIENT	PROJECT
MP Adams	MP Adams Plot 4, Eckington

DRAWING TITLE


PIR CUTTING - GROUND FLOOR - SHEET 32 OF 33

PIR 120mm 1200x2400 | Ground Floor

SCALE	SIZE	DATE	DRAWN
NTS	A3	14.09.26	TS

STATUS	DRAWING No.	REV
CONSTRUCTION	P4-CP-PIR-01 / 32	C02

Do not scale. All dimensions in mm. Check all dimensions on site.

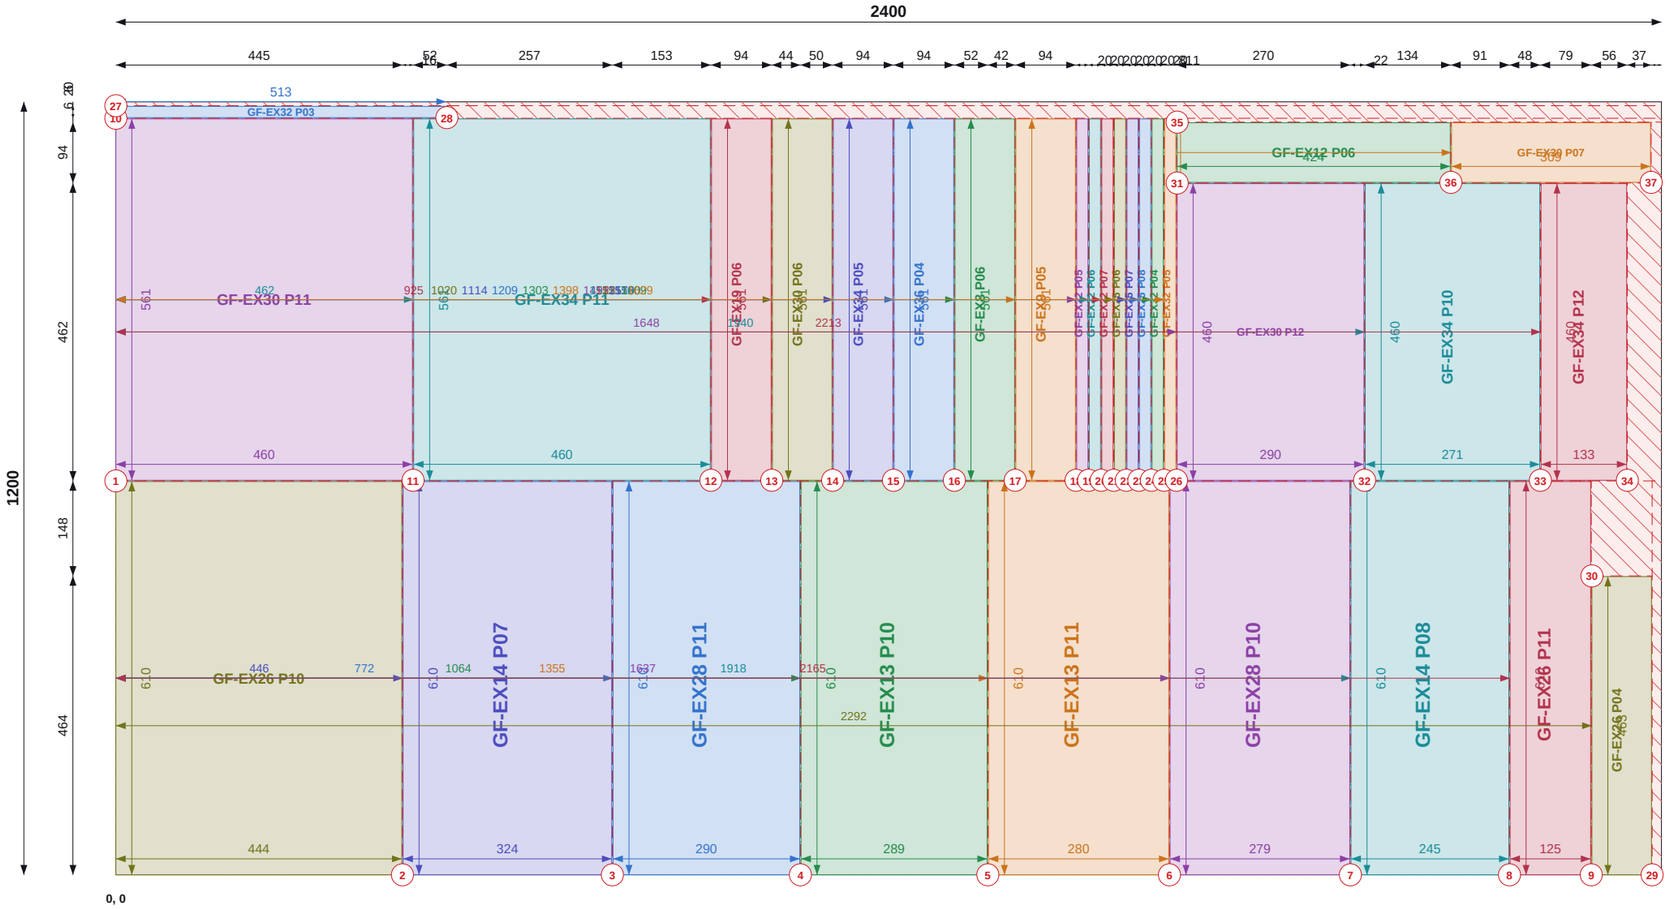

Top / left chains = saw cut positions (to cut centres). Coloured = part size and position.

SHEET 33 OF 33

THIS SHEET

Item	Value
Parts	31
Used / waste	95.0% / 0.14 m2
Reusable offcuts	0
Saw cuts / shared	37 / 30

PIECES (POSITION = BOTTOM-LEFT CORNER)

Label	Size	X, Y
GF-EX32 P03	513 x 18	0, 1175
GF-EX12 P06	424 x 93	1648, 1075
GF-EX30 P07	309 x 93	2074, 1075
GF-EX30 P11	561 x 460	0, 612
GF-EX34 P11	561 x 460	462, 612
GF-EX19 P06	561 x 93	925, 612
GF-EX30 P06	561 x 93	1020, 612
GF-EX34 P05	561 x 93	1114, 612
GF-EX36 P04	561 x 93	1209, 612
GF-EX8 P06	561 x 93	1303, 612
GF-EX9 P05	561 x 93	1398, 612
GF-EX22 P05	561 x 18	1492, 612
GF-EX22 P06	561 x 18	1512, 612
GF-EX22 P07	561 x 18	1531, 612
GF-EX25 P06	561 x 18	1551, 612
GF-EX25 P07	561 x 18	1570, 612
GF-EX25 P08	561 x 18	1590, 612
GF-EX32 P04	561 x 18	1609, 612
GF-EX32 P05	561 x 18	1629, 612
GF-EX30 P12	290 x 460	1648, 612
GF-EX34 P10	271 x 460	1940, 612
GF-EX34 P12	133 x 460	2213, 612
GF-EX26 P10	444 x 610	0, 0
GF-EX14 P07	324 x 610	446, 0
GF-EX28 P11	290 x 610	772, 0
GF-EX13 P10	289 x 610	1064, 0
GF-EX13 P11	280 x 610	1355, 0
GF-EX28 P10	279 x 610	1637, 0
GF-EX14 P08	245 x 610	1918, 0
GF-EX26 P11	125 x 610	2165, 0
GF-EX26 P04	463 x 93	2292, 0

NOTES

1. Cut from PIR 120mm 1200x2400, 2mm saw kerf. Viewed on the face; dimensions from the sheet's bottom-left corner (0,0). Red numbered lines = saw cuts in order, each edge to edge.
2. Coloured dimensions belong to the part of that colour: its width and height, and its position from the sheet edges. Raked parts: corner coordinates at each corner.
3. Red hatch = waste. Labels = panel + piece mark on the manufacture drawing.

REVISIONS

REV	DATE	DESCRIPTION
C01	14.09.26	Construction issue
C02	14.09.26	Roof trusses revised; SP diagonals added

TLS TIMBER FRAME
Design & Manufacture
Scan: 3D model + drawings

CLIENT	PROJECT
MP Adams	MP Adams Plot 4, Eckington


DRAWING TITLE
PIR CUTTING - GROUND FLOOR - SHEET 33 OF 33

PIR 120mm 1200x2400 | Ground Floor

SCALE	SIZE	DATE	DRAWN
NTS	A3	14.09.26	TS

STATUS	DRAWING No.	REV
CONSTRUCTION	P4-CP-PIR-01 / 33	C02

Do not scale. All dimensions in mm. Check all dimensions on site.

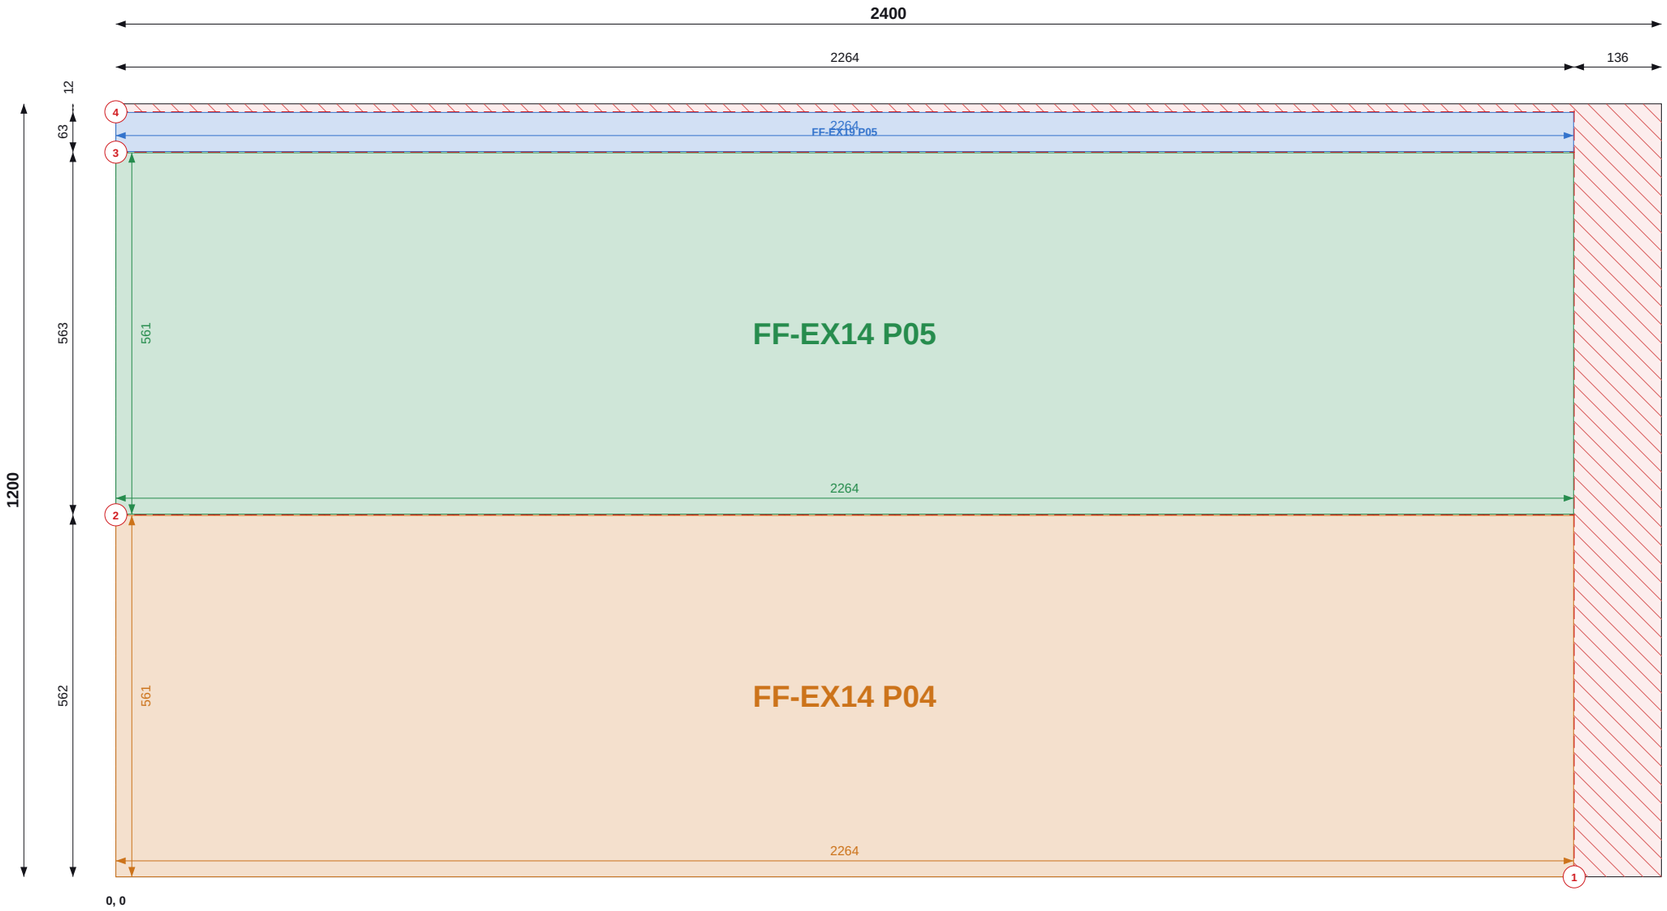

Top / left chains = saw cut positions (to cut centres). Coloured = part size and position.

Do not scale. All dimensions in mm. Check all dimensions on site.

SHEET 1 OF 23

THIS SHEET

Item	Value
Parts	3
Used / waste	92.9% / 0.20 m2
Reusable offcuts	0
Saw cuts / shared	4 / 2

PIECES (POSITION = BOTTOM-LEFT CORNER)

Label	Size	X, Y
FF-EX19 P05	61 x 2264	0, 1126
FF-EX14 P05	561 x 2264	0, 563
FF-EX14 P04	561 x 2264	0, 0

FIRST FLOOR TOTALS

Item	Value
Sheets / pieces	23 / 148
Yield / waste	90.0% / 6.64 m2
Saw cuts / shared / on stock edge	175 / 125 / 137

NOTES

1. Cut from PIR 120mm 1200x2400, 2mm saw kerf. Viewed on the face; dimensions from the sheet's bottom-left corner (0,0). Red numbered lines = saw cuts in order, each edge to edge.
2. Coloured dimensions belong to the part of that colour: its width and height, and its position from the sheet edges. Raked parts: corner coordinates at each corner.
3. Red hatch = waste. Labels = panel + piece mark on the manufacture drawing.

REVISIONS

REV	DATE	DESCRIPTION
C01	14.09.26	Construction issue
C02	14.09.26	Roof trusses revised; SP diagonals added

TLS TIMBER FRAME
Design & Manufacture
Scan: 3D model + drawings


CLIENT	PROJECT
MP Adams	MP Adams Plot 4, Eckington

DRAWING TITLE
PIR CUTTING - FIRST FLOOR - SHEET 1 OF 23

PIR 120mm 1200x2400 | First Floor

SCALE	SIZE	DATE	DRAWN
NTS	A3	14.09.26	TS

STATUS	DRAWING No.	REV
CONSTRUCTION	P4-CP-PIR-02 / 01	C02

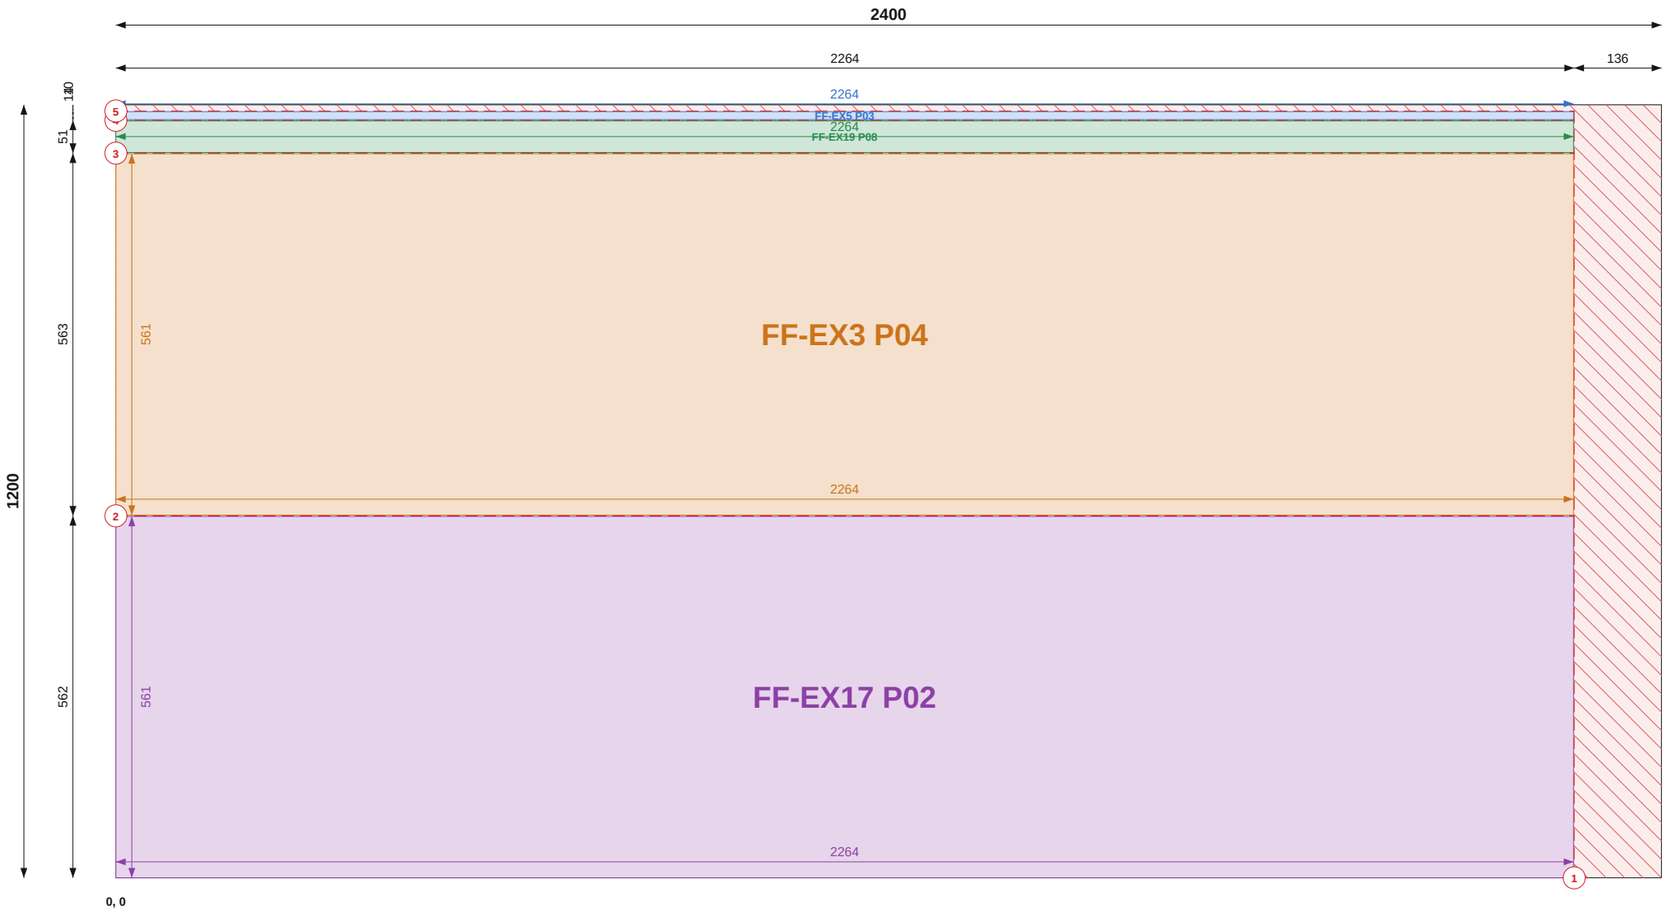

Top / left chains = saw cut positions (to cut centres). Coloured = part size and position.

Do not scale. All dimensions in mm. Check all dimensions on site.

SHEET 2 OF 23

THIS SHEET

Item	Value
Parts	4
Used / waste	93.0% / 0.20 m2
Reusable offcuts	0
Saw cuts / shared	5 / 3

PIECES (POSITION = BOTTOM-LEFT CORNER)

Label	Size	X, Y
FF-EX5 P03	12 x 2264	0, 1177
FF-EX19 P08	49 x 2264	0, 1126
FF-EX3 P04	561 x 2264	0, 563
FF-EX17 P02	561 x 2264	0, 0

NOTES

1. Cut from PIR 120mm 1200x2400, 2mm saw kerf. Viewed on the face; dimensions from the sheet's bottom-left corner (0,0). Red numbered lines = saw cuts in order, each edge to edge.
2. Coloured dimensions belong to the part of that colour: its width and height, and its position from the sheet edges. Raked parts: corner coordinates at each corner.
3. Red hatch = waste. Labels = panel + piece mark on the manufacture drawing.

REVISIONS

REV	DATE	DESCRIPTION
C01	14.09.26	Construction issue
C02	14.09.26	Roof trusses revised; SP diagonals added

TLS TIMBER FRAME
Design & Manufacture
Scan: 3D model + drawings

CLIENT	PROJECT
MP Adams	MP Adams Plot 4, Eckington


DRAWING TITLE

PIR CUTTING - FIRST FLOOR - SHEET 2 OF 23

PIR 120mm 1200x2400 | First Floor

SCALE	SIZE	DATE	DRAWN
NTS	A3	14.09.26	TS

STATUS	DRAWING No.	REV
CONSTRUCTION	P4-CP-PIR-02 / 02	C02

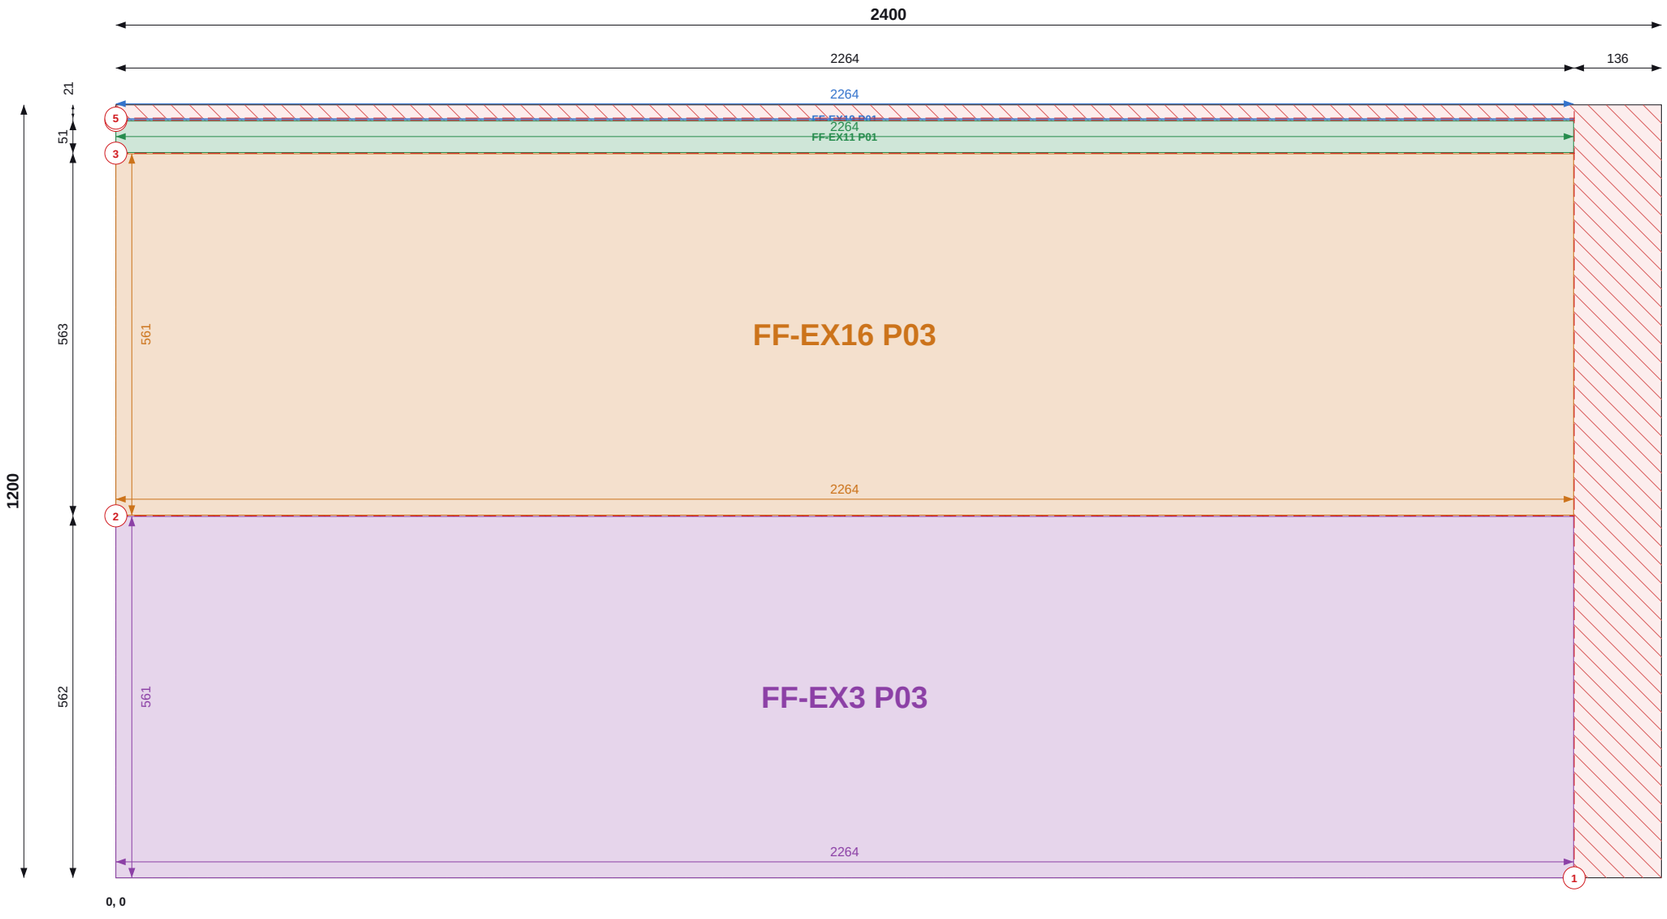

Top / left chains = saw cut positions (to cut centres). Coloured = part size and position.

SHEET 3 OF 23

THIS SHEET

Item	Value
Parts	4
Used / waste	92.1% / 0.23 m2
Reusable offcuts	0
Saw cuts / shared	5 / 3

PIECES (POSITION = BOTTOM-LEFT CORNER)

Label	Size	X, Y
FF-EX19 P01	1 x 2264	0, 1177
FF-EX11 P01	49 x 2264	0, 1126
FF-EX16 P03	561 x 2264	0, 563
FF-EX3 P03	561 x 2264	0, 0

NOTES

1. Cut from PIR 120mm 1200x2400, 2mm saw kerf. Viewed on the face; dimensions from the sheet's bottom-left corner (0,0). Red numbered lines = saw cuts in order, each edge to edge.
2. Coloured dimensions belong to the part of that colour: its width and height, and its position from the sheet edges. Raked parts: corner coordinates at each corner.
3. Red hatch = waste. Labels = panel + piece mark on the manufacture drawing.

REVISIONS

REV	DATE	DESCRIPTION
C01	14.09.26	Construction issue
C02	14.09.26	Roof trusses revised; SP diagonals added

TLS TIMBER FRAME
Design & Manufacture
Scan: 3D model + drawings

CLIENT	PROJECT
MP Adams	MP Adams Plot 4, Eckington

DRAWING TITLE


PIR CUTTING - FIRST FLOOR - SHEET 3 OF 23

PIR 120mm 1200x2400 | First Floor

SCALE	SIZE	DATE	DRAWN
NTS	A3	14.09.26	TS

STATUS	DRAWING No.	REV
CONSTRUCTION	P4-CP-PIR-02 / 03	C02

Do not scale. All dimensions in mm. Check all dimensions on site.

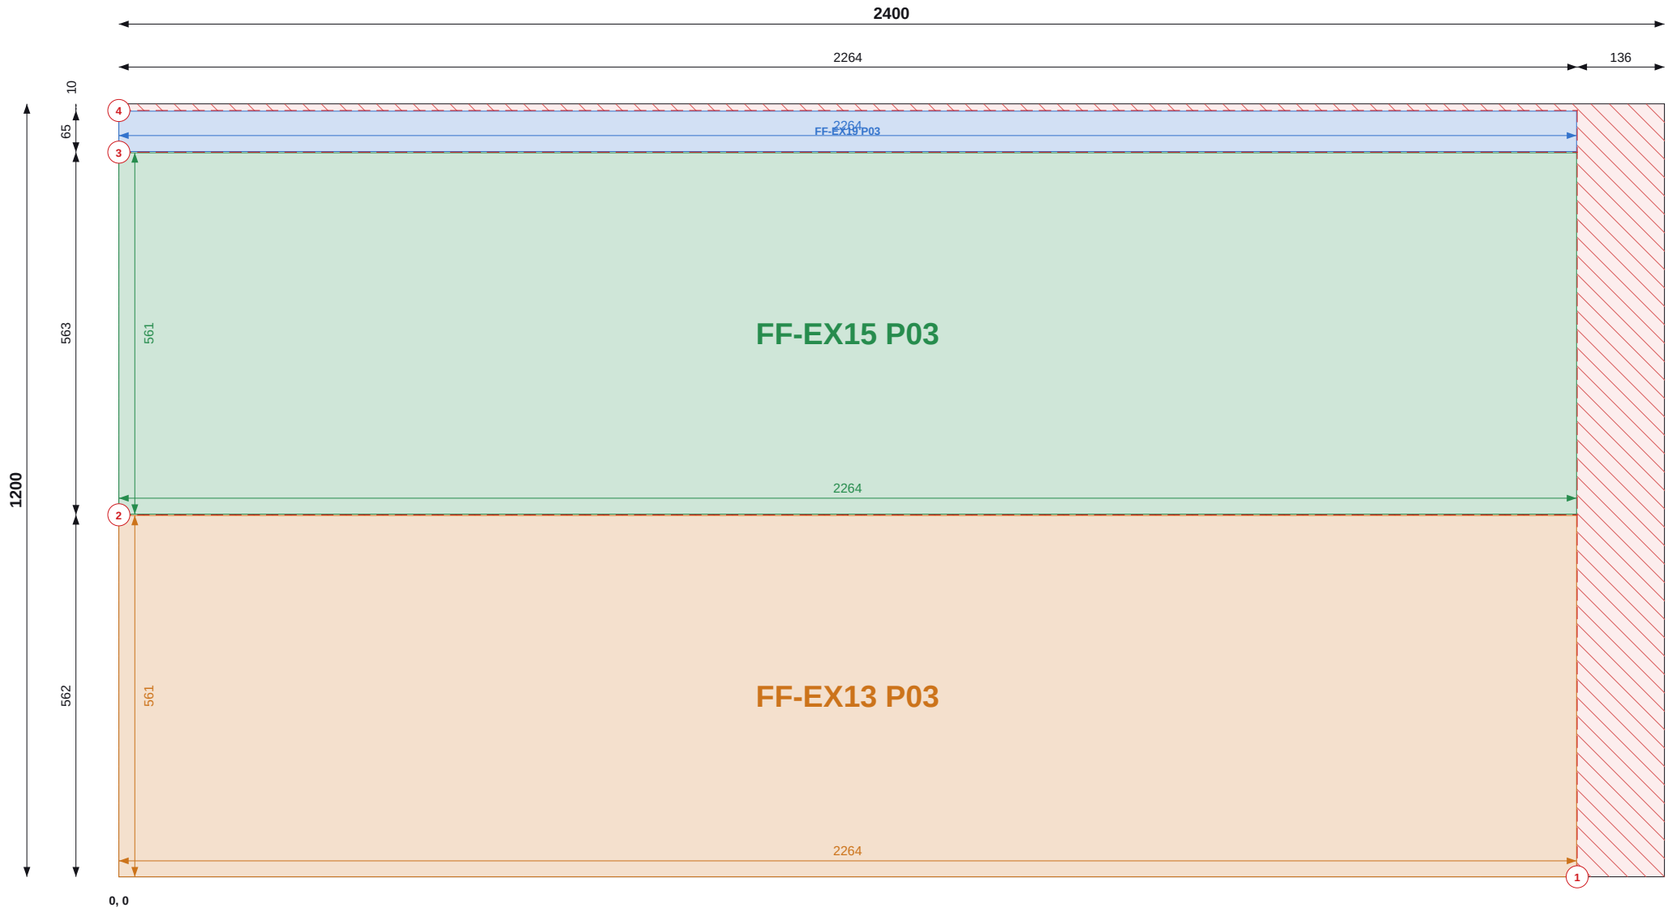

Top / left chains = saw cut positions (to cut centres). Coloured = part size and position.

SHEET 4 OF 23

THIS SHEET

Item	Value
Parts	3
Used / waste	93.1% / 0.20 m2
Reusable offcuts	0
Saw cuts / shared	4 / 2

PIECES (POSITION = BOTTOM-LEFT CORNER)

Label	Size	X, Y
FF-EX19 P03	63 x 2264	0, 1126
FF-EX15 P03	561 x 2264	0, 563
FF-EX13 P03	561 x 2264	0, 0

NOTES

1. Cut from PIR 120mm 1200x2400, 2mm saw kerf. Viewed on the face; dimensions from the sheet's bottom-left corner (0,0). Red numbered lines = saw cuts in order, each edge to edge.
2. Coloured dimensions belong to the part of that colour: its width and height, and its position from the sheet edges. Raked parts: corner coordinates at each corner.
3. Red hatch = waste. Labels = panel + piece mark on the manufacture drawing.

REVISIONS

REV	DATE	DESCRIPTION
C01	14.09.26	Construction issue
C02	14.09.26	Roof trusses revised; SP diagonals added

TLS TIMBER FRAME
Design & Manufacture
Scan: 3D model + drawings

CLIENT	PROJECT
MP Adams	MP Adams Plot 4, Eckington


DRAWING TITLE
PIR CUTTING - FIRST FLOOR - SHEET 4 OF 23

PIR 120mm 1200x2400 | First Floor

SCALE	SIZE	DATE	DRAWN
NTS	A3	14.09.26	TS

STATUS	DRAWING No.	REV
CONSTRUCTION	P4-CP-PIR-02 / 04	C02

Do not scale. All dimensions in mm. Check all dimensions on site.

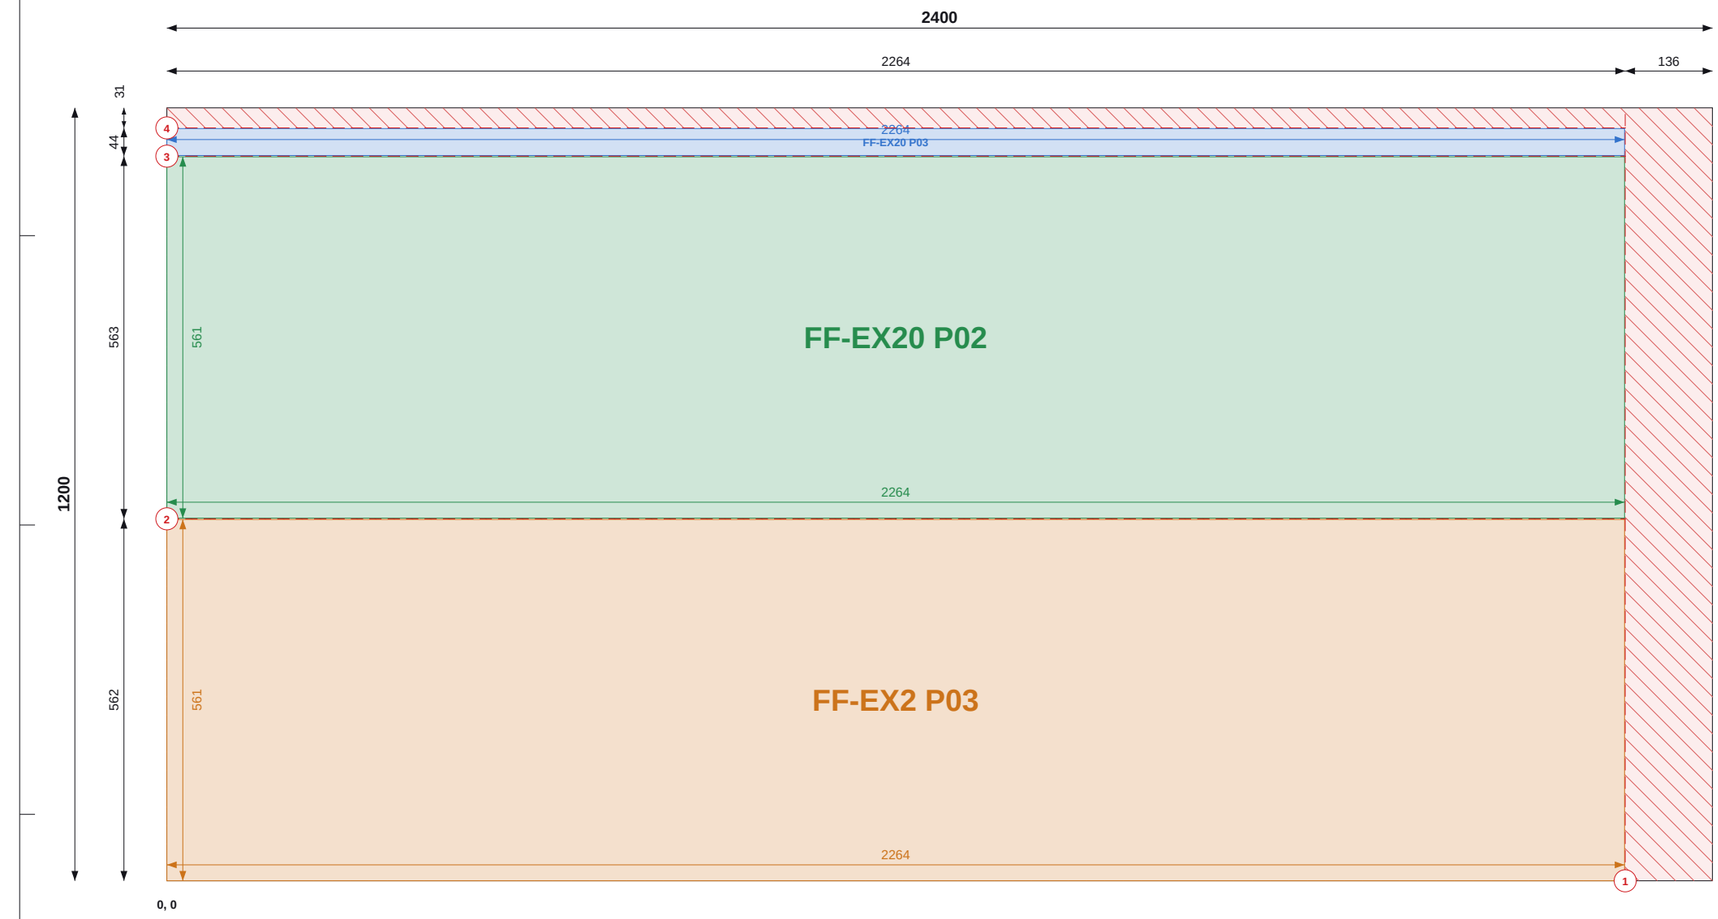

Top / left chains = saw cut positions (to cut centres). Coloured = part size and position.

SHEET 5 OF 23

THIS SHEET

Item	Value
Parts	3
Used / waste	91.5% / 0.25 m2
Reusable offcuts	0
Saw cuts / shared	4 / 2

PIECES (POSITION = BOTTOM-LEFT CORNER)

Label	Size	X, Y
FF-EX20 P03	42 x 2264	0, 1126
FF-EX20 P02	561 x 2264	0, 563
FF-EX2 P03	561 x 2264	0, 0

NOTES

1. Cut from PIR 120mm 1200x2400, 2mm saw kerf. Viewed on the face; dimensions from the sheet's bottom-left corner (0,0). Red numbered lines = saw cuts in order, each edge to edge.
2. Coloured dimensions belong to the part of that colour: its width and height, and its position from the sheet edges. Raked parts: corner coordinates at each corner.
3. Red hatch = waste. Labels = panel + piece mark on the manufacture drawing.

REVISIONS

REV	DATE	DESCRIPTION
C01	14.09.26	Construction issue
C02	14.09.26	Roof trusses revised; SP diagonals added

TLS TIMBER FRAME
Design & Manufacture
Scan: 3D model + drawings

CLIENT	PROJECT
MP Adams	MP Adams Plot 4, Eckington


DRAWING TITLE
PIR CUTTING - FIRST FLOOR - SHEET 5 OF 23

PIR 120mm 1200x2400 | First Floor

SCALE	SIZE	DATE	DRAWN
NTS	A3	14.09.26	TS

STATUS	DRAWING No.	REV
CONSTRUCTION	P4-CP-PIR-02 / 05	C02

Do not scale. All dimensions in mm. Check all dimensions on site.

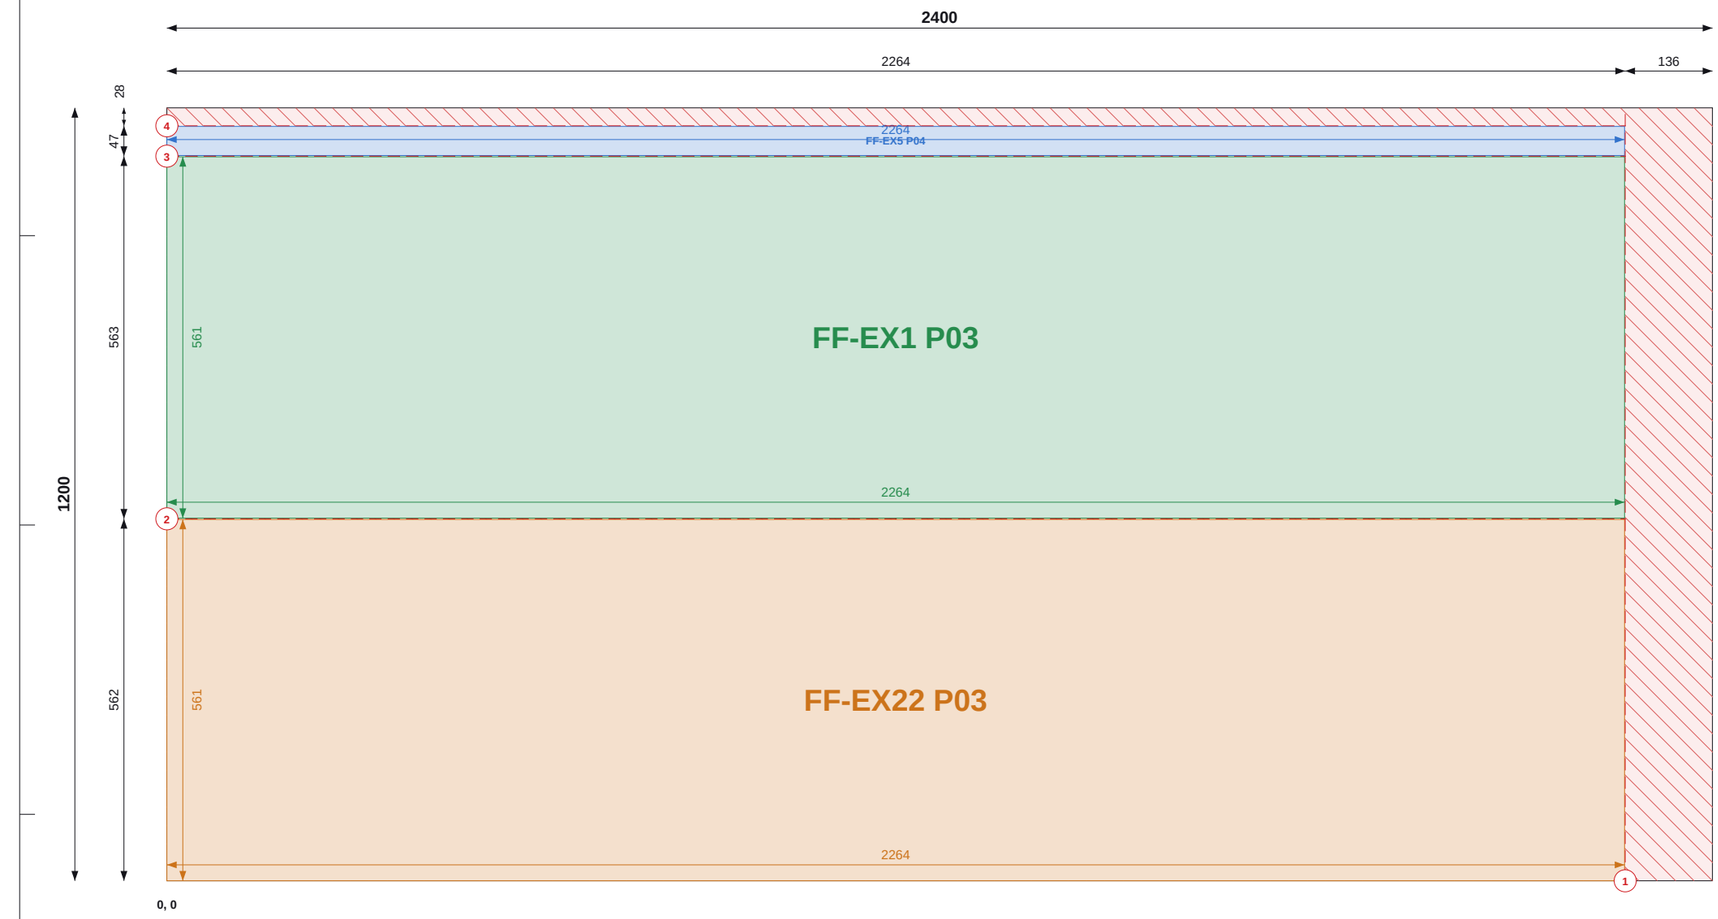

Top / left chains = saw cut positions (to cut centres). Coloured = part size and position.

SHEET 6 OF 23

THIS SHEET

Item	Value
Parts	3
Used / waste	91.7% / 0.24 m2
Reusable offcuts	0
Saw cuts / shared	4 / 2

PIECES (POSITION = BOTTOM-LEFT CORNER)

Label	Size	X, Y
FF-EX5 P04	45 x 2264	0, 1126
FF-EX1 P03	561 x 2264	0, 563
FF-EX22 P03	561 x 2264	0, 0

NOTES

1. Cut from PIR 120mm 1200x2400, 2mm saw kerf. Viewed on the face; dimensions from the sheet's bottom-left corner (0,0). Red numbered lines = saw cuts in order, each edge to edge.
2. Coloured dimensions belong to the part of that colour: its width and height, and its position from the sheet edges. Raked parts: corner coordinates at each corner.
3. Red hatch = waste. Labels = panel + piece mark on the manufacture drawing.

REVISIONS

REV	DATE	DESCRIPTION
C01	14.09.26	Construction issue
C02	14.09.26	Roof trusses revised; SP diagonals added

TLS TIMBER FRAME
Design & Manufacture
Scan: 3D model + drawings

CLIENT	PROJECT
MP Adams	MP Adams Plot 4, Eckington


DRAWING TITLE
PIR CUTTING - FIRST FLOOR - SHEET 6 OF 23

PIR 120mm 1200x2400 | First Floor

SCALE	SIZE	DATE	DRAWN
NTS	A3	14.09.26	TS

STATUS	DRAWING No.	REV
CONSTRUCTION	P4-CP-PIR-02 / 06	C02

Do not scale. All dimensions in mm. Check all dimensions on site.

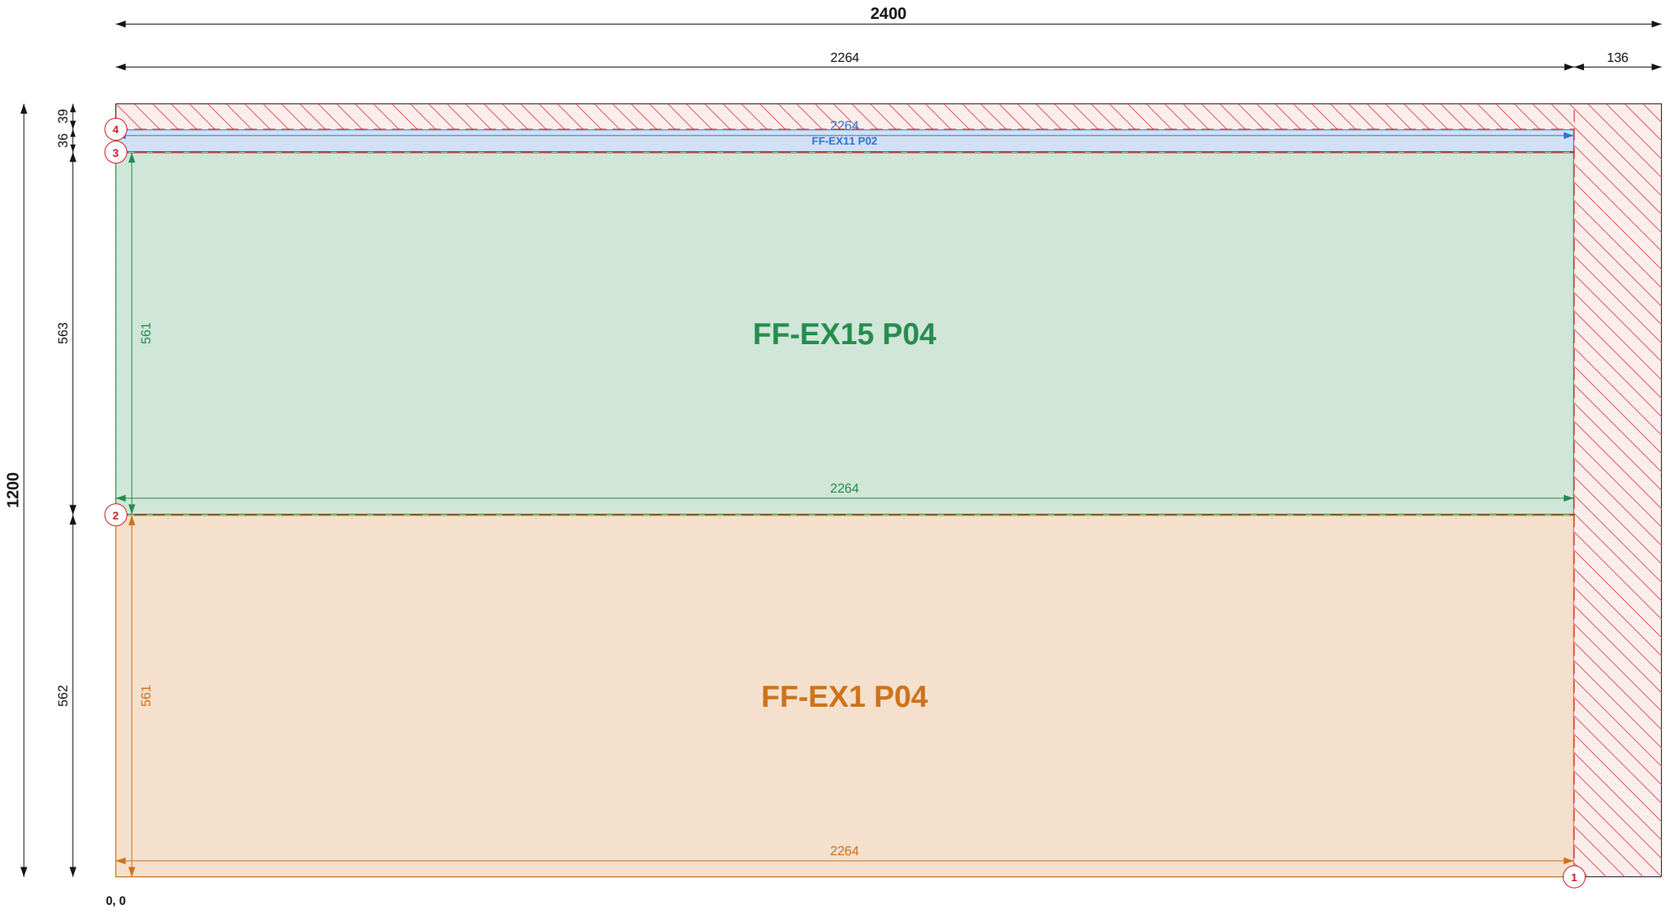

Top / left chains = saw cut positions (to cut centres). Coloured = part size and position.

SHEET 7 OF 23

THIS SHEET

Item	Value
Parts	3
Used / waste	90.8% / 0.26 m2
Reusable offcuts	0
Saw cuts / shared	4 / 2

PIECES (POSITION = BOTTOM-LEFT CORNER)

Label	Size	X, Y
FF-EX11 P02	34 x 2264	0, 1126
FF-EX15 P04	561 x 2264	0, 563
FF-EX1 P04	561 x 2264	0, 0

NOTES

1. Cut from PIR 120mm 1200x2400, 2mm saw kerf. Viewed on the face; dimensions from the sheet's bottom-left corner (0,0). Red numbered lines = saw cuts in order, each edge to edge.
2. Coloured dimensions belong to the part of that colour: its width and height, and its position from the sheet edges. Raked parts: corner coordinates at each corner.
3. Red hatch = waste. Labels = panel + piece mark on the manufacture drawing.

REVISIONS

REV	DATE	DESCRIPTION
C01	14.09.26	Construction issue
C02	14.09.26	Roof trusses revised; SP diagonals added

TLS TIMBER FRAME
Design & Manufacture
Scan: 3D model + drawings

CLIENT	PROJECT
MP Adams	MP Adams Plot 4, Eckington

DRAWING TITLE


PIR CUTTING - FIRST FLOOR - SHEET 7 OF 23

PIR 120mm 1200x2400 | First Floor

SCALE	SIZE	DATE	DRAWN
NTS	A3	14.09.26	TS

STATUS	DRAWING No.	REV
CONSTRUCTION	P4-CP-PIR-02 / 07	C02

Do not scale. All dimensions in mm. Check all dimensions on site.

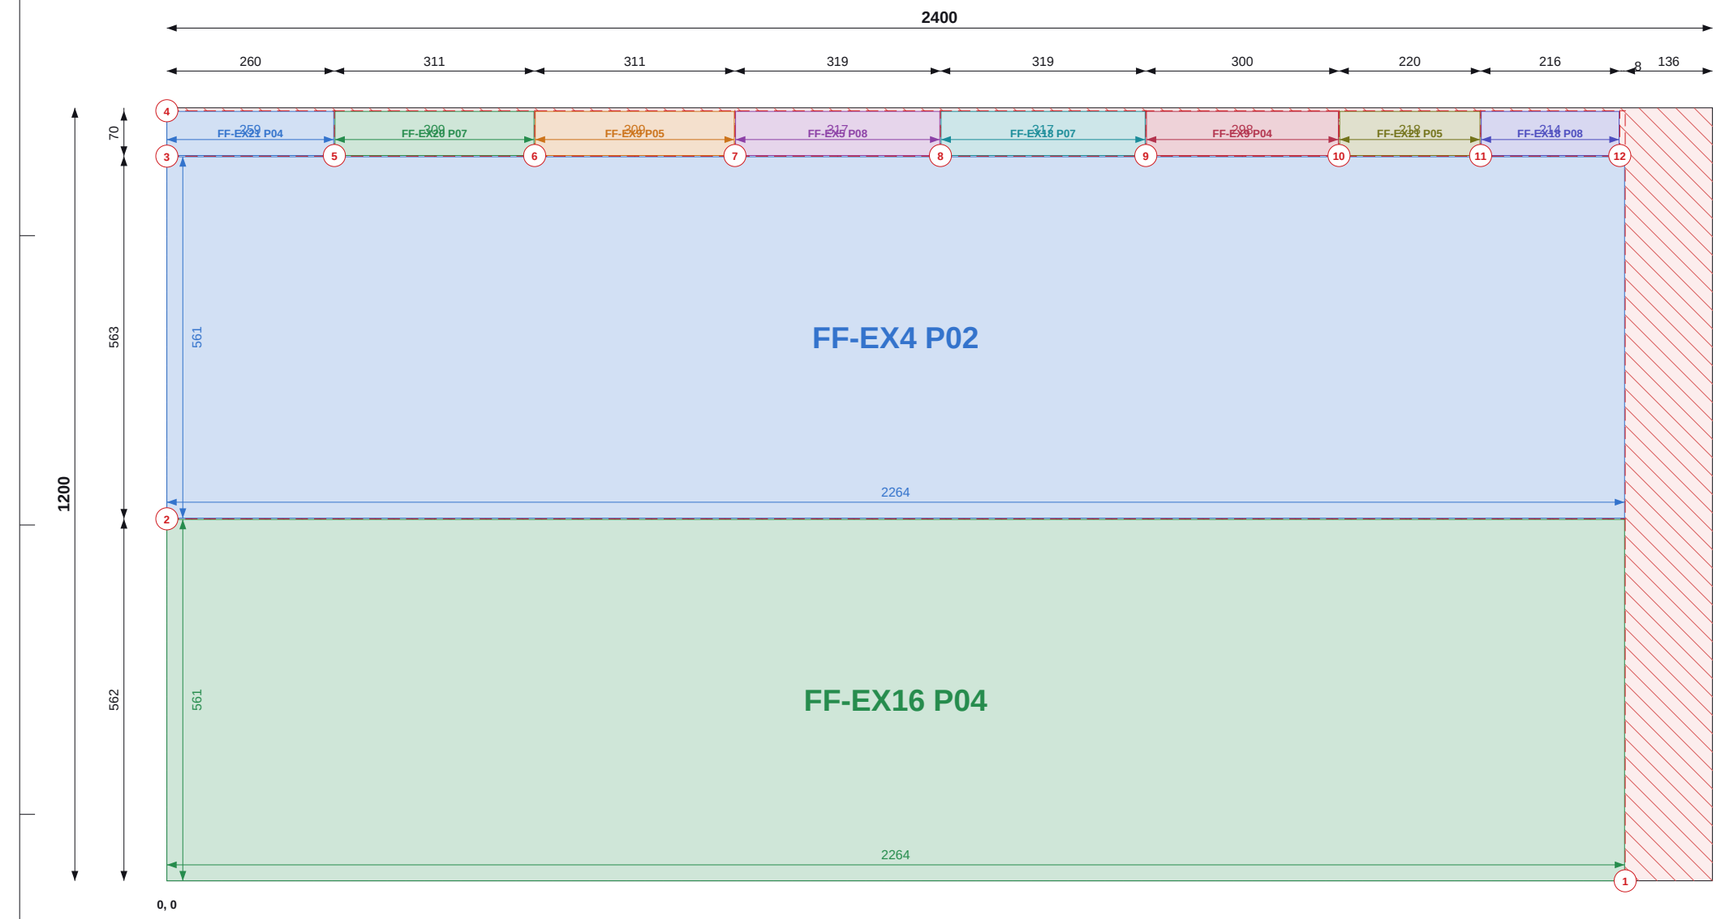

Top / left chains = saw cut positions (to cut centres). Coloured = part size and position.

Do not scale. All dimensions in mm. Check all dimensions on site.

SHEET 8 OF 23

THIS SHEET

Item	Value
Parts	10
Used / waste	93.5% / 0.19 m2
Reusable offcuts	0
Saw cuts / shared	12 / 9

PIECES (POSITION = BOTTOM-LEFT CORNER)

Label	Size	X, Y
FF-EX21 P04	259 x 69	0, 1126
FF-EX20 P07	309 x 69	261, 1126
FF-EX9 P05	309 x 69	572, 1126
FF-EX5 P08	317 x 69	883, 1126
FF-EX18 P07	317 x 69	1202, 1126
FF-EX9 P04	298 x 69	1521, 1126
FF-EX21 P05	218 x 69	1821, 1126
FF-EX18 P08	214 x 69	2041, 1126
FF-EX4 P02	561 x 2264	0, 563
FF-EX16 P04	561 x 2264	0, 0

NOTES

1. Cut from PIR 120mm 1200x2400, 2mm saw kerf. Viewed on the face; dimensions from the sheet's bottom-left corner (0,0). Red numbered lines = saw cuts in order, each edge to edge.
2. Coloured dimensions belong to the part of that colour: its width and height, and its position from the sheet edges. Raked parts: corner coordinates at each corner.
3. Red hatch = waste. Labels = panel + piece mark on the manufacture drawing.

REVISIONS

REV	DATE	DESCRIPTION
C01	14.09.26	Construction issue
C02	14.09.26	Roof trusses revised; SP diagonals added

TLS TIMBER FRAME
Design & Manufacture
Scan: 3D model + drawings

CLIENT	PROJECT
MP Adams	MP Adams Plot 4, Eckington


DRAWING TITLE

PIR CUTTING - FIRST FLOOR - SHEET 8 OF 23

PIR 120mm 1200x2400 | First Floor

SCALE	SIZE	DATE	DRAWN
NTS	A3	14.09.26	TS

STATUS	DRAWING No.	REV
CONSTRUCTION	P4-CP-PIR-02 / 08	C02

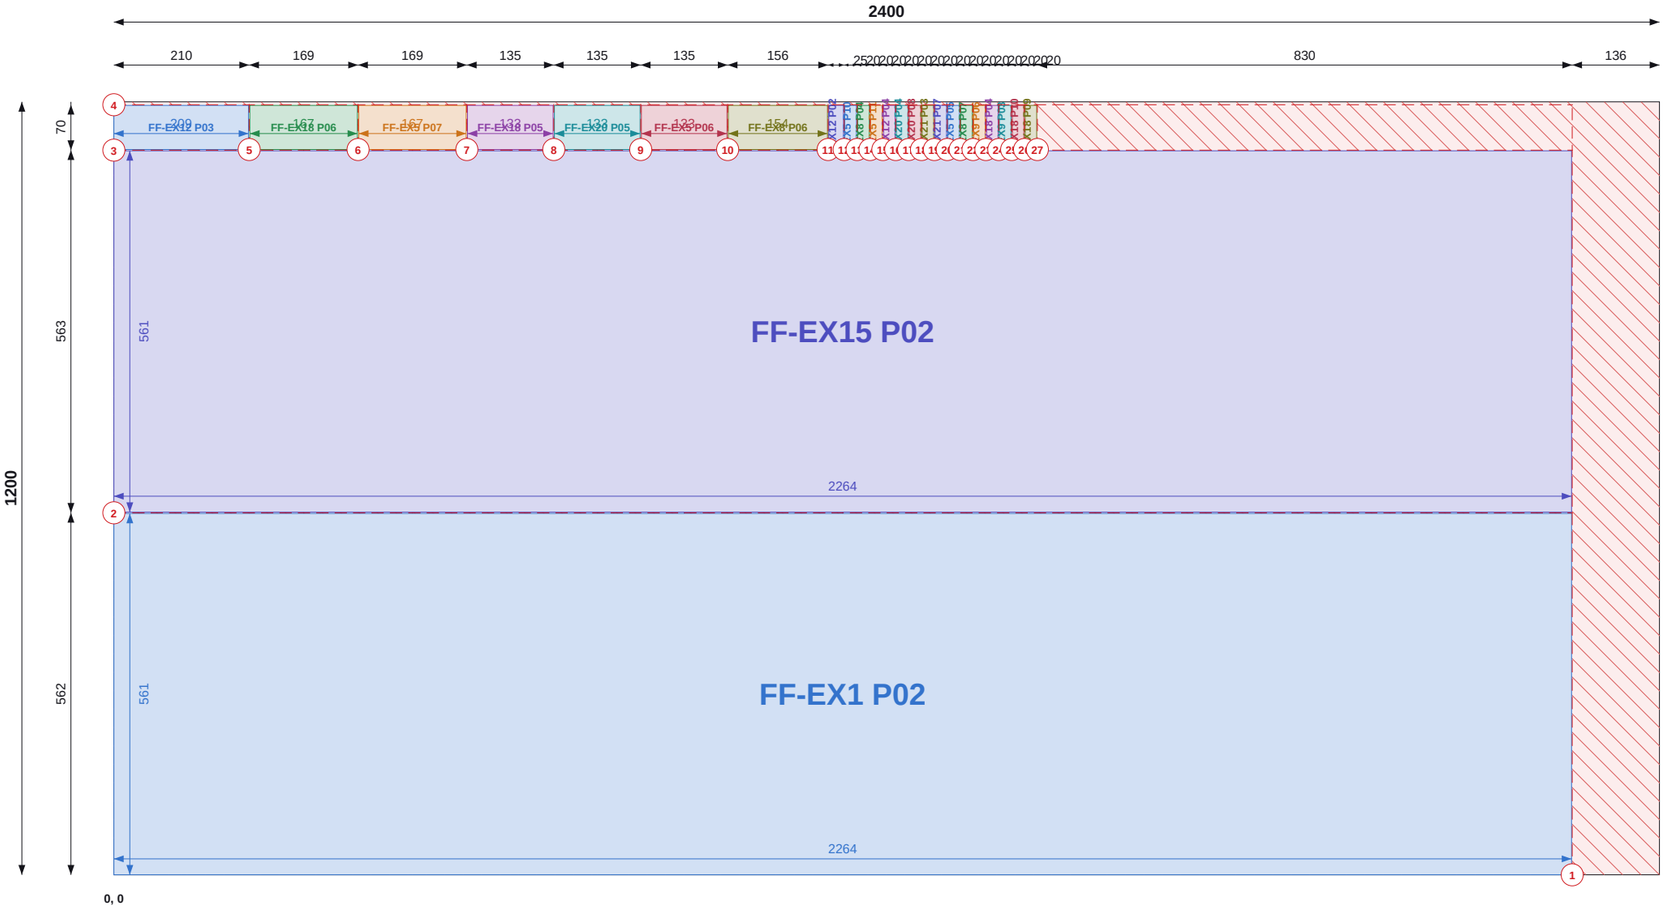

Top / left chains = saw cut positions (to cut centres). Coloured = part size and position.

SHEET 9 OF 23

THIS SHEET

Item	Value
Parts	25
Used / waste	91.5% / 0.25 m2
Reusable offcuts	0
Saw cuts / shared	27 / 24

PIECES (POSITION = BOTTOM-LEFT CORNER)

Label	Size	X, Y
FF-EX12 P03	209 x 69	0, 1126
FF-EX18 P06	167 x 69	211, 1126
FF-EX5 P07	167 x 69	380, 1126
FF-EX18 P05	133 x 69	549, 1126
FF-EX20 P05	133 x 69	684, 1126
FF-EX5 P06	133 x 69	819, 1126
FF-EX8 P06	154 x 69	954, 1126
FF-EX12 P02	23 x 69	1110, 1126
FF-EX5 P10	18 x 69	1135, 1126
FF-EX8 P04	18 x 69	1155, 1126
FF-EX5 P11	18 x 69	1175, 1126
FF-EX12 P04	18 x 69	1195, 1126
FF-EX20 P04	18 x 69	1215, 1126
FF-EX20 P08	18 x 69	1235, 1126
FF-EX21 P03	18 x 69	1255, 1126
FF-EX21 P07	18 x 69	1275, 1126
FF-EX5 P05	18 x 69	1295, 1126
FF-EX8 P07	18 x 69	1315, 1126
FF-EX9 P06	18 x 69	1335, 1126
FF-EX18 P04	18 x 69	1355, 1126
FF-EX9 P03	18 x 69	1375, 1126
FF-EX18 P10	18 x 69	1395, 1126
FF-EX18 P09	18 x 69	1415, 1126
FF-EX15 P02	561 x 2264	0, 563
FF-EX1 P02	561 x 2264	0, 0

NOTES

1. Cut from PIR 120mm 1200x2400, 2mm saw kerf. Viewed on the face; dimensions from the sheet's bottom-left corner (0,0). Red numbered lines = saw cuts in order, each edge to edge.
2. Coloured dimensions belong to the part of that colour: its width and height, and its position from the sheet edges. Raked parts: corner coordinates at each corner.
3. Red hatch = waste. Labels = panel + piece mark on the manufacture drawing.

REVISIONS

REV	DATE	DESCRIPTION
C01	14.09.26	Construction issue
C02	14.09.26	Roof trusses revised; SP diagonals added

TLS TIMBER FRAME
Design & Manufacture
Scan: 3D model + drawings

CLIENT	PROJECT
MP Adams	MP Adams Plot 4, Eckington

DRAWING TITLE


PIR CUTTING - FIRST FLOOR - SHEET 9 OF 23

PIR 120mm 1200x2400 | First Floor

SCALE	SIZE	DATE	DRAWN
NTS	A3	14.09.26	TS

STATUS	DRAWING No.	REV
CONSTRUCTION	P4-CP-PIR-02 / 09	C02

Do not scale. All dimensions in mm. Check all dimensions on site.

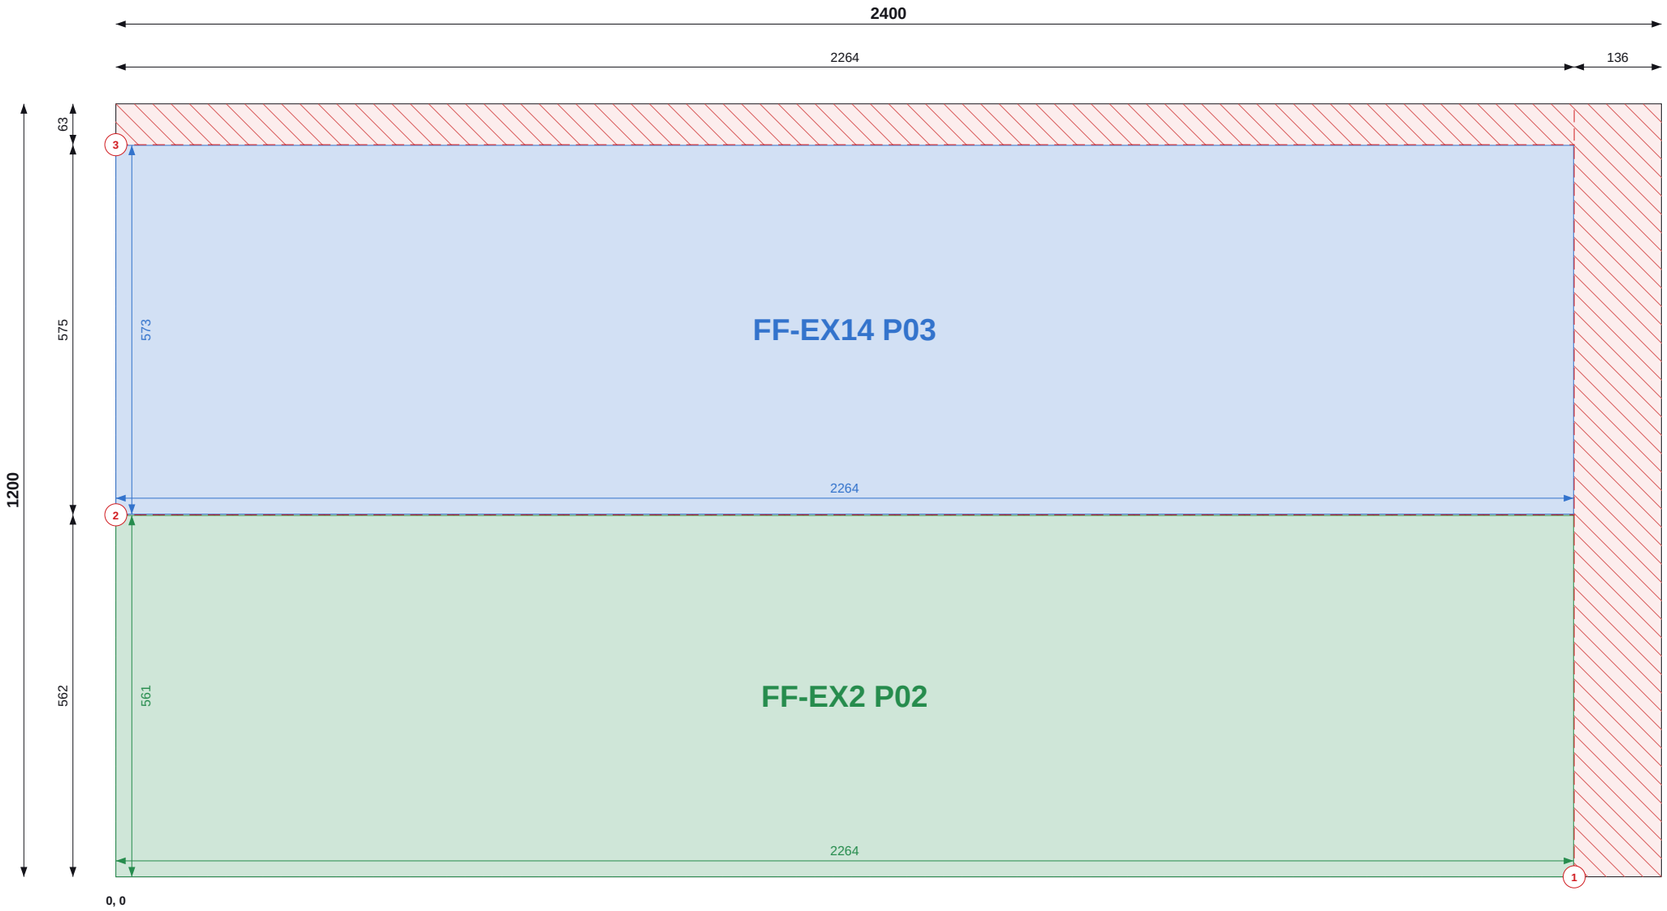

Top / left chains = saw cut positions (to cut centres). Coloured = part size and position.

Do not scale. All dimensions in mm. Check all dimensions on site.

SHEET 10 OF 23

THIS SHEET

Item	Value
Parts	2
Used / waste	89.1% / 0.31 m2
Reusable offcuts	0
Saw cuts / shared	3 / 1

PIECES (POSITION = BOTTOM-LEFT CORNER)

Label	Size	X, Y
FF-EX14 P03	573 x 2264	0, 563
FF-EX2 P02	561 x 2264	0, 0

NOTES

1. Cut from PIR 120mm 1200x2400, 2mm saw kerf. Viewed on the face; dimensions from the sheet's bottom-left corner (0,0). Red numbered lines = saw cuts in order, each edge to edge.
2. Coloured dimensions belong to the part of that colour: its width and height, and its position from the sheet edges. Raked parts: corner coordinates at each corner.
3. Red hatch = waste. Labels = panel + piece mark on the manufacture drawing.

REVISIONS

REV	DATE	DESCRIPTION
C01	14.09.26	Construction issue
C02	14.09.26	Roof trusses revised; SP diagonals added

TLS TIMBER FRAME
Design & Manufacture
Scan: 3D model + drawings


CLIENT	PROJECT
MP Adams	MP Adams Plot 4, Eckington

DRAWING TITLE
PIR CUTTING - FIRST FLOOR - SHEET 10 OF 23

PIR 120mm 1200x2400 | First Floor

SCALE	SIZE	DATE	DRAWN
NTS	A3	14.09.26	TS

STATUS	DRAWING No.	REV
CONSTRUCTION	P4-CP-PIR-02 / 10	C02

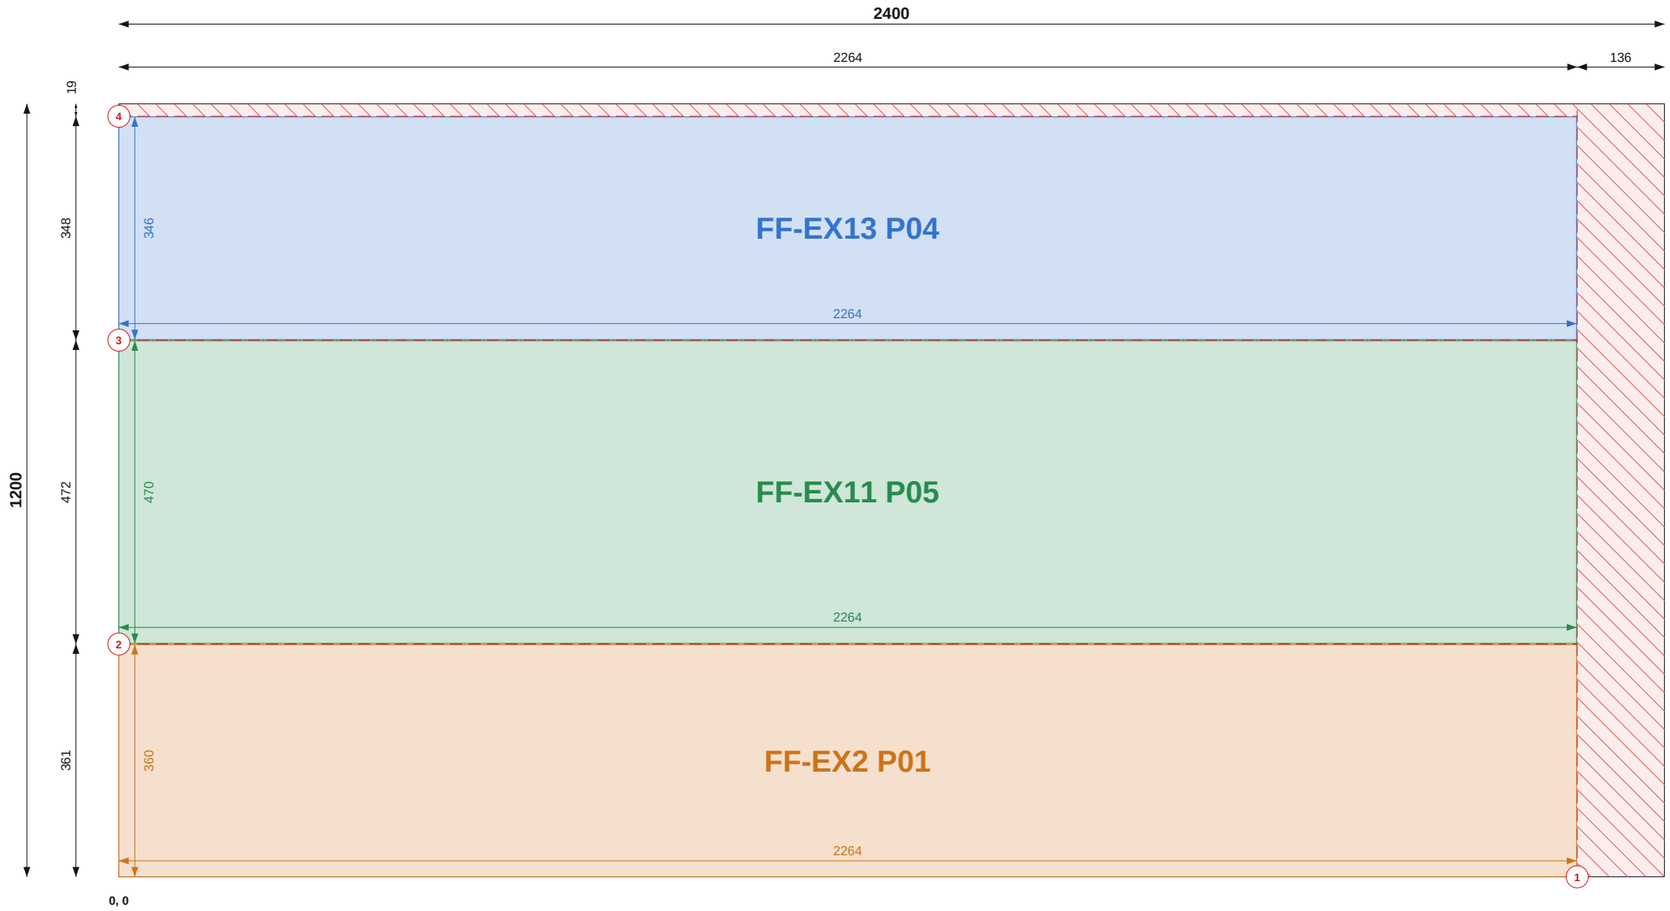

Top / left chains = saw cut positions (to cut centres). Coloured = part size and position.

Do not scale. All dimensions in mm. Check all dimensions on site.

SHEET 11 OF 23

THIS SHEET

Item	Value
Parts	3
Used / waste	92.4% / 0.22 m2
Reusable offcuts	0
Saw cuts / shared	4 / 2

PIECES (POSITION = BOTTOM-LEFT CORNER)

Label	Size	X, Y
FF-EX13 P04	346 x 2264	0, 834
FF-EX11 P05	470 x 2264	0, 362
FF-EX2 P01	360 x 2264	0, 0

NOTES

1. Cut from PIR 120mm 1200x2400, 2mm saw kerf. Viewed on the face; dimensions from the sheet's bottom-left corner (0,0). Red numbered lines = saw cuts in order, each edge to edge.
2. Coloured dimensions belong to the part of that colour: its width and height, and its position from the sheet edges. Raked parts: corner coordinates at each corner.
3. Red hatch = waste. Labels = panel + piece mark on the manufacture drawing.

REVISIONS

REV	DATE	DESCRIPTION
C01	14.09.26	Construction issue
C02	14.09.26	Roof trusses revised; SP diagonals added

TLS TIMBER FRAME
Design & Manufacture
Scan: 3D model + drawings


CLIENT	PROJECT
MP Adams	MP Adams Plot 4, Eckington

DRAWING TITLE
PIR CUTTING - FIRST FLOOR - SHEET 11 OF 23

PIR 120mm 1200x2400 | First Floor

SCALE	SIZE	DATE	DRAWN
NTS	A3	14.09.26	TS

STATUS	DRAWING No.	REV
CONSTRUCTION	P4-CP-PIR-02 / 11	C02

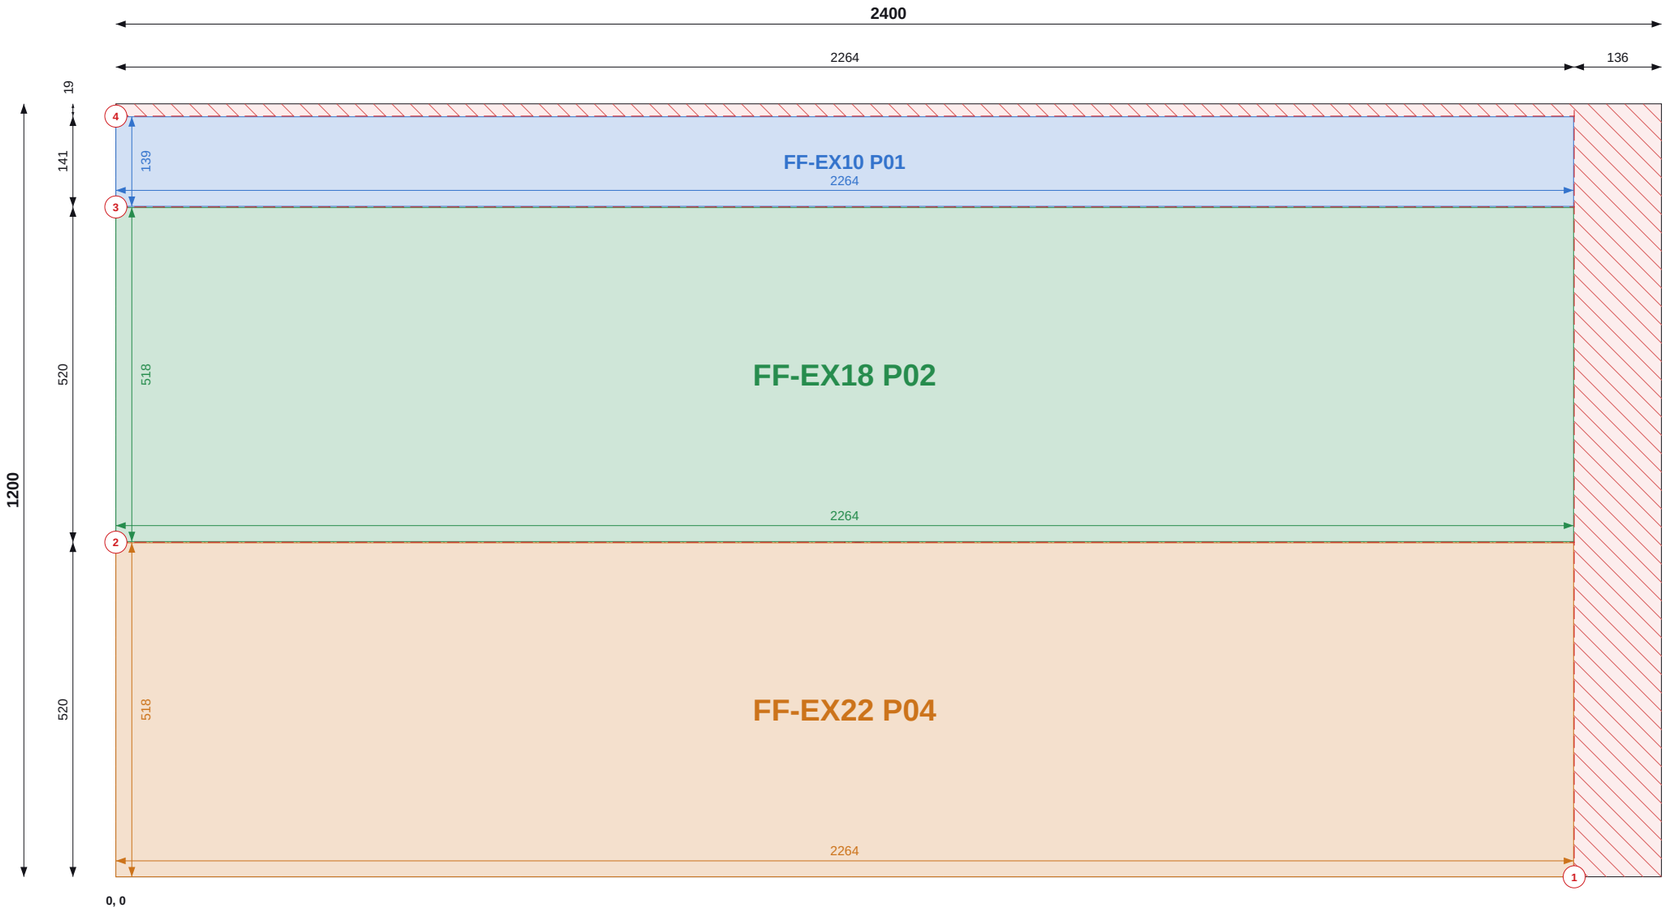

Top / left chains = saw cut positions (to cut centres). Coloured = part size and position.

SHEET 12 OF 23

THIS SHEET

Item	Value
Parts	3
Used / waste	92.4% / 0.22 m2
Reusable offcuts	0
Saw cuts / shared	4 / 2

PIECES (POSITION = BOTTOM-LEFT CORNER)

Label	Size	X, Y
FF-EX10 P01	139 x 2264	0, 1041
FF-EX18 P02	518 x 2264	0, 520
FF-EX22 P04	518 x 2264	0, 0

NOTES

1. Cut from PIR 120mm 1200x2400, 2mm saw kerf. Viewed on the face; dimensions from the sheet's bottom-left corner (0,0). Red numbered lines = saw cuts in order, each edge to edge.
2. Coloured dimensions belong to the part of that colour: its width and height, and its position from the sheet edges. Raked parts: corner coordinates at each corner.
3. Red hatch = waste. Labels = panel + piece mark on the manufacture drawing.

REVISIONS

REV	DATE	DESCRIPTION
C01	14.09.26	Construction issue
C02	14.09.26	Roof trusses revised; SP diagonals added

TLS TIMBER FRAME
Design & Manufacture
Scan: 3D model + drawings

CLIENT	PROJECT
MP Adams	MP Adams Plot 4, Eckington

DRAWING TITLE


PIR CUTTING - FIRST FLOOR - SHEET 12 OF 23

PIR 120mm 1200x2400 | First Floor

SCALE	SIZE	DATE	DRAWN
NTS	A3	14.09.26	TS

STATUS	DRAWING No.	REV
CONSTRUCTION	P4-CP-PIR-02 / 12	C02

Do not scale. All dimensions in mm. Check all dimensions on site.

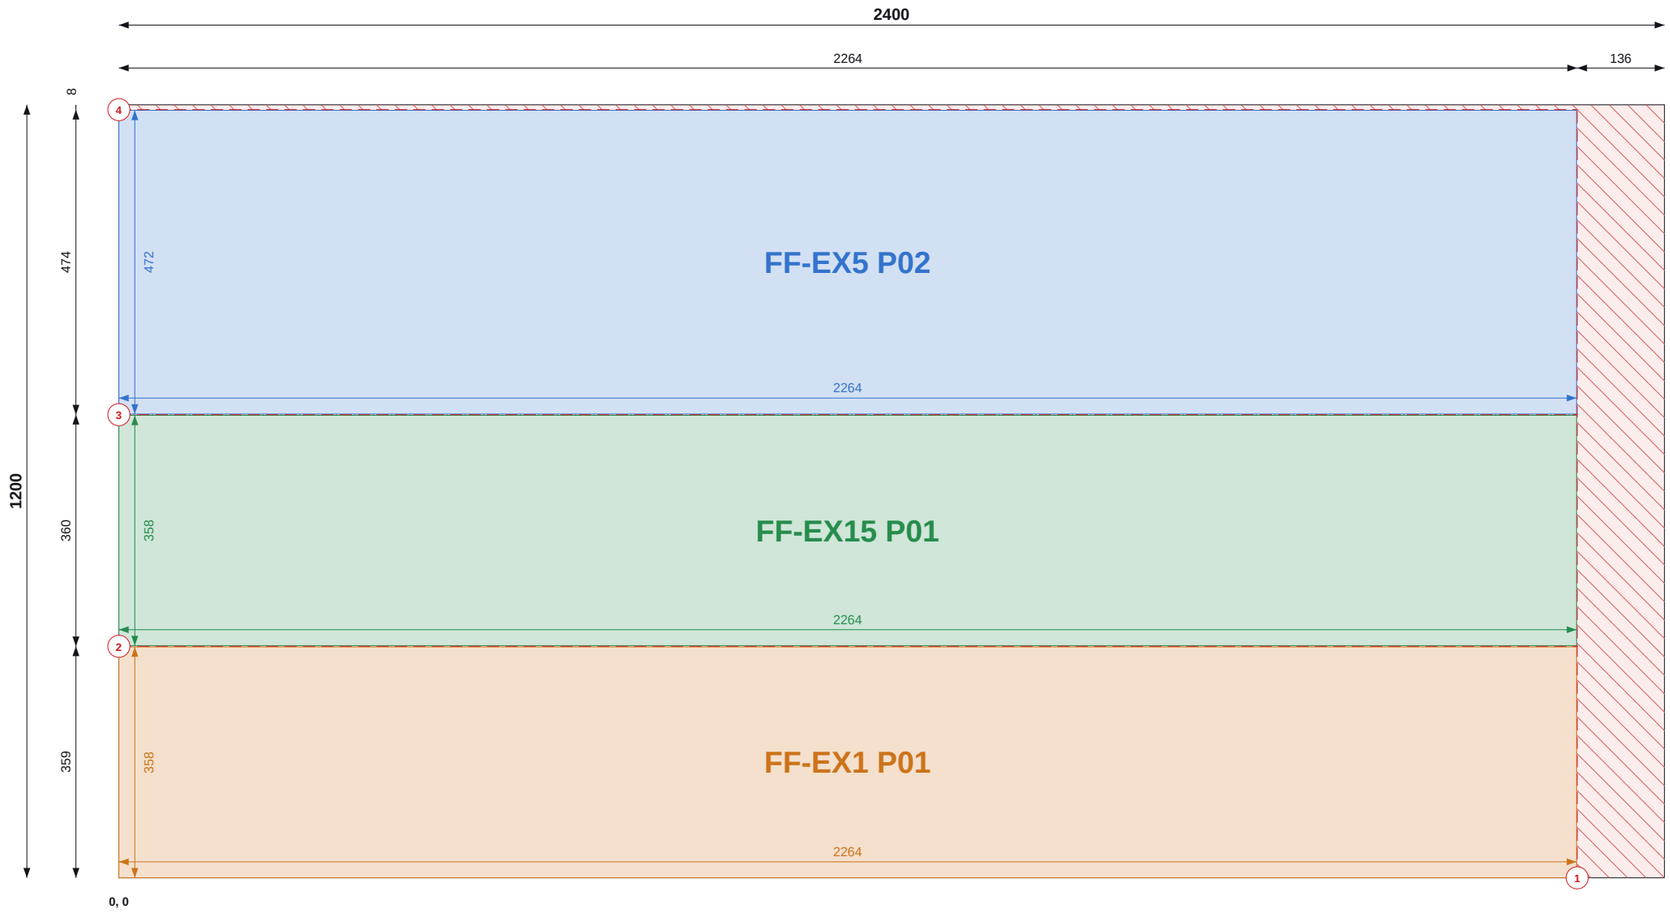

Top / left chains = saw cut positions (to cut centres). Coloured = part size and position.

SHEET 13 OF 23

THIS SHEET

Item	Value
Parts	3
Used / waste	93.3% / 0.19 m2
Reusable offcuts	0
Saw cuts / shared	4 / 2

PIECES (POSITION = BOTTOM-LEFT CORNER)

Label	Size	X, Y
FF-EX5 P02	472 x 2264	0, 720
FF-EX15 P01	358 x 2264	0, 360
FF-EX1 P01	358 x 2264	0, 0

NOTES

1. Cut from PIR 120mm 1200x2400, 2mm saw kerf. Viewed on the face; dimensions from the sheet's bottom-left corner (0,0). Red numbered lines = saw cuts in order, each edge to edge.
2. Coloured dimensions belong to the part of that colour: its width and height, and its position from the sheet edges. Raked parts: corner coordinates at each corner.
3. Red hatch = waste. Labels = panel + piece mark on the manufacture drawing.

REVISIONS

REV	DATE	DESCRIPTION
C01	14.09.26	Construction issue
C02	14.09.26	Roof trusses revised; SP diagonals added

TLS TIMBER FRAME
Design & Manufacture
Scan: 3D model + drawings

CLIENT	PROJECT
MP Adams	MP Adams Plot 4, Eckington

DRAWING TITLE


PIR CUTTING - FIRST FLOOR - SHEET 13 OF 23

PIR 120mm 1200x2400 | First Floor

SCALE	SIZE	DATE	DRAWN
NTS	A3	14.09.26	TS

STATUS	DRAWING No.	REV
CONSTRUCTION	P4-CP-PIR-02 / 13	C02

Do not scale. All dimensions in mm. Check all dimensions on site.

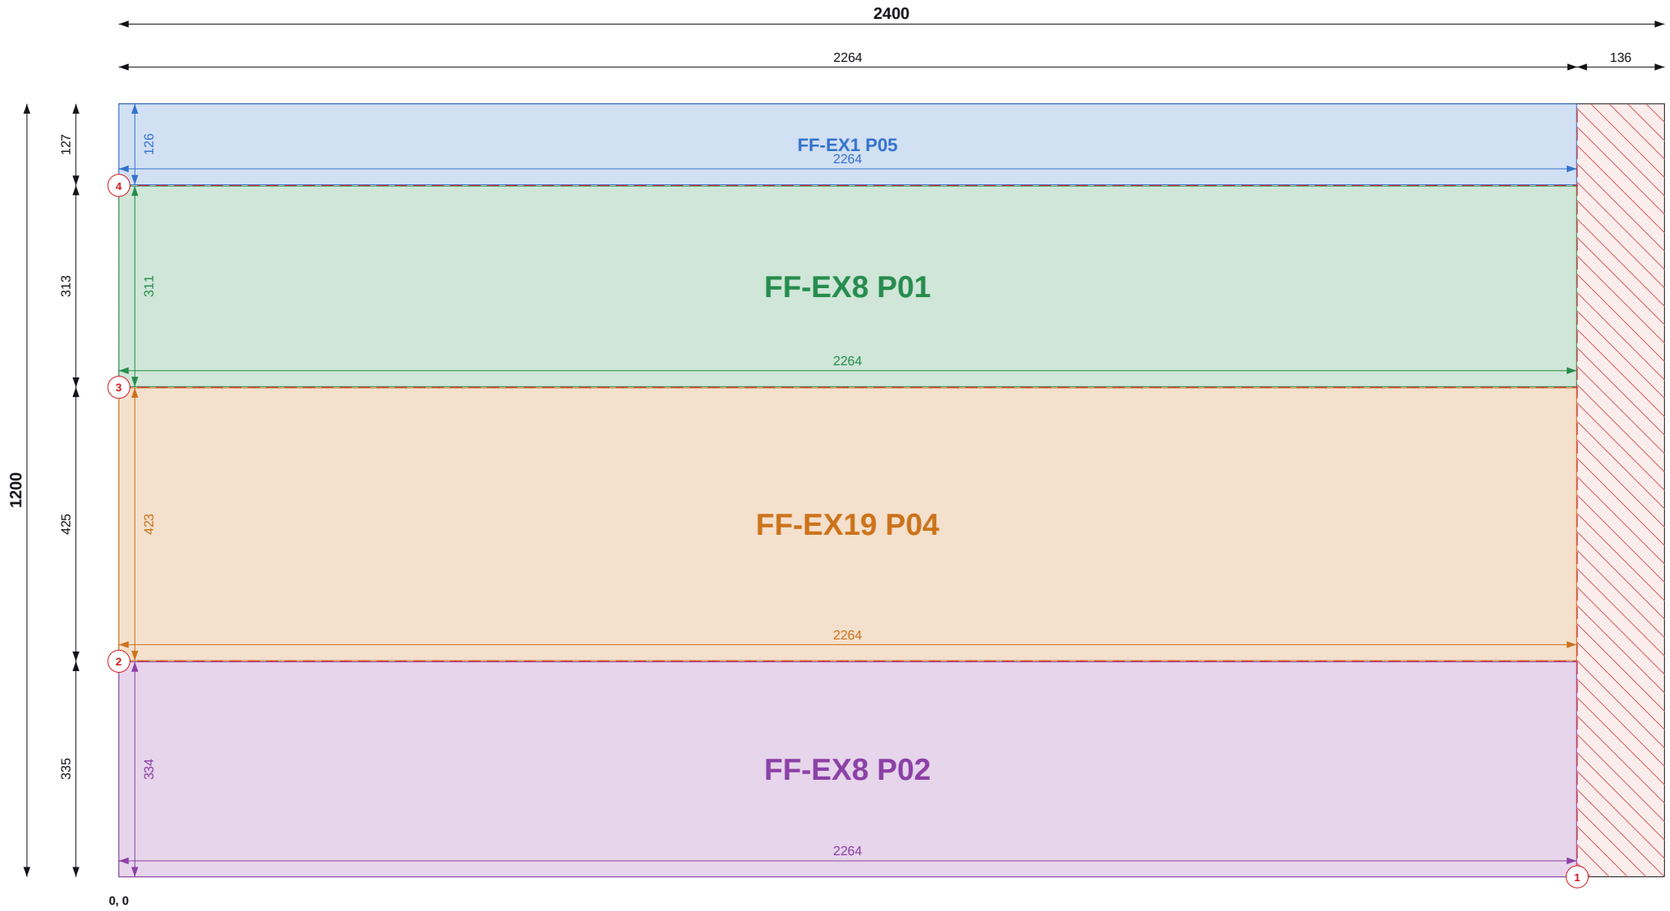

Top / left chains = saw cut positions (to cut centres). Coloured = part size and position.

SHEET 14 OF 23

THIS SHEET

Item	Value
Parts	4
Used / waste	93.8% / 0.18 m2
Reusable offcuts	0
Saw cuts / shared	4 / 3

PIECES (POSITION = BOTTOM-LEFT CORNER)

Label	Size	X, Y
FF-EX1 P05	126 x 2264	0, 1074
FF-EX8 P01	311 x 2264	0, 761
FF-EX19 P04	423 x 2264	0, 336
FF-EX8 P02	334 x 2264	0, 0

NOTES

1. Cut from PIR 120mm 1200x2400, 2mm saw kerf. Viewed on the face; dimensions from the sheet's bottom-left corner (0,0). Red numbered lines = saw cuts in order, each edge to edge.
2. Coloured dimensions belong to the part of that colour: its width and height, and its position from the sheet edges. Raked parts: corner coordinates at each corner.
3. Red hatch = waste. Labels = panel + piece mark on the manufacture drawing.

REVISIONS

REV	DATE	DESCRIPTION
C01	14.09.26	Construction issue
C02	14.09.26	Roof trusses revised; SP diagonals added

TLS TIMBER FRAME
Design & Manufacture
Scan: 3D model + drawings

CLIENT	PROJECT
MP Adams	MP Adams Plot 4, Eckington

DRAWING TITLE


PIR CUTTING - FIRST FLOOR - SHEET 14 OF 23

PIR 120mm 1200x2400 | First Floor

SCALE	SIZE	DATE	DRAWN
NTS	A3	14.09.26	TS

STATUS	DRAWING No.	REV
CONSTRUCTION	P4-CP-PIR-02 / 14	C02

Do not scale. All dimensions in mm. Check all dimensions on site.

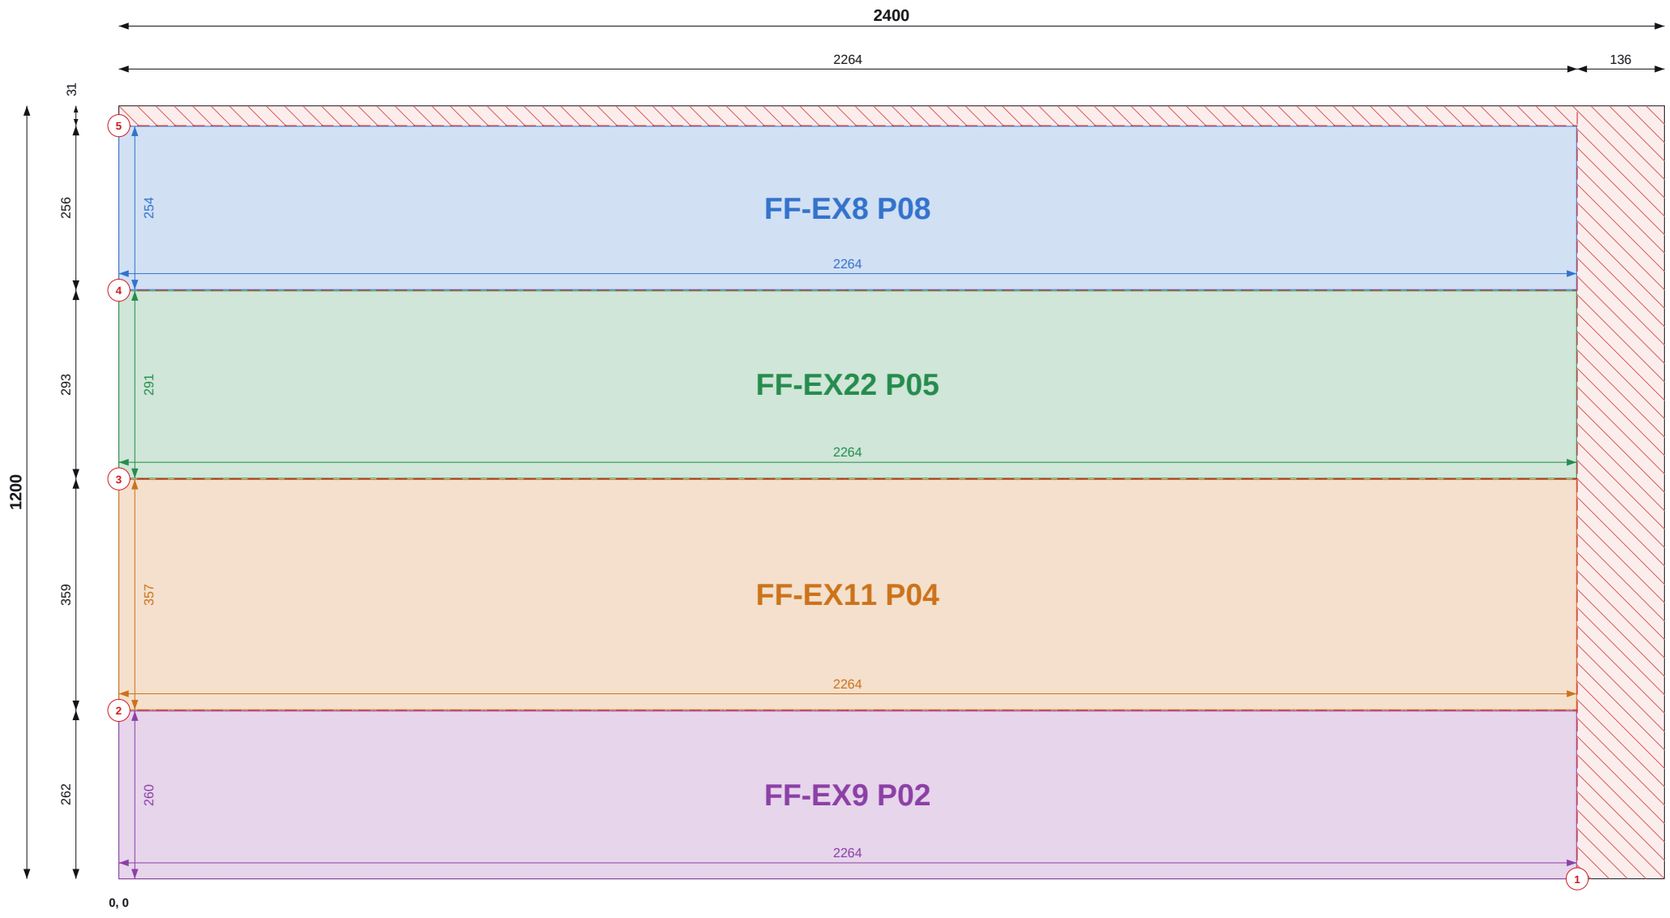

Top / left chains = saw cut positions (to cut centres). Coloured = part size and position.

SHEET 15 OF 23

THIS SHEET

Item	Value
Parts	4
Used / waste	91.3% / 0.25 m2
Reusable offcuts	0
Saw cuts / shared	5 / 3

PIECES (POSITION = BOTTOM-LEFT CORNER)

Label	Size	X, Y
FF-EX8 P08	254 x 2264	0, 915
FF-EX22 P05	291 x 2264	0, 622
FF-EX11 P04	357 x 2264	0, 262
FF-EX9 P02	260 x 2264	0, 0

NOTES

1. Cut from PIR 120mm 1200x2400, 2mm saw kerf. Viewed on the face; dimensions from the sheet's bottom-left corner (0,0). Red numbered lines = saw cuts in order, each edge to edge.
2. Coloured dimensions belong to the part of that colour: its width and height, and its position from the sheet edges. Raked parts: corner coordinates at each corner.
3. Red hatch = waste. Labels = panel + piece mark on the manufacture drawing.

REVISIONS

REV	DATE	DESCRIPTION
C01	14.09.26	Construction issue
C02	14.09.26	Roof trusses revised; SP diagonals added

TLS TIMBER FRAME
Design & Manufacture
Scan: 3D model + drawings

CLIENT	PROJECT
MP Adams	MP Adams Plot 4, Eckington

DRAWING TITLE


PIR CUTTING - FIRST FLOOR - SHEET 15 OF 23

PIR 120mm 1200x2400 | First Floor

SCALE	SIZE	DATE	DRAWN
NTS	A3	14.09.26	TS

STATUS	DRAWING No.	REV
CONSTRUCTION	P4-CP-PIR-02 / 15	C02

Do not scale. All dimensions in mm. Check all dimensions on site.

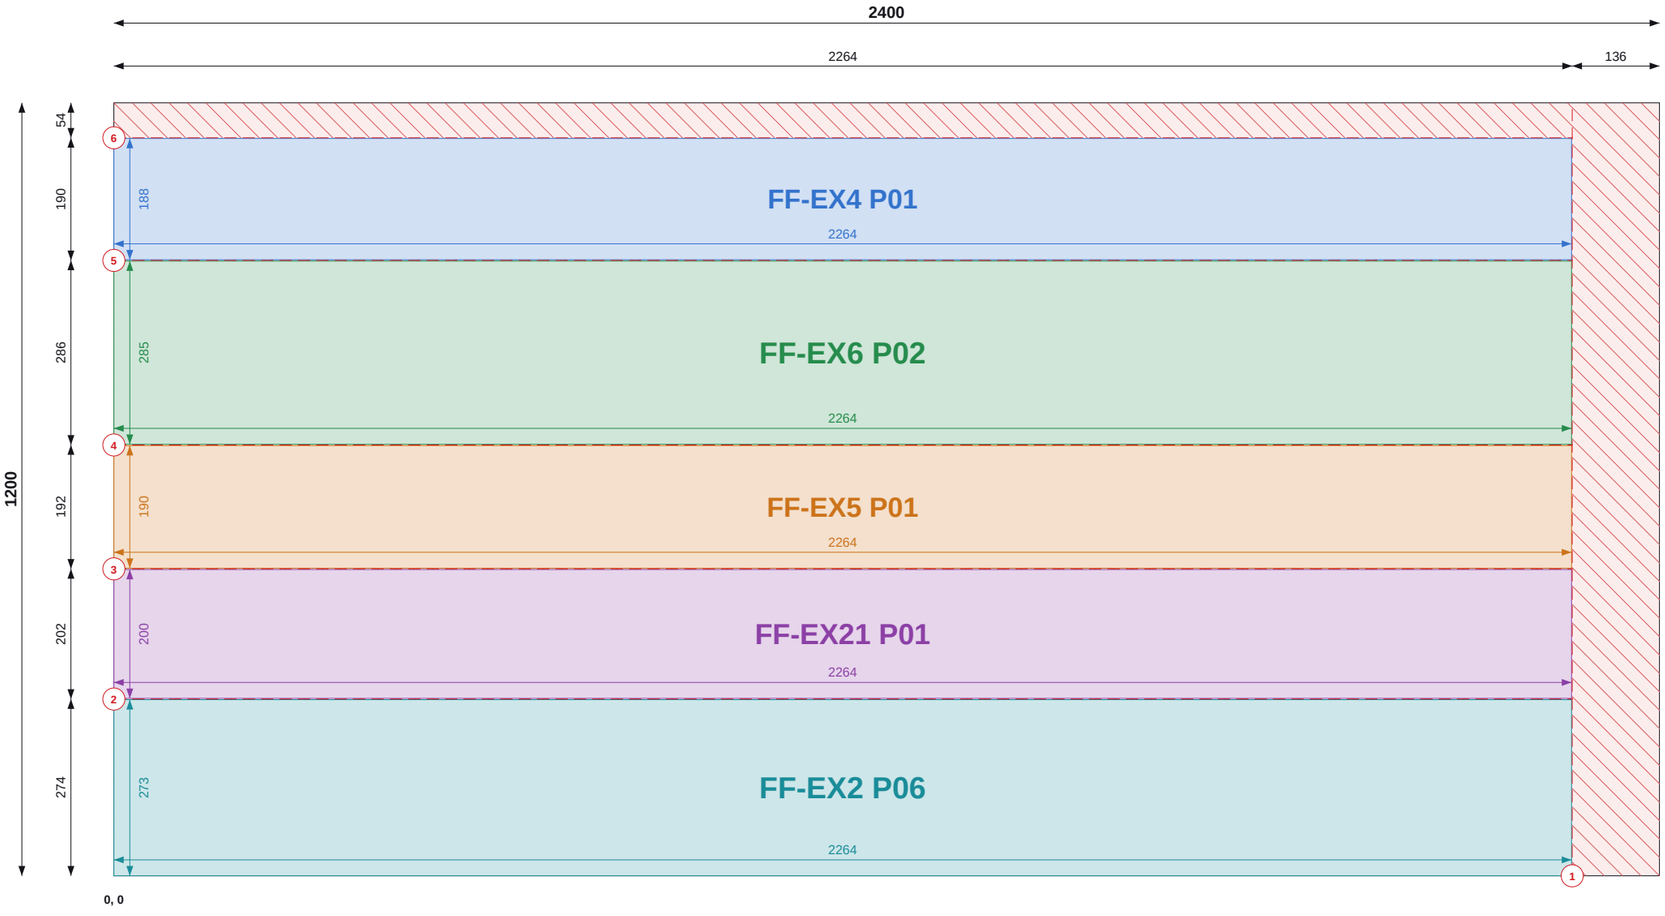

Top / left chains = saw cut positions (to cut centres). Coloured = part size and position.

Do not scale. All dimensions in mm. Check all dimensions on site.

SHEET 16 OF 23

THIS SHEET

Item	Value
Parts	5
Used / waste	89.3% / 0.31 m2
Reusable offcuts	0
Saw cuts / shared	6 / 4

PIECES (POSITION = BOTTOM-LEFT CORNER)

Label	Size	X, Y
FF-EX4 P01	188 x 2264	0, 956
FF-EX6 P02	285 x 2264	0, 670
FF-EX5 P01	190 x 2264	0, 478
FF-EX21 P01	200 x 2264	0, 275
FF-EX2 P06	273 x 2264	0, 0

NOTES

1. Cut from PIR 120mm 1200x2400, 2mm saw kerf. Viewed on the face; dimensions from the sheet's bottom-left corner (0,0). Red numbered lines = saw cuts in order, each edge to edge.
2. Coloured dimensions belong to the part of that colour: its width and height, and its position from the sheet edges. Raked parts: corner coordinates at each corner.
3. Red hatch = waste. Labels = panel + piece mark on the manufacture drawing.

REVISIONS

REV	DATE	DESCRIPTION
C01	14.09.26	Construction issue
C02	14.09.26	Roof trusses revised; SP diagonals added

TLS TIMBER FRAME
Design & Manufacture
Scan: 3D model + drawings

CLIENT	PROJECT
MP Adams	MP Adams Plot 4, Eckington


DRAWING TITLE

PIR CUTTING - FIRST FLOOR - SHEET 16 OF 23

PIR 120mm 1200x2400 | First Floor

SCALE	SIZE	DATE	DRAWN
NTS	A3	14.09.26	TS

STATUS	DRAWING No.	REV
CONSTRUCTION	P4-CP-PIR-02 / 16	C02

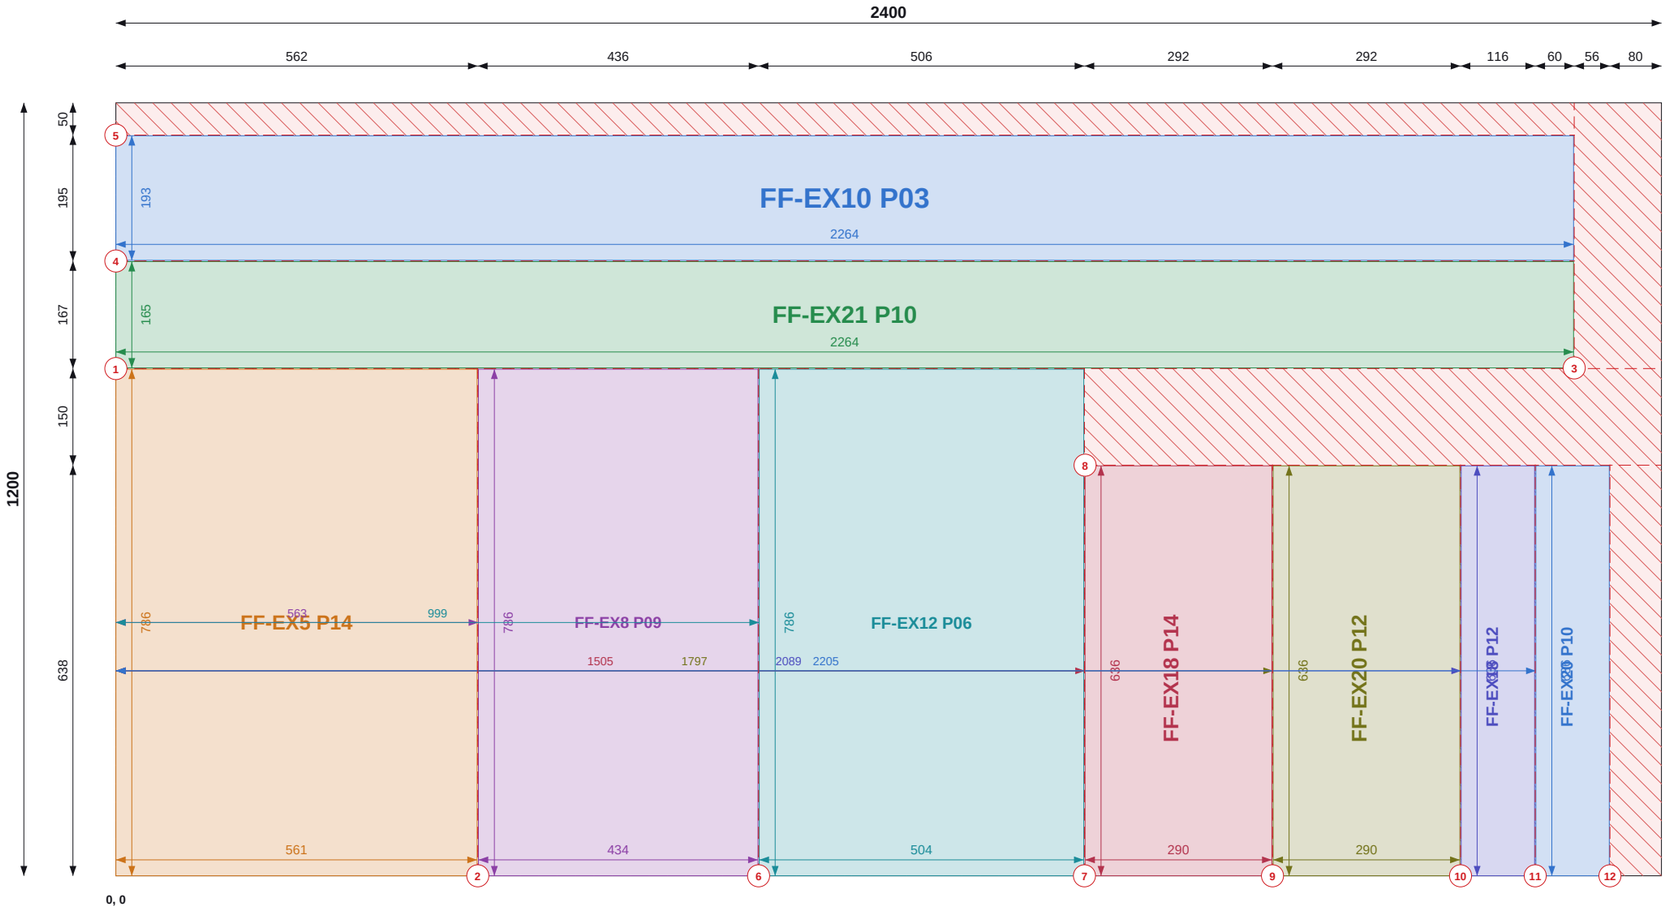

Top / left chains = saw cut positions (to cut centres). Coloured = part size and position.

Do not scale. All dimensions in mm. Check all dimensions on site.

SHEET 17 OF 23

THIS SHEET

Item	Value
Parts	9
Used / waste	87.0% / 0.38 m2
Reusable offcuts	0
Saw cuts / shared	12 / 8

PIECES (POSITION = BOTTOM-LEFT CORNER)

Label	Size	X, Y
FF-EX10 P03	193 x 2264	0, 956
FF-EX21 P10	165 x 2264	0, 788
FF-EX5 P14	561 x 786	0, 0
FF-EX8 P09	434 x 786	563, 0
FF-EX12 P06	504 x 786	999, 0
FF-EX18 P14	290 x 636	1505, 0
FF-EX20 P12	290 x 636	1797, 0
FF-EX18 P12	114 x 636	2089, 0
FF-EX20 P10	114 x 636	2205, 0

NOTES

1. Cut from PIR 120mm 1200x2400, 2mm saw kerf. Viewed on the face; dimensions from the sheet's bottom-left corner (0,0). Red numbered lines = saw cuts in order, each edge to edge.
2. Coloured dimensions belong to the part of that colour: its width and height, and its position from the sheet edges. Raked parts: corner coordinates at each corner.
3. Red hatch = waste. Labels = panel + piece mark on the manufacture drawing.

REVISIONS

REV	DATE	DESCRIPTION
C01	14.09.26	Construction issue
C02	14.09.26	Roof trusses revised; SP diagonals added

TLS TIMBER FRAME
Design & Manufacture
Scan: 3D model + drawings

CLIENT	PROJECT
MP Adams	MP Adams Plot 4, Eckington


DRAWING TITLE

PIR CUTTING - FIRST FLOOR - SHEET 17 OF 23

PIR 120mm 1200x2400 | First Floor

SCALE	SIZE	DATE	DRAWN
NTS	A3	14.09.26	TS

STATUS	DRAWING No.	REV
CONSTRUCTION	P4-CP-PIR-02 / 17	C02

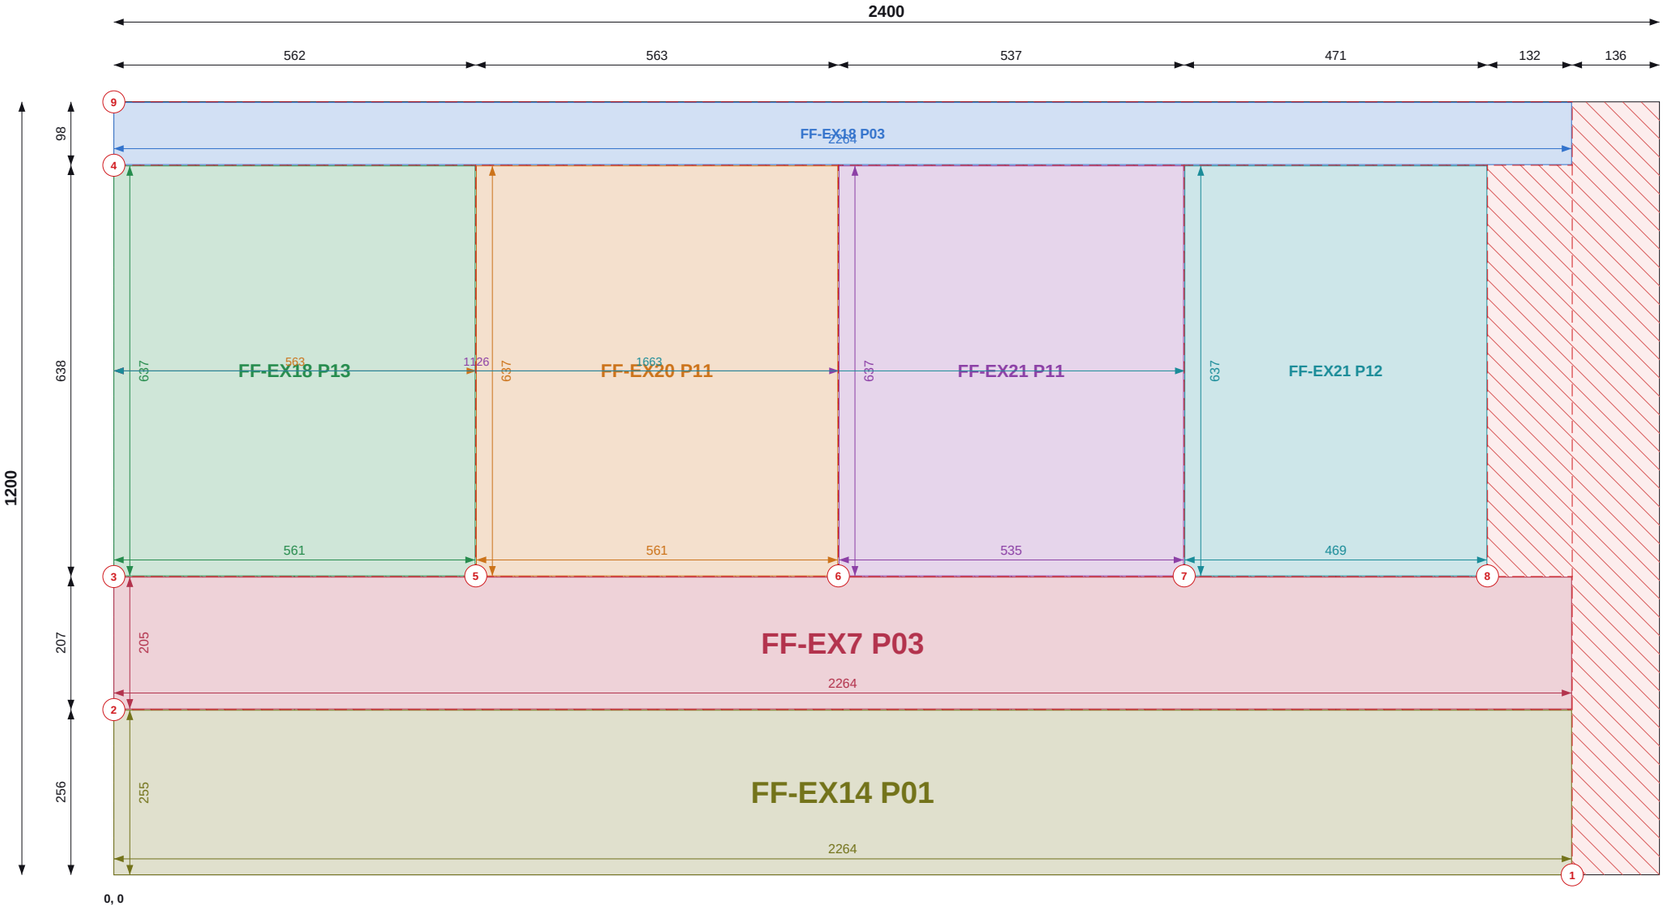

Top / left chains = saw cut positions (to cut centres). Coloured = part size and position.

SHEET 18 OF 23

THIS SHEET

Item	Value
Parts	7
Used / waste	90.7% / 0.27 m2
Reusable offcuts	0
Saw cuts / shared	9 / 6

PIECES (POSITION = BOTTOM-LEFT CORNER)

Label	Size	X, Y
FF-EX18 P03	96 x 2264	0, 1103
FF-EX18 P13	561 x 636	0, 464
FF-EX20 P11	561 x 636	563, 464
FF-EX21 P11	535 x 636	1126, 464
FF-EX21 P12	469 x 636	1663, 464
FF-EX7 P03	205 x 2264	0, 257
FF-EX14 P01	255 x 2264	0, 0

NOTES

1. Cut from PIR 120mm 1200x2400, 2mm saw kerf. Viewed on the face; dimensions from the sheet's bottom-left corner (0,0). Red numbered lines = saw cuts in order, each edge to edge.
2. Coloured dimensions belong to the part of that colour: its width and height, and its position from the sheet edges. Raked parts: corner coordinates at each corner.
3. Red hatch = waste. Labels = panel + piece mark on the manufacture drawing.

REVISIONS

REV	DATE	DESCRIPTION
C01	14.09.26	Construction issue
C02	14.09.26	Roof trusses revised; SP diagonals added

TLS TIMBER FRAME
Design & Manufacture
Scan: 3D model + drawings

CLIENT	PROJECT
MP Adams	MP Adams Plot 4, Eckington

DRAWING TITLE


PIR CUTTING - FIRST FLOOR - SHEET 18 OF 23

PIR 120mm 1200x2400 | First Floor

SCALE	SIZE	DATE	DRAWN
NTS	A3	14.09.26	TS

STATUS	DRAWING No.	REV
CONSTRUCTION	P4-CP-PIR-02 / 18	C02

Do not scale. All dimensions in mm. Check all dimensions on site.

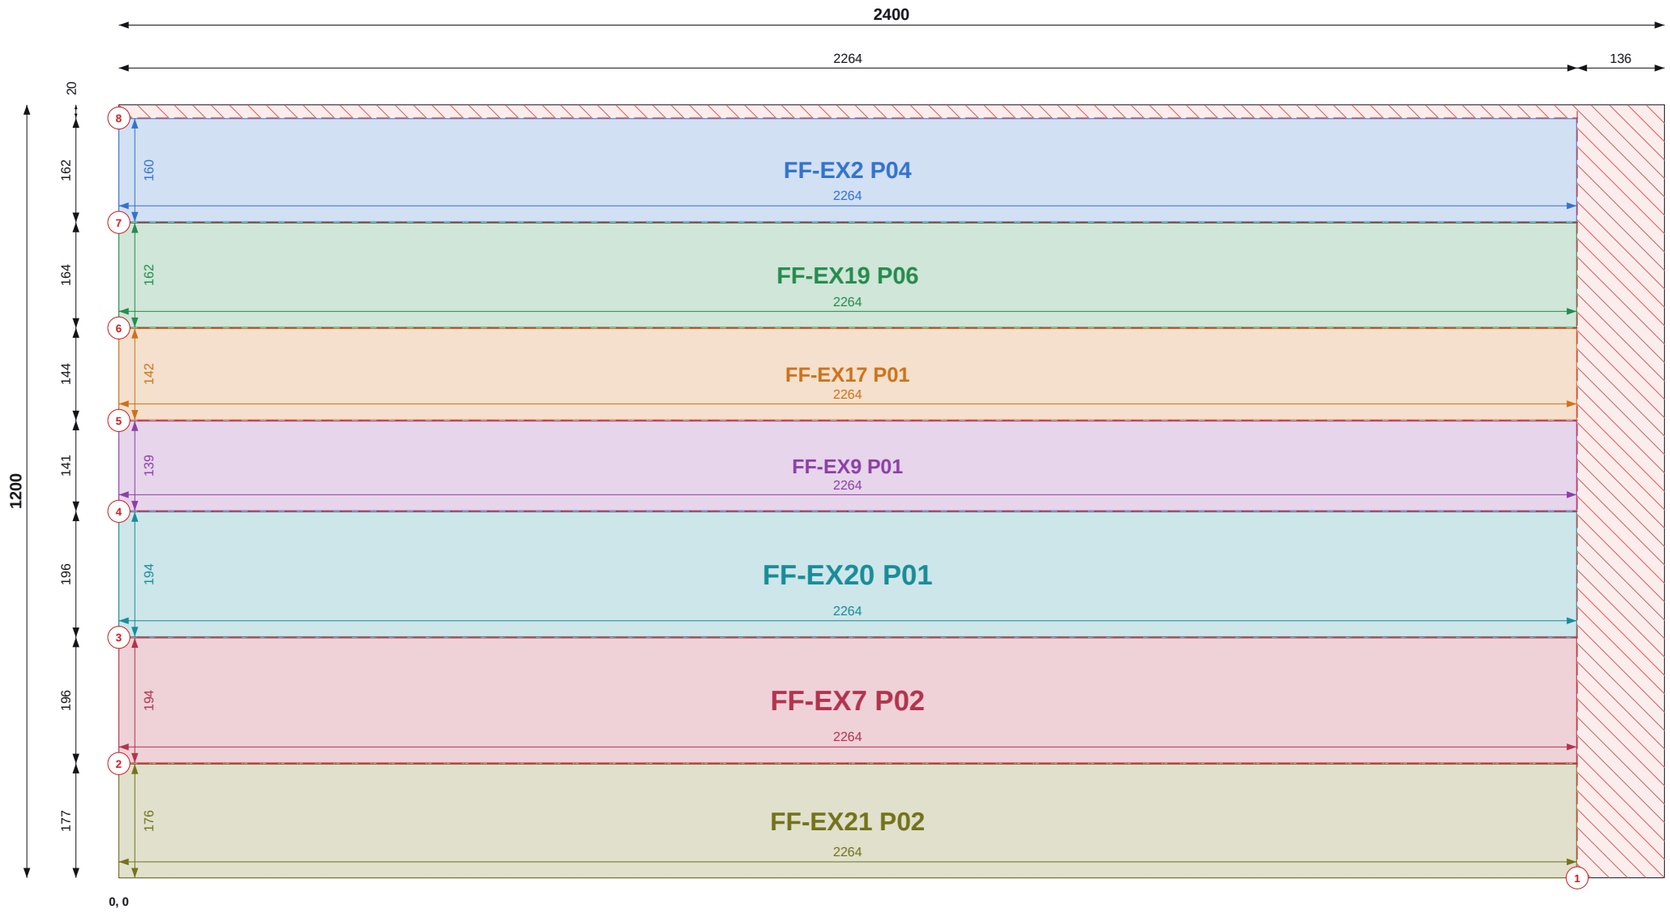

Top / left chains = saw cut positions (to cut centres). Coloured = part size and position.

Do not scale. All dimensions in mm. Check all dimensions on site.

SHEET 19 OF 23

THIS SHEET

Item	Value
Parts	7
Used / waste	91.7% / 0.24 m2
Reusable offcuts	0
Saw cuts / shared	8 / 6

PIECES (POSITION = BOTTOM-LEFT CORNER)

Label	Size	X, Y
FF-EX2 P04	160 x 2264	0, 1018
FF-EX19 P06	162 x 2264	0, 855
FF-EX17 P01	142 x 2264	0, 711
FF-EX9 P01	139 x 2264	0, 570
FF-EX20 P01	194 x 2264	0, 374
FF-EX7 P02	194 x 2264	0, 178
FF-EX21 P02	176 x 2264	0, 0

NOTES

1. Cut from PIR 120mm 1200x2400, 2mm saw kerf. Viewed on the face; dimensions from the sheet's bottom-left corner (0,0). Red numbered lines = saw cuts in order, each edge to edge.
2. Coloured dimensions belong to the part of that colour: its width and height, and its position from the sheet edges. Raked parts: corner coordinates at each corner.
3. Red hatch = waste. Labels = panel + piece mark on the manufacture drawing.

REVISIONS

REV	DATE	DESCRIPTION
C01	14.09.26	Construction issue
C02	14.09.26	Roof trusses revised; SP diagonals added

TLS TIMBER FRAME
Design & Manufacture
Scan: 3D model + drawings

CLIENT	PROJECT
MP Adams	MP Adams Plot 4, Eckington


DRAWING TITLE

PIR CUTTING - FIRST FLOOR - SHEET 19 OF 23

PIR 120mm 1200x2400 | First Floor

SCALE	SIZE	DATE	DRAWN
NTS	A3	14.09.26	TS

STATUS	DRAWING No.	REV
CONSTRUCTION	P4-CP-PIR-02 / 19	C02

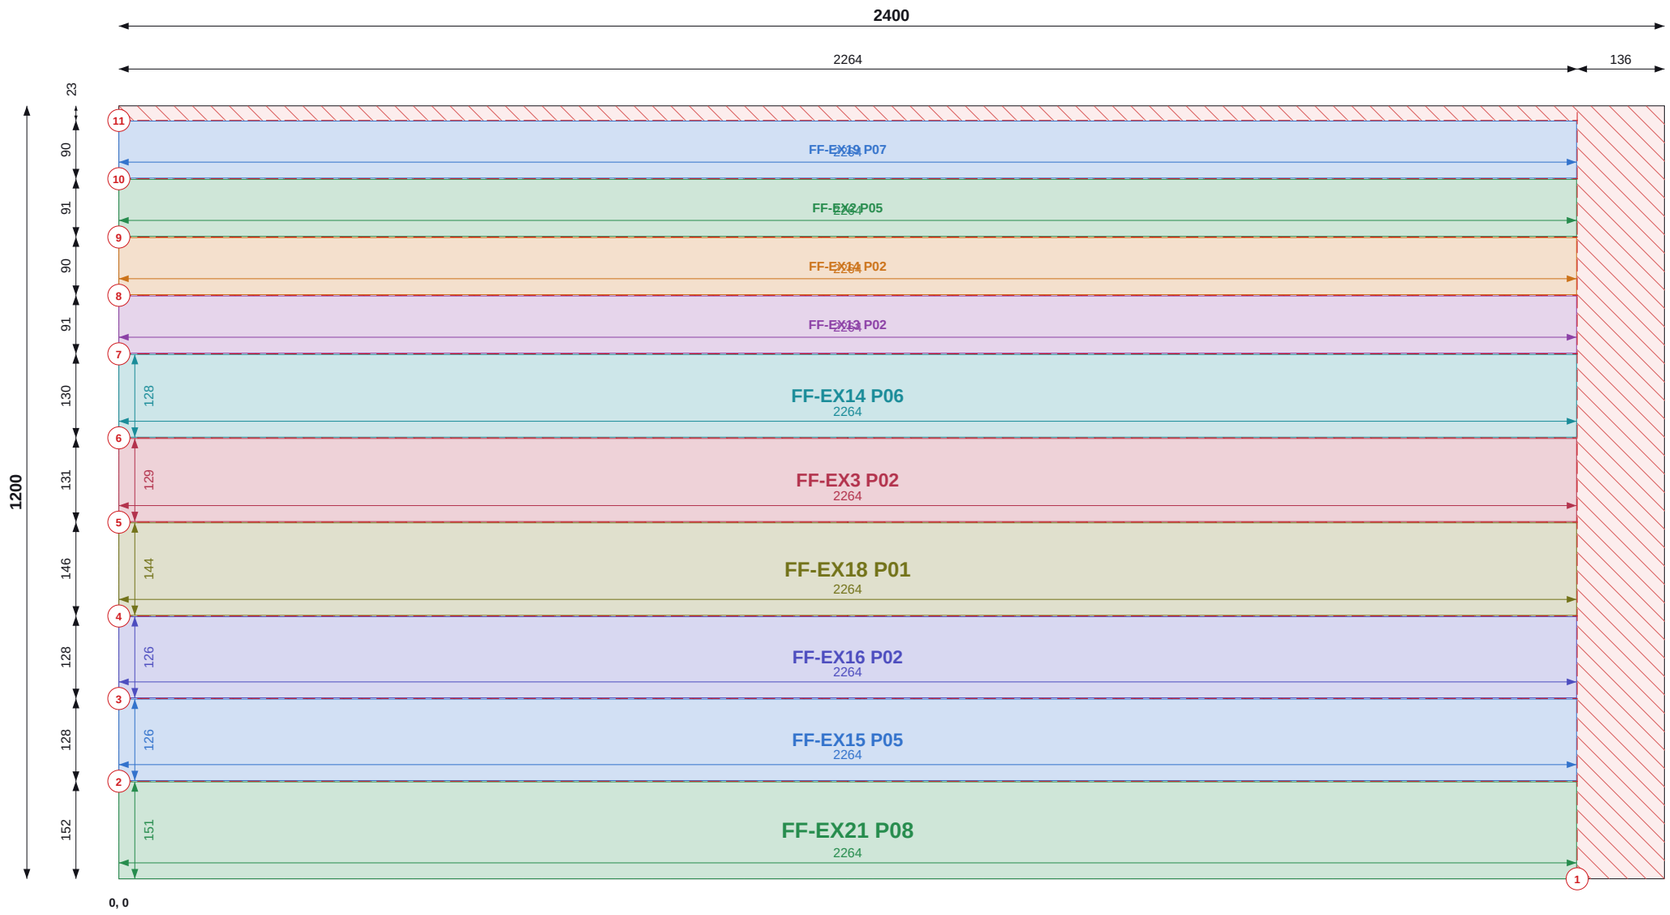

Top / left chains = saw cut positions (to cut centres). Coloured = part size and position.

SHEET 20 OF 23

THIS SHEET

Item	Value
Parts	10
Used / waste	91.0% / 0.26 m2
Reusable offcuts	0
Saw cuts / shared	11 / 9

PIECES (POSITION = BOTTOM-LEFT CORNER)

Label	Size	X, Y
FF-EX19 P07	89 x 2264	0, 1088
FF-EX2 P05	89 x 2264	0, 997
FF-EX14 P02	89 x 2264	0, 907
FF-EX13 P02	89 x 2264	0, 816
FF-EX14 P06	128 x 2264	0, 686
FF-EX3 P02	129 x 2264	0, 555
FF-EX18 P01	144 x 2264	0, 409
FF-EX16 P02	126 x 2264	0, 281
FF-EX15 P05	126 x 2264	0, 153
FF-EX21 P08	151 x 2264	0, 0

NOTES

1. Cut from PIR 120mm 1200x2400, 2mm saw kerf. Viewed on the face; dimensions from the sheet's bottom-left corner (0,0). Red numbered lines = saw cuts in order, each edge to edge.
2. Coloured dimensions belong to the part of that colour: its width and height, and its position from the sheet edges. Raked parts: corner coordinates at each corner.
3. Red hatch = waste. Labels = panel + piece mark on the manufacture drawing.

REVISIONS

REV	DATE	DESCRIPTION
C01	14.09.26	Construction issue
C02	14.09.26	Roof trusses revised; SP diagonals added

TLS TIMBER FRAME
Design & Manufacture
Scan: 3D model + drawings

CLIENT	PROJECT
MP Adams	MP Adams Plot 4, Eckington

DRAWING TITLE


PIR CUTTING - FIRST FLOOR - SHEET 20 OF 23

PIR 120mm 1200x2400 | First Floor

SCALE	SIZE	DATE	DRAWN
NTS	A3	14.09.26	TS

STATUS	DRAWING No.	REV
CONSTRUCTION	P4-CP-PIR-02 / 20	C02

Do not scale. All dimensions in mm. Check all dimensions on site.

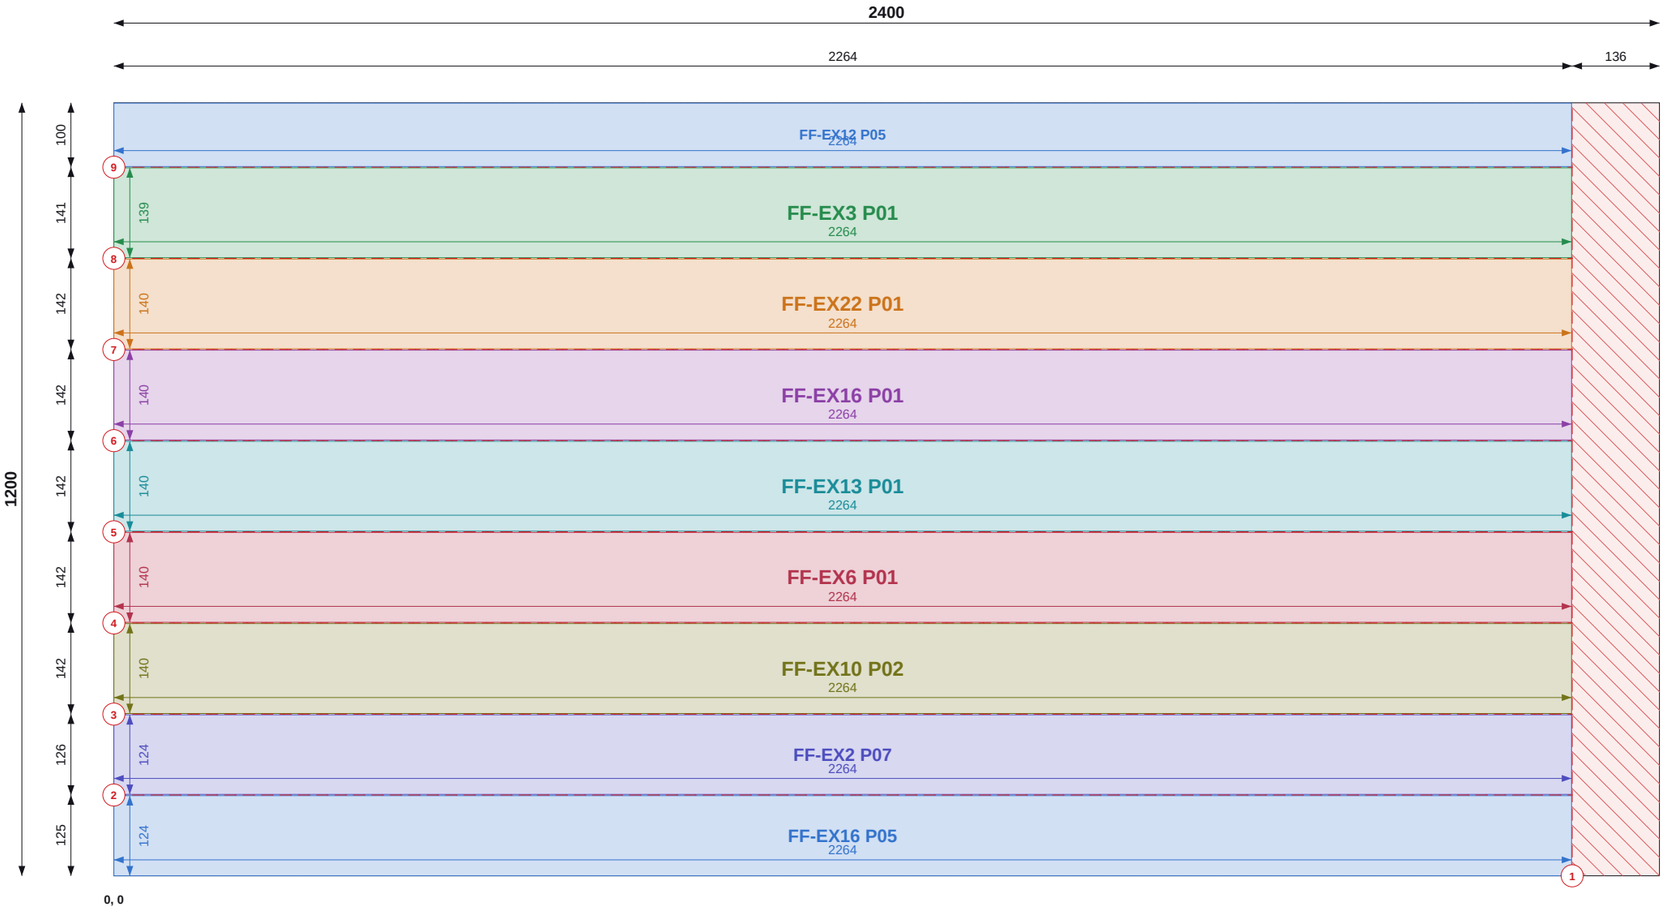

Top / left chains = saw cut positions (to cut centres). Coloured = part size and position.

SHEET 21 OF 23

THIS SHEET

Item	Value
Parts	9
Used / waste	93.0% / 0.20 m2
Reusable offcuts	0
Saw cuts / shared	9 / 8

PIECES (POSITION = BOTTOM-LEFT CORNER)

Label	Size	X, Y
FF-EX12 P05	99 x 2264	0, 1101
FF-EX3 P01	140 x 2264	0, 960
FF-EX22 P01	140 x 2264	0, 818
FF-EX16 P01	140 x 2264	0, 677
FF-EX13 P01	140 x 2264	0, 535
FF-EX6 P01	140 x 2264	0, 394
FF-EX10 P02	140 x 2264	0, 252
FF-EX2 P07	124 x 2264	0, 126
FF-EX16 P05	124 x 2264	0, 0

NOTES

1. Cut from PIR 120mm 1200x2400, 2mm saw kerf. Viewed on the face; dimensions from the sheet's bottom-left corner (0,0). Red numbered lines = saw cuts in order, each edge to edge.
2. Coloured dimensions belong to the part of that colour: its width and height, and its position from the sheet edges. Raked parts: corner coordinates at each corner.
3. Red hatch = waste. Labels = panel + piece mark on the manufacture drawing.

REVISIONS

REV	DATE	DESCRIPTION
C01	14.09.26	Construction issue
C02	14.09.26	Roof trusses revised; SP diagonals added

TLS TIMBER FRAME
Design & Manufacture
Scan: 3D model + drawings

CLIENT	PROJECT
MP Adams	MP Adams Plot 4, Eckington


DRAWING TITLE
PIR CUTTING - FIRST FLOOR - SHEET 21 OF 23

PIR 120mm 1200x2400 | First Floor

SCALE	SIZE	DATE	DRAWN
NTS	A3	14.09.26	TS

STATUS	DRAWING No.	REV
CONSTRUCTION	P4-CP-PIR-02 / 21	C02

Do not scale. All dimensions in mm. Check all dimensions on site.

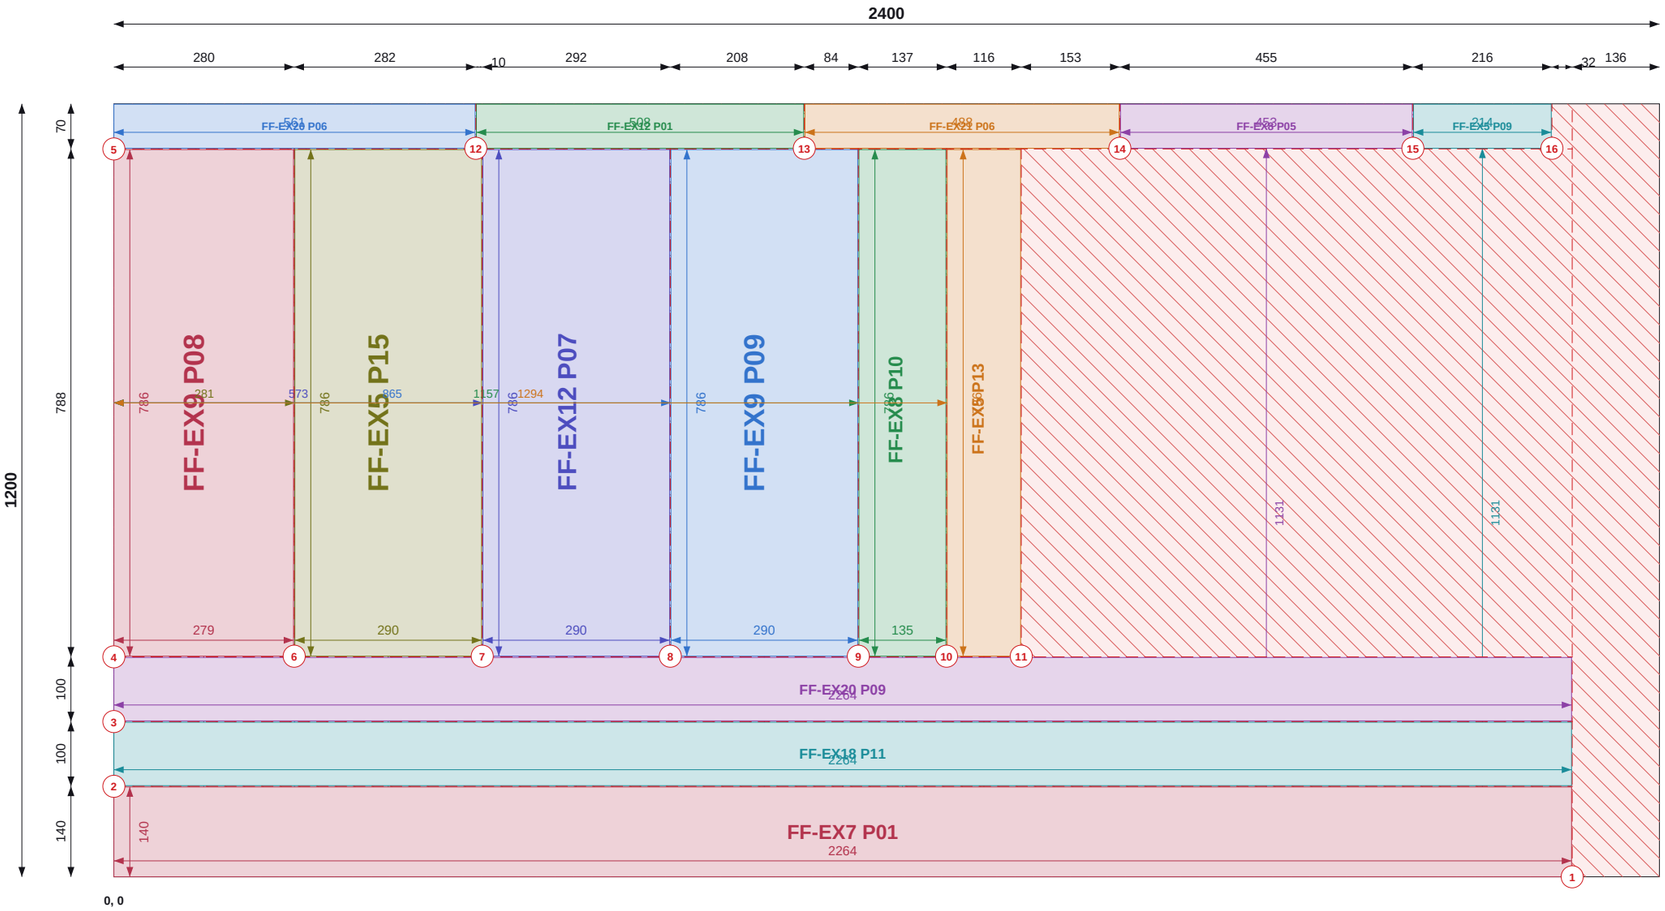

Top / left chains = saw cut positions (to cut centres). Coloured = part size and position.

Do not scale. All dimensions in mm. Check all dimensions on site.

SHEET 22 OF 23

THIS SHEET

Item	Value
Parts	14
Used / waste	69.9% / 0.87 m2
Reusable offcuts	1
Saw cuts / shared	16 / 13

PIECES (POSITION = BOTTOM-LEFT CORNER)

Label	Size	X, Y
FF-EX20 P06	561 x 69	0, 1131
FF-EX12 P01	508 x 69	563, 1131
FF-EX21 P06	488 x 69	1073, 1131
FF-EX8 P05	453 x 69	1563, 1131
FF-EX5 P09	214 x 69	2018, 1131
FF-EX9 P08	279 x 786	0, 343
FF-EX5 P15	290 x 786	281, 343
FF-EX12 P07	290 x 786	573, 343
FF-EX9 P09	290 x 786	865, 343
FF-EX8 P10	135 x 786	1157, 343
FF-EX5 P13	114 x 786	1294, 343
FF-EX20 P09	99 x 2264	0, 242
FF-EX18 P11	99 x 2264	0, 142
FF-EX7 P01	140 x 2264	0, 0

NOTES

1. Cut from PIR 120mm 1200x2400, 2mm saw kerf. Viewed on the face; dimensions from the sheet's bottom-left corner (0,0). Red numbered lines = saw cuts in order, each edge to edge.
2. Coloured dimensions belong to the part of that colour: its width and height, and its position from the sheet edges. Raked parts: corner coordinates at each corner.
3. Red hatch = waste. Labels = panel + piece mark on the manufacture drawing.

REVISIONS

REV	DATE	DESCRIPTION
C01	14.09.26	Construction issue
C02	14.09.26	Roof trusses revised; SP diagonals added

TLS TIMBER FRAME
Design & Manufacture
Scan: 3D model + drawings

CLIENT	PROJECT
MP Adams	MP Adams Plot 4, Eckington


DRAWING TITLE

PIR CUTTING - FIRST FLOOR - SHEET 22 OF 23

PIR 120mm 1200x2400 | First Floor

SCALE	SIZE	DATE	DRAWN
NTS	A3	14.09.26	TS

STATUS	DRAWING No.	REV
CONSTRUCTION	P4-CP-PIR-02 / 22	C02

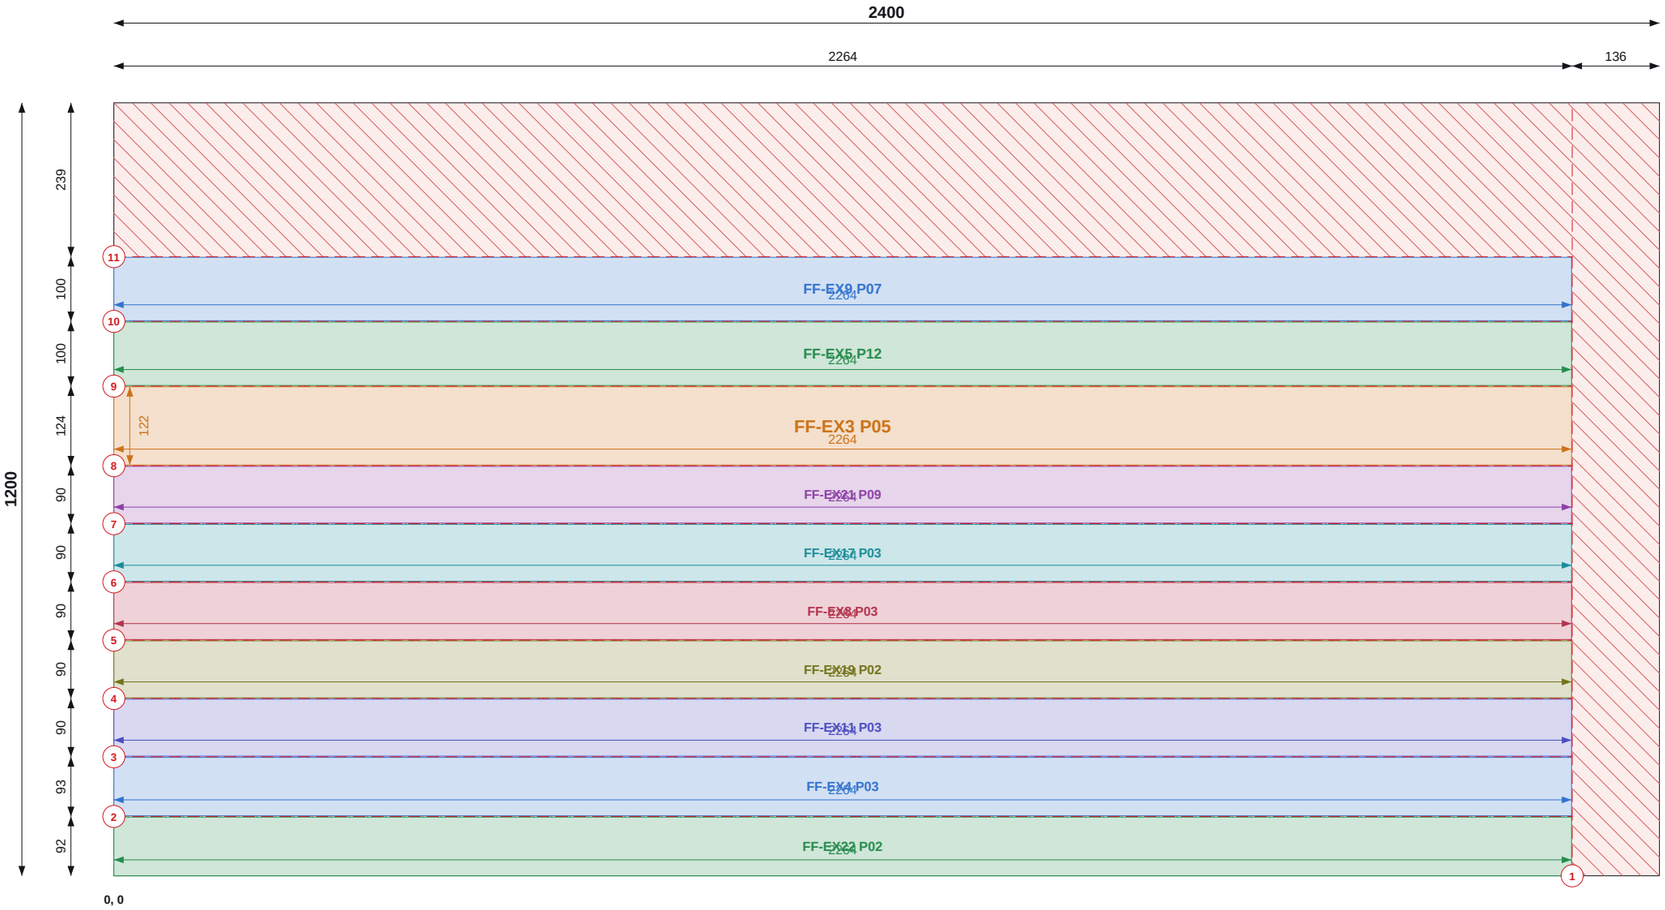

Top / left chains = saw cut positions (to cut centres). Coloured = part size and position.

Do not scale. All dimensions in mm. Check all dimensions on site.

SHEET 23 OF 23

THIS SHEET

Item	Value
Parts	10
Used / waste	74.1% / 0.75 m2
Reusable offcuts	0
Saw cuts / shared	11 / 9

PIECES (POSITION = BOTTOM-LEFT CORNER)

Label	Size	X, Y
FF-EX9 P07	98 x 2264	0, 862
FF-EX5 P12	98 x 2264	0, 761
FF-EX3 P05	122 x 2264	0, 638
FF-EX21 P09	88 x 2264	0, 548
FF-EX17 P03	88 x 2264	0, 457
FF-EX8 P03	88 x 2264	0, 367
FF-EX19 P02	88 x 2264	0, 276
FF-EX11 P03	88 x 2264	0, 186
FF-EX4 P03	91 x 2264	0, 93
FF-EX22 P02	91 x 2264	0, 0

NOTES

1. Cut from PIR 120mm 1200x2400, 2mm saw kerf. Viewed on the face; dimensions from the sheet's bottom-left corner (0,0). Red numbered lines = saw cuts in order, each edge to edge.
2. Coloured dimensions belong to the part of that colour: its width and height, and its position from the sheet edges. Raked parts: corner coordinates at each corner.
3. Red hatch = waste. Labels = panel + piece mark on the manufacture drawing.

REVISIONS

REV	DATE	DESCRIPTION
C01	14.09.26	Construction issue
C02	14.09.26	Roof trusses revised; SP diagonals added

TLS TIMBER FRAME
Design & Manufacture
Scan: 3D model + drawings


CLIENT	PROJECT
MP Adams	MP Adams Plot 4, Eckington

DRAWING TITLE
PIR CUTTING - FIRST FLOOR - SHEET 23 OF 23

PIR 120mm 1200x2400 | First Floor

SCALE	SIZE	DATE	DRAWN
NTS	A3	14.09.26	TS

STATUS	DRAWING No.	REV
CONSTRUCTION	P4-CP-PIR-02 / 23	C02

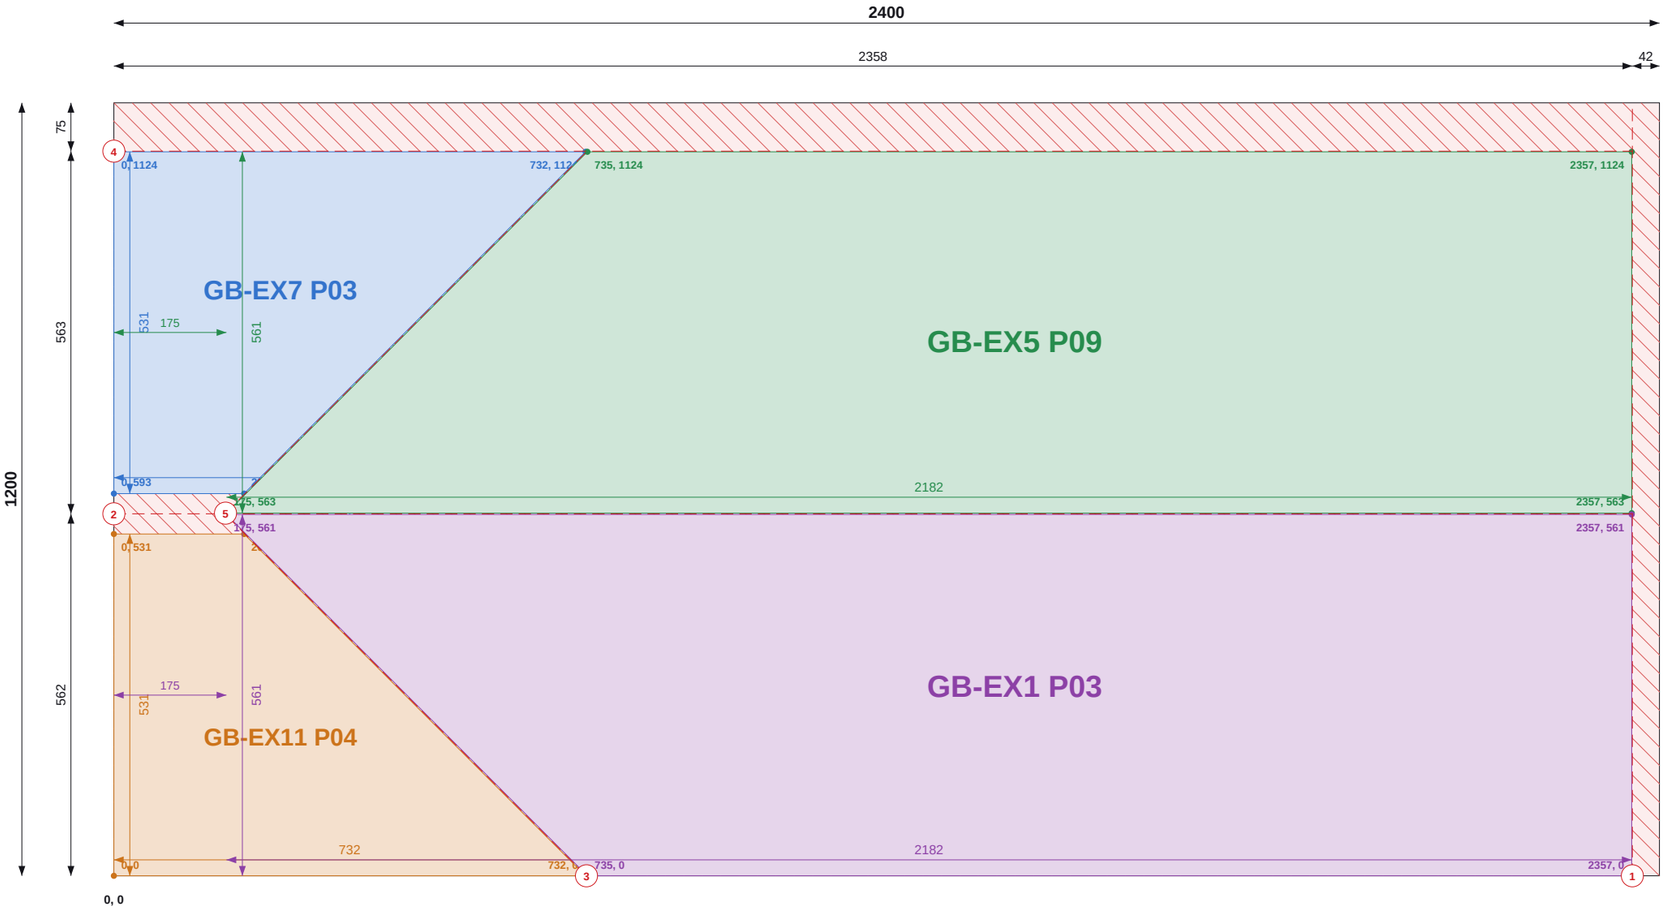

Top / left chains = saw cut positions (to cut centres). Coloured = part size and position.

Do not scale. All dimensions in mm. Check all dimensions on site.

SHEET 1 OF 18

THIS SHEET

Item	Value
Parts	4
Used / waste	91.3% / 0.25 m2
Reusable offcuts	0
Saw cuts / shared	5 / 3

PIECES (POSITION = BOTTOM-LEFT CORNER)

Label	Size	X, Y
GB-EX7 P03	531 x 732 rake to 203	0, 593
GB-EX5 P09	561 x 2182 rake to 1623	175, 563
GB-EX11 P04	531 x 732 rake to 203	0, 0
GB-EX1 P03	561 x 2182 rake to 1623	175, 0

GABLES TOTALS

Item	Value
Sheets / pieces	18 / 86
Yield / waste	83.1% / 8.77 m2
Saw cuts / shared / on stock edge	135 / 80 / 69

NOTES

1. Cut from PIR 120mm 1200x2400, 2mm saw kerf. Viewed on the face; dimensions from the sheet's bottom-left corner (0,0). Red numbered lines = saw cuts in order, each edge to edge.
2. Coloured dimensions belong to the part of that colour: its width and height, and its position from the sheet edges. Raked parts: corner coordinates at each corner.
3. Red hatch = waste. Labels = panel + piece mark on the manufacture drawing.

REVISIONS

REV	DATE	DESCRIPTION
C01	14.09.26	Construction issue
C02	14.09.26	Roof trusses revised; SP diagonals added

TLS TIMBER FRAME
Design & Manufacture
Scan: 3D model + drawings


CLIENT	PROJECT
MP Adams	MP Adams Plot 4, Eckington

DRAWING TITLE
PIR CUTTING - GABLES - SHEET 1 OF 18

PIR 120mm 1200x2400 | Gables

SCALE	SIZE	DATE	DRAWN
NTS	A3	14.09.26	TS

STATUS	DRAWING No.	REV
CONSTRUCTION	P4-CP-PIR-03 / 01	C02

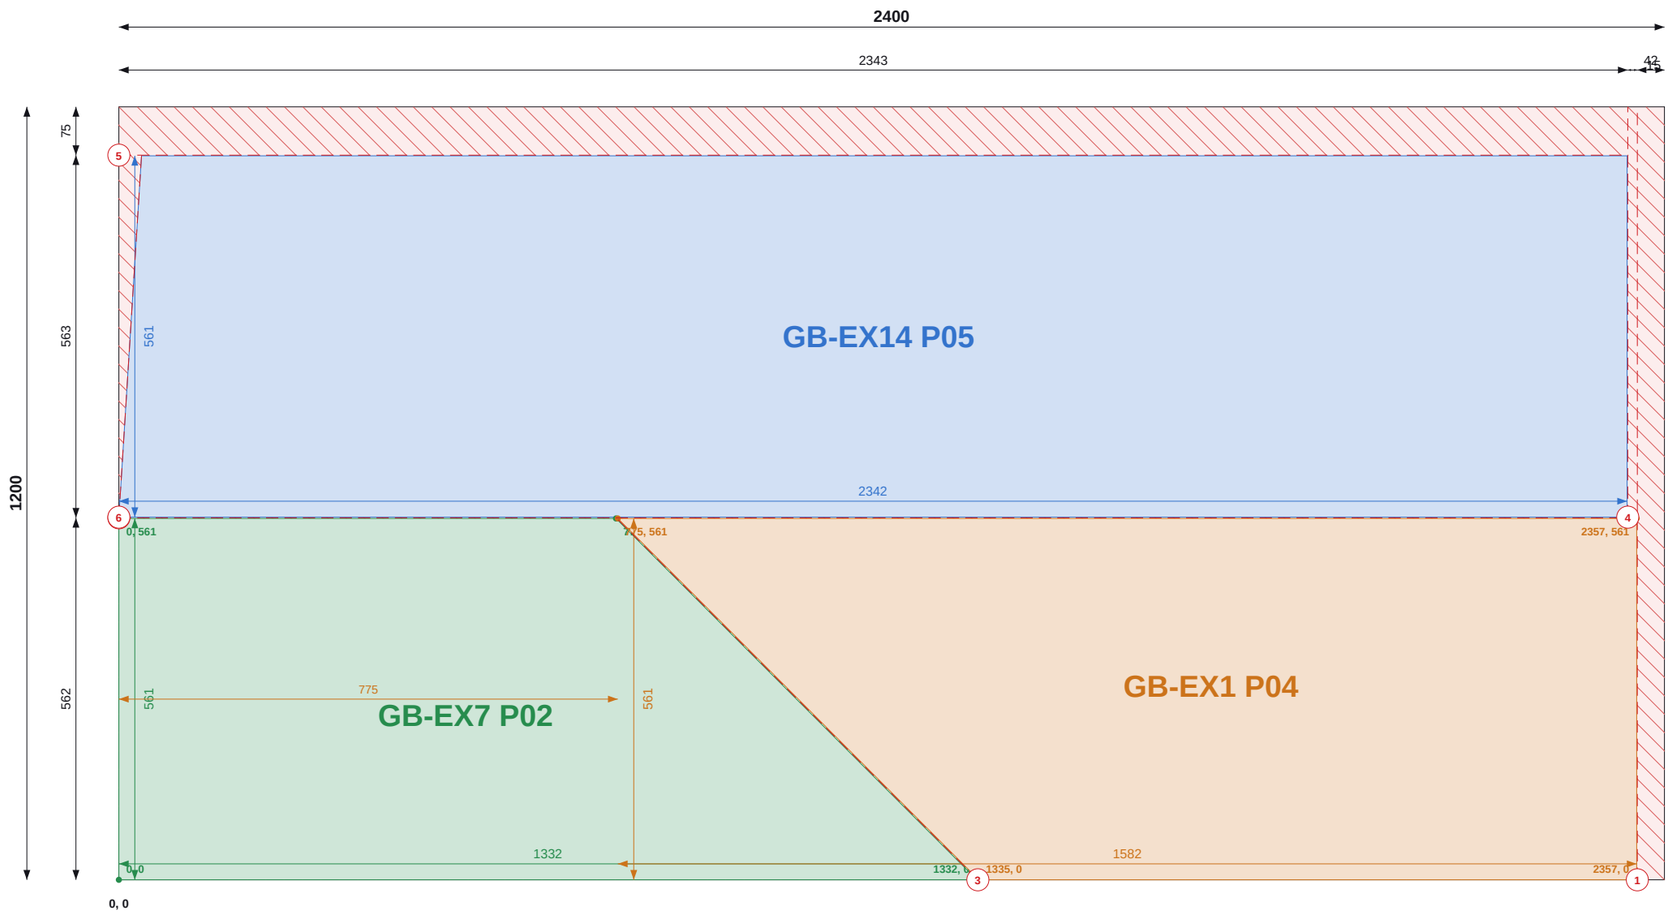

Top / left chains = saw cut positions (to cut centres). Coloured = part size and position.

SHEET 2 OF 18

THIS SHEET

Item	Value
Parts	3
Used / waste	91.1% / 0.26 m2
Reusable offcuts	0
Saw cuts / shared	6 / 3

PIECES (POSITION = BOTTOM-LEFT CORNER)

Label	Size	X, Y
GB-EX14 P05	561 x 2342	0, 563
GB-EX7 P02	561 x 1332 rake to 773	0, 0
GB-EX1 P04	561 x 1582 rake to 1023	775, 0

NOTES

1. Cut from PIR 120mm 1200x2400, 2mm saw kerf. Viewed on the face; dimensions from the sheet's bottom-left corner (0,0). Red numbered lines = saw cuts in order, each edge to edge.
2. Coloured dimensions belong to the part of that colour: its width and height, and its position from the sheet edges. Raked parts: corner coordinates at each corner.
3. Red hatch = waste. Labels = panel + piece mark on the manufacture drawing.

REVISIONS

REV	DATE	DESCRIPTION
C01	14.09.26	Construction issue
C02	14.09.26	Roof trusses revised; SP diagonals added

TLS TIMBER FRAME
Design & Manufacture
Scan: 3D model + drawings


CLIENT	PROJECT
MP Adams	MP Adams Plot 4, Eckington

DRAWING TITLE
PIR CUTTING - GABLES - SHEET 2 OF 18
PIR 120mm 1200x2400 | Gables

SCALE	SIZE	DATE	DRAWN
NTS	A3	14.09.26	TS

STATUS	DRAWING No.	REV
CONSTRUCTION	P4-CP-PIR-03 / 02	C02

Do not scale. All dimensions in mm. Check all dimensions on site.

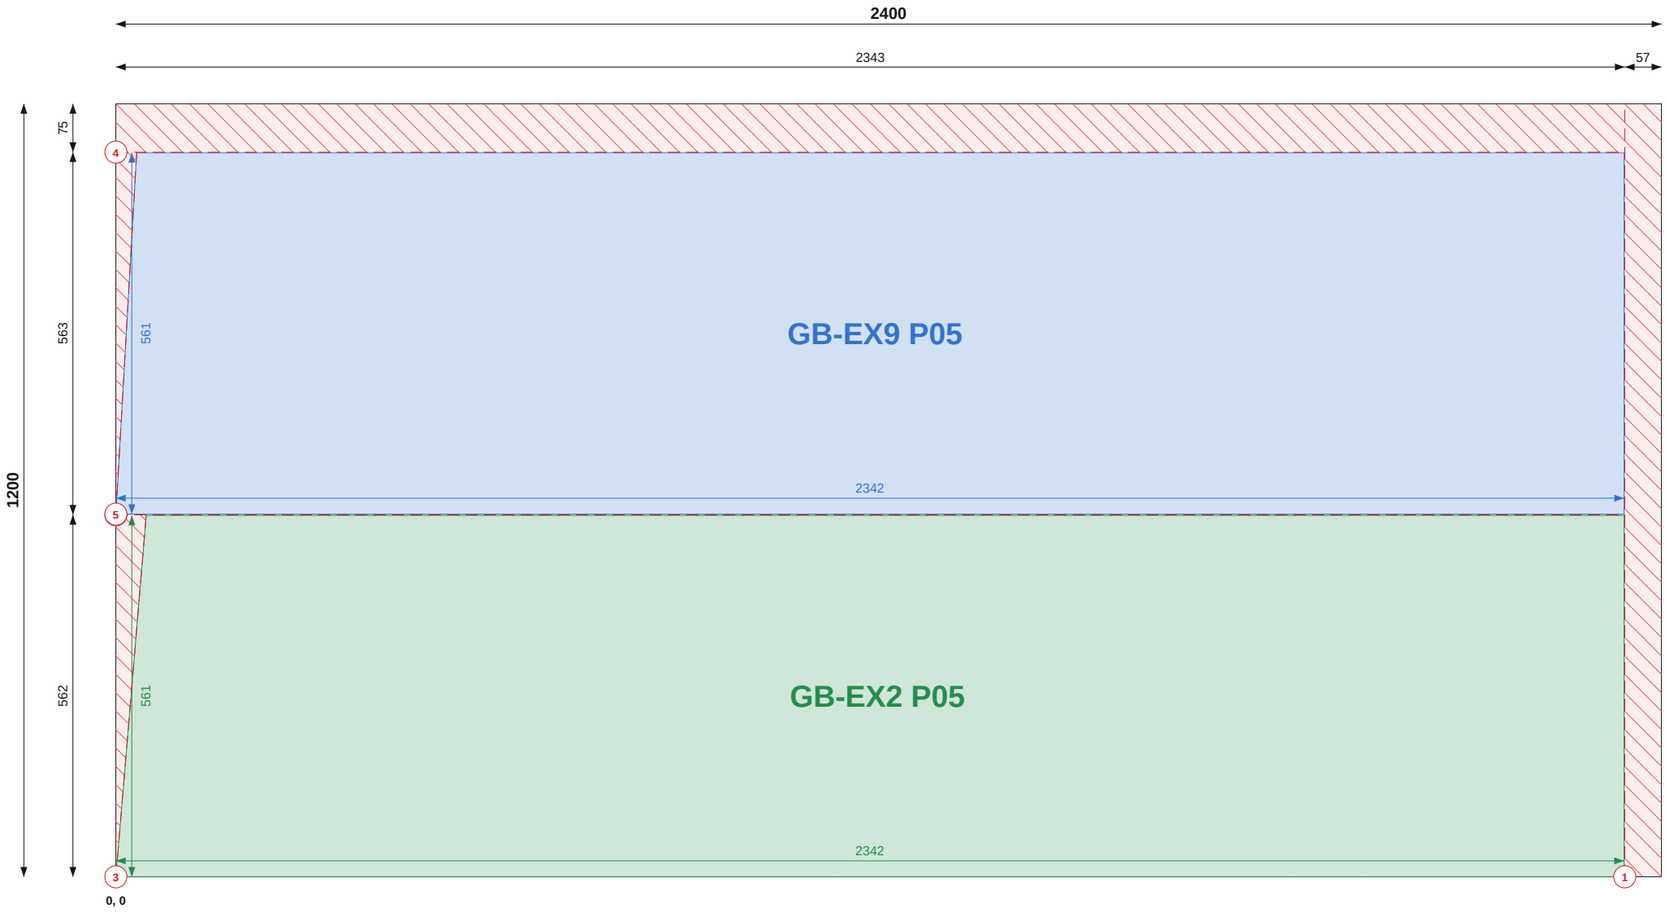

Top / left chains = saw cut positions (to cut centres). Coloured = part size and position.

SHEET 3 OF 18

THIS SHEET

Item	Value
Parts	2
Used / waste	90.5% / 0.27 m2
Reusable offcuts	0
Saw cuts / shared	5 / 3

PIECES (POSITION = BOTTOM-LEFT CORNER)

Label	Size	X, Y
GB-EX9 P05	561 x 2342	0, 563
GB-EX2 P05	561 x 2342	0, 0

NOTES

1. Cut from PIR 120mm 1200x2400, 2mm saw kerf. Viewed on the face; dimensions from the sheet's bottom-left corner (0,0). Red numbered lines = saw cuts in order, each edge to edge.
2. Coloured dimensions belong to the part of that colour: its width and height, and its position from the sheet edges. Raked parts: corner coordinates at each corner.
3. Red hatch = waste. Labels = panel + piece mark on the manufacture drawing.

REVISIONS

REV	DATE	DESCRIPTION
C01	14.09.26	Construction issue
C02	14.09.26	Roof trusses revised; SP diagonals added

TLS TIMBER FRAME DESIGN SUITE

TLS TIMBER FRAME

Design & Manufacture

Scan: 3D model + drawings

CLIENT	PROJECT
MP Adams	MP Adams Plot 4, Eckington

DRAWING TITLE


PIR CUTTING - GABLES - SHEET 3 OF 18

PIR 120mm 1200x2400 | Gables

SCALE	SIZE	DATE	DRAWN
NTS	A3	14.09.26	TS

STATUS	DRAWING No.	REV
CONSTRUCTION	P4-CP-PIR-03 / 03	C02

Do not scale. All dimensions in mm. Check all dimensions on site.

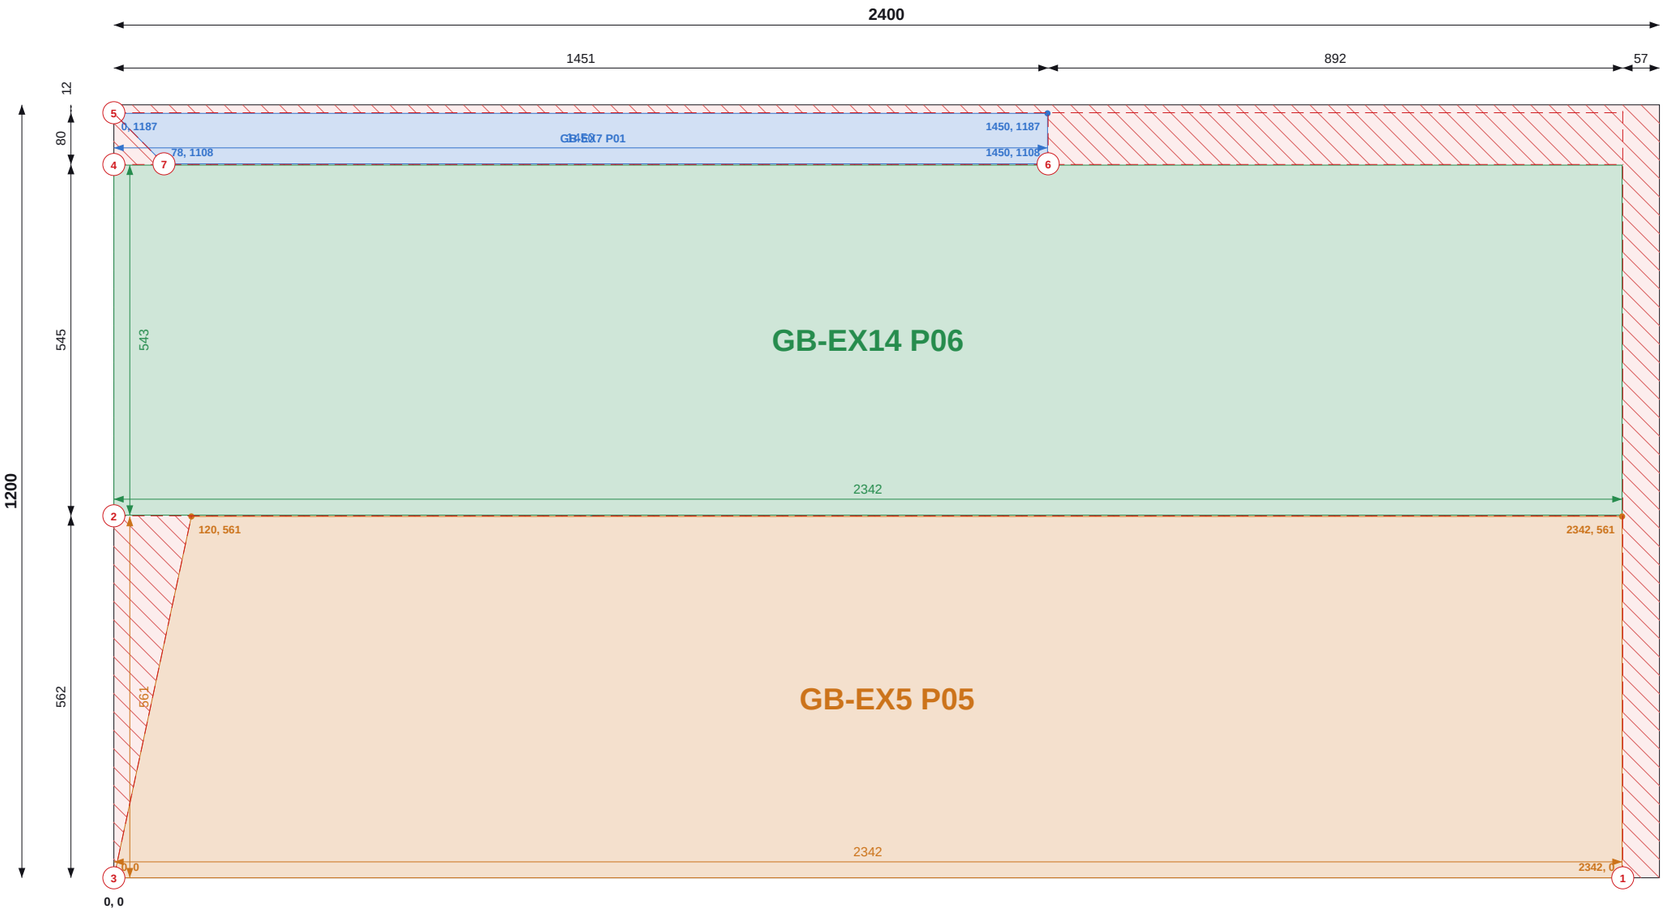

Top / left chains = saw cut positions (to cut centres). Coloured = part size and position.

SHEET 4 OF 18

THIS SHEET

Item	Value
Parts	3
Used / waste	92.5% / 0.22 m2
Reusable offcuts	0
Saw cuts / shared	7 / 4

PIECES (POSITION = BOTTOM-LEFT CORNER)

Label	Size	X, Y
GB-EX7 P01	78 x 1450 rake to 1373	0, 1108
GB-EX14 P06	543 x 2342	0, 563
GB-EX5 P05	561 x 2342 rake to 2222	0, 0

NOTES

1. Cut from PIR 120mm 1200x2400, 2mm saw kerf. Viewed on the face; dimensions from the sheet's bottom-left corner (0,0). Red numbered lines = saw cuts in order, each edge to edge.
2. Coloured dimensions belong to the part of that colour: its width and height, and its position from the sheet edges. Raked parts: corner coordinates at each corner.
3. Red hatch = waste. Labels = panel + piece mark on the manufacture drawing.

REVISIONS

REV	DATE	DESCRIPTION
C01	14.09.26	Construction issue
C02	14.09.26	Roof trusses revised; SP diagonals added

TLS TIMBER FRAME
Design & Manufacture
Scan: 3D model + drawings

CLIENT	PROJECT
MP Adams	MP Adams Plot 4, Eckington

DRAWING TITLE


PIR CUTTING - GABLES - SHEET 4 OF 18

PIR 120mm 1200x2400 | Gables

SCALE	SIZE	DATE	DRAWN
NTS	A3	14.09.26	TS

STATUS	DRAWING No.	REV
CONSTRUCTION	P4-CP-PIR-03 / 04	C02

Do not scale. All dimensions in mm. Check all dimensions on site.

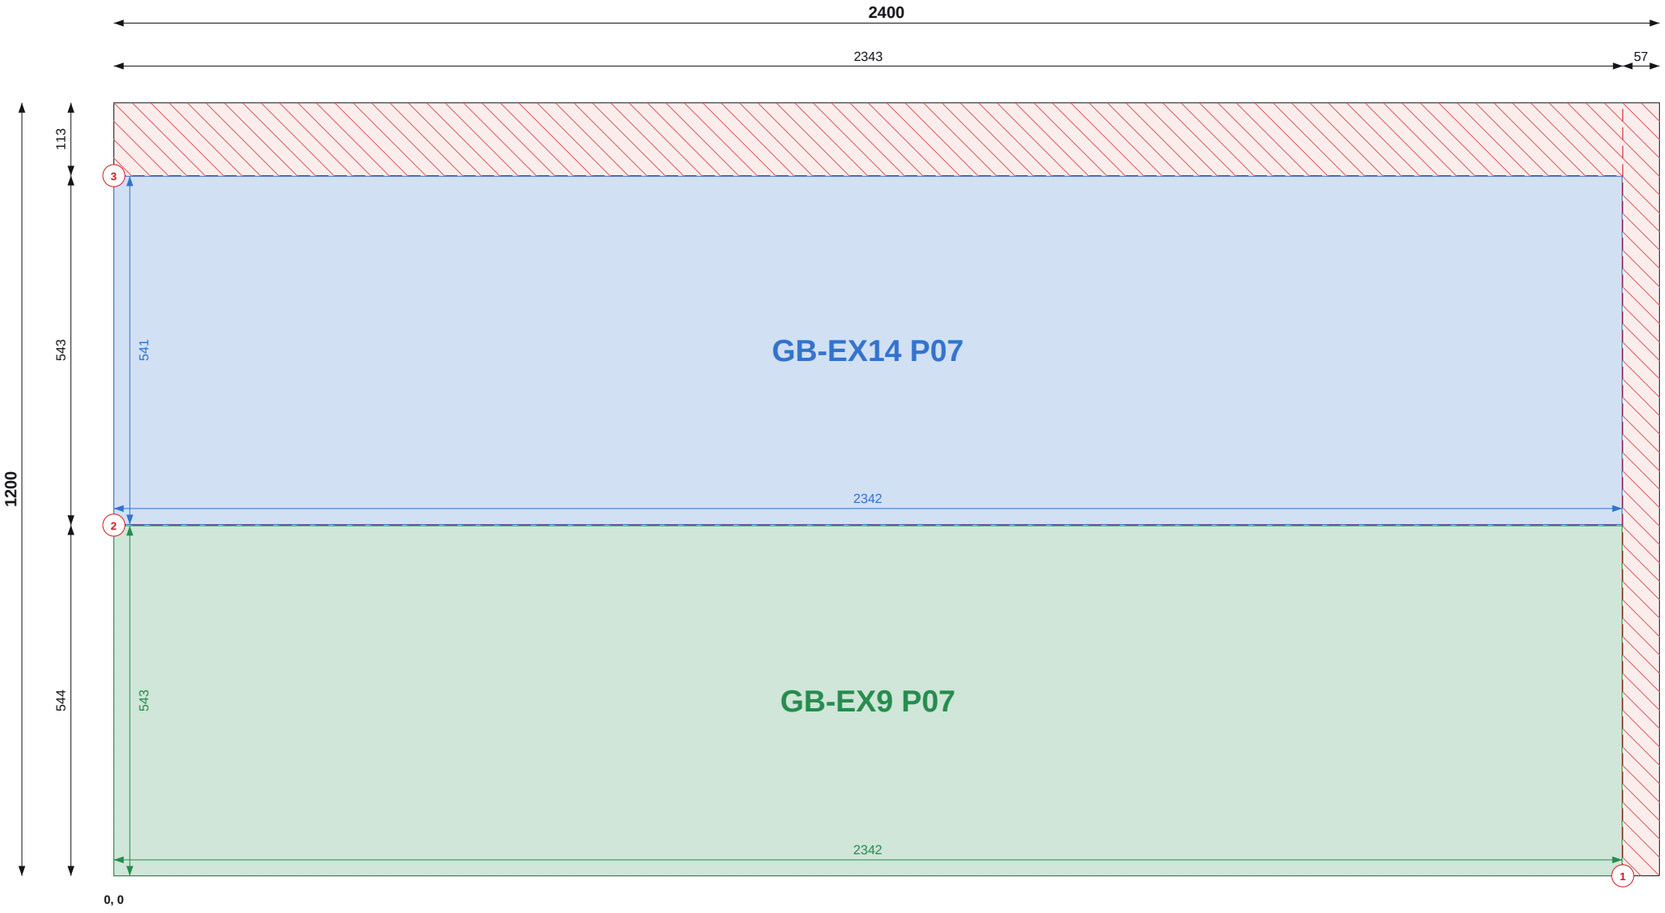

Top / left chains = saw cut positions (to cut centres). Coloured = part size and position.

SHEET 5 OF 18

THIS SHEET

Item	Value
Parts	2
Used / waste	88.2% / 0.34 m2
Reusable offcuts	0
Saw cuts / shared	3 / 1

PIECES (POSITION = BOTTOM-LEFT CORNER)

Label	Size	X, Y
GB-EX14 P07	541 x 2342	0, 545
GB-EX9 P07	543 x 2342	0, 0

NOTES

1. Cut from PIR 120mm 1200x2400, 2mm saw kerf. Viewed on the face; dimensions from the sheet's bottom-left corner (0,0). Red numbered lines = saw cuts in order, each edge to edge.
2. Coloured dimensions belong to the part of that colour: its width and height, and its position from the sheet edges. Raked parts: corner coordinates at each corner.
3. Red hatch = waste. Labels = panel + piece mark on the manufacture drawing.

REVISIONS

REV	DATE	DESCRIPTION
C01	14.09.26	Construction issue
C02	14.09.26	Roof trusses revised; SP diagonals added

TLS TIMBER FRAME
Design & Manufacture
Scan: 3D model + drawings

CLIENT	PROJECT
MP Adams	MP Adams Plot 4, Eckington


DRAWING TITLE
PIR CUTTING - GABLES - SHEET 5 OF 18

PIR 120mm 1200x2400 | Gables

SCALE	SIZE	DATE	DRAWN
NTS	A3	14.09.26	TS

STATUS	DRAWING No.	REV
CONSTRUCTION	P4-CP-PIR-03 / 05	C02

Do not scale. All dimensions in mm. Check all dimensions on site.

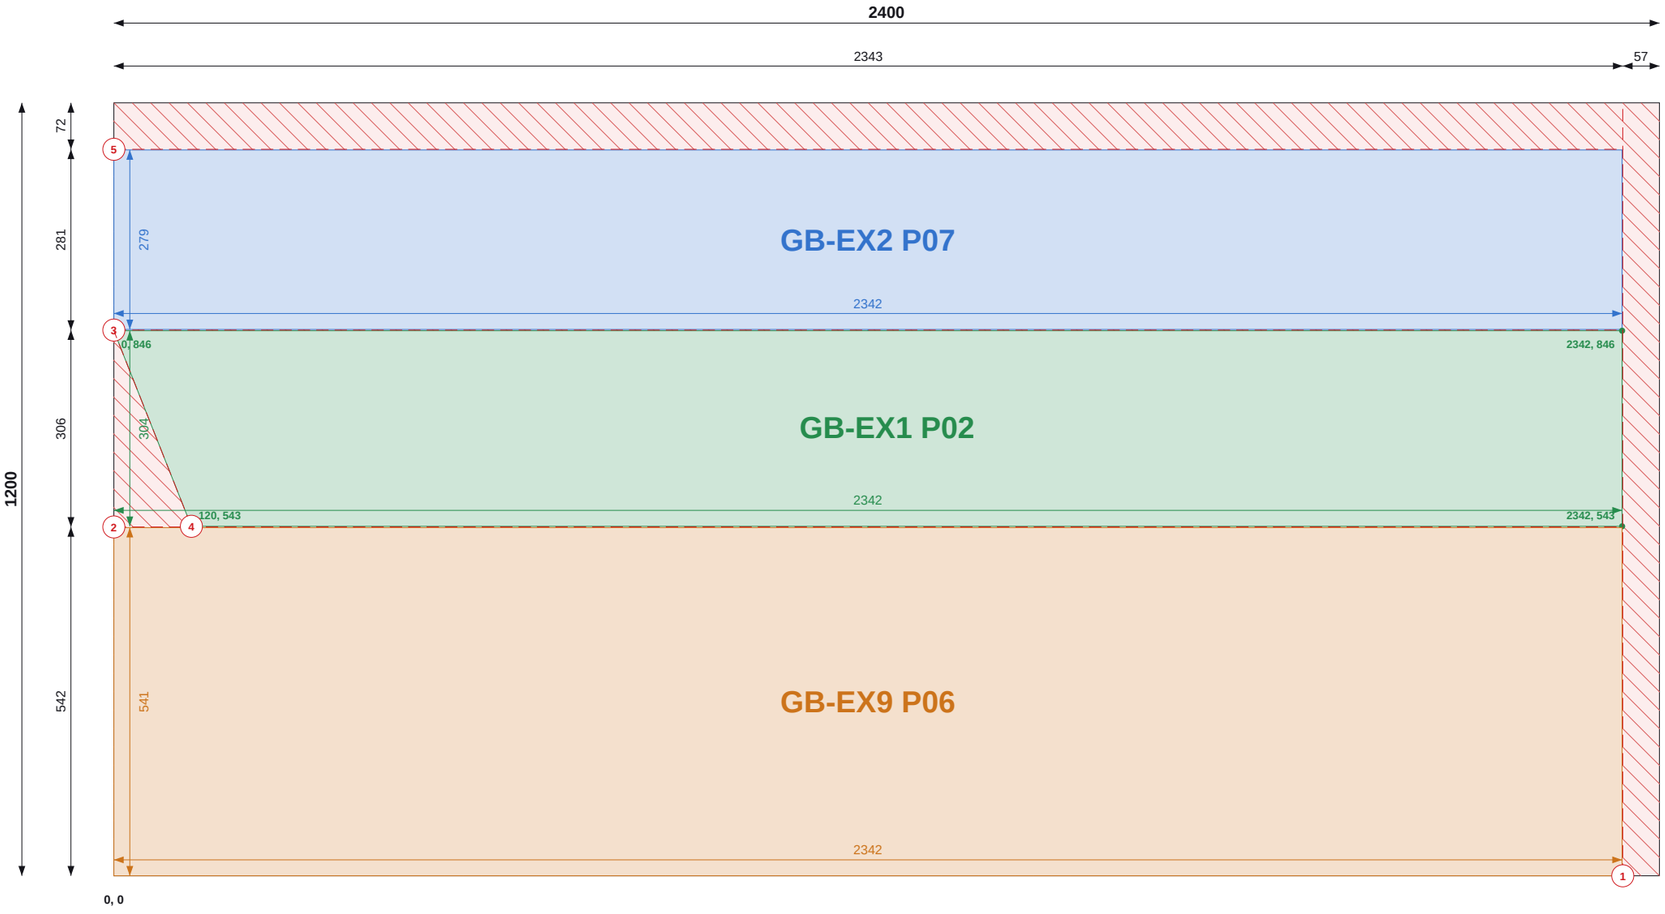

Top / left chains = saw cut positions (to cut centres). Coloured = part size and position.

SHEET 6 OF 18

THIS SHEET

Item	Value
Parts	3
Used / waste	90.7% / 0.27 m2
Reusable offcuts	0
Saw cuts / shared	5 / 3

PIECES (POSITION = BOTTOM-LEFT CORNER)

Label	Size	X, Y
GB-EX2 P07	279 x 2342	0, 848
GB-EX1 P02	304 x 2342 rake to 2222	0, 543
GB-EX9 P06	541 x 2342	0, 0

NOTES

1. Cut from PIR 120mm 1200x2400, 2mm saw kerf. Viewed on the face; dimensions from the sheet's bottom-left corner (0,0). Red numbered lines = saw cuts in order, each edge to edge.
2. Coloured dimensions belong to the part of that colour: its width and height, and its position from the sheet edges. Raked parts: corner coordinates at each corner.
3. Red hatch = waste. Labels = panel + piece mark on the manufacture drawing.

REVISIONS

REV	DATE	DESCRIPTION
C01	14.09.26	Construction issue
C02	14.09.26	Roof trusses revised; SP diagonals added

TLS TIMBER FRAME
Design & Manufacture
Scan: 3D model + drawings

CLIENT	PROJECT
MP Adams	MP Adams Plot 4, Eckington


DRAWING TITLE
PIR CUTTING - GABLES - SHEET 6 OF 18

PIR 120mm 1200x2400 | Gables

SCALE	SIZE	DATE	DRAWN
NTS	A3	14.09.26	TS

STATUS	DRAWING No.	REV
CONSTRUCTION	P4-CP-PIR-03 / 06	C02

Do not scale. All dimensions in mm. Check all dimensions on site.

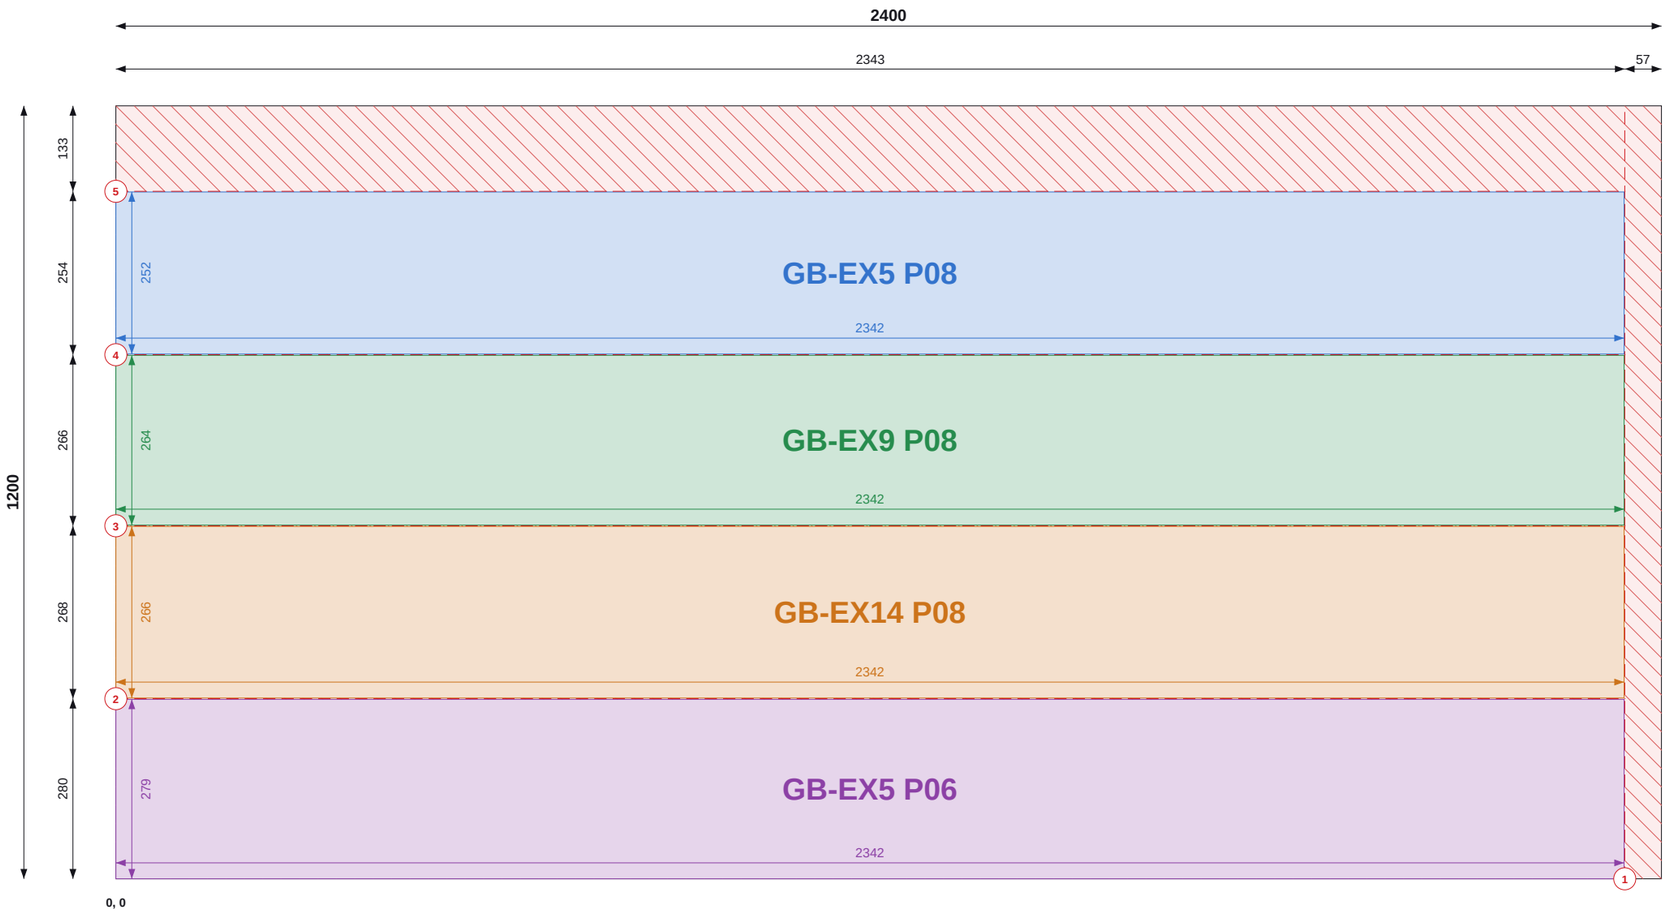

Top / left chains = saw cut positions (to cut centres). Coloured = part size and position.

SHEET 7 OF 18

THIS SHEET

Item	Value
Parts	4
Used / waste	86.2% / 0.40 m2
Reusable offcuts	0
Saw cuts / shared	5 / 3

PIECES (POSITION = BOTTOM-LEFT CORNER)

Label	Size	X, Y
GB-EX5 P08	252 x 2342	0, 815
GB-EX9 P08	264 x 2342	0, 549
GB-EX14 P08	266 x 2342	0, 281
GB-EX5 P06	279 x 2342	0, 0

NOTES

1. Cut from PIR 120mm 1200x2400, 2mm saw kerf. Viewed on the face; dimensions from the sheet's bottom-left corner (0,0). Red numbered lines = saw cuts in order, each edge to edge.
2. Coloured dimensions belong to the part of that colour: its width and height, and its position from the sheet edges. Raked parts: corner coordinates at each corner.
3. Red hatch = waste. Labels = panel + piece mark on the manufacture drawing.

REVISIONS

REV	DATE	DESCRIPTION
C01	14.09.26	Construction issue
C02	14.09.26	Roof trusses revised; SP diagonals added

TLS TIMBER FRAME
Design & Manufacture
Scan: 3D model + drawings


CLIENT	PROJECT
MP Adams	MP Adams Plot 4, Eckington

DRAWING TITLE
PIR CUTTING - GABLES - SHEET 7 OF 18
PIR 120mm 1200x2400 | Gables

SCALE	SIZE	DATE	DRAWN
NTS	A3	14.09.26	TS

STATUS	DRAWING No.	REV
CONSTRUCTION	P4-CP-PIR-03 / 07	C02

Do not scale. All dimensions in mm. Check all dimensions on site.

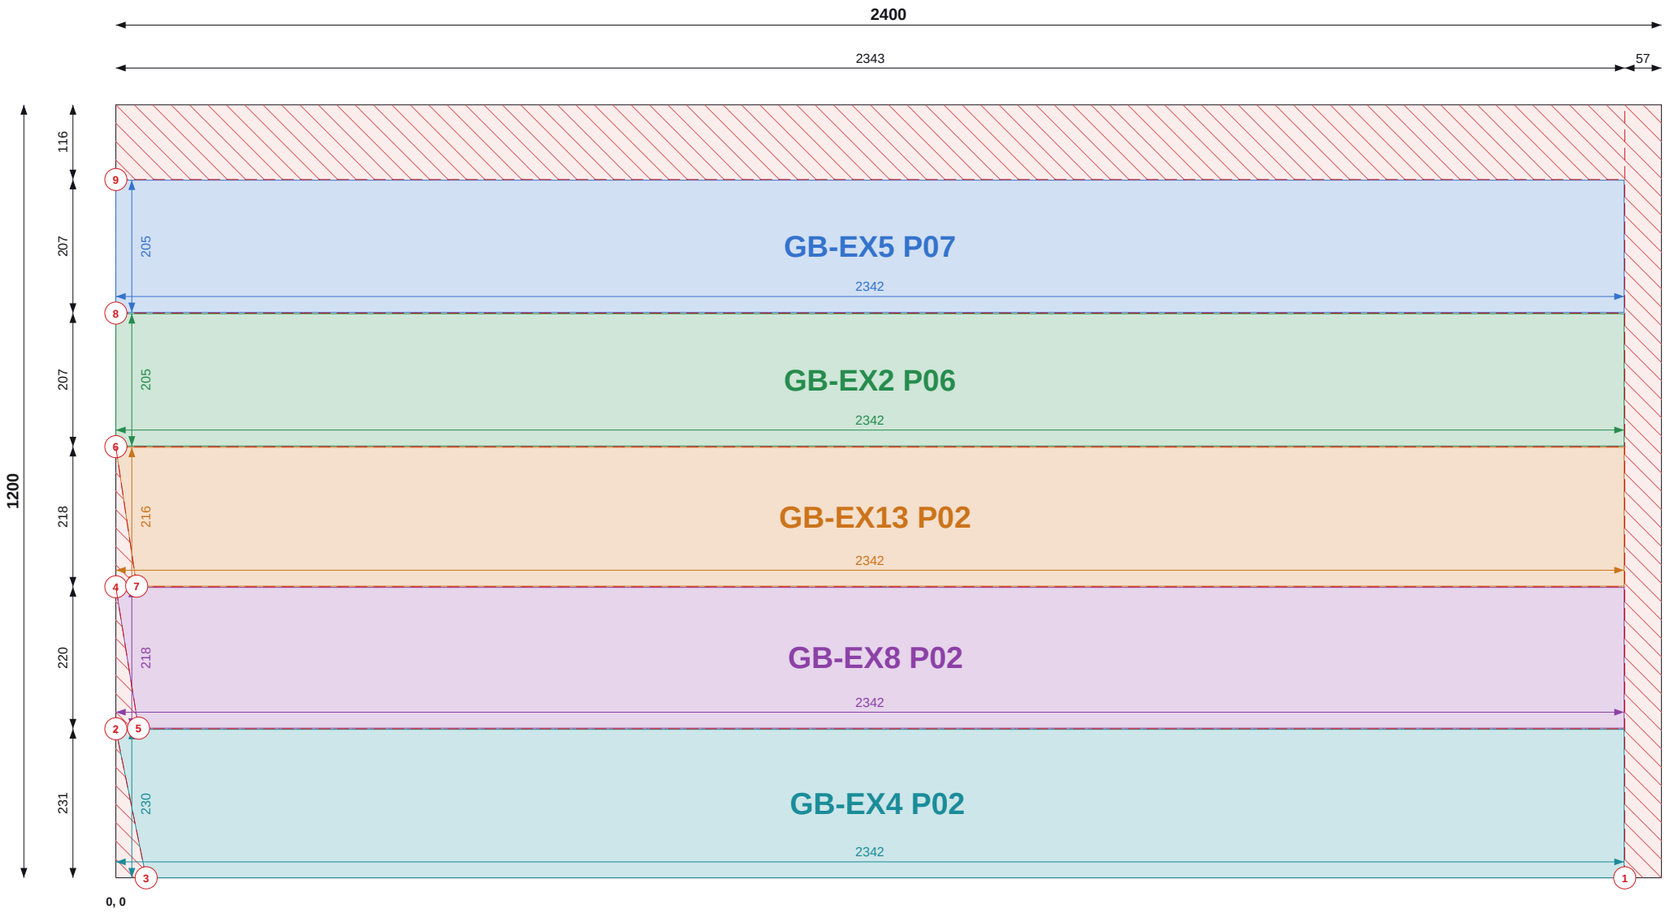

Top / left chains = saw cut positions (to cut centres). Coloured = part size and position.

SHEET 8 OF 18

THIS SHEET

Item	Value
Parts	5
Used / waste	87.0% / 0.37 m2
Reusable offcuts	0
Saw cuts / shared	9 / 7

PIECES (POSITION = BOTTOM-LEFT CORNER)

Label	Size	X, Y
GB-EX5 P07	205 x 2342	0, 878
GB-EX2 P06	205 x 2342	0, 670
GB-EX13 P02	216 x 2342	0, 453
GB-EX8 P02	218 x 2342	0, 232
GB-EX4 P02	230 x 2342	0, 0

NOTES

1. Cut from PIR 120mm 1200x2400, 2mm saw kerf. Viewed on the face; dimensions from the sheet's bottom-left corner (0,0). Red numbered lines = saw cuts in order, each edge to edge.
2. Coloured dimensions belong to the part of that colour: its width and height, and its position from the sheet edges. Raked parts: corner coordinates at each corner.
3. Red hatch = waste. Labels = panel + piece mark on the manufacture drawing.

REVISIONS

REV	DATE	DESCRIPTION
C01	14.09.26	Construction issue
C02	14.09.26	Roof trusses revised; SP diagonals added

TLS TIMBER FRAME
Design & Manufacture
Scan: 3D model + drawings

CLIENT	PROJECT
MP Adams	MP Adams Plot 4, Eckington

DRAWING TITLE


PIR CUTTING - GABLES - SHEET 8 OF 18

PIR 120mm 1200x2400 | Gables

SCALE	SIZE	DATE	DRAWN
NTS	A3	14.09.26	TS

STATUS	DRAWING No.	REV
CONSTRUCTION	P4-CP-PIR-03 / 08	C02

Do not scale. All dimensions in mm. Check all dimensions on site.

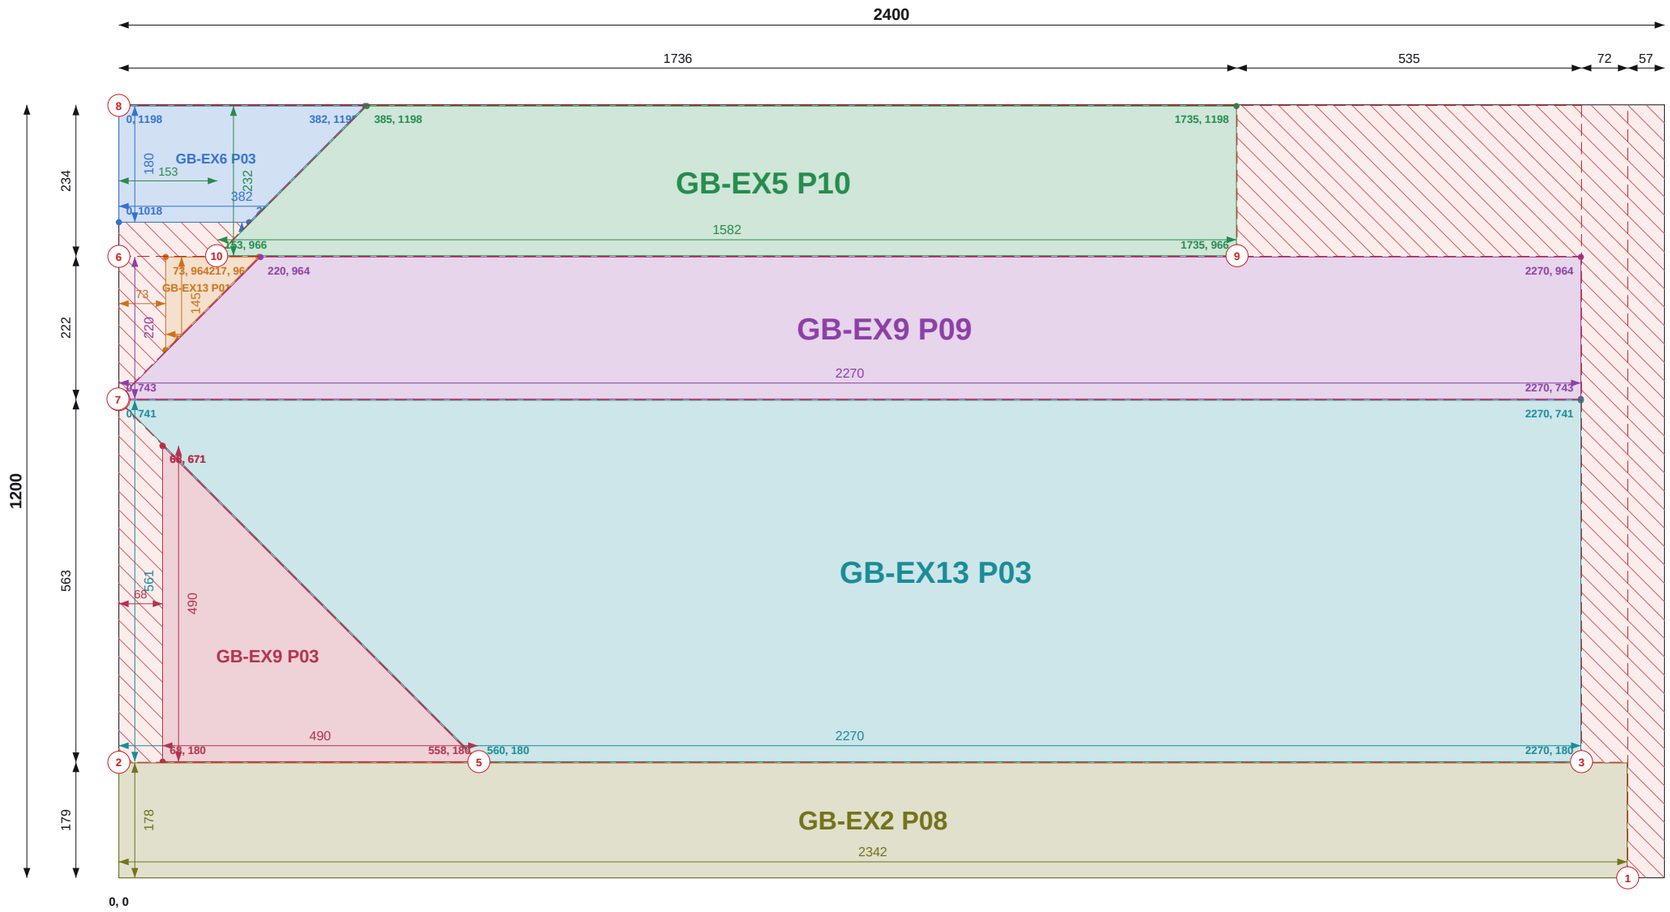

Top / left chains = saw cut positions (to cut centres). Coloured = part size and position.

SHEET 9 OF 18

THIS SHEET

Item	Value
Parts	7
Used / waste	88.0% / 0.35 m2
Reusable offcuts	0
Saw cuts / shared	10 / 6

PIECES (POSITION = BOTTOM-LEFT CORNER)

Label	Size	X, Y
GB-EX6 P03	180 x 382 rake to 203	0, 1018
GB-EX5 P10	232 x 1582 rake to 1351	153, 966
GB-EX13 P01	145 x 144 rake to 1	73, 819
GB-EX9 P09	220 x 2270 rake to 2051	0, 743
GB-EX13 P03	561 x 2270 rake to 1711	0, 180
GB-EX9 P03	490 x 490 rake to 1	68, 180
GB-EX2 P08	178 x 2342	0, 0

NOTES

1. Cut from PIR 120mm 1200x2400, 2mm saw kerf. Viewed on the face; dimensions from the sheet's bottom-left corner (0,0). Red numbered lines = saw cuts in order, each edge to edge.
2. Coloured dimensions belong to the part of that colour: its width and height, and its position from the sheet edges. Raked parts: corner coordinates at each corner.
3. Red hatch = waste. Labels = panel + piece mark on the manufacture drawing.

REVISIONS

REV	DATE	DESCRIPTION
C01	14.09.26	Construction issue
C02	14.09.26	Roof trusses revised; SP diagonals added

TLS TIMBER FRAME
Design & Manufacture
Scan: 3D model + drawings

CLIENT	PROJECT
MP Adams	MP Adams Plot 4, Eckington


DRAWING TITLE
PIR CUTTING - GABLES - SHEET 9 OF 18

PIR 120mm 1200x2400 | Gables

SCALE	SIZE	DATE	DRAWN
NTS	A3	14.09.26	TS

STATUS	DRAWING No.	REV
CONSTRUCTION	P4-CP-PIR-03 / 09	C02

Do not scale. All dimensions in mm. Check all dimensions on site.

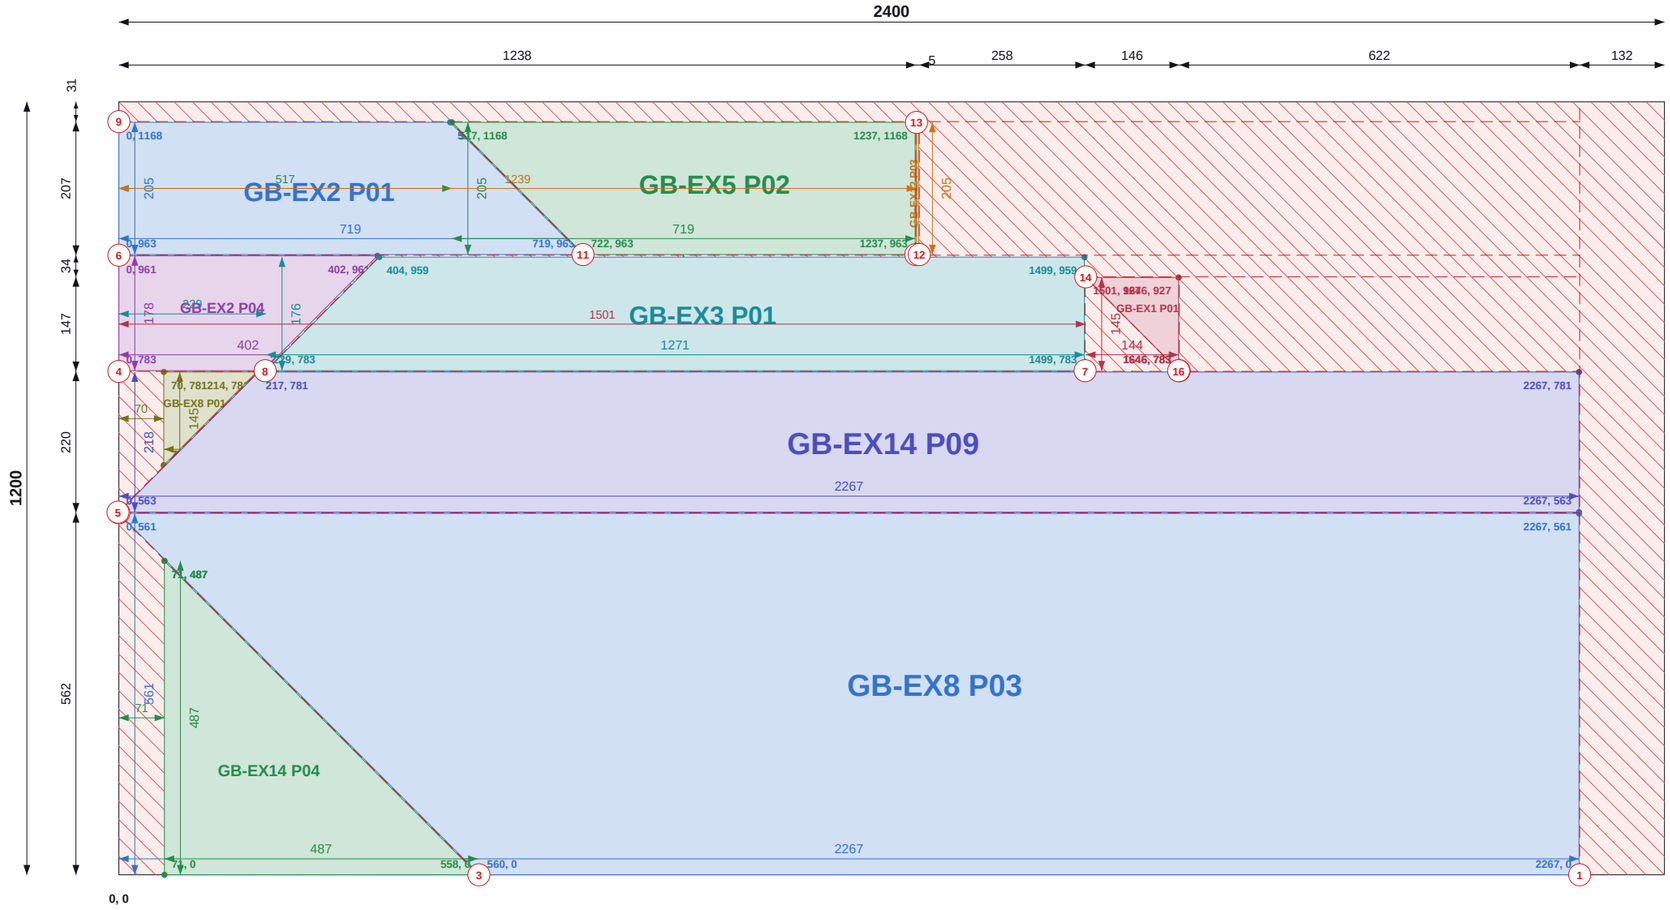

Top / left chains = saw cut positions (to cut centres). Coloured = part size and position.

Do not scale. All dimensions in mm. Check all dimensions on site.

SHEET 10 OF 18

THIS SHEET

Item	Value
Parts	10
Used / waste	77.9% / 0.64 m2
Reusable offcuts	0
Saw cuts / shared	16 / 11

PIECES (POSITION = BOTTOM-LEFT CORNER)

Label	Size	X, Y
GB-EX2 P01	205 x 719 rake to 516	0, 963
GB-EX5 P02	205 x 719 rake to 516	517, 963
GB-EX12 P03	3 x 205	1239, 963
GB-EX2 P04	178 x 402 rake to 225	0, 783
GB-EX3 P01	176 x 1271 rake to 1096	229, 783
GB-EX1 P01	145 x 144 rake to 1	1501, 783
GB-EX8 P01	145 x 144 rake to 1	70, 636
GB-EX14 P09	218 x 2267 rake to 2051	0, 563
GB-EX8 P03	561 x 2267 rake to 1708	0, 0
GB-EX14 P04	487 x 487 rake to 1	71, 0

NOTES

1. Cut from PIR 120mm 1200x2400, 2mm saw kerf. Viewed on the face; dimensions from the sheet's bottom-left corner (0,0). Red numbered lines = saw cuts in order, each edge to edge.
2. Coloured dimensions belong to the part of that colour: its width and height, and its position from the sheet edges. Raked parts: corner coordinates at each corner.
3. Red hatch = waste. Labels = panel + piece mark on the manufacture drawing.

REVISIONS

REV	DATE	DESCRIPTION
C01	14.09.26	Construction issue
C02	14.09.26	Roof trusses revised; SP diagonals added

TLS TIMBER FRAME
Design & Manufacture
Scan: 3D model + drawings


CLIENT	PROJECT
MP Adams	MP Adams Plot 4, Eckington

DRAWING TITLE
PIR CUTTING - GABLES - SHEET 10 OF 18

PIR 120mm 1200x2400 | Gables

SCALE	SIZE	DATE	DRAWN
NTS	A3	14.09.26	TS

STATUS	DRAWING No.	REV
CONSTRUCTION	P4-CP-PIR-03 / 10	C02

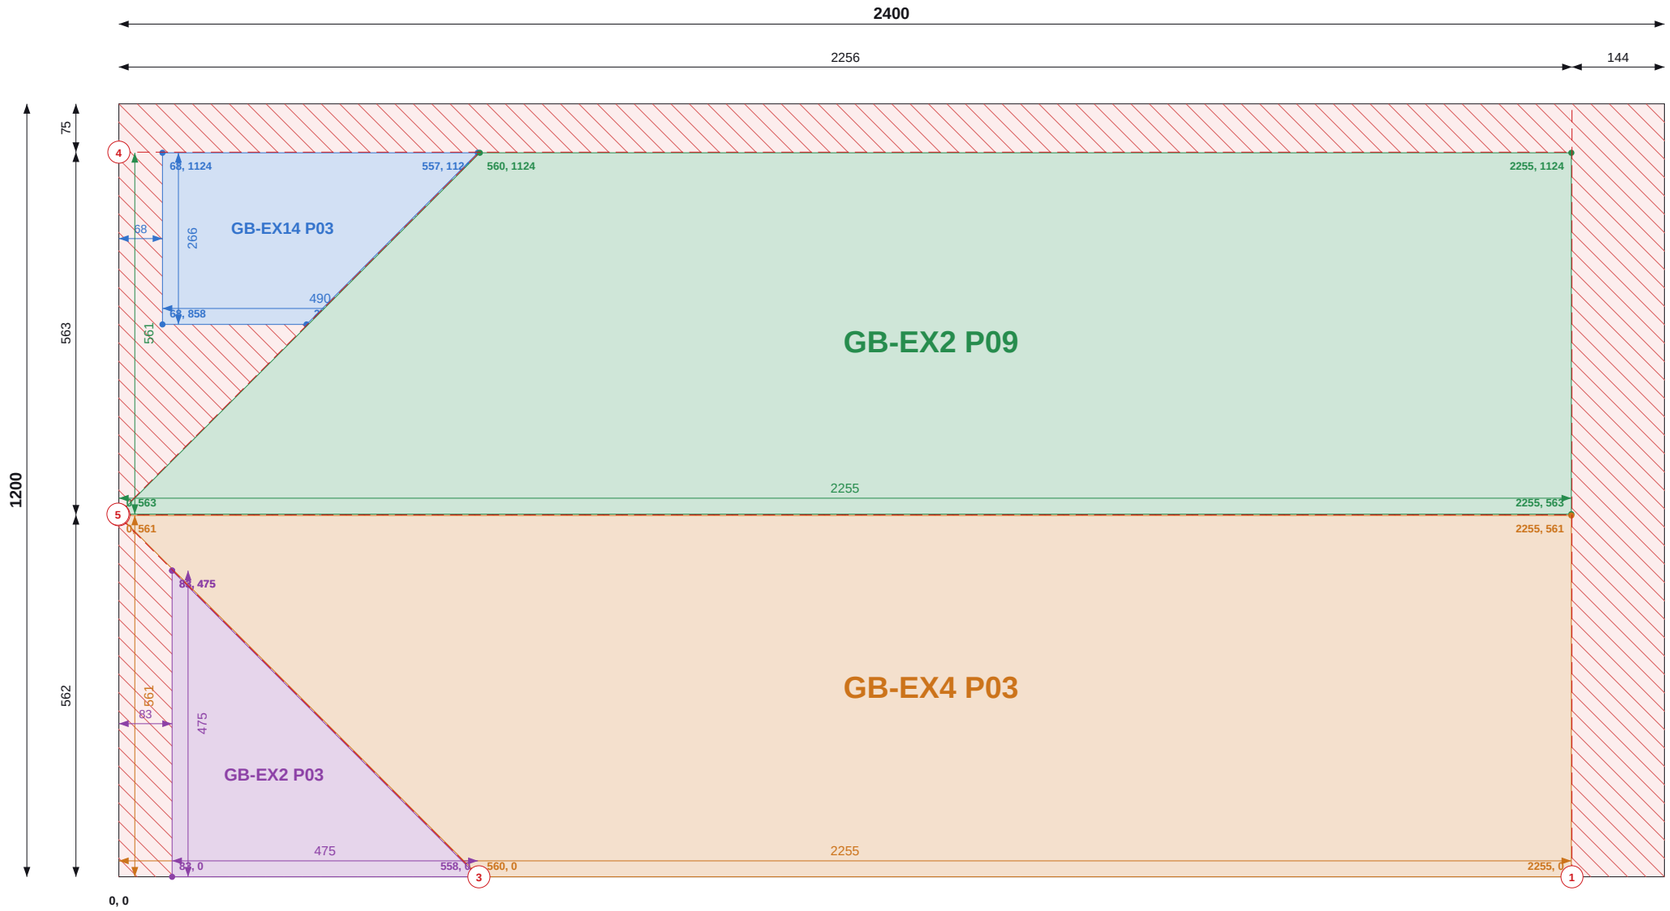

Top / left chains = saw cut positions (to cut centres). Coloured = part size and position.

SHEET 11 OF 18

THIS SHEET

Item	Value
Parts	4
Used / waste	84.2% / 0.46 m2
Reusable offcuts	0
Saw cuts / shared	5 / 3

PIECES (POSITION = BOTTOM-LEFT CORNER)

Label	Size	X, Y
GB-EX14 P03	266 x 490 rake to 225	68, 858
GB-EX2 P09	561 x 2255 rake to 1696	0, 563
GB-EX4 P03	561 x 2255 rake to 1696	0, 0
GB-EX2 P03	475 x 475 rake to 1	83, 0

NOTES

1. Cut from PIR 120mm 1200x2400, 2mm saw kerf. Viewed on the face; dimensions from the sheet's bottom-left corner (0,0). Red numbered lines = saw cuts in order, each edge to edge.
2. Coloured dimensions belong to the part of that colour: its width and height, and its position from the sheet edges. Raked parts: corner coordinates at each corner.
3. Red hatch = waste. Labels = panel + piece mark on the manufacture drawing.

REVISIONS

REV	DATE	DESCRIPTION
C01	14.09.26	Construction issue
C02	14.09.26	Roof trusses revised; SP diagonals added

TLS TIMBER FRAME
Design & Manufacture
Scan: 3D model + drawings

CLIENT	PROJECT
MP Adams	MP Adams Plot 4, Eckington

DRAWING TITLE


PIR CUTTING - GABLES - SHEET 11 OF 18

PIR 120mm 1200x2400 | Gables

SCALE	SIZE	DATE	DRAWN
NTS	A3	14.09.26	TS

STATUS	DRAWING No.	REV
CONSTRUCTION	P4-CP-PIR-03 / 11	C02

Do not scale. All dimensions in mm. Check all dimensions on site.

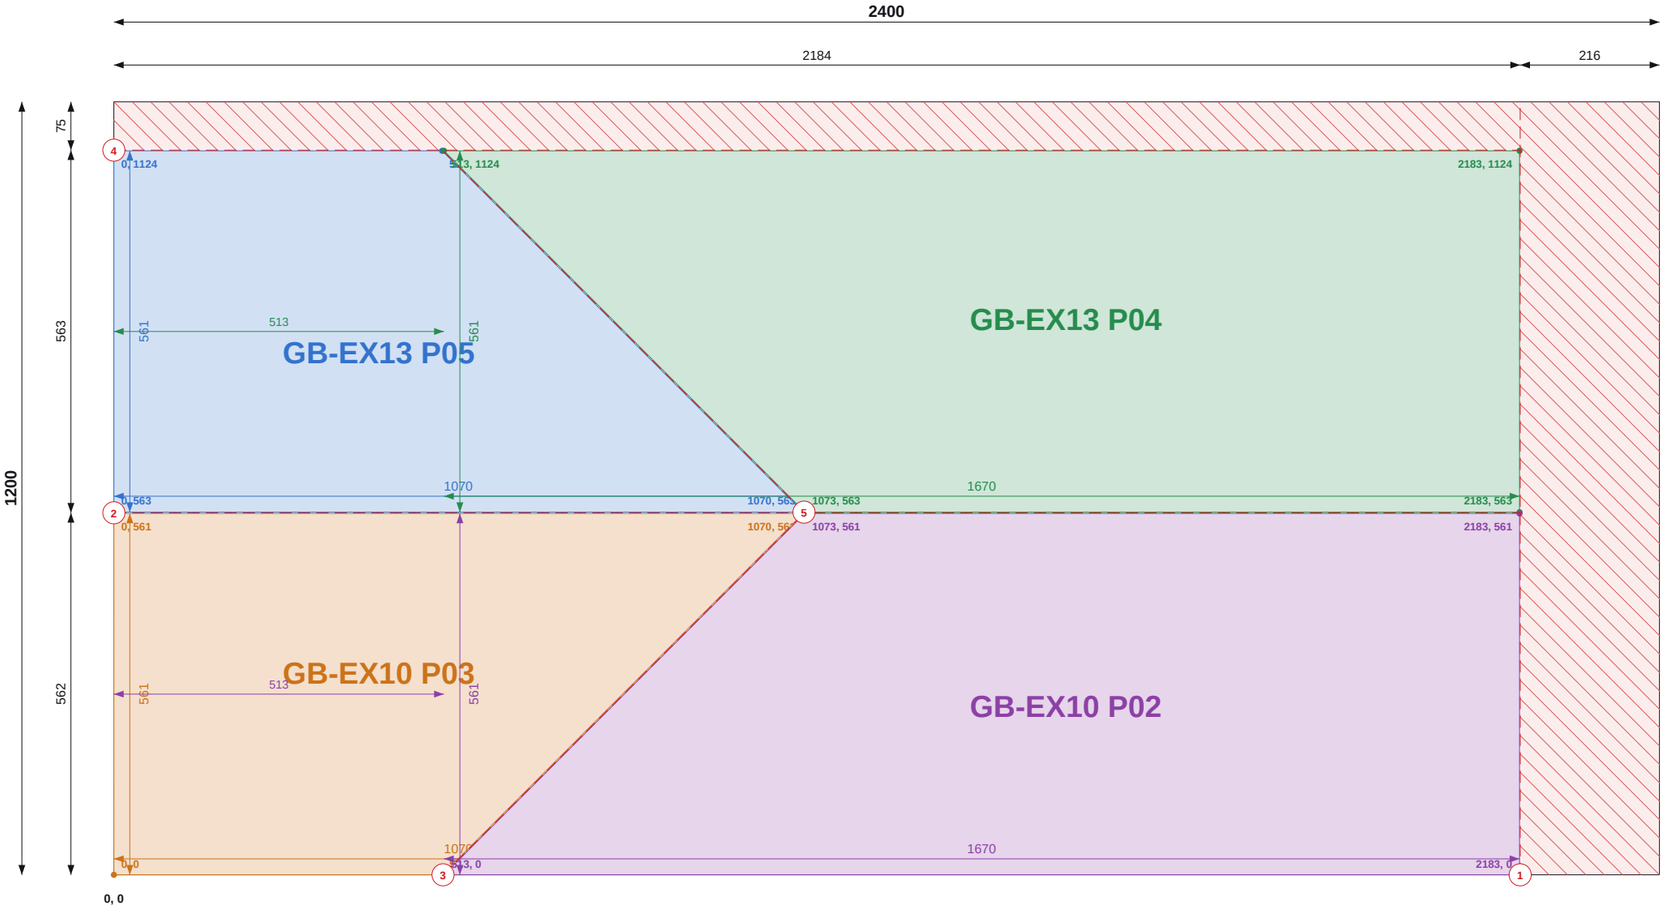

Top / left chains = saw cut positions (to cut centres). Coloured = part size and position.

Do not scale. All dimensions in mm. Check all dimensions on site.

SHEET 12 OF 18

THIS SHEET

Item	Value
Parts	4
Used / waste	84.9% / 0.43 m2
Reusable offcuts	0
Saw cuts / shared	5 / 3

PIECES (POSITION = BOTTOM-LEFT CORNER)

Label	Size	X, Y
GB-EX13 P05	561 x 1070 rake to 511	0, 563
GB-EX13 P04	561 x 1670 rake to 1111	513, 563
GB-EX10 P03	561 x 1070 rake to 511	0, 0
GB-EX10 P02	561 x 1670 rake to 1111	513, 0

NOTES

1. Cut from PIR 120mm 1200x2400, 2mm saw kerf. Viewed on the face; dimensions from the sheet's bottom-left corner (0,0). Red numbered lines = saw cuts in order, each edge to edge.
2. Coloured dimensions belong to the part of that colour: its width and height, and its position from the sheet edges. Raked parts: corner coordinates at each corner.
3. Red hatch = waste. Labels = panel + piece mark on the manufacture drawing.

REVISIONS

REV	DATE	DESCRIPTION
C01	14.09.26	Construction issue
C02	14.09.26	Roof trusses revised; SP diagonals added

TLS TIMBER FRAME
Design & Manufacture
Scan: 3D model + drawings

CLIENT	PROJECT
MP Adams	MP Adams Plot 4, Eckington


DRAWING TITLE

PIR CUTTING - GABLES - SHEET 12 OF 18

PIR 120mm 1200x2400 | Gables

SCALE	SIZE	DATE	DRAWN
NTS	A3	14.09.26	TS

STATUS	DRAWING No.	REV
CONSTRUCTION	P4-CP-PIR-03 / 12	C02

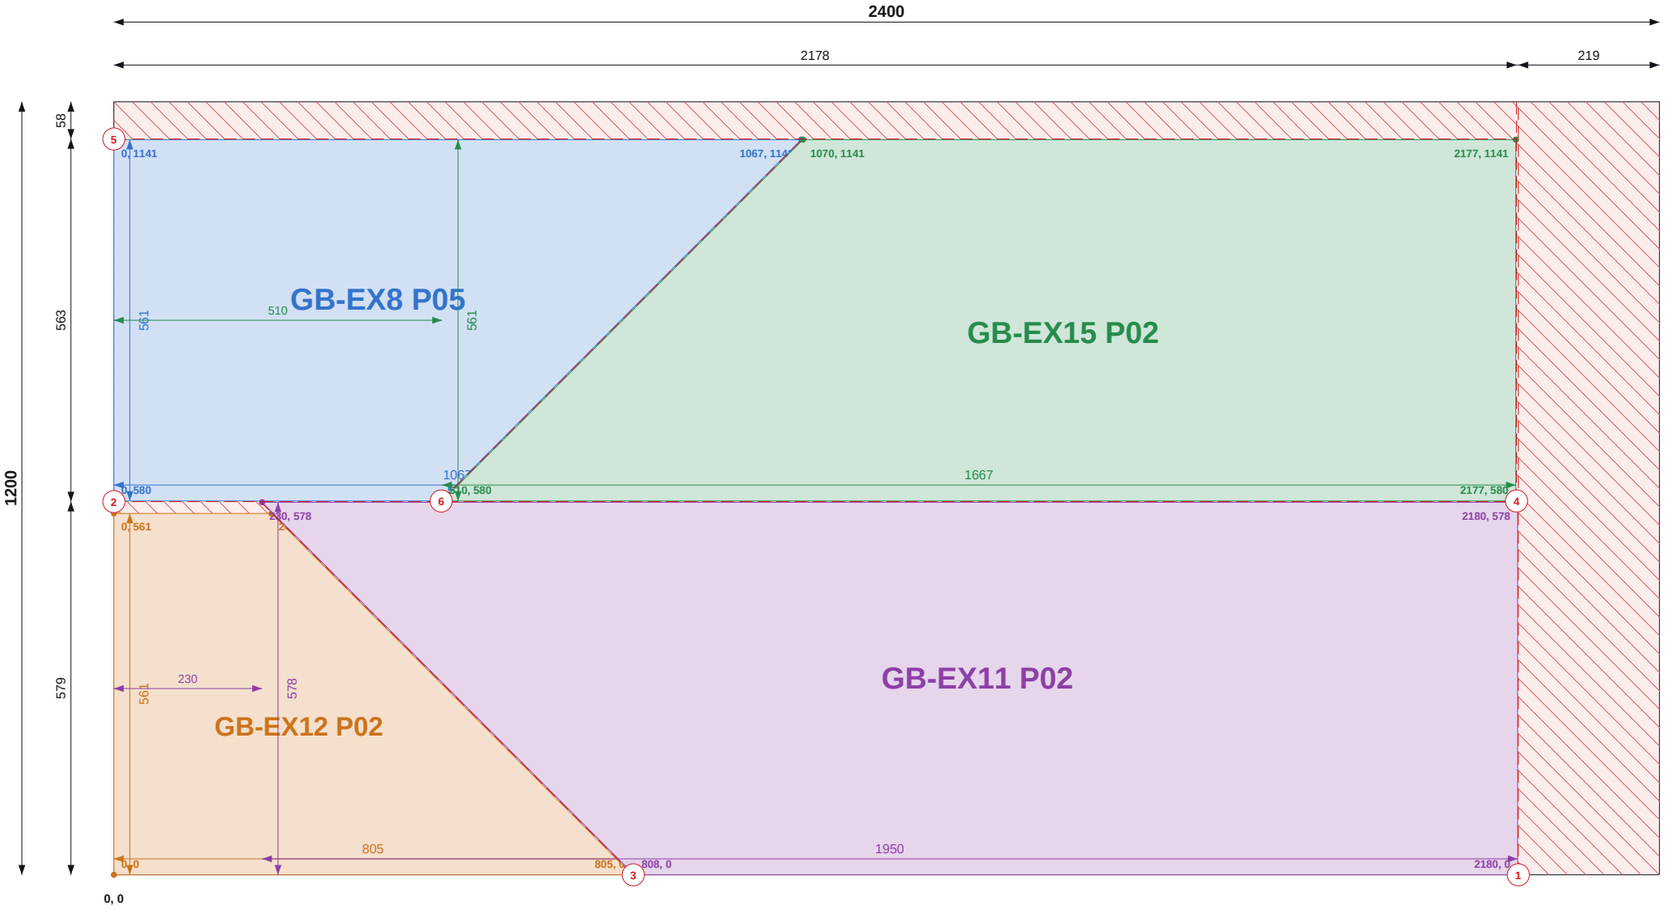

Top / left chains = saw cut positions (to cut centres). Coloured = part size and position.

Do not scale. All dimensions in mm. Check all dimensions on site.

SHEET 13 OF 18

THIS SHEET

Item	Value
Parts	4
Used / waste	85.9% / 0.41 m2
Reusable offcuts	0
Saw cuts / shared	6 / 3

PIECES (POSITION = BOTTOM-LEFT CORNER)

Label	Size	X, Y
GB-EX8 P05	561 x 1067 rake to 508	0, 580
GB-EX15 P02	561 x 1667 rake to 1108	510, 580
GB-EX12 P02	561 x 805 rake to 246	0, 0
GB-EX11 P02	578 x 1950 rake to 1373	230, 0

NOTES

1. Cut from PIR 120mm 1200x2400, 2mm saw kerf. Viewed on the face; dimensions from the sheet's bottom-left corner (0,0). Red numbered lines = saw cuts in order, each edge to edge.
2. Coloured dimensions belong to the part of that colour: its width and height, and its position from the sheet edges. Raked parts: corner coordinates at each corner.
3. Red hatch = waste. Labels = panel + piece mark on the manufacture drawing.

REVISIONS

REV	DATE	DESCRIPTION
C01	14.09.26	Construction issue
C02	14.09.26	Roof trusses revised; SP diagonals added

TLS TIMBER FRAME
Design & Manufacture
Scan: 3D model + drawings


CLIENT	PROJECT
MP Adams	MP Adams Plot 4, Eckington

DRAWING TITLE
PIR CUTTING - GABLES - SHEET 13 OF 18

PIR 120mm 1200x2400 | Gables

SCALE	SIZE	DATE	DRAWN
NTS	A3	14.09.26	TS

STATUS	DRAWING No.	REV
CONSTRUCTION	P4-CP-PIR-03 / 13	C02

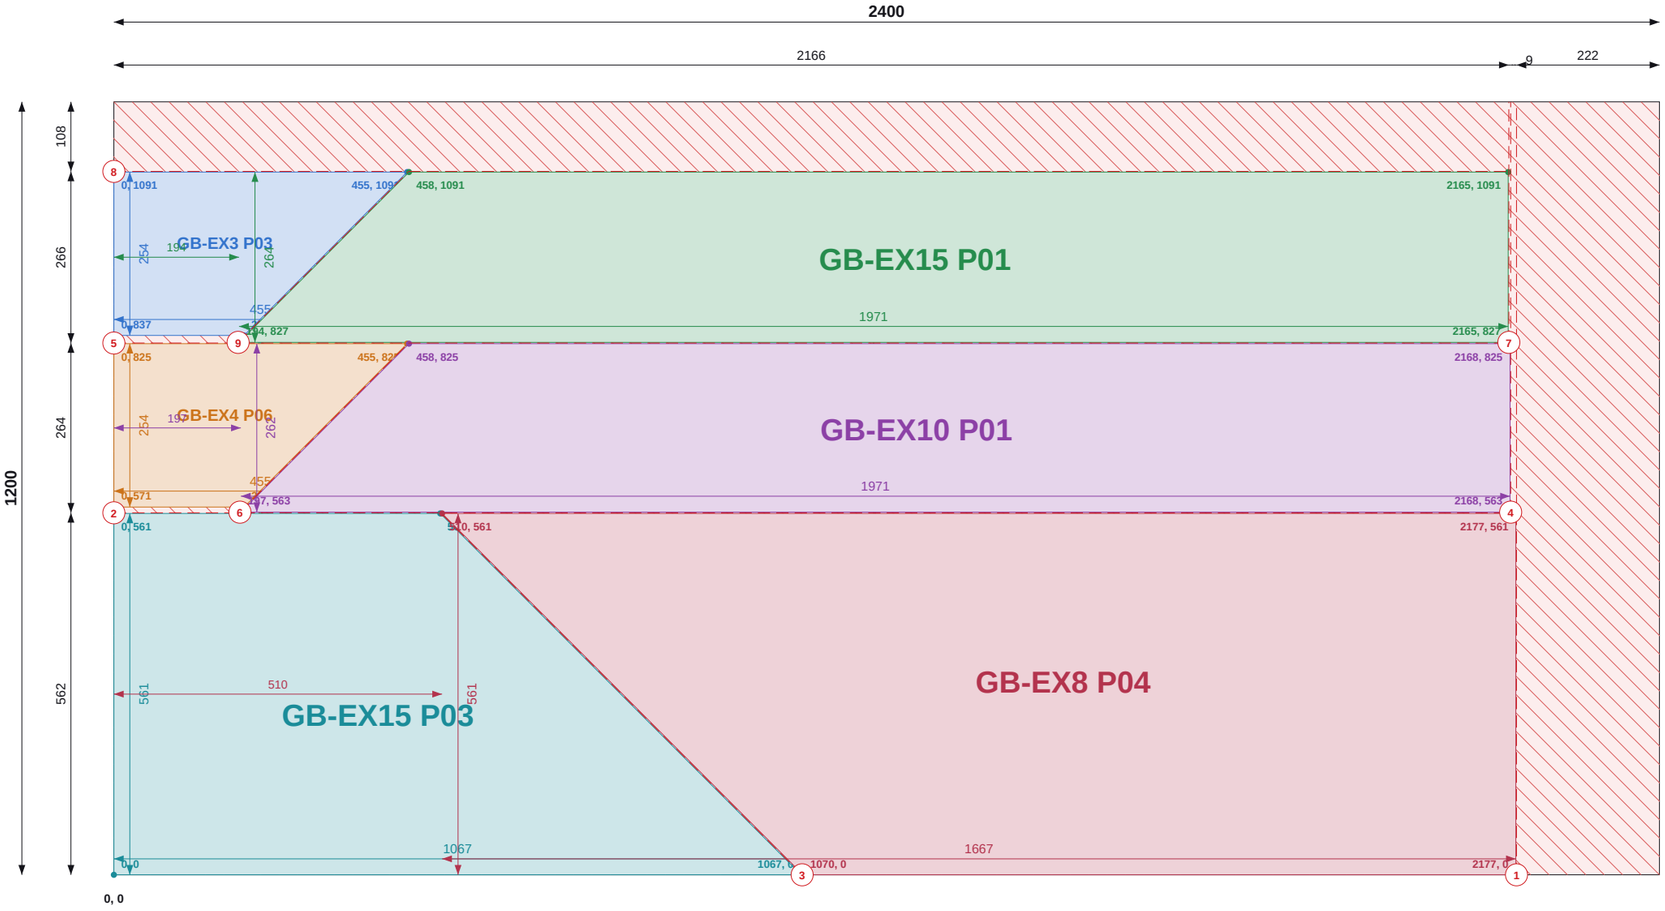

Top / left chains = saw cut positions (to cut centres). Coloured = part size and position.

SHEET 14 OF 18

THIS SHEET

Item	Value
Parts	6
Used / waste	81.7% / 0.53 m2
Reusable offcuts	0
Saw cuts / shared	9 / 5

PIECES (POSITION = BOTTOM-LEFT CORNER)

Label	Size	X, Y
GB-EX3 P03	254 x 455 rake to 203	0, 837
GB-EX15 P01	264 x 1971 rake to 1708	194, 827
GB-EX4 P06	254 x 455 rake to 203	0, 571
GB-EX10 P01	262 x 1971 rake to 1711	197, 563
GB-EX15 P03	561 x 1067 rake to 508	0, 0
GB-EX8 P04	561 x 1667 rake to 1108	510, 0

NOTES

1. Cut from PIR 120mm 1200x2400, 2mm saw kerf. Viewed on the face; dimensions from the sheet's bottom-left corner (0,0). Red numbered lines = saw cuts in order, each edge to edge.
2. Coloured dimensions belong to the part of that colour: its width and height, and its position from the sheet edges. Raked parts: corner coordinates at each corner.
3. Red hatch = waste. Labels = panel + piece mark on the manufacture drawing.

REVISIONS

REV	DATE	DESCRIPTION
C01	14.09.26	Construction issue
C02	14.09.26	Roof trusses revised; SP diagonals added

TLS TIMBER FRAME
Design & Manufacture
Scan: 3D model + drawings

CLIENT	PROJECT
MP Adams	MP Adams Plot 4, Eckington


DRAWING TITLE
PIR CUTTING - GABLES - SHEET 14 OF 18

PIR 120mm 1200x2400 | Gables

SCALE	SIZE	DATE	DRAWN
NTS	A3	14.09.26	TS

STATUS	DRAWING No.	REV
CONSTRUCTION	P4-CP-PIR-03 / 14	C02

Do not scale. All dimensions in mm. Check all dimensions on site.

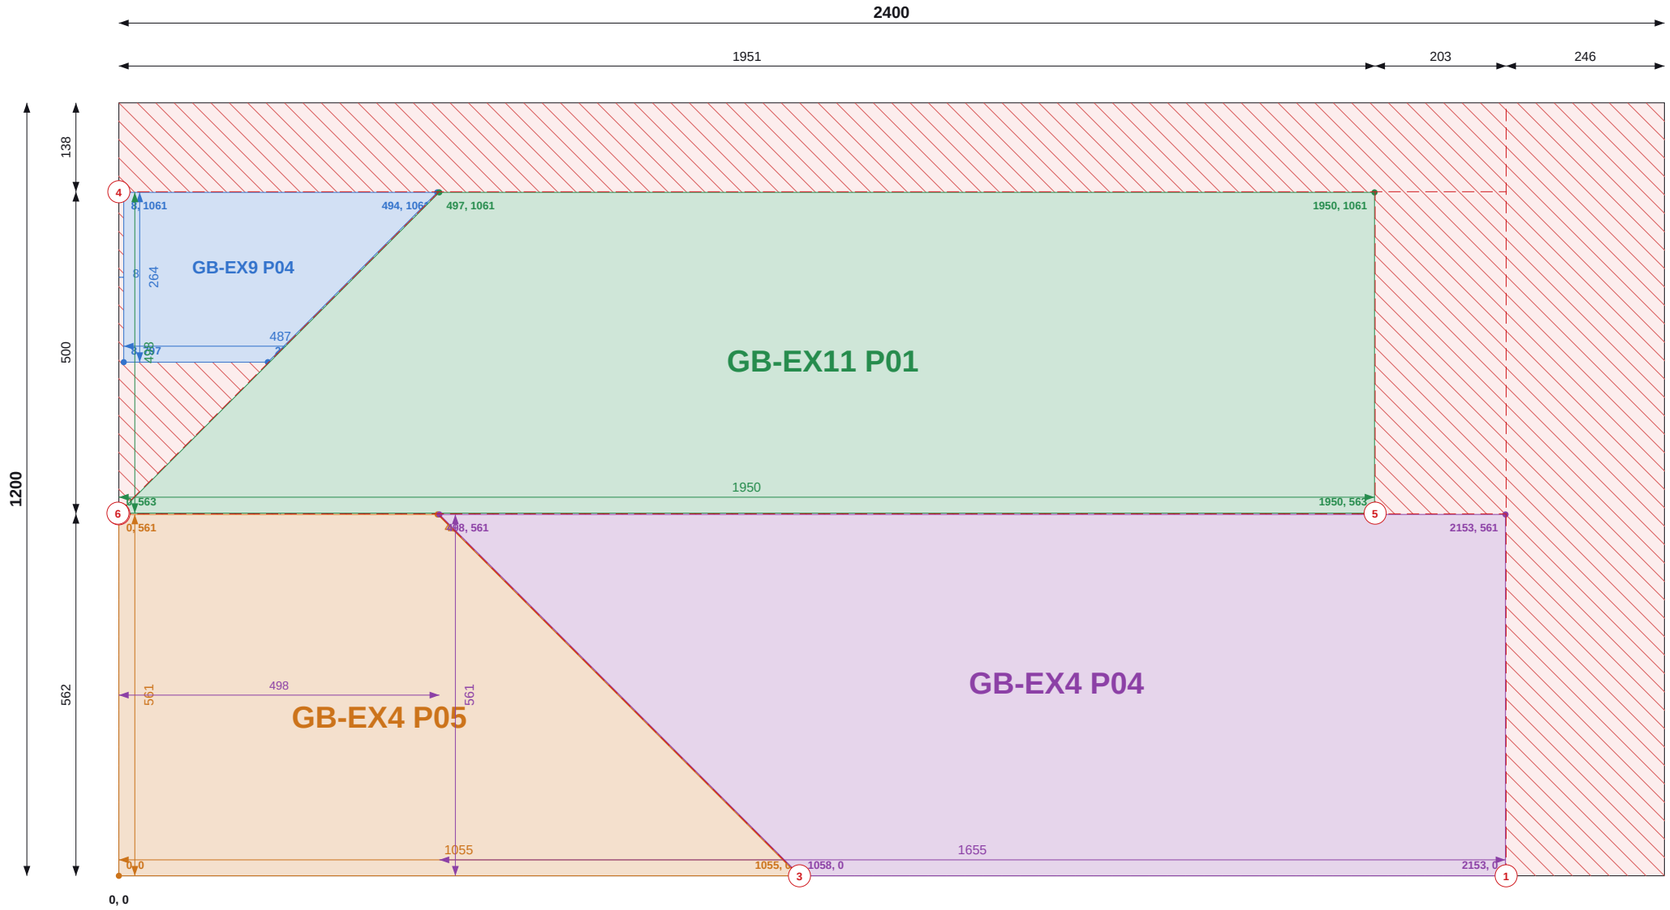

Top / left chains = saw cut positions (to cut centres). Coloured = part size and position.

Do not scale. All dimensions in mm. Check all dimensions on site.

SHEET 15 OF 18

THIS SHEET

Item	Value
Parts	4
Used / waste	74.6% / 0.73 m2
Reusable offcuts	0
Saw cuts / shared	6 / 3

PIECES (POSITION = BOTTOM-LEFT CORNER)

Label	Size	X, Y
GB-EX9 P04	264 x 487 rake to 225	8, 797
GB-EX11 P01	498 x 1950 rake to 1453	0, 563
GB-EX4 P05	561 x 1055 rake to 496	0, 0
GB-EX4 P04	561 x 1655 rake to 1096	498, 0

NOTES

1. Cut from PIR 120mm 1200x2400, 2mm saw kerf. Viewed on the face; dimensions from the sheet's bottom-left corner (0,0). Red numbered lines = saw cuts in order, each edge to edge.
2. Coloured dimensions belong to the part of that colour: its width and height, and its position from the sheet edges. Raked parts: corner coordinates at each corner.
3. Red hatch = waste. Labels = panel + piece mark on the manufacture drawing.

REVISIONS

REV	DATE	DESCRIPTION
C01	14.09.26	Construction issue
C02	14.09.26	Roof trusses revised; SP diagonals added

TLS TIMBER FRAME
Design & Manufacture
Scan: 3D model + drawings

CLIENT	PROJECT
MP Adams	MP Adams Plot 4, Eckington


DRAWING TITLE

PIR CUTTING - GABLES - SHEET 15 OF 18

PIR 120mm 1200x2400 | Gables

SCALE	SIZE	DATE	DRAWN
NTS	A3	14.09.26	TS

STATUS	DRAWING No.	REV
CONSTRUCTION	P4-CP-PIR-03 / 15	C02

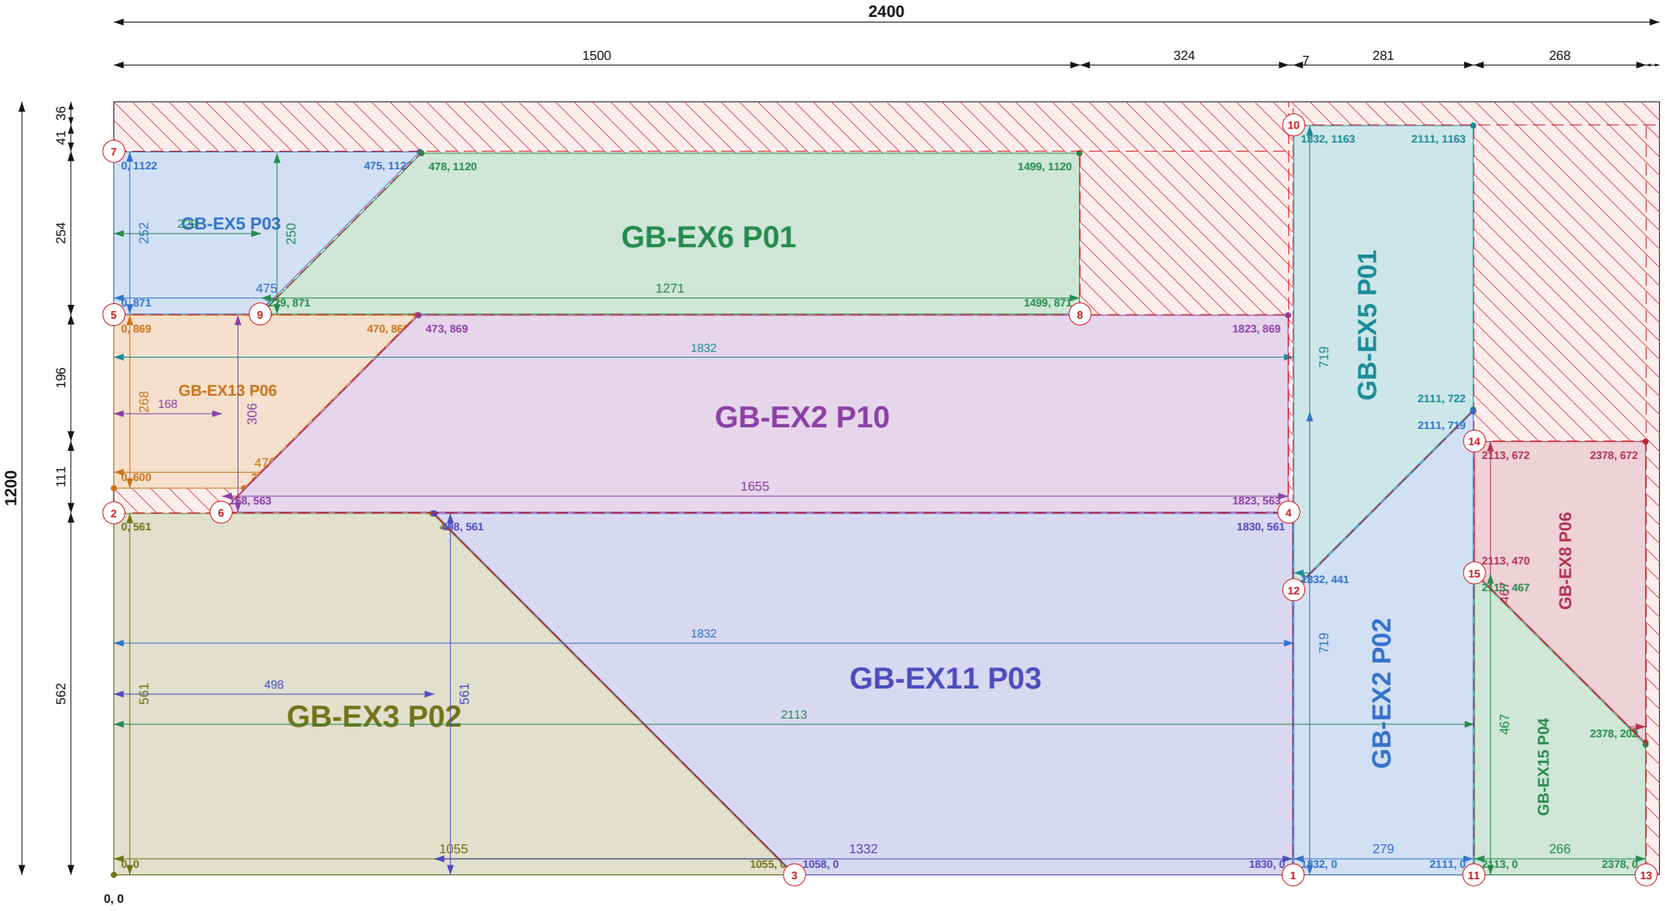

Top / left chains = saw cut positions (to cut centres). Coloured = part size and position.

SHEET 16 OF 18

THIS SHEET

Item	Value
Parts	10
Used / waste	85.1% / 0.43 m2
Reusable offcuts	0
Saw cuts / shared	15 / 9

PIECES (POSITION = BOTTOM-LEFT CORNER)

Label	Size	X, Y
GB-EX5 P03	252 x 475 rake to 225	0, 871
GB-EX6 P01	250 x 1271 rake to 1023	229, 871
GB-EX13 P06	268 x 470 rake to 203	0, 600
GB-EX2 P10	306 x 1655 rake to 1351	168, 563
GB-EX5 P01	279 x 719 rake to 442	1832, 444
GB-EX8 P06	266 x 467 rake to 203	2113, 205
GB-EX3 P02	561 x 1055 rake to 496	0, 0
GB-EX11 P03	561 x 1332 rake to 773	498, 0
GB-EX2 P02	279 x 719 rake to 442	1832, 0
GB-EX15 P04	266 x 467 rake to 203	2113, 0

NOTES

1. Cut from PIR 120mm 1200x2400, 2mm saw kerf. Viewed on the face; dimensions from the sheet's bottom-left corner (0,0). Red numbered lines = saw cuts in order, each edge to edge.
2. Coloured dimensions belong to the part of that colour: its width and height, and its position from the sheet edges. Raked parts: corner coordinates at each corner.
3. Red hatch = waste. Labels = panel + piece mark on the manufacture drawing.

REVISIONS

REV	DATE	DESCRIPTION
C01	14.09.26	Construction issue
C02	14.09.26	Roof trusses revised; SP diagonals added

TLS TIMBER FRAME
Design & Manufacture
Scan: 3D model + drawings

CLIENT	PROJECT
MP Adams	MP Adams Plot 4, Eckington


DRAWING TITLE
PIR CUTTING - GABLES - SHEET 16 OF 18

PIR 120mm 1200x2400 | Gables

SCALE	SIZE	DATE	DRAWN
NTS	A3	14.09.26	TS

STATUS	DRAWING No.	REV
CONSTRUCTION	P4-CP-PIR-03 / 16	C02

Do not scale. All dimensions in mm. Check all dimensions on site.

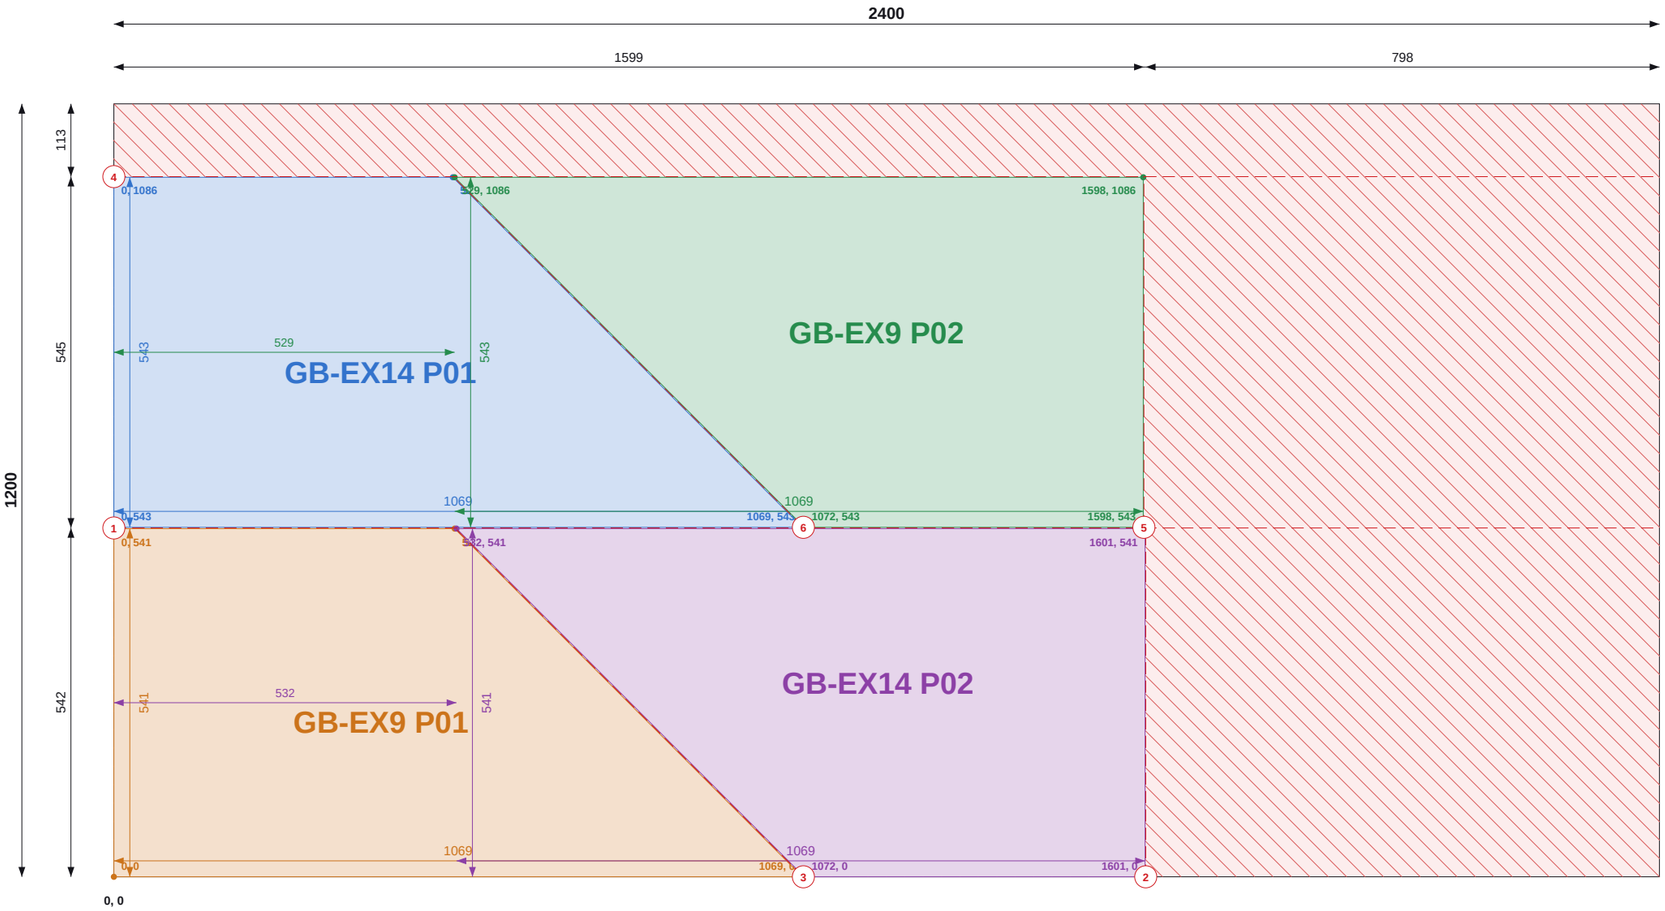

Top / left chains = saw cut positions (to cut centres). Coloured = part size and position.

Do not scale. All dimensions in mm. Check all dimensions on site.

SHEET 17 OF 18

THIS SHEET

Item	Value
Parts	4
Used / waste	60.1% / 1.15 m2
Reusable offcuts	2
Saw cuts / shared	6 / 3

PIECES (POSITION = BOTTOM-LEFT CORNER)

Label	Size	X, Y
GB-EX14 P01	543 x 1069 rake to 527	0, 543
GB-EX9 P02	543 x 1069 rake to 527	529, 543
GB-EX9 P01	541 x 1069 rake to 530	0, 0
GB-EX14 P02	541 x 1069 rake to 530	532, 0

NOTES

1. Cut from PIR 120mm 1200x2400, 2mm saw kerf. Viewed on the face; dimensions from the sheet's bottom-left corner (0,0). Red numbered lines = saw cuts in order, each edge to edge.
2. Coloured dimensions belong to the part of that colour: its width and height, and its position from the sheet edges. Raked parts: corner coordinates at each corner.
3. Red hatch = waste. Labels = panel + piece mark on the manufacture drawing.

REVISIONS

REV	DATE	DESCRIPTION
C01	14.09.26	Construction issue
C02	14.09.26	Roof trusses revised; SP diagonals added

TLS TIMBER FRAME
Design & Manufacture
Scan: 3D model + drawings

CLIENT	PROJECT
MP Adams	MP Adams Plot 4, Eckington


DRAWING TITLE

PIR CUTTING - GABLES - SHEET 17 OF 18

PIR 120mm 1200x2400 | Gables

SCALE	SIZE	DATE	DRAWN
NTS	A3	14.09.26	TS

STATUS	DRAWING No.	REV
CONSTRUCTION	P4-CP-PIR-03 / 17	C02

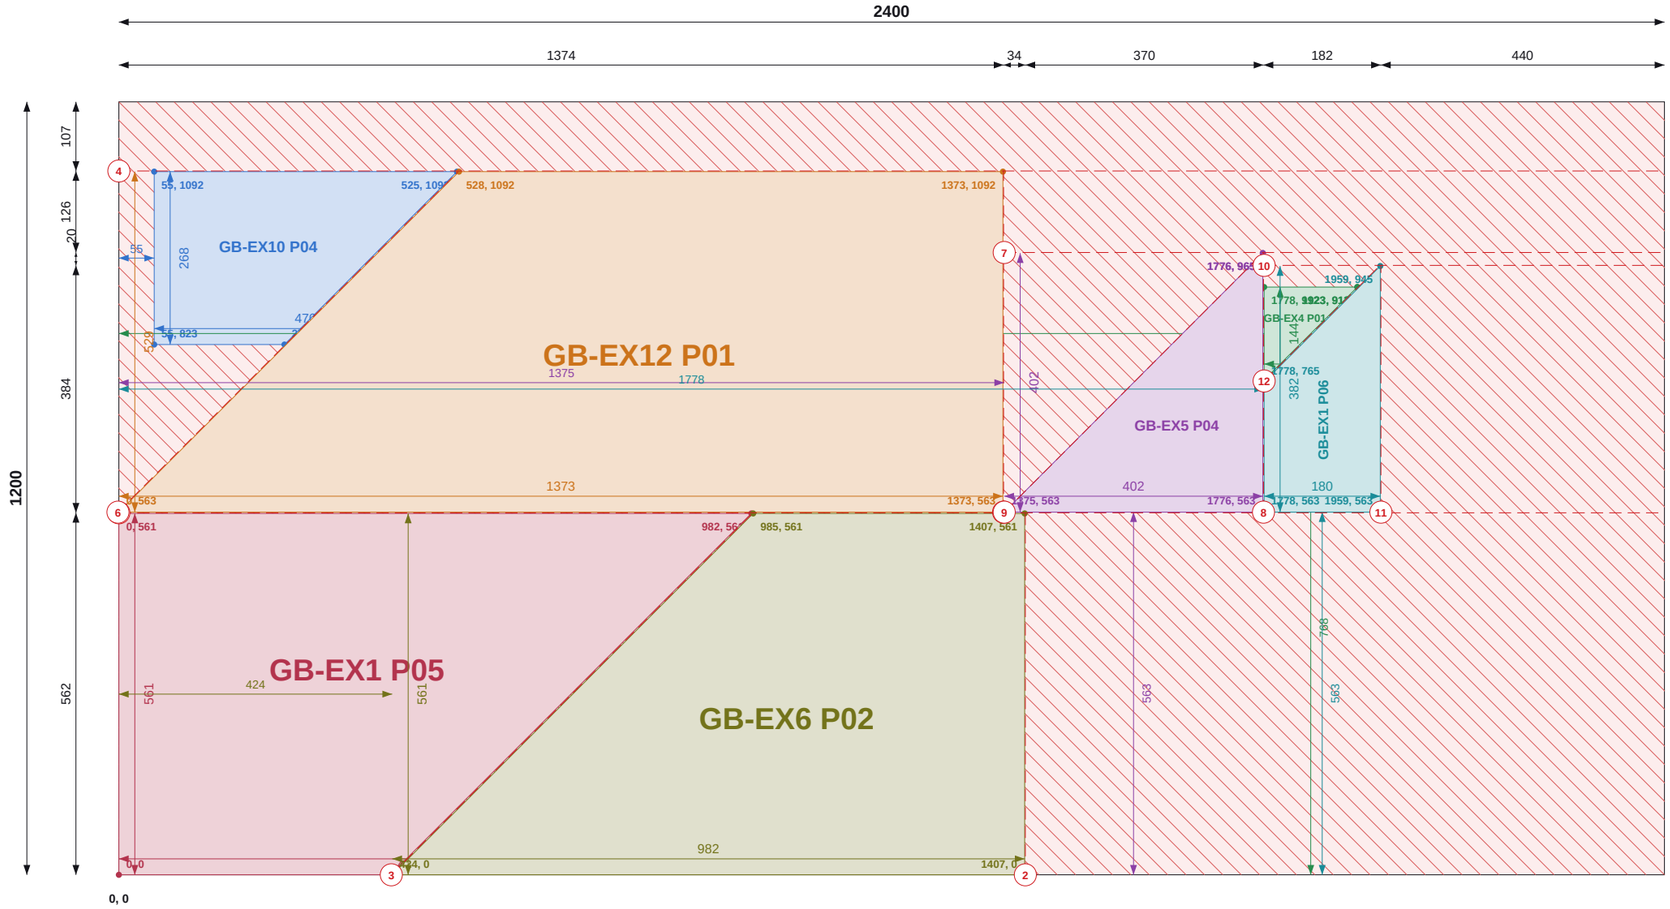

Top / left chains = saw cut positions (to cut centres). Coloured = part size and position.

Do not scale. All dimensions in mm. Check all dimensions on site.

SHEET 18 OF 18

THIS SHEET

Item	Value
Parts	7
Used / waste	55.8% / 1.27 m2
Reusable offcuts	2
Saw cuts / shared	12 / 7

PIECES (POSITION = BOTTOM-LEFT CORNER)

Label	Size	X, Y
GB-EX10 P04	268 x 470 rake to 203	55, 823
GB-EX4 P01	145 x 144 rake to 1	1778, 768
GB-EX12 P01	529 x 1373 rake to 846	0, 563
GB-EX5 P04	402 x 402 rake to 1	1375, 563
GB-EX1 P06	180 x 382 rake to 203	1778, 563
GB-EX1 P05	561 x 982 rake to 423	0, 0
GB-EX6 P02	561 x 982 rake to 423	424, 0

NOTES

1. Cut from PIR 120mm 1200x2400, 2mm saw kerf. Viewed on the face; dimensions from the sheet's bottom-left corner (0,0). Red numbered lines = saw cuts in order, each edge to edge.
2. Coloured dimensions belong to the part of that colour: its width and height, and its position from the sheet edges. Raked parts: corner coordinates at each corner.
3. Red hatch = waste. Labels = panel + piece mark on the manufacture drawing.

REVISIONS

REV	DATE	DESCRIPTION
C01	14.09.26	Construction issue
C02	14.09.26	Roof trusses revised; SP diagonals added

TLS TIMBER FRAME
Design & Manufacture
Scan: 3D model + drawings

CLIENT	PROJECT
MP Adams	MP Adams Plot 4, Eckington

DRAWING TITLE
PIR CUTTING - GABLES - SHEET 18 OF 18

PIR 120mm 1200x2400 | Gables

SCALE	SIZE	DATE	DRAWN
NTS	A3	14.09.26	TS

STATUS	DRAWING No.	REV
CONSTRUCTION	P4-CP-PIR-03 / 18	C02