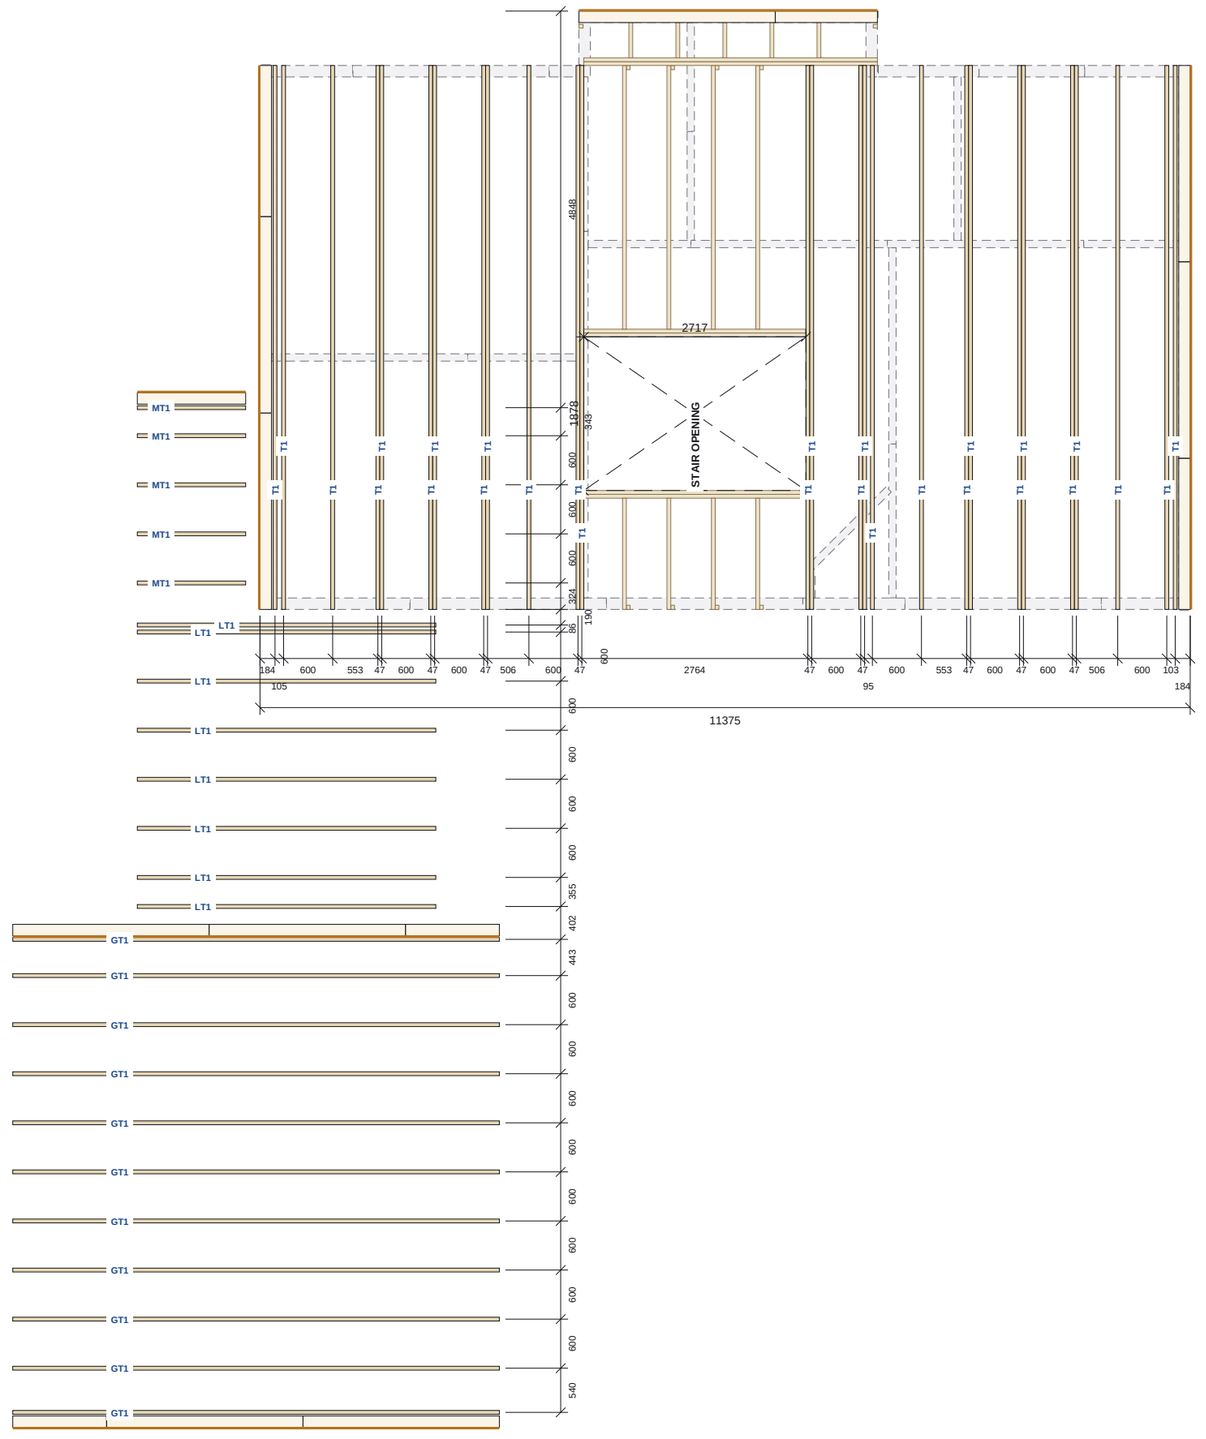


ROOF - CEILING LEVEL PLAN

Scale 1:75 @ A3 | Plan at +5415; first floor walls below grey dashed

CEILING LEVEL SCHEDULE

TRUSSES

Type	No.	Span	Height	Doubles
GT1	11	5950	3238	0
LT1	8	3650	2080	0
MT1	5	1325	1580	0
T1	27	6650	3588	9

Span over external frame faces; height from underside of bottom chord.

CEILING-LEVEL ROOF MEMBERS

Item	No.
Cut roof members bearing at ceiling level	29

Pop-out valley and junction framing, indicative.

NOTES

1. Ceiling level: attic truss bottom chords bear on the first floor head binder at +5115 above slab.
2. Truss bottom chords form the attic floor zone; double trusses trim the stair void and the pop-out junction.
3. Cut roof members at the pop-out valley shown at their low (ceiling-level) ends; see P4-RF-02.
4. Truss and roof member positions indicative; read with the truss manufacturer's layout and engineer's drawing 26-431-S-0010.

REVISIONS

REV	DATE	DESCRIPTION
C01	14.09.26	Construction issue
C02	14.09.26	Roof trusses revised; SP diagonals added

TLS TIMBER FRAME
Design & Manufacture
Scan: 3D model + drawings

CLIENT	PROJECT
MP Adams	MP Adams Plot 4, Eckington

DRAWING TITLE

ROOF - CEILING LEVEL

Attic truss bottom chords and ceiling-level roof members

SCALE	SIZE	DATE	DRAWN
1:75	A3	14.09.26	TS

STATUS	DRAWING No.	REV
CONSTRUCTION	P4-RF-01	C02

Do not scale. All dimensions in mm. Check all dimensions on site.