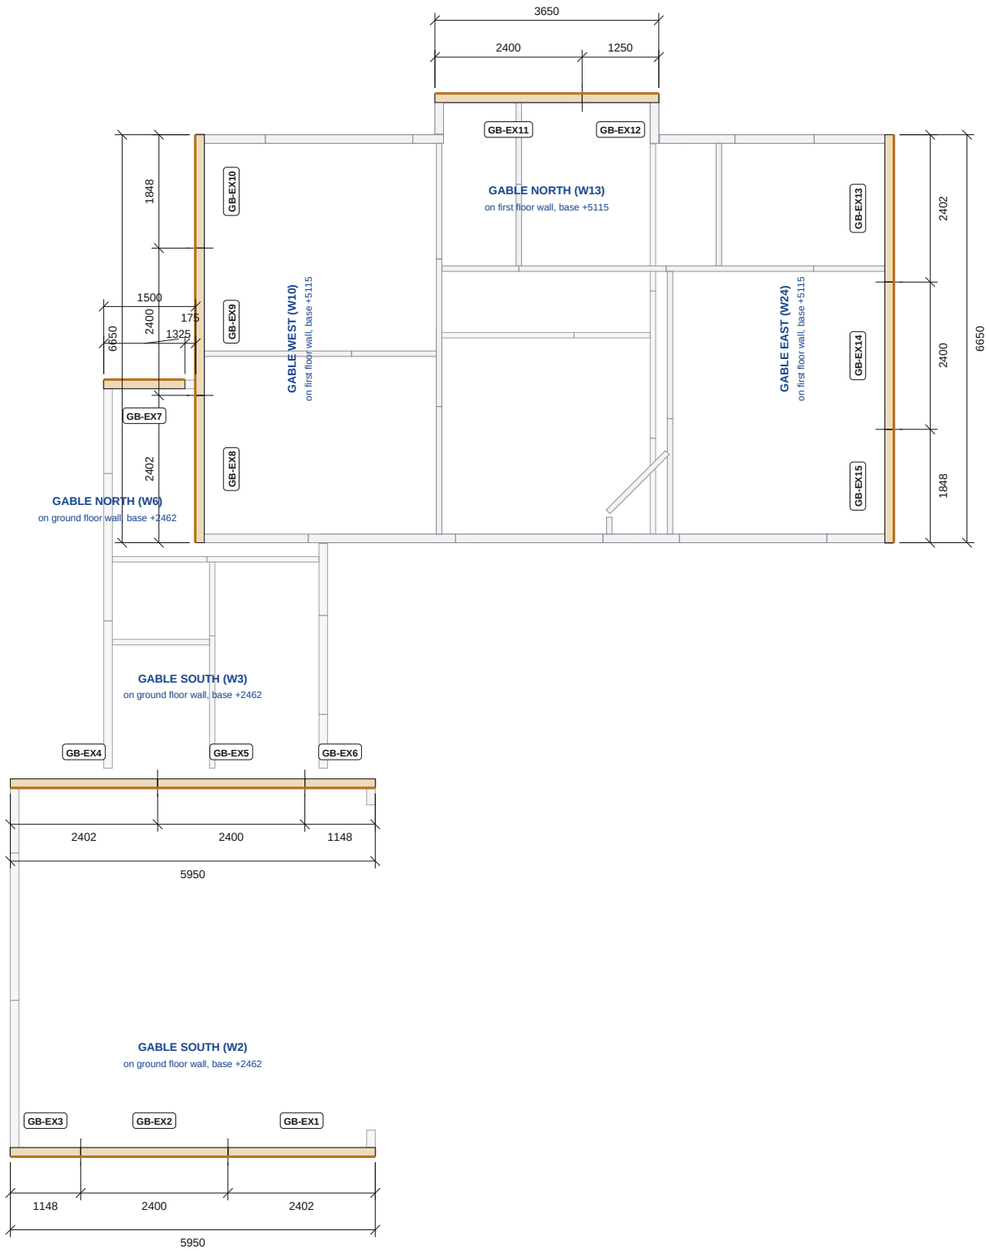


GABLE PANELS LAYOUT

Scale 1:100 @ A3 | Gable panels heavy; first floor walls grey, ground floor walls light grey

0 1 2 3 4 5m

GABLE PANEL SCHEDULES

GABLE PANELS

Mark	Gable	Width	Height	Wall
GB-EX8	West	2400	2656	W10
GB-EX9	West	2400	3580	W10
GB-EX10	West	1846	2102	W10
GB-EX13	East	2400	2656	W24
GB-EX14	East	2400	3580	W24
GB-EX15	East	1846	2102	W24
GB-EX11	North	2400	2080	W13
GB-EX12	North	1248	1504	W13
GB-EX1	South	2400	2656	W2
GB-EX2	South	2400	3230	W2
GB-EX3	South	1146	1402	W2
GB-EX4	South	2400	2656	W3
GB-EX5	South	2400	3230	W3
GB-EX6	South	1146	1402	W3
GB-EX7	North	1325	1580	W6

Width along the wall, height to the top of the raked rail.

TEMPORARY BRACING (NOT SHOWN)

Item	No.	Order
Brace 4x1 treated rough-sawn, 2.7m	9	6 x 5.4m
Noggin 38x89 C16, 600 (nailed)	9	3 x 4.8m

One brace per gable panel joint. +5%.

NOTES

1. Gable panels: 38x140 C16 studs, 9mm OSB/3 to the external face, raked top rails to the roof pitch. No sole plate or head binder: panels bear on the head binder of the wall below and the truss bottom chords.
2. Set out each gable from the outer edges of its central (ridge) panel to the ends of the wall below, as dimensioned on P4-GA-03.
3. Temporary bracing (not shown): one 2.7m 4x1 treated brace at every gable panel joint, fixed through a 600 38x89 noggin nailed to the deck.
4. Window battens 38x43 to gable openings: head and sill run over the jambs by 38.
5. Opening heads are measured from the underside of the panel bottom rail. Read with P4-GA-02, P4-GA-03 / GA-04 and P4-RF-02.

REVISIONS

REV	DATE	DESCRIPTION
C01	14.09.26	Construction issue
C02	14.09.26	Roof trusses revised; SP diagonals added
C03	11.10.26	FF windows coursed; steel + GP1 portal; steel drawings (ST)

TLS TIMBER FRAME DESIGN SUITE

TLS TIMBER FRAME
Design & Manufacture
Scan: 3D model + drawings

CLIENT	PROJECT
MP Adams	MP Adams Plot 4, Eckington

DRAWING TITLE

GABLE PANELS LAYOUT

Every gable on plan with its panel marks; elevations on P4-GA-04

SCALE	SIZE	DATE	DRAWN
1:100	A3	11.10.26	TS

STATUS	DRAWING No.	REV
CONSTRUCTION	P4-GA-03	C03

Do not scale. All dimensions in mm. Check all dimensions on site.