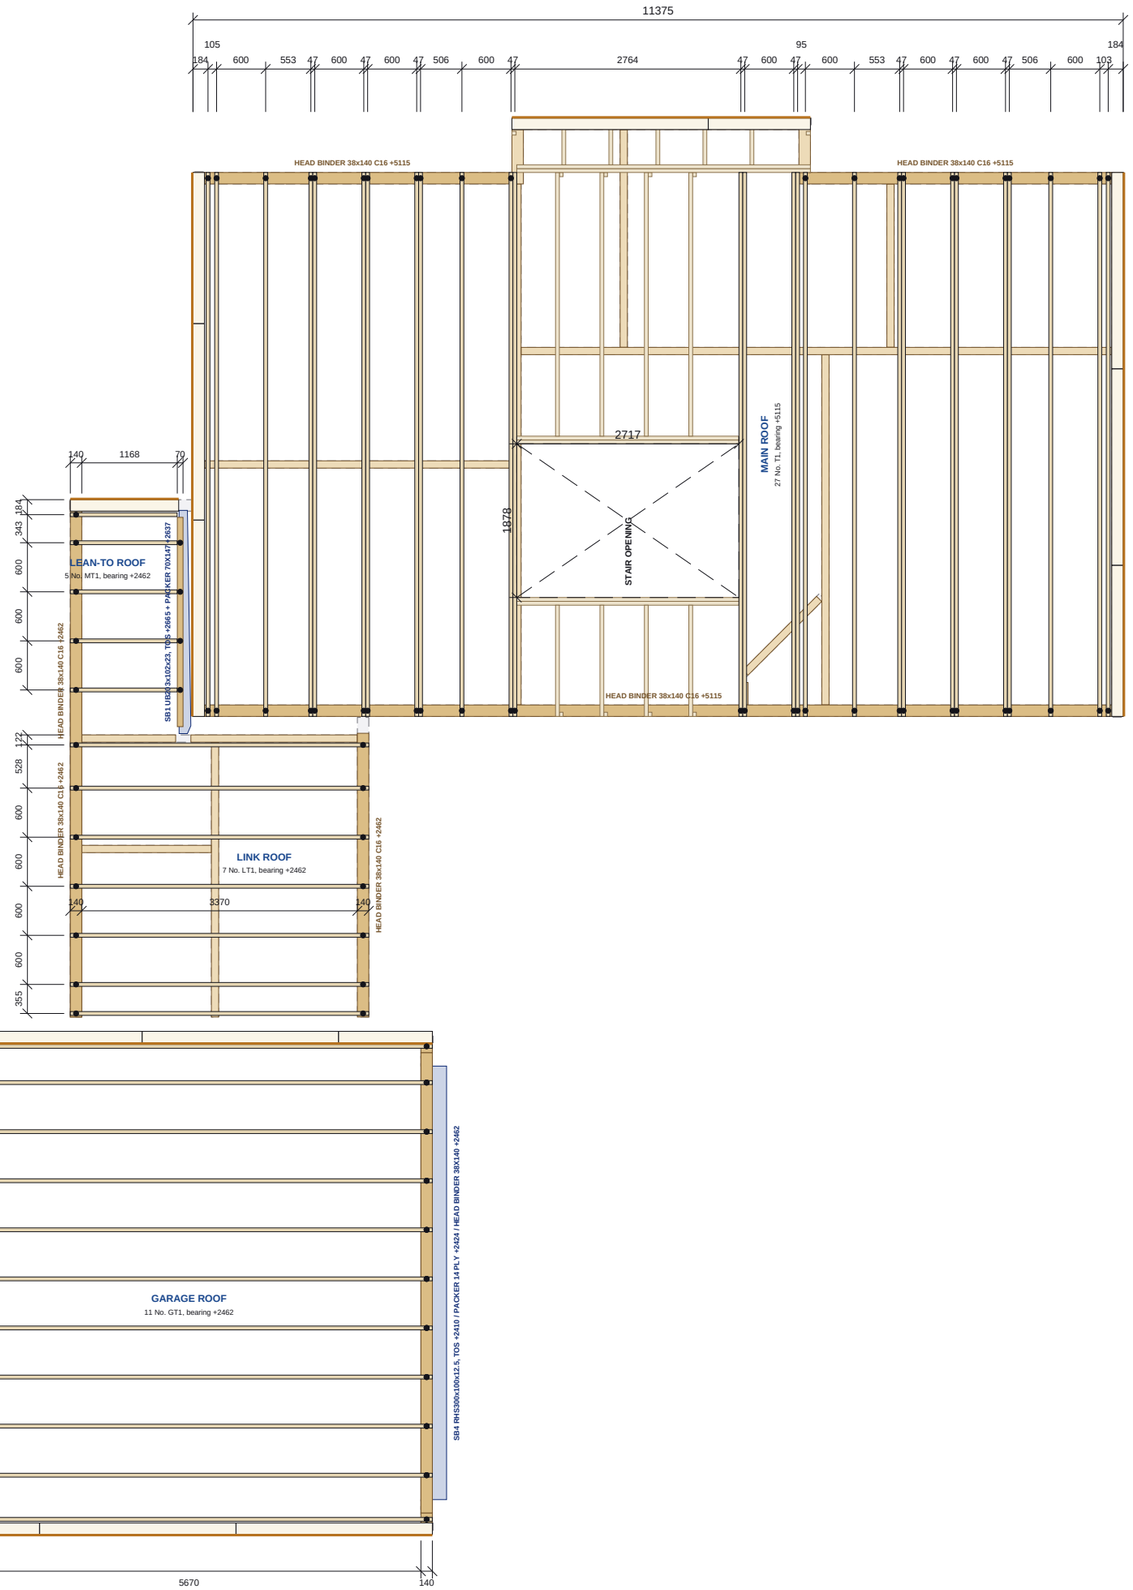


ROOF - CEILING LEVEL PLAN

Scale 1:75 @ A3 | Plan at +5415; first floor walls below grey dashed

0 1 2 3 4 5m

Do not scale. All dimensions in mm. Check all dimensions on site.

CEILING LEVEL SCHEDULE

TRUSSES

Type	No.	Span	Height	Doubles
GT1	11	5950	3238	0
LT1	7	3650	2080	0
MT1	5	1306	1562	0
T1	27	6650	3588	9

Span over external frame faces; height from underside of bottom chord.

TRUSS BEARINGS

Roof	Bearing	Top	Runs
Main	HEAD BINDER 38x140 C16	+5115	3
Garage	SB4 RHS300x100x12.5 S355J2H	+2410	1
Garage	SB4 head binder 38x140 C16	+2462	1
Garage	SB4 packer 14mm marine ply 140	+2424	1
Garage	HEAD BINDER 38x140 C16	+2462	3
Link	HEAD BINDER 38x140 C16	+2462	2
Lean-to	SB1 UB203x102x23 S355JR	+2665	1
Lean-to	SB1 packer 70x147 C24	+2637	1
Lean-to	HEAD BINDER 38x140 C16	+2462	1

Top of bearing above slab; runs = separate lengths on plan. Dots on plan mark each truss bearing.

CEILING-LEVEL ROOF MEMBERS

Item	No.
Cut roof members bearing at ceiling level	29

Pop-out valley and junction framing, indicative.

NOTES

1. Lower roofs (garage roof, link roof and lean-to roof): trusses bear at +2462 above slab on the ground floor head binders and the steel / packers shown solid, set out as dimensioned; dots mark each truss bearing.
2. Ceiling level: attic truss bottom chords bear on the first floor head binder at +5115 above slab.
3. Truss bottom chords form the attic floor zone; double trusses trim the stair void and the pop-out junction.
4. Cut roof members at the pop-out valley shown at their low (ceiling-level) ends; see P4-RF-02.
5. Truss and roof member positions indicative; read with the truss manufacturer's layout and engineer's drawing 26-431-S-0010.

REVISIONS

REV	DATE	DESCRIPTION
C01	14.09.26	Construction issue
C02	14.09.26	Roof trusses revised; SP diagonals added
C03	11.10.26	FF windows coursed; steel + GP1 portal; steel drawings (ST)

TLS TIMBER FRAME DESIGN SUITE

TLS TIMBER FRAME
Design & Manufacture
Scan: 3D model + drawings

CLIENT	PROJECT
MP Adams	MP Adams Plot 4, Eckington

DRAWING TITLE

ROOF - CEILING LEVEL

Attic truss bottom chords and ceiling-level roof members

SCALE	SIZE	DATE	DRAWN
1:75	A3	11.10.26	TS

STATUS	DRAWING No.	REV
CONSTRUCTION	P4-RF-01	C03