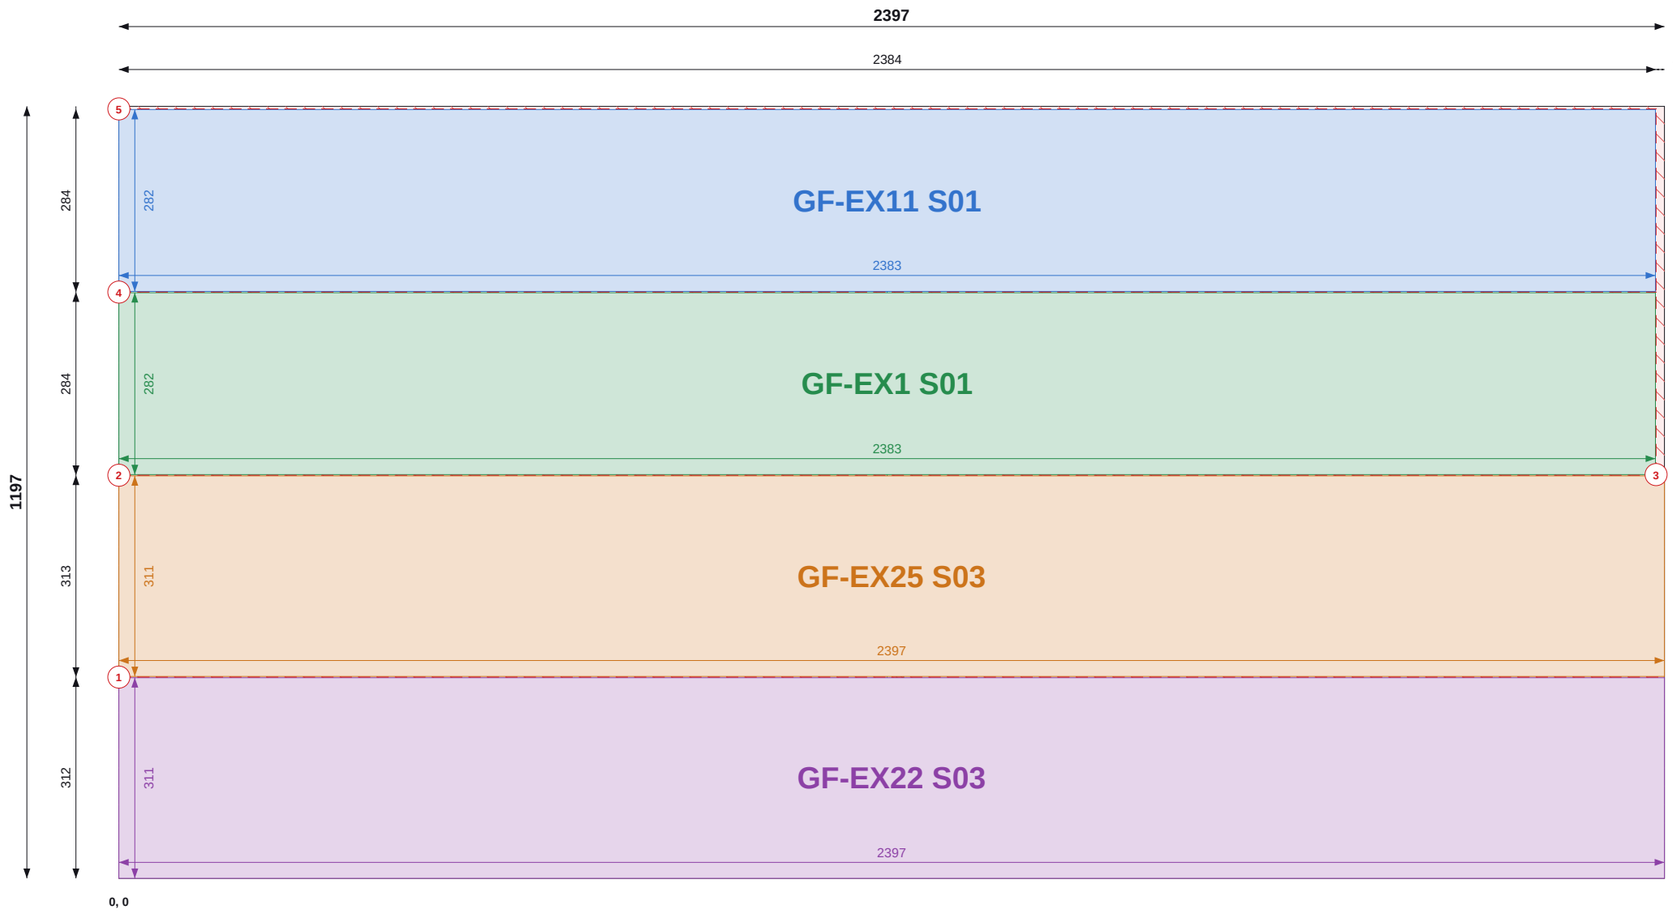



Top / left chains = saw cut positions (to cut centres). Coloured = part size and position.

Do not scale. All dimensions in mm. Check all dimensions on site.

## SHEET 1 OF 50

### THIS SHEET

| Item | Value |
|---|---|
| Parts | 4 |
| Used / waste | 98.8% / 0.03 m2 |
| Reusable offcuts | 0 |
| Saw cuts / shared | 5 / 3 |

### PIECES (POSITION = BOTTOM-LEFT CORNER)

| Label | Size | X, Y |
|---|---|---|
| GF-EX11 S01 | 282 x 2383 | 0, 910 |
| GF-EX1 S01 | 282 x 2383 | 0, 626 |
| GF-EX25 S03 | 2397 x 311 | 0, 313 |
| GF-EX22 S03 | 2397 x 311 | 0, 0 |

### GROUND FLOOR TOTALS

| Item | Value |
|---|---|
| Sheets / pieces | 50 / 105 |
| Yield / waste | 92.9% / 10.23 m2 |
| Saw cuts / shared / on stock edge | 157 / 55 / 153 |

### NOTES

1. Cut from OSB/3 9mm 1197x2397, 2mm saw kerf. Viewed on the face; dimensions from the sheet's bottom-left corner (0,0). Red numbered lines = saw cuts in order, each edge to edge.
2. Coloured dimensions belong to the part of that colour: its width and height, and its position from the sheet edges. Raked parts: corner coordinates at each corner.
3. Red hatch = waste. Labels = panel + piece mark on the manufacture drawing.

### REVISIONS

| REV | DATE | DESCRIPTION |
|---|---|---|
| C01 | 14.09.26 | Construction issue |
| C02 | 14.09.26 | Roof trusses revised; SP diagonals added |
| C03 | 11.10.26 | FF windows coursed; steel + GP1 portal; steel drawings (ST) |
| C04 | 13.10.26 | Steel approved by the engineer: steel + steel timber drawings issued for construction |

TLS TIMBER FRAME
Design & Manufacture
Scan: 3D model + drawings

| CLIENT | PROJECT |
|---|---|
| MP Adams | MP Adams Plot 4, Eckington |

DRAWING TITLE

**OSB CUTTING - GROUND FLOOR - SHEET 1 OF 50**

OSB/3 9mm 1197x2397 | Ground Floor

| SCALE | SIZE | DATE | DRAWN |
|---|---|---|---|
| NTS | A3 | 13.10.26 | TS |

| STATUS | DRAWING No. | REV |
|---|---|---|
| CONSTRUCTION | P4-CP-OSB-01 / 01 | C04 |




Top / left chains = saw cut positions (to cut centres). Coloured = part size and position.

Do not scale. All dimensions in mm. Check all dimensions on site.

## SHEET 2 OF 50

### THIS SHEET

| Item | Value |
|---|---|
| Parts | 1 |
| Used / waste | 99.4% / 0.02 m2 |
| Reusable offcuts | 0 |
| Saw cuts / shared | 1 / 0 |

### PIECES (POSITION = BOTTOM-LEFT CORNER)

| Label | Size | X, Y |
|---|---|---|
| GF-EX16 S02 | 1197 x 2383 | 0, 0 |

### NOTES

1. Cut from OSB/3 9mm 1197x2397, 2mm saw kerf. Viewed on the face; dimensions from the sheet's bottom-left corner (0,0). Red numbered lines = saw cuts in order, each edge to edge.
2. Coloured dimensions belong to the part of that colour: its width and height, and its position from the sheet edges. Raked parts: corner coordinates at each corner.
3. Red hatch = waste. Labels = panel + piece mark on the manufacture drawing.

### REVISIONS

| REV | DATE | DESCRIPTION |
|---|---|---|
| C01 | 14.09.26 | Construction issue |
| C02 | 14.09.26 | Roof trusses revised; SP diagonals added |
| C03 | 11.10.26 | FF windows coursed; steel + GP1 portal; steel drawings (ST) |
| C04 | 13.10.26 | Steel approved by the engineer: steel + steel timber drawings issued for construction |

TLS

TLS TIMBER FRAME

Design & Manufacture

Scan: 3D model + drawings

| CLIENT | PROJECT |
|---|---|
| MP Adams | MP Adams Plot 4, Eckington |

DRAWING TITLE

**OSB CUTTING - GROUND FLOOR - SHEET 2 OF 50**

OSB/3 9mm 1197x2397 | Ground Floor

| SCALE | SIZE | DATE | DRAWN |
|---|---|---|---|
| NTS | A3 | 13.10.26 | TS |

| STATUS | DRAWING No. | REV |
|---|---|---|
| CONSTRUCTION | P4-CP-OSB-01 / 02 | C04 |




Top / left chains = saw cut positions (to cut centres). Coloured = part size and position.

Do not scale. All dimensions in mm. Check all dimensions on site.

## SHEET 3 OF 50

### THIS SHEET

| Item | Value |
|---|---|
| Parts | 1 |
| Used / waste | 99.4% / 0.02 m2 |
| Reusable offcuts | 0 |
| Saw cuts / shared | 1 / 0 |

### PIECES (POSITION = BOTTOM-LEFT CORNER)

| Label | Size | X, Y |
|---|---|---|
| GF-EX2 S02 | 1197 x 2383 | 0, 0 |

### NOTES

1. Cut from OSB/3 9mm 1197x2397, 2mm saw kerf. Viewed on the face; dimensions from the sheet's bottom-left corner (0,0). Red numbered lines = saw cuts in order, each edge to edge.
2. Coloured dimensions belong to the part of that colour: its width and height, and its position from the sheet edges. Raked parts: corner coordinates at each corner.
3. Red hatch = waste. Labels = panel + piece mark on the manufacture drawing.

### REVISIONS

| REV | DATE | DESCRIPTION |
|---|---|---|
| C01 | 14.09.26 | Construction issue |
| C02 | 14.09.26 | Roof trusses revised; SP diagonals added |
| C03 | 11.10.26 | FF windows coursed; steel + GP1 portal; steel drawings (ST) |
| C04 | 13.10.26 | Steel approved by the engineer: steel + steel timber drawings issued for construction |

TLS

TLS TIMBER FRAME

Design & Manufacture

Scan: 3D model + drawings

| CLIENT | PROJECT |
|---|---|
| MP Adams | MP Adams Plot 4, Eckington |

DRAWING TITLE

**OSB CUTTING - GROUND FLOOR - SHEET 3 OF 50**

OSB/3 9mm 1197x2397 | Ground Floor

| SCALE | SIZE | DATE | DRAWN |
|---|---|---|---|
| NTS | A3 | 13.10.26 | TS |

| STATUS | DRAWING No. | REV |
|---|---|---|
| CONSTRUCTION | P4-CP-OSB-01 / 03 | C04 |




Top / left chains = saw cut positions (to cut centres). Coloured = part size and position.

Do not scale. All dimensions in mm. Check all dimensions on site.

## SHEET 4 OF 50

### THIS SHEET

| Item | Value |
|---|---|
| Parts | 1 |
| Used / waste | 99.4% / 0.02 m2 |
| Reusable offcuts | 0 |
| Saw cuts / shared | 1 / 0 |

### PIECES (POSITION = BOTTOM-LEFT CORNER)

| Label | Size | X, Y |
|---|---|---|
| GF-EX3 S02 | 1197 x 2383 | 0, 0 |

### NOTES

1. Cut from OSB/3 9mm 1197x2397, 2mm saw kerf. Viewed on the face; dimensions from the sheet's bottom-left corner (0,0). Red numbered lines = saw cuts in order, each edge to edge.
2. Coloured dimensions belong to the part of that colour: its width and height, and its position from the sheet edges. Raked parts: corner coordinates at each corner.
3. Red hatch = waste. Labels = panel + piece mark on the manufacture drawing.

### REVISIONS

| REV | DATE | DESCRIPTION |
|---|---|---|
| C01 | 14.09.26 | Construction issue |
| C02 | 14.09.26 | Roof trusses revised; SP diagonals added |
| C03 | 11.10.26 | FF windows coursed; steel + GP1 portal; steel drawings (ST) |
| C04 | 13.10.26 | Steel approved by the engineer: steel + steel timber drawings issued for construction |

TLS

TLS TIMBER FRAME

Design & Manufacture

Scan: 3D model + drawings

| CLIENT | PROJECT |
|---|---|
| MP Adams | MP Adams Plot 4, Eckington |


DRAWING TITLE

# OSB CUTTING - GROUND FLOOR - SHEET 4 OF 50

OSB/3 9mm 1197x2397 | Ground Floor

| SCALE | SIZE | DATE | DRAWN |
|---|---|---|---|
| NTS | A3 | 13.10.26 | TS |

| STATUS | DRAWING No. | REV |
|---|---|---|
| CONSTRUCTION | P4-CP-OSB-01 / 04 | C04 |

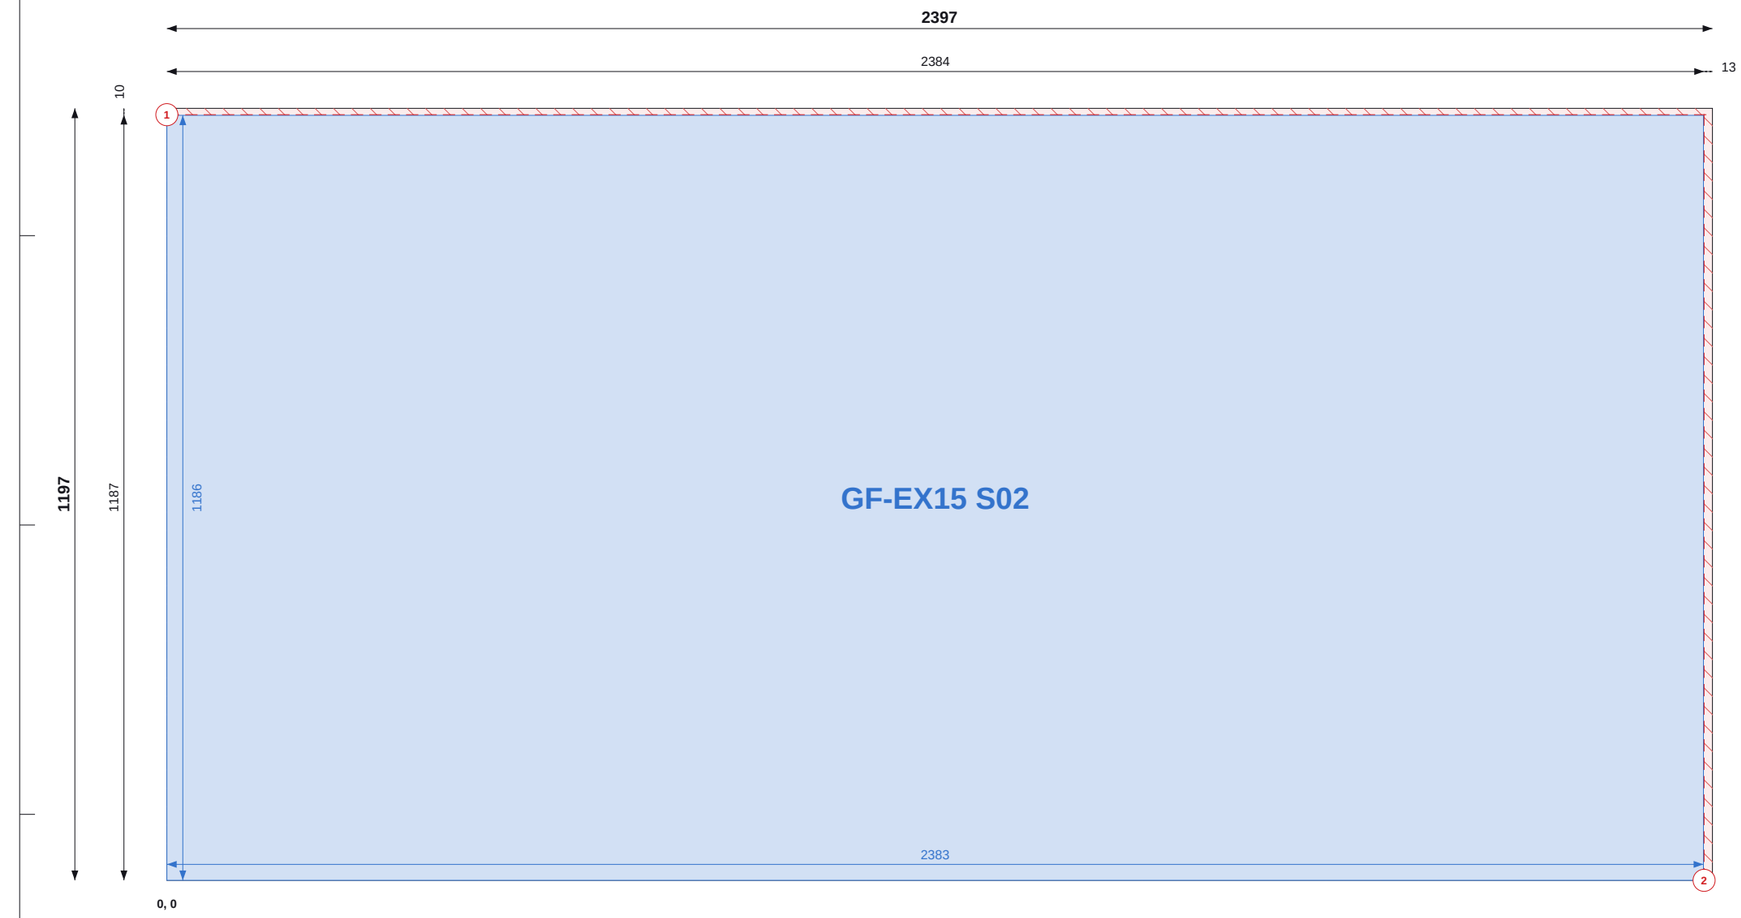


Top / left chains = saw cut positions (to cut centres). Coloured = part size and position.

## SHEET 5 OF 50

### THIS SHEET

| Item | Value |
|---|---|
| Parts | 1 |
| Used / waste | 98.5% / 0.04 m2 |
| Reusable offcuts | 0 |
| Saw cuts / shared | 2 / 0 |

### PIECES (POSITION = BOTTOM-LEFT CORNER)

| Label | Size | X, Y |
|---|---|---|
| GF-EX15 S02 | 1186 x 2383 | 0, 0 |

### NOTES

1. Cut from OSB/3 9mm 1197x2397, 2mm saw kerf. Viewed on the face; dimensions from the sheet's bottom-left corner (0,0). Red numbered lines = saw cuts in order, each edge to edge.
2. Coloured dimensions belong to the part of that colour: its width and height, and its position from the sheet edges. Raked parts: corner coordinates at each corner.
3. Red hatch = waste. Labels = panel + piece mark on the manufacture drawing.

### REVISIONS

| REV | DATE | DESCRIPTION |
|---|---|---|
| C01 | 14.09.26 | Construction issue |
| C02 | 14.09.26 | Roof trusses revised; SP diagonals added |
| C03 | 11.10.26 | FF windows coursed; steel + GP1 portal; steel drawings (ST) |
| C04 | 13.10.26 | Steel approved by the engineer: steel + steel timber drawings issued for construction |

TLS

TLS TIMBER FRAME

Design & Manufacture

Scan: 3D model + drawings

| CLIENT | PROJECT |
|---|---|
| MP Adams | MP Adams Plot 4, Eckington |

DRAWING TITLE


**OSB CUTTING - GROUND FLOOR - SHEET 5 OF 50**

OSB/3 9mm 1197x2397 | Ground Floor

| SCALE | SIZE | DATE | DRAWN |
|---|---|---|---|
| NTS | A3 | 13.10.26 | TS |

| STATUS | DRAWING No. | REV |
|---|---|---|
| CONSTRUCTION | P4-CP-OSB-01 / 05 | C04 |

Do not scale. All dimensions in mm. Check all dimensions on site.

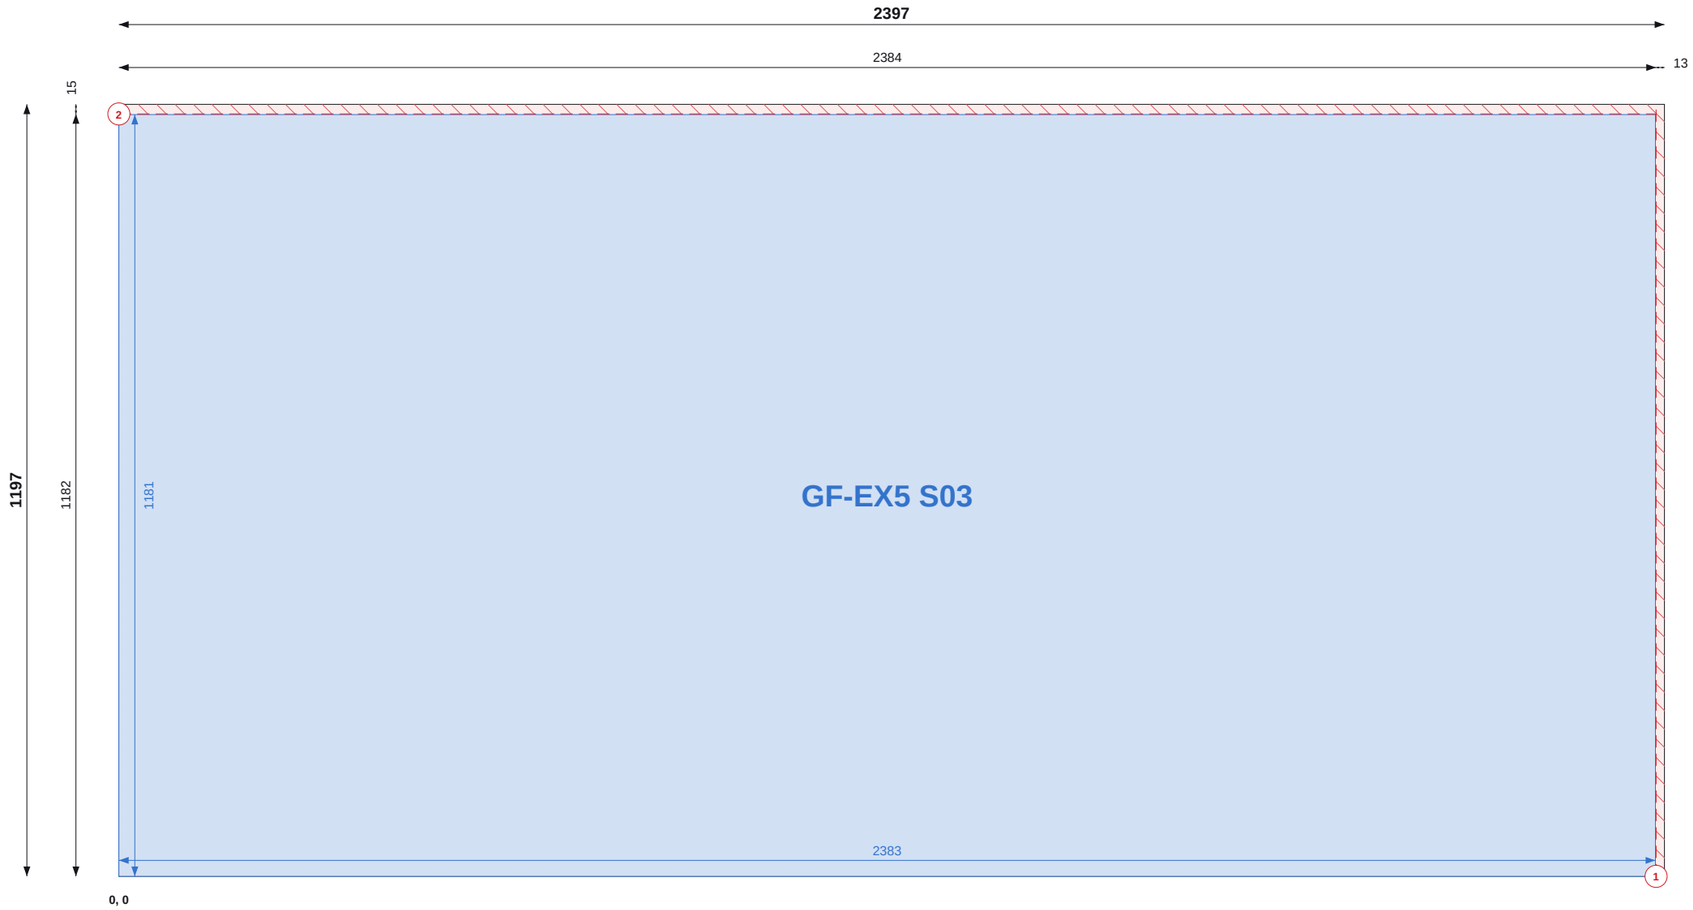


Top / left chains = saw cut positions (to cut centres). Coloured = part size and position.

## SHEET 6 OF 50

### THIS SHEET

| Item | Value |
|---|---|
| Parts | 1 |
| Used / waste | 98.1% / 0.05 m2 |
| Reusable offcuts | 0 |
| Saw cuts / shared | 2 / 0 |

### PIECES (POSITION = BOTTOM-LEFT CORNER)

| Label | Size | X, Y |
|---|---|---|
| GF-EX5 S03 | 1181 x 2383 | 0, 0 |

### NOTES

1. Cut from OSB/3 9mm 1197x2397, 2mm saw kerf. Viewed on the face; dimensions from the sheet's bottom-left corner (0,0). Red numbered lines = saw cuts in order, each edge to edge.
2. Coloured dimensions belong to the part of that colour: its width and height, and its position from the sheet edges. Raked parts: corner coordinates at each corner.
3. Red hatch = waste. Labels = panel + piece mark on the manufacture drawing.

### REVISIONS

| REV | DATE | DESCRIPTION |
|---|---|---|
| C01 | 14.09.26 | Construction issue |
| C02 | 14.09.26 | Roof trusses revised; SP diagonals added |
| C03 | 11.10.26 | FF windows coursed; steel + GP1 portal; steel drawings (ST) |
| C04 | 13.10.26 | Steel approved by the engineer: steel + steel timber drawings issued for construction |

TLS TIMBER FRAME
Design & Manufacture
Scan: 3D model + drawings

| CLIENT | PROJECT |
|---|---|
| MP Adams | MP Adams Plot 4, Eckington |

DRAWING TITLE


**OSB CUTTING - GROUND FLOOR - SHEET 6 OF 50**

OSB/3 9mm 1197x2397 | Ground Floor

| SCALE | SIZE | DATE | DRAWN |
|---|---|---|---|
| NTS | A3 | 13.10.26 | TS |

| STATUS | DRAWING No. | REV |
|---|---|---|
| CONSTRUCTION | P4-CP-OSB-01 / 06 | C04 |

Do not scale. All dimensions in mm. Check all dimensions on site.

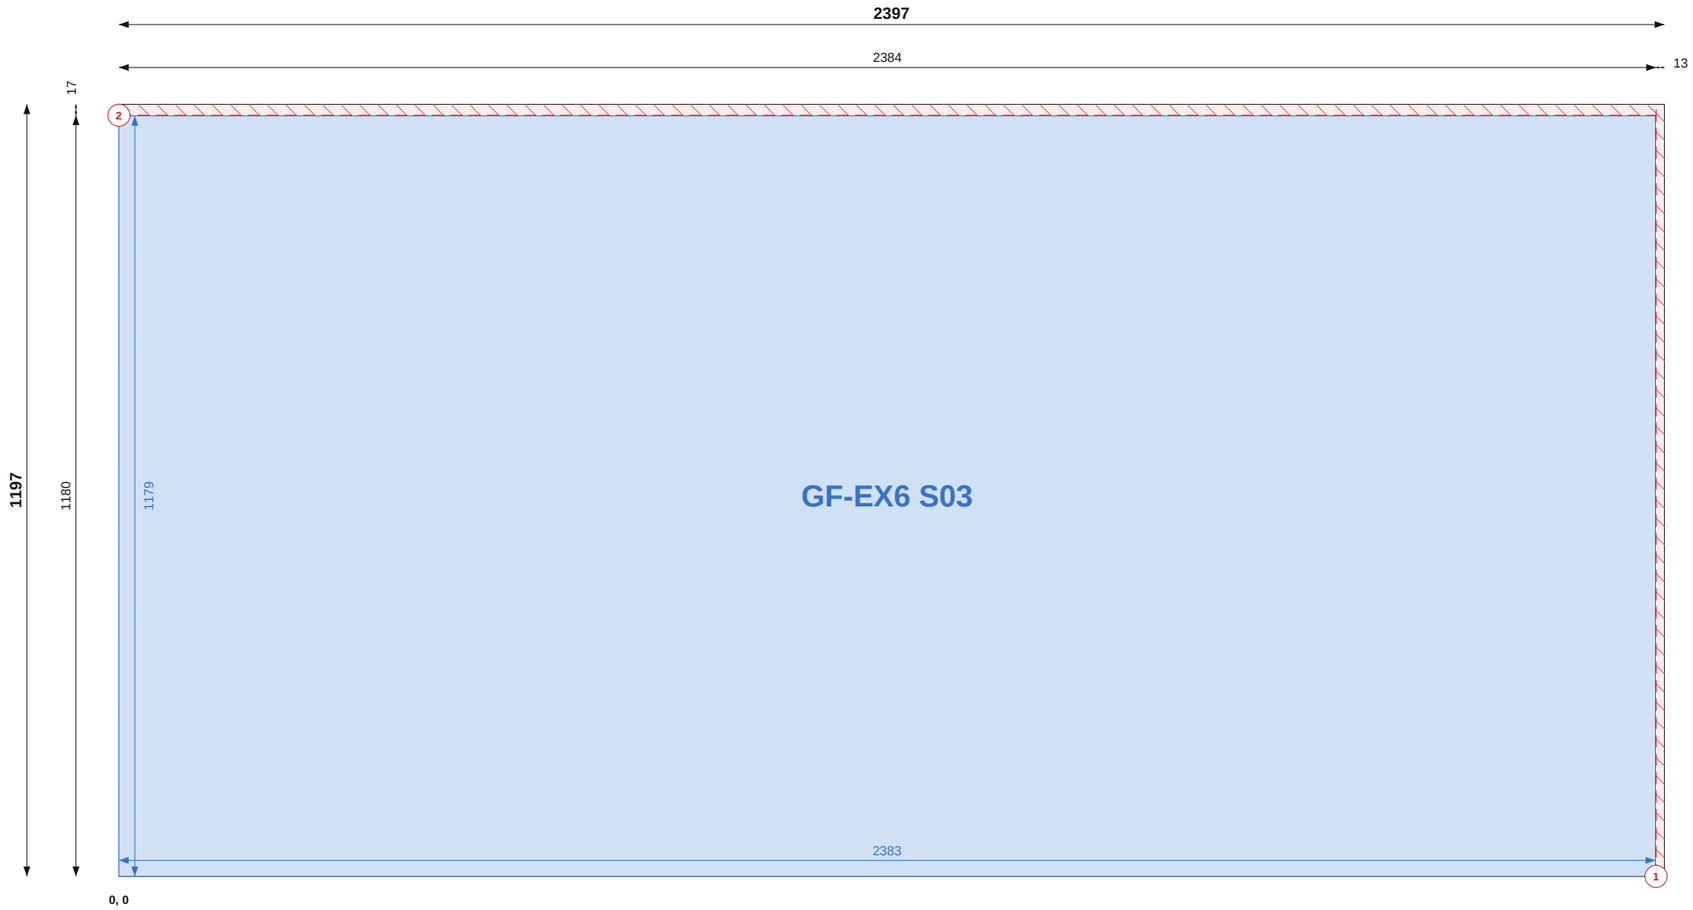


Top / left chains = saw cut positions (to cut centres). Coloured = part size and position.

## SHEET 7 OF 50

### THIS SHEET

| Item | Value |
|---|---|
| Parts | 1 |
| Used / waste | 97.9% / 0.06 m2 |
| Reusable offcuts | 0 |
| Saw cuts / shared | 2 / 0 |

### PIECES (POSITION = BOTTOM-LEFT CORNER)

| Label | Size | X, Y |
|---|---|---|
| GF-EX6 S03 | 1179 x 2383 | 0, 0 |

### NOTES

1. Cut from OSB/3 9mm 1197x2397, 2mm saw kerf. Viewed on the face; dimensions from the sheet's bottom-left corner (0,0). Red numbered lines = saw cuts in order, each edge to edge.
2. Coloured dimensions belong to the part of that colour: its width and height, and its position from the sheet edges. Raked parts: corner coordinates at each corner.
3. Red hatch = waste. Labels = panel + piece mark on the manufacture drawing.

### REVISIONS

| REV | DATE | DESCRIPTION |
|---|---|---|
| C01 | 14.09.26 | Construction issue |
| C02 | 14.09.26 | Roof trusses revised; SP diagonals added |
| C03 | 11.10.26 | FF windows coursed; steel + GP1 portal; steel drawings (ST) |
| C04 | 13.10.26 | Steel approved by the engineer: steel + steel timber drawings issued for construction |

TLS

TLS TIMBER FRAME

Design & Manufacture

Scan: 3D model + drawings

| CLIENT | PROJECT |
|---|---|
| MP Adams | MP Adams Plot 4, Eckington |

DRAWING TITLE


**OSB CUTTING - GROUND FLOOR - SHEET 7 OF 50**

OSB/3 9mm 1197x2397 | Ground Floor

| SCALE | SIZE | DATE | DRAWN |
|---|---|---|---|
| NTS | A3 | 13.10.26 | TS |

| STATUS | DRAWING No. | REV |
|---|---|---|
| CONSTRUCTION | P4-CP-OSB-01 / 07 | C04 |

Do not scale. All dimensions in mm. Check all dimensions on site.

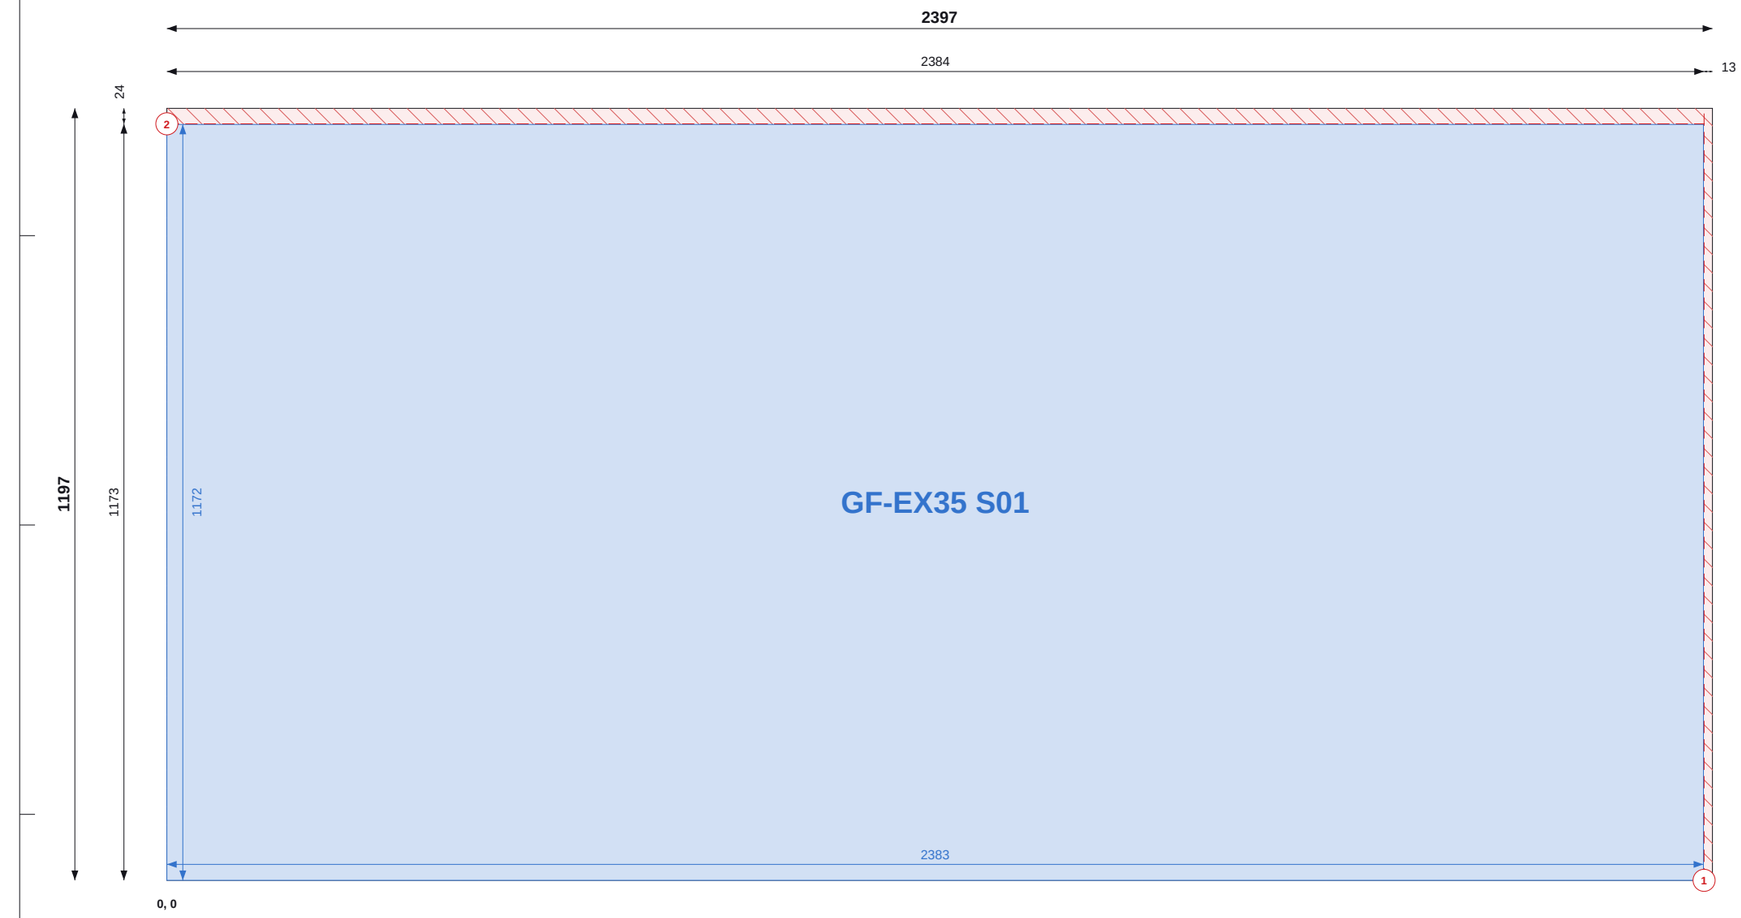


Top / left chains = saw cut positions (to cut centres). Coloured = part size and position.

## SHEET 8 OF 50

### THIS SHEET

| Item | Value |
|---|---|
| Parts | 1 |
| Used / waste | 97.3% / 0.08 m2 |
| Reusable offcuts | 0 |
| Saw cuts / shared | 2 / 0 |

### PIECES (POSITION = BOTTOM-LEFT CORNER)

| Label | Size | X, Y |
|---|---|---|
| GF-EX35 S01 | 1172 x 2383 | 0, 0 |

### NOTES

1. Cut from OSB/3 9mm 1197x2397, 2mm saw kerf. Viewed on the face; dimensions from the sheet's bottom-left corner (0,0). Red numbered lines = saw cuts in order, each edge to edge.
2. Coloured dimensions belong to the part of that colour: its width and height, and its position from the sheet edges. Raked parts: corner coordinates at each corner.
3. Red hatch = waste. Labels = panel + piece mark on the manufacture drawing.

### REVISIONS

| REV | DATE | DESCRIPTION |
|---|---|---|
| C01 | 14.09.26 | Construction issue |
| C02 | 14.09.26 | Roof trusses revised; SP diagonals added |
| C03 | 11.10.26 | FF windows coursed; steel + GP1 portal; steel drawings (ST) |
| C04 | 13.10.26 | Steel approved by the engineer: steel + steel timber drawings issued for construction |

TLS TIMBER FRAME
Design & Manufacture
Scan: 3D model + drawings

| CLIENT | PROJECT |
|---|---|
| MP Adams | MP Adams Plot 4, Eckington |

DRAWING TITLE


# OSB CUTTING - GROUND FLOOR - SHEET 8 OF 50

OSB/3 9mm 1197x2397 | Ground Floor

| SCALE | SIZE | DATE | DRAWN |
|---|---|---|---|
| NTS | A3 | 13.10.26 | TS |

| STATUS | DRAWING No. | REV |
|---|---|---|
| CONSTRUCTION | P4-CP-OSB-01 / 08 | C04 |

Do not scale. All dimensions in mm. Check all dimensions on site.

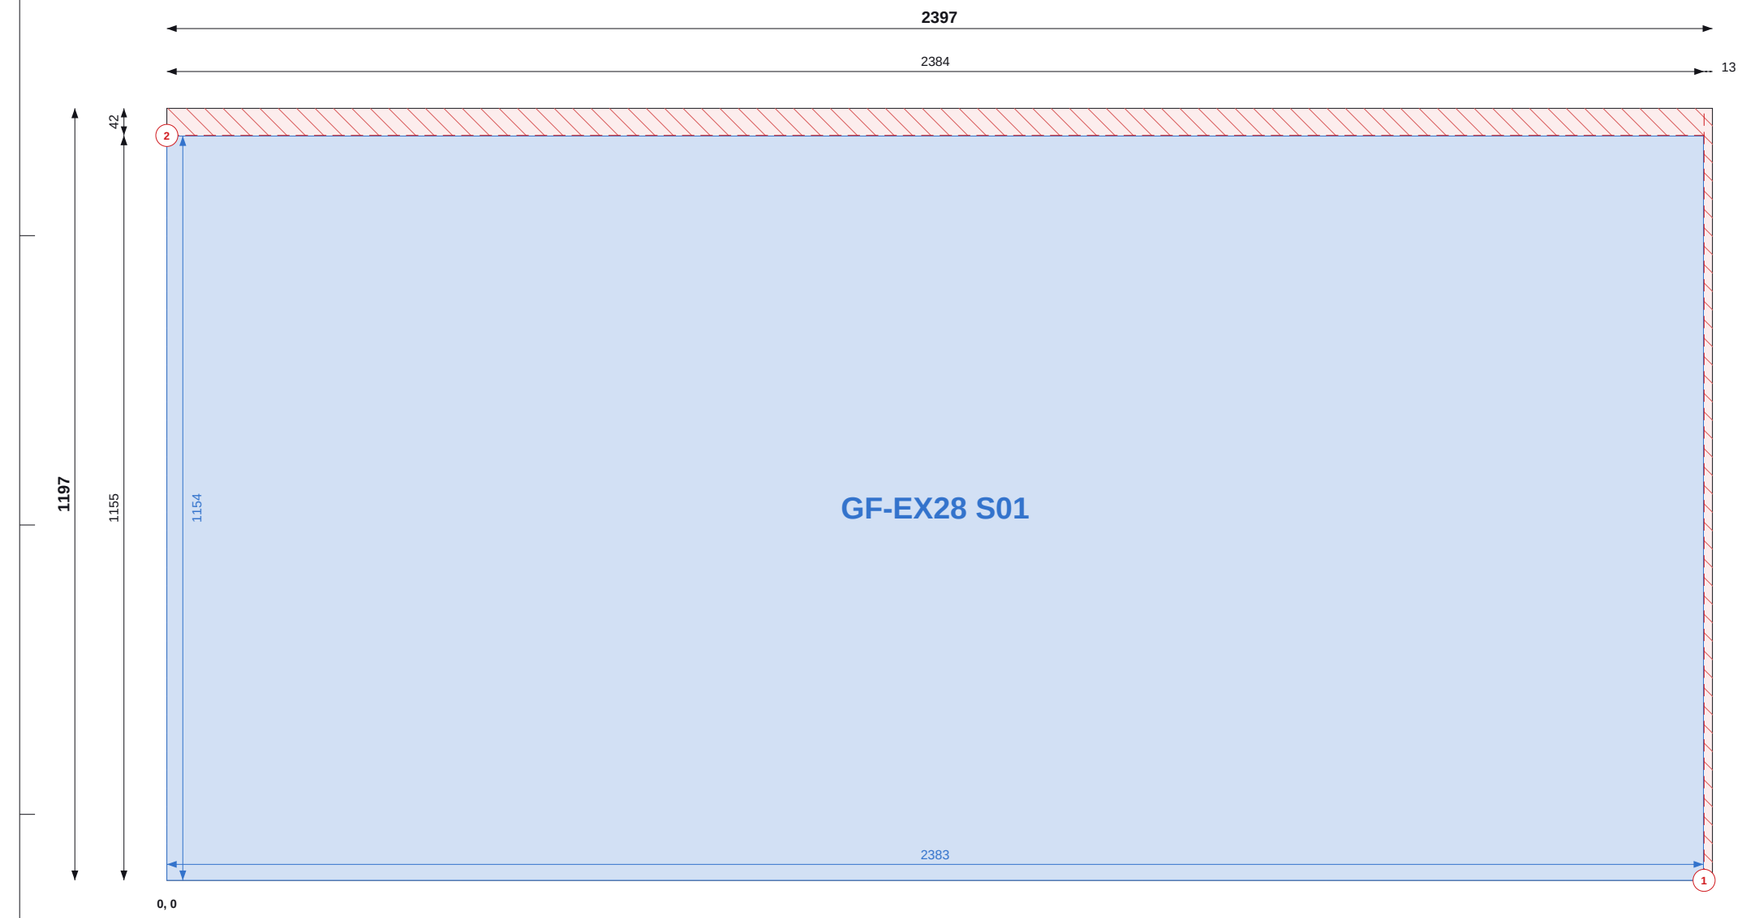


Top / left chains = saw cut positions (to cut centres). Coloured = part size and position.

## SHEET 9 OF 50

### THIS SHEET

| Item | Value |
|---|---|
| Parts | 1 |
| Used / waste | 95.8% / 0.12 m2 |
| Reusable offcuts | 0 |
| Saw cuts / shared | 2 / 0 |

### PIECES (POSITION = BOTTOM-LEFT CORNER)

| Label | Size | X, Y |
|---|---|---|
| GF-EX28 S01 | 1154 x 2383 | 0, 0 |

### NOTES

1. Cut from OSB/3 9mm 1197x2397, 2mm saw kerf. Viewed on the face; dimensions from the sheet's bottom-left corner (0,0). Red numbered lines = saw cuts in order, each edge to edge.
2. Coloured dimensions belong to the part of that colour: its width and height, and its position from the sheet edges. Raked parts: corner coordinates at each corner.
3. Red hatch = waste. Labels = panel + piece mark on the manufacture drawing.

### REVISIONS

| REV | DATE | DESCRIPTION |
|---|---|---|
| C01 | 14.09.26 | Construction issue |
| C02 | 14.09.26 | Roof trusses revised; SP diagonals added |
| C03 | 11.10.26 | FF windows coursed; steel + GP1 portal; steel drawings (ST) |
| C04 | 13.10.26 | Steel approved by the engineer: steel + steel timber drawings issued for construction |

TLS

TLS TIMBER FRAME

Design & Manufacture

Scan: 3D model + drawings

| CLIENT | PROJECT |
|---|---|
| MP Adams | MP Adams Plot 4, Eckington |

DRAWING TITLE


**OSB CUTTING - GROUND FLOOR - SHEET 9 OF 50**

OSB/3 9mm 1197x2397 | Ground Floor

| SCALE | SIZE | DATE | DRAWN |
|---|---|---|---|
| NTS | A3 | 13.10.26 | TS |

| STATUS | DRAWING No. | REV |
|---|---|---|
| CONSTRUCTION | P4-CP-OSB-01 / 09 | C04 |

Do not scale. All dimensions in mm. Check all dimensions on site.

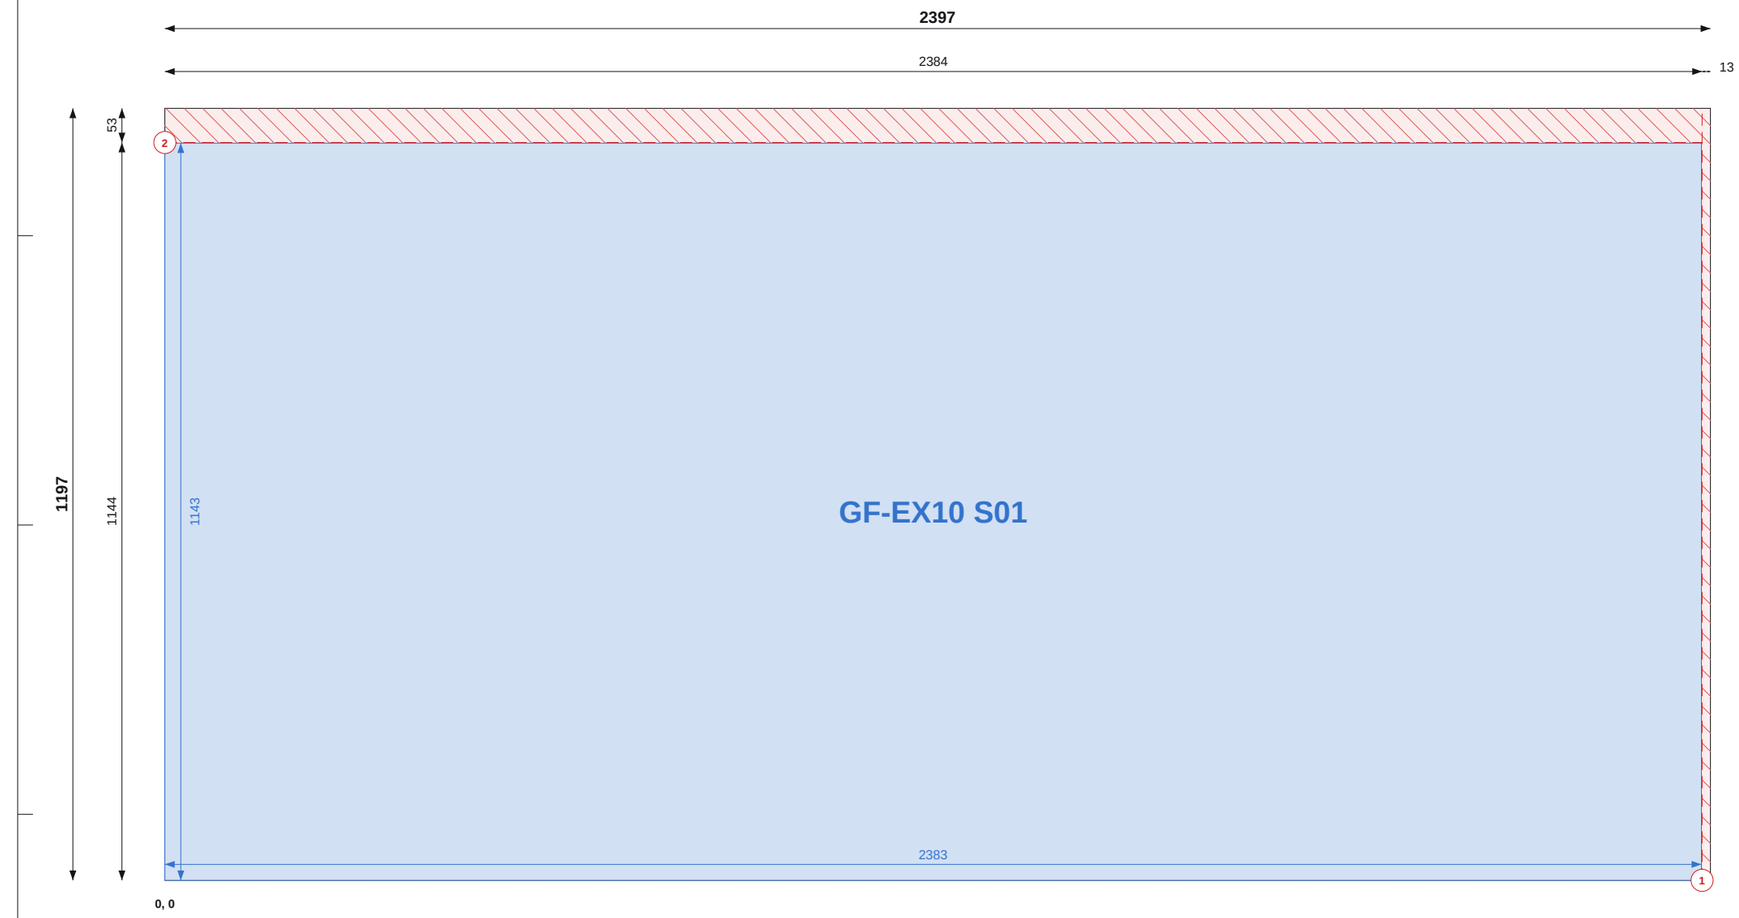


Top / left chains = saw cut positions (to cut centres). Coloured = part size and position.

## SHEET 10 OF 50

### THIS SHEET

| Item | Value |
|---|---|
| Parts | 1 |
| Used / waste | 94.9% / 0.15 m2 |
| Reusable offcuts | 0 |
| Saw cuts / shared | 2 / 0 |

### PIECES (POSITION = BOTTOM-LEFT CORNER)

| Label | Size | X, Y |
|---|---|---|
| GF-EX10 S01 | 1143 x 2383 | 0, 0 |

### NOTES

1. Cut from OSB/3 9mm 1197x2397, 2mm saw kerf. Viewed on the face; dimensions from the sheet's bottom-left corner (0,0). Red numbered lines = saw cuts in order, each edge to edge.
2. Coloured dimensions belong to the part of that colour: its width and height, and its position from the sheet edges. Raked parts: corner coordinates at each corner.
3. Red hatch = waste. Labels = panel + piece mark on the manufacture drawing.

### REVISIONS

| REV | DATE | DESCRIPTION |
|---|---|---|
| C01 | 14.09.26 | Construction issue |
| C02 | 14.09.26 | Roof trusses revised; SP diagonals added |
| C03 | 11.10.26 | FF windows coursed; steel + GP1 portal; steel drawings (ST) |
| C04 | 13.10.26 | Steel approved by the engineer: steel + steel timber drawings issued for construction |

TLS

TLS TIMBER FRAME

Design & Manufacture

Scan: 3D model + drawings

| CLIENT | PROJECT |
|---|---|
| MP Adams | MP Adams Plot 4, Eckington |

DRAWING TITLE


**OSB CUTTING - GROUND FLOOR - SHEET 10 OF 50**

OSB/3 9mm 1197x2397 | Ground Floor

| SCALE | SIZE | DATE | DRAWN |
|---|---|---|---|
| NTS | A3 | 13.10.26 | TS |

| STATUS | DRAWING No. | REV |
|---|---|---|
| CONSTRUCTION | P4-CP-OSB-01 / 10 | C04 |

Do not scale. All dimensions in mm. Check all dimensions on site.

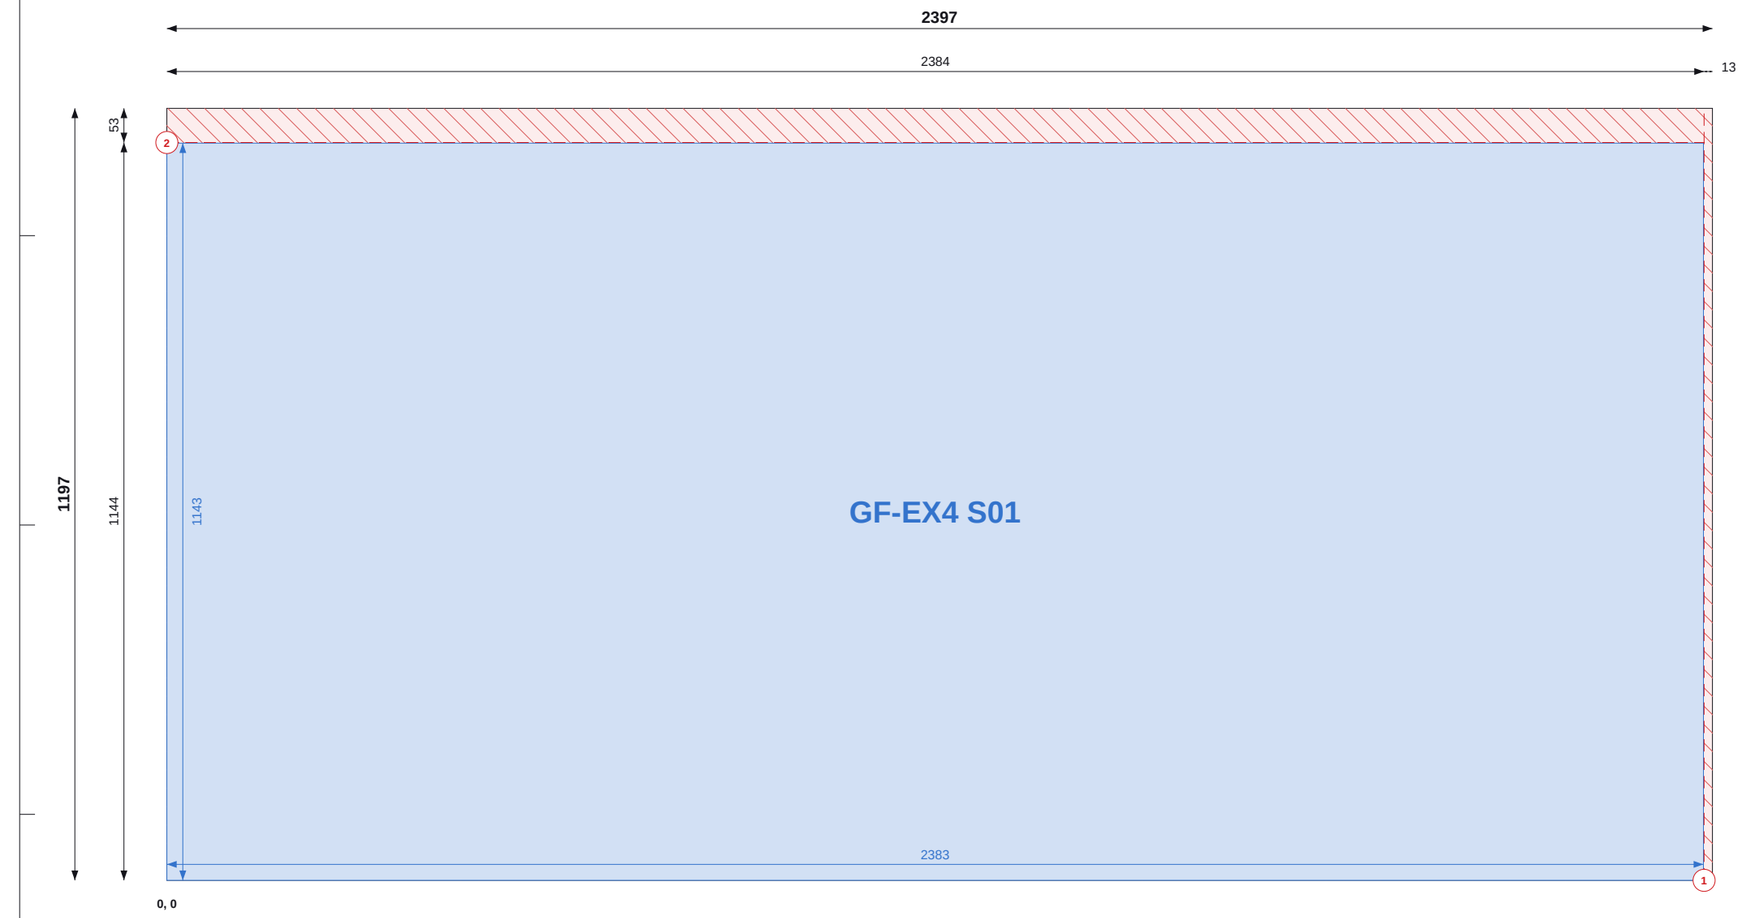


Top / left chains = saw cut positions (to cut centres). Coloured = part size and position.

## SHEET 11 OF 50

### THIS SHEET

| Item | Value |
|---|---|
| Parts | 1 |
| Used / waste | 94.9% / 0.15 m2 |
| Reusable offcuts | 0 |
| Saw cuts / shared | 2 / 0 |

### PIECES (POSITION = BOTTOM-LEFT CORNER)

| Label | Size | X, Y |
|---|---|---|
| GF-EX4 S01 | 1143 x 2383 | 0, 0 |

### NOTES

1. Cut from OSB/3 9mm 1197x2397, 2mm saw kerf. Viewed on the face; dimensions from the sheet's bottom-left corner (0,0). Red numbered lines = saw cuts in order, each edge to edge.
2. Coloured dimensions belong to the part of that colour: its width and height, and its position from the sheet edges. Raked parts: corner coordinates at each corner.
3. Red hatch = waste. Labels = panel + piece mark on the manufacture drawing.

### REVISIONS

| REV | DATE | DESCRIPTION |
|---|---|---|
| C01 | 14.09.26 | Construction issue |
| C02 | 14.09.26 | Roof trusses revised; SP diagonals added |
| C03 | 11.10.26 | FF windows coursed; steel + GP1 portal; steel drawings (ST) |
| C04 | 13.10.26 | Steel approved by the engineer: steel + steel timber drawings issued for construction |

TLS

TLS TIMBER FRAME

Design & Manufacture

Scan: 3D model + drawings

| CLIENT | PROJECT |
|---|---|
| MP Adams | MP Adams Plot 4, Eckington |

DRAWING TITLE


**OSB CUTTING - GROUND FLOOR - SHEET 11 OF 50**

OSB/3 9mm 1197x2397 | Ground Floor

| SCALE | SIZE | DATE | DRAWN |
|---|---|---|---|
| NTS | A3 | 13.10.26 | TS |

| STATUS | DRAWING No. | REV |
|---|---|---|
| CONSTRUCTION | P4-CP-OSB-01 / 11 | C04 |

Do not scale. All dimensions in mm. Check all dimensions on site.

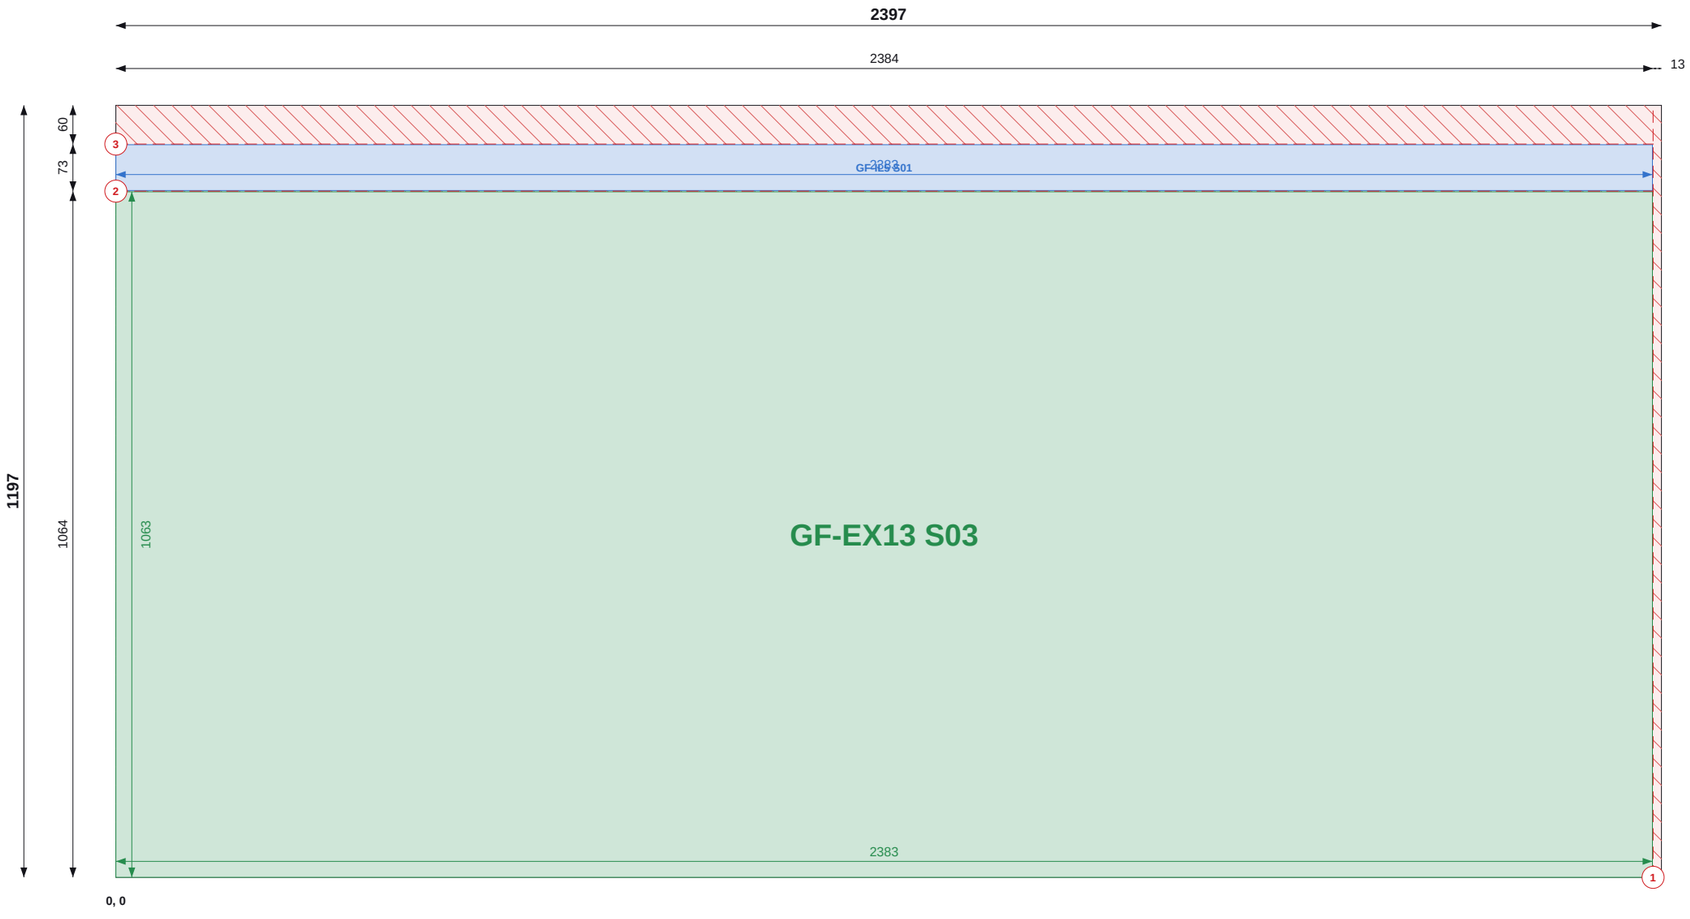


Top / left chains = saw cut positions (to cut centres). Coloured = part size and position.

## SHEET 12 OF 50

### THIS SHEET

| Item | Value |
|---|---|
| Parts | 2 |
| Used / waste | 94.2% / 0.17 m2 |
| Reusable offcuts | 0 |
| Saw cuts / shared | 3 / 1 |

### PIECES (POSITION = BOTTOM-LEFT CORNER)

| Label | Size | X, Y |
|---|---|---|
| GF-IL5 S01 | 71 x 2383 | 0, 1065 |
| GF-EX13 S03 | 1063 x 2383 | 0, 0 |

### NOTES

1. Cut from OSB/3 9mm 1197x2397, 2mm saw kerf. Viewed on the face; dimensions from the sheet's bottom-left corner (0,0). Red numbered lines = saw cuts in order, each edge to edge.
2. Coloured dimensions belong to the part of that colour: its width and height, and its position from the sheet edges. Raked parts: corner coordinates at each corner.
3. Red hatch = waste. Labels = panel + piece mark on the manufacture drawing.

### REVISIONS

| REV | DATE | DESCRIPTION |
|---|---|---|
| C01 | 14.09.26 | Construction issue |
| C02 | 14.09.26 | Roof trusses revised; SP diagonals added |
| C03 | 11.10.26 | FF windows coursed; steel + GP1 portal; steel drawings (ST) |
| C04 | 13.10.26 | Steel approved by the engineer: steel + steel timber drawings issued for construction |

TLS TIMBER FRAME DESIGN SUITE

**TLS TIMBER FRAME**

Design & Manufacture

Scan: 3D model + drawings

| CLIENT | PROJECT |
|---|---|
| MP Adams | MP Adams Plot 4, Eckington |

DRAWING TITLE


**OSB CUTTING - GROUND FLOOR - SHEET 12 OF 50**

OSB/3 9mm 1197x2397 | Ground Floor

| SCALE | SIZE | DATE | DRAWN |
|---|---|---|---|
| NTS | A3 | 13.10.26 | TS |

| STATUS | DRAWING No. | REV |
|---|---|---|
| CONSTRUCTION | P4-CP-OSB-01 / 12 | C04 |

Do not scale. All dimensions in mm. Check all dimensions on site.

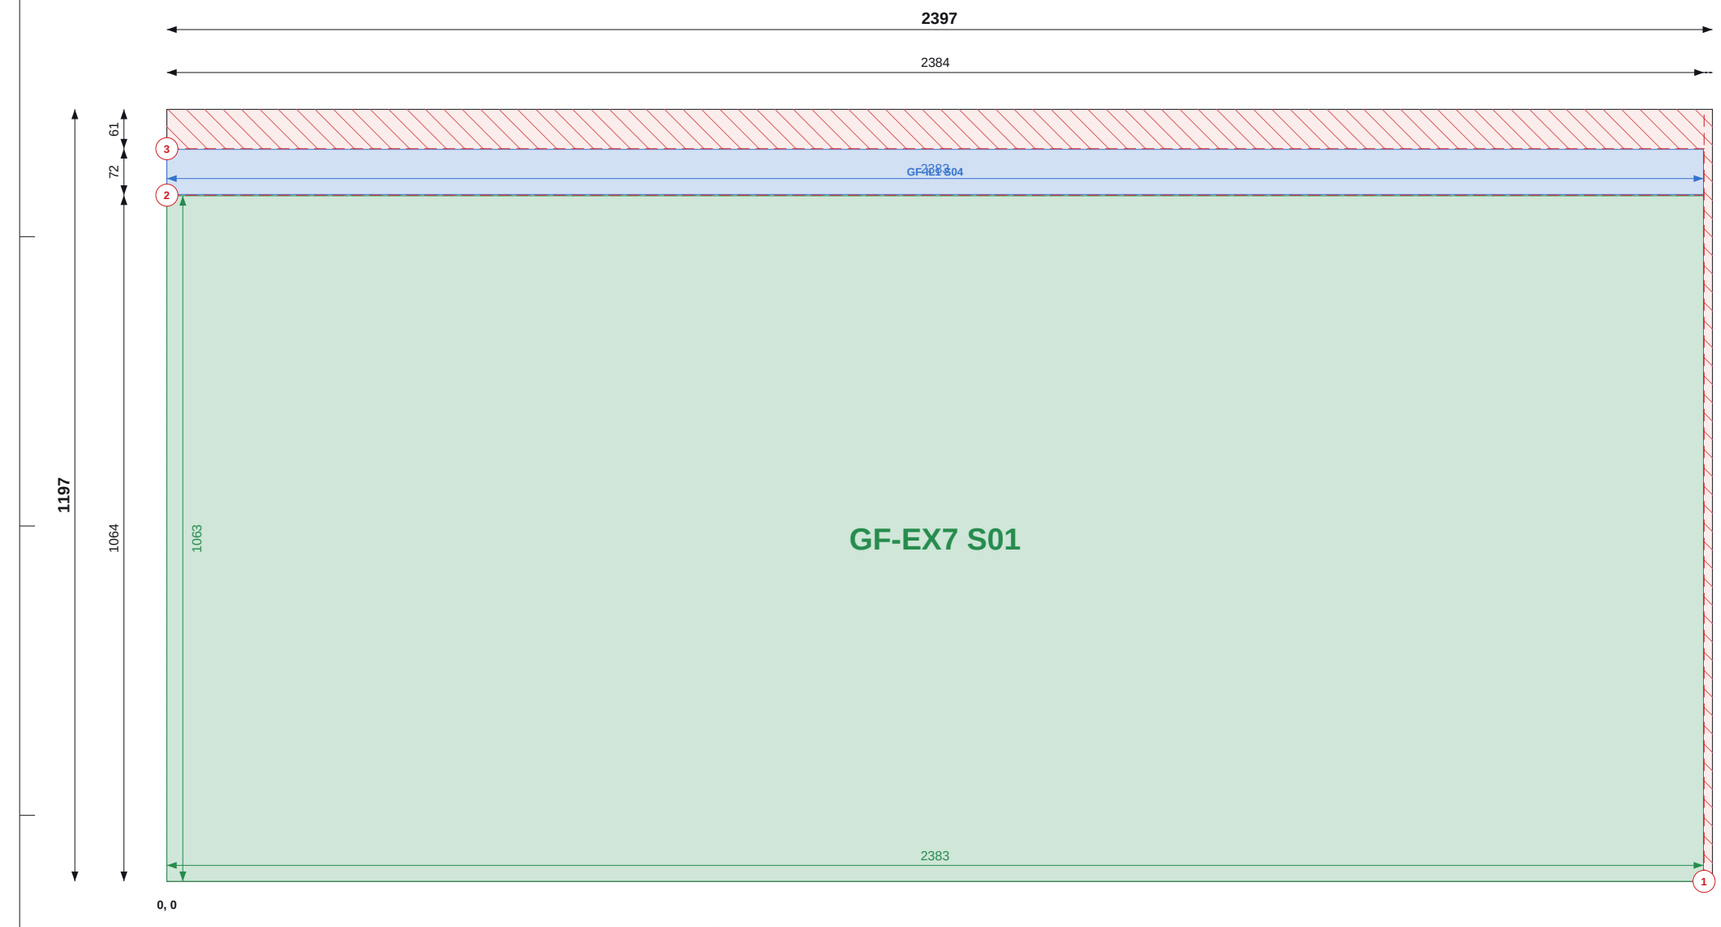


Top / left chains = saw cut positions (to cut centres). Coloured = part size and position.

## SHEET 13 OF 50

### THIS SHEET

| Item | Value |
|---|---|
| Parts | 2 |
| Used / waste | 94.1% / 0.17 m2 |
| Reusable offcuts | 0 |
| Saw cuts / shared | 3 / 1 |

### PIECES (POSITION = BOTTOM-LEFT CORNER)

| Label | Size | X, Y |
|---|---|---|
| GF-IL1 S04 | 70 x 2383 | 0, 1065 |
| GF-EX7 S01 | 1063 x 2383 | 0, 0 |

### NOTES

1. Cut from OSB/3 9mm 1197x2397, 2mm saw kerf. Viewed on the face; dimensions from the sheet's bottom-left corner (0,0). Red numbered lines = saw cuts in order, each edge to edge.
2. Coloured dimensions belong to the part of that colour: its width and height, and its position from the sheet edges. Raked parts: corner coordinates at each corner.
3. Red hatch = waste. Labels = panel + piece mark on the manufacture drawing.

### REVISIONS

| REV | DATE | DESCRIPTION |
|---|---|---|
| C01 | 14.09.26 | Construction issue |
| C02 | 14.09.26 | Roof trusses revised; SP diagonals added |
| C03 | 11.10.26 | FF windows coursed; steel + GP1 portal; steel drawings (ST) |
| C04 | 13.10.26 | Steel approved by the engineer: steel + steel timber drawings issued for construction |

TLS TIMBER FRAME DESIGN SUITE

**TLS TIMBER FRAME**

Design & Manufacture

Scan: 3D model + drawings

| CLIENT | PROJECT |
|---|---|
| MP Adams | MP Adams Plot 4, Eckington |

DRAWING TITLE


**OSB CUTTING - GROUND FLOOR - SHEET 13 OF 50**

OSB/3 9mm 1197x2397 | Ground Floor

| SCALE | SIZE | DATE | DRAWN |
|---|---|---|---|
| NTS | A3 | 13.10.26 | TS |

| STATUS | DRAWING No. | REV |
|---|---|---|
| CONSTRUCTION | P4-CP-OSB-01 / 13 | C04 |

Do not scale. All dimensions in mm. Check all dimensions on site.

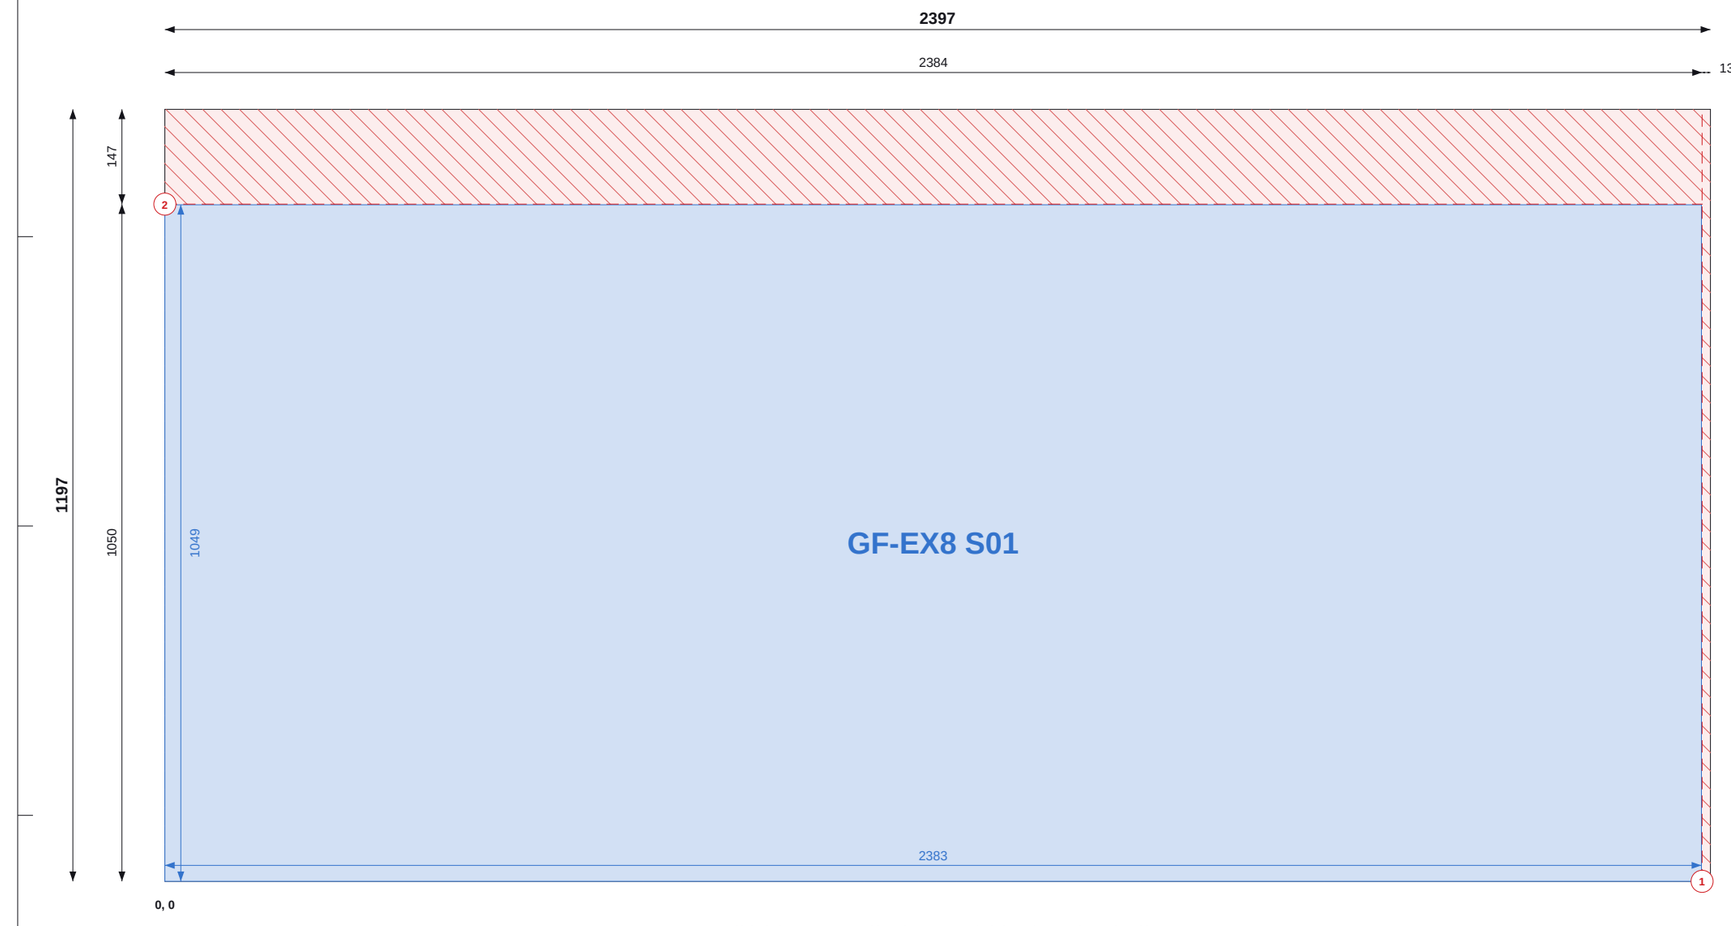


Top / left chains = saw cut positions (to cut centres). Coloured = part size and position.

## SHEET 14 OF 50

### THIS SHEET

| Item | Value |
|---|---|
| Parts | 1 |
| Used / waste | 87.1% / 0.37 m2 |
| Reusable offcuts | 0 |
| Saw cuts / shared | 2 / 0 |

### PIECES (POSITION = BOTTOM-LEFT CORNER)

| Label | Size | X, Y |
|---|---|---|
| GF-EX8 S01 | 1049 x 2383 | 0, 0 |

### NOTES

1. Cut from OSB/3 9mm 1197x2397, 2mm saw kerf. Viewed on the face; dimensions from the sheet's bottom-left corner (0,0). Red numbered lines = saw cuts in order, each edge to edge.
2. Coloured dimensions belong to the part of that colour: its width and height, and its position from the sheet edges. Raked parts: corner coordinates at each corner.
3. Red hatch = waste. Labels = panel + piece mark on the manufacture drawing.

### REVISIONS

| REV | DATE | DESCRIPTION |
|---|---|---|
| C01 | 14.09.26 | Construction issue |
| C02 | 14.09.26 | Roof trusses revised; SP diagonals added |
| C03 | 11.10.26 | FF windows coursed; steel + GP1 portal; steel drawings (ST) |
| C04 | 13.10.26 | Steel approved by the engineer: steel + steel timber drawings issued for construction |

TLS TIMBER FRAME DESIGN SUITE

**TLS TIMBER FRAME**
Design & Manufacture
Scan: 3D model + drawings

| CLIENT | PROJECT |
|---|---|
| MP Adams | MP Adams Plot 4, Eckington |

DRAWING TITLE


**OSB CUTTING - GROUND FLOOR - SHEET 14 OF 50**

OSB/3 9mm 1197x2397 | Ground Floor

| SCALE | SIZE | DATE | DRAWN |
|---|---|---|---|
| NTS | A3 | 13.10.26 | TS |

| STATUS | DRAWING No. | REV |
|---|---|---|
| CONSTRUCTION | P4-CP-OSB-01 / 14 | C04 |

Do not scale. All dimensions in mm. Check all dimensions on site.

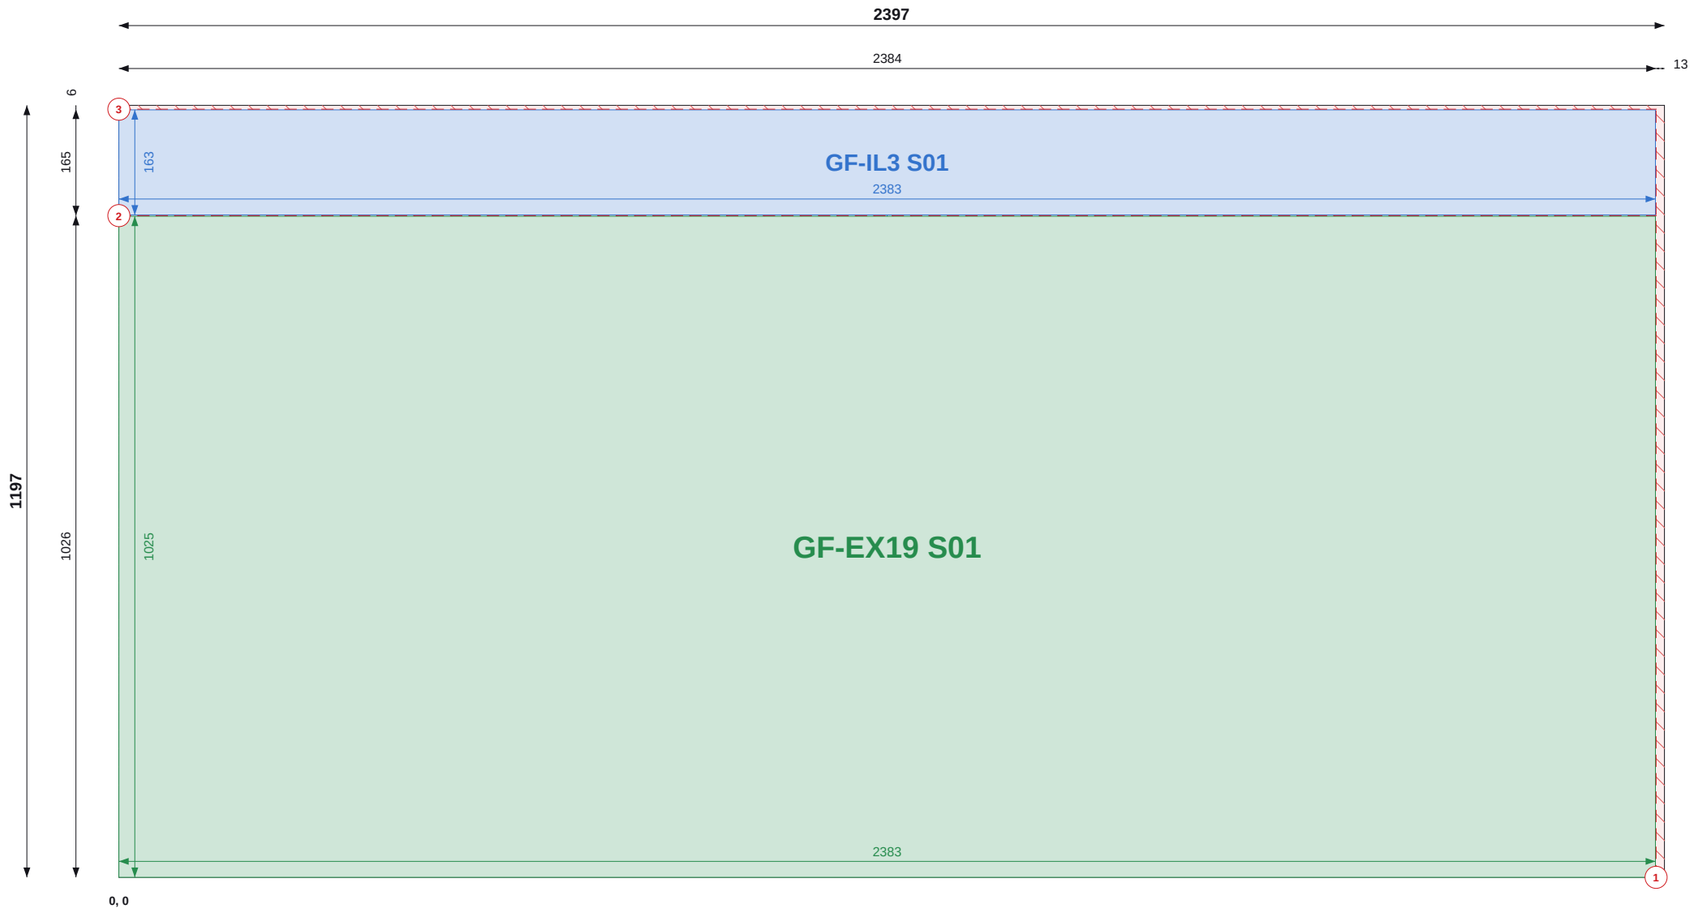


Top / left chains = saw cut positions (to cut centres). Coloured = part size and position.

## SHEET 15 OF 50

### THIS SHEET

| Item | Value |
|---|---|
| Parts | 2 |
| Used / waste | 98.7% / 0.04 m2 |
| Reusable offcuts | 0 |
| Saw cuts / shared | 3 / 1 |

### PIECES (POSITION = BOTTOM-LEFT CORNER)

| Label | Size | X, Y |
|---|---|---|
| GF-IL3 S01 | 163 x 2383 | 0, 1027 |
| GF-EX19 S01 | 1025 x 2383 | 0, 0 |

### NOTES

1. Cut from OSB/3 9mm 1197x2397, 2mm saw kerf. Viewed on the face; dimensions from the sheet's bottom-left corner (0,0). Red numbered lines = saw cuts in order, each edge to edge.
2. Coloured dimensions belong to the part of that colour: its width and height, and its position from the sheet edges. Raked parts: corner coordinates at each corner.
3. Red hatch = waste. Labels = panel + piece mark on the manufacture drawing.

### REVISIONS

| REV | DATE | DESCRIPTION |
|---|---|---|
| C01 | 14.09.26 | Construction issue |
| C02 | 14.09.26 | Roof trusses revised; SP diagonals added |
| C03 | 11.10.26 | FF windows coursed; steel + GP1 portal; steel drawings (ST) |
| C04 | 13.10.26 | Steel approved by the engineer: steel + steel timber drawings issued for construction |

TLS TIMBER FRAME
Design & Manufacture
Scan: 3D model + drawings

| CLIENT | PROJECT |
|---|---|
| MP Adams | MP Adams Plot 4, Eckington |

DRAWING TITLE


**OSB CUTTING - GROUND FLOOR - SHEET 15 OF 50**

OSB/3 9mm 1197x2397 | Ground Floor

| SCALE | SIZE | DATE | DRAWN |
|---|---|---|---|
| NTS | A3 | 13.10.26 | TS |

| STATUS | DRAWING No. | REV |
|---|---|---|
| CONSTRUCTION | P4-CP-OSB-01 / 15 | C04 |

Do not scale. All dimensions in mm. Check all dimensions on site.

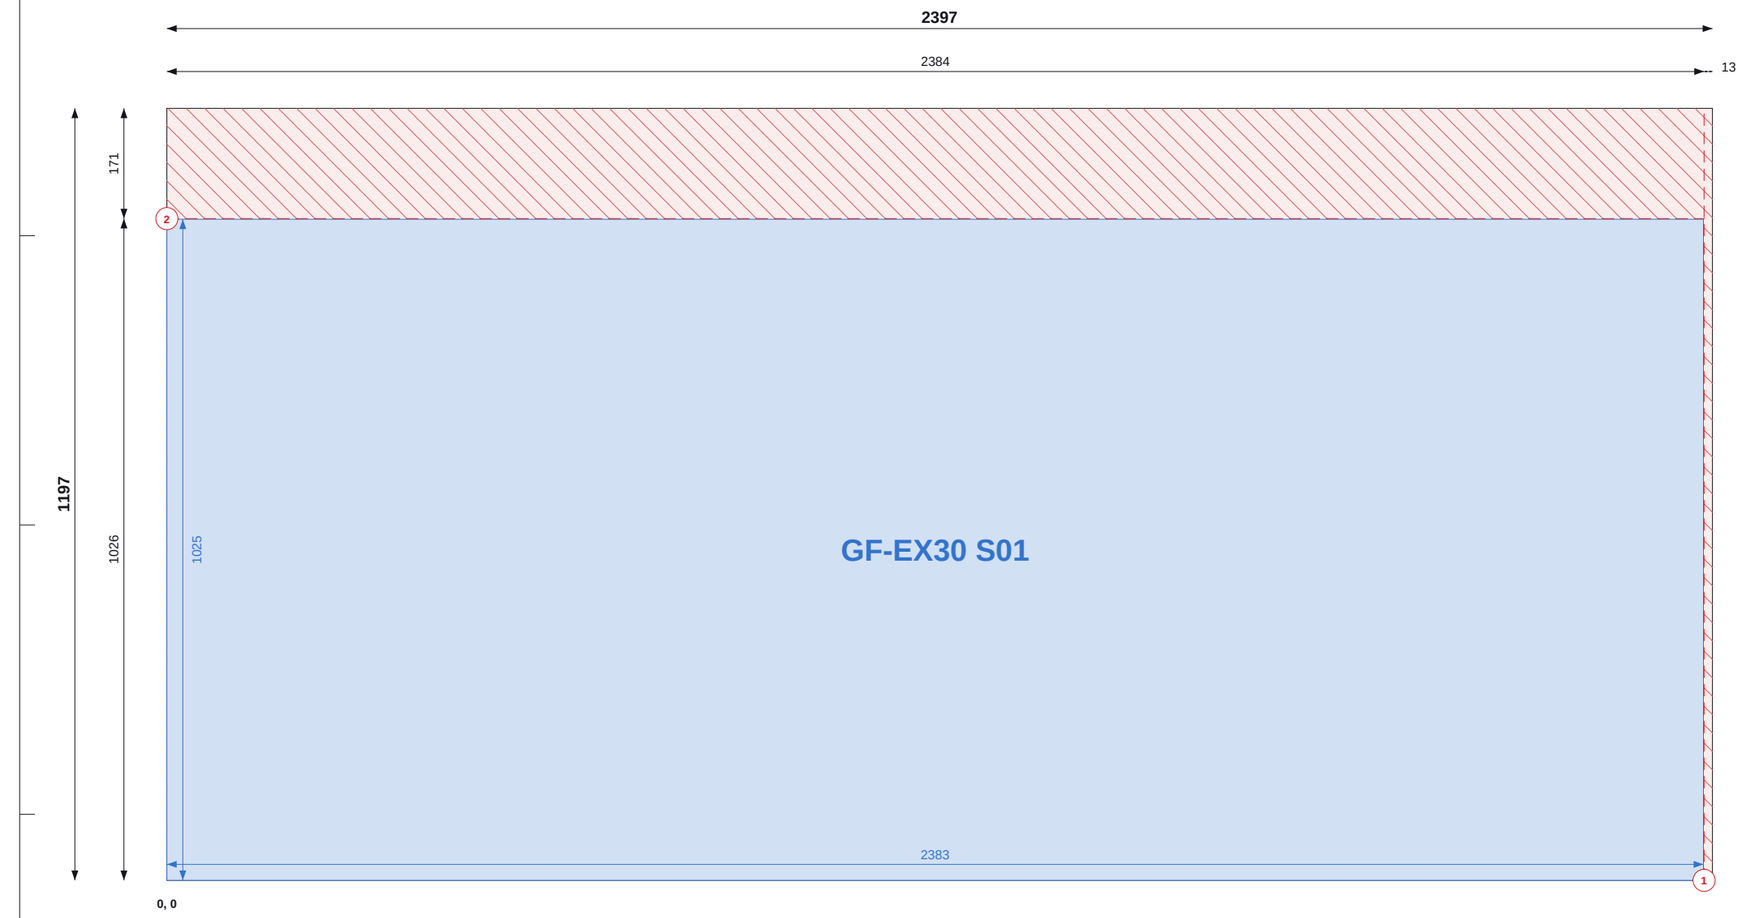


Top / left chains = saw cut positions (to cut centres). Coloured = part size and position.

## SHEET 16 OF 50

### THIS SHEET

| Item | Value |
|---|---|
| Parts | 1 |
| Used / waste | 85.1% / 0.43 m2 |
| Reusable offcuts | 0 |
| Saw cuts / shared | 2 / 0 |

### PIECES (POSITION = BOTTOM-LEFT CORNER)

| Label | Size | X, Y |
|---|---|---|
| GF-EX30 S01 | 1025 x 2383 | 0, 0 |

### NOTES

1. Cut from OSB/3 9mm 1197x2397, 2mm saw kerf. Viewed on the face; dimensions from the sheet's bottom-left corner (0,0). Red numbered lines = saw cuts in order, each edge to edge.
2. Coloured dimensions belong to the part of that colour: its width and height, and its position from the sheet edges. Raked parts: corner coordinates at each corner.
3. Red hatch = waste. Labels = panel + piece mark on the manufacture drawing.

### REVISIONS

| REV | DATE | DESCRIPTION |
|---|---|---|
| C01 | 14.09.26 | Construction issue |
| C02 | 14.09.26 | Roof trusses revised; SP diagonals added |
| C03 | 11.10.26 | FF windows coursed; steel + GP1 portal; steel drawings (ST) |
| C04 | 13.10.26 | Steel approved by the engineer: steel + steel timber drawings issued for construction |

TLS

TLS TIMBER FRAME

Design & Manufacture

Scan: 3D model + drawings

| CLIENT | PROJECT |
|---|---|
| MP Adams | MP Adams Plot 4, Eckington |

DRAWING TITLE


**OSB CUTTING - GROUND FLOOR - SHEET 16 OF 50**

OSB/3 9mm 1197x2397 | Ground Floor

| SCALE | SIZE | DATE | DRAWN |
|---|---|---|---|
| NTS | A3 | 13.10.26 | TS |

| STATUS | DRAWING No. | REV |
|---|---|---|
| CONSTRUCTION | P4-CP-OSB-01 / 16 | C04 |

Do not scale. All dimensions in mm. Check all dimensions on site.

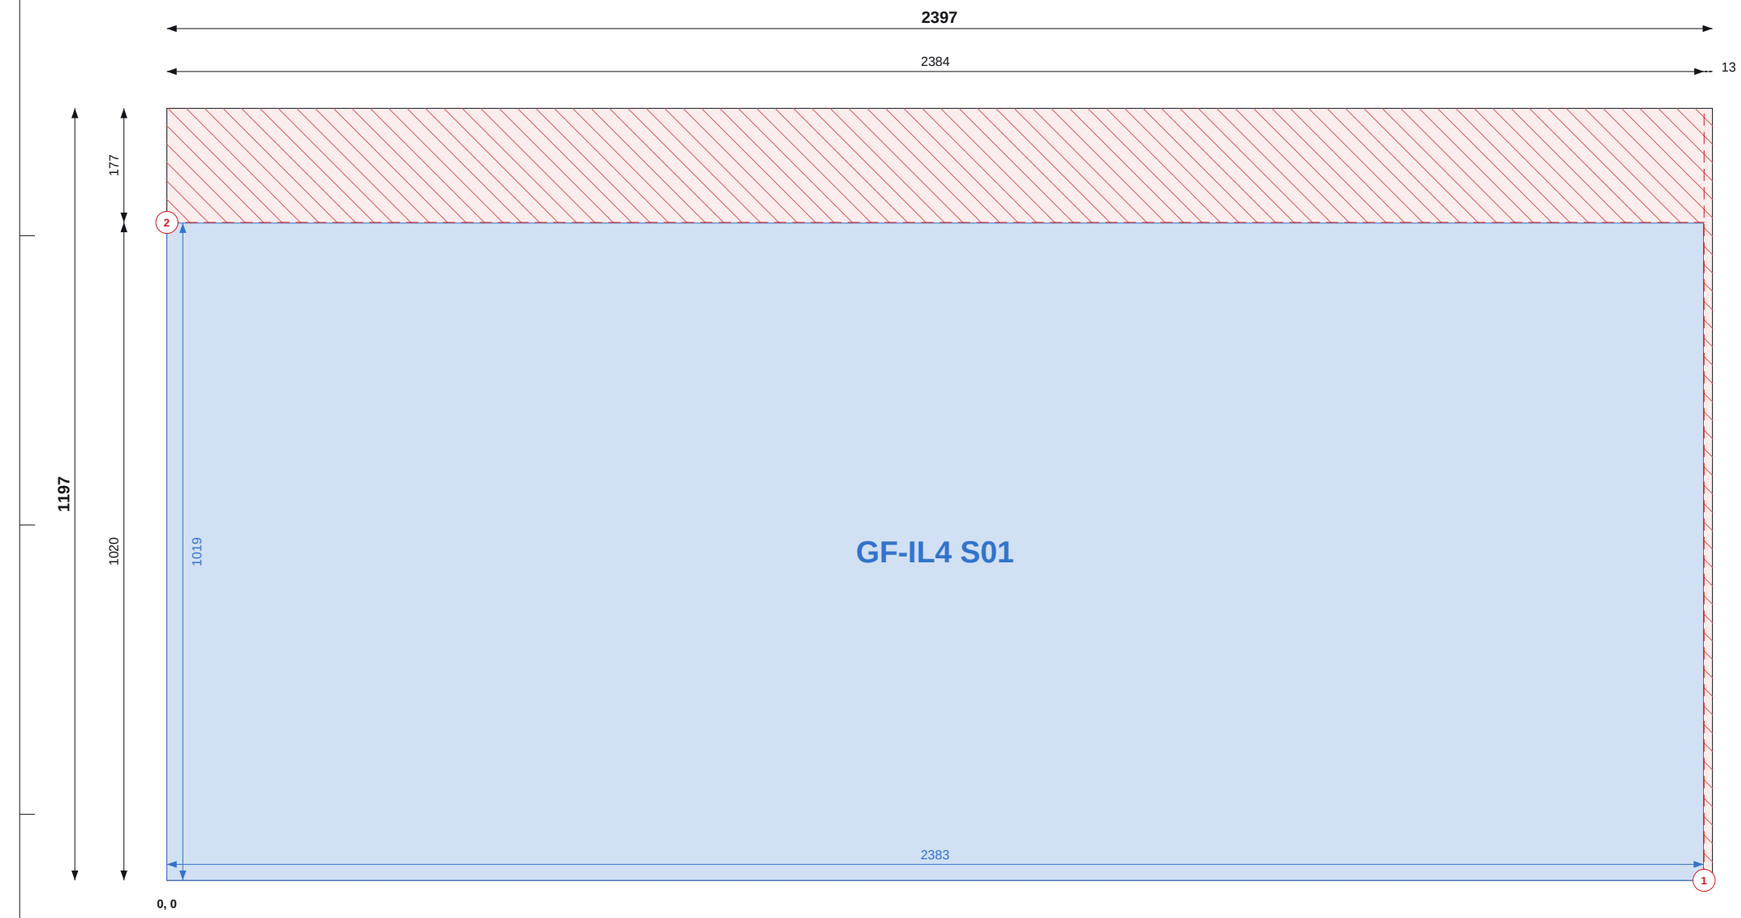


Top / left chains = saw cut positions (to cut centres). Coloured = part size and position.

## SHEET 17 OF 50

### THIS SHEET

| Item | Value |
|---|---|
| Parts | 1 |
| Used / waste | 84.6% / 0.44 m2 |
| Reusable offcuts | 0 |
| Saw cuts / shared | 2 / 0 |

### PIECES (POSITION = BOTTOM-LEFT CORNER)

| Label | Size | X, Y |
|---|---|---|
| GF-IL4 S01 | 1019 x 2383 | 0, 0 |

### NOTES

1. Cut from OSB/3 9mm 1197x2397, 2mm saw kerf. Viewed on the face; dimensions from the sheet's bottom-left corner (0,0). Red numbered lines = saw cuts in order, each edge to edge.
2. Coloured dimensions belong to the part of that colour: its width and height, and its position from the sheet edges. Raked parts: corner coordinates at each corner.
3. Red hatch = waste. Labels = panel + piece mark on the manufacture drawing.

### REVISIONS

| REV | DATE | DESCRIPTION |
|---|---|---|
| C01 | 14.09.26 | Construction issue |
| C02 | 14.09.26 | Roof trusses revised; SP diagonals added |
| C03 | 11.10.26 | FF windows coursed; steel + GP1 portal; steel drawings (ST) |
| C04 | 13.10.26 | Steel approved by the engineer: steel + steel timber drawings issued for construction |

TLS TIMBER FRAME
Design & Manufacture
Scan: 3D model + drawings

| CLIENT | PROJECT |
|---|---|
| MP Adams | MP Adams Plot 4, Eckington |


DRAWING TITLE
**OSB CUTTING - GROUND FLOOR - SHEET 17 OF 50**

OSB/3 9mm 1197x2397 | Ground Floor

| SCALE | SIZE | DATE | DRAWN |
|---|---|---|---|
| NTS | A3 | 13.10.26 | TS |

| STATUS | DRAWING No. | REV |
|---|---|---|
| CONSTRUCTION | P4-CP-OSB-01 / 17 | C04 |

Do not scale. All dimensions in mm. Check all dimensions on site.

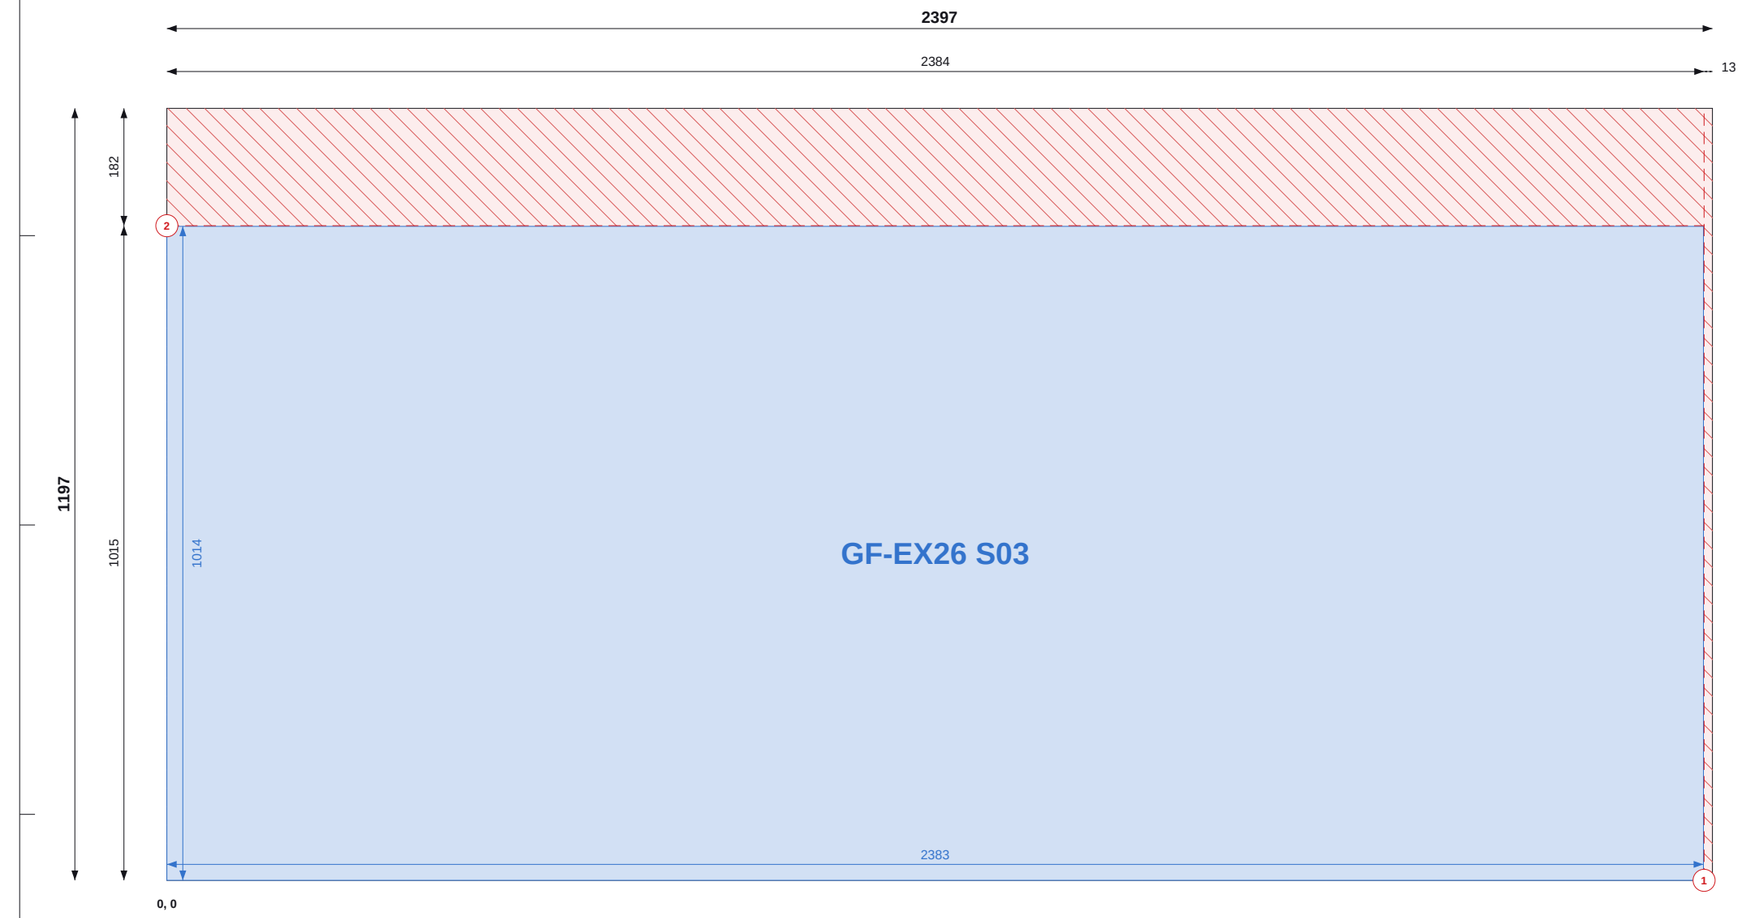


Top / left chains = saw cut positions (to cut centres). Coloured = part size and position.

Do not scale. All dimensions in mm. Check all dimensions on site.

## SHEET 18 OF 50

### THIS SHEET

| Item | Value |
|---|---|
| Parts | 1 |
| Used / waste | 84.2% / 0.45 m2 |
| Reusable offcuts | 0 |
| Saw cuts / shared | 2 / 0 |

### PIECES (POSITION = BOTTOM-LEFT CORNER)

| Label | Size | X, Y |
|---|---|---|
| GF-EX26 S03 | 1014 x 2383 | 0, 0 |

### NOTES

1. Cut from OSB/3 9mm 1197x2397, 2mm saw kerf. Viewed on the face; dimensions from the sheet's bottom-left corner (0,0). Red numbered lines = saw cuts in order, each edge to edge.
2. Coloured dimensions belong to the part of that colour: its width and height, and its position from the sheet edges. Raked parts: corner coordinates at each corner.
3. Red hatch = waste. Labels = panel + piece mark on the manufacture drawing.

### REVISIONS

| REV | DATE | DESCRIPTION |
|---|---|---|
| C01 | 14.09.26 | Construction issue |
| C02 | 14.09.26 | Roof trusses revised; SP diagonals added |
| C03 | 11.10.26 | FF windows coursed; steel + GP1 portal; steel drawings (ST) |
| C04 | 13.10.26 | Steel approved by the engineer: steel + steel timber drawings issued for construction |

TLS

TLS TIMBER FRAME

Design & Manufacture

Scan: 3D model + drawings

| CLIENT | PROJECT |
|---|---|
| MP Adams | MP Adams Plot 4, Eckington |


DRAWING TITLE

**OSB CUTTING - GROUND FLOOR - SHEET 18 OF 50**

OSB/3 9mm 1197x2397 | Ground Floor

| SCALE | SIZE | DATE | DRAWN |
|---|---|---|---|
| NTS | A3 | 13.10.26 | TS |

| STATUS | DRAWING No. | REV |
|---|---|---|
| CONSTRUCTION | P4-CP-OSB-01 / 18 | C04 |

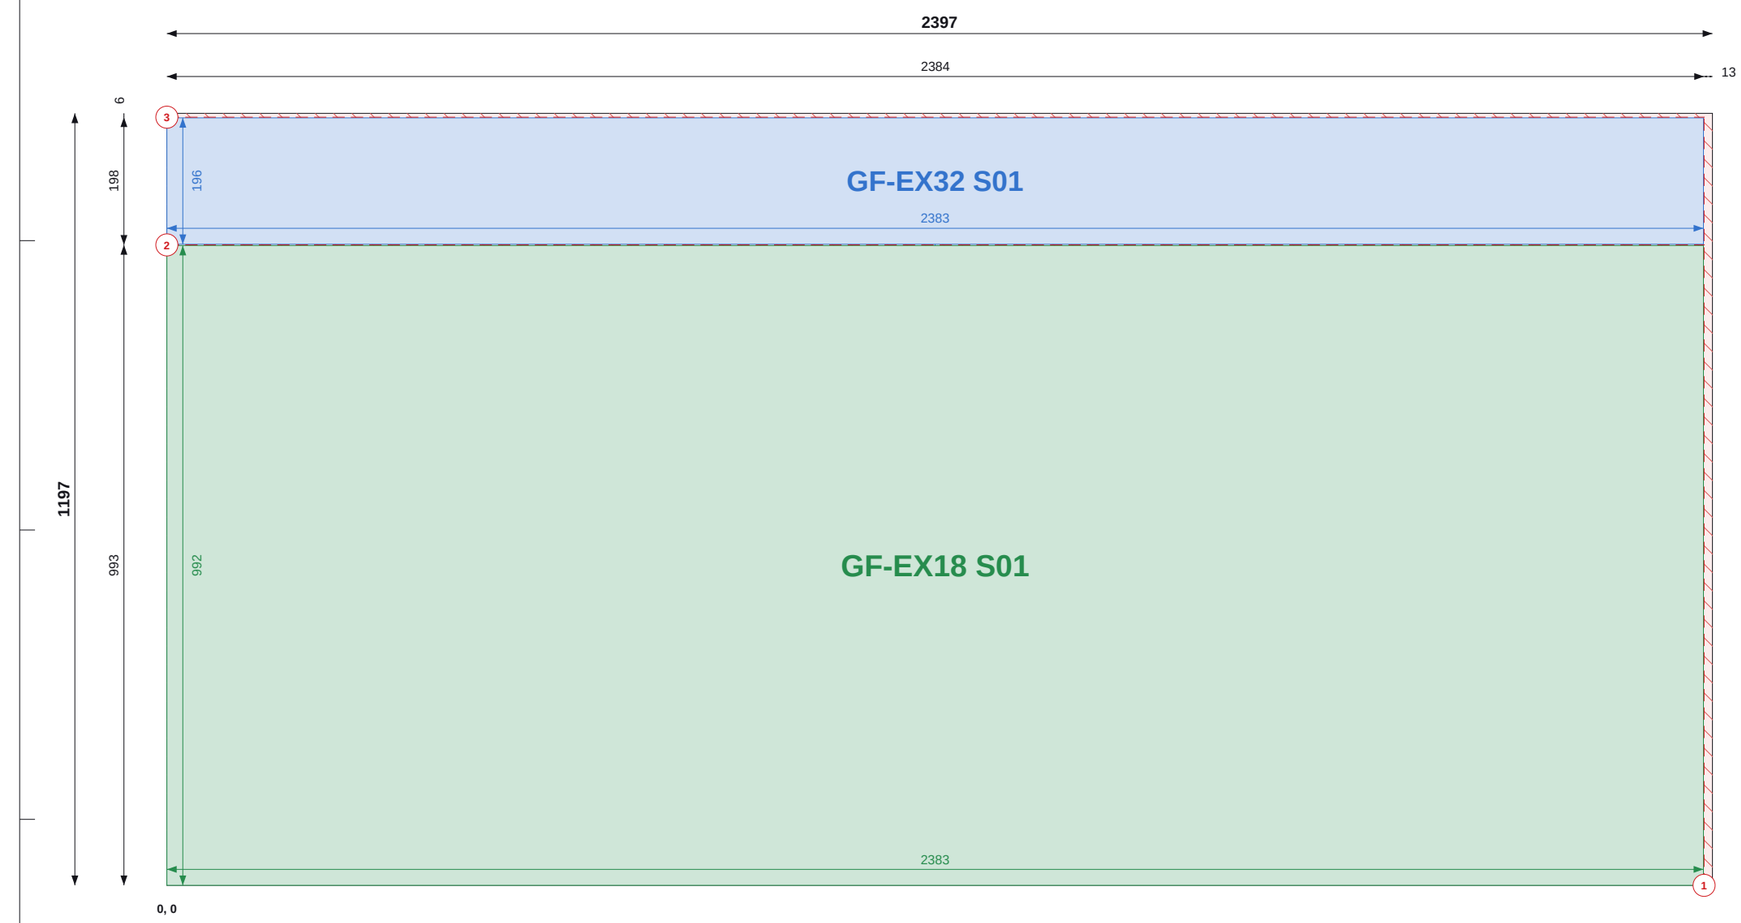


Top / left chains = saw cut positions (to cut centres). Coloured = part size and position.

## SHEET 19 OF 50

### THIS SHEET

| Item | Value |
|---|---|
| Parts | 2 |
| Used / waste | 98.7% / 0.04 m2 |
| Reusable offcuts | 0 |
| Saw cuts / shared | 3 / 1 |

### PIECES (POSITION = BOTTOM-LEFT CORNER)

| Label | Size | X, Y |
|---|---|---|
| GF-EX32 S01 | 196 x 2383 | 0, 994 |
| GF-EX18 S01 | 992 x 2383 | 0, 0 |

### NOTES

1. Cut from OSB/3 9mm 1197x2397, 2mm saw kerf. Viewed on the face; dimensions from the sheet's bottom-left corner (0,0). Red numbered lines = saw cuts in order, each edge to edge.
2. Coloured dimensions belong to the part of that colour: its width and height, and its position from the sheet edges. Raked parts: corner coordinates at each corner.
3. Red hatch = waste. Labels = panel + piece mark on the manufacture drawing.

### REVISIONS

| REV | DATE | DESCRIPTION |
|---|---|---|
| C01 | 14.09.26 | Construction issue |
| C02 | 14.09.26 | Roof trusses revised; SP diagonals added |
| C03 | 11.10.26 | FF windows coursed; steel + GP1 portal; steel drawings (ST) |
| C04 | 13.10.26 | Steel approved by the engineer: steel + steel timber drawings issued for construction |

TLS

TLS TIMBER FRAME

Design & Manufacture

Scan: 3D model + drawings

| CLIENT | PROJECT |
|---|---|
| MP Adams | MP Adams Plot 4, Eckington |

DRAWING TITLE


**OSB CUTTING - GROUND FLOOR - SHEET 19 OF 50**

OSB/3 9mm 1197x2397 | Ground Floor

| SCALE | SIZE | DATE | DRAWN |
|---|---|---|---|
| NTS | A3 | 13.10.26 | TS |

| STATUS | DRAWING No. | REV |
|---|---|---|
| CONSTRUCTION | P4-CP-OSB-01 / 19 | C04 |

Do not scale. All dimensions in mm. Check all dimensions on site.

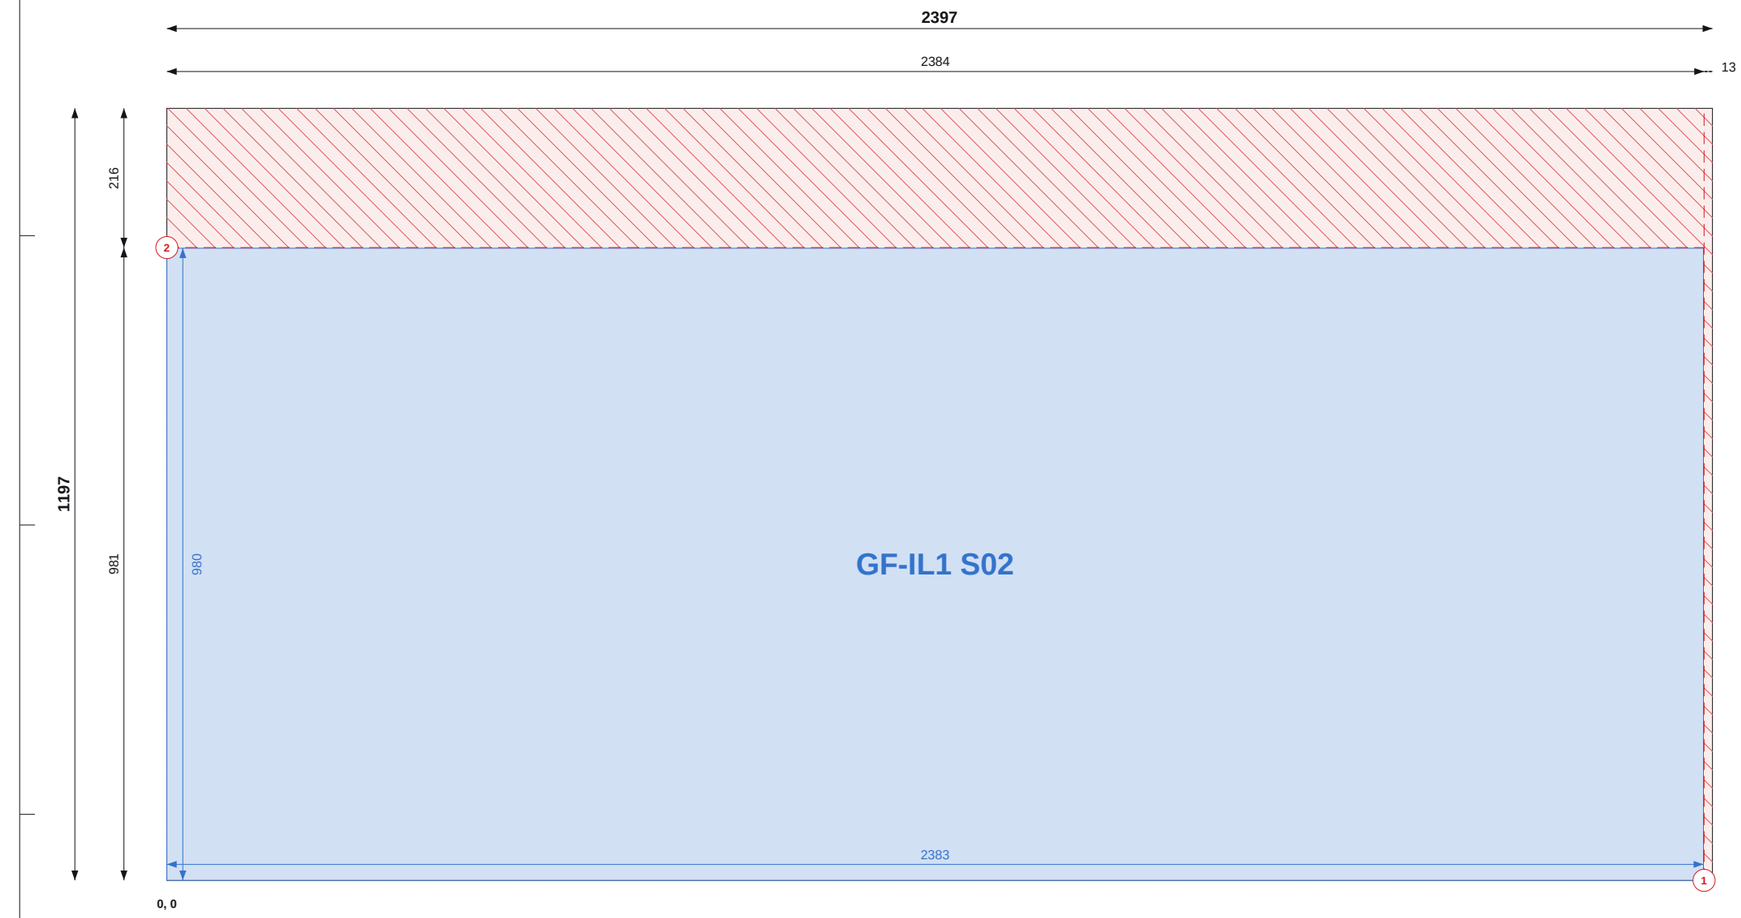


Top / left chains = saw cut positions (to cut centres). Coloured = part size and position.

## SHEET 20 OF 50

### THIS SHEET

| Item | Value |
|---|---|
| Parts | 1 |
| Used / waste | 81.4% / 0.53 m2 |
| Reusable offcuts | 0 |
| Saw cuts / shared | 2 / 0 |

### PIECES (POSITION = BOTTOM-LEFT CORNER)

| Label | Size | X, Y |
|---|---|---|
| GF-IL1 S02 | 980 x 2383 | 0, 0 |

### NOTES

1. Cut from OSB/3 9mm 1197x2397, 2mm saw kerf. Viewed on the face; dimensions from the sheet's bottom-left corner (0,0). Red numbered lines = saw cuts in order, each edge to edge.
2. Coloured dimensions belong to the part of that colour: its width and height, and its position from the sheet edges. Raked parts: corner coordinates at each corner.
3. Red hatch = waste. Labels = panel + piece mark on the manufacture drawing.

### REVISIONS

| REV | DATE | DESCRIPTION |
|---|---|---|
| C01 | 14.09.26 | Construction issue |
| C02 | 14.09.26 | Roof trusses revised; SP diagonals added |
| C03 | 11.10.26 | FF windows coursed; steel + GP1 portal; steel drawings (ST) |
| C04 | 13.10.26 | Steel approved by the engineer: steel + steel timber drawings issued for construction |

TLS TIMBER FRAME
Design & Manufacture
Scan: 3D model + drawings

| CLIENT | PROJECT |
|---|---|
| MP Adams | MP Adams Plot 4, Eckington |

DRAWING TITLE


**OSB CUTTING - GROUND FLOOR - SHEET 20 OF 50**

OSB/3 9mm 1197x2397 | Ground Floor

| SCALE | SIZE | DATE | DRAWN |
|---|---|---|---|
| NTS | A3 | 13.10.26 | TS |

| STATUS | DRAWING No. | REV |
|---|---|---|
| CONSTRUCTION | P4-CP-OSB-01 / 20 | C04 |

Do not scale. All dimensions in mm. Check all dimensions on site.

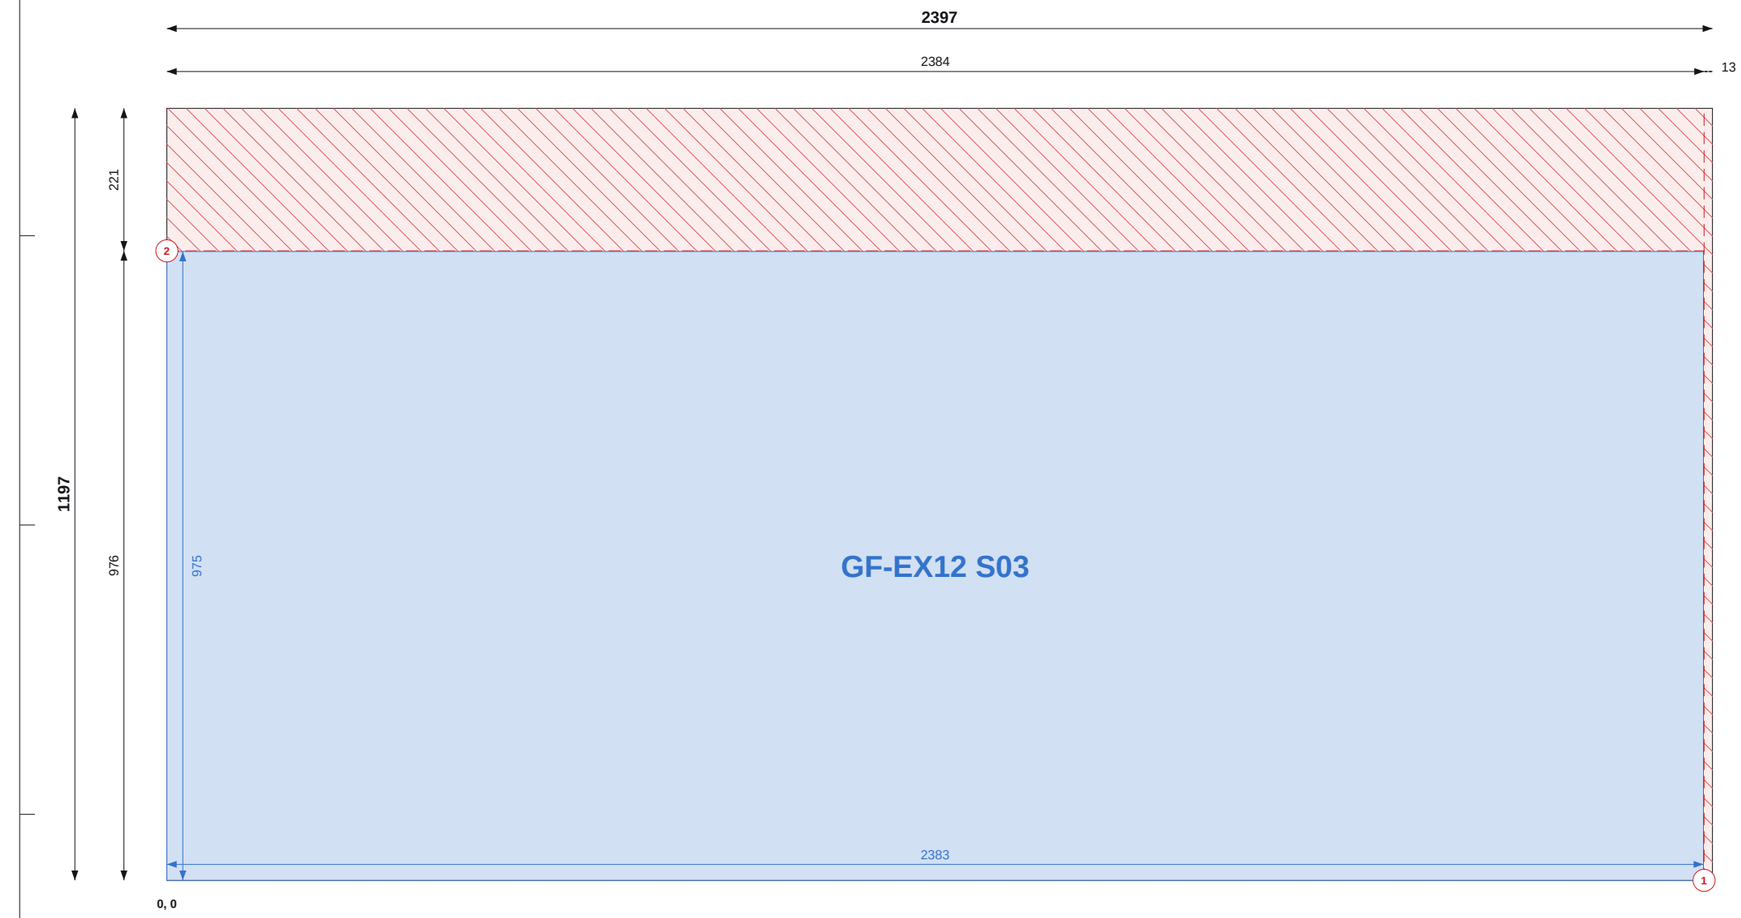


Top / left chains = saw cut positions (to cut centres). Coloured = part size and position.

## SHEET 21 OF 50

### THIS SHEET

| Item | Value |
|---|---|
| Parts | 1 |
| Used / waste | 81.0% / 0.55 m2 |
| Reusable offcuts | 0 |
| Saw cuts / shared | 2 / 0 |

### PIECES (POSITION = BOTTOM-LEFT CORNER)

| Label | Size | X, Y |
|---|---|---|
| GF-EX12 S03 | 975 x 2383 | 0, 0 |

### NOTES

1. Cut from OSB/3 9mm 1197x2397, 2mm saw kerf. Viewed on the face; dimensions from the sheet's bottom-left corner (0,0). Red numbered lines = saw cuts in order, each edge to edge.
2. Coloured dimensions belong to the part of that colour: its width and height, and its position from the sheet edges. Raked parts: corner coordinates at each corner.
3. Red hatch = waste. Labels = panel + piece mark on the manufacture drawing.

### REVISIONS

| REV | DATE | DESCRIPTION |
|---|---|---|
| C01 | 14.09.26 | Construction issue |
| C02 | 14.09.26 | Roof trusses revised; SP diagonals added |
| C03 | 11.10.26 | FF windows coursed; steel + GP1 portal; steel drawings (ST) |
| C04 | 13.10.26 | Steel approved by the engineer: steel + steel timber drawings issued for construction |

TLS TIMBER FRAME
Design & Manufacture
Scan: 3D model + drawings

| CLIENT | PROJECT |
|---|---|
| MP Adams | MP Adams Plot 4, Eckington |


DRAWING TITLE
**OSB CUTTING - GROUND FLOOR - SHEET 21 OF 50**

OSB/3 9mm 1197x2397 | Ground Floor

| SCALE | SIZE | DATE | DRAWN |
|---|---|---|---|
| NTS | A3 | 13.10.26 | TS |

| STATUS | DRAWING No. | REV |
|---|---|---|
| CONSTRUCTION | P4-CP-OSB-01 / 21 | C04 |

Do not scale. All dimensions in mm. Check all dimensions on site.

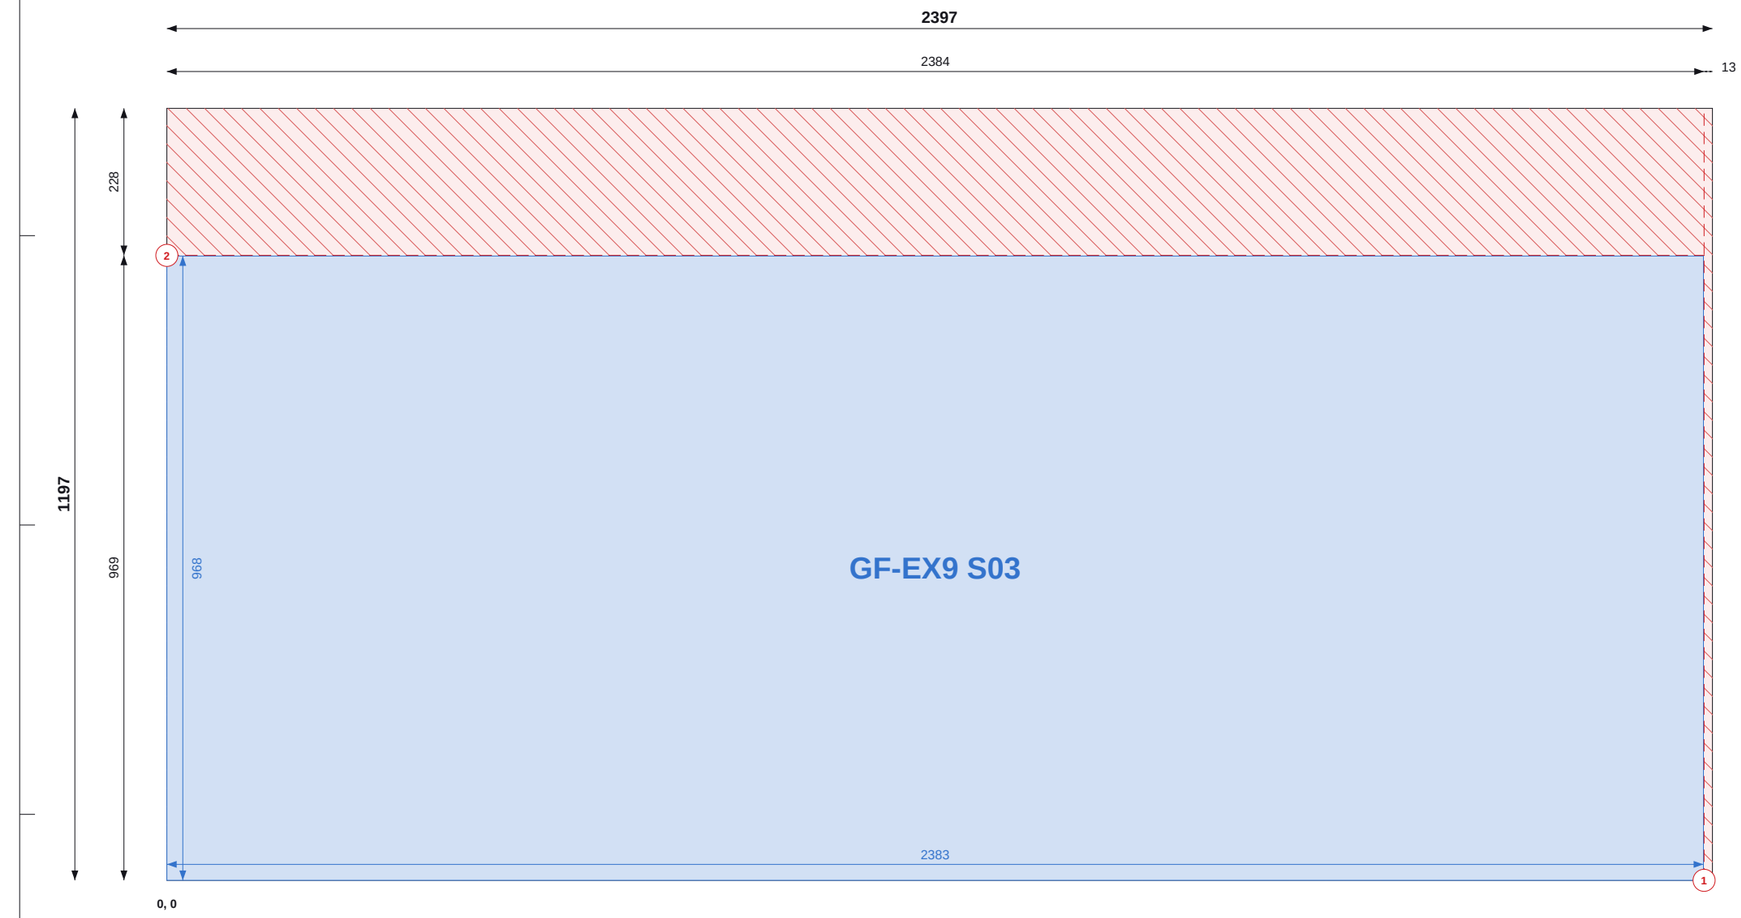


Top / left chains = saw cut positions (to cut centres). Coloured = part size and position.

## SHEET 22 OF 50

### THIS SHEET

| Item | Value |
|---|---|
| Parts | 1 |
| Used / waste | 80.4% / 0.56 m2 |
| Reusable offcuts | 0 |
| Saw cuts / shared | 2 / 0 |

### PIECES (POSITION = BOTTOM-LEFT CORNER)

| Label | Size | X, Y |
|---|---|---|
| GF-EX9 S03 | 968 x 2383 | 0, 0 |

### NOTES

1. Cut from OSB/3 9mm 1197x2397, 2mm saw kerf. Viewed on the face; dimensions from the sheet's bottom-left corner (0,0). Red numbered lines = saw cuts in order, each edge to edge.
2. Coloured dimensions belong to the part of that colour: its width and height, and its position from the sheet edges. Raked parts: corner coordinates at each corner.
3. Red hatch = waste. Labels = panel + piece mark on the manufacture drawing.

### REVISIONS

| REV | DATE | DESCRIPTION |
|---|---|---|
| C01 | 14.09.26 | Construction issue |
| C02 | 14.09.26 | Roof trusses revised; SP diagonals added |
| C03 | 11.10.26 | FF windows coursed; steel + GP1 portal; steel drawings (ST) |
| C04 | 13.10.26 | Steel approved by the engineer: steel + steel timber drawings issued for construction |

TLS

TLS TIMBER FRAME

Design & Manufacture

Scan: 3D model + drawings

| CLIENT | PROJECT |
|---|---|
| MP Adams | MP Adams Plot 4, Eckington |

DRAWING TITLE


**OSB CUTTING - GROUND FLOOR - SHEET 22 OF 50**

OSB/3 9mm 1197x2397 | Ground Floor

| SCALE | SIZE | DATE | DRAWN |
|---|---|---|---|
| NTS | A3 | 13.10.26 | TS |

| STATUS | DRAWING No. | REV |
|---|---|---|
| CONSTRUCTION | P4-CP-OSB-01 / 22 | C04 |

Do not scale. All dimensions in mm. Check all dimensions on site.

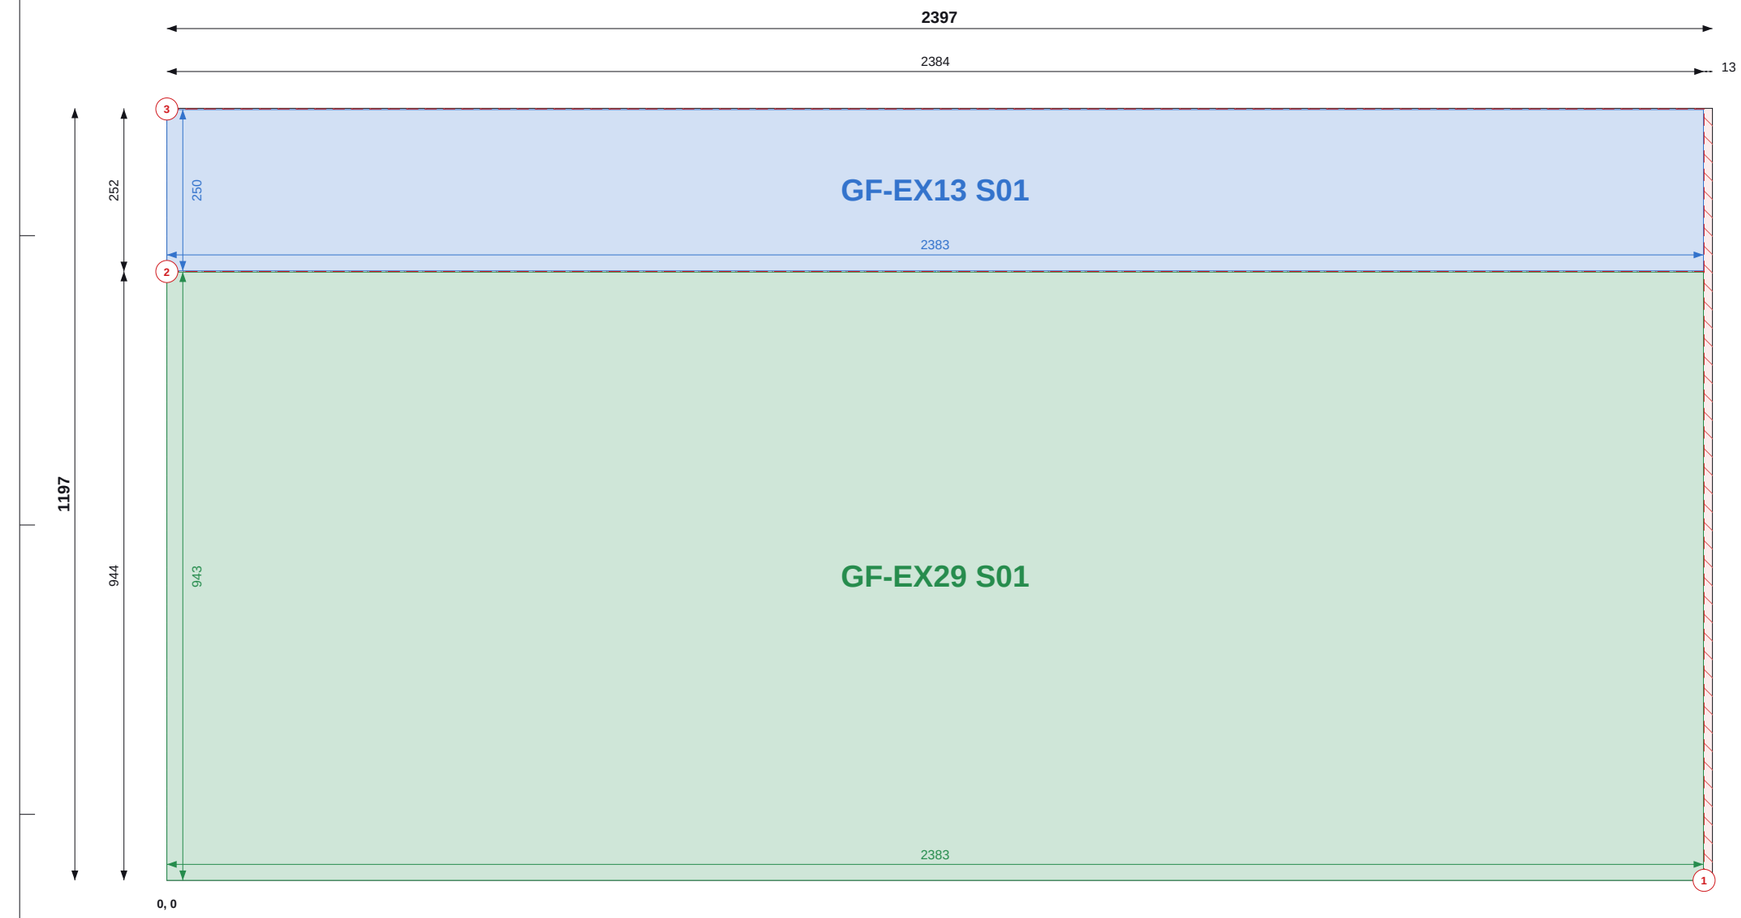


Top / left chains = saw cut positions (to cut centres). Coloured = part size and position.

## SHEET 23 OF 50

### THIS SHEET

| Item | Value |
|---|---|
| Parts | 2 |
| Used / waste | 99.1% / 0.03 m2 |
| Reusable offcuts | 0 |
| Saw cuts / shared | 3 / 1 |

### PIECES (POSITION = BOTTOM-LEFT CORNER)

| Label | Size | X, Y |
|---|---|---|
| GF-EX13 S01 | 250 x 2383 | 0, 945 |
| GF-EX29 S01 | 943 x 2383 | 0, 0 |

### NOTES

1. Cut from OSB/3 9mm 1197x2397, 2mm saw kerf. Viewed on the face; dimensions from the sheet's bottom-left corner (0,0). Red numbered lines = saw cuts in order, each edge to edge.
2. Coloured dimensions belong to the part of that colour: its width and height, and its position from the sheet edges. Raked parts: corner coordinates at each corner.
3. Red hatch = waste. Labels = panel + piece mark on the manufacture drawing.

### REVISIONS

| REV | DATE | DESCRIPTION |
|---|---|---|
| C01 | 14.09.26 | Construction issue |
| C02 | 14.09.26 | Roof trusses revised; SP diagonals added |
| C03 | 11.10.26 | FF windows coursed; steel + GP1 portal; steel drawings (ST) |
| C04 | 13.10.26 | Steel approved by the engineer: steel + steel timber drawings issued for construction |

TLS

TLS TIMBER FRAME

Design & Manufacture

Scan: 3D model + drawings

| CLIENT | PROJECT |
|---|---|
| MP Adams | MP Adams Plot 4, Eckington |

DRAWING TITLE


**OSB CUTTING - GROUND FLOOR - SHEET 23 OF 50**

OSB/3 9mm 1197x2397 | Ground Floor

| SCALE | SIZE | DATE | DRAWN |
|---|---|---|---|
| NTS | A3 | 13.10.26 | TS |

| STATUS | DRAWING No. | REV |
|---|---|---|
| CONSTRUCTION | P4-CP-OSB-01 / 23 | C04 |

Do not scale. All dimensions in mm. Check all dimensions on site.

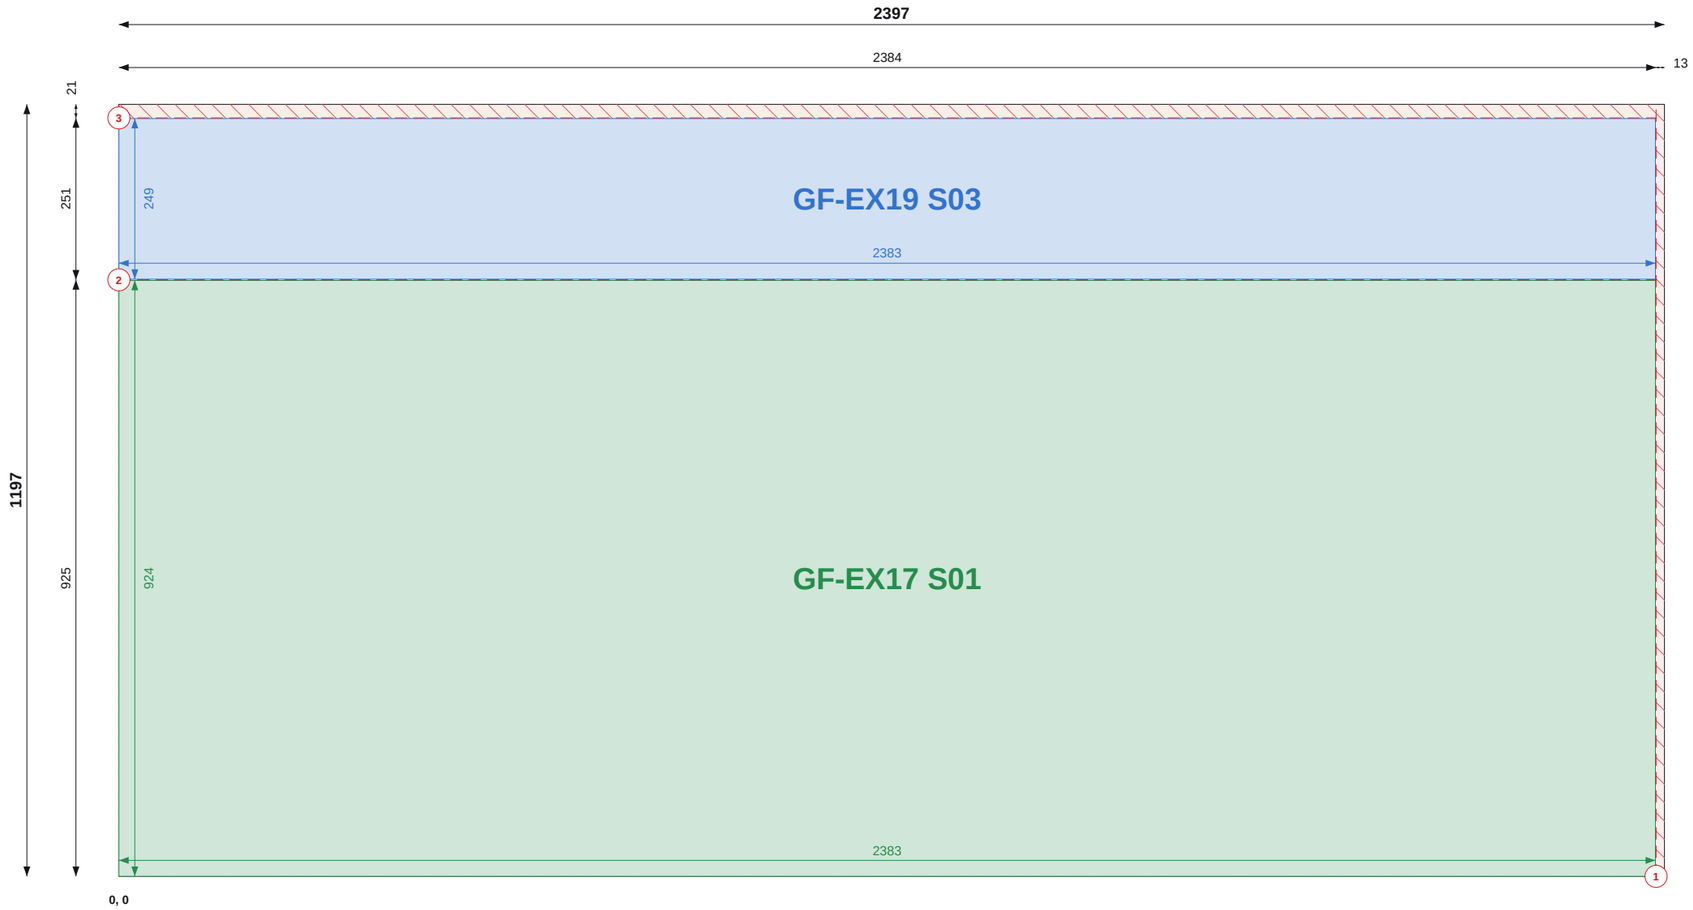


Top / left chains = saw cut positions (to cut centres). Coloured = part size and position.

## SHEET 24 OF 50

### THIS SHEET

| Item | Value |
|---|---|
| Parts | 2 |
| Used / waste | 97.4% / 0.07 m2 |
| Reusable offcuts | 0 |
| Saw cuts / shared | 3 / 1 |

### PIECES (POSITION = BOTTOM-LEFT CORNER)

| Label | Size | X, Y |
|---|---|---|
| GF-EX19 S03 | 249 x 2383 | 0, 926 |
| GF-EX17 S01 | 924 x 2383 | 0, 0 |

### NOTES

1. Cut from OSB/3 9mm 1197x2397, 2mm saw kerf. Viewed on the face; dimensions from the sheet's bottom-left corner (0,0). Red numbered lines = saw cuts in order, each edge to edge.
2. Coloured dimensions belong to the part of that colour: its width and height, and its position from the sheet edges. Raked parts: corner coordinates at each corner.
3. Red hatch = waste. Labels = panel + piece mark on the manufacture drawing.

### REVISIONS

| REV | DATE | DESCRIPTION |
|---|---|---|
| C01 | 14.09.26 | Construction issue |
| C02 | 14.09.26 | Roof trusses revised; SP diagonals added |
| C03 | 11.10.26 | FF windows coursed; steel + GP1 portal; steel drawings (ST) |
| C04 | 13.10.26 | Steel approved by the engineer: steel + steel timber drawings issued for construction |

TLS

TLS TIMBER FRAME

Design & Manufacture

Scan: 3D model + drawings

| CLIENT | PROJECT |
|---|---|
| MP Adams | MP Adams Plot 4, Eckington |

DRAWING TITLE


**OSB CUTTING - GROUND FLOOR - SHEET 24 OF 50**

OSB/3 9mm 1197x2397 | Ground Floor

| SCALE | SIZE | DATE | DRAWN |
|---|---|---|---|
| NTS | A3 | 13.10.26 | TS |

| STATUS | DRAWING No. | REV |
|---|---|---|
| CONSTRUCTION | P4-CP-OSB-01 / 24 | C04 |

Do not scale. All dimensions in mm. Check all dimensions on site.

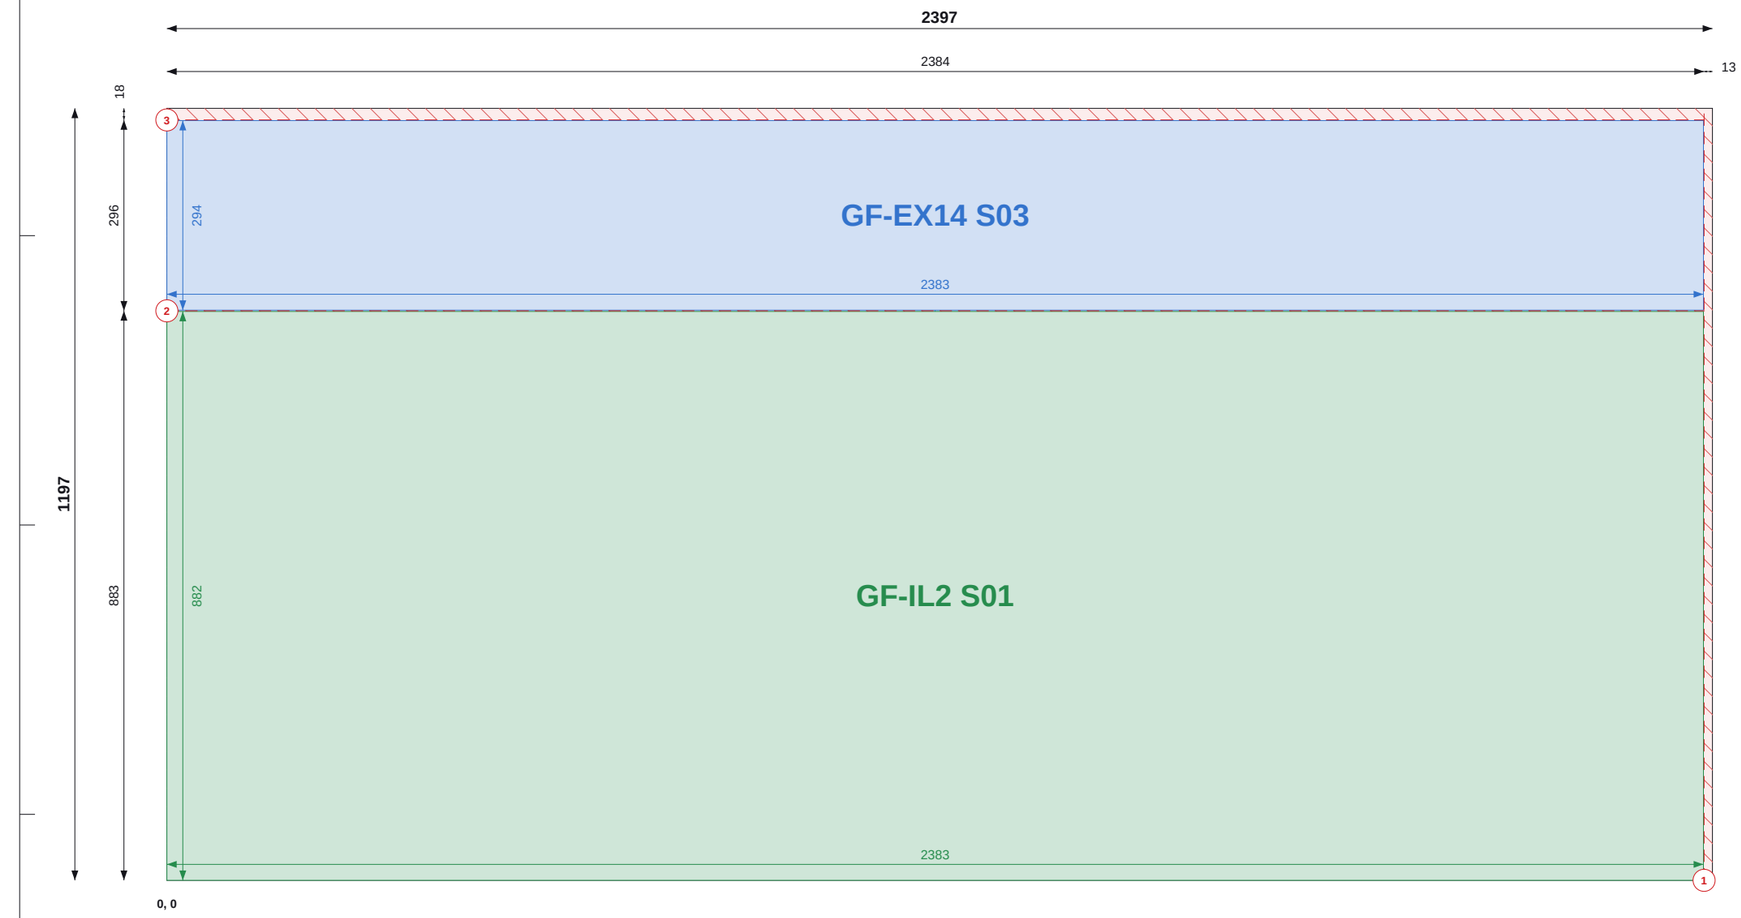


Top / left chains = saw cut positions (to cut centres). Coloured = part size and position.

## SHEET 25 OF 50

### THIS SHEET

| Item | Value |
|---|---|
| Parts | 2 |
| Used / waste | 97.7% / 0.07 m2 |
| Reusable offcuts | 0 |
| Saw cuts / shared | 3 / 1 |

### PIECES (POSITION = BOTTOM-LEFT CORNER)

| Label | Size | X, Y |
|---|---|---|
| GF-EX14 S03 | 294 x 2383 | 0, 884 |
| GF-IL2 S01 | 882 x 2383 | 0, 0 |

### NOTES

1. Cut from OSB/3 9mm 1197x2397, 2mm saw kerf. Viewed on the face; dimensions from the sheet's bottom-left corner (0,0). Red numbered lines = saw cuts in order, each edge to edge.
2. Coloured dimensions belong to the part of that colour: its width and height, and its position from the sheet edges. Raked parts: corner coordinates at each corner.
3. Red hatch = waste. Labels = panel + piece mark on the manufacture drawing.

### REVISIONS

| REV | DATE | DESCRIPTION |
|---|---|---|
| C01 | 14.09.26 | Construction issue |
| C02 | 14.09.26 | Roof trusses revised; SP diagonals added |
| C03 | 11.10.26 | FF windows coursed; steel + GP1 portal; steel drawings (ST) |
| C04 | 13.10.26 | Steel approved by the engineer: steel + steel timber drawings issued for construction |

TLS

TLS TIMBER FRAME

Design & Manufacture

Scan: 3D model + drawings

| CLIENT | PROJECT |
|---|---|
| MP Adams | MP Adams Plot 4, Eckington |

DRAWING TITLE


**OSB CUTTING - GROUND FLOOR - SHEET 25 OF 50**

OSB/3 9mm 1197x2397 | Ground Floor

| SCALE | SIZE | DATE | DRAWN |
|---|---|---|---|
| NTS | A3 | 13.10.26 | TS |

| STATUS | DRAWING No. | REV |
|---|---|---|
| CONSTRUCTION | P4-CP-OSB-01 / 25 | C04 |

Do not scale. All dimensions in mm. Check all dimensions on site.

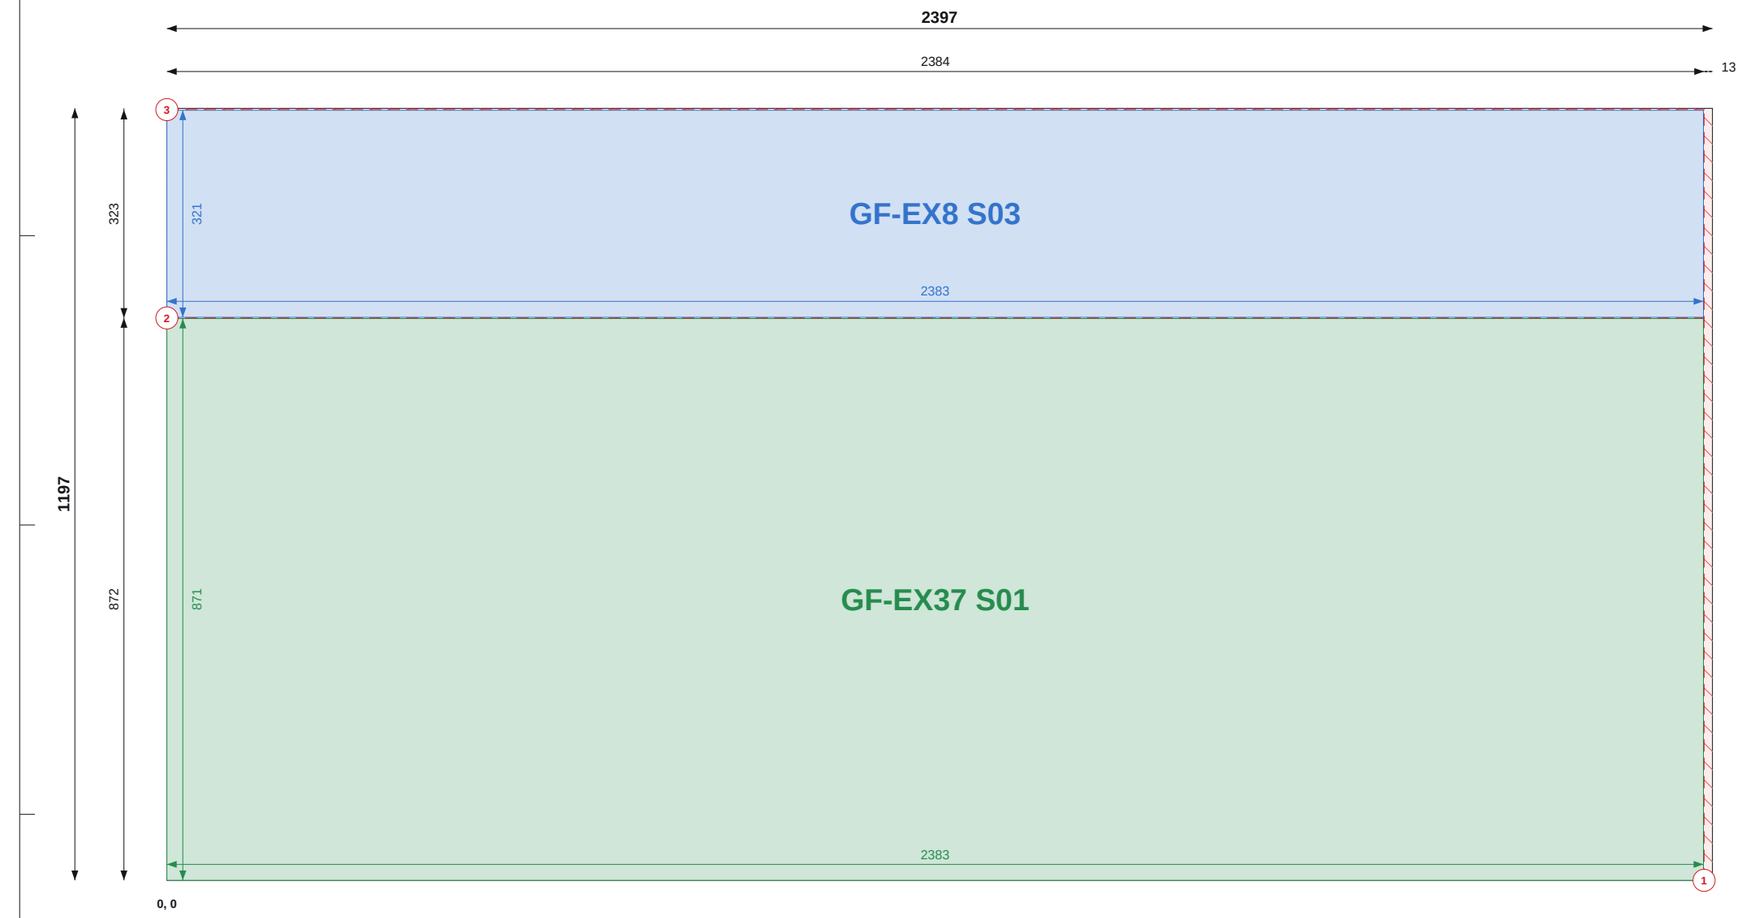


Top / left chains = saw cut positions (to cut centres). Coloured = part size and position.

## SHEET 26 OF 50

### THIS SHEET

| Item | Value |
|---|---|
| Parts | 2 |
| Used / waste | 99.0% / 0.03 m2 |
| Reusable offcuts | 0 |
| Saw cuts / shared | 3 / 1 |

### PIECES (POSITION = BOTTOM-LEFT CORNER)

| Label | Size | X, Y |
|---|---|---|
| GF-EX8 S03 | 321 x 2383 | 0, 873 |
| GF-EX37 S01 | 871 x 2383 | 0, 0 |

### NOTES

1. Cut from OSB/3 9mm 1197x2397, 2mm saw kerf. Viewed on the face; dimensions from the sheet's bottom-left corner (0,0). Red numbered lines = saw cuts in order, each edge to edge.
2. Coloured dimensions belong to the part of that colour: its width and height, and its position from the sheet edges. Raked parts: corner coordinates at each corner.
3. Red hatch = waste. Labels = panel + piece mark on the manufacture drawing.

### REVISIONS

| REV | DATE | DESCRIPTION |
|---|---|---|
| C01 | 14.09.26 | Construction issue |
| C02 | 14.09.26 | Roof trusses revised; SP diagonals added |
| C03 | 11.10.26 | FF windows coursed; steel + GP1 portal; steel drawings (ST) |
| C04 | 13.10.26 | Steel approved by the engineer: steel + steel timber drawings issued for construction |

TLS

TLS TIMBER FRAME

Design & Manufacture

Scan: 3D model + drawings

| CLIENT | PROJECT |
|---|---|
| MP Adams | MP Adams Plot 4, Eckington |

DRAWING TITLE


**OSB CUTTING - GROUND FLOOR - SHEET 26 OF 50**

OSB/3 9mm 1197x2397 | Ground Floor

| SCALE | SIZE | DATE | DRAWN |
|---|---|---|---|
| NTS | A3 | 13.10.26 | TS |

| STATUS | DRAWING No. | REV |
|---|---|---|
| CONSTRUCTION | P4-CP-OSB-01 / 26 | C04 |

Do not scale. All dimensions in mm. Check all dimensions on site.

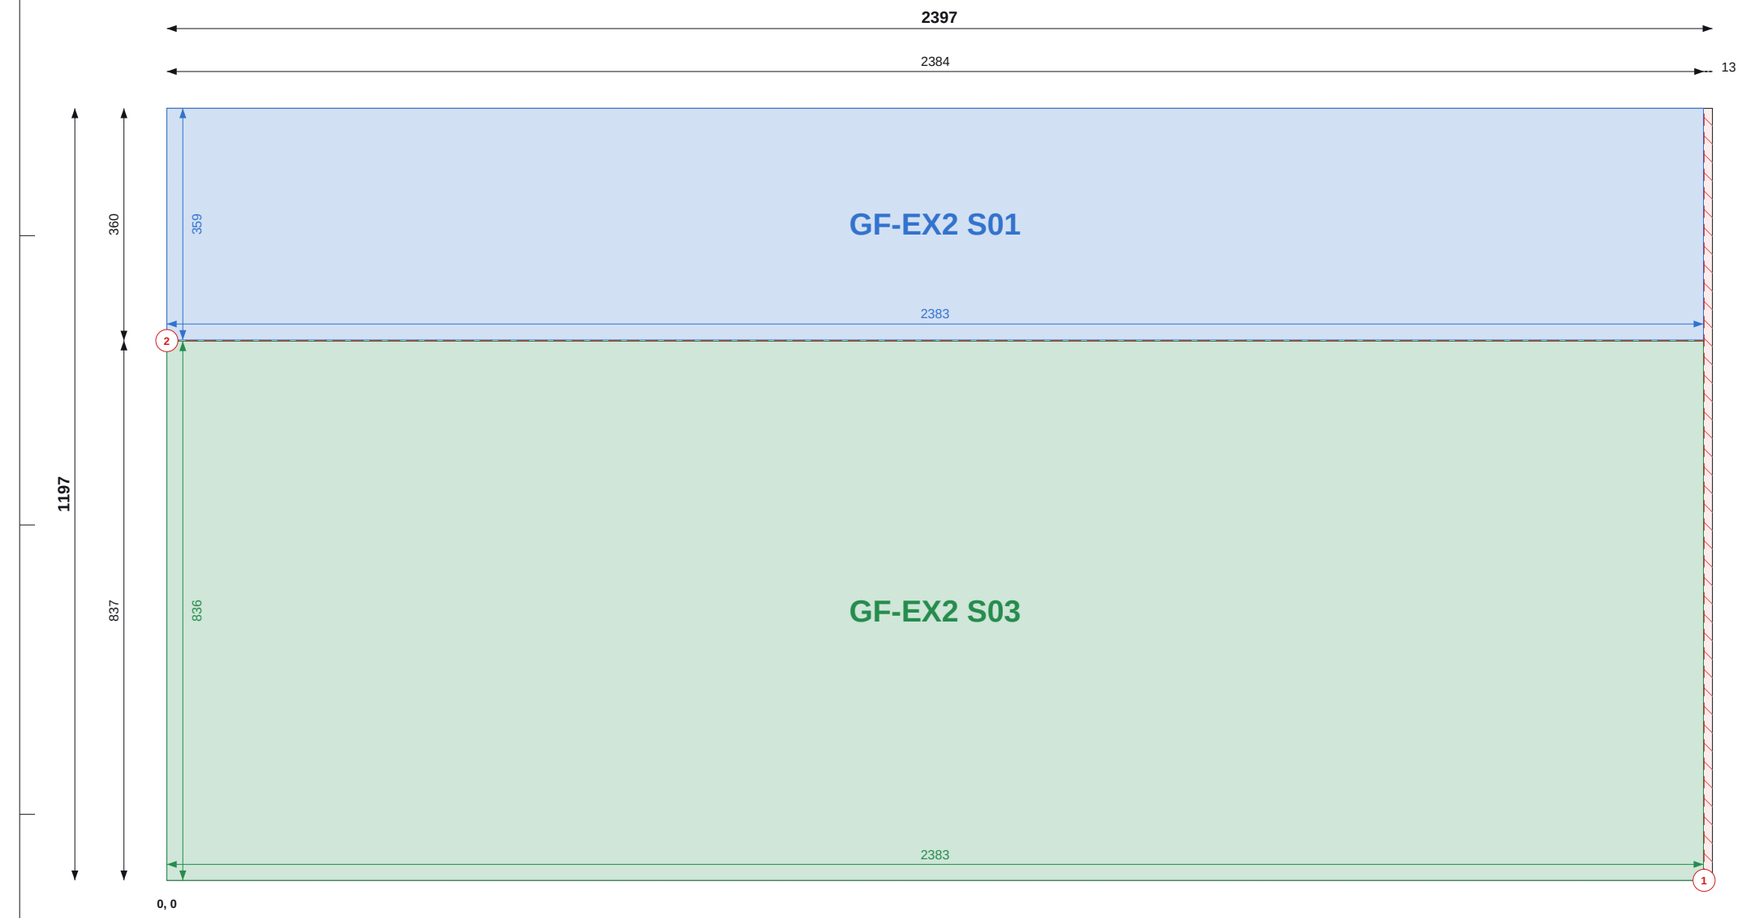


Top / left chains = saw cut positions (to cut centres). Coloured = part size and position.

## SHEET 27 OF 50

### THIS SHEET

| Item | Value |
|---|---|
| Parts | 2 |
| Used / waste | 99.2% / 0.02 m2 |
| Reusable offcuts | 0 |
| Saw cuts / shared | 2 / 1 |

### PIECES (POSITION = BOTTOM-LEFT CORNER)

| Label | Size | X, Y |
|---|---|---|
| GF-EX2 S01 | 359 x 2383 | 0, 838 |
| GF-EX2 S03 | 836 x 2383 | 0, 0 |

### NOTES

1. Cut from OSB/3 9mm 1197x2397, 2mm saw kerf. Viewed on the face; dimensions from the sheet's bottom-left corner (0,0). Red numbered lines = saw cuts in order, each edge to edge.
2. Coloured dimensions belong to the part of that colour: its width and height, and its position from the sheet edges. Raked parts: corner coordinates at each corner.
3. Red hatch = waste. Labels = panel + piece mark on the manufacture drawing.

### REVISIONS

| REV | DATE | DESCRIPTION |
|---|---|---|
| C01 | 14.09.26 | Construction issue |
| C02 | 14.09.26 | Roof trusses revised; SP diagonals added |
| C03 | 11.10.26 | FF windows coursed; steel + GP1 portal; steel drawings (ST) |
| C04 | 13.10.26 | Steel approved by the engineer: steel + steel timber drawings issued for construction |

TLS

TLS TIMBER FRAME

Design & Manufacture

Scan: 3D model + drawings

| CLIENT | PROJECT |
|---|---|
| MP Adams | MP Adams Plot 4, Eckington |

DRAWING TITLE


**OSB CUTTING - GROUND FLOOR - SHEET 27 OF 50**

OSB/3 9mm 1197x2397 | Ground Floor

| SCALE | SIZE | DATE | DRAWN |
|---|---|---|---|
| NTS | A3 | 13.10.26 | TS |

| STATUS | DRAWING No. | REV |
|---|---|---|
| CONSTRUCTION | P4-CP-OSB-01 / 27 | C04 |

Do not scale. All dimensions in mm. Check all dimensions on site.

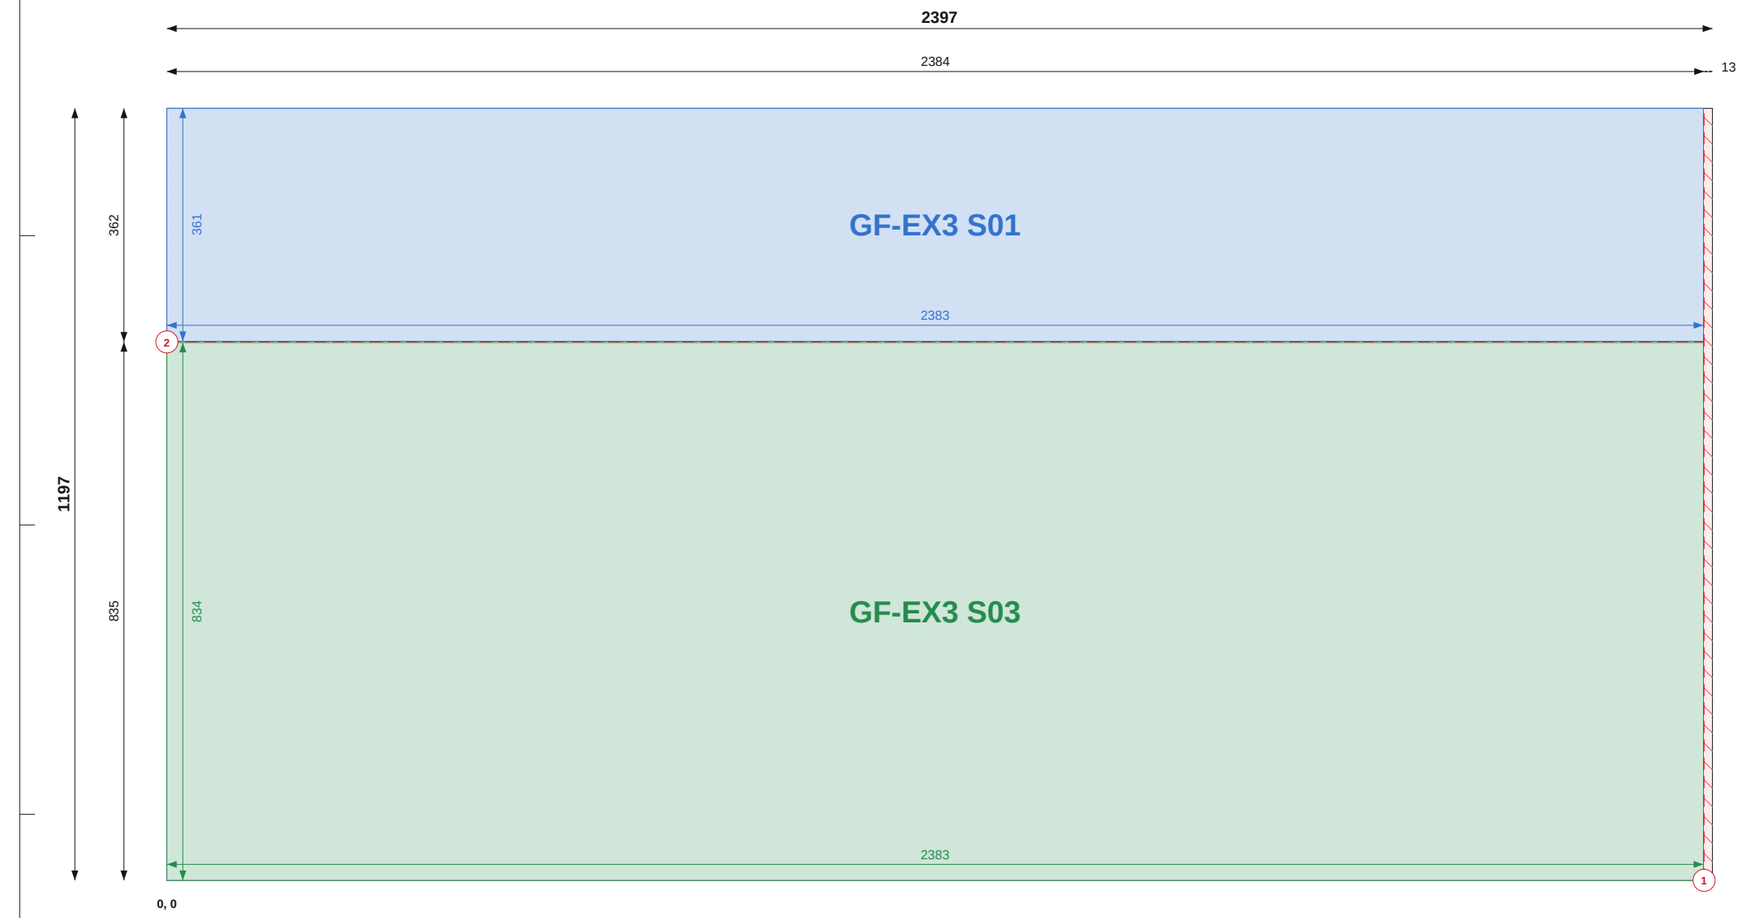


Top / left chains = saw cut positions (to cut centres). Coloured = part size and position.

## SHEET 28 OF 50

### THIS SHEET

| Item | Value |
|---|---|
| Parts | 2 |
| Used / waste | 99.2% / 0.02 m2 |
| Reusable offcuts | 0 |
| Saw cuts / shared | 2 / 1 |

### PIECES (POSITION = BOTTOM-LEFT CORNER)

| Label | Size | X, Y |
|---|---|---|
| GF-EX3 S01 | 361 x 2383 | 0, 836 |
| GF-EX3 S03 | 834 x 2383 | 0, 0 |

### NOTES

1. Cut from OSB/3 9mm 1197x2397, 2mm saw kerf. Viewed on the face; dimensions from the sheet's bottom-left corner (0,0). Red numbered lines = saw cuts in order, each edge to edge.
2. Coloured dimensions belong to the part of that colour: its width and height, and its position from the sheet edges. Raked parts: corner coordinates at each corner.
3. Red hatch = waste. Labels = panel + piece mark on the manufacture drawing.

### REVISIONS

| REV | DATE | DESCRIPTION |
|---|---|---|
| C01 | 14.09.26 | Construction issue |
| C02 | 14.09.26 | Roof trusses revised; SP diagonals added |
| C03 | 11.10.26 | FF windows coursed; steel + GP1 portal; steel drawings (ST) |
| C04 | 13.10.26 | Steel approved by the engineer: steel + steel timber drawings issued for construction |

TLS

TLS TIMBER FRAME

Design & Manufacture

Scan: 3D model + drawings

| CLIENT | PROJECT |
|---|---|
| MP Adams | MP Adams Plot 4, Eckington |

DRAWING TITLE


**OSB CUTTING - GROUND FLOOR - SHEET 28 OF 50**

OSB/3 9mm 1197x2397 | Ground Floor

| SCALE | SIZE | DATE | DRAWN |
|---|---|---|---|
| NTS | A3 | 13.10.26 | TS |

| STATUS | DRAWING No. | REV |
|---|---|---|
| CONSTRUCTION | P4-CP-OSB-01 / 28 | C04 |

Do not scale. All dimensions in mm. Check all dimensions on site.

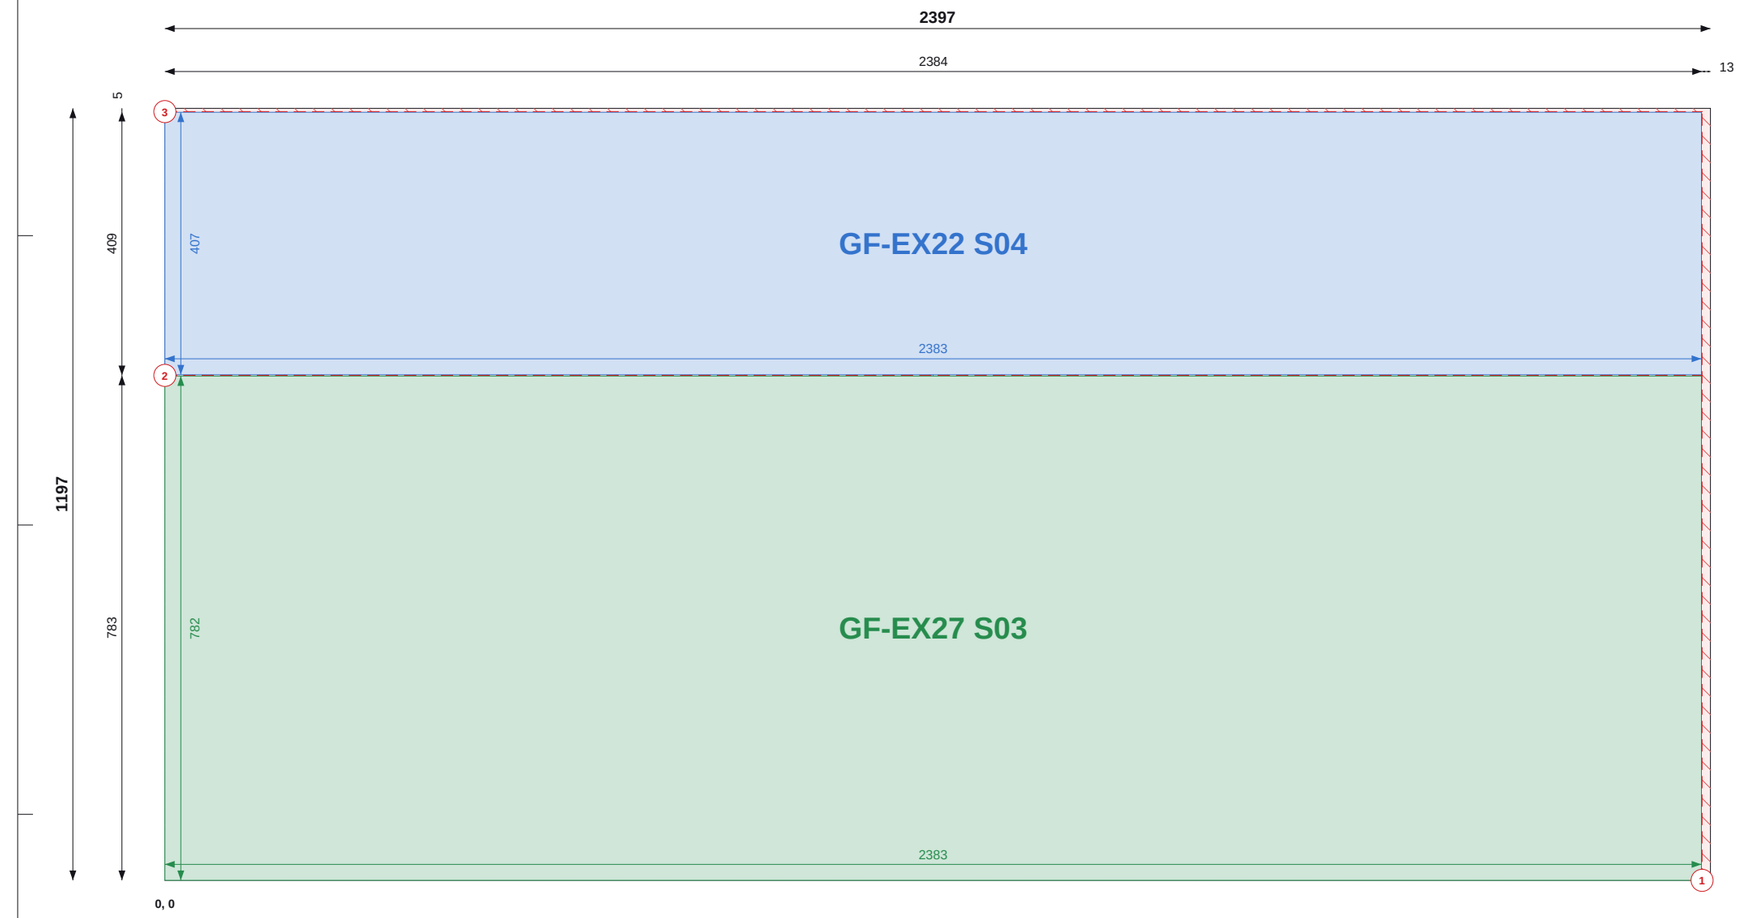


Top / left chains = saw cut positions (to cut centres). Coloured = part size and position.

## SHEET 29 OF 50

### THIS SHEET

| Item | Value |
|---|---|
| Parts | 2 |
| Used / waste | 98.7% / 0.04 m2 |
| Reusable offcuts | 0 |
| Saw cuts / shared | 3 / 1 |

### PIECES (POSITION = BOTTOM-LEFT CORNER)

| Label | Size | X, Y |
|---|---|---|
| GF-EX22 S04 | 407 x 2383 | 0, 784 |
| GF-EX27 S03 | 782 x 2383 | 0, 0 |

### NOTES

1. Cut from OSB/3 9mm 1197x2397, 2mm saw kerf. Viewed on the face; dimensions from the sheet's bottom-left corner (0,0). Red numbered lines = saw cuts in order, each edge to edge.
2. Coloured dimensions belong to the part of that colour: its width and height, and its position from the sheet edges. Raked parts: corner coordinates at each corner.
3. Red hatch = waste. Labels = panel + piece mark on the manufacture drawing.

### REVISIONS

| REV | DATE | DESCRIPTION |
|---|---|---|
| C01 | 14.09.26 | Construction issue |
| C02 | 14.09.26 | Roof trusses revised; SP diagonals added |
| C03 | 11.10.26 | FF windows coursed; steel + GP1 portal; steel drawings (ST) |
| C04 | 13.10.26 | Steel approved by the engineer: steel + steel timber drawings issued for construction |

TLS

TLS TIMBER FRAME

Design & Manufacture

Scan: 3D model + drawings

| CLIENT | PROJECT |
|---|---|
| MP Adams | MP Adams Plot 4, Eckington |

DRAWING TITLE

**OSB CUTTING - GROUND FLOOR - SHEET 29 OF 50**

OSB/3 9mm 1197x2397 | Ground Floor

| SCALE | SIZE | DATE | DRAWN |
|---|---|---|---|
| NTS | A3 | 13.10.26 | TS |

| STATUS | DRAWING No. | REV |
|---|---|---|
| CONSTRUCTION | P4-CP-OSB-01 / 29 | C04 |

Do not scale. All dimensions in mm. Check all dimensions on site.




Top / left chains = saw cut positions (to cut centres). Coloured = part size and position.

## SHEET 30 OF 50

### THIS SHEET

| Item | Value |
|---|---|
| Parts | 2 |
| Used / waste | 98.4% / 0.05 m2 |
| Reusable offcuts | 0 |
| Saw cuts / shared | 3 / 1 |

### PIECES (POSITION = BOTTOM-LEFT CORNER)

| Label | Size | X, Y |
|---|---|---|
| GF-EX34 S01 | 432 x 2383 | 0, 755 |
| GF-EX31 S01 | 753 x 2383 | 0, 0 |

### NOTES

1. Cut from OSB/3 9mm 1197x2397, 2mm saw kerf. Viewed on the face; dimensions from the sheet's bottom-left corner (0,0). Red numbered lines = saw cuts in order, each edge to edge.
2. Coloured dimensions belong to the part of that colour: its width and height, and its position from the sheet edges. Raked parts: corner coordinates at each corner.
3. Red hatch = waste. Labels = panel + piece mark on the manufacture drawing.

### REVISIONS

| REV | DATE | DESCRIPTION |
|---|---|---|
| C01 | 14.09.26 | Construction issue |
| C02 | 14.09.26 | Roof trusses revised; SP diagonals added |
| C03 | 11.10.26 | FF windows coursed; steel + GP1 portal; steel drawings (ST) |
| C04 | 13.10.26 | Steel approved by the engineer: steel + steel timber drawings issued for construction |

TLS

TLS TIMBER FRAME

Design & Manufacture

Scan: 3D model + drawings

| CLIENT | PROJECT |
|---|---|
| MP Adams | MP Adams Plot 4, Eckington |

DRAWING TITLE


**OSB CUTTING - GROUND FLOOR - SHEET 30 OF 50**

OSB/3 9mm 1197x2397 | Ground Floor

| SCALE | SIZE | DATE | DRAWN |
|---|---|---|---|
| NTS | A3 | 13.10.26 | TS |

| STATUS | DRAWING No. | REV |
|---|---|---|
| CONSTRUCTION | P4-CP-OSB-01 / 30 | C04 |

Do not scale. All dimensions in mm. Check all dimensions on site.

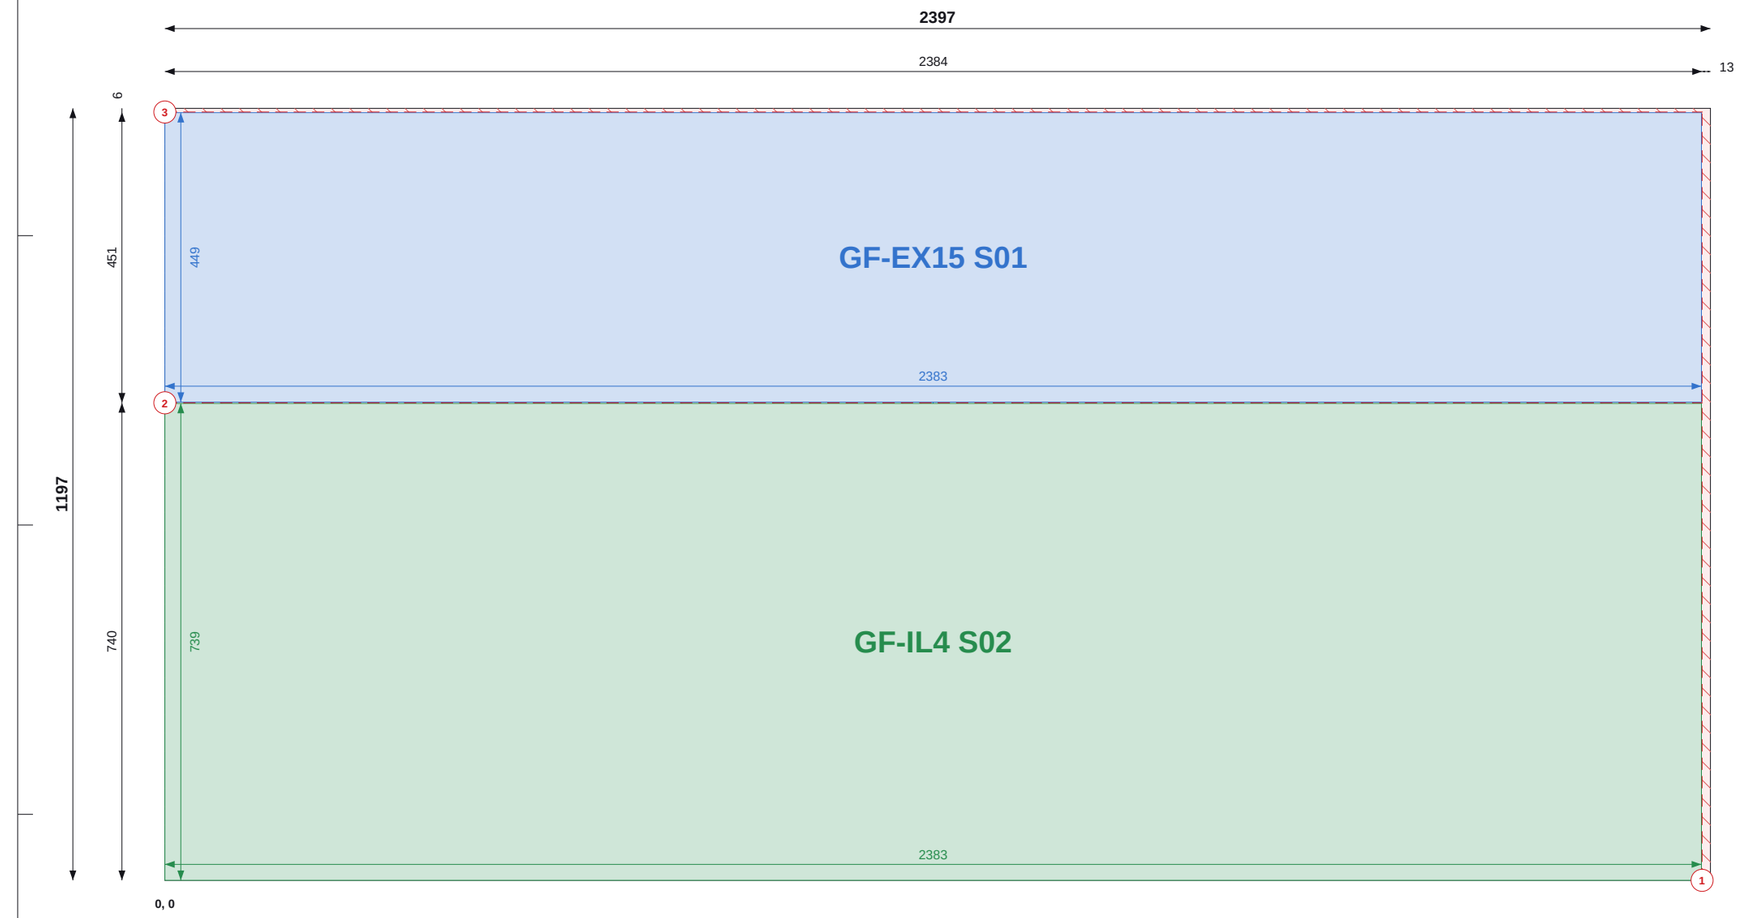


Top / left chains = saw cut positions (to cut centres). Coloured = part size and position.

## SHEET 31 OF 50

### THIS SHEET

| Item | Value |
|---|---|
| Parts | 2 |
| Used / waste | 98.7% / 0.04 m2 |
| Reusable offcuts | 0 |
| Saw cuts / shared | 3 / 1 |

### PIECES (POSITION = BOTTOM-LEFT CORNER)

| Label | Size | X, Y |
|---|---|---|
| GF-EX15 S01 | 449 x 2383 | 0, 741 |
| GF-IL4 S02 | 739 x 2383 | 0, 0 |

### NOTES

1. Cut from OSB/3 9mm 1197x2397, 2mm saw kerf. Viewed on the face; dimensions from the sheet's bottom-left corner (0,0). Red numbered lines = saw cuts in order, each edge to edge.
2. Coloured dimensions belong to the part of that colour: its width and height, and its position from the sheet edges. Raked parts: corner coordinates at each corner.
3. Red hatch = waste. Labels = panel + piece mark on the manufacture drawing.

### REVISIONS

| REV | DATE | DESCRIPTION |
|---|---|---|
| C01 | 14.09.26 | Construction issue |
| C02 | 14.09.26 | Roof trusses revised; SP diagonals added |
| C03 | 11.10.26 | FF windows coursed; steel + GP1 portal; steel drawings (ST) |
| C04 | 13.10.26 | Steel approved by the engineer: steel + steel timber drawings issued for construction |

TLS

TLS TIMBER FRAME

Design & Manufacture

Scan: 3D model + drawings

| CLIENT | PROJECT |
|---|---|
| MP Adams | MP Adams Plot 4, Eckington |

DRAWING TITLE


**OSB CUTTING - GROUND FLOOR - SHEET 31 OF 50**

OSB/3 9mm 1197x2397 | Ground Floor

| SCALE | SIZE | DATE | DRAWN |
|---|---|---|---|
| NTS | A3 | 13.10.26 | TS |

| STATUS | DRAWING No. | REV |
|---|---|---|
| CONSTRUCTION | P4-CP-OSB-01 / 31 | C04 |

Do not scale. All dimensions in mm. Check all dimensions on site.

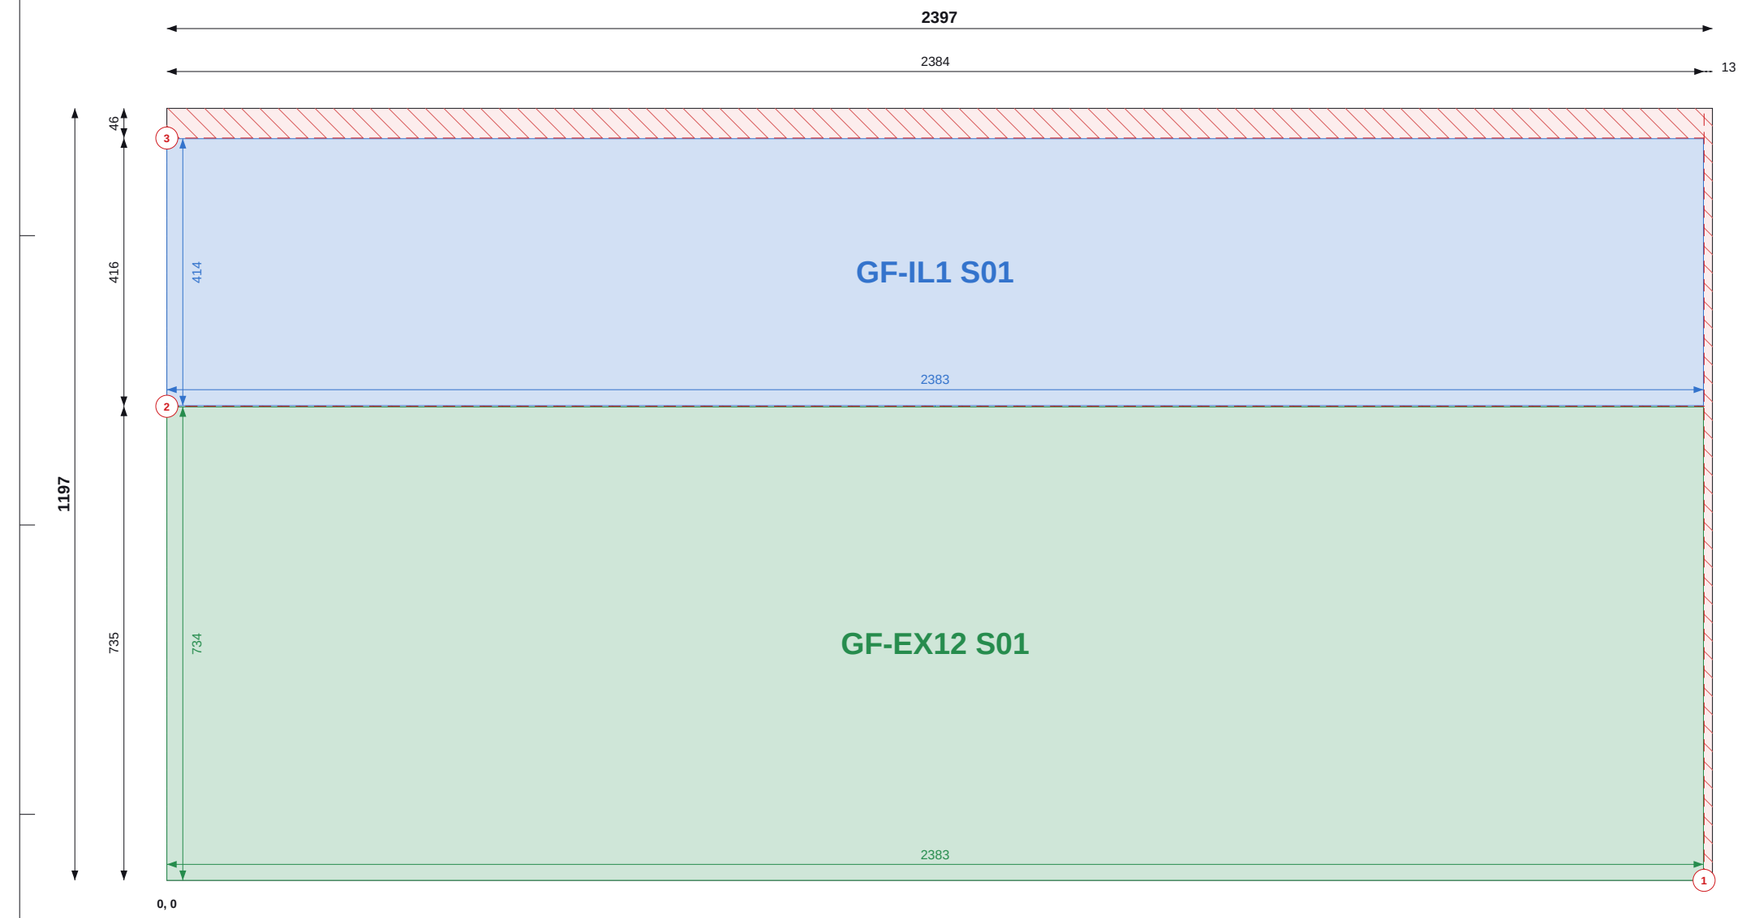


Top / left chains = saw cut positions (to cut centres). Coloured = part size and position.

## SHEET 32 OF 50

### THIS SHEET

| Item | Value |
|---|---|
| Parts | 2 |
| Used / waste | 95.3% / 0.13 m2 |
| Reusable offcuts | 0 |
| Saw cuts / shared | 3 / 1 |

### PIECES (POSITION = BOTTOM-LEFT CORNER)

| Label | Size | X, Y |
|---|---|---|
| GF-IL1 S01 | 414 x 2383 | 0, 736 |
| GF-EX12 S01 | 734 x 2383 | 0, 0 |

### NOTES

1. Cut from OSB/3 9mm 1197x2397, 2mm saw kerf. Viewed on the face; dimensions from the sheet's bottom-left corner (0,0). Red numbered lines = saw cuts in order, each edge to edge.
2. Coloured dimensions belong to the part of that colour: its width and height, and its position from the sheet edges. Raked parts: corner coordinates at each corner.
3. Red hatch = waste. Labels = panel + piece mark on the manufacture drawing.

### REVISIONS

| REV | DATE | DESCRIPTION |
|---|---|---|
| C01 | 14.09.26 | Construction issue |
| C02 | 14.09.26 | Roof trusses revised; SP diagonals added |
| C03 | 11.10.26 | FF windows coursed; steel + GP1 portal; steel drawings (ST) |
| C04 | 13.10.26 | Steel approved by the engineer: steel + steel timber drawings issued for construction |

TLS

TLS TIMBER FRAME
Design & Manufacture
Scan: 3D model + drawings

| CLIENT | PROJECT |
|---|---|
| MP Adams | MP Adams Plot 4, Eckington |

DRAWING TITLE

**OSB CUTTING - GROUND FLOOR - SHEET 32 OF 50**

OSB/3 9mm 1197x2397 | Ground Floor

| SCALE | SIZE | DATE | DRAWN |
|---|---|---|---|
| NTS | A3 | 13.10.26 | TS |

| STATUS | DRAWING No. | REV |
|---|---|---|
| CONSTRUCTION | P4-CP-OSB-01 / 32 | C04 |

Do not scale. All dimensions in mm. Check all dimensions on site.




Top / left chains = saw cut positions (to cut centres). Coloured = part size and position.

Do not scale. All dimensions in mm. Check all dimensions on site.

## SHEET 33 OF 50

### THIS SHEET

| Item | Value |
|---|---|
| Parts | 2 |
| Used / waste | 99.1% / 0.03 m2 |
| Reusable offcuts | 0 |
| Saw cuts / shared | 3 / 1 |

### PIECES (POSITION = BOTTOM-LEFT CORNER)

| Label | Size | X, Y |
|---|---|---|
| GF-EX20 S01 | 498 x 2383 | 0, 697 |
| GF-EX26 S01 | 695 x 2383 | 0, 0 |

### NOTES

1. Cut from OSB/3 9mm 1197x2397, 2mm saw kerf. Viewed on the face; dimensions from the sheet's bottom-left corner (0,0). Red numbered lines = saw cuts in order, each edge to edge.
2. Coloured dimensions belong to the part of that colour: its width and height, and its position from the sheet edges. Raked parts: corner coordinates at each corner.
3. Red hatch = waste. Labels = panel + piece mark on the manufacture drawing.

### REVISIONS

| REV | DATE | DESCRIPTION |
|---|---|---|
| C01 | 14.09.26 | Construction issue |
| C02 | 14.09.26 | Roof trusses revised; SP diagonals added |
| C03 | 11.10.26 | FF windows coursed; steel + GP1 portal; steel drawings (ST) |
| C04 | 13.10.26 | Steel approved by the engineer: steel + steel timber drawings issued for construction |

TLS

TLS TIMBER FRAME

Design & Manufacture

Scan: 3D model + drawings

| CLIENT | PROJECT |
|---|---|
| MP Adams | MP Adams Plot 4, Eckington |


DRAWING TITLE

**OSB CUTTING - GROUND FLOOR - SHEET 33 OF 50**

OSB/3 9mm 1197x2397 | Ground Floor

| SCALE | SIZE | DATE | DRAWN |
|---|---|---|---|
| NTS | A3 | 13.10.26 | TS |

| STATUS | DRAWING No. | REV |
|---|---|---|
| CONSTRUCTION | P4-CP-OSB-01 / 33 | C04 |

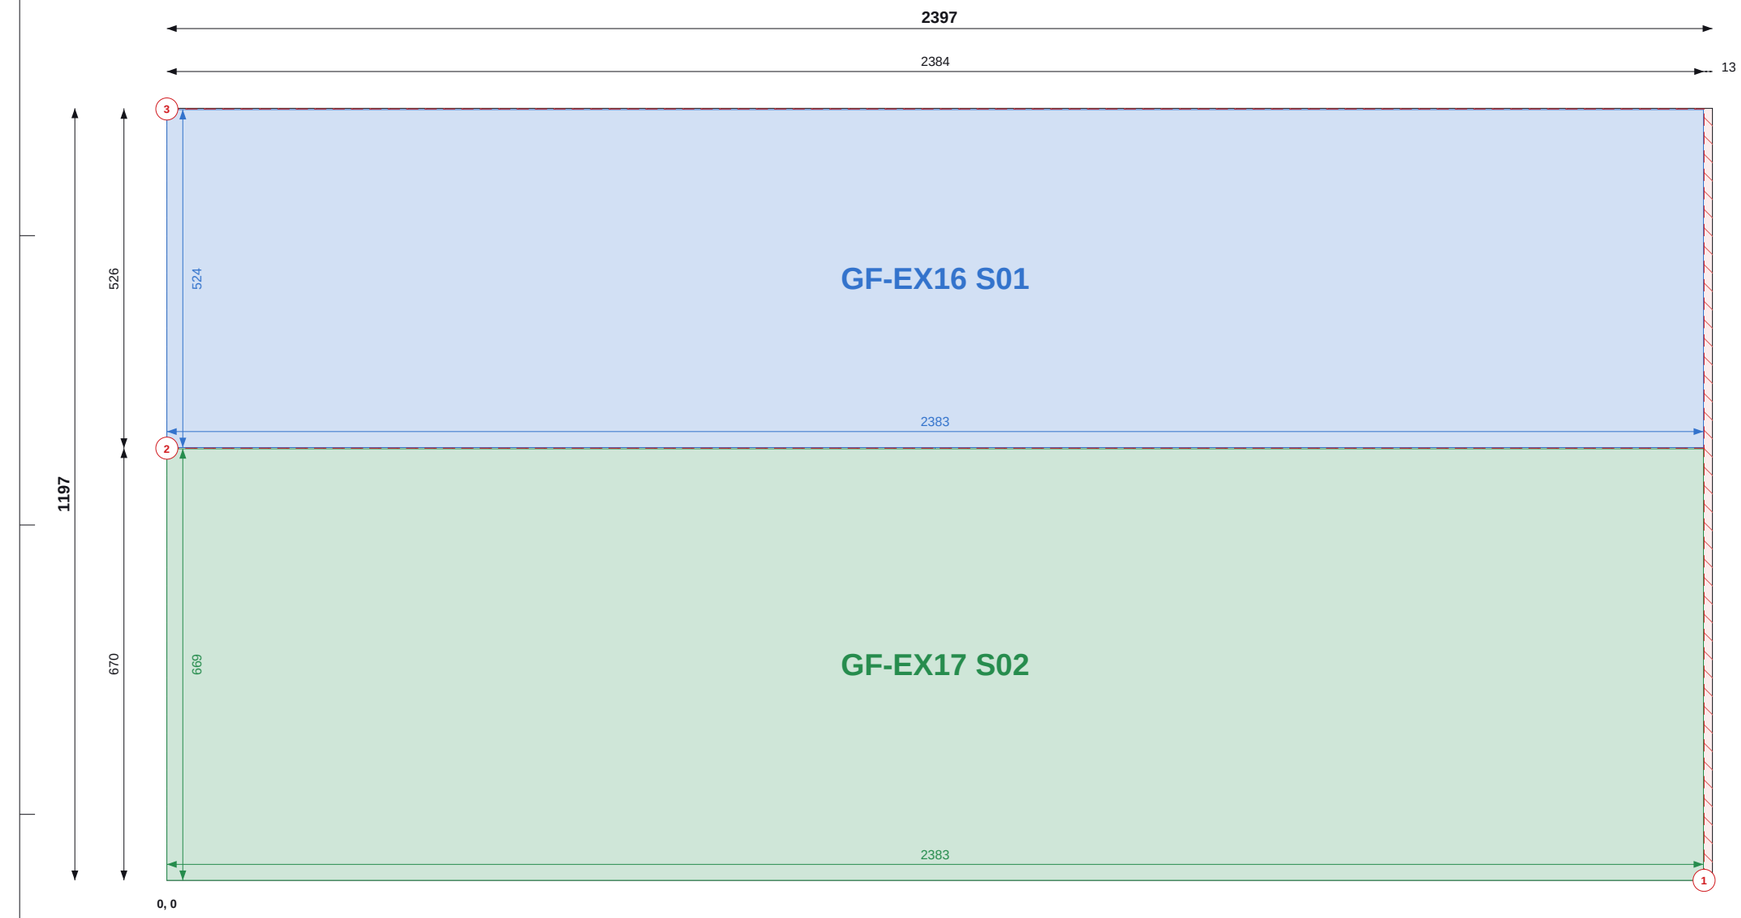


Top / left chains = saw cut positions (to cut centres). Coloured = part size and position.

## SHEET 34 OF 50

### THIS SHEET

| Item | Value |
|---|---|
| Parts | 2 |
| Used / waste | 99.1% / 0.03 m2 |
| Reusable offcuts | 0 |
| Saw cuts / shared | 3 / 1 |

### PIECES (POSITION = BOTTOM-LEFT CORNER)

| Label | Size | X, Y |
|---|---|---|
| GF-EX16 S01 | 524 x 2383 | 0, 671 |
| GF-EX17 S02 | 669 x 2383 | 0, 0 |

### NOTES

1. Cut from OSB/3 9mm 1197x2397, 2mm saw kerf. Viewed on the face; dimensions from the sheet's bottom-left corner (0,0). Red numbered lines = saw cuts in order, each edge to edge.
2. Coloured dimensions belong to the part of that colour: its width and height, and its position from the sheet edges. Raked parts: corner coordinates at each corner.
3. Red hatch = waste. Labels = panel + piece mark on the manufacture drawing.

### REVISIONS

| REV | DATE | DESCRIPTION |
|---|---|---|
| C01 | 14.09.26 | Construction issue |
| C02 | 14.09.26 | Roof trusses revised; SP diagonals added |
| C03 | 11.10.26 | FF windows coursed; steel + GP1 portal; steel drawings (ST) |
| C04 | 13.10.26 | Steel approved by the engineer: steel + steel timber drawings issued for construction |

TLS

TLS TIMBER FRAME

Design & Manufacture

Scan: 3D model + drawings

| CLIENT | PROJECT |
|---|---|
| MP Adams | MP Adams Plot 4, Eckington |

DRAWING TITLE


**OSB CUTTING - GROUND FLOOR - SHEET 34 OF 50**

OSB/3 9mm 1197x2397 | Ground Floor

| SCALE | SIZE | DATE | DRAWN |
|---|---|---|---|
| NTS | A3 | 13.10.26 | TS |

| STATUS | DRAWING No. | REV |
|---|---|---|
| CONSTRUCTION | P4-CP-OSB-01 / 34 | C04 |

Do not scale. All dimensions in mm. Check all dimensions on site.

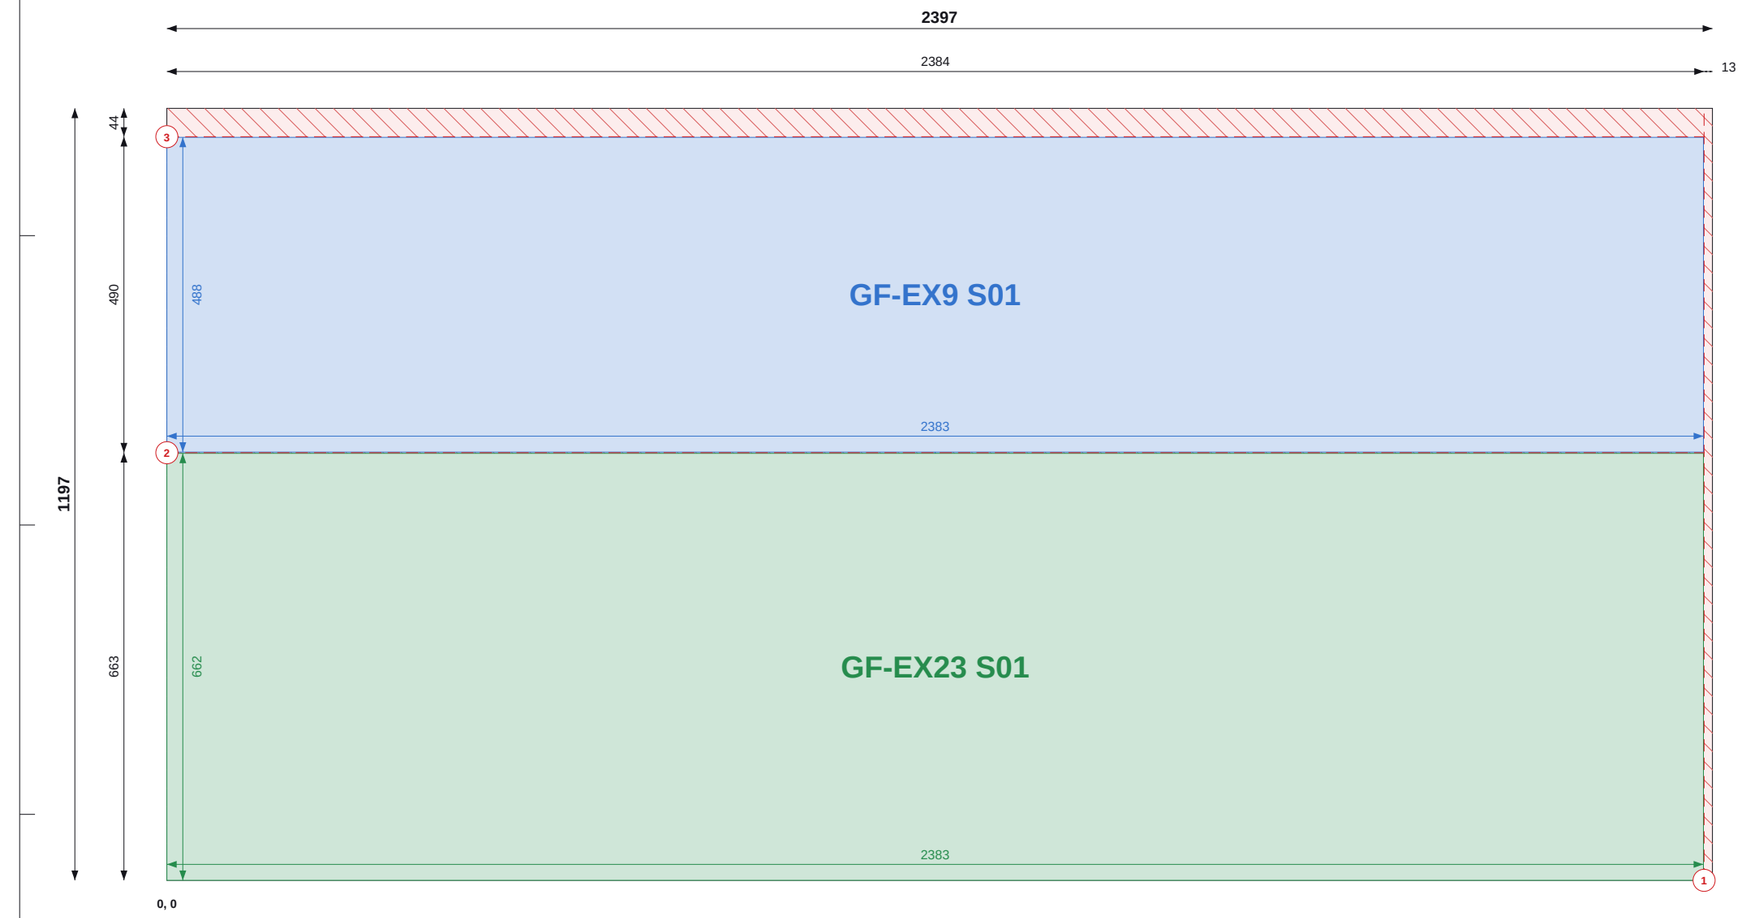


Top / left chains = saw cut positions (to cut centres). Coloured = part size and position.

Do not scale. All dimensions in mm. Check all dimensions on site.

## SHEET 35 OF 50

### THIS SHEET

| Item | Value |
|---|---|
| Parts | 2 |
| Used / waste | 95.5% / 0.13 m2 |
| Reusable offcuts | 0 |
| Saw cuts / shared | 3 / 1 |

### PIECES (POSITION = BOTTOM-LEFT CORNER)

| Label | Size | X, Y |
|---|---|---|
| GF-EX9 S01 | 488 x 2383 | 0, 664 |
| GF-EX23 S01 | 662 x 2383 | 0, 0 |

### NOTES

1. Cut from OSB/3 9mm 1197x2397, 2mm saw kerf. Viewed on the face; dimensions from the sheet's bottom-left corner (0,0). Red numbered lines = saw cuts in order, each edge to edge.
2. Coloured dimensions belong to the part of that colour: its width and height, and its position from the sheet edges. Raked parts: corner coordinates at each corner.
3. Red hatch = waste. Labels = panel + piece mark on the manufacture drawing.

### REVISIONS

| REV | DATE | DESCRIPTION |
|---|---|---|
| C01 | 14.09.26 | Construction issue |
| C02 | 14.09.26 | Roof trusses revised; SP diagonals added |
| C03 | 11.10.26 | FF windows coursed; steel + GP1 portal; steel drawings (ST) |
| C04 | 13.10.26 | Steel approved by the engineer: steel + steel timber drawings issued for construction |

TLS

TLS TIMBER FRAME

Design & Manufacture

Scan: 3D model + drawings

| CLIENT | PROJECT |
|---|---|
| MP Adams | MP Adams Plot 4, Eckington |


DRAWING TITLE

**OSB CUTTING - GROUND FLOOR - SHEET 35 OF 50**

OSB/3 9mm 1197x2397 | Ground Floor

| SCALE | SIZE | DATE | DRAWN |
|---|---|---|---|
| NTS | A3 | 13.10.26 | TS |

| STATUS | DRAWING No. | REV |
|---|---|---|
| CONSTRUCTION | P4-CP-OSB-01 / 35 | C04 |

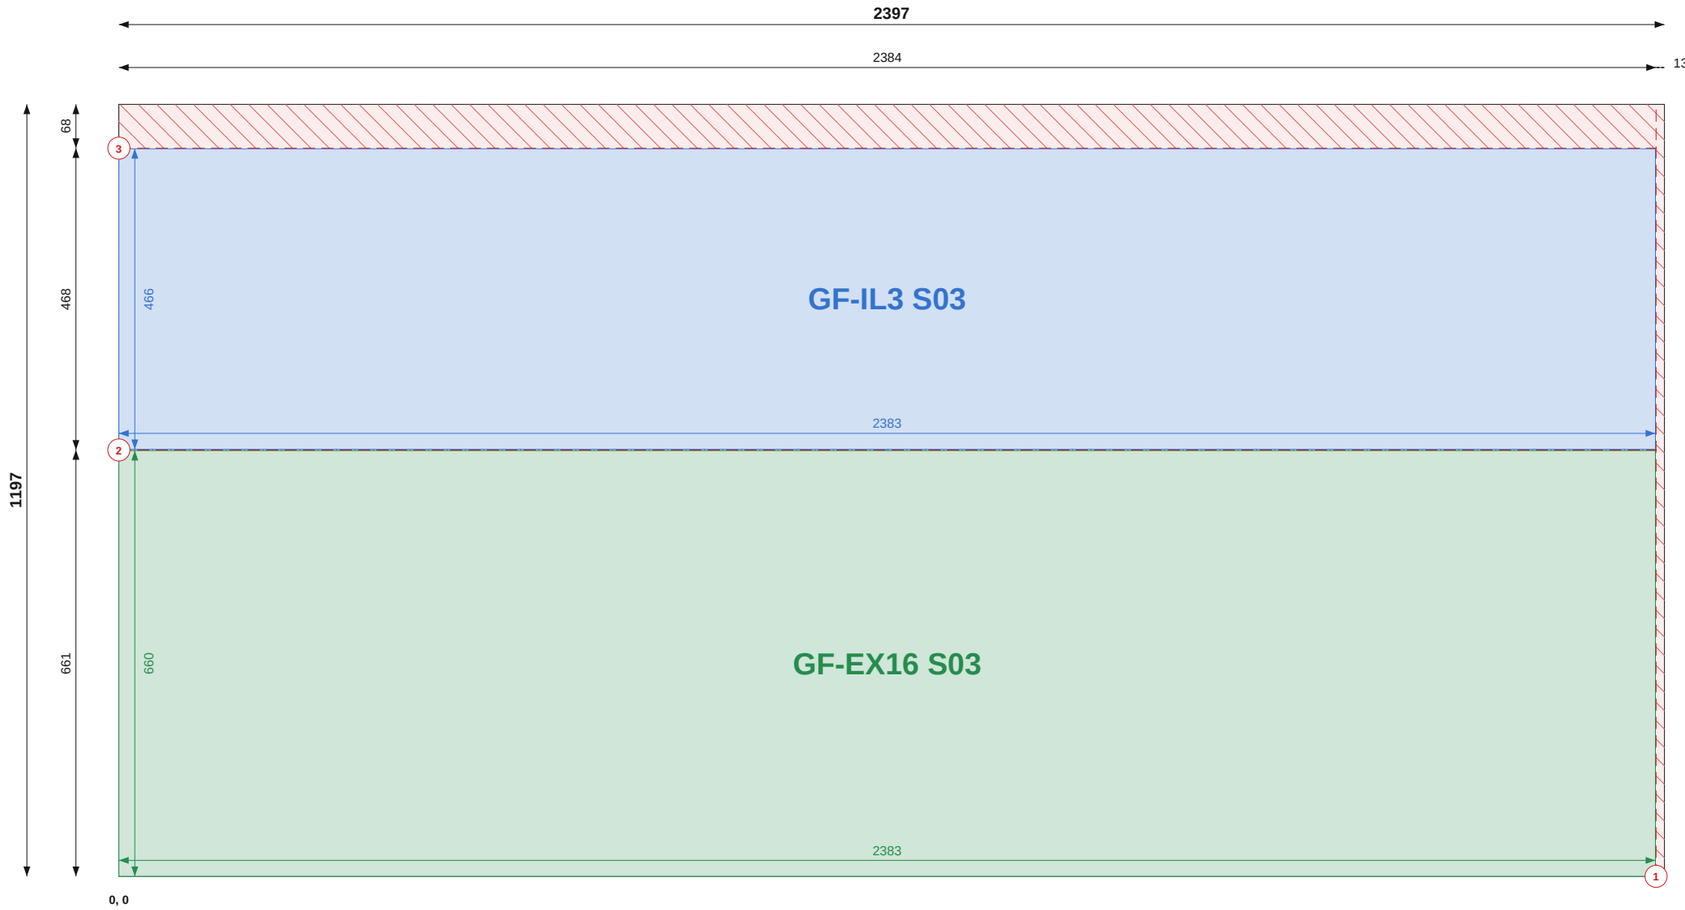


Top / left chains = saw cut positions (to cut centres). Coloured = part size and position.

## SHEET 36 OF 50

### THIS SHEET

| Item | Value |
|---|---|
| Parts | 2 |
| Used / waste | 93.5% / 0.19 m2 |
| Reusable offcuts | 0 |
| Saw cuts / shared | 3 / 1 |

### PIECES (POSITION = BOTTOM-LEFT CORNER)

| Label | Size | X, Y |
|---|---|---|
| GF-IL3 S03 | 466 x 2383 | 0, 662 |
| GF-EX16 S03 | 660 x 2383 | 0, 0 |

### NOTES

1. Cut from OSB/3 9mm 1197x2397, 2mm saw kerf. Viewed on the face; dimensions from the sheet's bottom-left corner (0,0). Red numbered lines = saw cuts in order, each edge to edge.
2. Coloured dimensions belong to the part of that colour: its width and height, and its position from the sheet edges. Raked parts: corner coordinates at each corner.
3. Red hatch = waste. Labels = panel + piece mark on the manufacture drawing.

### REVISIONS

| REV | DATE | DESCRIPTION |
|---|---|---|
| C01 | 14.09.26 | Construction issue |
| C02 | 14.09.26 | Roof trusses revised; SP diagonals added |
| C03 | 11.10.26 | FF windows coursed; steel + GP1 portal; steel drawings (ST) |
| C04 | 13.10.26 | Steel approved by the engineer: steel + steel timber drawings issued for construction |

TLS

TLS TIMBER FRAME

Design & Manufacture

Scan: 3D model + drawings

| CLIENT | PROJECT |
|---|---|
| MP Adams | MP Adams Plot 4, Eckington |

DRAWING TITLE


**OSB CUTTING - GROUND FLOOR - SHEET 36 OF 50**

OSB/3 9mm 1197x2397 | Ground Floor

| SCALE | SIZE | DATE | DRAWN |
|---|---|---|---|
| NTS | A3 | 13.10.26 | TS |

| STATUS | DRAWING No. | REV |
|---|---|---|
| CONSTRUCTION | P4-CP-OSB-01 / 36 | C04 |

Do not scale. All dimensions in mm. Check all dimensions on site.

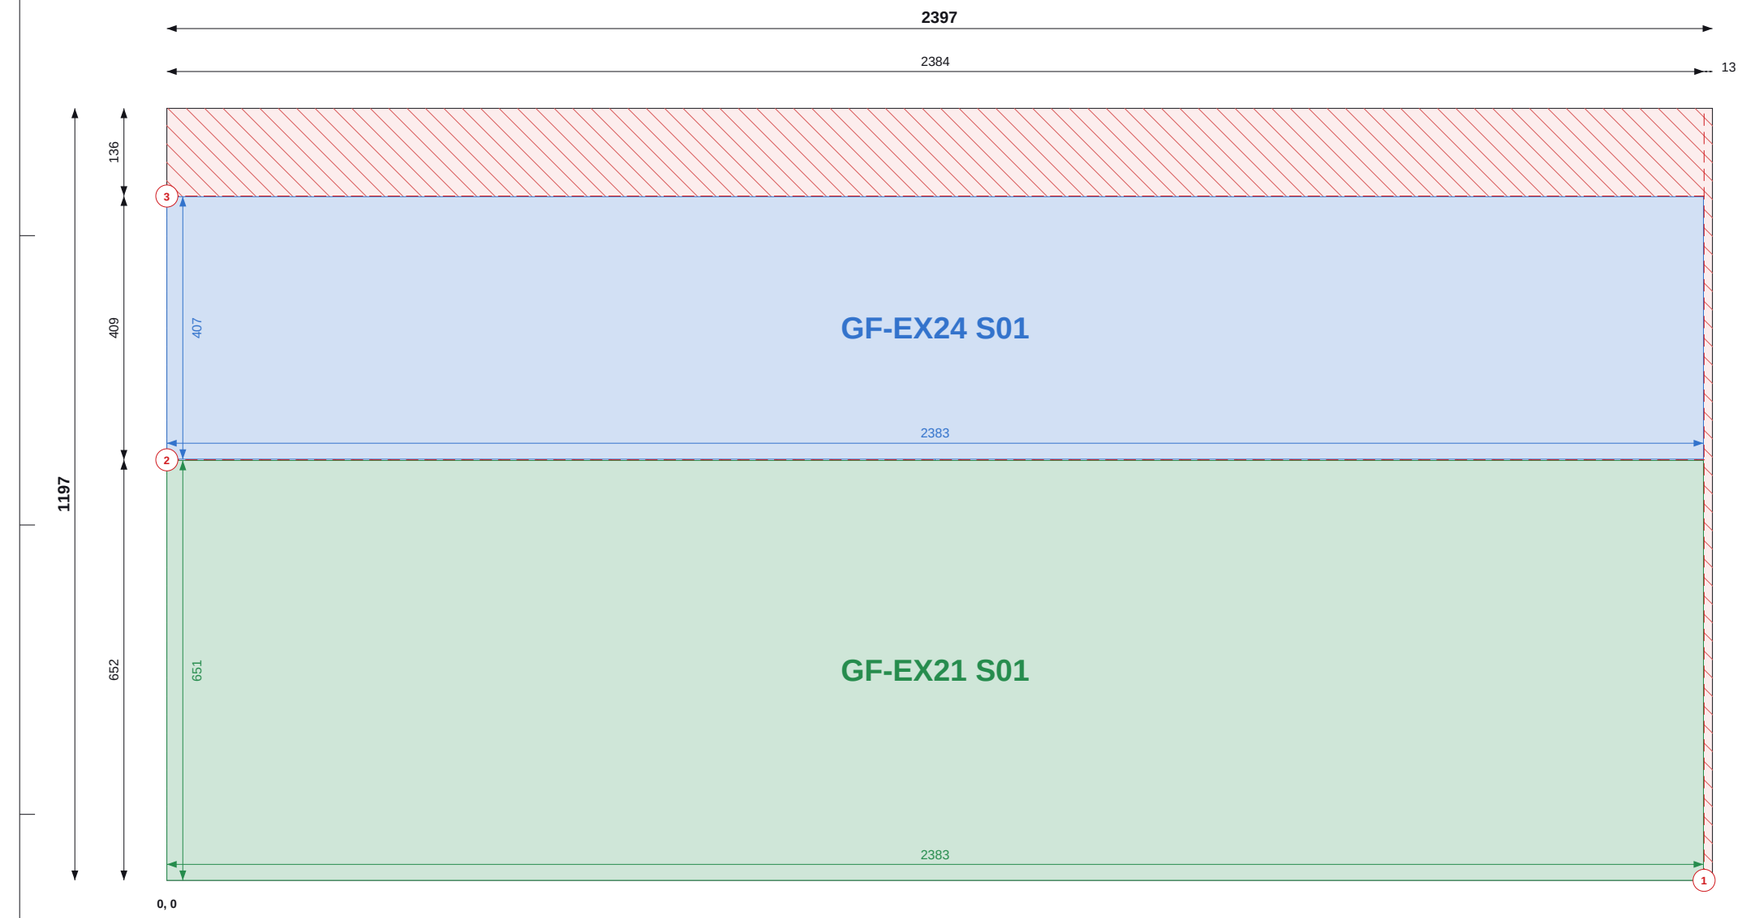


Top / left chains = saw cut positions (to cut centres). Coloured = part size and position.

## SHEET 37 OF 50

### THIS SHEET

| Item | Value |
|---|---|
| Parts | 2 |
| Used / waste | 87.9% / 0.35 m2 |
| Reusable offcuts | 0 |
| Saw cuts / shared | 3 / 1 |

### PIECES (POSITION = BOTTOM-LEFT CORNER)

| Label | Size | X, Y |
|---|---|---|
| GF-EX24 S01 | 407 x 2383 | 0, 653 |
| GF-EX21 S01 | 651 x 2383 | 0, 0 |

### NOTES

1. Cut from OSB/3 9mm 1197x2397, 2mm saw kerf. Viewed on the face; dimensions from the sheet's bottom-left corner (0,0). Red numbered lines = saw cuts in order, each edge to edge.
2. Coloured dimensions belong to the part of that colour: its width and height, and its position from the sheet edges. Raked parts: corner coordinates at each corner.
3. Red hatch = waste. Labels = panel + piece mark on the manufacture drawing.

### REVISIONS

| REV | DATE | DESCRIPTION |
|---|---|---|
| C01 | 14.09.26 | Construction issue |
| C02 | 14.09.26 | Roof trusses revised; SP diagonals added |
| C03 | 11.10.26 | FF windows coursed; steel + GP1 portal; steel drawings (ST) |
| C04 | 13.10.26 | Steel approved by the engineer: steel + steel timber drawings issued for construction |

TLS

TLS TIMBER FRAME

Design & Manufacture

Scan: 3D model + drawings

| CLIENT | PROJECT |
|---|---|
| MP Adams | MP Adams Plot 4, Eckington |

DRAWING TITLE


**OSB CUTTING - GROUND FLOOR - SHEET 37 OF 50**

OSB/3 9mm 1197x2397 | Ground Floor

| SCALE | SIZE | DATE | DRAWN |
|---|---|---|---|
| NTS | A3 | 13.10.26 | TS |

| STATUS | DRAWING No. | REV |
|---|---|---|
| CONSTRUCTION | P4-CP-OSB-01 / 37 | C04 |

Do not scale. All dimensions in mm. Check all dimensions on site.

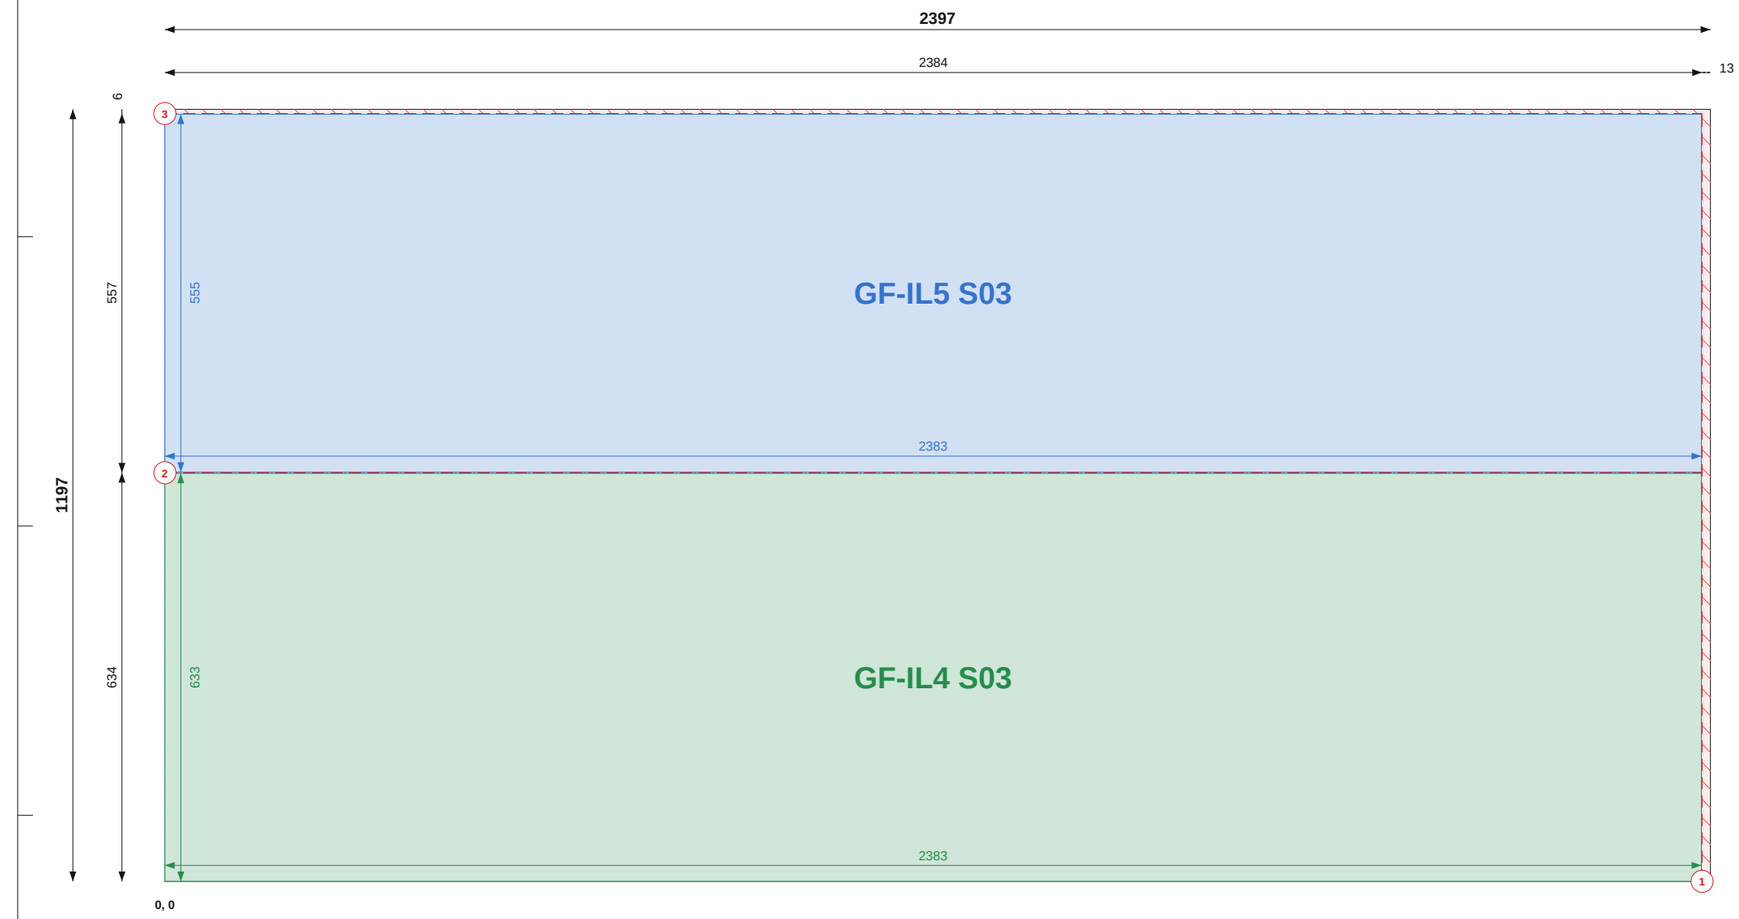


Top / left chains = saw cut positions (to cut centres). Coloured = part size and position.

## SHEET 38 OF 50

### THIS SHEET

| Item | Value |
|---|---|
| Parts | 2 |
| Used / waste | 98.6% / 0.04 m2 |
| Reusable offcuts | 0 |
| Saw cuts / shared | 3 / 1 |

### PIECES (POSITION = BOTTOM-LEFT CORNER)

| Label | Size | X, Y |
|---|---|---|
| GF-IL5 S03 | 555 x 2383 | 0, 635 |
| GF-IL4 S03 | 633 x 2383 | 0, 0 |

### NOTES

1. Cut from OSB/3 9mm 1197x2397, 2mm saw kerf. Viewed on the face; dimensions from the sheet's bottom-left corner (0,0). Red numbered lines = saw cuts in order, each edge to edge.
2. Coloured dimensions belong to the part of that colour: its width and height, and its position from the sheet edges. Raked parts: corner coordinates at each corner.
3. Red hatch = waste. Labels = panel + piece mark on the manufacture drawing.

### REVISIONS

| REV | DATE | DESCRIPTION |
|---|---|---|
| C01 | 14.09.26 | Construction issue |
| C02 | 14.09.26 | Roof trusses revised; SP diagonals added |
| C03 | 11.10.26 | FF windows coursed; steel + GP1 portal; steel drawings (ST) |
| C04 | 13.10.26 | Steel approved by the engineer: steel + steel timber drawings issued for construction |

TLS

TLS TIMBER FRAME

Design & Manufacture

Scan: 3D model + drawings

| CLIENT | PROJECT |
|---|---|
| MP Adams | MP Adams Plot 4, Eckington |

DRAWING TITLE


**OSB CUTTING - GROUND FLOOR - SHEET 38 OF 50**

OSB/3 9mm 1197x2397 | Ground Floor

| SCALE | SIZE | DATE | DRAWN |
|---|---|---|---|
| NTS | A3 | 13.10.26 | TS |

| STATUS | DRAWING No. | REV |
|---|---|---|
| CONSTRUCTION | P4-CP-OSB-01 / 38 | C04 |

Do not scale. All dimensions in mm. Check all dimensions on site.

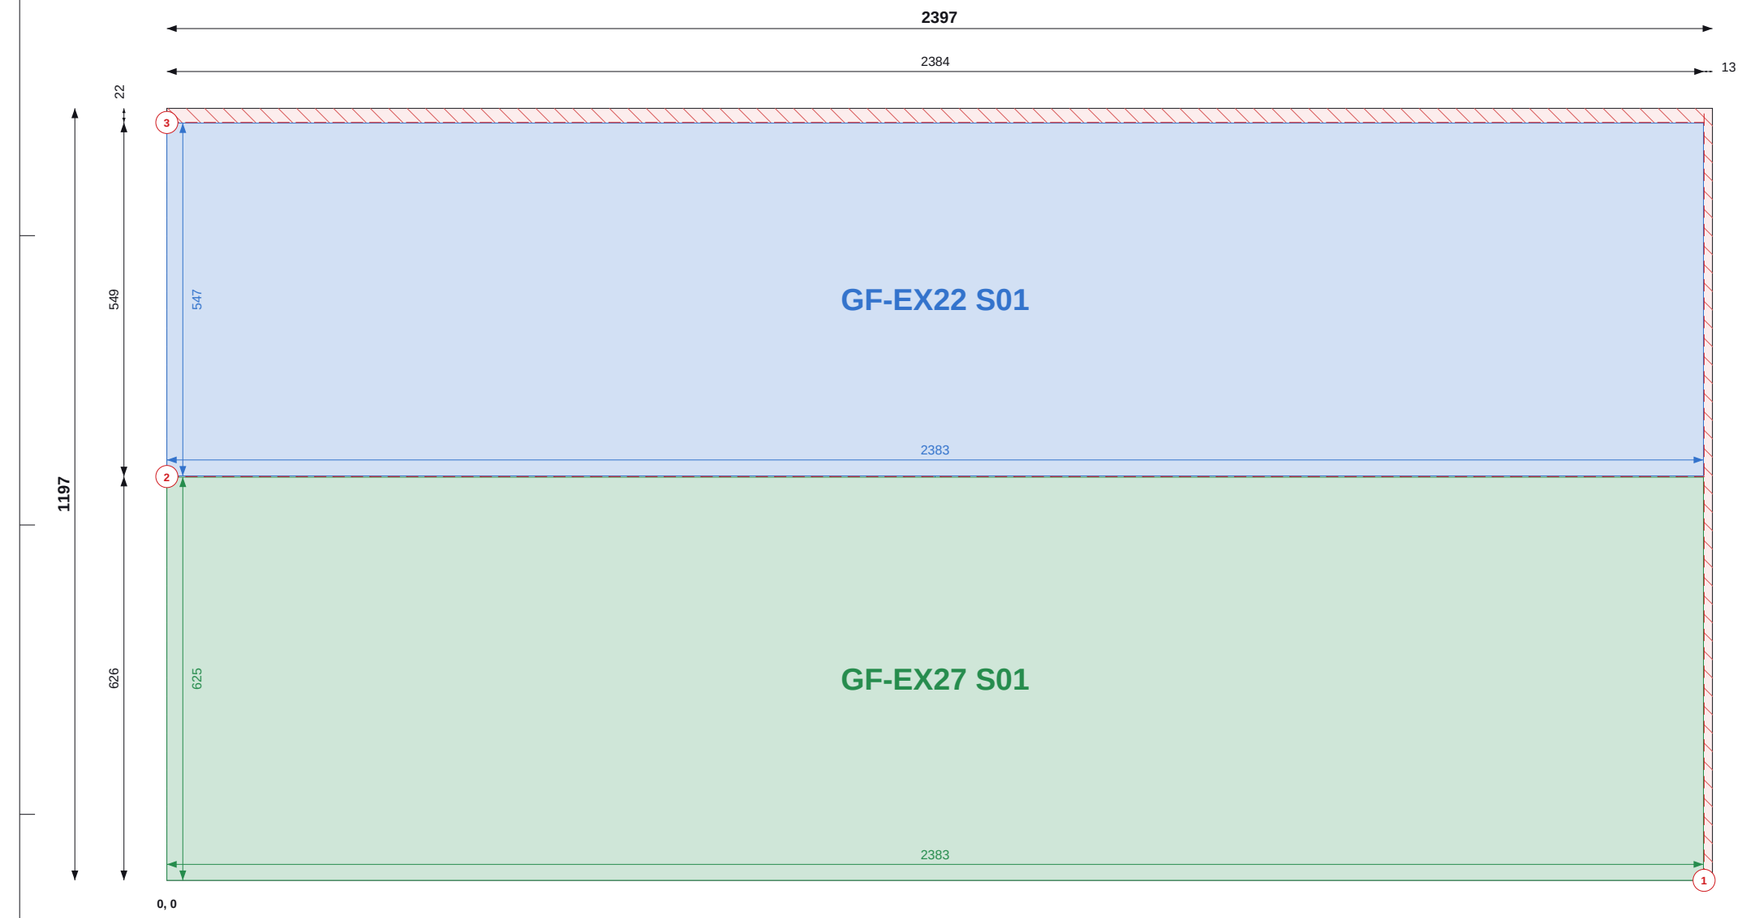


Top / left chains = saw cut positions (to cut centres). Coloured = part size and position.

## SHEET 39 OF 50

### THIS SHEET

| Item | Value |
|---|---|
| Parts | 2 |
| Used / waste | 97.3% / 0.08 m2 |
| Reusable offcuts | 0 |
| Saw cuts / shared | 3 / 1 |

### PIECES (POSITION = BOTTOM-LEFT CORNER)

| Label | Size | X, Y |
|---|---|---|
| GF-EX22 S01 | 547 x 2383 | 0, 627 |
| GF-EX27 S01 | 625 x 2383 | 0, 0 |

### NOTES

1. Cut from OSB/3 9mm 1197x2397, 2mm saw kerf. Viewed on the face; dimensions from the sheet's bottom-left corner (0,0). Red numbered lines = saw cuts in order, each edge to edge.
2. Coloured dimensions belong to the part of that colour: its width and height, and its position from the sheet edges. Raked parts: corner coordinates at each corner.
3. Red hatch = waste. Labels = panel + piece mark on the manufacture drawing.

### REVISIONS

| REV | DATE | DESCRIPTION |
|---|---|---|
| C01 | 14.09.26 | Construction issue |
| C02 | 14.09.26 | Roof trusses revised; SP diagonals added |
| C03 | 11.10.26 | FF windows coursed; steel + GP1 portal; steel drawings (ST) |
| C04 | 13.10.26 | Steel approved by the engineer: steel + steel timber drawings issued for construction |

TLS

TLS TIMBER FRAME

Design & Manufacture

Scan: 3D model + drawings

| CLIENT | PROJECT |
|---|---|
| MP Adams | MP Adams Plot 4, Eckington |

DRAWING TITLE


**OSB CUTTING - GROUND FLOOR - SHEET 39 OF 50**

OSB/3 9mm 1197x2397 | Ground Floor

| SCALE | SIZE | DATE | DRAWN |
|---|---|---|---|
| NTS | A3 | 13.10.26 | TS |

| STATUS | DRAWING No. | REV |
|---|---|---|
| CONSTRUCTION | P4-CP-OSB-01 / 39 | C04 |

Do not scale. All dimensions in mm. Check all dimensions on site.

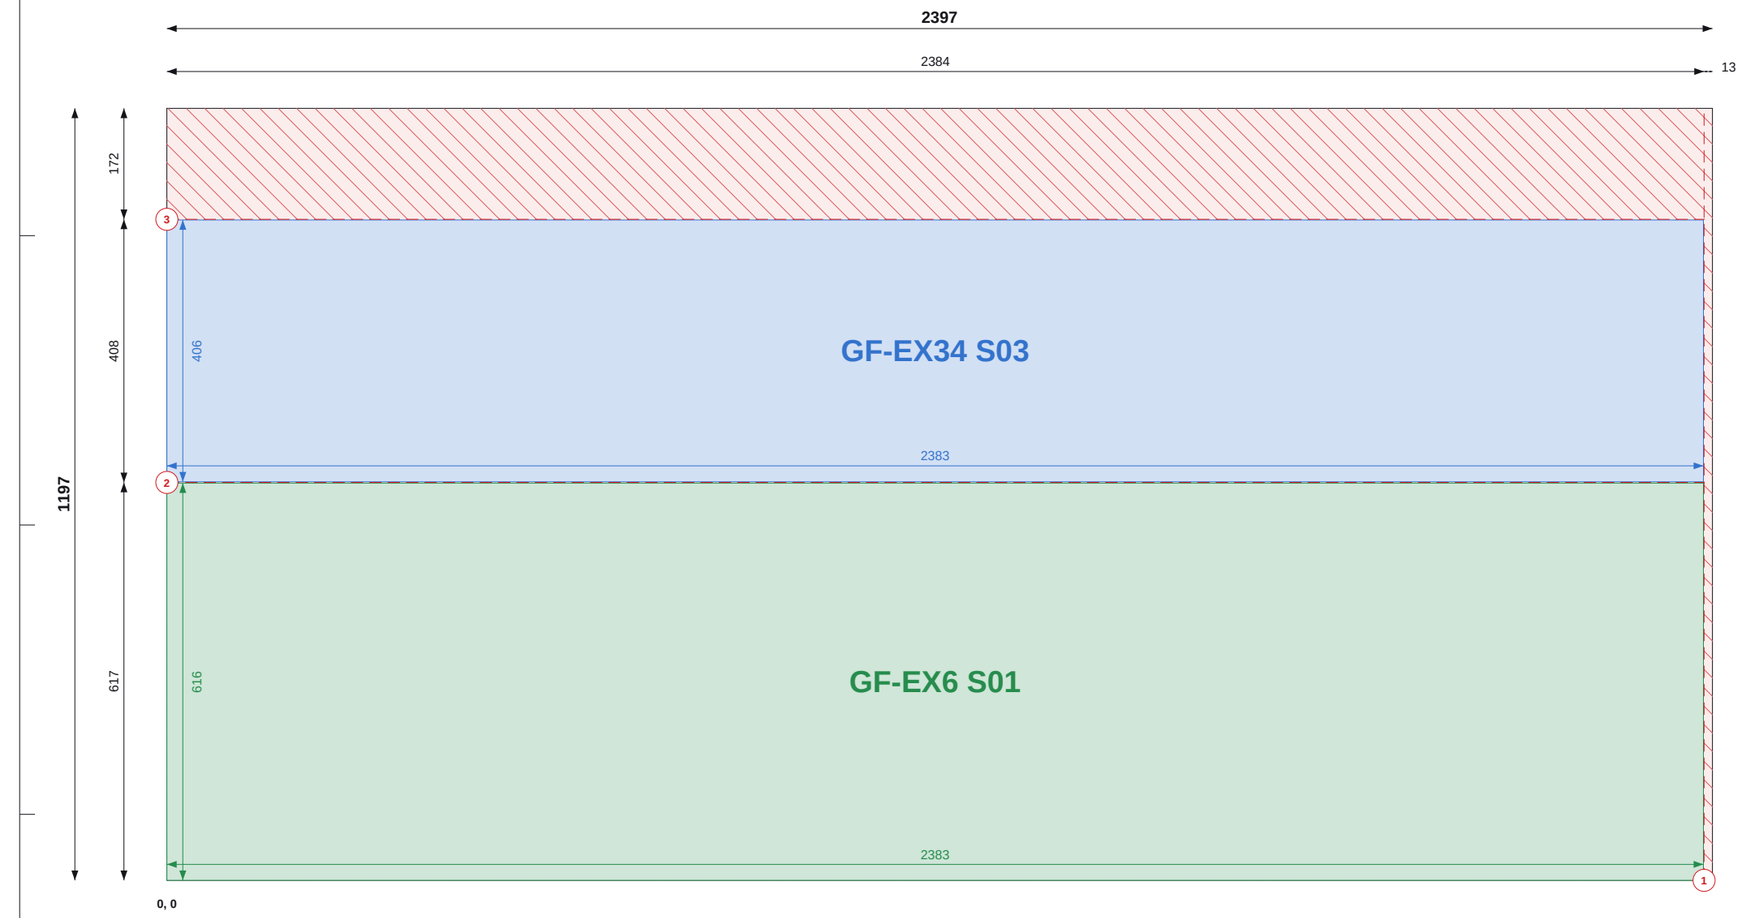


Top / left chains = saw cut positions (to cut centres). Coloured = part size and position.

Do not scale. All dimensions in mm. Check all dimensions on site.

## SHEET 40 OF 50

### THIS SHEET

| Item | Value |
|---|---|
| Parts | 2 |
| Used / waste | 84.9% / 0.43 m2 |
| Reusable offcuts | 0 |
| Saw cuts / shared | 3 / 1 |

### PIECES (POSITION = BOTTOM-LEFT CORNER)

| Label | Size | X, Y |
|---|---|---|
| GF-EX34 S03 | 406 x 2383 | 0, 618 |
| GF-EX6 S01 | 616 x 2383 | 0, 0 |

### NOTES

1. Cut from OSB/3 9mm 1197x2397, 2mm saw kerf. Viewed on the face; dimensions from the sheet's bottom-left corner (0,0). Red numbered lines = saw cuts in order, each edge to edge.
2. Coloured dimensions belong to the part of that colour: its width and height, and its position from the sheet edges. Raked parts: corner coordinates at each corner.
3. Red hatch = waste. Labels = panel + piece mark on the manufacture drawing.

### REVISIONS

| REV | DATE | DESCRIPTION |
|---|---|---|
| C01 | 14.09.26 | Construction issue |
| C02 | 14.09.26 | Roof trusses revised; SP diagonals added |
| C03 | 11.10.26 | FF windows coursed; steel + GP1 portal; steel drawings (ST) |
| C04 | 13.10.26 | Steel approved by the engineer: steel + steel timber drawings issued for construction |

TLS

TLS TIMBER FRAME

Design & Manufacture

Scan: 3D model + drawings

| CLIENT | PROJECT |
|---|---|
| MP Adams | MP Adams Plot 4, Eckington |


DRAWING TITLE

**OSB CUTTING - GROUND FLOOR - SHEET 40 OF 50**

OSB/3 9mm 1197x2397 | Ground Floor

| SCALE | SIZE | DATE | DRAWN |
|---|---|---|---|
| NTS | A3 | 13.10.26 | TS |

| STATUS | DRAWING No. | REV |
|---|---|---|
| CONSTRUCTION | P4-CP-OSB-01 / 40 | C04 |

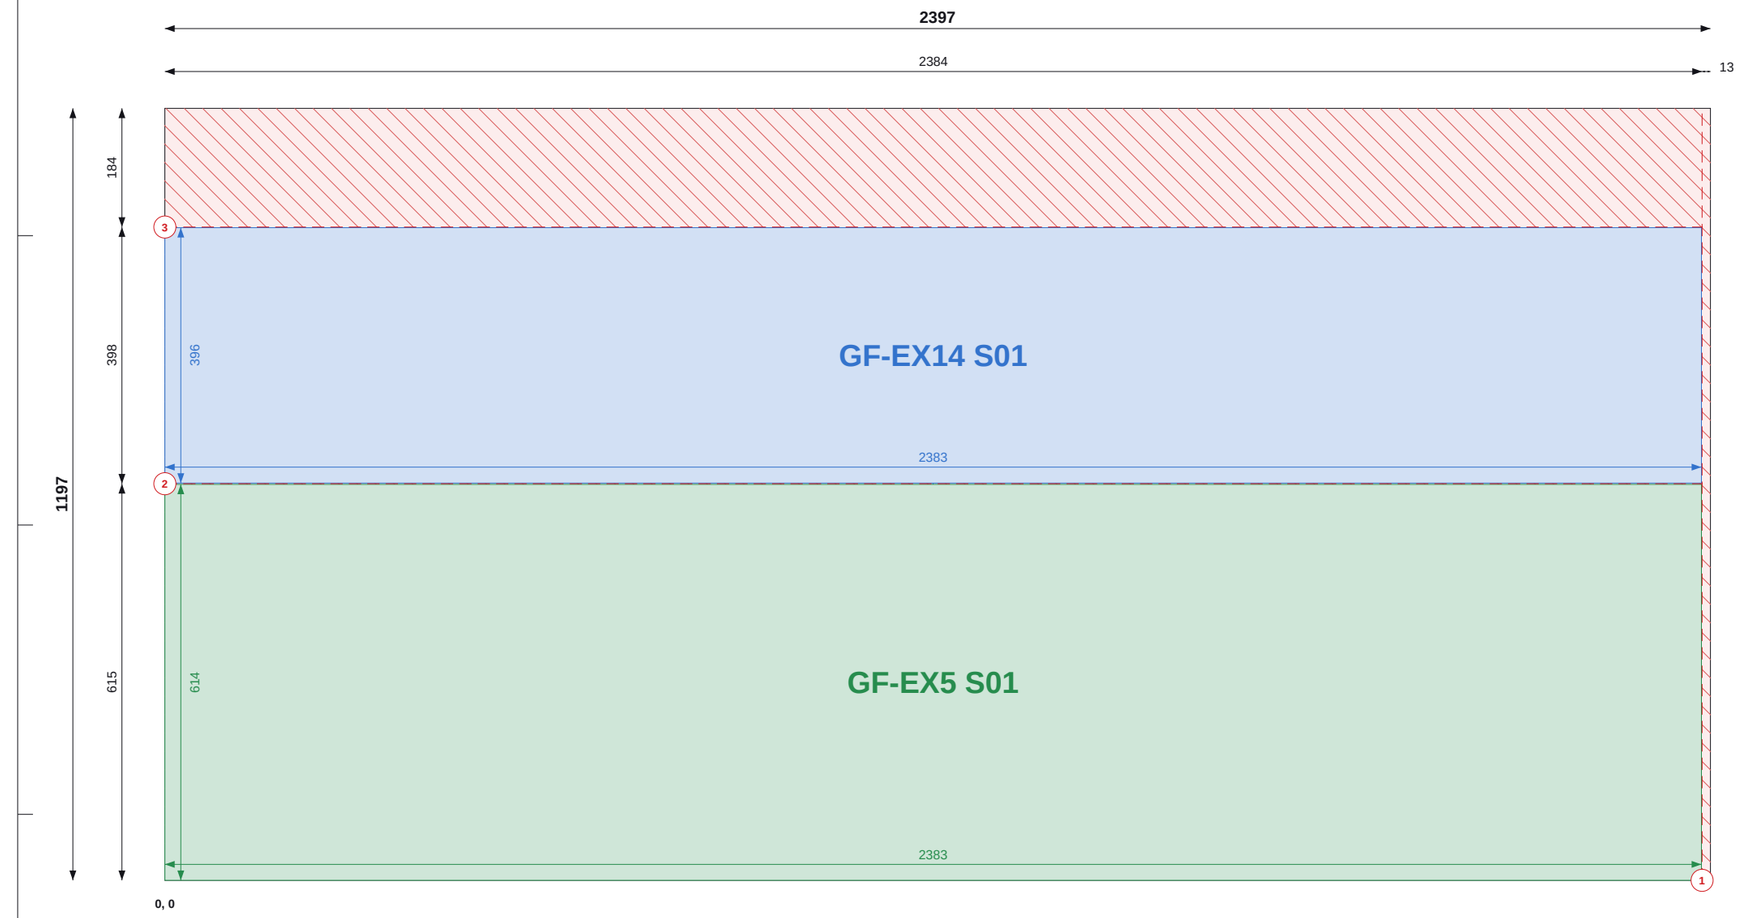


Top / left chains = saw cut positions (to cut centres). Coloured = part size and position.

Do not scale. All dimensions in mm. Check all dimensions on site.

## SHEET 41 OF 50

### THIS SHEET

| Item | Value |
|---|---|
| Parts | 2 |
| Used / waste | 83.9% / 0.46 m2 |
| Reusable offcuts | 0 |
| Saw cuts / shared | 3 / 1 |

### PIECES (POSITION = BOTTOM-LEFT CORNER)

| Label | Size | X, Y |
|---|---|---|
| GF-EX14 S01 | 396 x 2383 | 0, 616 |
| GF-EX5 S01 | 614 x 2383 | 0, 0 |

### NOTES

1. Cut from OSB/3 9mm 1197x2397, 2mm saw kerf. Viewed on the face; dimensions from the sheet's bottom-left corner (0,0). Red numbered lines = saw cuts in order, each edge to edge.
2. Coloured dimensions belong to the part of that colour: its width and height, and its position from the sheet edges. Raked parts: corner coordinates at each corner.
3. Red hatch = waste. Labels = panel + piece mark on the manufacture drawing.

### REVISIONS

| REV | DATE | DESCRIPTION |
|---|---|---|
| C01 | 14.09.26 | Construction issue |
| C02 | 14.09.26 | Roof trusses revised; SP diagonals added |
| C03 | 11.10.26 | FF windows coursed; steel + GP1 portal; steel drawings (ST) |
| C04 | 13.10.26 | Steel approved by the engineer: steel + steel timber drawings issued for construction |

TLS

TLS TIMBER FRAME

Design & Manufacture

Scan: 3D model + drawings

| CLIENT | PROJECT |
|---|---|
| MP Adams | MP Adams Plot 4, Eckington |

DRAWING TITLE

**OSB CUTTING - GROUND FLOOR - SHEET 41 OF 50**

OSB/3 9mm 1197x2397 | Ground Floor

| SCALE | SIZE | DATE | DRAWN |
|---|---|---|---|
| NTS | A3 | 13.10.26 | TS |

| STATUS | DRAWING No. | REV |
|---|---|---|
| CONSTRUCTION | P4-CP-OSB-01 / 41 | C04 |




Top / left chains = saw cut positions (to cut centres). Coloured = part size and position.

## SHEET 42 OF 50

### THIS SHEET

| Item | Value |
|---|---|
| Parts | 2 |
| Used / waste | 99.2% / 0.02 m2 |
| Reusable offcuts | 0 |
| Saw cuts / shared | 2 / 1 |

### PIECES (POSITION = BOTTOM-LEFT CORNER)

| Label | Size | X, Y |
|---|---|---|
| GF-EX25 S01 | 597 x 2383 | 0, 600 |
| GF-EX27 S02 | 598 x 2383 | 0, 0 |

### NOTES

1. Cut from OSB/3 9mm 1197x2397, 2mm saw kerf. Viewed on the face; dimensions from the sheet's bottom-left corner (0,0). Red numbered lines = saw cuts in order, each edge to edge.
2. Coloured dimensions belong to the part of that colour: its width and height, and its position from the sheet edges. Raked parts: corner coordinates at each corner.
3. Red hatch = waste. Labels = panel + piece mark on the manufacture drawing.

### REVISIONS

| REV | DATE | DESCRIPTION |
|---|---|---|
| C01 | 14.09.26 | Construction issue |
| C02 | 14.09.26 | Roof trusses revised; SP diagonals added |
| C03 | 11.10.26 | FF windows coursed; steel + GP1 portal; steel drawings (ST) |
| C04 | 13.10.26 | Steel approved by the engineer: steel + steel timber drawings issued for construction |

TLS

TLS TIMBER FRAME

Design & Manufacture

Scan: 3D model + drawings

| CLIENT | PROJECT |
|---|---|
| MP Adams | MP Adams Plot 4, Eckington |

DRAWING TITLE


**OSB CUTTING - GROUND FLOOR - SHEET 42 OF 50**

OSB/3 9mm 1197x2397 | Ground Floor

| SCALE | SIZE | DATE | DRAWN |
|---|---|---|---|
| NTS | A3 | 13.10.26 | TS |

| STATUS | DRAWING No. | REV |
|---|---|---|
| CONSTRUCTION | P4-CP-OSB-01 / 42 | C04 |

Do not scale. All dimensions in mm. Check all dimensions on site.

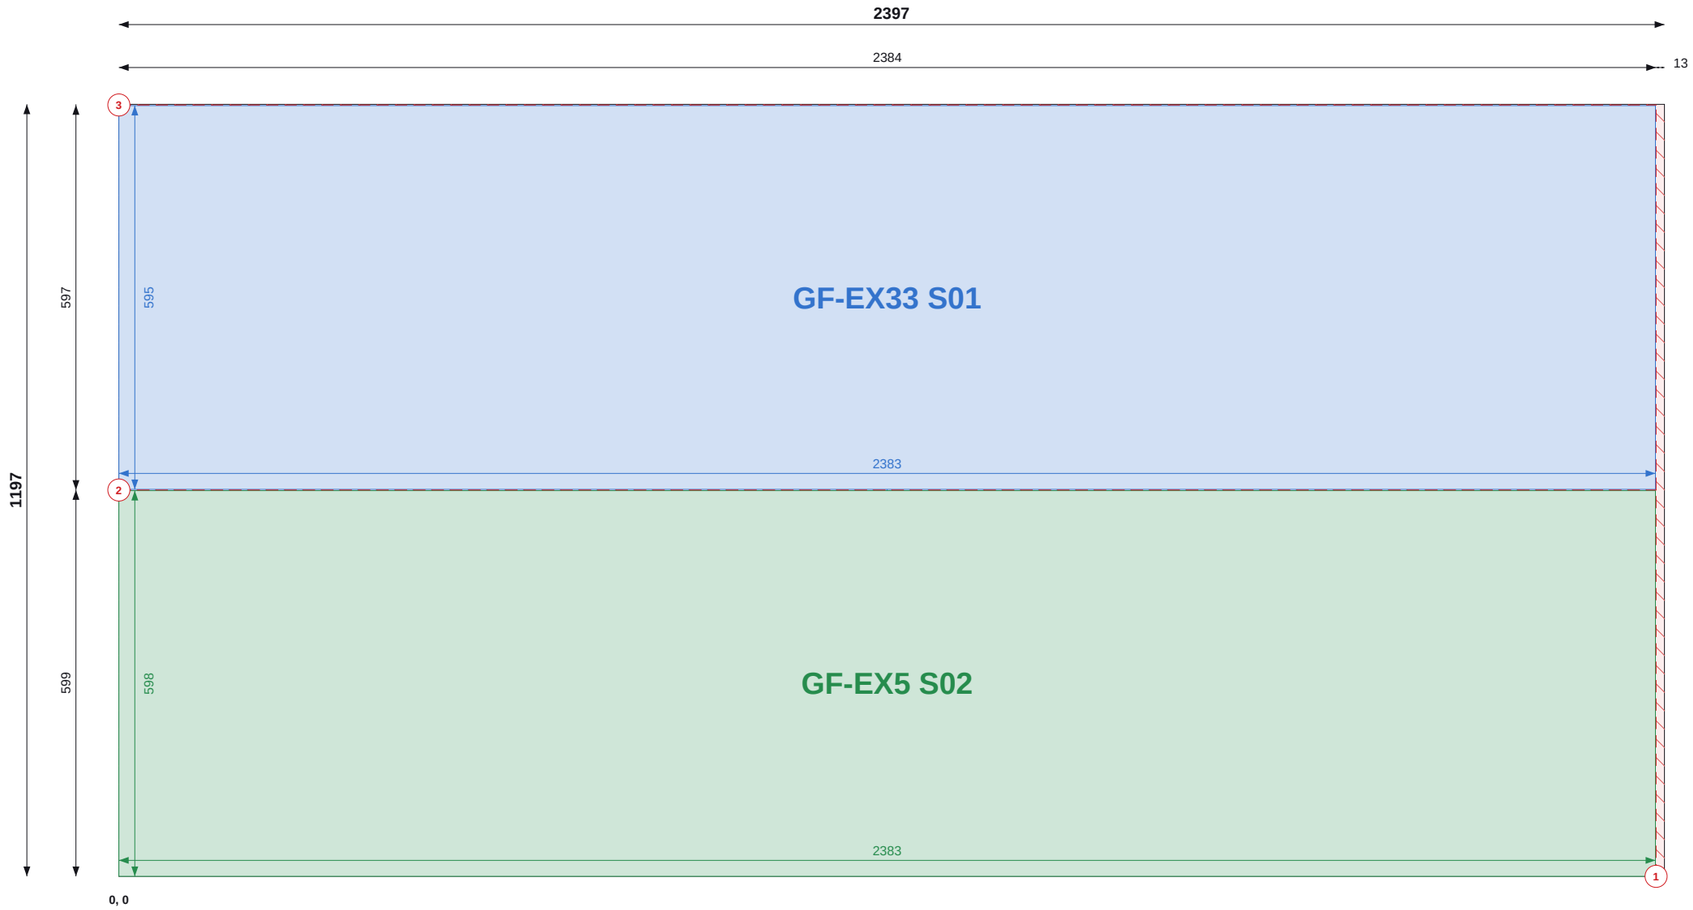


Top / left chains = saw cut positions (to cut centres). Coloured = part size and position.

## SHEET 43 OF 50

### THIS SHEET

| Item | Value |
|---|---|
| Parts | 2 |
| Used / waste | 99.1% / 0.03 m2 |
| Reusable offcuts | 0 |
| Saw cuts / shared | 3 / 1 |

### PIECES (POSITION = BOTTOM-LEFT CORNER)

| Label | Size | X, Y |
|---|---|---|
| GF-EX33 S01 | 595 x 2383 | 0, 600 |
| GF-EX5 S02 | 598 x 2383 | 0, 0 |

### NOTES

1. Cut from OSB/3 9mm 1197x2397, 2mm saw kerf. Viewed on the face; dimensions from the sheet's bottom-left corner (0,0). Red numbered lines = saw cuts in order, each edge to edge.
2. Coloured dimensions belong to the part of that colour: its width and height, and its position from the sheet edges. Raked parts: corner coordinates at each corner.
3. Red hatch = waste. Labels = panel + piece mark on the manufacture drawing.

### REVISIONS

| REV | DATE | DESCRIPTION |
|---|---|---|
| C01 | 14.09.26 | Construction issue |
| C02 | 14.09.26 | Roof trusses revised; SP diagonals added |
| C03 | 11.10.26 | FF windows coursed; steel + GP1 portal; steel drawings (ST) |
| C04 | 13.10.26 | Steel approved by the engineer: steel + steel timber drawings issued for construction |

TLS

TLS TIMBER FRAME

Design & Manufacture

Scan: 3D model + drawings

| CLIENT | PROJECT |
|---|---|
| MP Adams | MP Adams Plot 4, Eckington |

DRAWING TITLE


**OSB CUTTING - GROUND FLOOR - SHEET 43 OF 50**

OSB/3 9mm 1197x2397 | Ground Floor

| SCALE | SIZE | DATE | DRAWN |
|---|---|---|---|
| NTS | A3 | 13.10.26 | TS |

| STATUS | DRAWING No. | REV |
|---|---|---|
| CONSTRUCTION | P4-CP-OSB-01 / 43 | C04 |

Do not scale. All dimensions in mm. Check all dimensions on site.

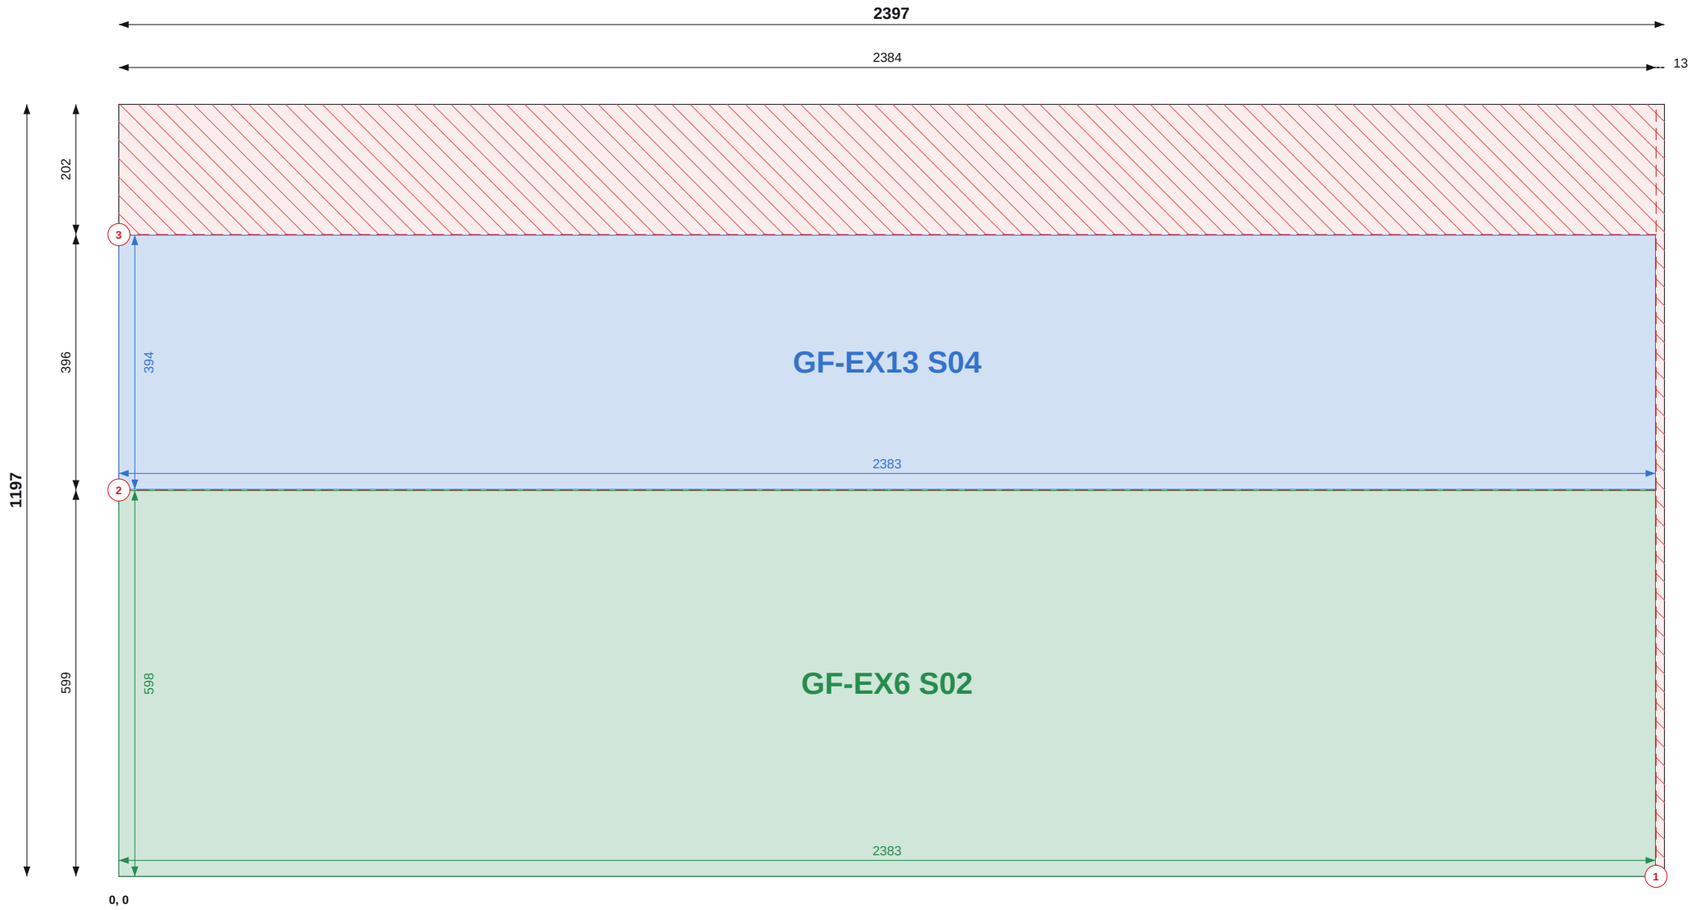


Top / left chains = saw cut positions (to cut centres). Coloured = part size and position.

## SHEET 44 OF 50

### THIS SHEET

| Item | Value |
|---|---|
| Parts | 2 |
| Used / waste | 82.4% / 0.51 m2 |
| Reusable offcuts | 0 |
| Saw cuts / shared | 3 / 1 |

### PIECES (POSITION = BOTTOM-LEFT CORNER)

| Label | Size | X, Y |
|---|---|---|
| GF-EX13 S04 | 394 x 2383 | 0, 600 |
| GF-EX6 S02 | 598 x 2383 | 0, 0 |

### NOTES

1. Cut from OSB/3 9mm 1197x2397, 2mm saw kerf. Viewed on the face; dimensions from the sheet's bottom-left corner (0,0). Red numbered lines = saw cuts in order, each edge to edge.
2. Coloured dimensions belong to the part of that colour: its width and height, and its position from the sheet edges. Raked parts: corner coordinates at each corner.
3. Red hatch = waste. Labels = panel + piece mark on the manufacture drawing.

### REVISIONS

| REV | DATE | DESCRIPTION |
|---|---|---|
| C01 | 14.09.26 | Construction issue |
| C02 | 14.09.26 | Roof trusses revised; SP diagonals added |
| C03 | 11.10.26 | FF windows coursed; steel + GP1 portal; steel drawings (ST) |
| C04 | 13.10.26 | Steel approved by the engineer: steel + steel timber drawings issued for construction |

TLS TIMBER FRAME
Design & Manufacture
Scan: 3D model + drawings

| CLIENT | PROJECT |
|---|---|
| MP Adams | MP Adams Plot 4, Eckington |


DRAWING TITLE
**OSB CUTTING - GROUND FLOOR - SHEET 44 OF 50**

OSB/3 9mm 1197x2397 | Ground Floor

| SCALE | SIZE | DATE | DRAWN |
|---|---|---|---|
| NTS | A3 | 13.10.26 | TS |

| STATUS | DRAWING No. | REV |
|---|---|---|
| CONSTRUCTION | P4-CP-OSB-01 / 44 | C04 |

Do not scale. All dimensions in mm. Check all dimensions on site.

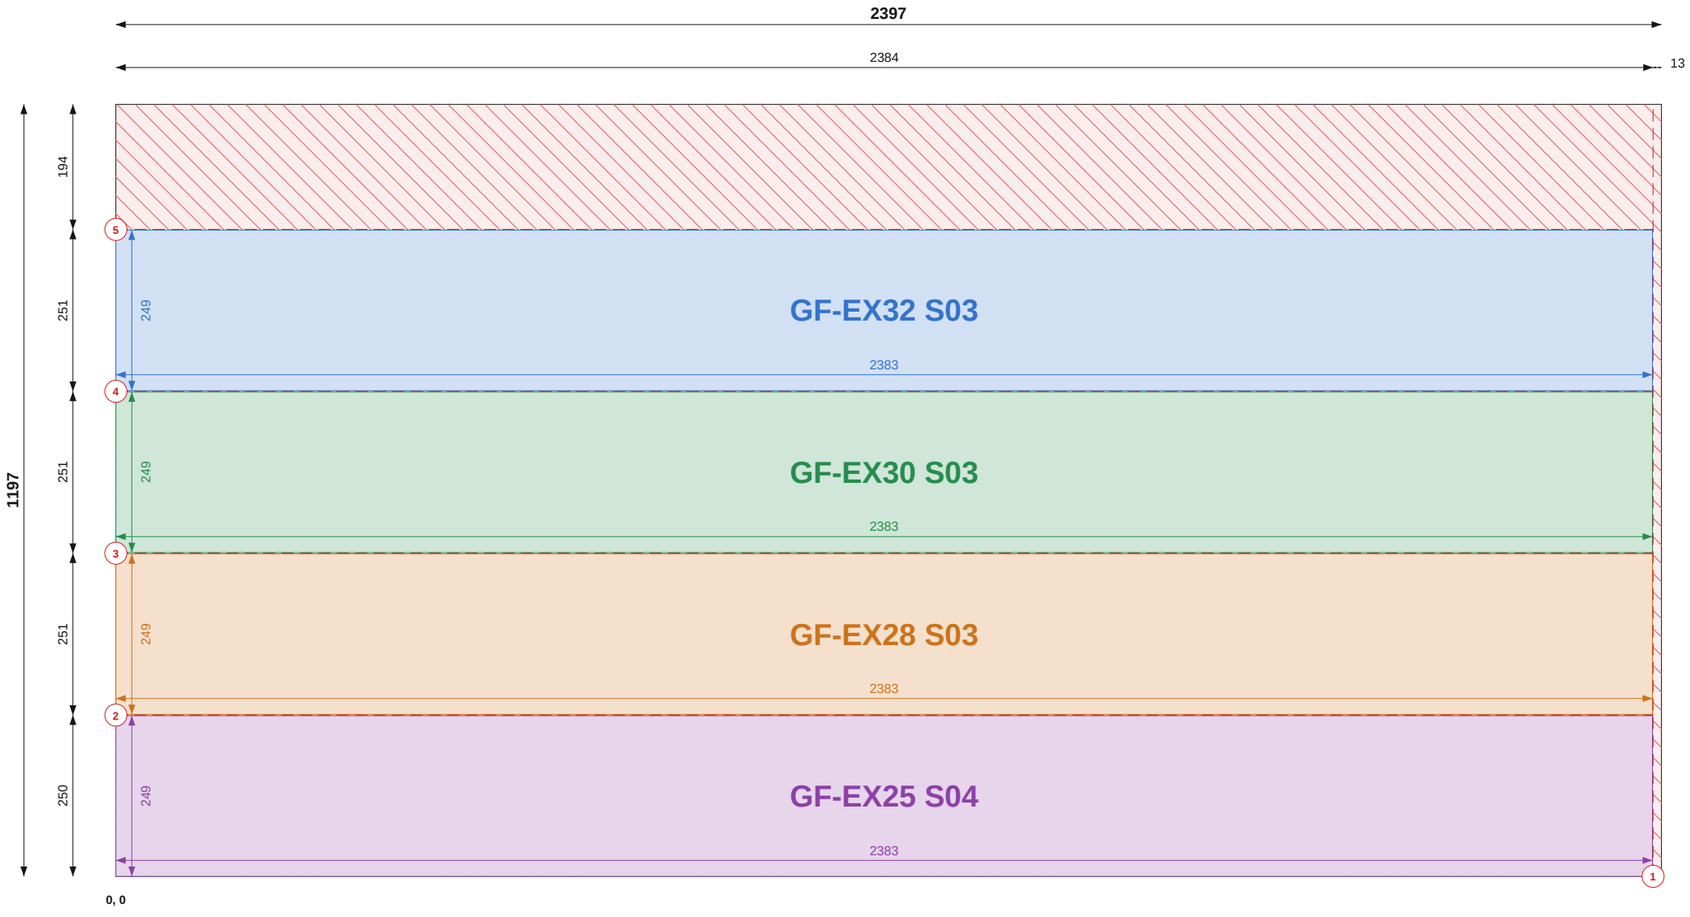


Top / left chains = saw cut positions (to cut centres). Coloured = part size and position.

## SHEET 45 OF 50

### THIS SHEET

| Item | Value |
|---|---|
| Parts | 4 |
| Used / waste | 82.7% / 0.50 m2 |
| Reusable offcuts | 0 |
| Saw cuts / shared | 5 / 3 |

### PIECES (POSITION = BOTTOM-LEFT CORNER)

| Label | Size | X, Y |
|---|---|---|
| GF-EX32 S03 | 249 x 2383 | 0, 753 |
| GF-EX30 S03 | 249 x 2383 | 0, 502 |
| GF-EX28 S03 | 249 x 2383 | 0, 251 |
| GF-EX25 S04 | 249 x 2383 | 0, 0 |

### NOTES

1. Cut from OSB/3 9mm 1197x2397, 2mm saw kerf. Viewed on the face; dimensions from the sheet's bottom-left corner (0,0). Red numbered lines = saw cuts in order, each edge to edge.
2. Coloured dimensions belong to the part of that colour: its width and height, and its position from the sheet edges. Raked parts: corner coordinates at each corner.
3. Red hatch = waste. Labels = panel + piece mark on the manufacture drawing.

### REVISIONS

| REV | DATE | DESCRIPTION |
|---|---|---|
| C01 | 14.09.26 | Construction issue |
| C02 | 14.09.26 | Roof trusses revised; SP diagonals added |
| C03 | 11.10.26 | FF windows coursed; steel + GP1 portal; steel drawings (ST) |
| C04 | 13.10.26 | Steel approved by the engineer: steel + steel timber drawings issued for construction |

TLS TIMBER FRAME DESIGN SUITE

**TLS TIMBER FRAME**
Design & Manufacture
Scan: 3D model + drawings

| CLIENT | PROJECT |
|---|---|
| MP Adams | MP Adams Plot 4, Eckington |

DRAWING TITLE


**OSB CUTTING - GROUND FLOOR - SHEET 45 OF 50**

OSB/3 9mm 1197x2397 | Ground Floor

| SCALE | SIZE | DATE | DRAWN |
|---|---|---|---|
| NTS | A3 | 13.10.26 | TS |

| STATUS | DRAWING No. | REV |
|---|---|---|
| CONSTRUCTION | P4-CP-OSB-01 / 45 | C04 |

Do not scale. All dimensions in mm. Check all dimensions on site.

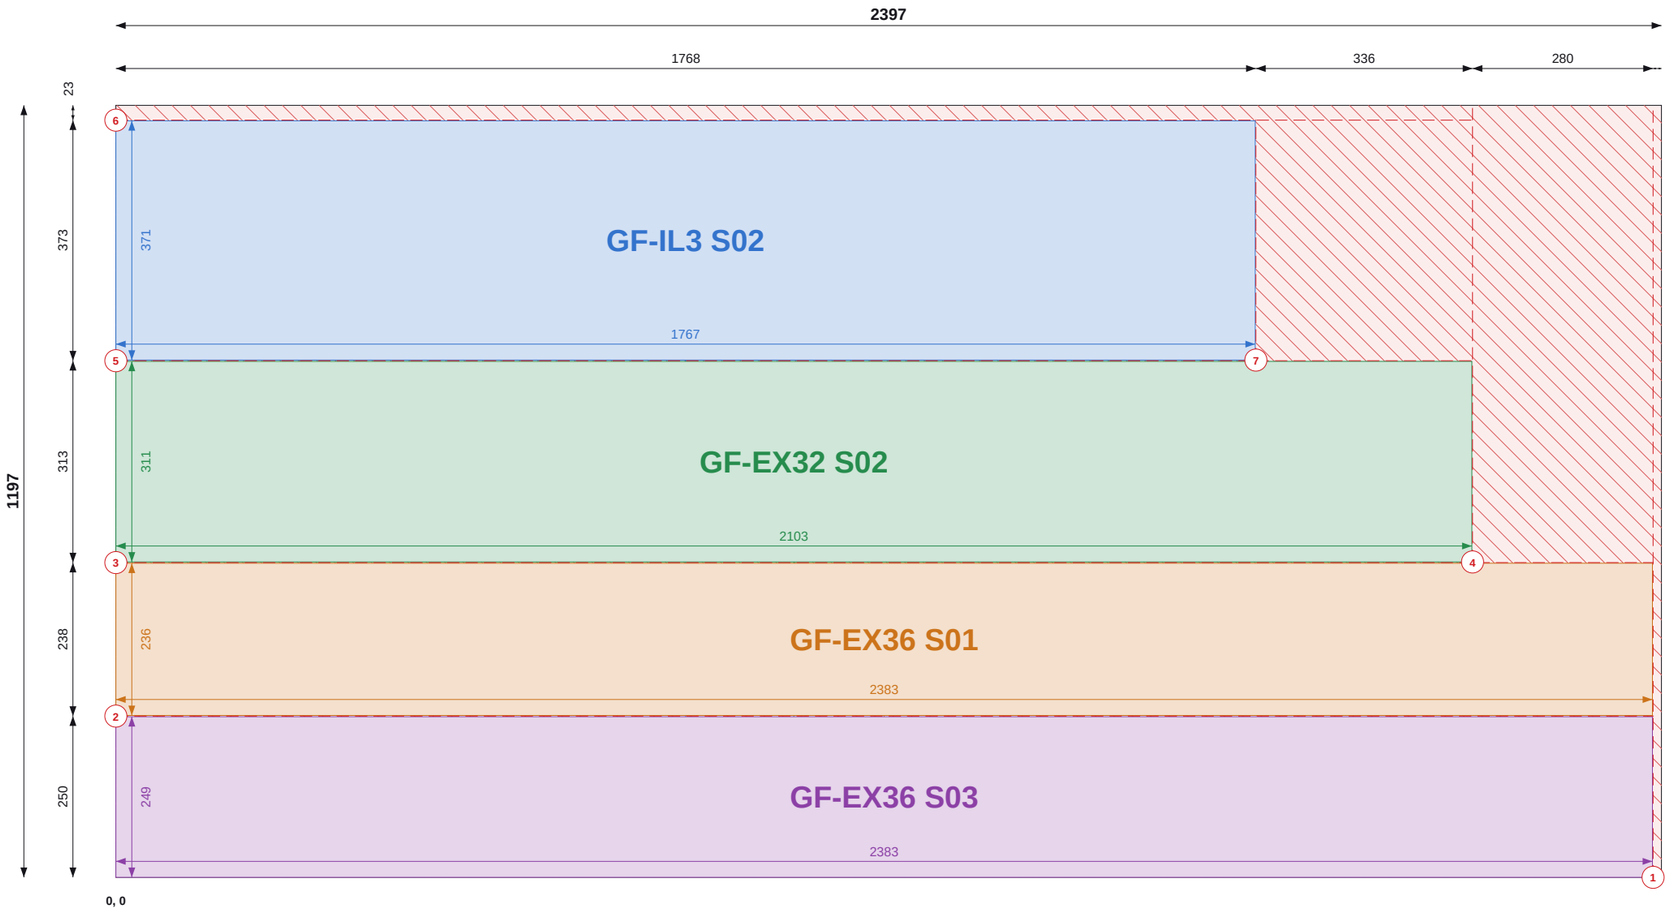


Top / left chains = saw cut positions (to cut centres). Coloured = part size and position.

## SHEET 46 OF 50

### THIS SHEET

| Item | Value |
|---|---|
| Parts | 4 |
| Used / waste | 85.9% / 0.40 m2 |
| Reusable offcuts | 1 |
| Saw cuts / shared | 7 / 3 |

### PIECES (POSITION = BOTTOM-LEFT CORNER)

| Label | Size | X, Y |
|---|---|---|
| GF-IL3 S02 | 1767 x 371 | 0, 802 |
| GF-EX32 S02 | 2103 x 311 | 0, 489 |
| GF-EX36 S01 | 236 x 2383 | 0, 251 |
| GF-EX36 S03 | 249 x 2383 | 0, 0 |

### NOTES

1. Cut from OSB/3 9mm 1197x2397, 2mm saw kerf. Viewed on the face; dimensions from the sheet's bottom-left corner (0,0). Red numbered lines = saw cuts in order, each edge to edge.
2. Coloured dimensions belong to the part of that colour: its width and height, and its position from the sheet edges. Raked parts: corner coordinates at each corner.
3. Red hatch = waste. Labels = panel + piece mark on the manufacture drawing.

### REVISIONS

| REV | DATE | DESCRIPTION |
|---|---|---|
| C01 | 14.09.26 | Construction issue |
| C02 | 14.09.26 | Roof trusses revised; SP diagonals added |
| C03 | 11.10.26 | FF windows coursed; steel + GP1 portal; steel drawings (ST) |
| C04 | 13.10.26 | Steel approved by the engineer: steel + steel timber drawings issued for construction |

TLS TIMBER FRAME
Design & Manufacture
Scan: 3D model + drawings

| CLIENT | PROJECT |
|---|---|
| MP Adams | MP Adams Plot 4, Eckington |

DRAWING TITLE


**OSB CUTTING - GROUND FLOOR - SHEET 46 OF 50**

OSB/3 9mm 1197x2397 | Ground Floor

| SCALE | SIZE | DATE | DRAWN |
|---|---|---|---|
| NTS | A3 | 13.10.26 | TS |

| STATUS | DRAWING No. | REV |
|---|---|---|
| CONSTRUCTION | P4-CP-OSB-01 / 46 | C04 |

Do not scale. All dimensions in mm. Check all dimensions on site.

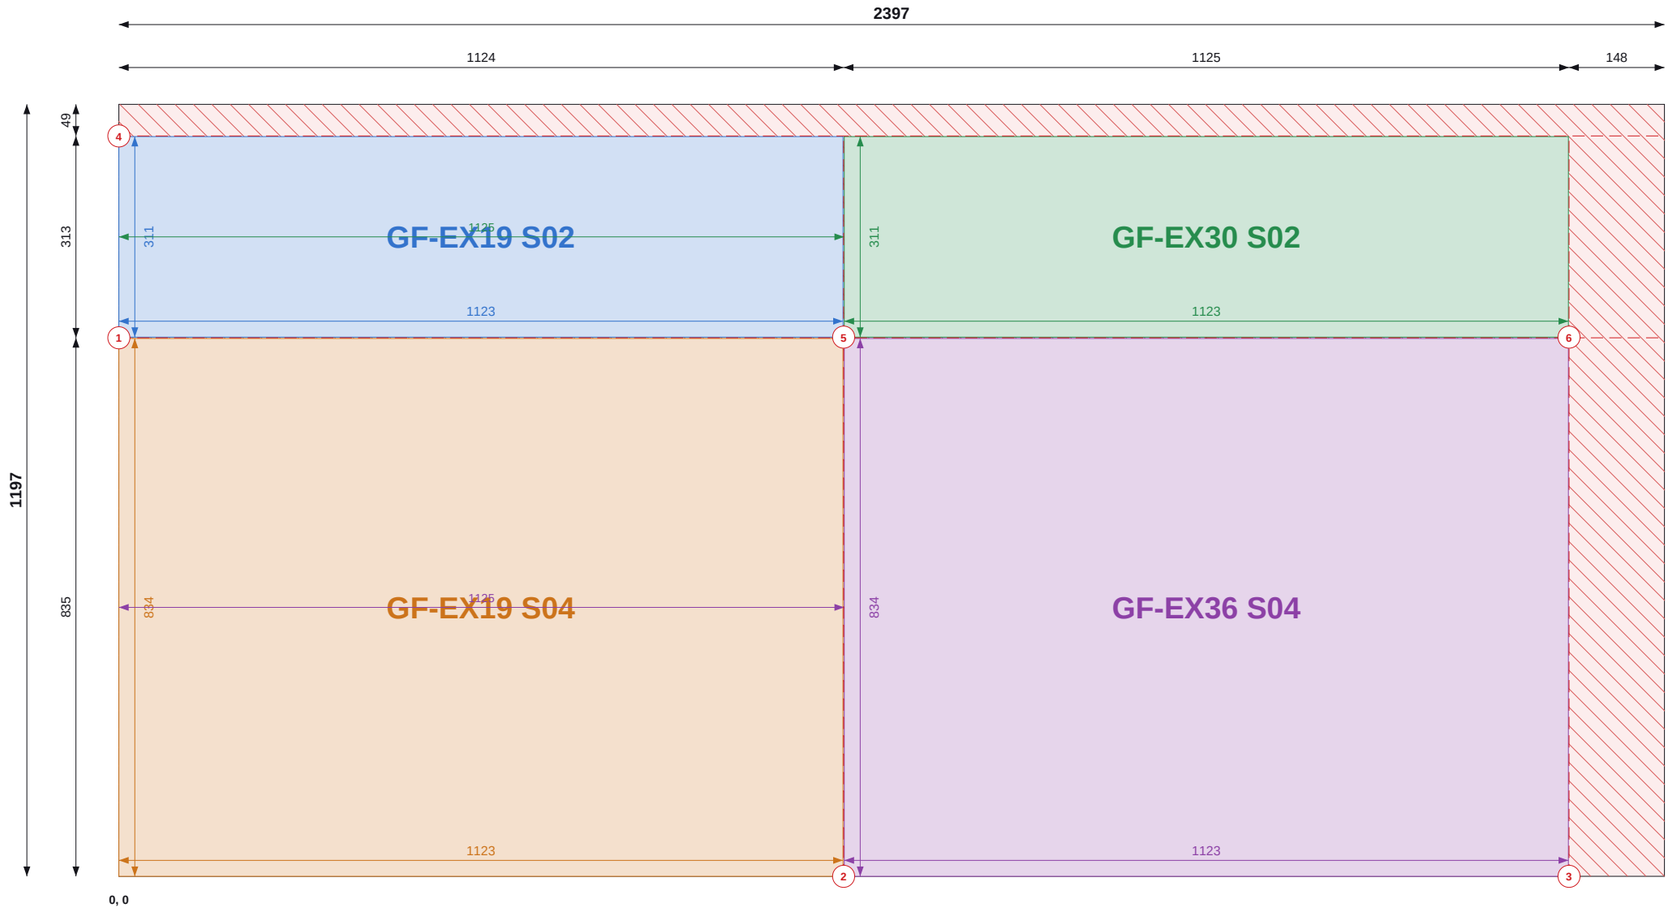


Top / left chains = saw cut positions (to cut centres). Coloured = part size and position.

## SHEET 47 OF 50

### THIS SHEET

| Item | Value |
|---|---|
| Parts | 4 |
| Used / waste | 89.6% / 0.30 m2 |
| Reusable offcuts | 0 |
| Saw cuts / shared | 6 / 3 |

### PIECES (POSITION = BOTTOM-LEFT CORNER)

| Label | Size | X, Y |
|---|---|---|
| GF-EX19 S02 | 1123 x 311 | 0, 836 |
| GF-EX30 S02 | 1123 x 311 | 1125, 836 |
| GF-EX19 S04 | 1123 x 834 | 0, 0 |
| GF-EX36 S04 | 1123 x 834 | 1125, 0 |

### NOTES

1. Cut from OSB/3 9mm 1197x2397, 2mm saw kerf. Viewed on the face; dimensions from the sheet's bottom-left corner (0,0). Red numbered lines = saw cuts in order, each edge to edge.
2. Coloured dimensions belong to the part of that colour: its width and height, and its position from the sheet edges. Raked parts: corner coordinates at each corner.
3. Red hatch = waste. Labels = panel + piece mark on the manufacture drawing.

### REVISIONS

| REV | DATE | DESCRIPTION |
|---|---|---|
| C01 | 14.09.26 | Construction issue |
| C02 | 14.09.26 | Roof trusses revised; SP diagonals added |
| C03 | 11.10.26 | FF windows coursed; steel + GP1 portal; steel drawings (ST) |
| C04 | 13.10.26 | Steel approved by the engineer: steel + steel timber drawings issued for construction |

TLS TIMBER FRAME
Design & Manufacture
Scan: 3D model + drawings

| CLIENT | PROJECT |
|---|---|
| MP Adams | MP Adams Plot 4, Eckington |


DRAWING TITLE
**OSB CUTTING - GROUND FLOOR - SHEET 47 OF 50**

OSB/3 9mm 1197x2397 | Ground Floor

| SCALE | SIZE | DATE | DRAWN |
|---|---|---|---|
| NTS | A3 | 13.10.26 | TS |

| STATUS | DRAWING No. | REV |
|---|---|---|
| CONSTRUCTION | P4-CP-OSB-01 / 47 | C04 |

Do not scale. All dimensions in mm. Check all dimensions on site.

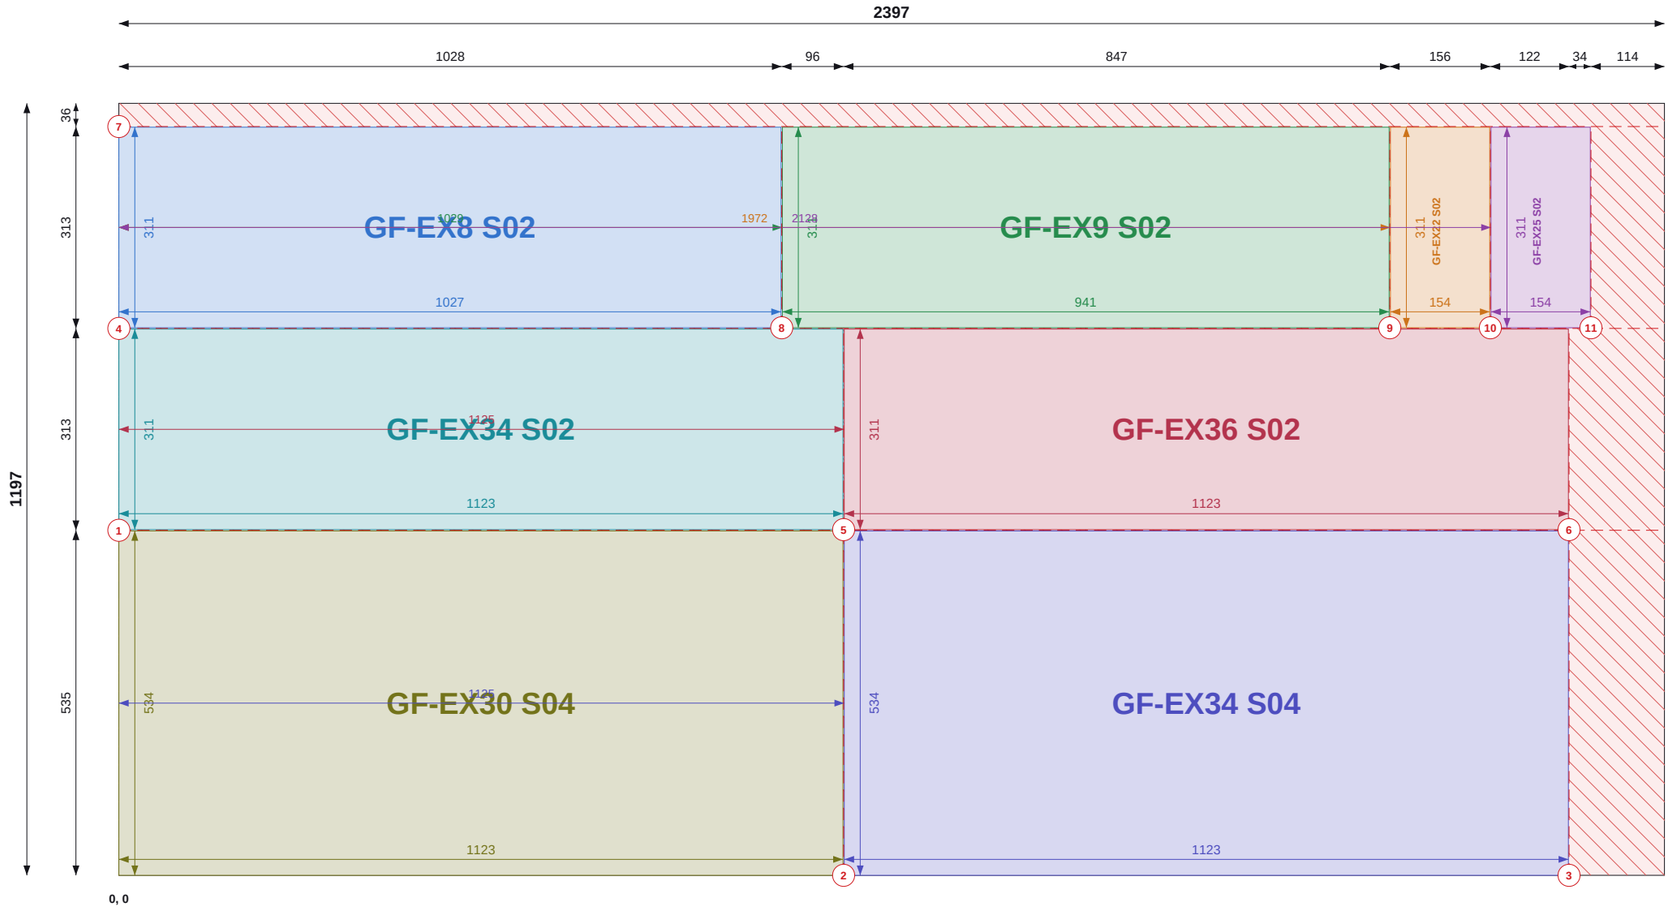


Top / left chains = saw cut positions (to cut centres). Coloured = part size and position.

## SHEET 48 OF 50

### THIS SHEET

| Item | Value |
|---|---|
| Parts | 8 |
| Used / waste | 90.8% / 0.26 m2 |
| Reusable offcuts | 0 |
| Saw cuts / shared | 11 / 7 |

### PIECES (POSITION = BOTTOM-LEFT CORNER)

| Label | Size | X, Y |
|---|---|---|
| GF-EX8 S02 | 1027 x 311 | 0, 849 |
| GF-EX9 S02 | 941 x 311 | 1029, 849 |
| GF-EX22 S02 | 154 x 311 | 1972, 849 |
| GF-EX25 S02 | 154 x 311 | 2128, 849 |
| GF-EX34 S02 | 1123 x 311 | 0, 536 |
| GF-EX36 S02 | 1123 x 311 | 1125, 536 |
| GF-EX30 S04 | 1123 x 534 | 0, 0 |
| GF-EX34 S04 | 1123 x 534 | 1125, 0 |

### NOTES

1. Cut from OSB/3 9mm 1197x2397, 2mm saw kerf. Viewed on the face; dimensions from the sheet's bottom-left corner (0,0). Red numbered lines = saw cuts in order, each edge to edge.
2. Coloured dimensions belong to the part of that colour: its width and height, and its position from the sheet edges. Raked parts: corner coordinates at each corner.
3. Red hatch = waste. Labels = panel + piece mark on the manufacture drawing.

### REVISIONS

| REV | DATE | DESCRIPTION |
|---|---|---|
| C01 | 14.09.26 | Construction issue |
| C02 | 14.09.26 | Roof trusses revised; SP diagonals added |
| C03 | 11.10.26 | FF windows coursed; steel + GP1 portal; steel drawings (ST) |
| C04 | 13.10.26 | Steel approved by the engineer: steel + steel timber drawings issued for construction |

TLS TIMBER FRAME
Design & Manufacture
Scan: 3D model + drawings

| CLIENT | PROJECT |
|---|---|
| MP Adams | MP Adams Plot 4, Eckington |


DRAWING TITLE
**OSB CUTTING - GROUND FLOOR - SHEET 48 OF 50**

OSB/3 9mm 1197x2397 | Ground Floor

| SCALE | SIZE | DATE | DRAWN |
|---|---|---|---|
| NTS | A3 | 13.10.26 | TS |

| STATUS | DRAWING No. | REV |
|---|---|---|
| CONSTRUCTION | P4-CP-OSB-01 / 48 | C04 |

Do not scale. All dimensions in mm. Check all dimensions on site.

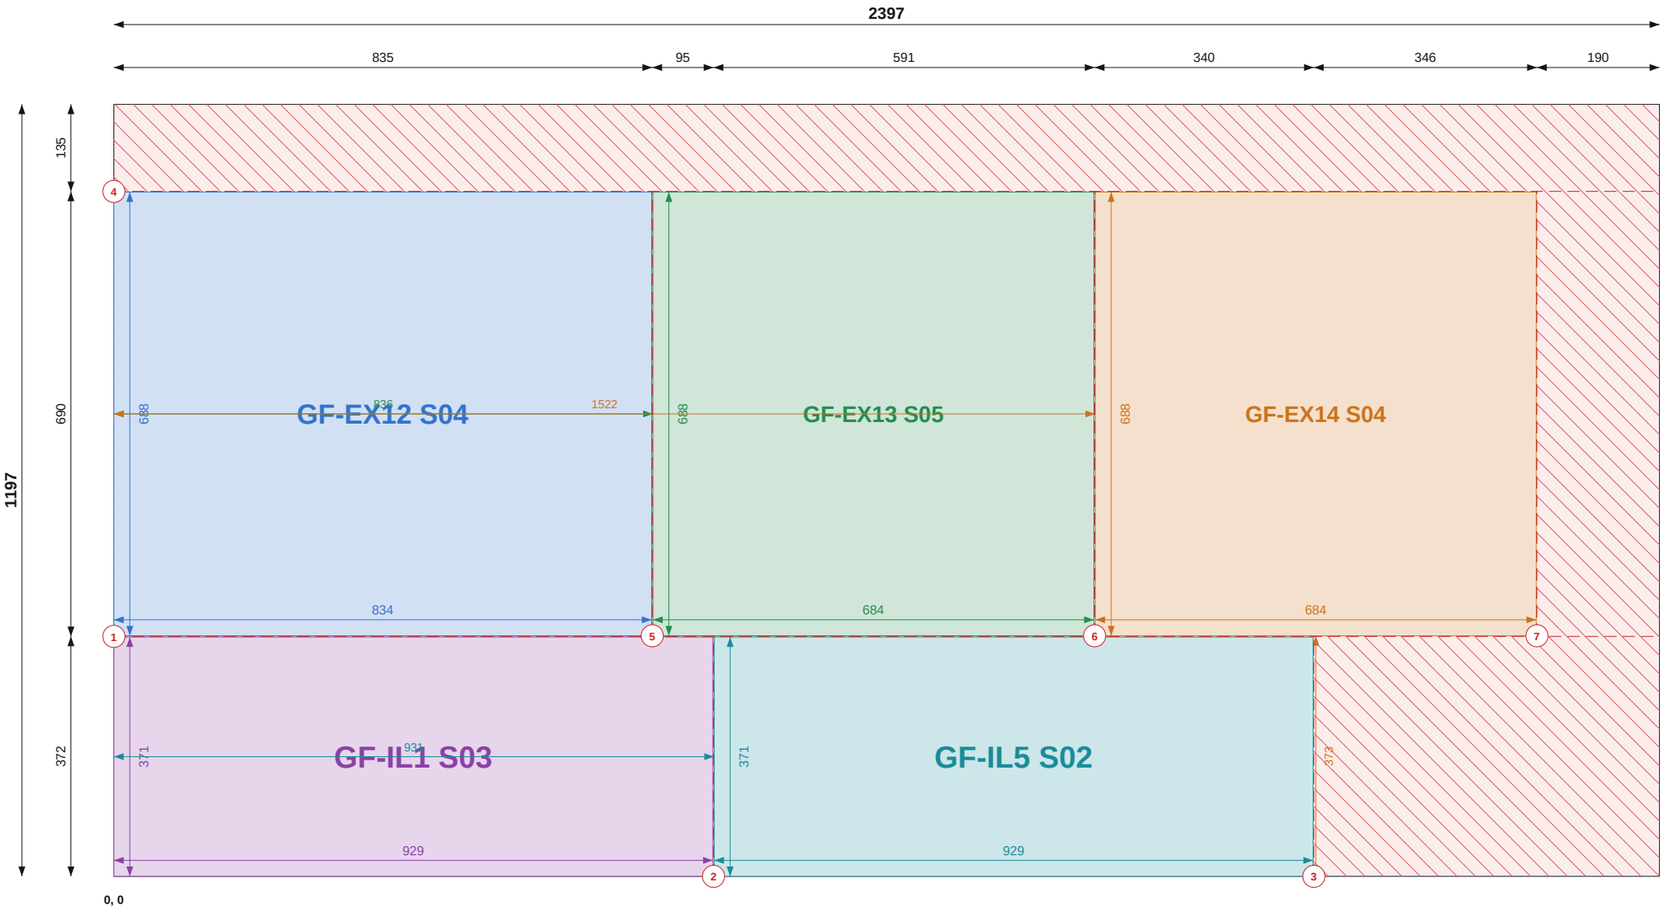


Top / left chains = saw cut positions (to cut centres). Coloured = part size and position.

## SHEET 49 OF 50

### THIS SHEET

| Item | Value |
|---|---|
| Parts | 5 |
| Used / waste | 76.8% / 0.66 m2 |
| Reusable offcuts | 1 |
| Saw cuts / shared | 7 / 4 |

### PIECES (POSITION = BOTTOM-LEFT CORNER)

| Label | Size | X, Y |
|---|---|---|
| GF-EX12 S04 | 688 x 834 | 0, 373 |
| GF-EX13 S05 | 688 x 684 | 836, 373 |
| GF-EX14 S04 | 688 x 684 | 1522, 373 |
| GF-IL1 S03 | 929 x 371 | 0, 0 |
| GF-IL5 S02 | 929 x 371 | 931, 0 |

### NOTES

1. Cut from OSB/3 9mm 1197x2397, 2mm saw kerf. Viewed on the face; dimensions from the sheet's bottom-left corner (0,0). Red numbered lines = saw cuts in order, each edge to edge.
2. Coloured dimensions belong to the part of that colour: its width and height, and its position from the sheet edges. Raked parts: corner coordinates at each corner.
3. Red hatch = waste. Labels = panel + piece mark on the manufacture drawing.

### REVISIONS

| REV | DATE | DESCRIPTION |
|---|---|---|
| C01 | 14.09.26 | Construction issue |
| C02 | 14.09.26 | Roof trusses revised; SP diagonals added |
| C03 | 11.10.26 | FF windows coursed; steel + GP1 portal; steel drawings (ST) |
| C04 | 13.10.26 | Steel approved by the engineer: steel + steel timber drawings issued for construction |

TLS TIMBER FRAME
Design & Manufacture
Scan: 3D model + drawings

| CLIENT | PROJECT |
|---|---|
| MP Adams | MP Adams Plot 4, Eckington |


DRAWING TITLE
**OSB CUTTING - GROUND FLOOR - SHEET 49 OF 50**

OSB/3 9mm 1197x2397 | Ground Floor

| SCALE | SIZE | DATE | DRAWN |
|---|---|---|---|
| NTS | A3 | 13.10.26 | TS |

| STATUS | DRAWING No. | REV |
|---|---|---|
| CONSTRUCTION | P4-CP-OSB-01 / 49 | C04 |

Do not scale. All dimensions in mm. Check all dimensions on site.

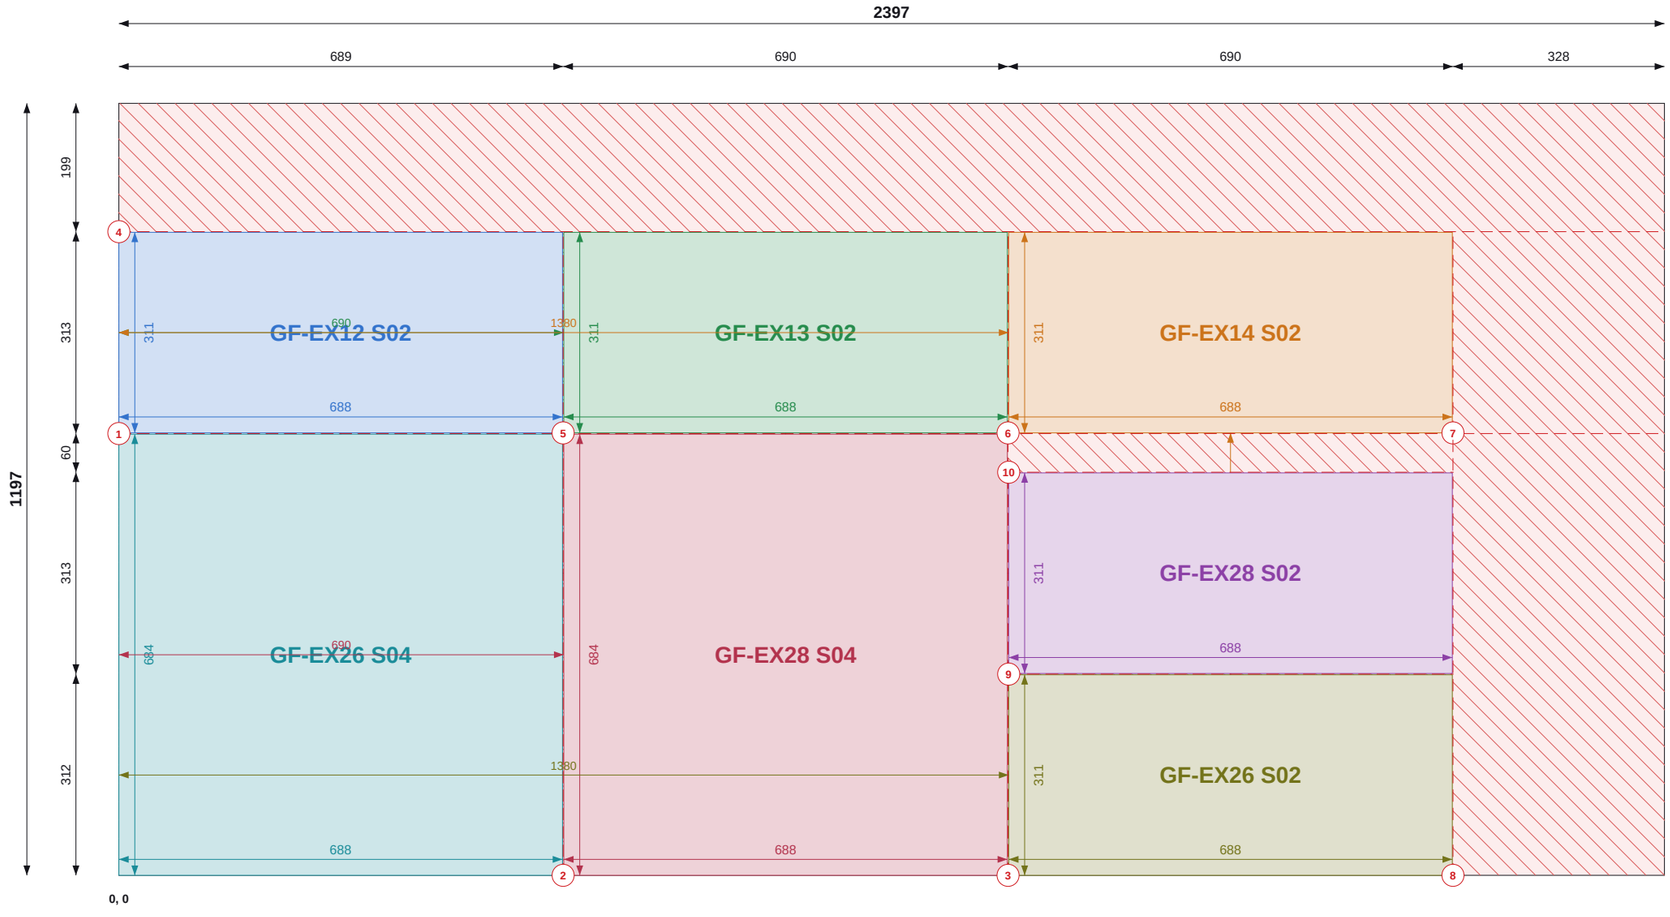


Top / left chains = saw cut positions (to cut centres). Coloured = part size and position.

## SHEET 50 OF 50

### THIS SHEET

| Item | Value |
|---|---|
| Parts | 7 |
| Used / waste | 70.1% / 0.86 m2 |
| Reusable offcuts | 2 |
| Saw cuts / shared | 10 / 6 |

### PIECES (POSITION = BOTTOM-LEFT CORNER)

| Label | Size | X, Y |
|---|---|---|
| GF-EX12 S02 | 688 x 311 | 0, 686 |
| GF-EX13 S02 | 688 x 311 | 690, 686 |
| GF-EX14 S02 | 688 x 311 | 1380, 686 |
| GF-EX28 S02 | 688 x 311 | 1380, 313 |
| GF-EX26 S04 | 688 x 684 | 0, 0 |
| GF-EX28 S04 | 688 x 684 | 690, 0 |
| GF-EX26 S02 | 688 x 311 | 1380, 0 |

### NOTES

1. Cut from OSB/3 9mm 1197x2397, 2mm saw kerf. Viewed on the face; dimensions from the sheet's bottom-left corner (0,0). Red numbered lines = saw cuts in order, each edge to edge.
2. Coloured dimensions belong to the part of that colour: its width and height, and its position from the sheet edges. Raked parts: corner coordinates at each corner.
3. Red hatch = waste. Labels = panel + piece mark on the manufacture drawing.

### REVISIONS

| REV | DATE | DESCRIPTION |
|---|---|---|
| C01 | 14.09.26 | Construction issue |
| C02 | 14.09.26 | Roof trusses revised; SP diagonals added |
| C03 | 11.10.26 | FF windows coursed; steel + GP1 portal; steel drawings (ST) |
| C04 | 13.10.26 | Steel approved by the engineer: steel + steel timber drawings issued for construction |

TLS TIMBER FRAME
Design & Manufacture
Scan: 3D model + drawings

| CLIENT | PROJECT |
|---|---|
| MP Adams | MP Adams Plot 4, Eckington |


DRAWING TITLE
**OSB CUTTING - GROUND FLOOR - SHEET 50 OF 50**

OSB/3 9mm 1197x2397 | Ground Floor

| SCALE | SIZE | DATE | DRAWN |
|---|---|---|---|
| NTS | A3 | 13.10.26 | TS |

| STATUS | DRAWING No. | REV |
|---|---|---|
| CONSTRUCTION | P4-CP-OSB-01 / 50 | C04 |

Do not scale. All dimensions in mm. Check all dimensions on site.

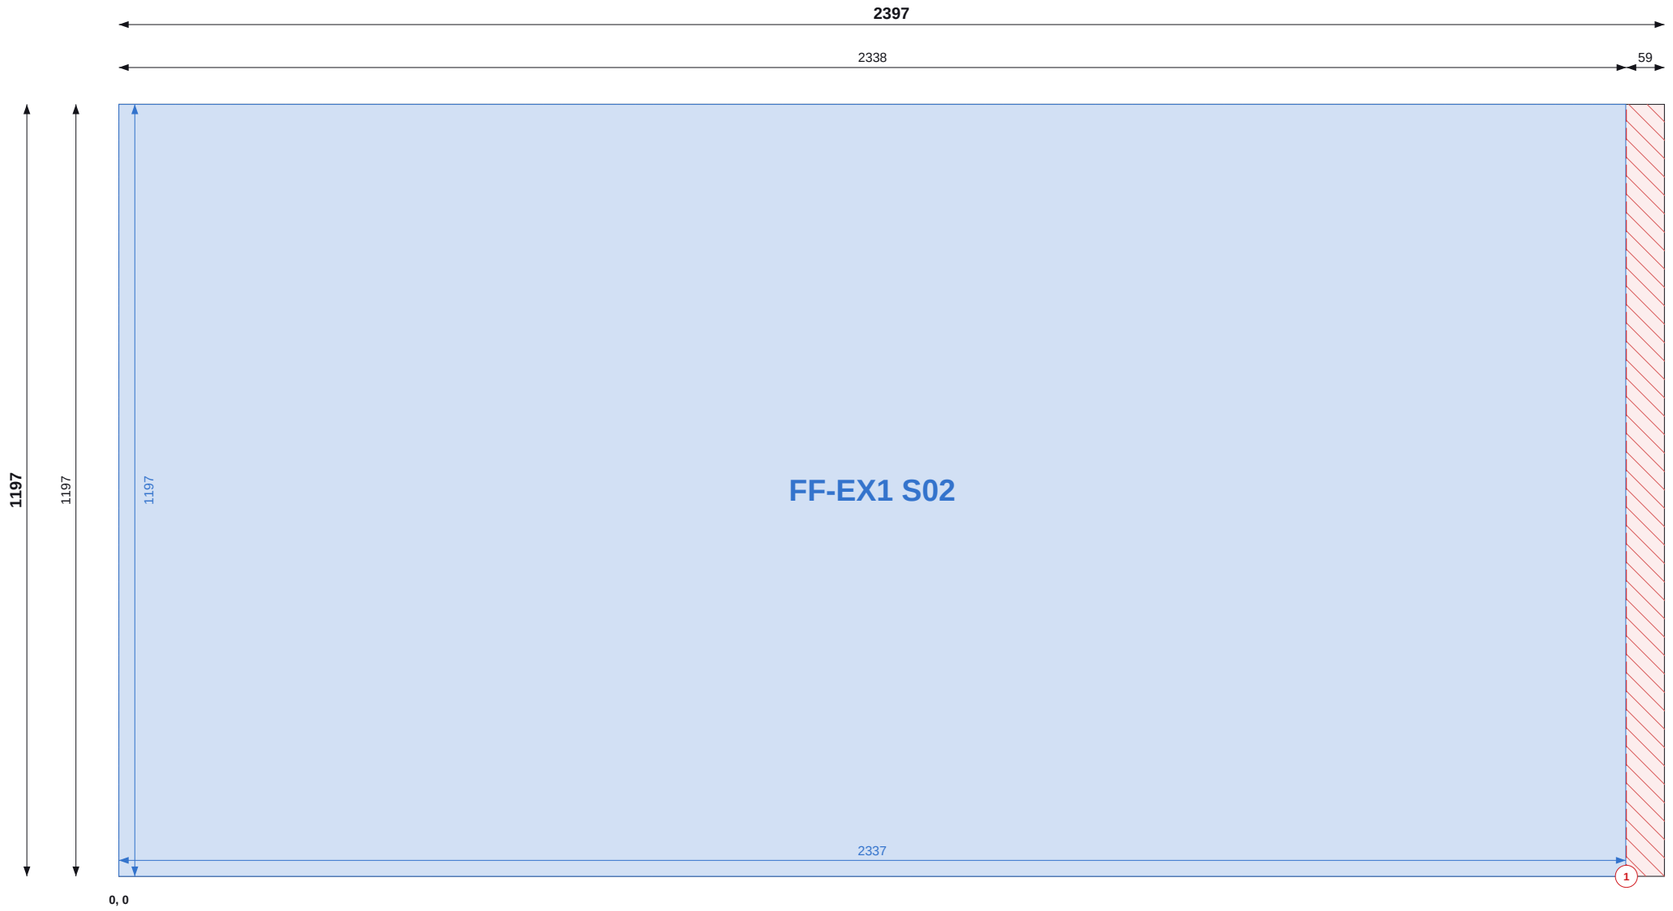


Top / left chains = saw cut positions (to cut centres). Coloured = part size and position.

Do not scale. All dimensions in mm. Check all dimensions on site.

## SHEET 1 OF 31

### THIS SHEET

| Item | Value |
|---|---|
| Parts | 1 |
| Used / waste | 97.5% / 0.07 m2 |
| Reusable offcuts | 0 |
| Saw cuts / shared | 1 / 0 |

### PIECES (POSITION = BOTTOM-LEFT CORNER)

| Label | Size | X, Y |
|---|---|---|
| FF-EX1 S02 | 1197 x 2337 | 0, 0 |

### FIRST FLOOR TOTALS

| Item | Value |
|---|---|
| Sheets / pieces | 31 / 57 |
| Yield / waste | 86.4% / 12.14 m2 |
| Saw cuts / shared / on stock edge | 86 / 26 / 90 |

### NOTES

1. Cut from OSB/3 9mm 1197x2397, 2mm saw kerf. Viewed on the face; dimensions from the sheet's bottom-left corner (0,0). Red numbered lines = saw cuts in order, each edge to edge.
2. Coloured dimensions belong to the part of that colour: its width and height, and its position from the sheet edges. Raked parts: corner coordinates at each corner.
3. Red hatch = waste. Labels = panel + piece mark on the manufacture drawing.

### REVISIONS

| REV | DATE | DESCRIPTION |
|---|---|---|
| C01 | 14.09.26 | Construction issue |
| C02 | 14.09.26 | Roof trusses revised; SP diagonals added |
| C03 | 11.10.26 | FF windows coursed; steel + GP1 portal; steel drawings (ST) |
| C04 | 13.10.26 | Steel approved by the engineer: steel + steel timber drawings issued for construction |

TLS TIMBER FRAME
Design & Manufacture
Scan: 3D model + drawings

| CLIENT | PROJECT |
|---|---|
| MP Adams | MP Adams Plot 4, Eckington |

DRAWING TITLE

**OSB CUTTING - FIRST FLOOR - SHEET 1 OF 31**

OSB/3 9mm 1197x2397 | First Floor

| SCALE | SIZE | DATE | DRAWN |
|---|---|---|---|
| NTS | A3 | 13.10.26 | TS |

| STATUS | DRAWING No. | REV |
|---|---|---|
| CONSTRUCTION | P4-CP-OSB-02 / 01 | C04 |




Top / left chains = saw cut positions (to cut centres). Coloured = part size and position.

Do not scale. All dimensions in mm. Check all dimensions on site.

## SHEET 2 OF 31

### THIS SHEET

| Item | Value |
|---|---|
| Parts | 1 |
| Used / waste | 97.5% / 0.07 m2 |
| Reusable offcuts | 0 |
| Saw cuts / shared | 1 / 0 |

### PIECES (POSITION = BOTTOM-LEFT CORNER)

| Label | Size | X, Y |
|---|---|---|
| FF-EX15 S02 | 1197 x 2337 | 0, 0 |

### NOTES

1. Cut from OSB/3 9mm 1197x2397, 2mm saw kerf. Viewed on the face; dimensions from the sheet's bottom-left corner (0,0). Red numbered lines = saw cuts in order, each edge to edge.
2. Coloured dimensions belong to the part of that colour: its width and height, and its position from the sheet edges. Raked parts: corner coordinates at each corner.
3. Red hatch = waste. Labels = panel + piece mark on the manufacture drawing.

### REVISIONS

| REV | DATE | DESCRIPTION |
|---|---|---|
| C01 | 14.09.26 | Construction issue |
| C02 | 14.09.26 | Roof trusses revised; SP diagonals added |
| C03 | 11.10.26 | FF windows coursed; steel + GP1 portal; steel drawings (ST) |
| C04 | 13.10.26 | Steel approved by the engineer: steel + steel timber drawings issued for construction |

TLS TIMBER FRAME
Design & Manufacture
Scan: 3D model + drawings

| CLIENT | PROJECT |
|---|---|
| MP Adams | MP Adams Plot 4, Eckington |


DRAWING TITLE

# OSB CUTTING - FIRST FLOOR - SHEET 2 OF 31

OSB/3 9mm 1197x2397 | First Floor

| SCALE | SIZE | DATE | DRAWN |
|---|---|---|---|
| NTS | A3 | 13.10.26 | TS |

| STATUS | DRAWING No. | REV |
|---|---|---|
| CONSTRUCTION | P4-CP-OSB-02 / 02 | C04 |

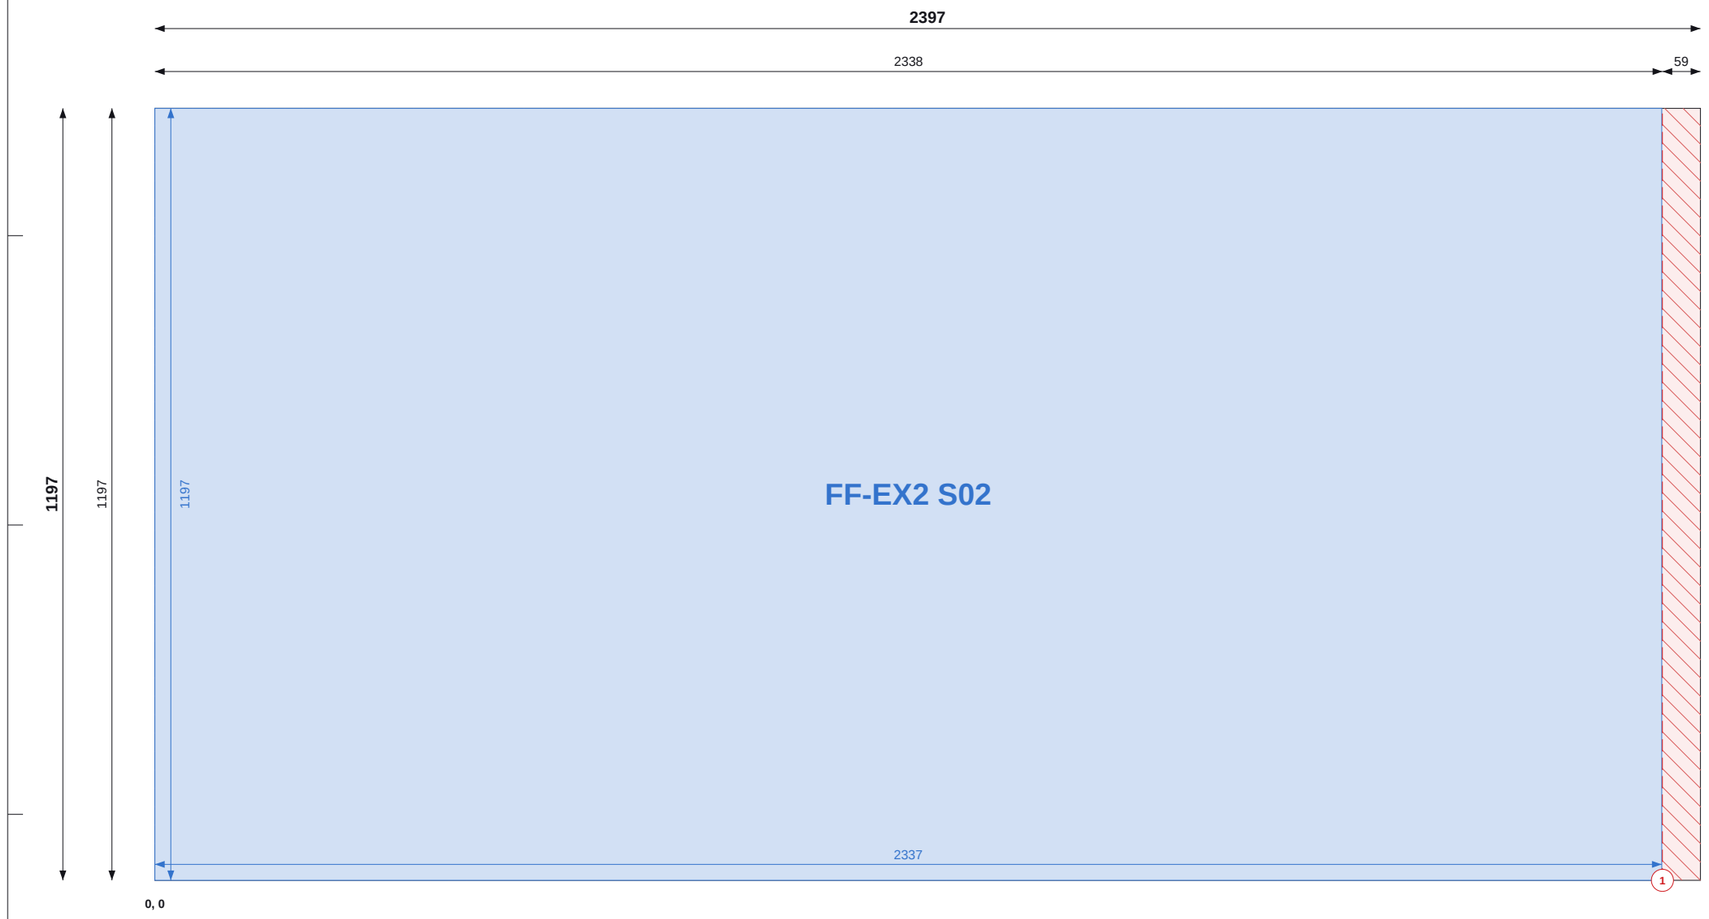


Top / left chains = saw cut positions (to cut centres). Coloured = part size and position.

Do not scale. All dimensions in mm. Check all dimensions on site.

## SHEET 3 OF 31

### THIS SHEET

| Item | Value |
|---|---|
| Parts | 1 |
| Used / waste | 97.5% / 0.07 m2 |
| Reusable offcuts | 0 |
| Saw cuts / shared | 1 / 0 |

### PIECES (POSITION = BOTTOM-LEFT CORNER)

| Label | Size | X, Y |
|---|---|---|
| FF-EX2 S02 | 1197 x 2337 | 0, 0 |

### NOTES

1. Cut from OSB/3 9mm 1197x2397, 2mm saw kerf. Viewed on the face; dimensions from the sheet's bottom-left corner (0,0). Red numbered lines = saw cuts in order, each edge to edge.
2. Coloured dimensions belong to the part of that colour: its width and height, and its position from the sheet edges. Raked parts: corner coordinates at each corner.
3. Red hatch = waste. Labels = panel + piece mark on the manufacture drawing.

### REVISIONS

| REV | DATE | DESCRIPTION |
|---|---|---|
| C01 | 14.09.26 | Construction issue |
| C02 | 14.09.26 | Roof trusses revised; SP diagonals added |
| C03 | 11.10.26 | FF windows coursed; steel + GP1 portal; steel drawings (ST) |
| C04 | 13.10.26 | Steel approved by the engineer: steel + steel timber drawings issued for construction |

TLS TIMBER FRAME
Design & Manufacture
Scan: 3D model + drawings

| CLIENT | PROJECT |
|---|---|
| MP Adams | MP Adams Plot 4, Eckington |


DRAWING TITLE

**OSB CUTTING - FIRST FLOOR - SHEET 3 OF 31**

OSB/3 9mm 1197x2397 | First Floor

| SCALE | SIZE | DATE | DRAWN |
|---|---|---|---|
| NTS | A3 | 13.10.26 | TS |

| STATUS | DRAWING No. | REV |
|---|---|---|
| CONSTRUCTION | P4-CP-OSB-02 / 03 | C04 |

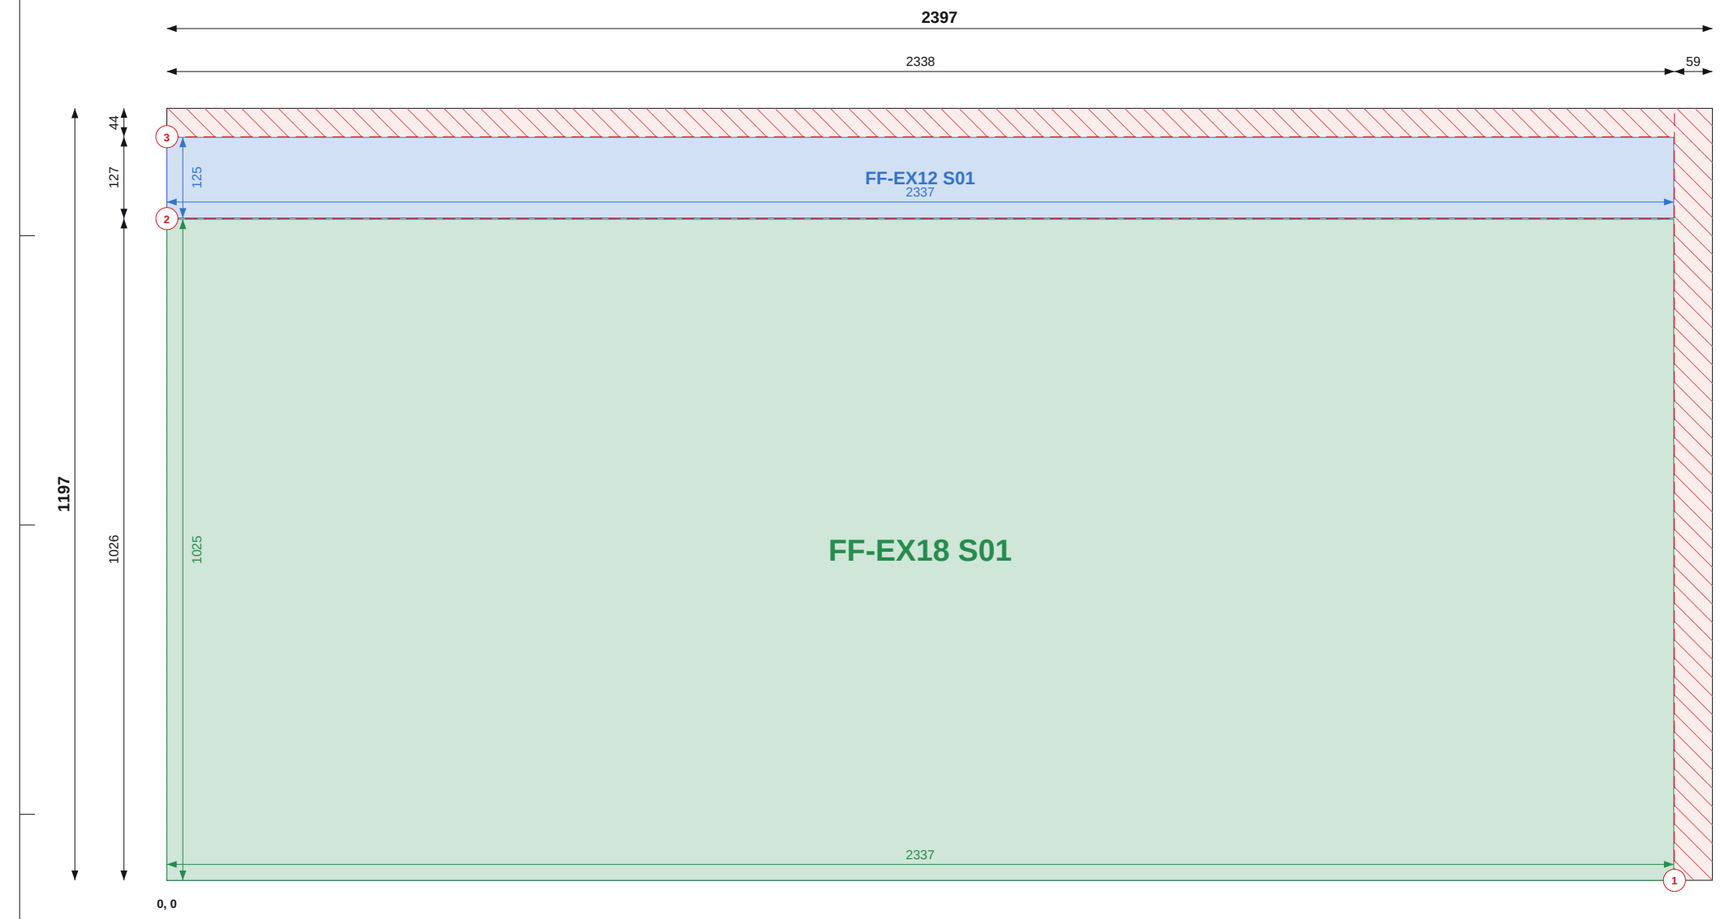


Top / left chains = saw cut positions (to cut centres). Coloured = part size and position.

Do not scale. All dimensions in mm. Check all dimensions on site.

## SHEET 4 OF 31

### THIS SHEET

| Item | Value |
|---|---|
| Parts | 2 |
| Used / waste | 93.7% / 0.18 m2 |
| Reusable offcuts | 0 |
| Saw cuts / shared | 3 / 1 |

### PIECES (POSITION = BOTTOM-LEFT CORNER)

| Label | Size | X, Y |
|---|---|---|
| FF-EX12 S01 | 125 x 2337 | 0, 1027 |
| FF-EX18 S01 | 1025 x 2337 | 0, 0 |

### NOTES

1. Cut from OSB/3 9mm 1197x2397, 2mm saw kerf. Viewed on the face; dimensions from the sheet's bottom-left corner (0,0). Red numbered lines = saw cuts in order, each edge to edge.
2. Coloured dimensions belong to the part of that colour: its width and height, and its position from the sheet edges. Raked parts: corner coordinates at each corner.
3. Red hatch = waste. Labels = panel + piece mark on the manufacture drawing.

### REVISIONS

| REV | DATE | DESCRIPTION |
|---|---|---|
| C01 | 14.09.26 | Construction issue |
| C02 | 14.09.26 | Roof trusses revised; SP diagonals added |
| C03 | 11.10.26 | FF windows coursed; steel + GP1 portal; steel drawings (ST) |
| C04 | 13.10.26 | Steel approved by the engineer: steel + steel timber drawings issued for construction |

TLS TIMBER FRAME
Design & Manufacture
Scan: 3D model + drawings

| CLIENT | PROJECT |
|---|---|
| MP Adams | MP Adams Plot 4, Eckington |


DRAWING TITLE

**OSB CUTTING - FIRST FLOOR - SHEET 4 OF 31**

OSB/3 9mm 1197x2397 | First Floor

| SCALE | SIZE | DATE | DRAWN |
|---|---|---|---|
| NTS | A3 | 13.10.26 | TS |

| STATUS | DRAWING No. | REV |
|---|---|---|
| CONSTRUCTION | P4-CP-OSB-02 / 04 | C04 |

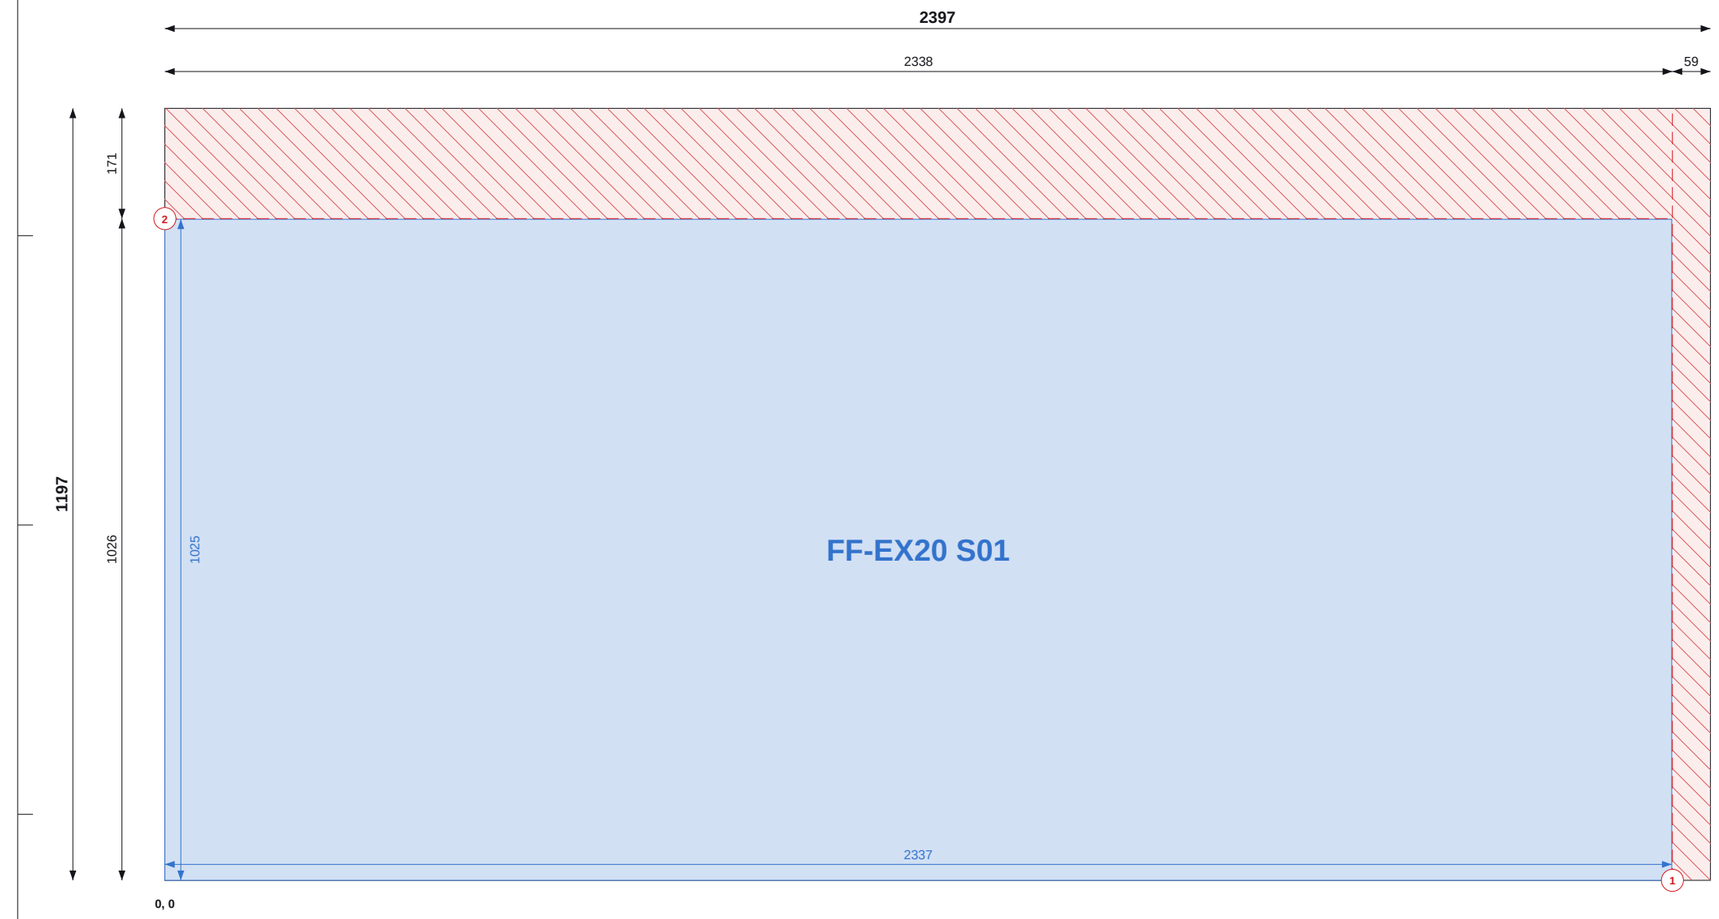


Top / left chains = saw cut positions (to cut centres). Coloured = part size and position.

## SHEET 5 OF 31

### THIS SHEET

| Item | Value |
|---|---|
| Parts | 1 |
| Used / waste | 83.5% / 0.47 m2 |
| Reusable offcuts | 0 |
| Saw cuts / shared | 2 / 0 |

### PIECES (POSITION = BOTTOM-LEFT CORNER)

| Label | Size | X, Y |
|---|---|---|
| FF-EX20 S01 | 1025 x 2337 | 0, 0 |

### NOTES

1. Cut from OSB/3 9mm 1197x2397, 2mm saw kerf. Viewed on the face; dimensions from the sheet's bottom-left corner (0,0). Red numbered lines = saw cuts in order, each edge to edge.
2. Coloured dimensions belong to the part of that colour: its width and height, and its position from the sheet edges. Raked parts: corner coordinates at each corner.
3. Red hatch = waste. Labels = panel + piece mark on the manufacture drawing.

### REVISIONS

| REV | DATE | DESCRIPTION |
|---|---|---|
| C01 | 14.09.26 | Construction issue |
| C02 | 14.09.26 | Roof trusses revised; SP diagonals added |
| C03 | 11.10.26 | FF windows coursed; steel + GP1 portal; steel drawings (ST) |
| C04 | 13.10.26 | Steel approved by the engineer: steel + steel timber drawings issued for construction |

TLS TIMBER FRAME
Design & Manufacture
Scan: 3D model + drawings

| CLIENT | PROJECT |
|---|---|
| MP Adams | MP Adams Plot 4, Eckington |

DRAWING TITLE


**OSB CUTTING - FIRST FLOOR - SHEET 5 OF 31**

OSB/3 9mm 1197x2397 | First Floor

| SCALE | SIZE | DATE | DRAWN |
|---|---|---|---|
| NTS | A3 | 13.10.26 | TS |

| STATUS | DRAWING No. | REV |
|---|---|---|
| CONSTRUCTION | P4-CP-OSB-02 / 05 | C04 |

Do not scale. All dimensions in mm. Check all dimensions on site.

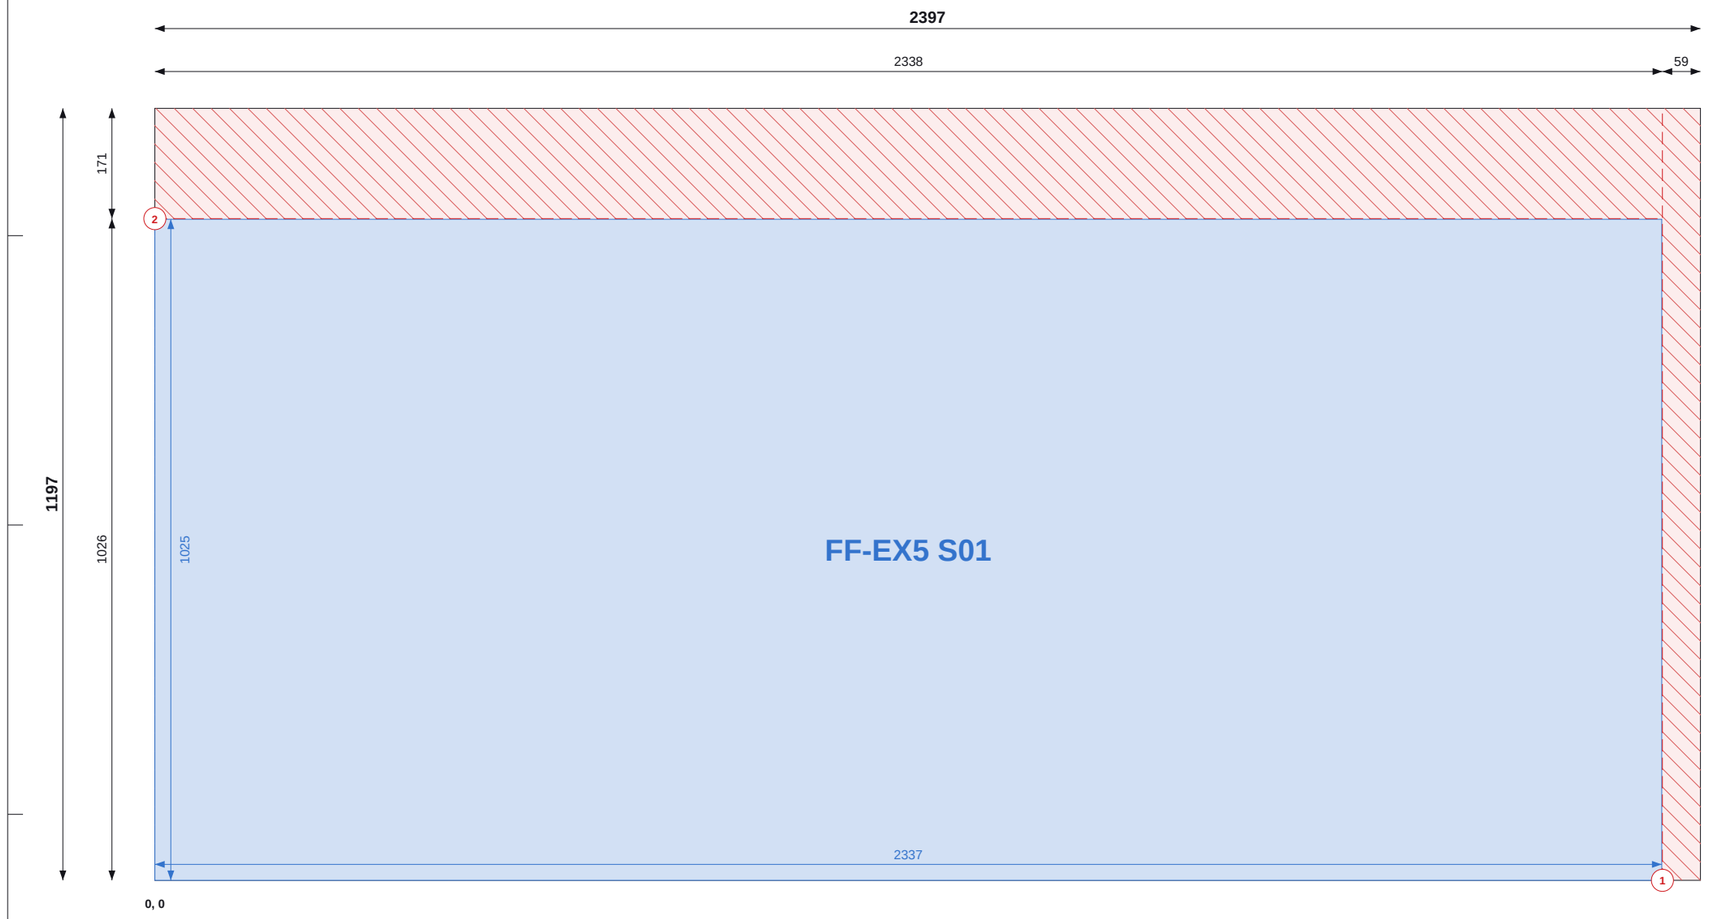


Top / left chains = saw cut positions (to cut centres). Coloured = part size and position.

Do not scale. All dimensions in mm. Check all dimensions on site.

## SHEET 6 OF 31

### THIS SHEET

| Item | Value |
|---|---|
| Parts | 1 |
| Used / waste | 83.5% / 0.47 m2 |
| Reusable offcuts | 0 |
| Saw cuts / shared | 2 / 0 |

### PIECES (POSITION = BOTTOM-LEFT CORNER)

| Label | Size | X, Y |
|---|---|---|
| FF-EX5 S01 | 1025 x 2337 | 0, 0 |

### NOTES

1. Cut from OSB/3 9mm 1197x2397, 2mm saw kerf. Viewed on the face; dimensions from the sheet's bottom-left corner (0,0). Red numbered lines = saw cuts in order, each edge to edge.
2. Coloured dimensions belong to the part of that colour: its width and height, and its position from the sheet edges. Raked parts: corner coordinates at each corner.
3. Red hatch = waste. Labels = panel + piece mark on the manufacture drawing.

### REVISIONS

| REV | DATE | DESCRIPTION |
|---|---|---|
| C01 | 14.09.26 | Construction issue |
| C02 | 14.09.26 | Roof trusses revised; SP diagonals added |
| C03 | 11.10.26 | FF windows coursed; steel + GP1 portal; steel drawings (ST) |
| C04 | 13.10.26 | Steel approved by the engineer: steel + steel timber drawings issued for construction |

TLS TIMBER FRAME
Design & Manufacture
Scan: 3D model + drawings

| CLIENT | PROJECT |
|---|---|
| MP Adams | MP Adams Plot 4, Eckington |


DRAWING TITLE

**OSB CUTTING - FIRST FLOOR - SHEET 6 OF 31**

OSB/3 9mm 1197x2397 | First Floor

| SCALE | SIZE | DATE | DRAWN |
|---|---|---|---|
| NTS | A3 | 13.10.26 | TS |

| STATUS | DRAWING No. | REV |
|---|---|---|
| CONSTRUCTION | P4-CP-OSB-02 / 06 | C04 |

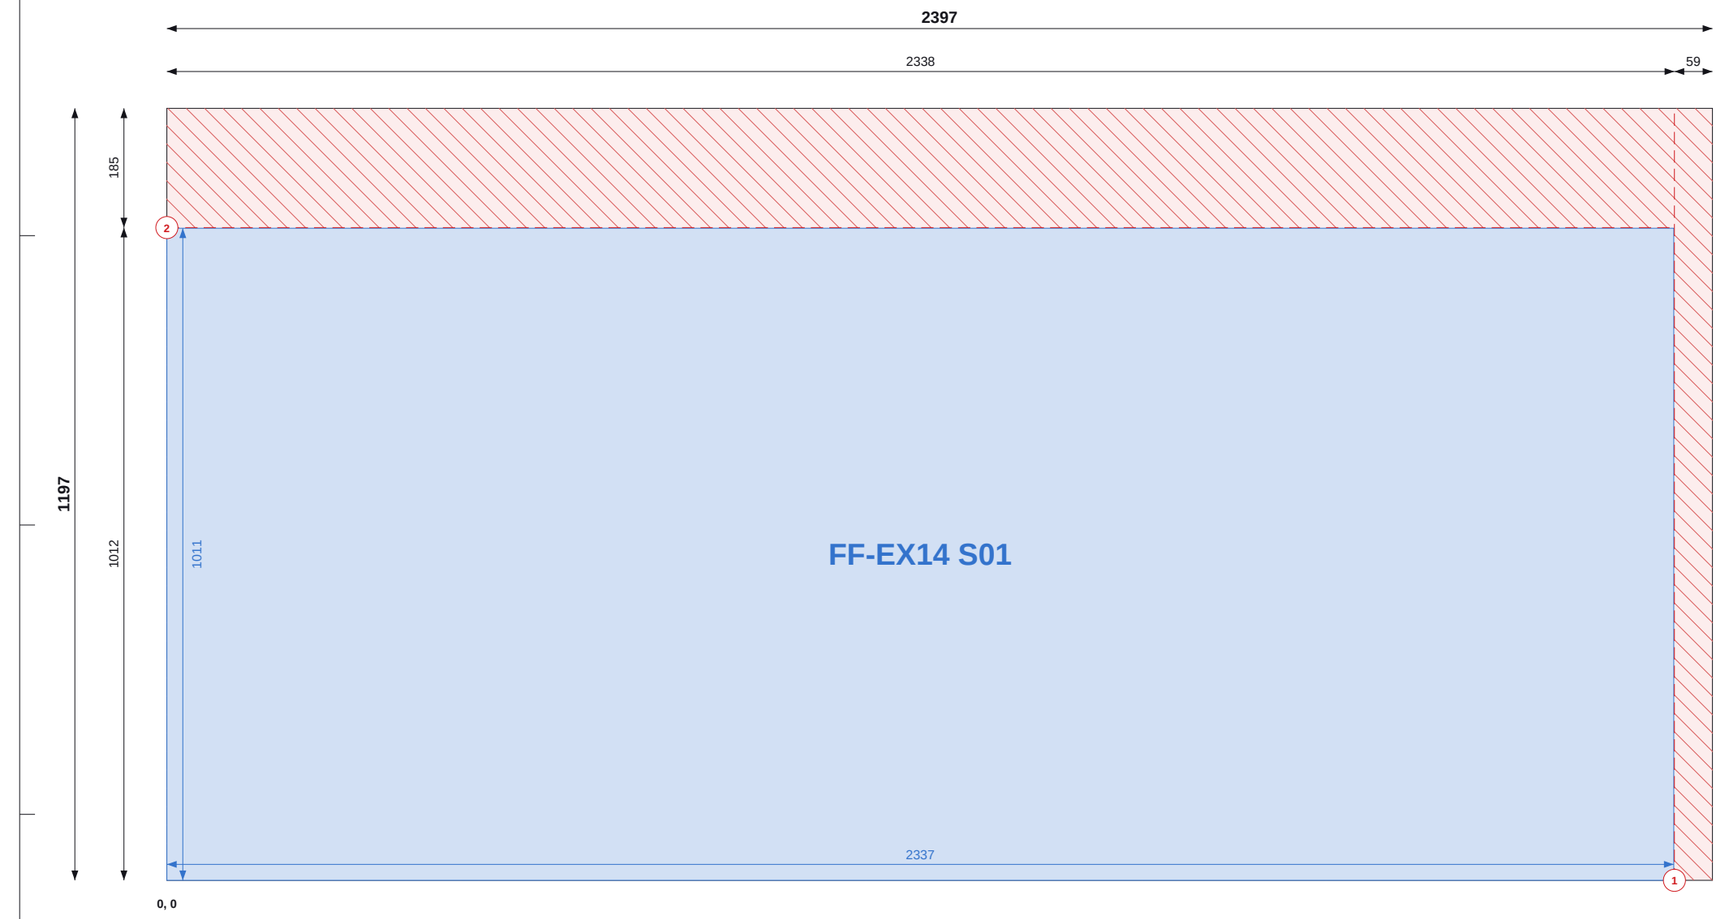


Top / left chains = saw cut positions (to cut centres). Coloured = part size and position.

Do not scale. All dimensions in mm. Check all dimensions on site.

## SHEET 7 OF 31

### THIS SHEET

| Item | Value |
|---|---|
| Parts | 1 |
| Used / waste | 82.4% / 0.51 m2 |
| Reusable offcuts | 0 |
| Saw cuts / shared | 2 / 0 |

### PIECES (POSITION = BOTTOM-LEFT CORNER)

| Label | Size | X, Y |
|---|---|---|
| FF-EX14 S01 | 1011 x 2337 | 0, 0 |

### NOTES

1. Cut from OSB/3 9mm 1197x2397, 2mm saw kerf. Viewed on the face; dimensions from the sheet's bottom-left corner (0,0). Red numbered lines = saw cuts in order, each edge to edge.
2. Coloured dimensions belong to the part of that colour: its width and height, and its position from the sheet edges. Raked parts: corner coordinates at each corner.
3. Red hatch = waste. Labels = panel + piece mark on the manufacture drawing.

### REVISIONS

| REV | DATE | DESCRIPTION |
|---|---|---|
| C01 | 14.09.26 | Construction issue |
| C02 | 14.09.26 | Roof trusses revised; SP diagonals added |
| C03 | 11.10.26 | FF windows coursed; steel + GP1 portal; steel drawings (ST) |
| C04 | 13.10.26 | Steel approved by the engineer: steel + steel timber drawings issued for construction |

TLS TIMBER FRAME
Design & Manufacture
Scan: 3D model + drawings

| CLIENT | PROJECT |
|---|---|
| MP Adams | MP Adams Plot 4, Eckington |


DRAWING TITLE

**OSB CUTTING - FIRST FLOOR - SHEET 7 OF 31**

OSB/3 9mm 1197x2397 | First Floor

| SCALE | SIZE | DATE | DRAWN |
|---|---|---|---|
| NTS | A3 | 13.10.26 | TS |

| STATUS | DRAWING No. | REV |
|---|---|---|
| CONSTRUCTION | P4-CP-OSB-02 / 07 | C04 |

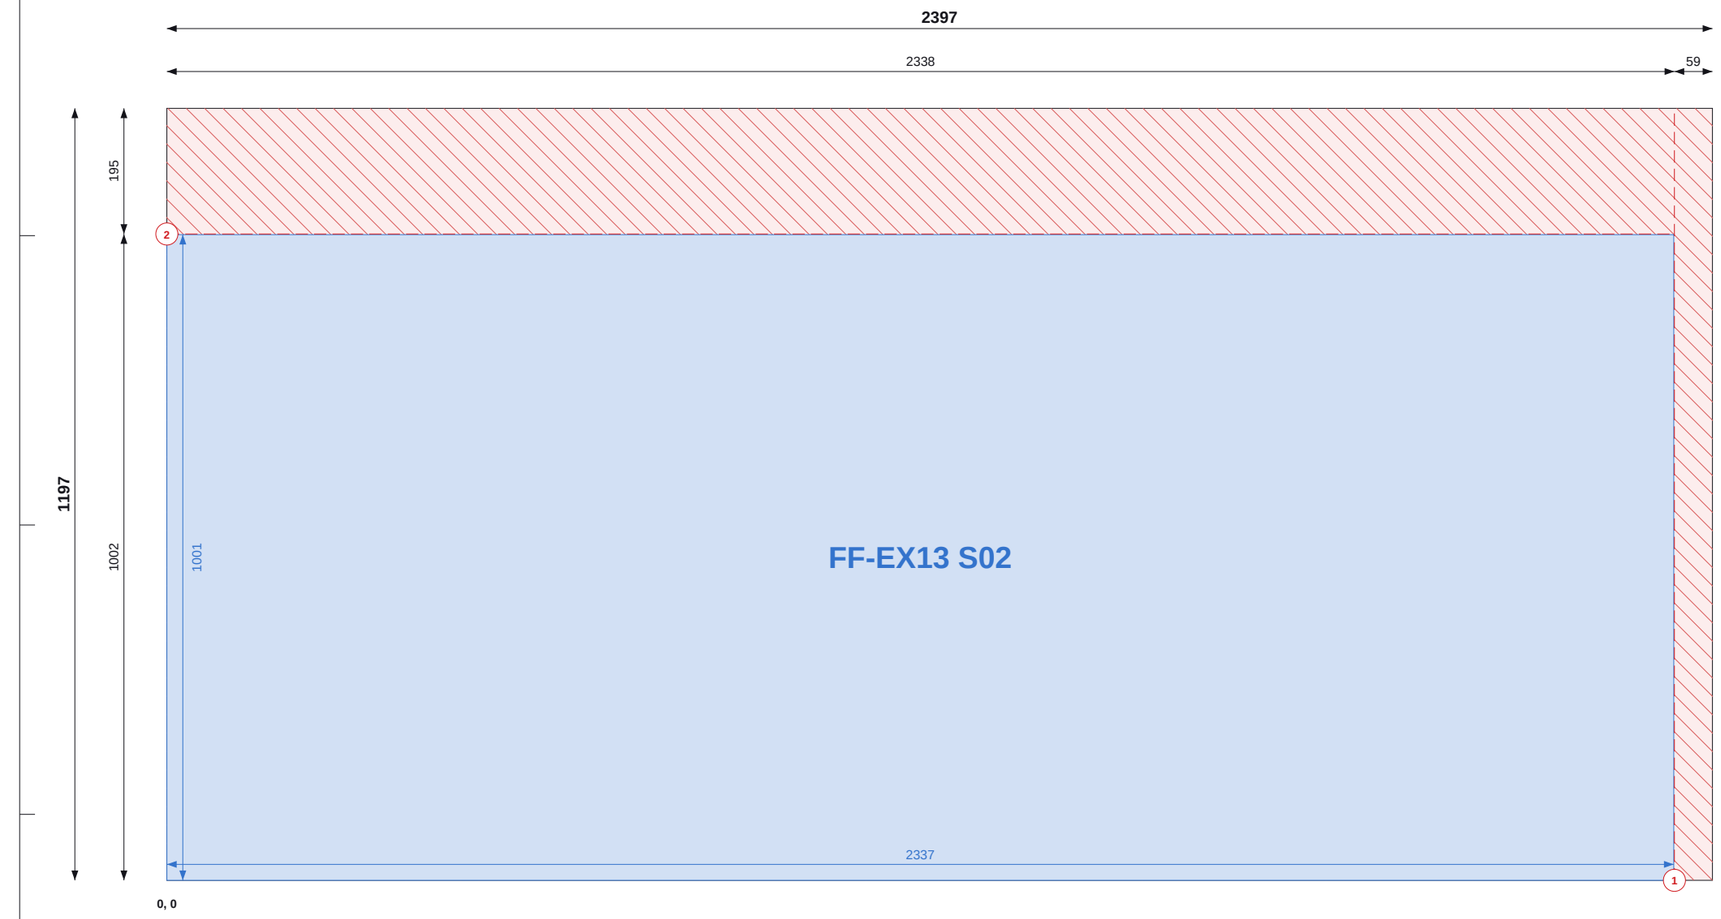


Top / left chains = saw cut positions (to cut centres). Coloured = part size and position.

Do not scale. All dimensions in mm. Check all dimensions on site.

## SHEET 8 OF 31

### THIS SHEET

| Item | Value |
|---|---|
| Parts | 1 |
| Used / waste | 81.5% / 0.53 m2 |
| Reusable offcuts | 0 |
| Saw cuts / shared | 2 / 0 |

### PIECES (POSITION = BOTTOM-LEFT CORNER)

| Label | Size | X, Y |
|---|---|---|
| FF-EX13 S02 | 1001 x 2337 | 0, 0 |

### NOTES

1. Cut from OSB/3 9mm 1197x2397, 2mm saw kerf. Viewed on the face; dimensions from the sheet's bottom-left corner (0,0). Red numbered lines = saw cuts in order, each edge to edge.
2. Coloured dimensions belong to the part of that colour: its width and height, and its position from the sheet edges. Raked parts: corner coordinates at each corner.
3. Red hatch = waste. Labels = panel + piece mark on the manufacture drawing.

### REVISIONS

| REV | DATE | DESCRIPTION |
|---|---|---|
| C01 | 14.09.26 | Construction issue |
| C02 | 14.09.26 | Roof trusses revised; SP diagonals added |
| C03 | 11.10.26 | FF windows coursed; steel + GP1 portal; steel drawings (ST) |
| C04 | 13.10.26 | Steel approved by the engineer: steel + steel timber drawings issued for construction |

TLS TIMBER FRAME
Design & Manufacture
Scan: 3D model + drawings

| CLIENT | PROJECT |
|---|---|
| MP Adams | MP Adams Plot 4, Eckington |


DRAWING TITLE

**OSB CUTTING - FIRST FLOOR - SHEET 8 OF 31**

OSB/3 9mm 1197x2397 | First Floor

| SCALE | SIZE | DATE | DRAWN |
|---|---|---|---|
| NTS | A3 | 13.10.26 | TS |

| STATUS | DRAWING No. | REV |
|---|---|---|
| CONSTRUCTION | P4-CP-OSB-02 / 08 | C04 |

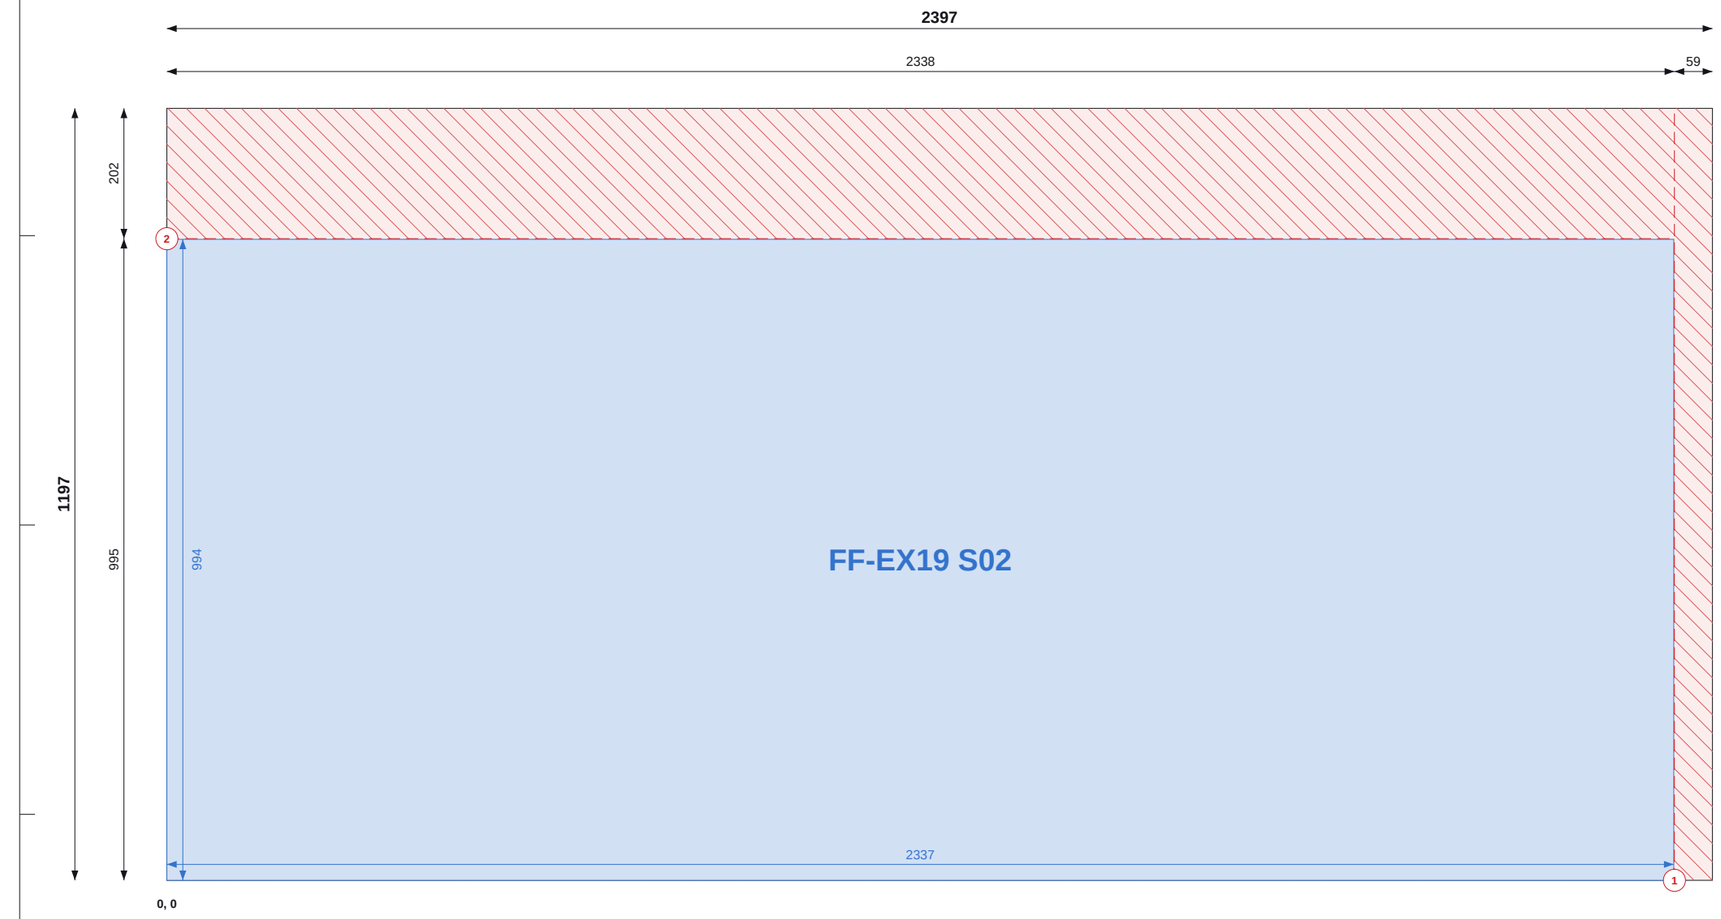


Top / left chains = saw cut positions (to cut centres). Coloured = part size and position.

Do not scale. All dimensions in mm. Check all dimensions on site.

## SHEET 9 OF 31

### THIS SHEET

| Item | Value |
|---|---|
| Parts | 1 |
| Used / waste | 81.0% / 0.55 m2 |
| Reusable offcuts | 0 |
| Saw cuts / shared | 2 / 0 |

### PIECES (POSITION = BOTTOM-LEFT CORNER)

| Label | Size | X, Y |
|---|---|---|
| FF-EX19 S02 | 994 x 2337 | 0, 0 |

### NOTES

1. Cut from OSB/3 9mm 1197x2397, 2mm saw kerf. Viewed on the face; dimensions from the sheet's bottom-left corner (0,0). Red numbered lines = saw cuts in order, each edge to edge.
2. Coloured dimensions belong to the part of that colour: its width and height, and its position from the sheet edges. Raked parts: corner coordinates at each corner.
3. Red hatch = waste. Labels = panel + piece mark on the manufacture drawing.

### REVISIONS

| REV | DATE | DESCRIPTION |
|---|---|---|
| C01 | 14.09.26 | Construction issue |
| C02 | 14.09.26 | Roof trusses revised; SP diagonals added |
| C03 | 11.10.26 | FF windows coursed; steel + GP1 portal; steel drawings (ST) |
| C04 | 13.10.26 | Steel approved by the engineer: steel + steel timber drawings issued for construction |

TLS TIMBER FRAME
Design & Manufacture
Scan: 3D model + drawings

| CLIENT | PROJECT |
|---|---|
| MP Adams | MP Adams Plot 4, Eckington |


DRAWING TITLE

**OSB CUTTING - FIRST FLOOR - SHEET 9 OF 31**

OSB/3 9mm 1197x2397 | First Floor

| SCALE | SIZE | DATE | DRAWN |
|---|---|---|---|
| NTS | A3 | 13.10.26 | TS |

| STATUS | DRAWING No. | REV |
|---|---|---|
| CONSTRUCTION | P4-CP-OSB-02 / 09 | C04 |

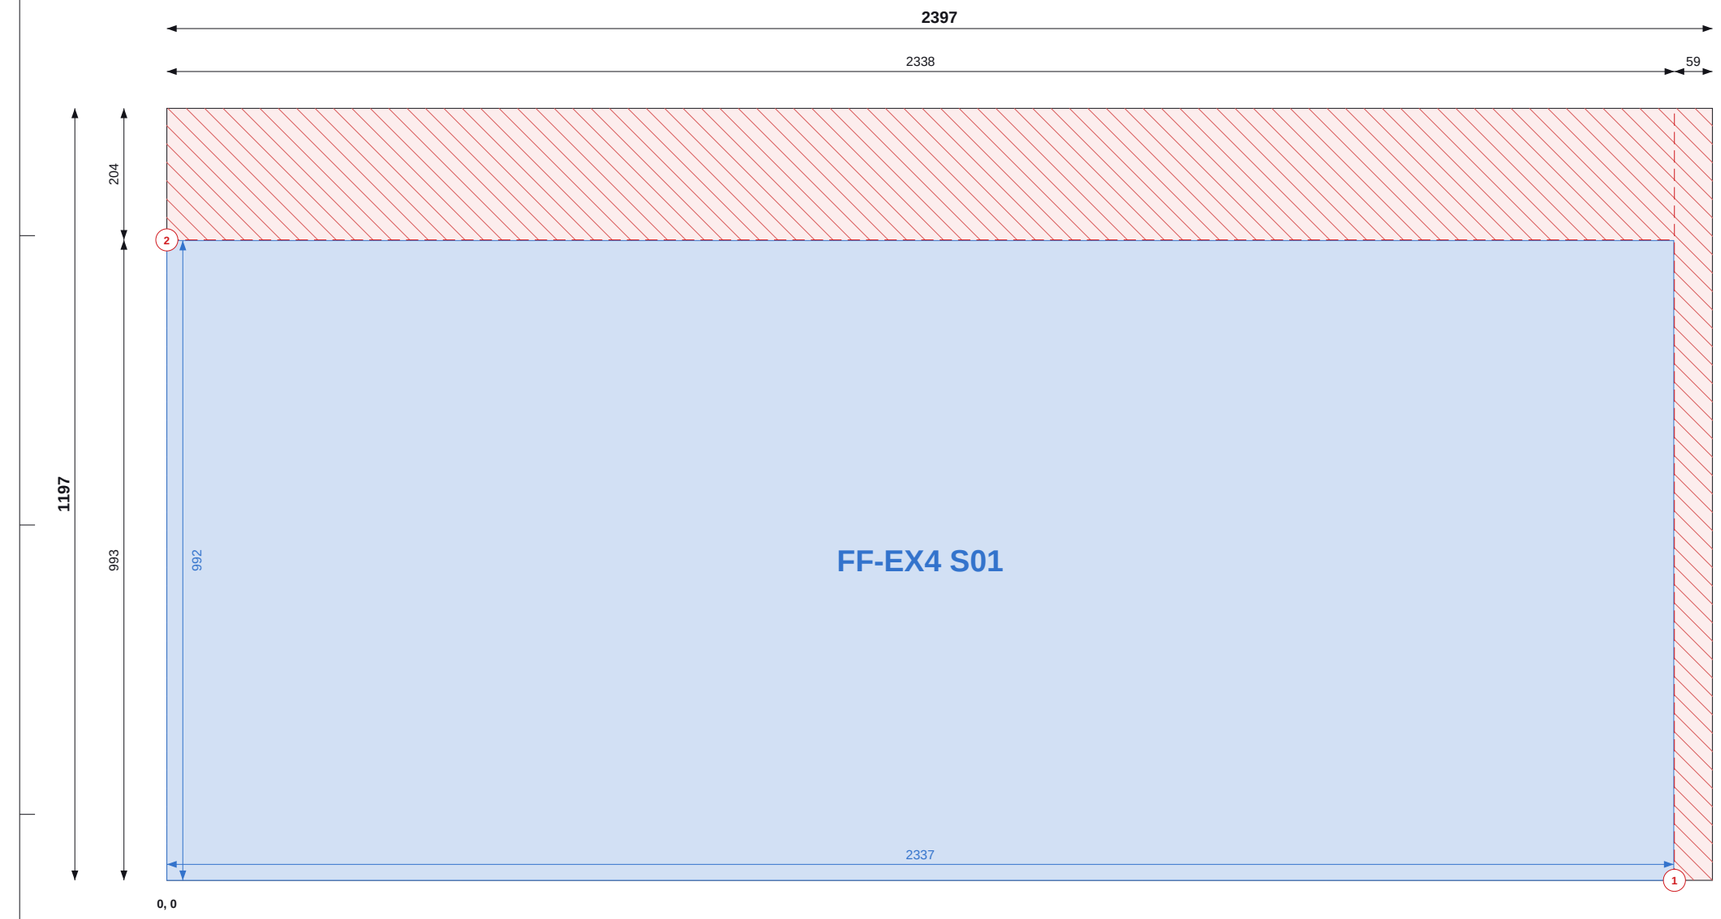


Top / left chains = saw cut positions (to cut centres). Coloured = part size and position.

Do not scale. All dimensions in mm. Check all dimensions on site.

## SHEET 10 OF 31

### THIS SHEET

| Item | Value |
|---|---|
| Parts | 1 |
| Used / waste | 80.8% / 0.55 m2 |
| Reusable offcuts | 0 |
| Saw cuts / shared | 2 / 0 |

### PIECES (POSITION = BOTTOM-LEFT CORNER)

| Label | Size | X, Y |
|---|---|---|
| FF-EX4 S01 | 992 x 2337 | 0, 0 |

### NOTES

1. Cut from OSB/3 9mm 1197x2397, 2mm saw kerf. Viewed on the face; dimensions from the sheet's bottom-left corner (0,0). Red numbered lines = saw cuts in order, each edge to edge.
2. Coloured dimensions belong to the part of that colour: its width and height, and its position from the sheet edges. Raked parts: corner coordinates at each corner.
3. Red hatch = waste. Labels = panel + piece mark on the manufacture drawing.

### REVISIONS

| REV | DATE | DESCRIPTION |
|---|---|---|
| C01 | 14.09.26 | Construction issue |
| C02 | 14.09.26 | Roof trusses revised; SP diagonals added |
| C03 | 11.10.26 | FF windows coursed; steel + GP1 portal; steel drawings (ST) |
| C04 | 13.10.26 | Steel approved by the engineer: steel + steel timber drawings issued for construction |

TLS TIMBER FRAME
Design & Manufacture
Scan: 3D model + drawings

| CLIENT | PROJECT |
|---|---|
| MP Adams | MP Adams Plot 4, Eckington |


DRAWING TITLE

**OSB CUTTING - FIRST FLOOR - SHEET 10 OF 31**

OSB/3 9mm 1197x2397 | First Floor

| SCALE | SIZE | DATE | DRAWN |
|---|---|---|---|
| NTS | A3 | 13.10.26 | TS |

| STATUS | DRAWING No. | REV |
|---|---|---|
| CONSTRUCTION | P4-CP-OSB-02 / 10 | C04 |

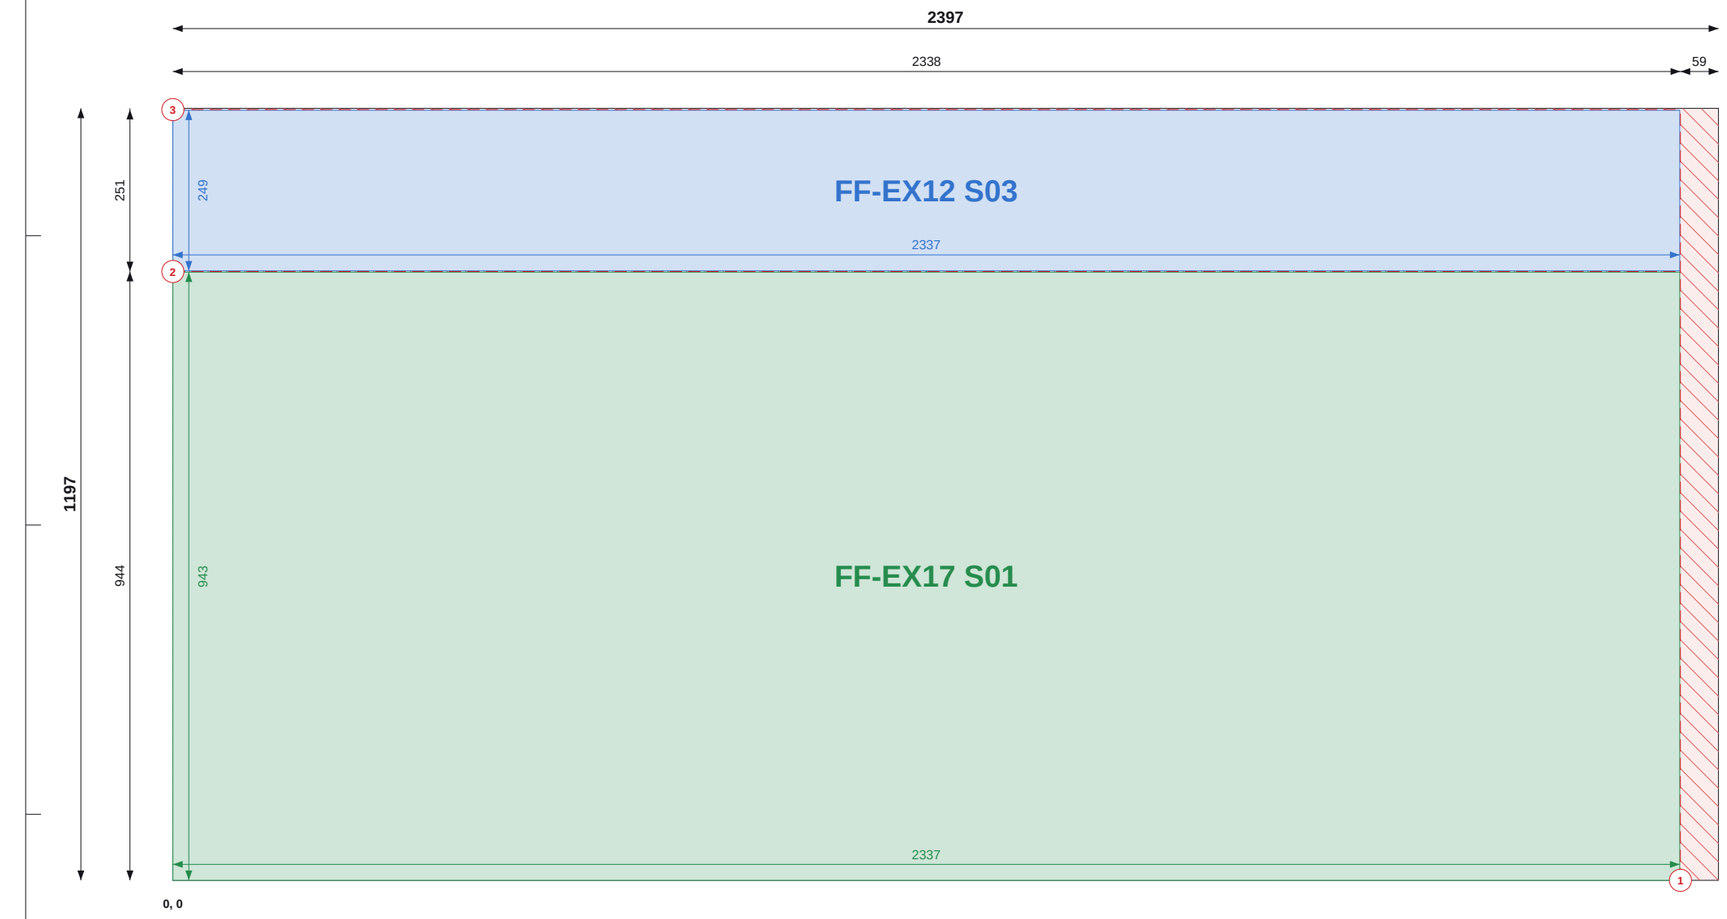


Top / left chains = saw cut positions (to cut centres). Coloured = part size and position.

Do not scale. All dimensions in mm. Check all dimensions on site.

## SHEET 11 OF 31

### THIS SHEET

| Item | Value |
|---|---|
| Parts | 2 |
| Used / waste | 97.1% / 0.08 m2 |
| Reusable offcuts | 0 |
| Saw cuts / shared | 3 / 1 |

### PIECES (POSITION = BOTTOM-LEFT CORNER)

| Label | Size | X, Y |
|---|---|---|
| FF-EX12 S03 | 249 x 2337 | 0, 945 |
| FF-EX17 S01 | 943 x 2337 | 0, 0 |

### NOTES

1. Cut from OSB/3 9mm 1197x2397, 2mm saw kerf. Viewed on the face; dimensions from the sheet's bottom-left corner (0,0). Red numbered lines = saw cuts in order, each edge to edge.
2. Coloured dimensions belong to the part of that colour: its width and height, and its position from the sheet edges. Raked parts: corner coordinates at each corner.
3. Red hatch = waste. Labels = panel + piece mark on the manufacture drawing.

### REVISIONS

| REV | DATE | DESCRIPTION |
|---|---|---|
| C01 | 14.09.26 | Construction issue |
| C02 | 14.09.26 | Roof trusses revised; SP diagonals added |
| C03 | 11.10.26 | FF windows coursed; steel + GP1 portal; steel drawings (ST) |
| C04 | 13.10.26 | Steel approved by the engineer: steel + steel timber drawings issued for construction |

TLS TIMBER FRAME
Design & Manufacture
Scan: 3D model + drawings

| CLIENT | PROJECT |
|---|---|
| MP Adams | MP Adams Plot 4, Eckington |


DRAWING TITLE

**OSB CUTTING - FIRST FLOOR - SHEET 11 OF 31**

OSB/3 9mm 1197x2397 | First Floor

| SCALE | SIZE | DATE | DRAWN |
|---|---|---|---|
| NTS | A3 | 13.10.26 | TS |

| STATUS | DRAWING No. | REV |
|---|---|---|
| CONSTRUCTION | P4-CP-OSB-02 / 11 | C04 |

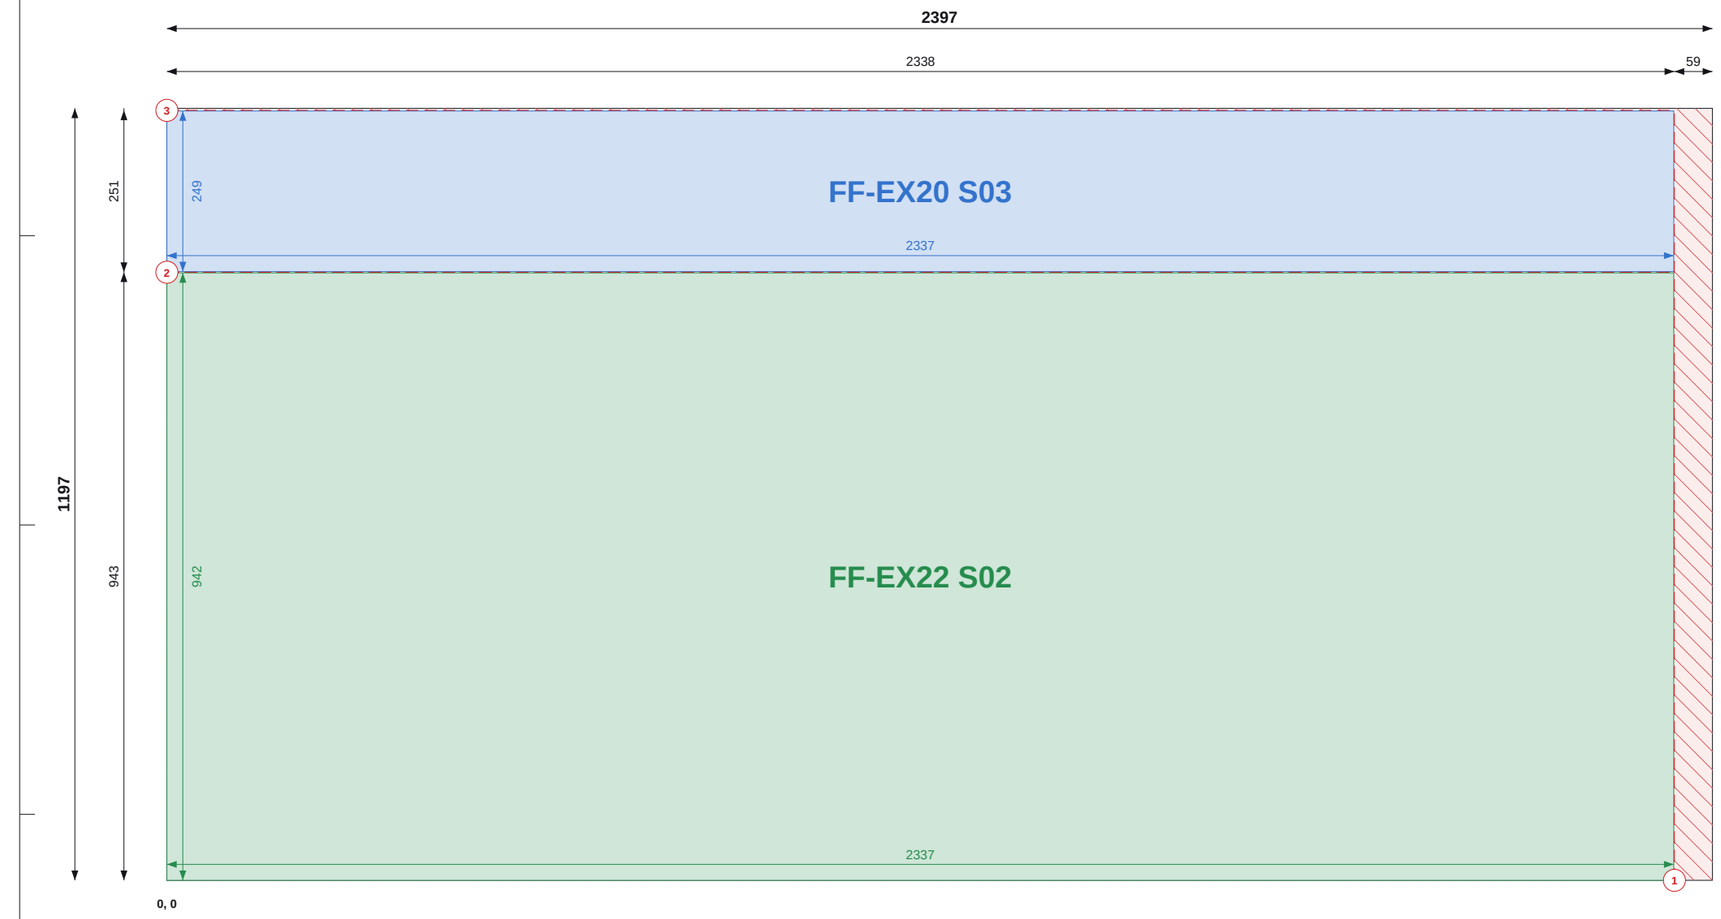


Top / left chains = saw cut positions (to cut centres). Coloured = part size and position.

## SHEET 12 OF 31

### THIS SHEET

| Item | Value |
|---|---|
| Parts | 2 |
| Used / waste | 97.0% / 0.09 m2 |
| Reusable offcuts | 0 |
| Saw cuts / shared | 3 / 1 |

### PIECES (POSITION = BOTTOM-LEFT CORNER)

| Label | Size | X, Y |
|---|---|---|
| FF-EX20 S03 | 249 x 2337 | 0, 944 |
| FF-EX22 S02 | 942 x 2337 | 0, 0 |

### NOTES

1. Cut from OSB/3 9mm 1197x2397, 2mm saw kerf. Viewed on the face; dimensions from the sheet's bottom-left corner (0,0). Red numbered lines = saw cuts in order, each edge to edge.
2. Coloured dimensions belong to the part of that colour: its width and height, and its position from the sheet edges. Raked parts: corner coordinates at each corner.
3. Red hatch = waste. Labels = panel + piece mark on the manufacture drawing.

### REVISIONS

| REV | DATE | DESCRIPTION |
|---|---|---|
| C01 | 14.09.26 | Construction issue |
| C02 | 14.09.26 | Roof trusses revised; SP diagonals added |
| C03 | 11.10.26 | FF windows coursed; steel + GP1 portal; steel drawings (ST) |
| C04 | 13.10.26 | Steel approved by the engineer: steel + steel timber drawings issued for construction |

TLS TIMBER FRAME
Design & Manufacture
Scan: 3D model + drawings

| CLIENT | PROJECT |
|---|---|
| MP Adams | MP Adams Plot 4, Eckington |

DRAWING TITLE


**OSB CUTTING - FIRST FLOOR - SHEET 12 OF 31**

OSB/3 9mm 1197x2397 | First Floor

| SCALE | SIZE | DATE | DRAWN |
|---|---|---|---|
| NTS | A3 | 13.10.26 | TS |

| STATUS | DRAWING No. | REV |
|---|---|---|
| CONSTRUCTION | P4-CP-OSB-02 / 12 | C04 |

Do not scale. All dimensions in mm. Check all dimensions on site.

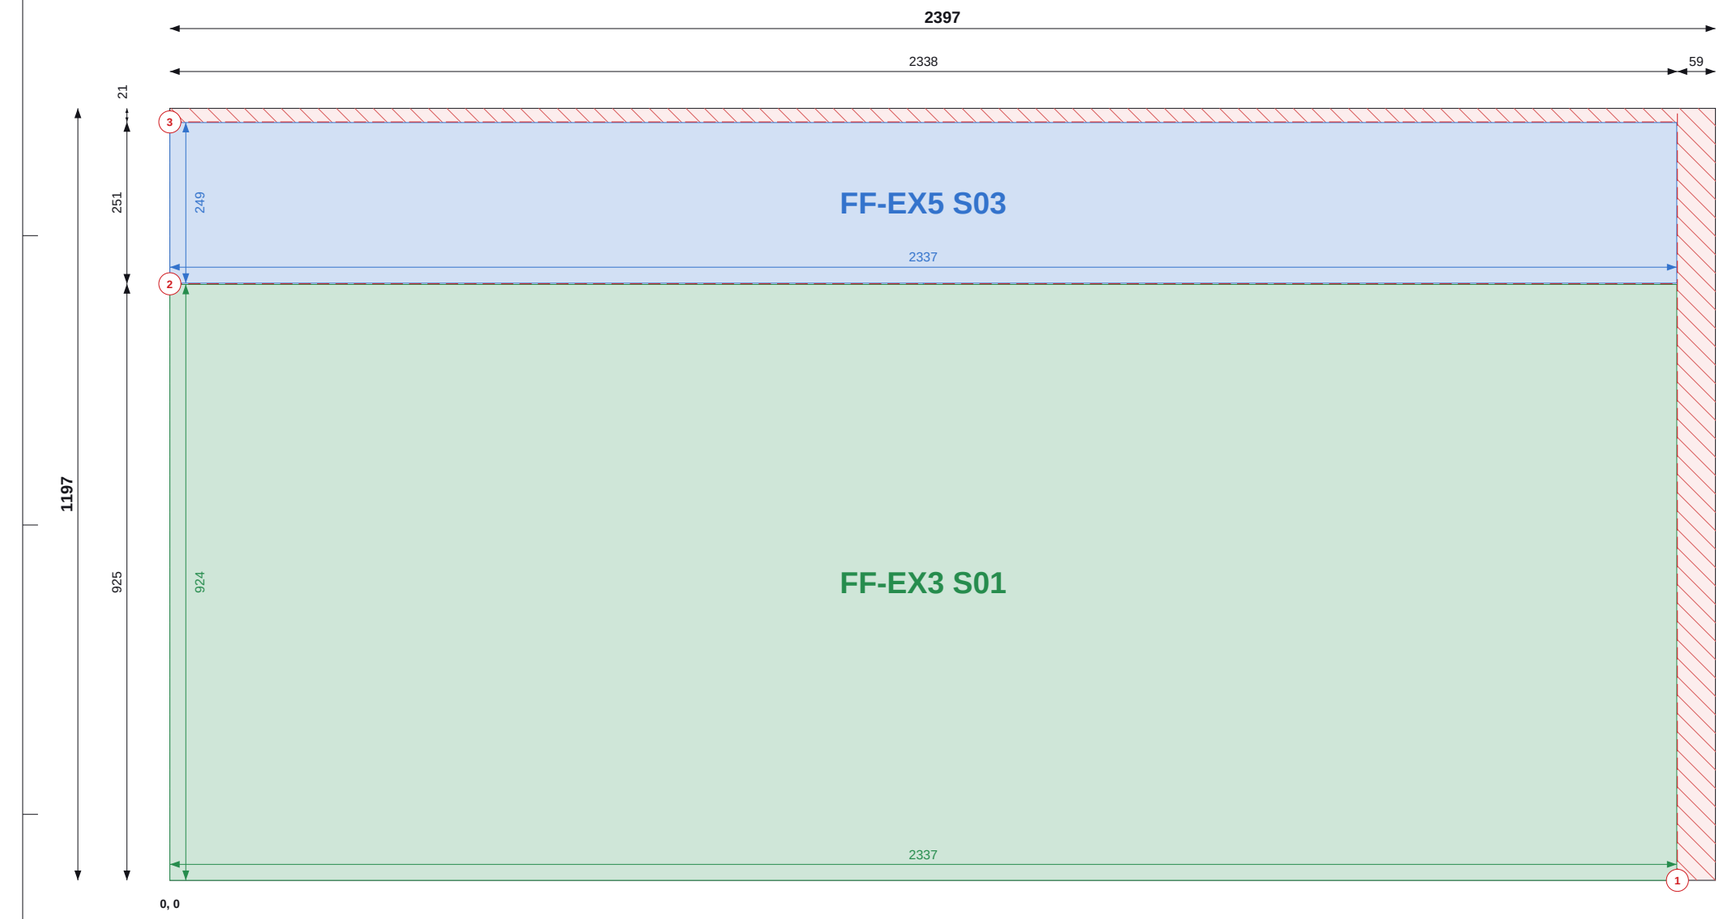


Top / left chains = saw cut positions (to cut centres). Coloured = part size and position.

Do not scale. All dimensions in mm. Check all dimensions on site.

## SHEET 13 OF 31

### THIS SHEET

| Item | Value |
|---|---|
| Parts | 2 |
| Used / waste | 95.5% / 0.13 m2 |
| Reusable offcuts | 0 |
| Saw cuts / shared | 3 / 1 |

### PIECES (POSITION = BOTTOM-LEFT CORNER)

| Label | Size | X, Y |
|---|---|---|
| FF-EX5 S03 | 249 x 2337 | 0, 926 |
| FF-EX3 S01 | 924 x 2337 | 0, 0 |

### NOTES

1. Cut from OSB/3 9mm 1197x2397, 2mm saw kerf. Viewed on the face; dimensions from the sheet's bottom-left corner (0,0). Red numbered lines = saw cuts in order, each edge to edge.
2. Coloured dimensions belong to the part of that colour: its width and height, and its position from the sheet edges. Raked parts: corner coordinates at each corner.
3. Red hatch = waste. Labels = panel + piece mark on the manufacture drawing.

### REVISIONS

| REV | DATE | DESCRIPTION |
|---|---|---|
| C01 | 14.09.26 | Construction issue |
| C02 | 14.09.26 | Roof trusses revised; SP diagonals added |
| C03 | 11.10.26 | FF windows coursed; steel + GP1 portal; steel drawings (ST) |
| C04 | 13.10.26 | Steel approved by the engineer: steel + steel timber drawings issued for construction |

TLS TIMBER FRAME
Design & Manufacture
Scan: 3D model + drawings

| CLIENT | PROJECT |
|---|---|
| MP Adams | MP Adams Plot 4, Eckington |


DRAWING TITLE

**OSB CUTTING - FIRST FLOOR - SHEET 13 OF 31**

OSB/3 9mm 1197x2397 | First Floor

| SCALE | SIZE | DATE | DRAWN |
|---|---|---|---|
| NTS | A3 | 13.10.26 | TS |

| STATUS | DRAWING No. | REV |
|---|---|---|
| CONSTRUCTION | P4-CP-OSB-02 / 13 | C04 |

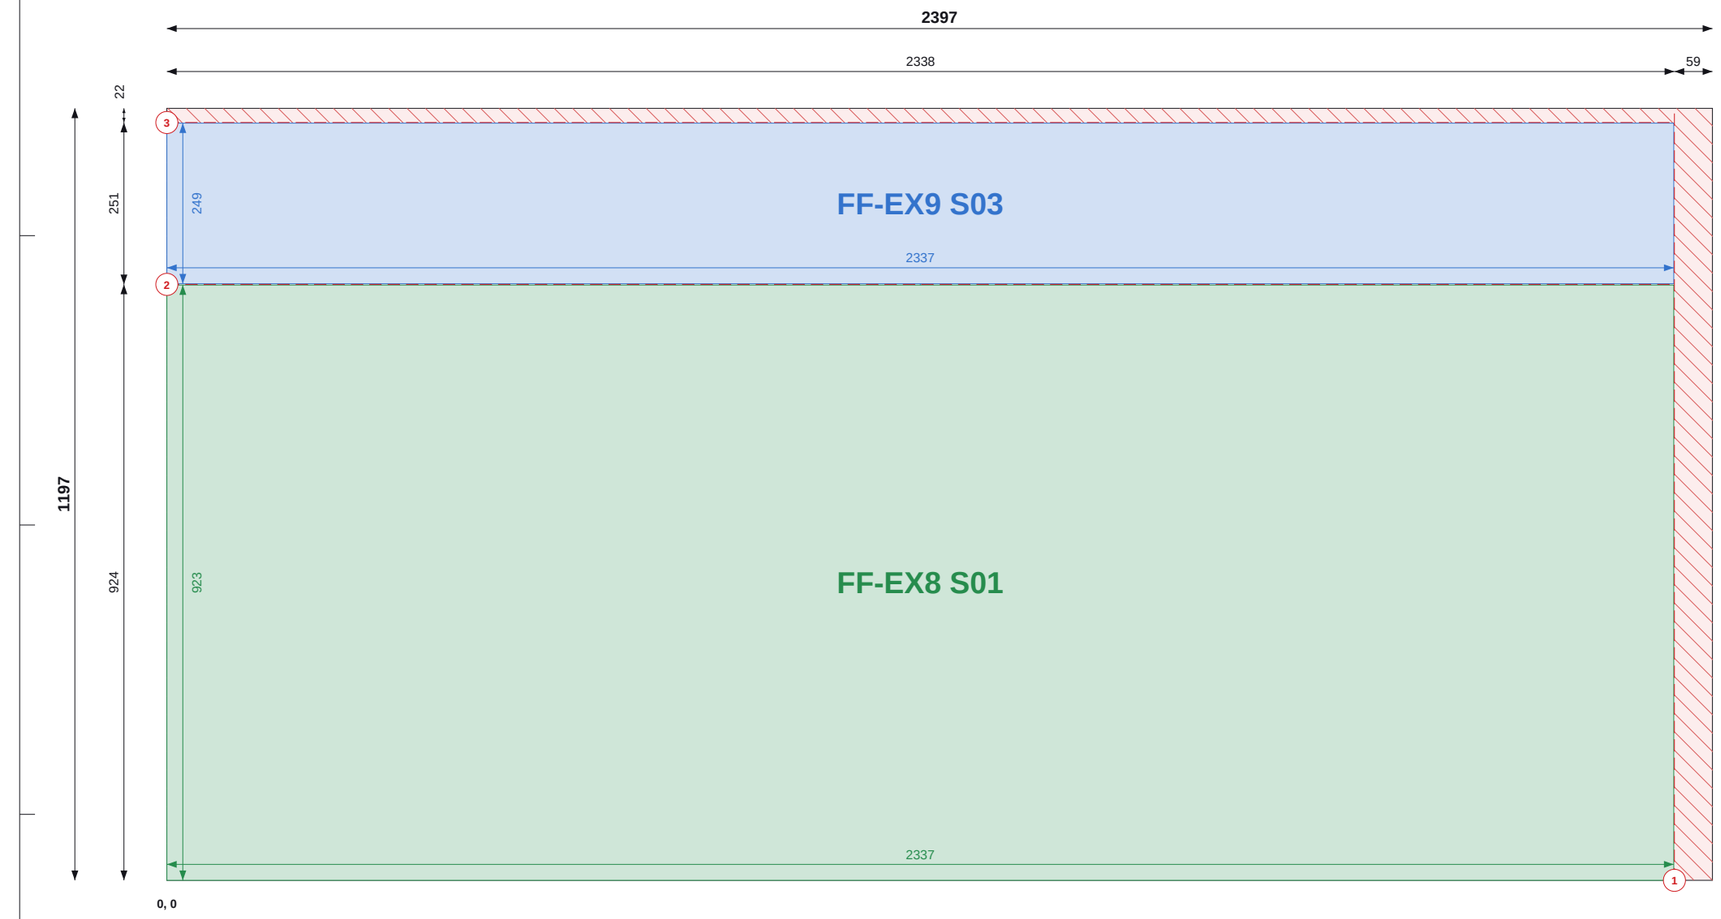


Top / left chains = saw cut positions (to cut centres). Coloured = part size and position.

## SHEET 14 OF 31

### THIS SHEET

| Item | Value |
|---|---|
| Parts | 2 |
| Used / waste | 95.5% / 0.13 m2 |
| Reusable offcuts | 0 |
| Saw cuts / shared | 3 / 1 |

### PIECES (POSITION = BOTTOM-LEFT CORNER)

| Label | Size | X, Y |
|---|---|---|
| FF-EX9 S03 | 249 x 2337 | 0, 925 |
| FF-EX8 S01 | 923 x 2337 | 0, 0 |

### NOTES

1. Cut from OSB/3 9mm 1197x2397, 2mm saw kerf. Viewed on the face; dimensions from the sheet's bottom-left corner (0,0). Red numbered lines = saw cuts in order, each edge to edge.
2. Coloured dimensions belong to the part of that colour: its width and height, and its position from the sheet edges. Raked parts: corner coordinates at each corner.
3. Red hatch = waste. Labels = panel + piece mark on the manufacture drawing.

### REVISIONS

| REV | DATE | DESCRIPTION |
|---|---|---|
| C01 | 14.09.26 | Construction issue |
| C02 | 14.09.26 | Roof trusses revised; SP diagonals added |
| C03 | 11.10.26 | FF windows coursed; steel + GP1 portal; steel drawings (ST) |
| C04 | 13.10.26 | Steel approved by the engineer: steel + steel timber drawings issued for construction |

TLS TIMBER FRAME
Design & Manufacture
Scan: 3D model + drawings

| CLIENT | PROJECT |
|---|---|
| MP Adams | MP Adams Plot 4, Eckington |

DRAWING TITLE


**OSB CUTTING - FIRST FLOOR - SHEET 14 OF 31**

OSB/3 9mm 1197x2397 | First Floor

| SCALE | SIZE | DATE | DRAWN |
|---|---|---|---|
| NTS | A3 | 13.10.26 | TS |

| STATUS | DRAWING No. | REV |
|---|---|---|
| CONSTRUCTION | P4-CP-OSB-02 / 14 | C04 |

Do not scale. All dimensions in mm. Check all dimensions on site.

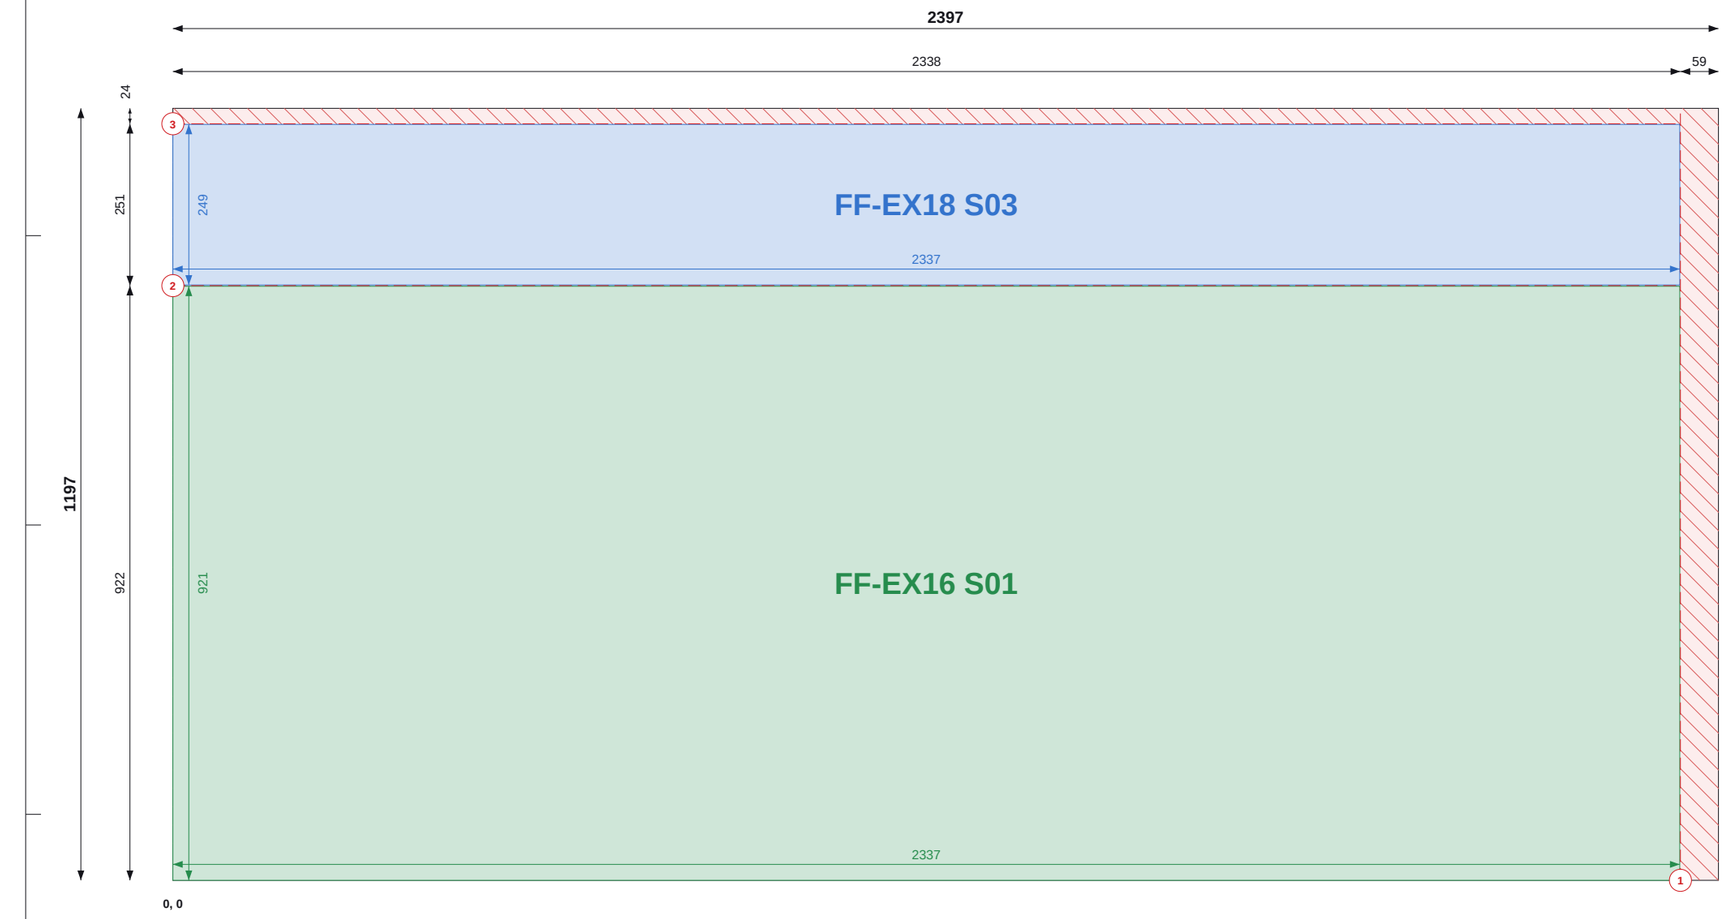


Top / left chains = saw cut positions (to cut centres). Coloured = part size and position.

## SHEET 15 OF 31

### THIS SHEET

| Item | Value |
|---|---|
| Parts | 2 |
| Used / waste | 95.3% / 0.13 m2 |
| Reusable offcuts | 0 |
| Saw cuts / shared | 3 / 1 |

### PIECES (POSITION = BOTTOM-LEFT CORNER)

| Label | Size | X, Y |
|---|---|---|
| FF-EX18 S03 | 249 x 2337 | 0, 923 |
| FF-EX16 S01 | 921 x 2337 | 0, 0 |

### NOTES

1. Cut from OSB/3 9mm 1197x2397, 2mm saw kerf. Viewed on the face; dimensions from the sheet's bottom-left corner (0,0). Red numbered lines = saw cuts in order, each edge to edge.
2. Coloured dimensions belong to the part of that colour: its width and height, and its position from the sheet edges. Raked parts: corner coordinates at each corner.
3. Red hatch = waste. Labels = panel + piece mark on the manufacture drawing.

### REVISIONS

| REV | DATE | DESCRIPTION |
|---|---|---|
| C01 | 14.09.26 | Construction issue |
| C02 | 14.09.26 | Roof trusses revised; SP diagonals added |
| C03 | 11.10.26 | FF windows coursed; steel + GP1 portal; steel drawings (ST) |
| C04 | 13.10.26 | Steel approved by the engineer: steel + steel timber drawings issued for construction |

TLS TIMBER FRAME
Design & Manufacture
Scan: 3D model + drawings

| CLIENT | PROJECT |
|---|---|
| MP Adams | MP Adams Plot 4, Eckington |

DRAWING TITLE


**OSB CUTTING - FIRST FLOOR - SHEET 15 OF 31**

OSB/3 9mm 1197x2397 | First Floor

| SCALE | SIZE | DATE | DRAWN |
|---|---|---|---|
| NTS | A3 | 13.10.26 | TS |

| STATUS | DRAWING No. | REV |
|---|---|---|
| CONSTRUCTION | P4-CP-OSB-02 / 15 | C04 |

Do not scale. All dimensions in mm. Check all dimensions on site.

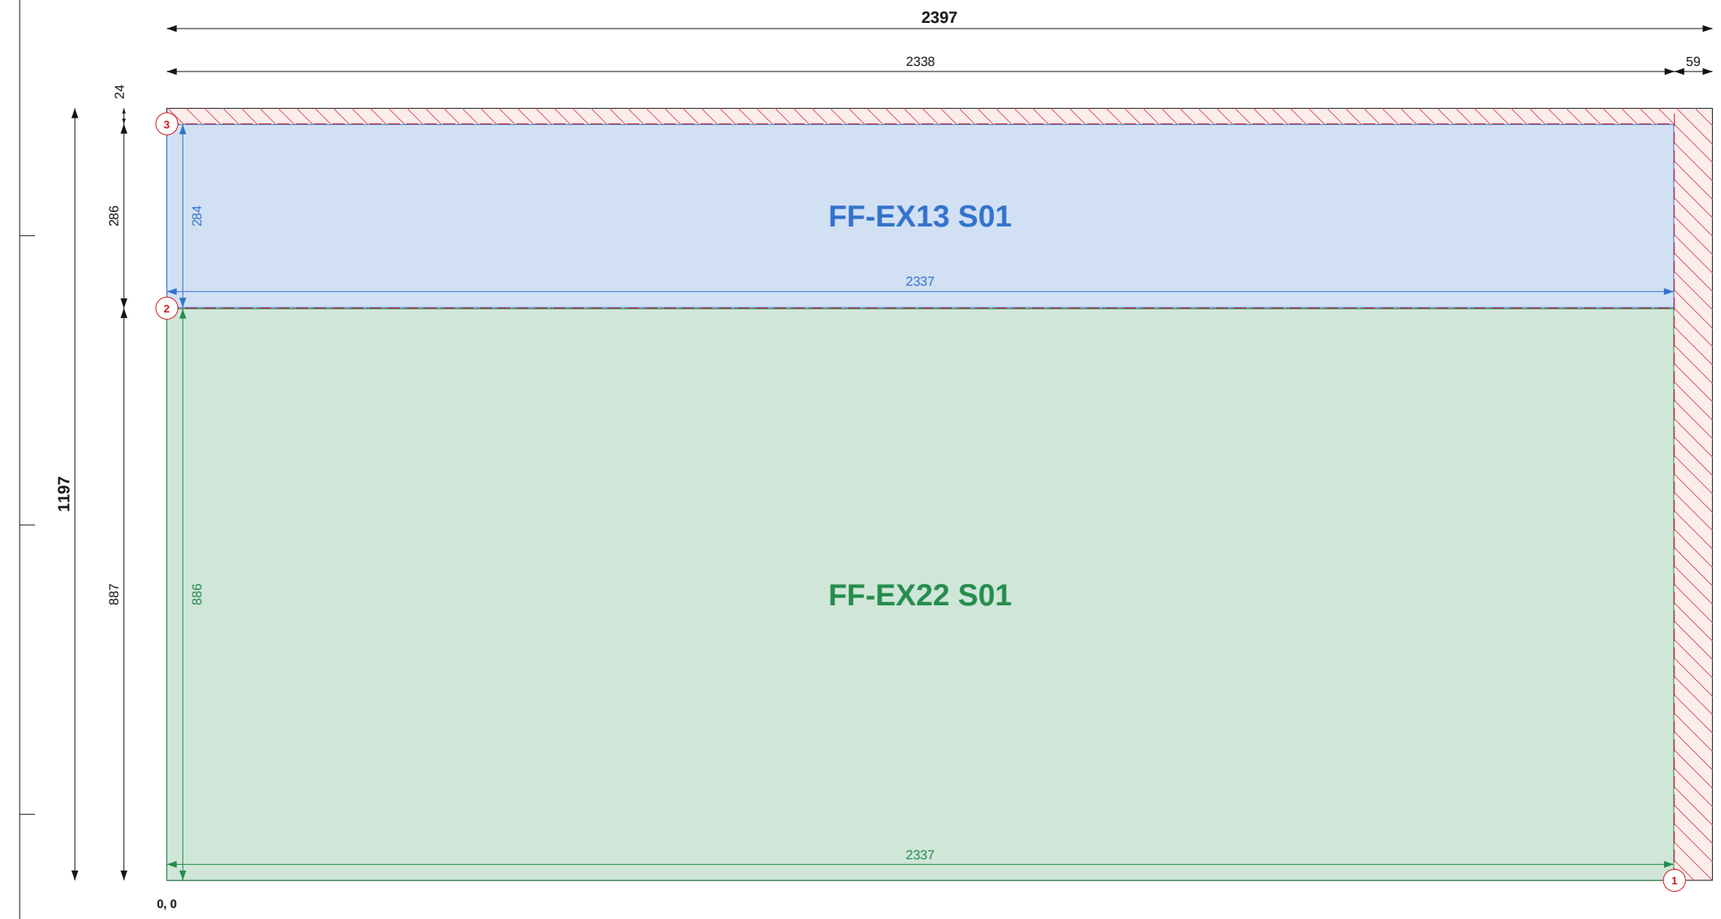


Top / left chains = saw cut positions (to cut centres). Coloured = part size and position.

Do not scale. All dimensions in mm. Check all dimensions on site.

## SHEET 16 OF 31

### THIS SHEET

| Item | Value |
|---|---|
| Parts | 2 |
| Used / waste | 95.3% / 0.13 m2 |
| Reusable offcuts | 0 |
| Saw cuts / shared | 3 / 1 |

### PIECES (POSITION = BOTTOM-LEFT CORNER)

| Label | Size | X, Y |
|---|---|---|
| FF-EX13 S01 | 284 x 2337 | 0, 888 |
| FF-EX22 S01 | 886 x 2337 | 0, 0 |

### NOTES

1. Cut from OSB/3 9mm 1197x2397, 2mm saw kerf. Viewed on the face; dimensions from the sheet's bottom-left corner (0,0). Red numbered lines = saw cuts in order, each edge to edge.
2. Coloured dimensions belong to the part of that colour: its width and height, and its position from the sheet edges. Raked parts: corner coordinates at each corner.
3. Red hatch = waste. Labels = panel + piece mark on the manufacture drawing.

### REVISIONS

| REV | DATE | DESCRIPTION |
|---|---|---|
| C01 | 14.09.26 | Construction issue |
| C02 | 14.09.26 | Roof trusses revised; SP diagonals added |
| C03 | 11.10.26 | FF windows coursed; steel + GP1 portal; steel drawings (ST) |
| C04 | 13.10.26 | Steel approved by the engineer: steel + steel timber drawings issued for construction |

TLS

TLS TIMBER FRAME

Design & Manufacture

Scan: 3D model + drawings

| CLIENT | PROJECT |
|---|---|
| MP Adams | MP Adams Plot 4, Eckington |

DRAWING TITLE

**OSB CUTTING - FIRST FLOOR - SHEET 16 OF 31**

OSB/3 9mm 1197x2397 | First Floor

| SCALE | SIZE | DATE | DRAWN |
|---|---|---|---|
| NTS | A3 | 13.10.26 | TS |

| STATUS | DRAWING No. | REV |
|---|---|---|
| CONSTRUCTION | P4-CP-OSB-02 / 16 | C04 |




Top / left chains = saw cut positions (to cut centres). Coloured = part size and position.

Do not scale. All dimensions in mm. Check all dimensions on site.

## SHEET 17 OF 31

### THIS SHEET

| Item | Value |
|---|---|
| Parts | 2 |
| Used / waste | 96.8% / 0.09 m2 |
| Reusable offcuts | 0 |
| Saw cuts / shared | 3 / 1 |

### PIECES (POSITION = BOTTOM-LEFT CORNER)

| Label | Size | X, Y |
|---|---|---|
| FF-EX8 S03 | 404 x 2337 | 0, 786 |
| FF-EX14 S03 | 784 x 2337 | 0, 0 |

### NOTES

1. Cut from OSB/3 9mm 1197x2397, 2mm saw kerf. Viewed on the face; dimensions from the sheet's bottom-left corner (0,0). Red numbered lines = saw cuts in order, each edge to edge.
2. Coloured dimensions belong to the part of that colour: its width and height, and its position from the sheet edges. Raked parts: corner coordinates at each corner.
3. Red hatch = waste. Labels = panel + piece mark on the manufacture drawing.

### REVISIONS

| REV | DATE | DESCRIPTION |
|---|---|---|
| C01 | 14.09.26 | Construction issue |
| C02 | 14.09.26 | Roof trusses revised; SP diagonals added |
| C03 | 11.10.26 | FF windows coursed; steel + GP1 portal; steel drawings (ST) |
| C04 | 13.10.26 | Steel approved by the engineer: steel + steel timber drawings issued for construction |

TLS TIMBER FRAME
Design & Manufacture
Scan: 3D model + drawings

| CLIENT | PROJECT |
|---|---|
| MP Adams | MP Adams Plot 4, Eckington |

DRAWING TITLE

**OSB CUTTING - FIRST FLOOR - SHEET 17 OF 31**

OSB/3 9mm 1197x2397 | First Floor

| SCALE | SIZE | DATE | DRAWN |
|---|---|---|---|
| NTS | A3 | 13.10.26 | TS |

| STATUS | DRAWING No. | REV |
|---|---|---|
| CONSTRUCTION | P4-CP-OSB-02 / 17 | C04 |




Top / left chains = saw cut positions (to cut centres). Coloured = part size and position.

Do not scale. All dimensions in mm. Check all dimensions on site.

## SHEET 18 OF 31

### THIS SHEET

| Item | Value |
|---|---|
| Parts | 2 |
| Used / waste | 97.3% / 0.08 m2 |
| Reusable offcuts | 0 |
| Saw cuts / shared | 2 / 1 |

### PIECES (POSITION = BOTTOM-LEFT CORNER)

| Label | Size | X, Y |
|---|---|---|
| FF-EX15 S01 | 413 x 2337 | 0, 784 |
| FF-EX15 S03 | 782 x 2337 | 0, 0 |

### NOTES

1. Cut from OSB/3 9mm 1197x2397, 2mm saw kerf. Viewed on the face; dimensions from the sheet's bottom-left corner (0,0). Red numbered lines = saw cuts in order, each edge to edge.
2. Coloured dimensions belong to the part of that colour: its width and height, and its position from the sheet edges. Raked parts: corner coordinates at each corner.
3. Red hatch = waste. Labels = panel + piece mark on the manufacture drawing.

### REVISIONS

| REV | DATE | DESCRIPTION |
|---|---|---|
| C01 | 14.09.26 | Construction issue |
| C02 | 14.09.26 | Roof trusses revised; SP diagonals added |
| C03 | 11.10.26 | FF windows coursed; steel + GP1 portal; steel drawings (ST) |
| C04 | 13.10.26 | Steel approved by the engineer: steel + steel timber drawings issued for construction |

TLS TIMBER FRAME
Design & Manufacture
Scan: 3D model + drawings

| CLIENT | PROJECT |
|---|---|
| MP Adams | MP Adams Plot 4, Eckington |

DRAWING TITLE
**OSB CUTTING - FIRST FLOOR - SHEET 18 OF 31**

OSB/3 9mm 1197x2397 | First Floor

| SCALE | SIZE | DATE | DRAWN |
|---|---|---|---|
| NTS | A3 | 13.10.26 | TS |

| STATUS | DRAWING No. | REV |
|---|---|---|
| CONSTRUCTION | P4-CP-OSB-02 / 18 | C04 |




Top / left chains = saw cut positions (to cut centres). Coloured = part size and position.

Do not scale. All dimensions in mm. Check all dimensions on site.

## SHEET 19 OF 31

### THIS SHEET

| Item | Value |
|---|---|
| Parts | 2 |
| Used / waste | 97.3% / 0.08 m2 |
| Reusable offcuts | 0 |
| Saw cuts / shared | 2 / 1 |

### PIECES (POSITION = BOTTOM-LEFT CORNER)

| Label | Size | X, Y |
|---|---|---|
| FF-EX1 S01 | 414 x 2337 | 0, 783 |
| FF-EX1 S03 | 781 x 2337 | 0, 0 |

### NOTES

1. Cut from OSB/3 9mm 1197x2397, 2mm saw kerf. Viewed on the face; dimensions from the sheet's bottom-left corner (0,0). Red numbered lines = saw cuts in order, each edge to edge.
2. Coloured dimensions belong to the part of that colour: its width and height, and its position from the sheet edges. Raked parts: corner coordinates at each corner.
3. Red hatch = waste. Labels = panel + piece mark on the manufacture drawing.

### REVISIONS

| REV | DATE | DESCRIPTION |
|---|---|---|
| C01 | 14.09.26 | Construction issue |
| C02 | 14.09.26 | Roof trusses revised; SP diagonals added |
| C03 | 11.10.26 | FF windows coursed; steel + GP1 portal; steel drawings (ST) |
| C04 | 13.10.26 | Steel approved by the engineer: steel + steel timber drawings issued for construction |

TLS TIMBER FRAME
Design & Manufacture
Scan: 3D model + drawings

| CLIENT | PROJECT |
|---|---|
| MP Adams | MP Adams Plot 4, Eckington |


DRAWING TITLE

**OSB CUTTING - FIRST FLOOR - SHEET 19 OF 31**

OSB/3 9mm 1197x2397 | First Floor

| SCALE | SIZE | DATE | DRAWN |
|---|---|---|---|
| NTS | A3 | 13.10.26 | TS |

| STATUS | DRAWING No. | REV |
|---|---|---|
| CONSTRUCTION | P4-CP-OSB-02 / 19 | C04 |

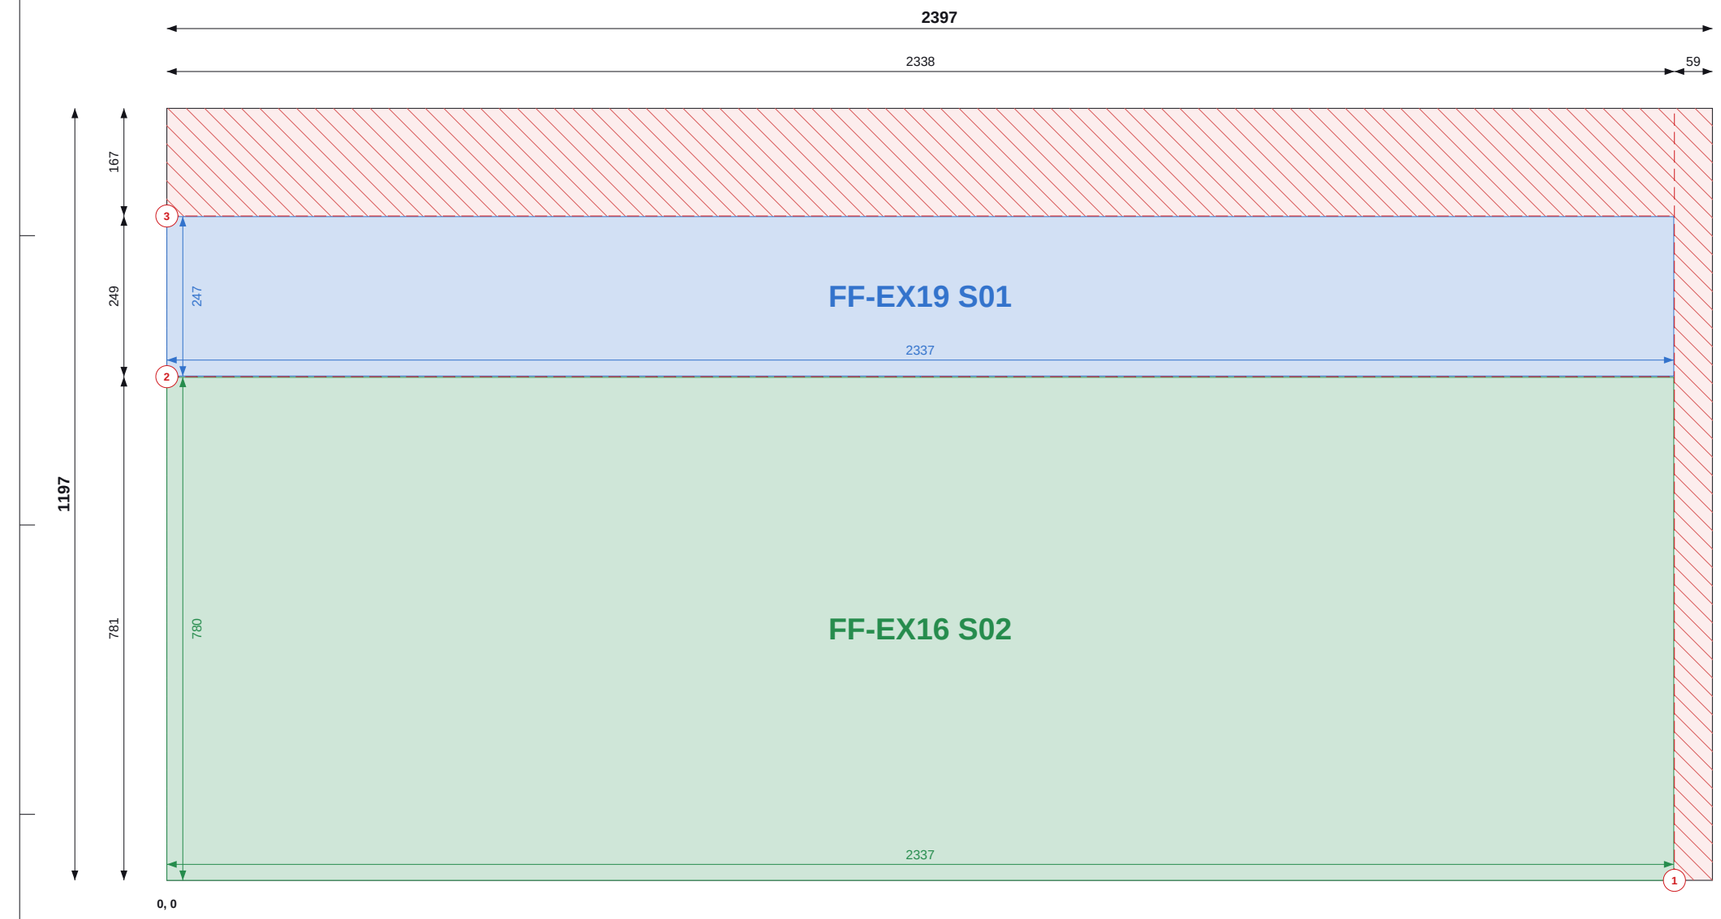


Top / left chains = saw cut positions (to cut centres). Coloured = part size and position.

## SHEET 20 OF 31

### THIS SHEET

| Item | Value |
|---|---|
| Parts | 2 |
| Used / waste | 83.7% / 0.47 m2 |
| Reusable offcuts | 0 |
| Saw cuts / shared | 3 / 1 |

### PIECES (POSITION = BOTTOM-LEFT CORNER)

| Label | Size | X, Y |
|---|---|---|
| FF-EX19 S01 | 247 x 2337 | 0, 782 |
| FF-EX16 S02 | 780 x 2337 | 0, 0 |

### NOTES

1. Cut from OSB/3 9mm 1197x2397, 2mm saw kerf. Viewed on the face; dimensions from the sheet's bottom-left corner (0,0). Red numbered lines = saw cuts in order, each edge to edge.
2. Coloured dimensions belong to the part of that colour: its width and height, and its position from the sheet edges. Raked parts: corner coordinates at each corner.
3. Red hatch = waste. Labels = panel + piece mark on the manufacture drawing.

### REVISIONS

| REV | DATE | DESCRIPTION |
|---|---|---|
| C01 | 14.09.26 | Construction issue |
| C02 | 14.09.26 | Roof trusses revised; SP diagonals added |
| C03 | 11.10.26 | FF windows coursed; steel + GP1 portal; steel drawings (ST) |
| C04 | 13.10.26 | Steel approved by the engineer: steel + steel timber drawings issued for construction |

TLS TIMBER FRAME
Design & Manufacture
Scan: 3D model + drawings

| CLIENT | PROJECT |
|---|---|
| MP Adams | MP Adams Plot 4, Eckington |


DRAWING TITLE
**OSB CUTTING - FIRST FLOOR - SHEET 20 OF 31**

OSB/3 9mm 1197x2397 | First Floor

| SCALE | SIZE | DATE | DRAWN |
|---|---|---|---|
| NTS | A3 | 13.10.26 | TS |

| STATUS | DRAWING No. | REV |
|---|---|---|
| CONSTRUCTION | P4-CP-OSB-02 / 20 | C04 |

Do not scale. All dimensions in mm. Check all dimensions on site.

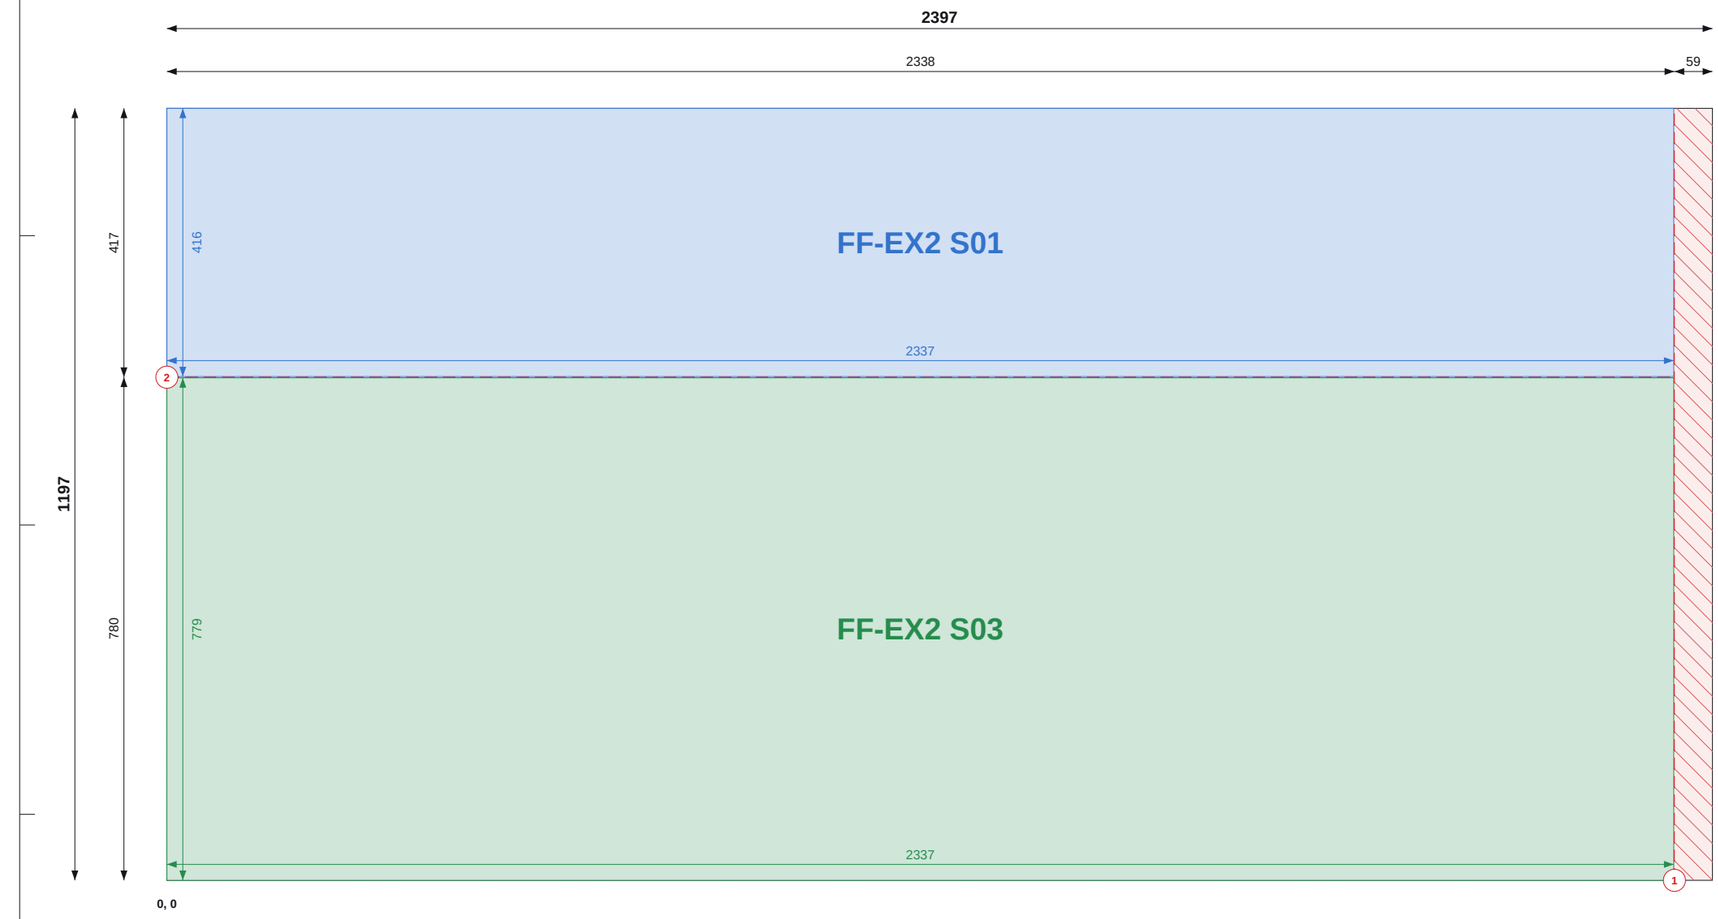


Top / left chains = saw cut positions (to cut centres). Coloured = part size and position.

Do not scale. All dimensions in mm. Check all dimensions on site.

## SHEET 21 OF 31

### THIS SHEET

| Item | Value |
|---|---|
| Parts | 2 |
| Used / waste | 97.3% / 0.08 m2 |
| Reusable offcuts | 0 |
| Saw cuts / shared | 2 / 1 |

### PIECES (POSITION = BOTTOM-LEFT CORNER)

| Label | Size | X, Y |
|---|---|---|
| FF-EX2 S01 | 416 x 2337 | 0, 781 |
| FF-EX2 S03 | 779 x 2337 | 0, 0 |

### NOTES

1. Cut from OSB/3 9mm 1197x2397, 2mm saw kerf. Viewed on the face; dimensions from the sheet's bottom-left corner (0,0). Red numbered lines = saw cuts in order, each edge to edge.
2. Coloured dimensions belong to the part of that colour: its width and height, and its position from the sheet edges. Raked parts: corner coordinates at each corner.
3. Red hatch = waste. Labels = panel + piece mark on the manufacture drawing.

### REVISIONS

| REV | DATE | DESCRIPTION |
|---|---|---|
| C01 | 14.09.26 | Construction issue |
| C02 | 14.09.26 | Roof trusses revised; SP diagonals added |
| C03 | 11.10.26 | FF windows coursed; steel + GP1 portal; steel drawings (ST) |
| C04 | 13.10.26 | Steel approved by the engineer: steel + steel timber drawings issued for construction |

TLS TIMBER FRAME
Design & Manufacture
Scan: 3D model + drawings


| CLIENT | PROJECT |
|---|---|
| MP Adams | MP Adams Plot 4, Eckington |

DRAWING TITLE
**OSB CUTTING - FIRST FLOOR - SHEET 21 OF 31**

OSB/3 9mm 1197x2397 | First Floor

| SCALE | SIZE | DATE | DRAWN |
|---|---|---|---|
| NTS | A3 | 13.10.26 | TS |

| STATUS | DRAWING No. | REV |
|---|---|---|
| CONSTRUCTION | P4-CP-OSB-02 / 21 | C04 |

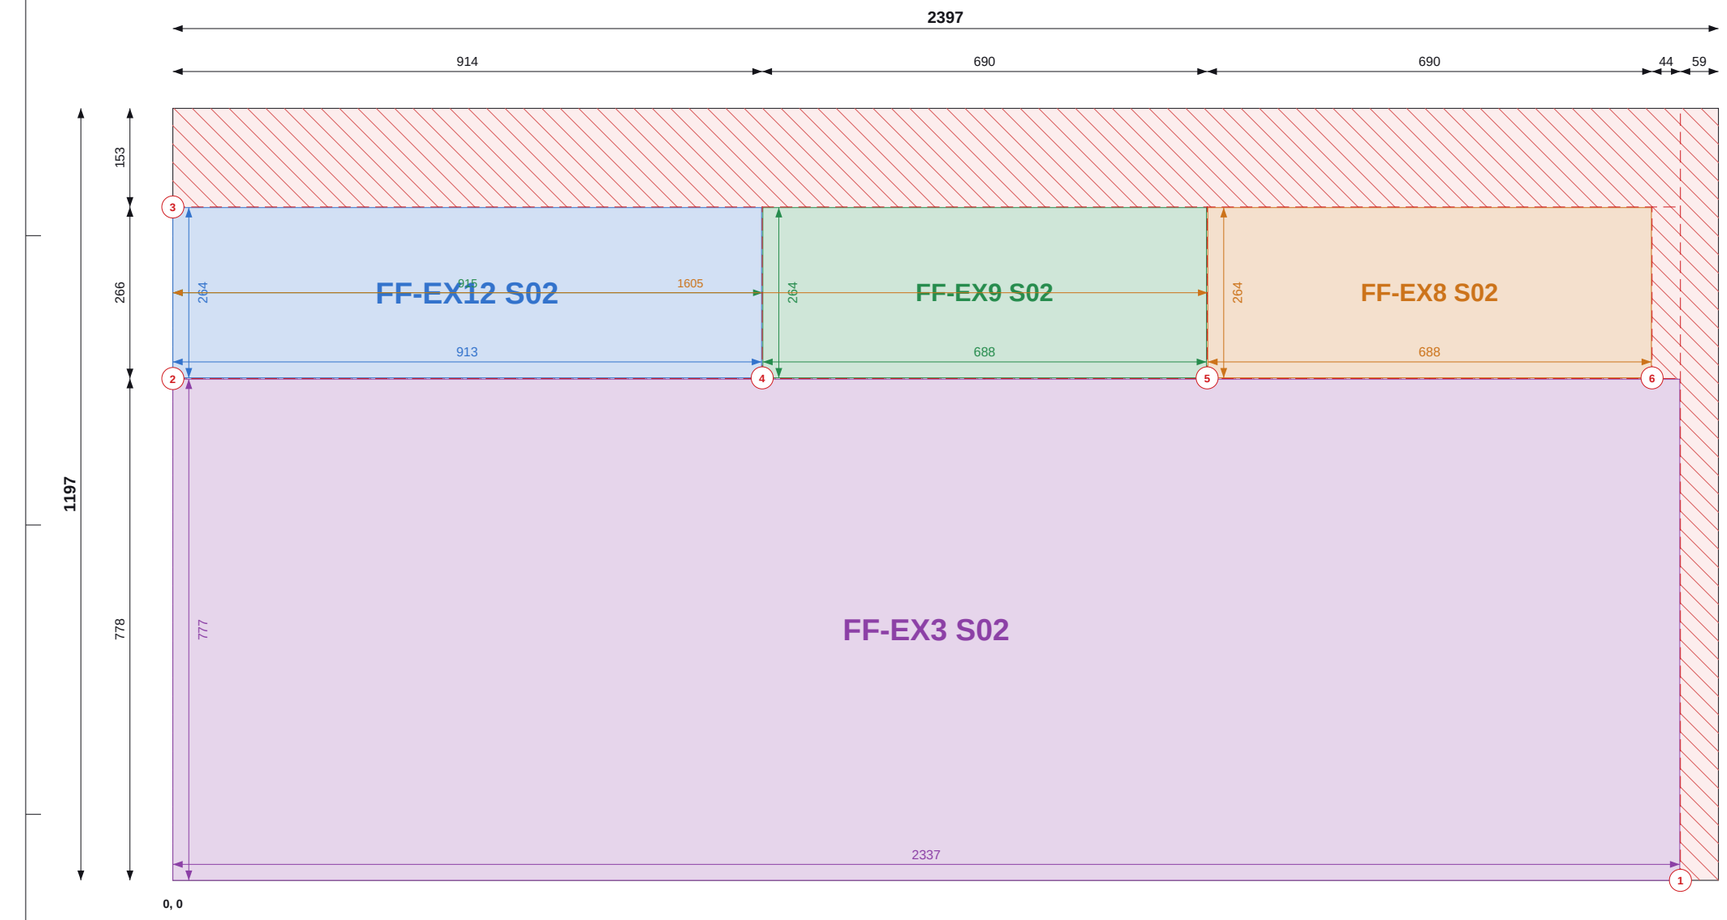


Top / left chains = saw cut positions (to cut centres). Coloured = part size and position.

Do not scale. All dimensions in mm. Check all dimensions on site.

## SHEET 22 OF 31

### THIS SHEET

| Item | Value |
|---|---|
| Parts | 4 |
| Used / waste | 84.4% / 0.45 m2 |
| Reusable offcuts | 0 |
| Saw cuts / shared | 6 / 3 |

### PIECES (POSITION = BOTTOM-LEFT CORNER)

| Label | Size | X, Y |
|---|---|---|
| FF-EX12 S02 | 913 x 264 | 0, 779 |
| FF-EX9 S02 | 688 x 264 | 915, 779 |
| FF-EX8 S02 | 688 x 264 | 1605, 779 |
| FF-EX3 S02 | 777 x 2337 | 0, 0 |

### NOTES

1. Cut from OSB/3 9mm 1197x2397, 2mm saw kerf. Viewed on the face; dimensions from the sheet's bottom-left corner (0,0). Red numbered lines = saw cuts in order, each edge to edge.
2. Coloured dimensions belong to the part of that colour: its width and height, and its position from the sheet edges. Raked parts: corner coordinates at each corner.
3. Red hatch = waste. Labels = panel + piece mark on the manufacture drawing.

### REVISIONS

| REV | DATE | DESCRIPTION |
|---|---|---|
| C01 | 14.09.26 | Construction issue |
| C02 | 14.09.26 | Roof trusses revised; SP diagonals added |
| C03 | 11.10.26 | FF windows coursed; steel + GP1 portal; steel drawings (ST) |
| C04 | 13.10.26 | Steel approved by the engineer: steel + steel timber drawings issued for construction |

TLS

TLS TIMBER FRAME

Design & Manufacture

Scan: 3D model + drawings

| CLIENT | PROJECT |
|---|---|
| MP Adams | MP Adams Plot 4, Eckington |


DRAWING TITLE

**OSB CUTTING - FIRST FLOOR - SHEET 22 OF 31**

OSB/3 9mm 1197x2397 | First Floor

| SCALE | SIZE | DATE | DRAWN |
|---|---|---|---|
| NTS | A3 | 13.10.26 | TS |

| STATUS | DRAWING No. | REV |
|---|---|---|
| CONSTRUCTION | P4-CP-OSB-02 / 22 | C04 |

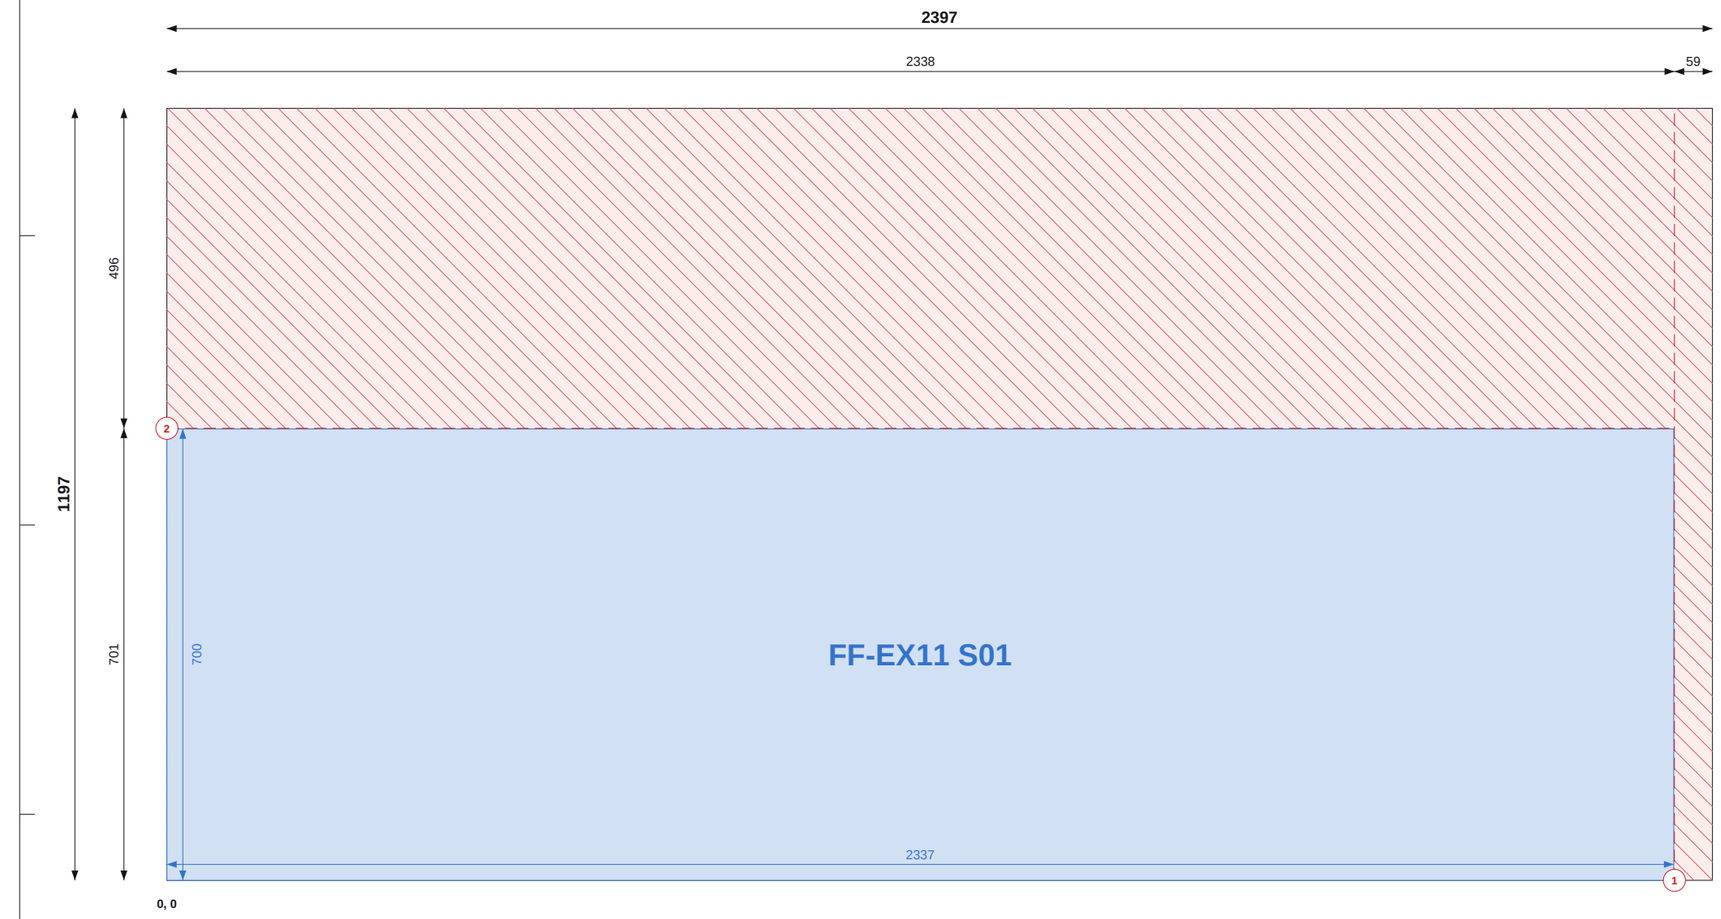


Top / left chains = saw cut positions (to cut centres). Coloured = part size and position.

## SHEET 23 OF 31

### THIS SHEET

| Item | Value |
|---|---|
| Parts | 1 |
| Used / waste | 57.0% / 1.23 m2 |
| Reusable offcuts | 1 |
| Saw cuts / shared | 2 / 0 |

### PIECES (POSITION = BOTTOM-LEFT CORNER)

| Label | Size | X, Y |
|---|---|---|
| FF-EX11 S01 | 700 x 2337 | 0, 0 |

### NOTES

1. Cut from OSB/3 9mm 1197x2397, 2mm saw kerf. Viewed on the face; dimensions from the sheet's bottom-left corner (0,0). Red numbered lines = saw cuts in order, each edge to edge.
2. Coloured dimensions belong to the part of that colour: its width and height, and its position from the sheet edges. Raked parts: corner coordinates at each corner.
3. Red hatch = waste. Labels = panel + piece mark on the manufacture drawing.

### REVISIONS

| REV | DATE | DESCRIPTION |
|---|---|---|
| C01 | 14.09.26 | Construction issue |
| C02 | 14.09.26 | Roof trusses revised; SP diagonals added |
| C03 | 11.10.26 | FF windows coursed; steel + GP1 portal; steel drawings (ST) |
| C04 | 13.10.26 | Steel approved by the engineer: steel + steel timber drawings issued for construction |

TLS TIMBER FRAME
Design & Manufacture
Scan: 3D model + drawings

| CLIENT | PROJECT |
|---|---|
| MP Adams | MP Adams Plot 4, Eckington |


DRAWING TITLE
**OSB CUTTING - FIRST FLOOR - SHEET 23 OF 31**

OSB/3 9mm 1197x2397 | First Floor

| SCALE | SIZE | DATE | DRAWN |
|---|---|---|---|
| NTS | A3 | 13.10.26 | TS |

| STATUS | DRAWING No. | REV |
|---|---|---|
| CONSTRUCTION | P4-CP-OSB-02 / 23 | C04 |

Do not scale. All dimensions in mm. Check all dimensions on site.

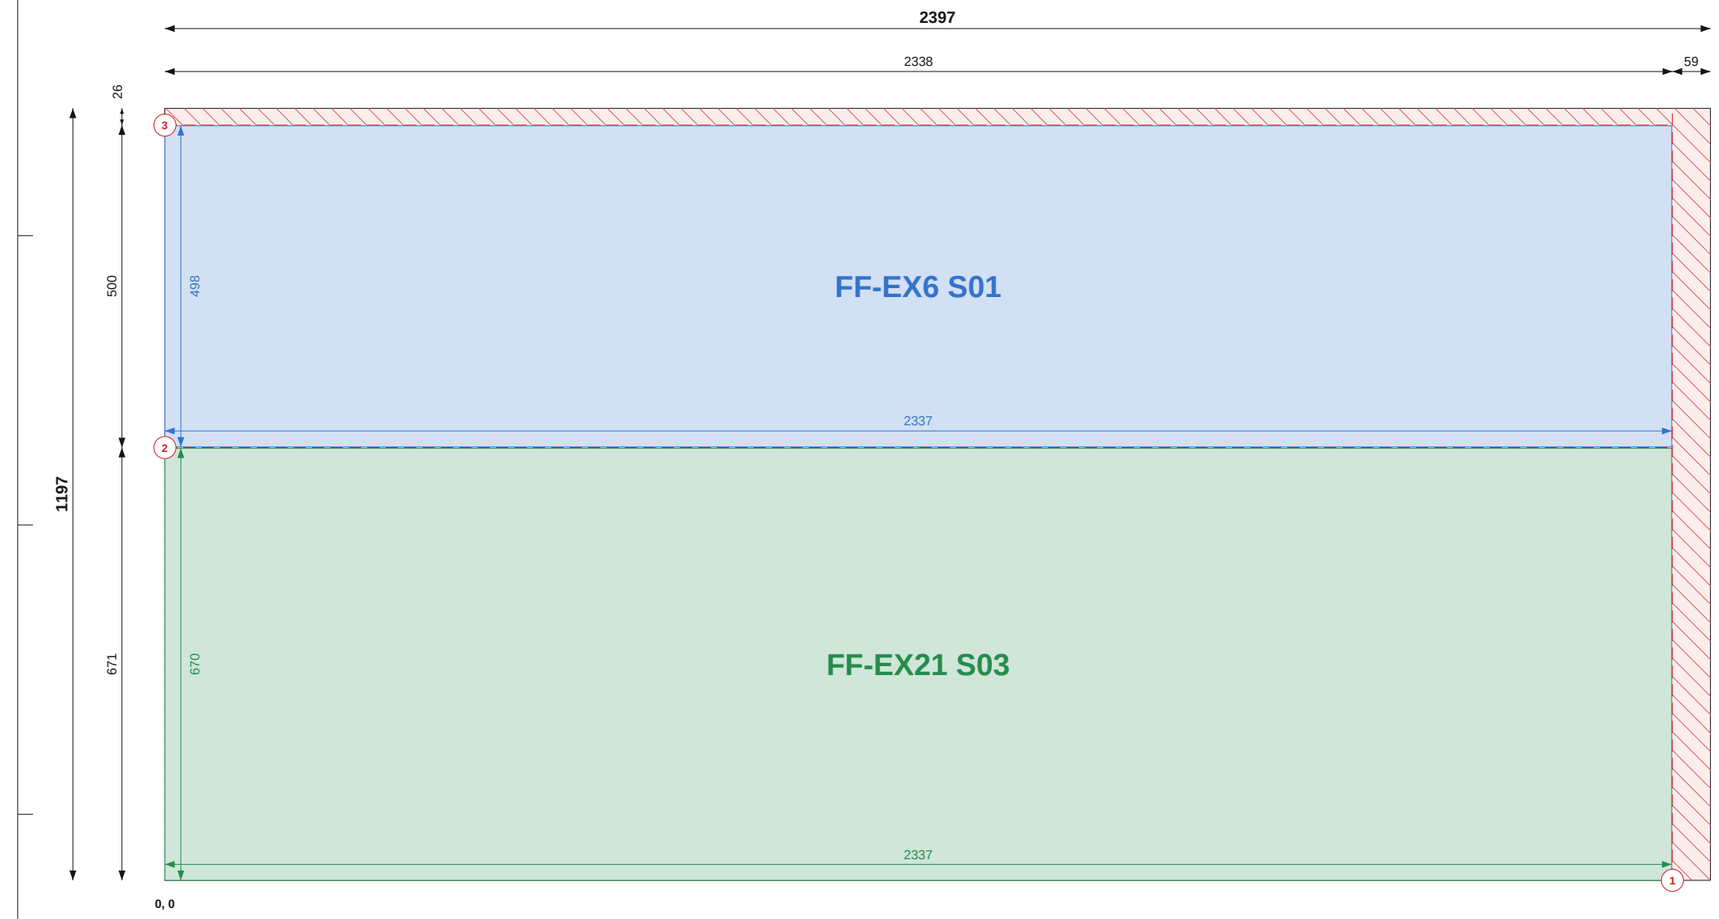


Top / left chains = saw cut positions (to cut centres). Coloured = part size and position.

Do not scale. All dimensions in mm. Check all dimensions on site.

## SHEET 24 OF 31

### THIS SHEET

| Item | Value |
|---|---|
| Parts | 2 |
| Used / waste | 95.1% / 0.14 m2 |
| Reusable offcuts | 0 |
| Saw cuts / shared | 3 / 1 |

### PIECES (POSITION = BOTTOM-LEFT CORNER)

| Label | Size | X, Y |
|---|---|---|
| FF-EX6 S01 | 498 x 2337 | 0, 672 |
| FF-EX21 S03 | 670 x 2337 | 0, 0 |

### NOTES

1. Cut from OSB/3 9mm 1197x2397, 2mm saw kerf. Viewed on the face; dimensions from the sheet's bottom-left corner (0,0). Red numbered lines = saw cuts in order, each edge to edge.
2. Coloured dimensions belong to the part of that colour: its width and height, and its position from the sheet edges. Raked parts: corner coordinates at each corner.
3. Red hatch = waste. Labels = panel + piece mark on the manufacture drawing.

### REVISIONS

| REV | DATE | DESCRIPTION |
|---|---|---|
| C01 | 14.09.26 | Construction issue |
| C02 | 14.09.26 | Roof trusses revised; SP diagonals added |
| C03 | 11.10.26 | FF windows coursed; steel + GP1 portal; steel drawings (ST) |
| C04 | 13.10.26 | Steel approved by the engineer: steel + steel timber drawings issued for construction |

TLS TIMBER FRAME
Design & Manufacture
Scan: 3D model + drawings

| CLIENT | PROJECT |
|---|---|
| MP Adams | MP Adams Plot 4, Eckington |

DRAWING TITLE
**OSB CUTTING - FIRST FLOOR - SHEET 24 OF 31**

OSB/3 9mm 1197x2397 | First Floor

| SCALE | SIZE | DATE | DRAWN |
|---|---|---|---|
| NTS | A3 | 13.10.26 | TS |

| STATUS | DRAWING No. | REV |
|---|---|---|
| CONSTRUCTION | P4-CP-OSB-02 / 24 | C04 |




Top / left chains = saw cut positions (to cut centres). Coloured = part size and position.

## SHEET 25 OF 31

### THIS SHEET

| Item | Value |
|---|---|
| Parts | 2 |
| Used / waste | 96.7% / 0.09 m2 |
| Reusable offcuts | 0 |
| Saw cuts / shared | 3 / 1 |

### PIECES (POSITION = BOTTOM-LEFT CORNER)

| Label | Size | X, Y |
|---|---|---|
| FF-EX11 S02 | 525 x 2337 | 0, 664 |
| FF-EX10 S01 | 662 x 2337 | 0, 0 |

### NOTES

1. Cut from OSB/3 9mm 1197x2397, 2mm saw kerf. Viewed on the face; dimensions from the sheet's bottom-left corner (0,0). Red numbered lines = saw cuts in order, each edge to edge.
2. Coloured dimensions belong to the part of that colour: its width and height, and its position from the sheet edges. Raked parts: corner coordinates at each corner.
3. Red hatch = waste. Labels = panel + piece mark on the manufacture drawing.

### REVISIONS

| REV | DATE | DESCRIPTION |
|---|---|---|
| C01 | 14.09.26 | Construction issue |
| C02 | 14.09.26 | Roof trusses revised; SP diagonals added |
| C03 | 11.10.26 | FF windows coursed; steel + GP1 portal; steel drawings (ST) |
| C04 | 13.10.26 | Steel approved by the engineer: steel + steel timber drawings issued for construction |

TLS TIMBER FRAME
Design & Manufacture
Scan: 3D model + drawings

| CLIENT | PROJECT |
|---|---|
| MP Adams | MP Adams Plot 4, Eckington |


DRAWING TITLE
**OSB CUTTING - FIRST FLOOR - SHEET 25 OF 31**

OSB/3 9mm 1197x2397 | First Floor

| SCALE | SIZE | DATE | DRAWN |
|---|---|---|---|
| NTS | A3 | 13.10.26 | TS |

| STATUS | DRAWING No. | REV |
|---|---|---|
| CONSTRUCTION | P4-CP-OSB-02 / 25 | C04 |

Do not scale. All dimensions in mm. Check all dimensions on site.

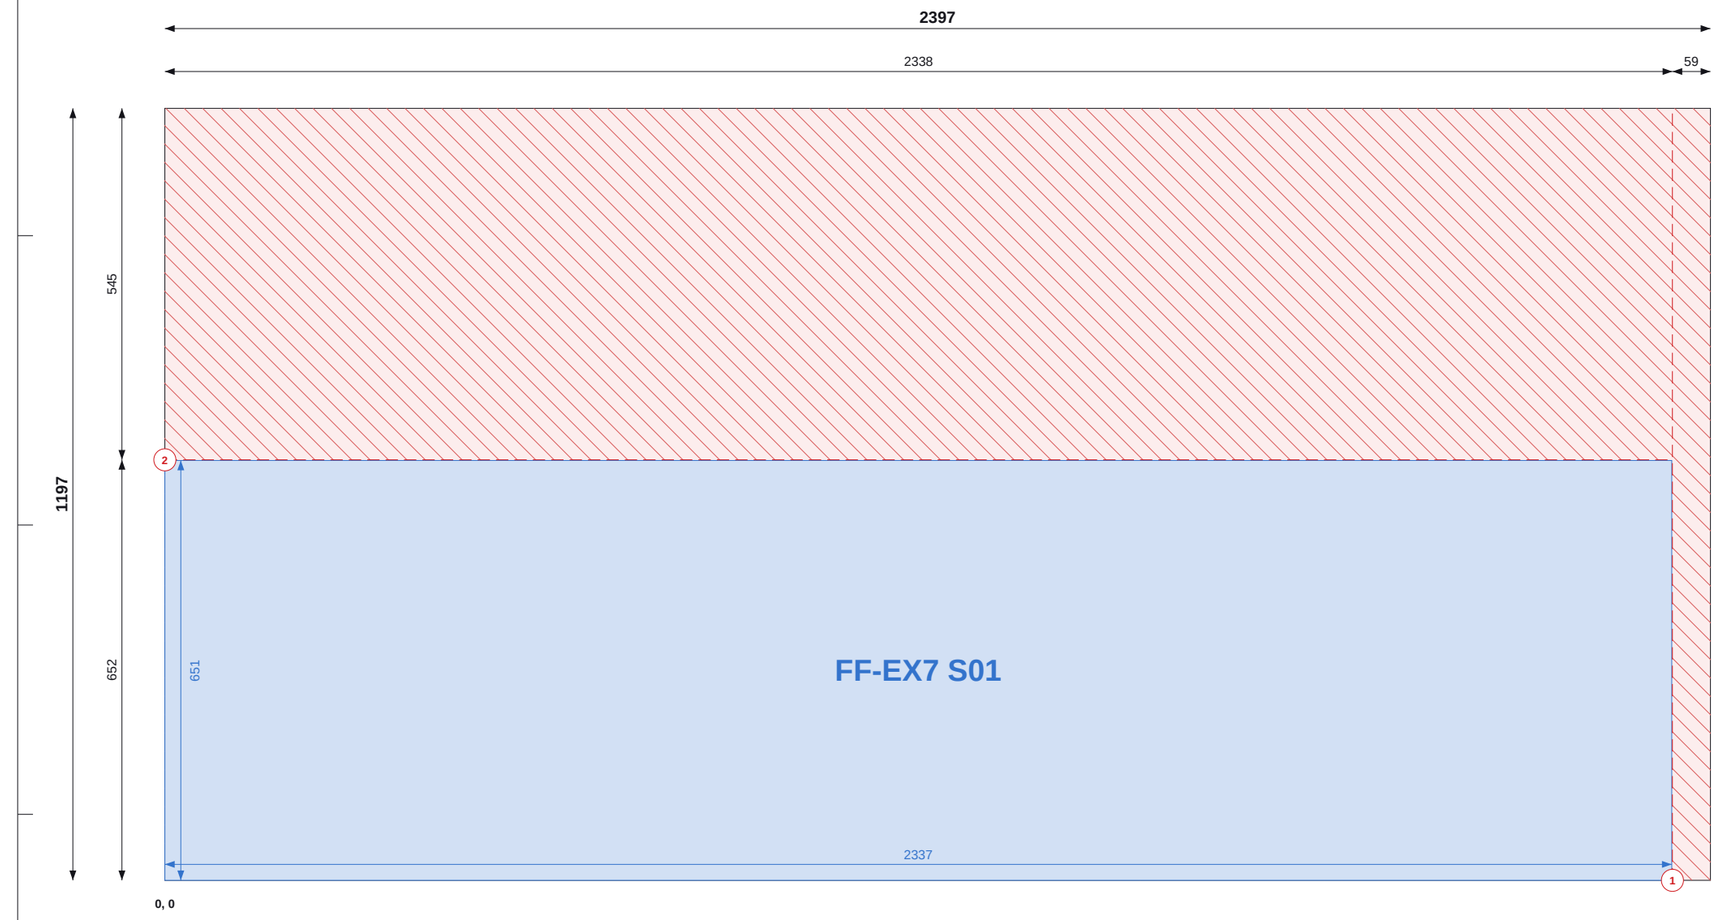


Top / left chains = saw cut positions (to cut centres). Coloured = part size and position.

Do not scale. All dimensions in mm. Check all dimensions on site.

## SHEET 26 OF 31

### THIS SHEET

| Item | Value |
|---|---|
| Parts | 1 |
| Used / waste | 53.0% / 1.35 m2 |
| Reusable offcuts | 1 |
| Saw cuts / shared | 2 / 0 |

### PIECES (POSITION = BOTTOM-LEFT CORNER)

| Label | Size | X, Y |
|---|---|---|
| FF-EX7 S01 | 651 x 2337 | 0, 0 |

### NOTES

1. Cut from OSB/3 9mm 1197x2397, 2mm saw kerf. Viewed on the face; dimensions from the sheet's bottom-left corner (0,0). Red numbered lines = saw cuts in order, each edge to edge.
2. Coloured dimensions belong to the part of that colour: its width and height, and its position from the sheet edges. Raked parts: corner coordinates at each corner.
3. Red hatch = waste. Labels = panel + piece mark on the manufacture drawing.

### REVISIONS

| REV | DATE | DESCRIPTION |
|---|---|---|
| C01 | 14.09.26 | Construction issue |
| C02 | 14.09.26 | Roof trusses revised; SP diagonals added |
| C03 | 11.10.26 | FF windows coursed; steel + GP1 portal; steel drawings (ST) |
| C04 | 13.10.26 | Steel approved by the engineer: steel + steel timber drawings issued for construction |

TLS TIMBER FRAME
Design & Manufacture
Scan: 3D model + drawings


| CLIENT | PROJECT |
|---|---|
| MP Adams | MP Adams Plot 4, Eckington |

DRAWING TITLE
**OSB CUTTING - FIRST FLOOR - SHEET 26 OF 31**

OSB/3 9mm 1197x2397 | First Floor

| SCALE | SIZE | DATE | DRAWN |
|---|---|---|---|
| NTS | A3 | 13.10.26 | TS |

| STATUS | DRAWING No. | REV |
|---|---|---|
| CONSTRUCTION | P4-CP-OSB-02 / 26 | C04 |

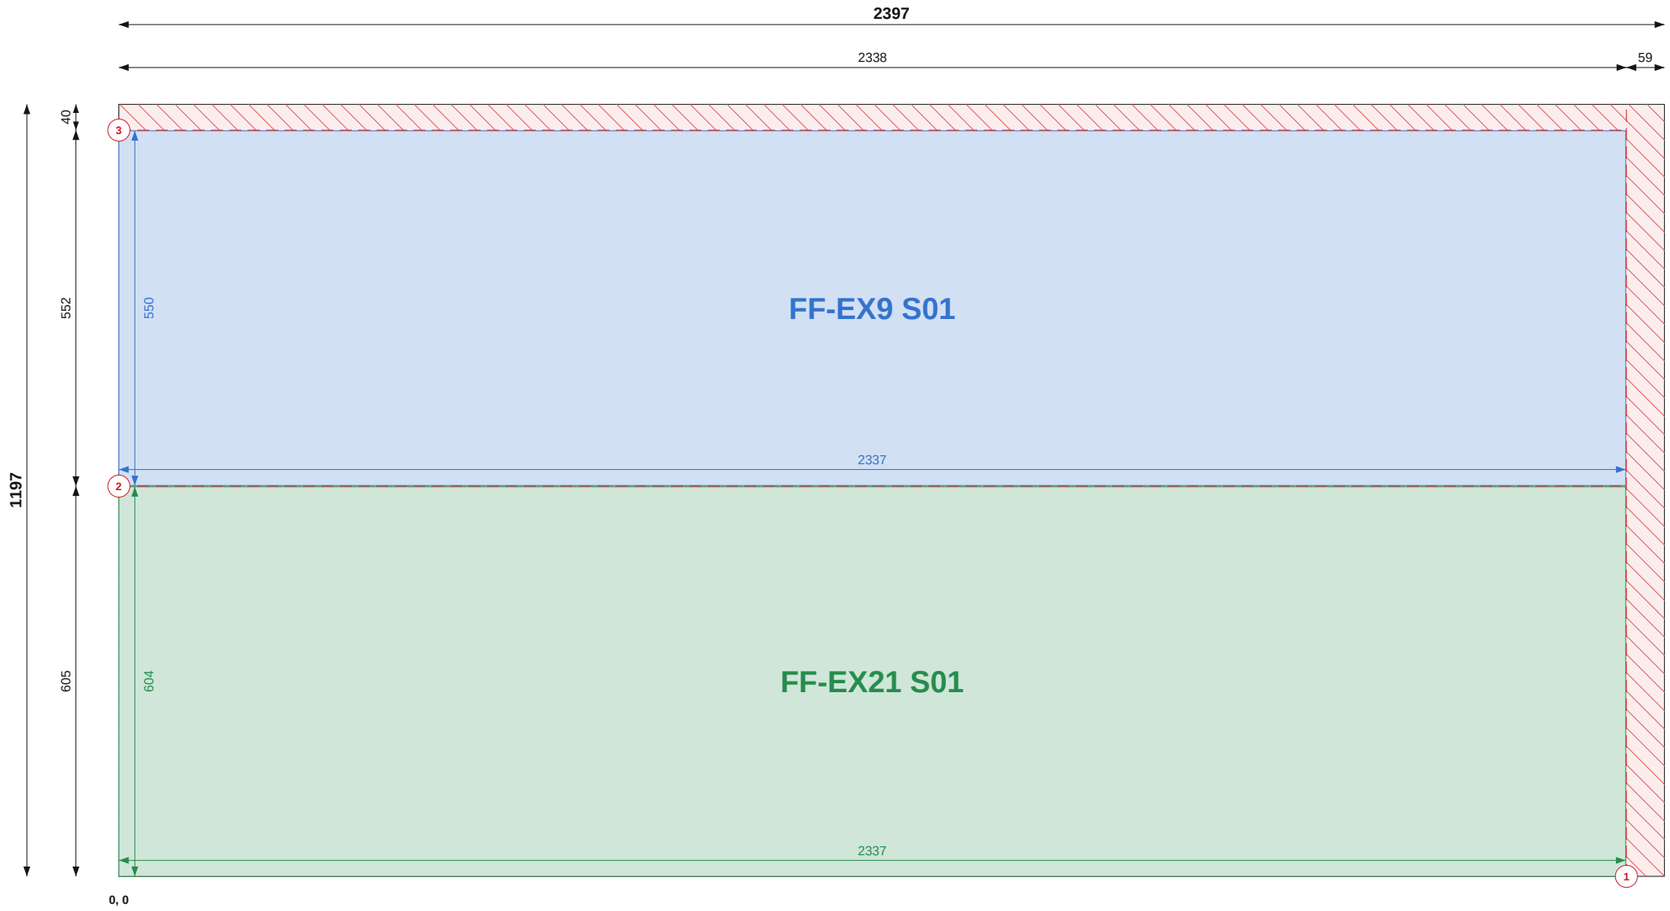


Top / left chains = saw cut positions (to cut centres). Coloured = part size and position.

## SHEET 27 OF 31

### THIS SHEET

| Item | Value |
|---|---|
| Parts | 2 |
| Used / waste | 94.0% / 0.17 m2 |
| Reusable offcuts | 0 |
| Saw cuts / shared | 3 / 1 |

### PIECES (POSITION = BOTTOM-LEFT CORNER)

| Label | Size | X, Y |
|---|---|---|
| FF-EX9 S01 | 550 x 2337 | 0, 606 |
| FF-EX21 S01 | 604 x 2337 | 0, 0 |

### NOTES

1. Cut from OSB/3 9mm 1197x2397, 2mm saw kerf. Viewed on the face; dimensions from the sheet's bottom-left corner (0,0). Red numbered lines = saw cuts in order, each edge to edge.
2. Coloured dimensions belong to the part of that colour: its width and height, and its position from the sheet edges. Raked parts: corner coordinates at each corner.
3. Red hatch = waste. Labels = panel + piece mark on the manufacture drawing.

### REVISIONS

| REV | DATE | DESCRIPTION |
|---|---|---|
| C01 | 14.09.26 | Construction issue |
| C02 | 14.09.26 | Roof trusses revised; SP diagonals added |
| C03 | 11.10.26 | FF windows coursed; steel + GP1 portal; steel drawings (ST) |
| C04 | 13.10.26 | Steel approved by the engineer: steel + steel timber drawings issued for construction |

TLS TIMBER FRAME
Design & Manufacture
Scan: 3D model + drawings

| CLIENT | PROJECT |
|---|---|
| MP Adams | MP Adams Plot 4, Eckington |


DRAWING TITLE
**OSB CUTTING - FIRST FLOOR - SHEET 27 OF 31**

OSB/3 9mm 1197x2397 | First Floor

| SCALE | SIZE | DATE | DRAWN |
|---|---|---|---|
| NTS | A3 | 13.10.26 | TS |

| STATUS | DRAWING No. | REV |
|---|---|---|
| CONSTRUCTION | P4-CP-OSB-02 / 27 | C04 |

Do not scale. All dimensions in mm. Check all dimensions on site.

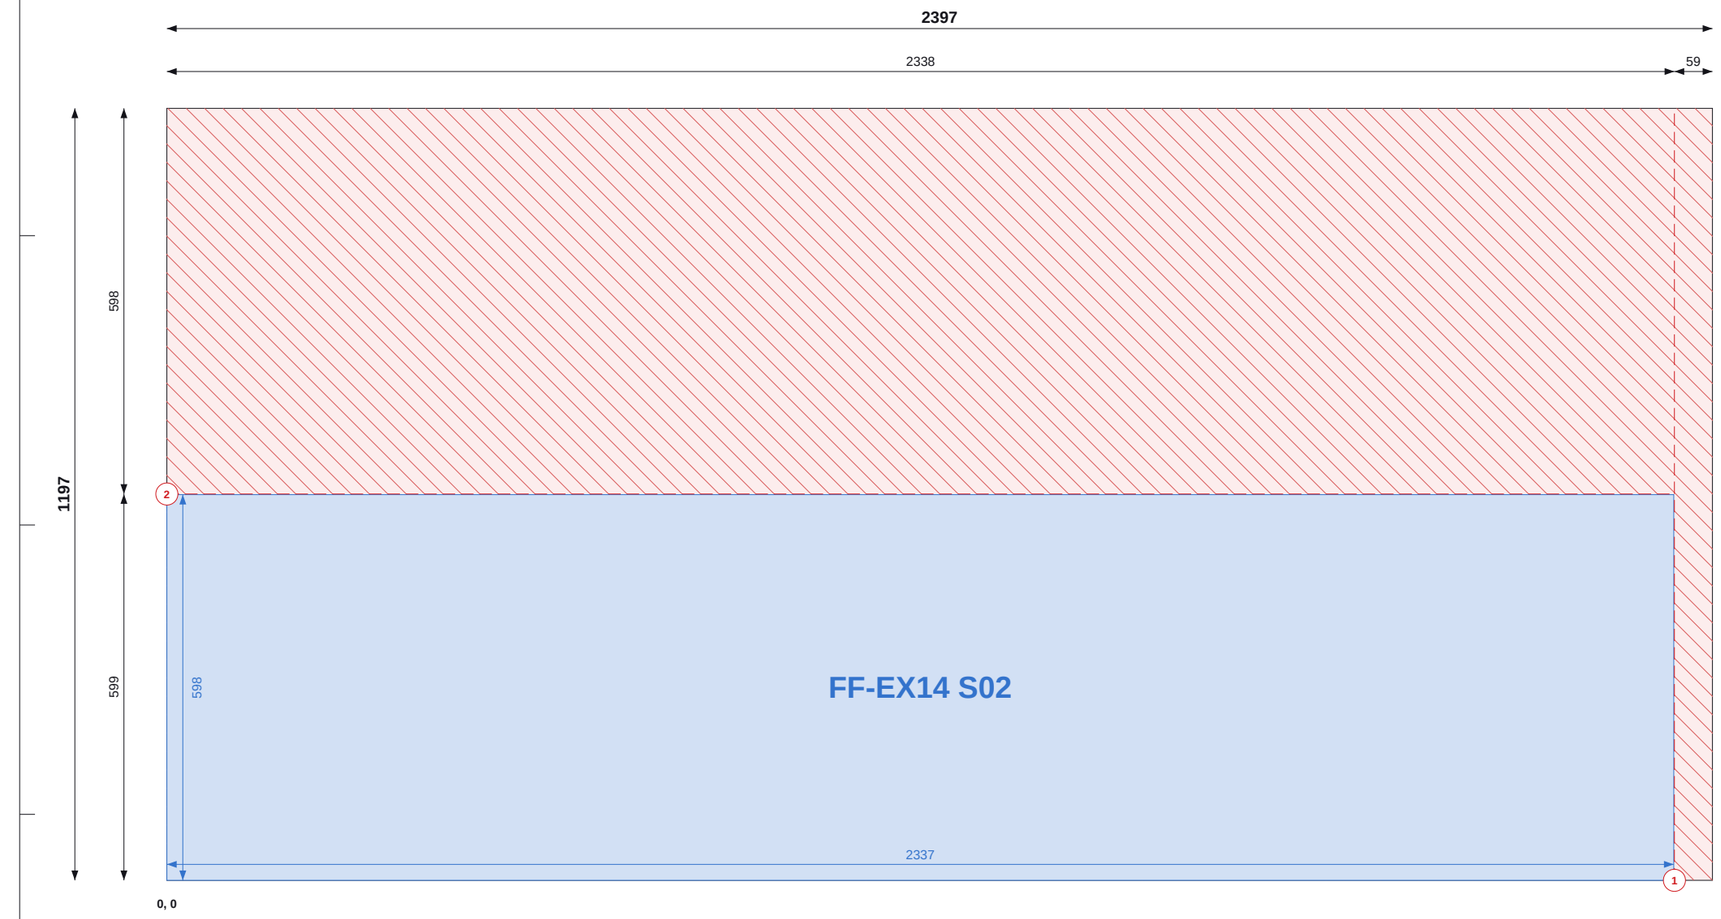


Top / left chains = saw cut positions (to cut centres). Coloured = part size and position.

Do not scale. All dimensions in mm. Check all dimensions on site.

## SHEET 28 OF 31

### THIS SHEET

| Item | Value |
|---|---|
| Parts | 1 |
| Used / waste | 48.7% / 1.47 m2 |
| Reusable offcuts | 1 |
| Saw cuts / shared | 2 / 0 |

### PIECES (POSITION = BOTTOM-LEFT CORNER)

| Label | Size | X, Y |
|---|---|---|
| FF-EX14 S02 | 598 x 2337 | 0, 0 |

### NOTES

1. Cut from OSB/3 9mm 1197x2397, 2mm saw kerf. Viewed on the face; dimensions from the sheet's bottom-left corner (0,0). Red numbered lines = saw cuts in order, each edge to edge.
2. Coloured dimensions belong to the part of that colour: its width and height, and its position from the sheet edges. Raked parts: corner coordinates at each corner.
3. Red hatch = waste. Labels = panel + piece mark on the manufacture drawing.

### REVISIONS

| REV | DATE | DESCRIPTION |
|---|---|---|
| C01 | 14.09.26 | Construction issue |
| C02 | 14.09.26 | Roof trusses revised; SP diagonals added |
| C03 | 11.10.26 | FF windows coursed; steel + GP1 portal; steel drawings (ST) |
| C04 | 13.10.26 | Steel approved by the engineer: steel + steel timber drawings issued for construction |

TLS TIMBER FRAME
Design & Manufacture
Scan: 3D model + drawings


| CLIENT | PROJECT |
|---|---|
| MP Adams | MP Adams Plot 4, Eckington |

DRAWING TITLE
**OSB CUTTING - FIRST FLOOR - SHEET 28 OF 31**

OSB/3 9mm 1197x2397 | First Floor

| SCALE | SIZE | DATE | DRAWN |
|---|---|---|---|
| NTS | A3 | 13.10.26 | TS |

| STATUS | DRAWING No. | REV |
|---|---|---|
| CONSTRUCTION | P4-CP-OSB-02 / 28 | C04 |

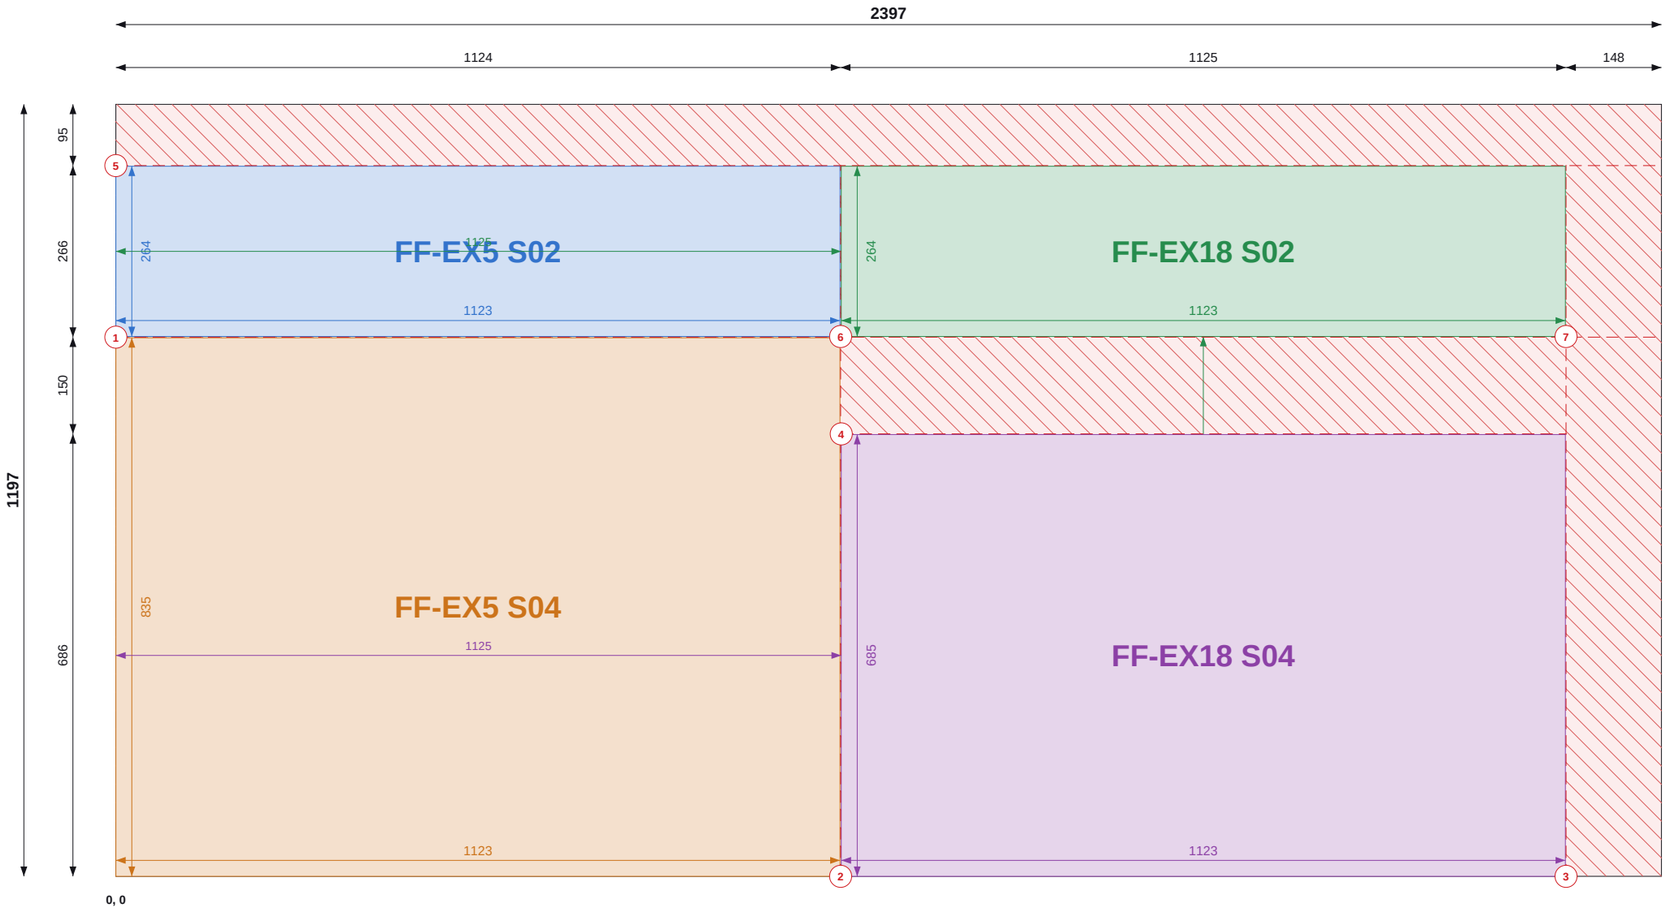


Top / left chains = saw cut positions (to cut centres). Coloured = part size and position.

## SHEET 29 OF 31

### THIS SHEET

| Item | Value |
|---|---|
| Parts | 4 |
| Used / waste | 80.2% / 0.57 m2 |
| Reusable offcuts | 0 |
| Saw cuts / shared | 7 / 3 |

### PIECES (POSITION = BOTTOM-LEFT CORNER)

| Label | Size | X, Y |
|---|---|---|
| FF-EX5 S02 | 1123 x 264 | 0, 837 |
| FF-EX18 S02 | 1123 x 264 | 1125, 837 |
| FF-EX5 S04 | 1123 x 835 | 0, 0 |
| FF-EX18 S04 | 1123 x 685 | 1125, 0 |

### NOTES

1. Cut from OSB/3 9mm 1197x2397, 2mm saw kerf. Viewed on the face; dimensions from the sheet's bottom-left corner (0,0). Red numbered lines = saw cuts in order, each edge to edge.
2. Coloured dimensions belong to the part of that colour: its width and height, and its position from the sheet edges. Raked parts: corner coordinates at each corner.
3. Red hatch = waste. Labels = panel + piece mark on the manufacture drawing.

### REVISIONS

| REV | DATE | DESCRIPTION |
|---|---|---|
| C01 | 14.09.26 | Construction issue |
| C02 | 14.09.26 | Roof trusses revised; SP diagonals added |
| C03 | 11.10.26 | FF windows coursed; steel + GP1 portal; steel drawings (ST) |
| C04 | 13.10.26 | Steel approved by the engineer: steel + steel timber drawings issued for construction |

TLS TIMBER FRAME
Design & Manufacture
Scan: 3D model + drawings

| CLIENT | PROJECT |
|---|---|
| MP Adams | MP Adams Plot 4, Eckington |


DRAWING TITLE
**OSB CUTTING - FIRST FLOOR - SHEET 29 OF 31**

OSB/3 9mm 1197x2397 | First Floor

| SCALE | SIZE | DATE | DRAWN |
|---|---|---|---|
| NTS | A3 | 13.10.26 | TS |

| STATUS | DRAWING No. | REV |
|---|---|---|
| CONSTRUCTION | P4-CP-OSB-02 / 29 | C04 |

Do not scale. All dimensions in mm. Check all dimensions on site.

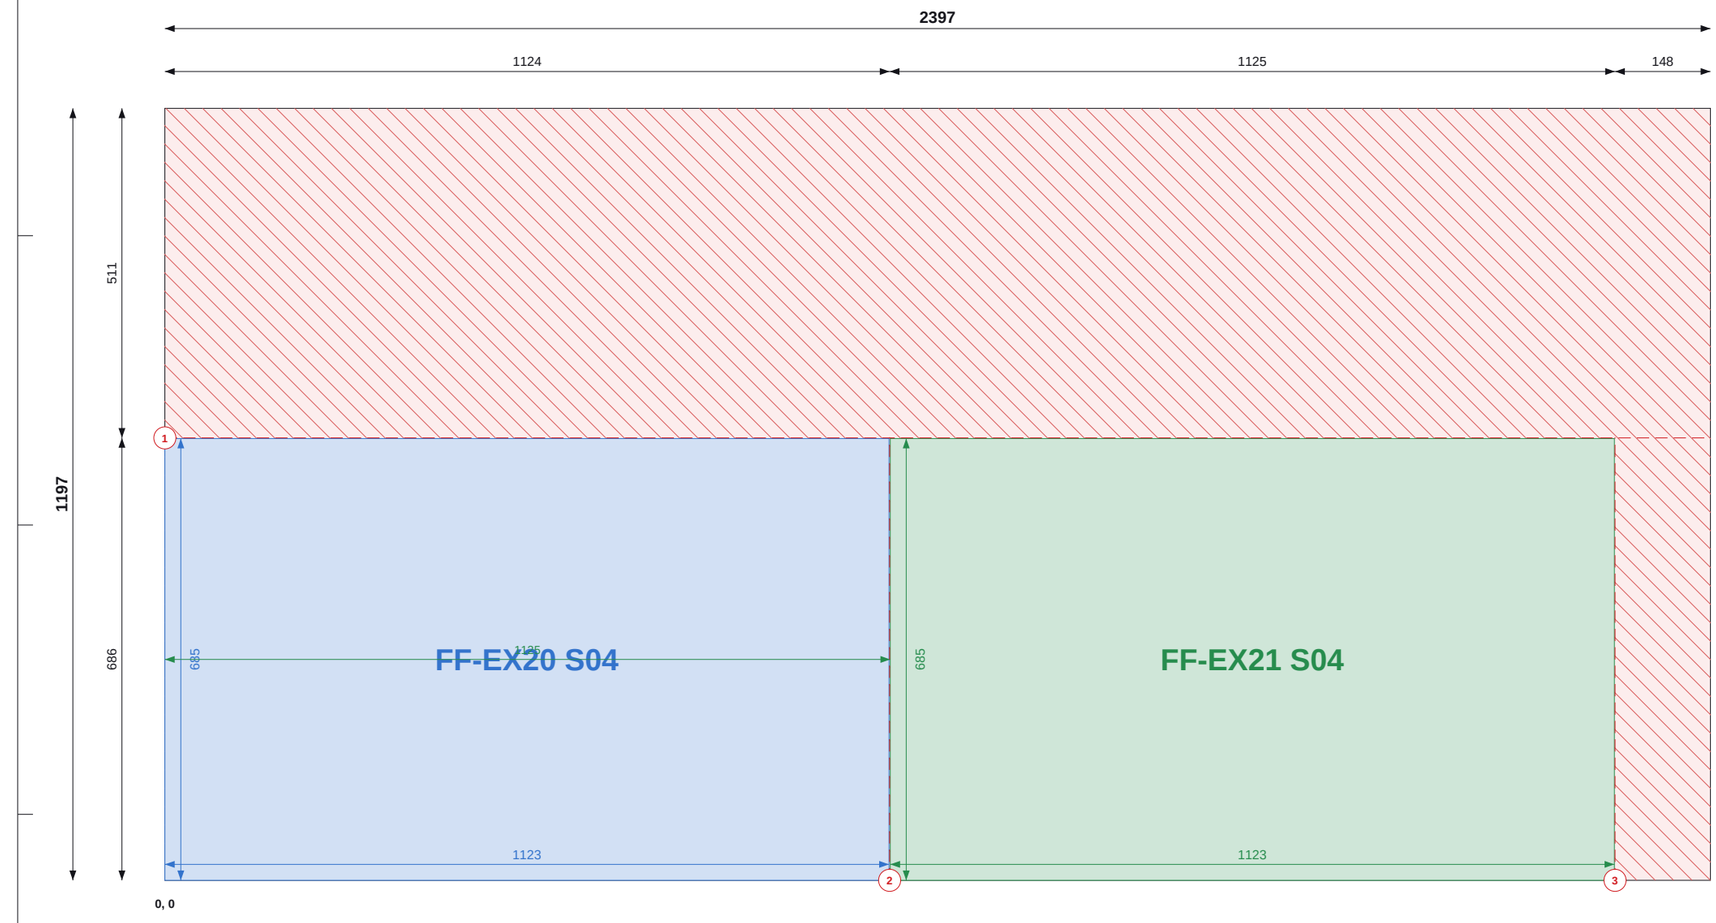


Top / left chains = saw cut positions (to cut centres). Coloured = part size and position.

## SHEET 30 OF 31

### THIS SHEET

| Item | Value |
|---|---|
| Parts | 2 |
| Used / waste | 53.6% / 1.33 m2 |
| Reusable offcuts | 1 |
| Saw cuts / shared | 3 / 1 |

### PIECES (POSITION = BOTTOM-LEFT CORNER)

| Label | Size | X, Y |
|---|---|---|
| FF-EX20 S04 | 1123 x 685 | 0, 0 |
| FF-EX21 S04 | 1123 x 685 | 1125, 0 |

### NOTES

1. Cut from OSB/3 9mm 1197x2397, 2mm saw kerf. Viewed on the face; dimensions from the sheet's bottom-left corner (0,0). Red numbered lines = saw cuts in order, each edge to edge.
2. Coloured dimensions belong to the part of that colour: its width and height, and its position from the sheet edges. Raked parts: corner coordinates at each corner.
3. Red hatch = waste. Labels = panel + piece mark on the manufacture drawing.

### REVISIONS

| REV | DATE | DESCRIPTION |
|---|---|---|
| C01 | 14.09.26 | Construction issue |
| C02 | 14.09.26 | Roof trusses revised; SP diagonals added |
| C03 | 11.10.26 | FF windows coursed; steel + GP1 portal; steel drawings (ST) |
| C04 | 13.10.26 | Steel approved by the engineer: steel + steel timber drawings issued for construction |

TLS TIMBER FRAME DESIGN SUITE

**TLS TIMBER FRAME**

Design & Manufacture

Scan: 3D model + drawings

| CLIENT | PROJECT |
|---|---|
| MP Adams | MP Adams Plot 4, Eckington |

DRAWING TITLE


**OSB CUTTING - FIRST FLOOR - SHEET 30 OF 31**

OSB/3 9mm 1197x2397 | First Floor

| SCALE | SIZE | DATE | DRAWN |
|---|---|---|---|
| NTS | A3 | 13.10.26 | TS |

| STATUS | DRAWING No. | REV |
|---|---|---|
| CONSTRUCTION | P4-CP-OSB-02 / 30 | C04 |

Do not scale. All dimensions in mm. Check all dimensions on site.

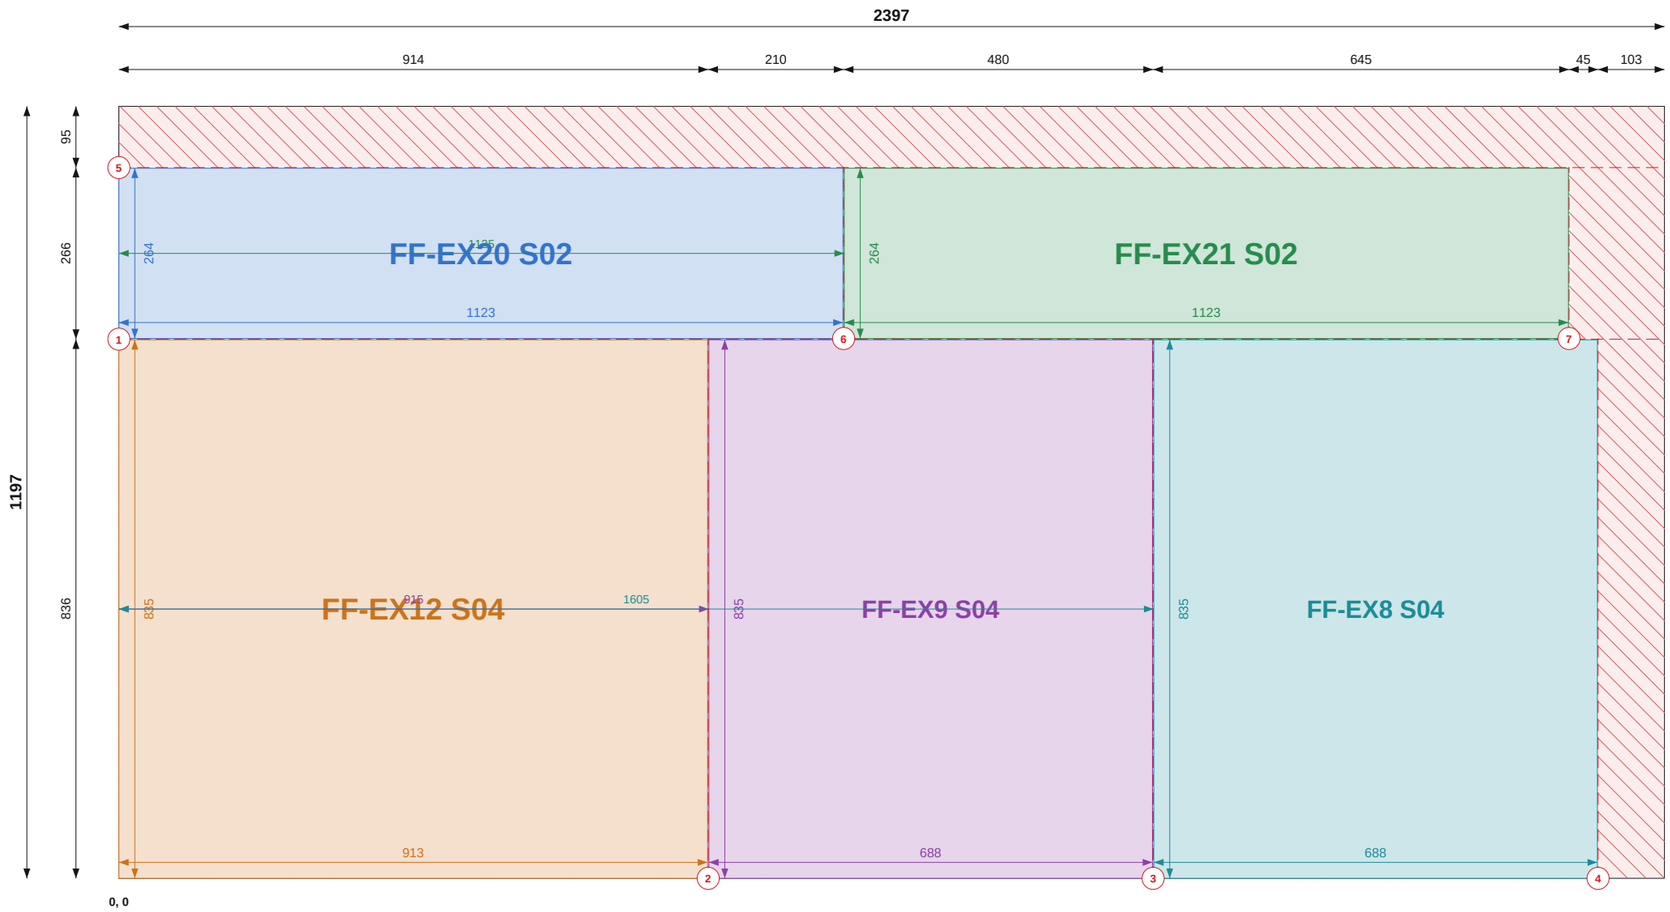


Top / left chains = saw cut positions (to cut centres). Coloured = part size and position.

## SHEET 31 OF 31

### THIS SHEET

| Item | Value |
|---|---|
| Parts | 5 |
| Used / waste | 87.3% / 0.36 m2 |
| Reusable offcuts | 0 |
| Saw cuts / shared | 7 / 4 |

### PIECES (POSITION = BOTTOM-LEFT CORNER)

| Label | Size | X, Y |
|---|---|---|
| FF-EX20 S02 | 1123 x 264 | 0, 837 |
| FF-EX21 S02 | 1123 x 264 | 1125, 837 |
| FF-EX12 S04 | 913 x 835 | 0, 0 |
| FF-EX9 S04 | 688 x 835 | 915, 0 |
| FF-EX8 S04 | 688 x 835 | 1605, 0 |

### NOTES

1. Cut from OSB/3 9mm 1197x2397, 2mm saw kerf. Viewed on the face; dimensions from the sheet's bottom-left corner (0,0). Red numbered lines = saw cuts in order, each edge to edge.
2. Coloured dimensions belong to the part of that colour: its width and height, and its position from the sheet edges. Raked parts: corner coordinates at each corner.
3. Red hatch = waste. Labels = panel + piece mark on the manufacture drawing.

### REVISIONS

| REV | DATE | DESCRIPTION |
|---|---|---|
| C01 | 14.09.26 | Construction issue |
| C02 | 14.09.26 | Roof trusses revised; SP diagonals added |
| C03 | 11.10.26 | FF windows coursed; steel + GP1 portal; steel drawings (ST) |
| C04 | 13.10.26 | Steel approved by the engineer: steel + steel timber drawings issued for construction |

TLS TIMBER FRAME
Design & Manufacture
Scan: 3D model + drawings

| CLIENT | PROJECT |
|---|---|
| MP Adams | MP Adams Plot 4, Eckington |


DRAWING TITLE
**OSB CUTTING - FIRST FLOOR - SHEET 31 OF 31**

OSB/3 9mm 1197x2397 | First Floor

| SCALE | SIZE | DATE | DRAWN |
|---|---|---|---|
| NTS | A3 | 13.10.26 | TS |

| STATUS | DRAWING No. | REV |
|---|---|---|
| CONSTRUCTION | P4-CP-OSB-02 / 31 | C04 |

Do not scale. All dimensions in mm. Check all dimensions on site.

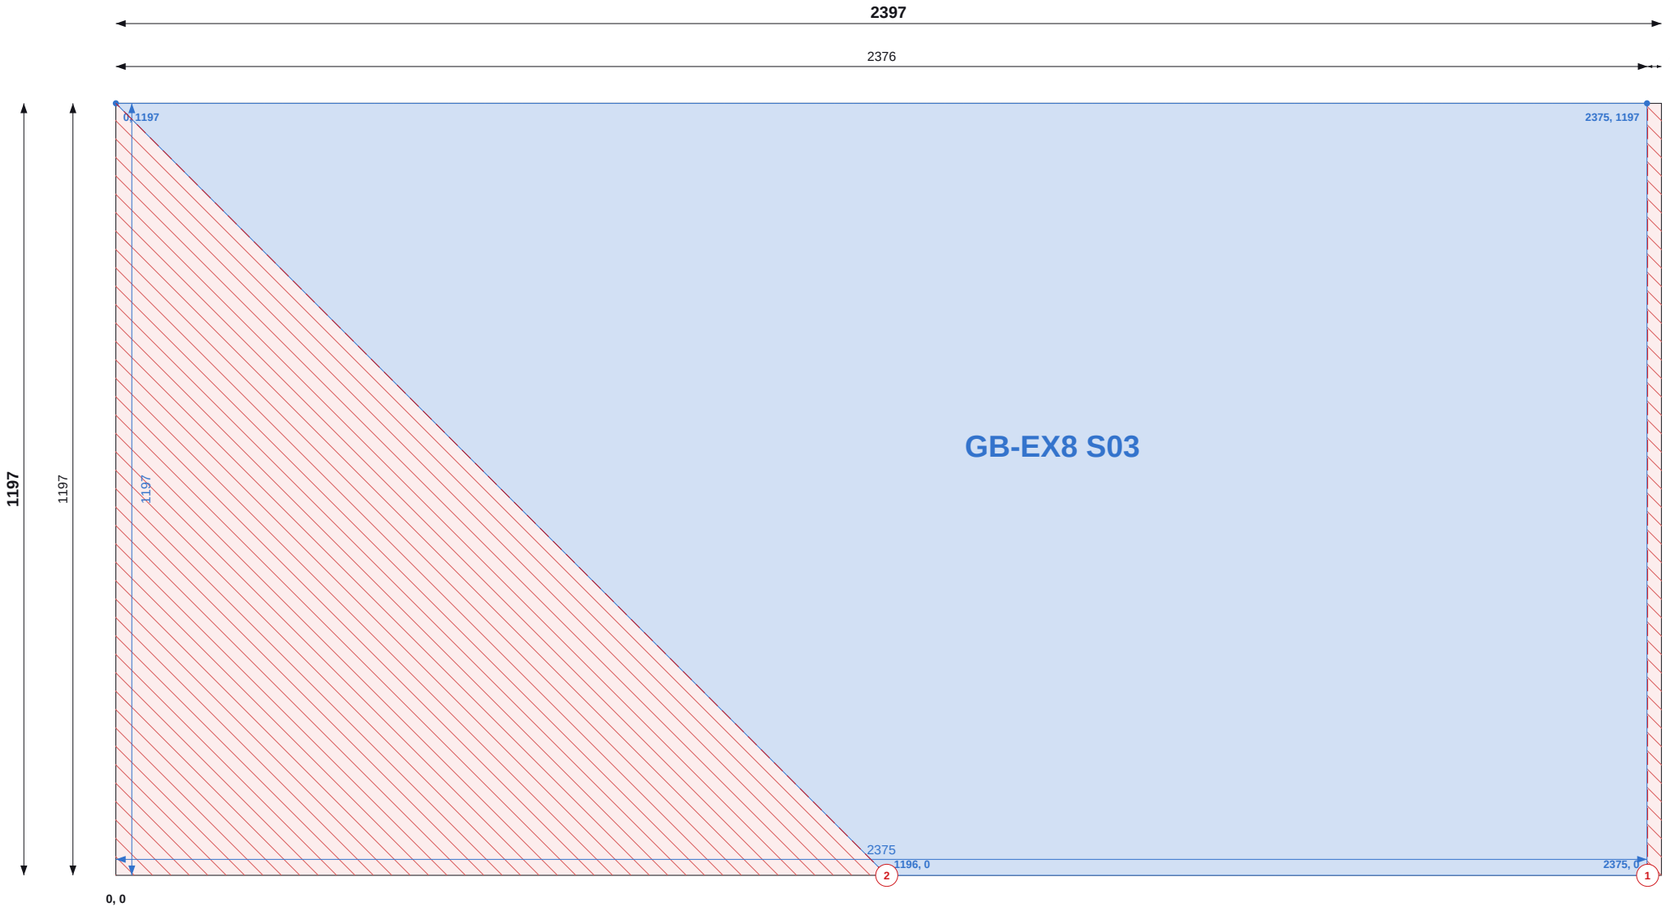


Top / left chains = saw cut positions (to cut centres). Coloured = part size and position.

## SHEET 1 OF 21

### THIS SHEET

| Item | Value |
|---|---|
| Parts | 1 |
| Used / waste | 74.1% / 0.74 m2 |
| Reusable offcuts | 0 |
| Saw cuts / shared | 2 / 1 |

### PIECES (POSITION = BOTTOM-LEFT CORNER)

| Label | Size | X, Y |
|---|---|---|
| GB-EX8 S03 | 1197 x 2374 rake to 1180 | 0, 0 |

### GABLES TOTALS

| Item | Value |
|---|---|
| Sheets / pieces | 21 / 51 |
| Yield / waste | 84.5% / 9.34 m2 |
| Saw cuts / shared / on stock edge | 79 / 50 / 82 |

### NOTES

1. Cut from OSB/3 9mm 1197x2397, 2mm saw kerf. Viewed on the face; dimensions from the sheet's bottom-left corner (0,0). Red numbered lines = saw cuts in order, each edge to edge.
2. Coloured dimensions belong to the part of that colour: its width and height, and its position from the sheet edges. Raked parts: corner coordinates at each corner.
3. Red hatch = waste. Labels = panel + piece mark on the manufacture drawing.

### REVISIONS

| REV | DATE | DESCRIPTION |
|---|---|---|
| C01 | 14.09.26 | Construction issue |
| C02 | 14.09.26 | Roof trusses revised; SP diagonals added |
| C03 | 11.10.26 | FF windows coursed; steel + GP1 portal; steel drawings (ST) |
| C04 | 13.10.26 | Steel approved by the engineer: steel + steel timber drawings issued for construction |

TLS

TLS TIMBER FRAME

Design & Manufacture

Scan: 3D model + drawings

| CLIENT | PROJECT |
|---|---|
| MP Adams | MP Adams Plot 4, Eckington |

DRAWING TITLE


**OSB CUTTING - GABLES - SHEET 1 OF 21**

OSB/3 9mm 1197x2397 | Gables

| SCALE | SIZE | DATE | DRAWN |
|---|---|---|---|
| NTS | A3 | 13.10.26 | TS |

| STATUS | DRAWING No. | REV |
|---|---|---|
| CONSTRUCTION | P4-CP-OSB-03 / 01 | C04 |

Do not scale. All dimensions in mm. Check all dimensions on site.

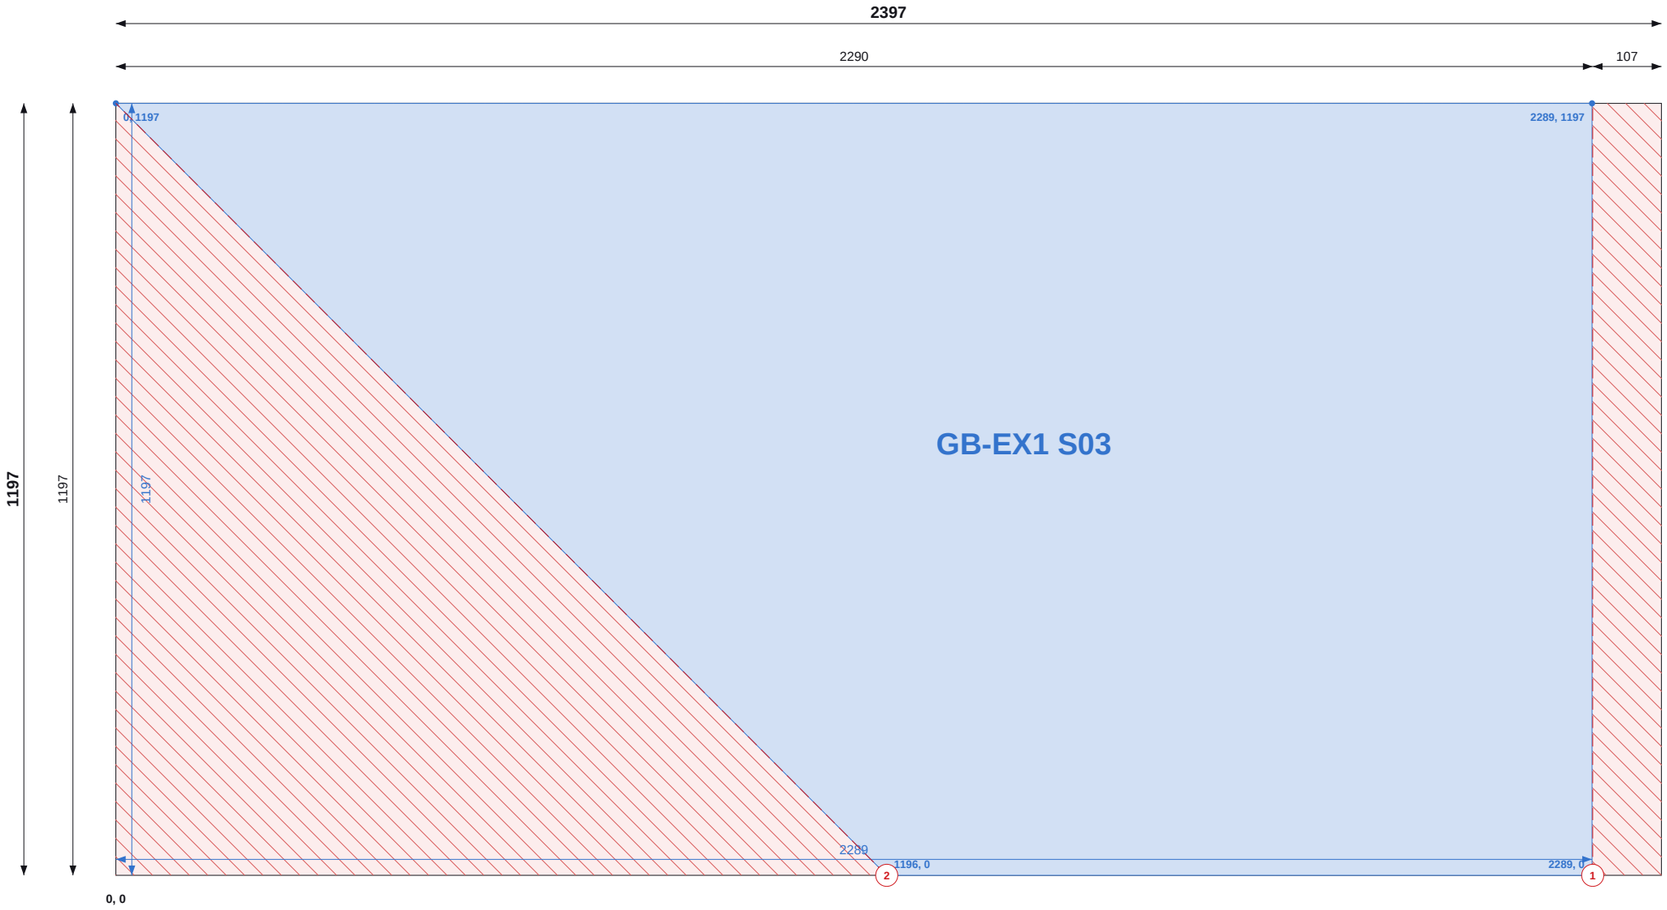


Top / left chains = saw cut positions (to cut centres). Coloured = part size and position.

## SHEET 2 OF 21

### THIS SHEET

| Item | Value |
|---|---|
| Parts | 1 |
| Used / waste | 70.6% / 0.84 m2 |
| Reusable offcuts | 0 |
| Saw cuts / shared | 2 / 1 |

### PIECES (POSITION = BOTTOM-LEFT CORNER)

| Label | Size | X, Y |
|---|---|---|
| GB-EX1 S03 | 1197 x 2289 rake to 1095 | 0, 0 |

### NOTES

1. Cut from OSB/3 9mm 1197x2397, 2mm saw kerf. Viewed on the face; dimensions from the sheet's bottom-left corner (0,0). Red numbered lines = saw cuts in order, each edge to edge.
2. Coloured dimensions belong to the part of that colour: its width and height, and its position from the sheet edges. Raked parts: corner coordinates at each corner.
3. Red hatch = waste. Labels = panel + piece mark on the manufacture drawing.

### REVISIONS

| REV | DATE | DESCRIPTION |
|---|---|---|
| C01 | 14.09.26 | Construction issue |
| C02 | 14.09.26 | Roof trusses revised; SP diagonals added |
| C03 | 11.10.26 | FF windows coursed; steel + GP1 portal; steel drawings (ST) |
| C04 | 13.10.26 | Steel approved by the engineer: steel + steel timber drawings issued for construction |

TLS

TLS TIMBER FRAME

Design & Manufacture

Scan: 3D model + drawings

| CLIENT | PROJECT |
|---|---|
| MP Adams | MP Adams Plot 4, Eckington |

DRAWING TITLE


**OSB CUTTING - GABLES - SHEET 2 OF 21**

OSB/3 9mm 1197x2397 | Gables

| SCALE | SIZE | DATE | DRAWN |
|---|---|---|---|
| NTS | A3 | 13.10.26 | TS |

| STATUS | DRAWING No. | REV |
|---|---|---|
| CONSTRUCTION | P4-CP-OSB-03 / 02 | C04 |

Do not scale. All dimensions in mm. Check all dimensions on site.

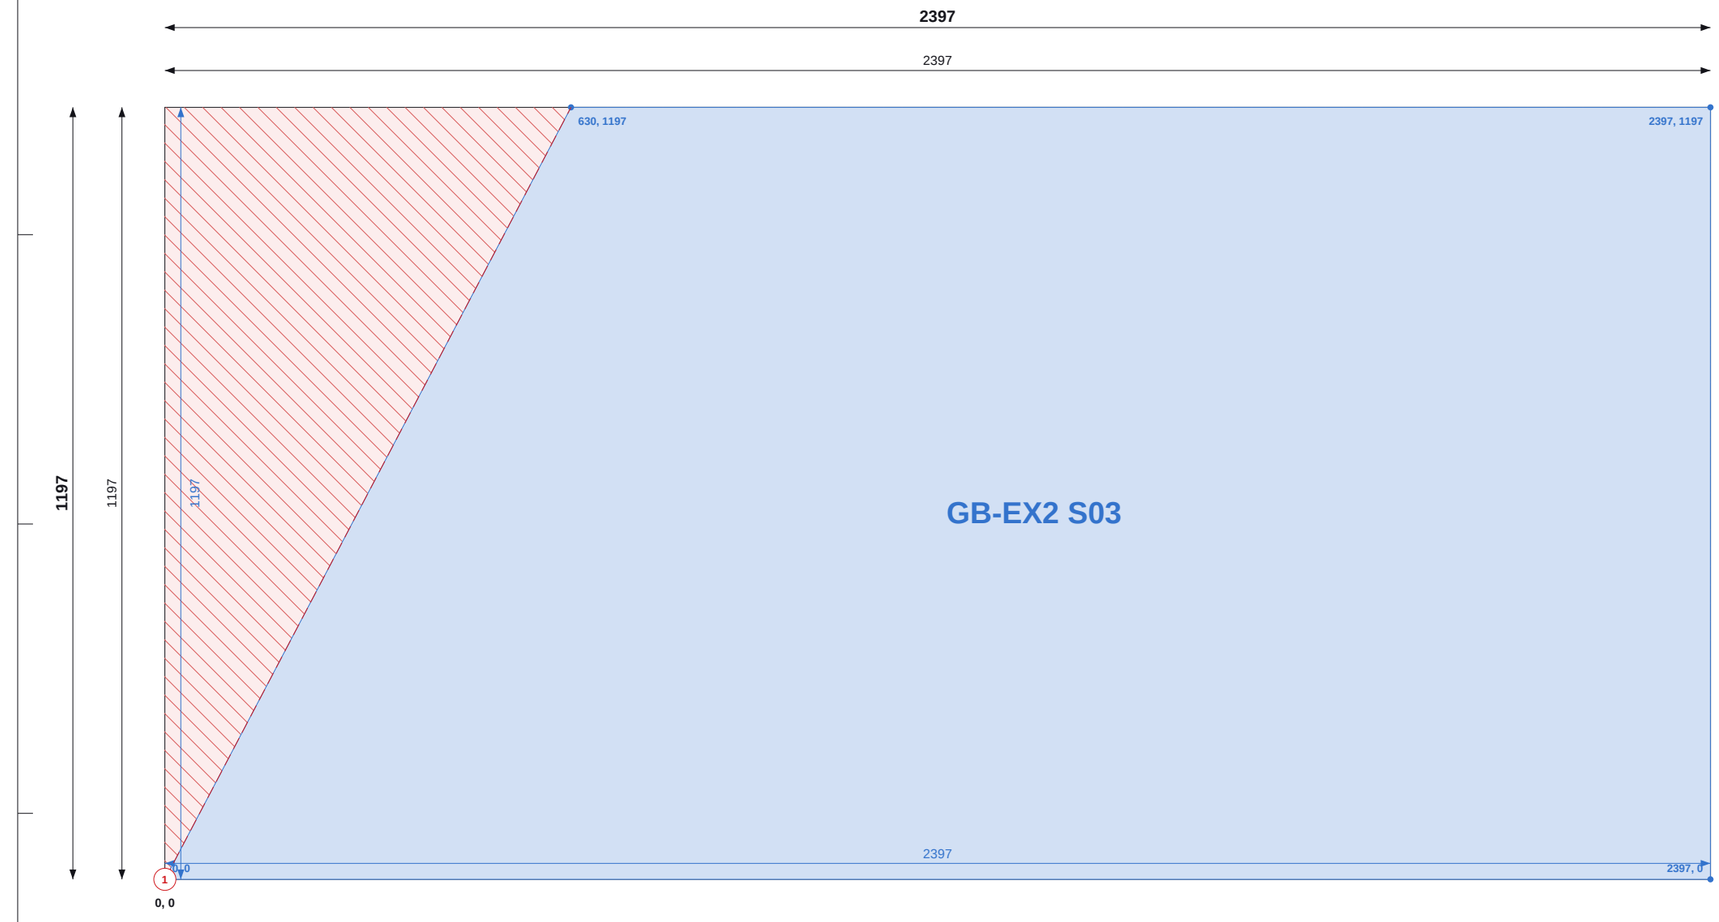


Top / left chains = saw cut positions (to cut centres). Coloured = part size and position.

## SHEET 3 OF 21

### THIS SHEET

| Item | Value |
|---|---|
| Parts | 1 |
| Used / waste | 86.9% / 0.38 m2 |
| Reusable offcuts | 0 |
| Saw cuts / shared | 1 / 1 |

### PIECES (POSITION = BOTTOM-LEFT CORNER)

| Label | Size | X, Y |
|---|---|---|
| GB-EX2 S03 | 1197 x 2397 rake to 1768 | 0, 0 |

### NOTES

1. Cut from OSB/3 9mm 1197x2397, 2mm saw kerf. Viewed on the face; dimensions from the sheet's bottom-left corner (0,0). Red numbered lines = saw cuts in order, each edge to edge.
2. Coloured dimensions belong to the part of that colour: its width and height, and its position from the sheet edges. Raked parts: corner coordinates at each corner.
3. Red hatch = waste. Labels = panel + piece mark on the manufacture drawing.

### REVISIONS

| REV | DATE | DESCRIPTION |
|---|---|---|
| C01 | 14.09.26 | Construction issue |
| C02 | 14.09.26 | Roof trusses revised; SP diagonals added |
| C03 | 11.10.26 | FF windows coursed; steel + GP1 portal; steel drawings (ST) |
| C04 | 13.10.26 | Steel approved by the engineer: steel + steel timber drawings issued for construction |

TLS

TLS TIMBER FRAME

Design & Manufacture

Scan: 3D model + drawings

| CLIENT | PROJECT |
|---|---|
| MP Adams | MP Adams Plot 4, Eckington |

DRAWING TITLE


**OSB CUTTING - GABLES - SHEET 3 OF 21**

OSB/3 9mm 1197x2397 | Gables

| SCALE | SIZE | DATE | DRAWN |
|---|---|---|---|
| NTS | A3 | 13.10.26 | TS |

| STATUS | DRAWING No. | REV |
|---|---|---|
| CONSTRUCTION | P4-CP-OSB-03 / 03 | C04 |

Do not scale. All dimensions in mm. Check all dimensions on site.

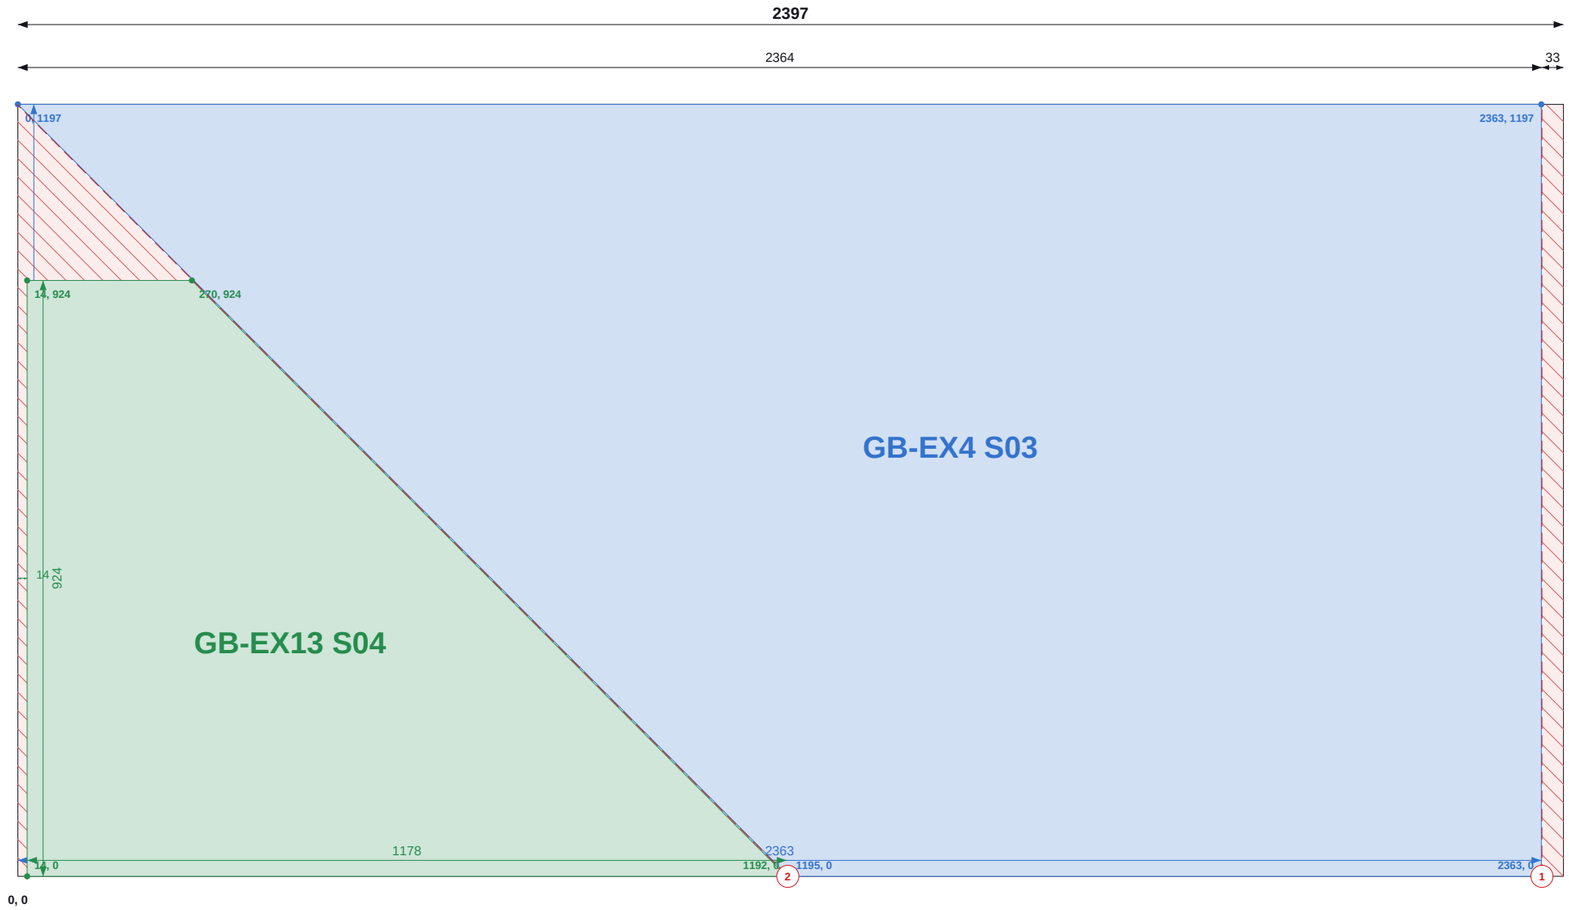


Top / left chains = saw cut positions (to cut centres). Coloured = part size and position.

## SHEET 4 OF 21

### THIS SHEET

| Item | Value |
|---|---|
| Parts | 2 |
| Used / waste | 96.7% / 0.09 m2 |
| Reusable offcuts | 0 |
| Saw cuts / shared | 2 / 1 |

### PIECES (POSITION = BOTTOM-LEFT CORNER)

| Label | Size | X, Y |
|---|---|---|
| GB-EX4 S03 | 1197 x 2363 rake to 1168 | 0, 0 |
| GB-EX13 S04 | 924 x 1178 rake to 257 | 14, 0 |

### NOTES

1. Cut from OSB/3 9mm 1197x2397, 2mm saw kerf. Viewed on the face; dimensions from the sheet's bottom-left corner (0,0). Red numbered lines = saw cuts in order, each edge to edge.
2. Coloured dimensions belong to the part of that colour: its width and height, and its position from the sheet edges. Raked parts: corner coordinates at each corner.
3. Red hatch = waste. Labels = panel + piece mark on the manufacture drawing.

### REVISIONS

| REV | DATE | DESCRIPTION |
|---|---|---|
| C01 | 14.09.26 | Construction issue |
| C02 | 14.09.26 | Roof trusses revised; SP diagonals added |
| C03 | 11.10.26 | FF windows coursed; steel + GP1 portal; steel drawings (ST) |
| C04 | 13.10.26 | Steel approved by the engineer: steel + steel timber drawings issued for construction |

TLS TIMBER FRAME
Design & Manufacture
Scan: 3D model + drawings

| CLIENT | PROJECT |
|---|---|
| MP Adams | MP Adams Plot 4, Eckington |

DRAWING TITLE
**OSB CUTTING - GABLES - SHEET 4 OF 21**

OSB/3 9mm 1197x2397 | Gables

| SCALE | SIZE | DATE | DRAWN |
|---|---|---|---|
| NTS | A3 | 13.10.26 | TS |

| STATUS | DRAWING No. | REV |
|---|---|---|
| CONSTRUCTION | P4-CP-OSB-03 / 04 | C04 |

Do not scale. All dimensions in mm. Check all dimensions on site.




Top / left chains = saw cut positions (to cut centres). Coloured = part size and position.

## SHEET 5 OF 21

### THIS SHEET

| Item | Value |
|---|---|
| Parts | 1 |
| Used / waste | 100.0% / 0.00 m2 |
| Reusable offcuts | 0 |
| Saw cuts / shared | 0 / 0 |

### PIECES (POSITION = BOTTOM-LEFT CORNER)

| Label | Size | X, Y |
|---|---|---|
| GB-EX14 S05 | 1197 x 2397 | 0, 0 |

### NOTES

1. Cut from OSB/3 9mm 1197x2397, 2mm saw kerf. Viewed on the face; dimensions from the sheet's bottom-left corner (0,0). Red numbered lines = saw cuts in order, each edge to edge.
2. Coloured dimensions belong to the part of that colour: its width and height, and its position from the sheet edges. Raked parts: corner coordinates at each corner.
3. Red hatch = waste. Labels = panel + piece mark on the manufacture drawing.

### REVISIONS

| REV | DATE | DESCRIPTION |
|---|---|---|
| C01 | 14.09.26 | Construction issue |
| C02 | 14.09.26 | Roof trusses revised; SP diagonals added |
| C03 | 11.10.26 | FF windows coursed; steel + GP1 portal; steel drawings (ST) |
| C04 | 13.10.26 | Steel approved by the engineer: steel + steel timber drawings issued for construction |

TLS TIMBER FRAME
Design & Manufacture
Scan: 3D model + drawings

| CLIENT | PROJECT |
|---|---|
| MP Adams | MP Adams Plot 4, Eckington |

DRAWING TITLE

**OSB CUTTING - GABLES - SHEET 5 OF 21**

OSB/3 9mm 1197x2397 | Gables

| SCALE | SIZE | DATE | DRAWN |
|---|---|---|---|
| NTS | A3 | 13.10.26 | TS |

| STATUS | DRAWING No. | REV |
|---|---|---|
| CONSTRUCTION | P4-CP-OSB-03 / 05 | C04 |

Do not scale. All dimensions in mm. Check all dimensions on site.




Top / left chains = saw cut positions (to cut centres). Coloured = part size and position.

Do not scale. All dimensions in mm. Check all dimensions on site.

## SHEET 6 OF 21

### THIS SHEET

| Item | Value |
|---|---|
| Parts | 1 |
| Used / waste | 100.0% / 0.00 m2 |
| Reusable offcuts | 0 |
| Saw cuts / shared | 0 / 0 |

### PIECES (POSITION = BOTTOM-LEFT CORNER)

| Label | Size | X, Y |
|---|---|---|
| GB-EX9 S05 | 1197 x 2397 | 0, 0 |

### NOTES

1. Cut from OSB/3 9mm 1197x2397, 2mm saw kerf. Viewed on the face; dimensions from the sheet's bottom-left corner (0,0). Red numbered lines = saw cuts in order, each edge to edge.
2. Coloured dimensions belong to the part of that colour: its width and height, and its position from the sheet edges. Raked parts: corner coordinates at each corner.
3. Red hatch = waste. Labels = panel + piece mark on the manufacture drawing.

### REVISIONS

| REV | DATE | DESCRIPTION |
|---|---|---|
| C01 | 14.09.26 | Construction issue |
| C02 | 14.09.26 | Roof trusses revised; SP diagonals added |
| C03 | 11.10.26 | FF windows coursed; steel + GP1 portal; steel drawings (ST) |
| C04 | 13.10.26 | Steel approved by the engineer: steel + steel timber drawings issued for construction |

TLS TIMBER FRAME
Design & Manufacture
Scan: 3D model + drawings

| CLIENT | PROJECT |
|---|---|
| MP Adams | MP Adams Plot 4, Eckington |


DRAWING TITLE

**OSB CUTTING - GABLES - SHEET 6 OF 21**

OSB/3 9mm 1197x2397 | Gables

| SCALE | SIZE | DATE | DRAWN |
|---|---|---|---|
| NTS | A3 | 13.10.26 | TS |

| STATUS | DRAWING No. | REV |
|---|---|---|
| CONSTRUCTION | P4-CP-OSB-03 / 06 | C04 |

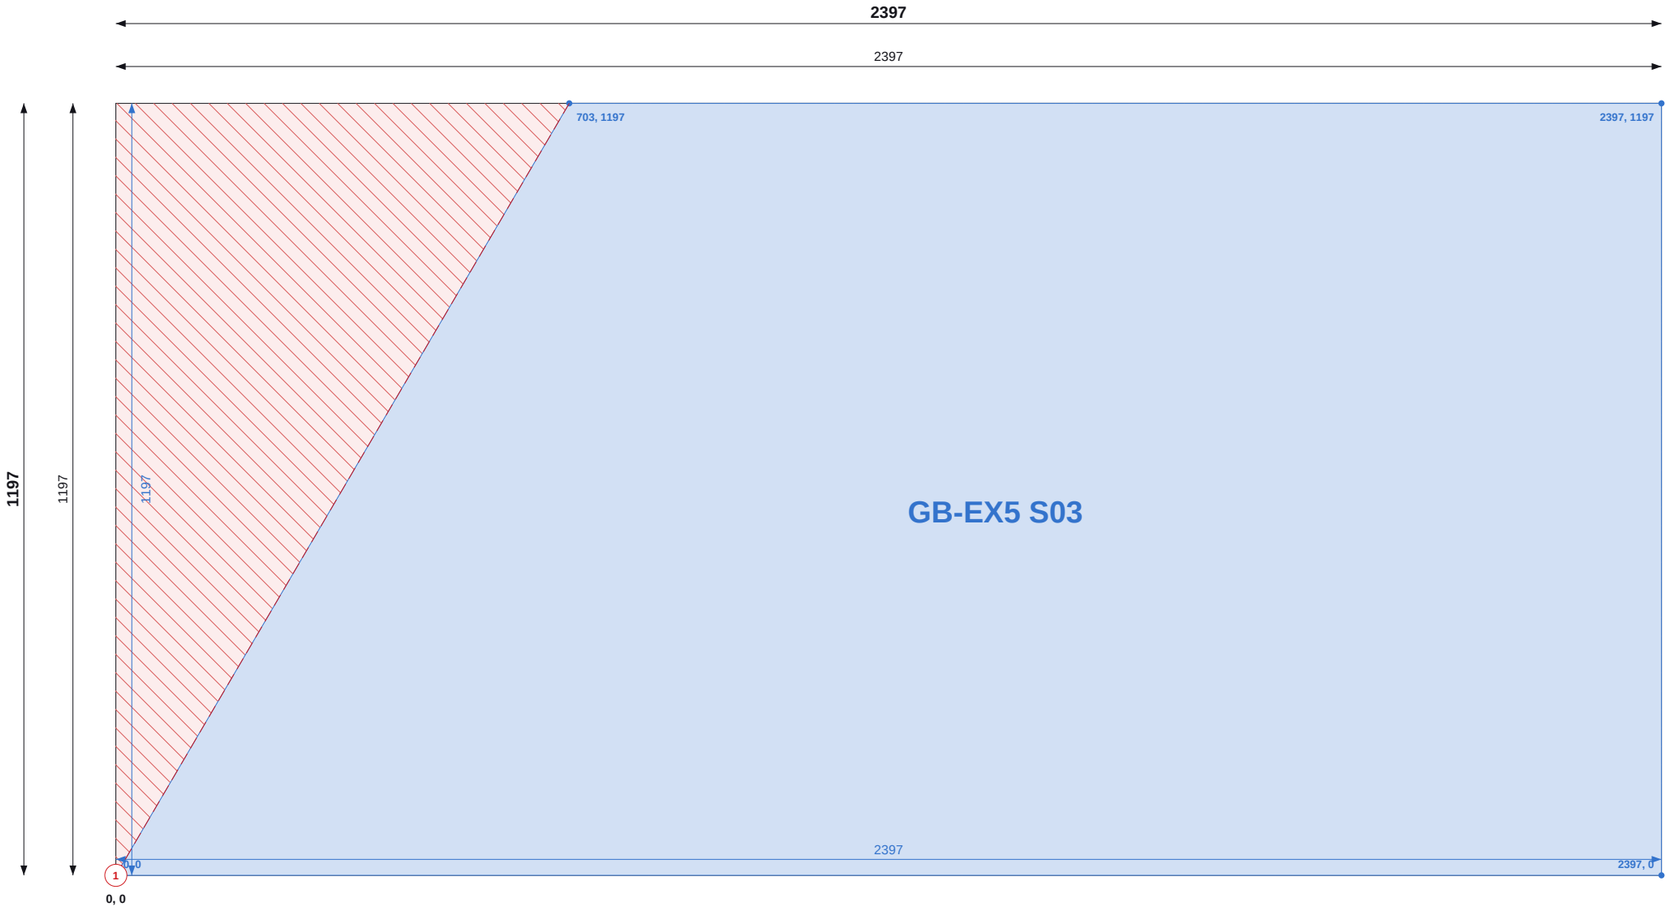


Top / left chains = saw cut positions (to cut centres). Coloured = part size and position.

Do not scale. All dimensions in mm. Check all dimensions on site.

## SHEET 7 OF 21

### THIS SHEET

| Item | Value |
|---|---|
| Parts | 1 |
| Used / waste | 85.3% / 0.42 m2 |
| Reusable offcuts | 0 |
| Saw cuts / shared | 1 / 1 |

### PIECES (POSITION = BOTTOM-LEFT CORNER)

| Label | Size | X, Y |
|---|---|---|
| GB-EX5 S03 | 1197 x 2397 rake to 1694 | 0, 0 |

### NOTES

1. Cut from OSB/3 9mm 1197x2397, 2mm saw kerf. Viewed on the face; dimensions from the sheet's bottom-left corner (0,0). Red numbered lines = saw cuts in order, each edge to edge.
2. Coloured dimensions belong to the part of that colour: its width and height, and its position from the sheet edges. Raked parts: corner coordinates at each corner.
3. Red hatch = waste. Labels = panel + piece mark on the manufacture drawing.

### REVISIONS

| REV | DATE | DESCRIPTION |
|---|---|---|
| C01 | 14.09.26 | Construction issue |
| C02 | 14.09.26 | Roof trusses revised; SP diagonals added |
| C03 | 11.10.26 | FF windows coursed; steel + GP1 portal; steel drawings (ST) |
| C04 | 13.10.26 | Steel approved by the engineer: steel + steel timber drawings issued for construction |

TLS

TLS TIMBER FRAME

Design & Manufacture

Scan: 3D model + drawings

| CLIENT | PROJECT |
|---|---|
| MP Adams | MP Adams Plot 4, Eckington |


DRAWING TITLE

**OSB CUTTING - GABLES - SHEET 7 OF 21**

OSB/3 9mm 1197x2397 | Gables

| SCALE | SIZE | DATE | DRAWN |
|---|---|---|---|
| NTS | A3 | 13.10.26 | TS |

| STATUS | DRAWING No. | REV |
|---|---|---|
| CONSTRUCTION | P4-CP-OSB-03 / 07 | C04 |

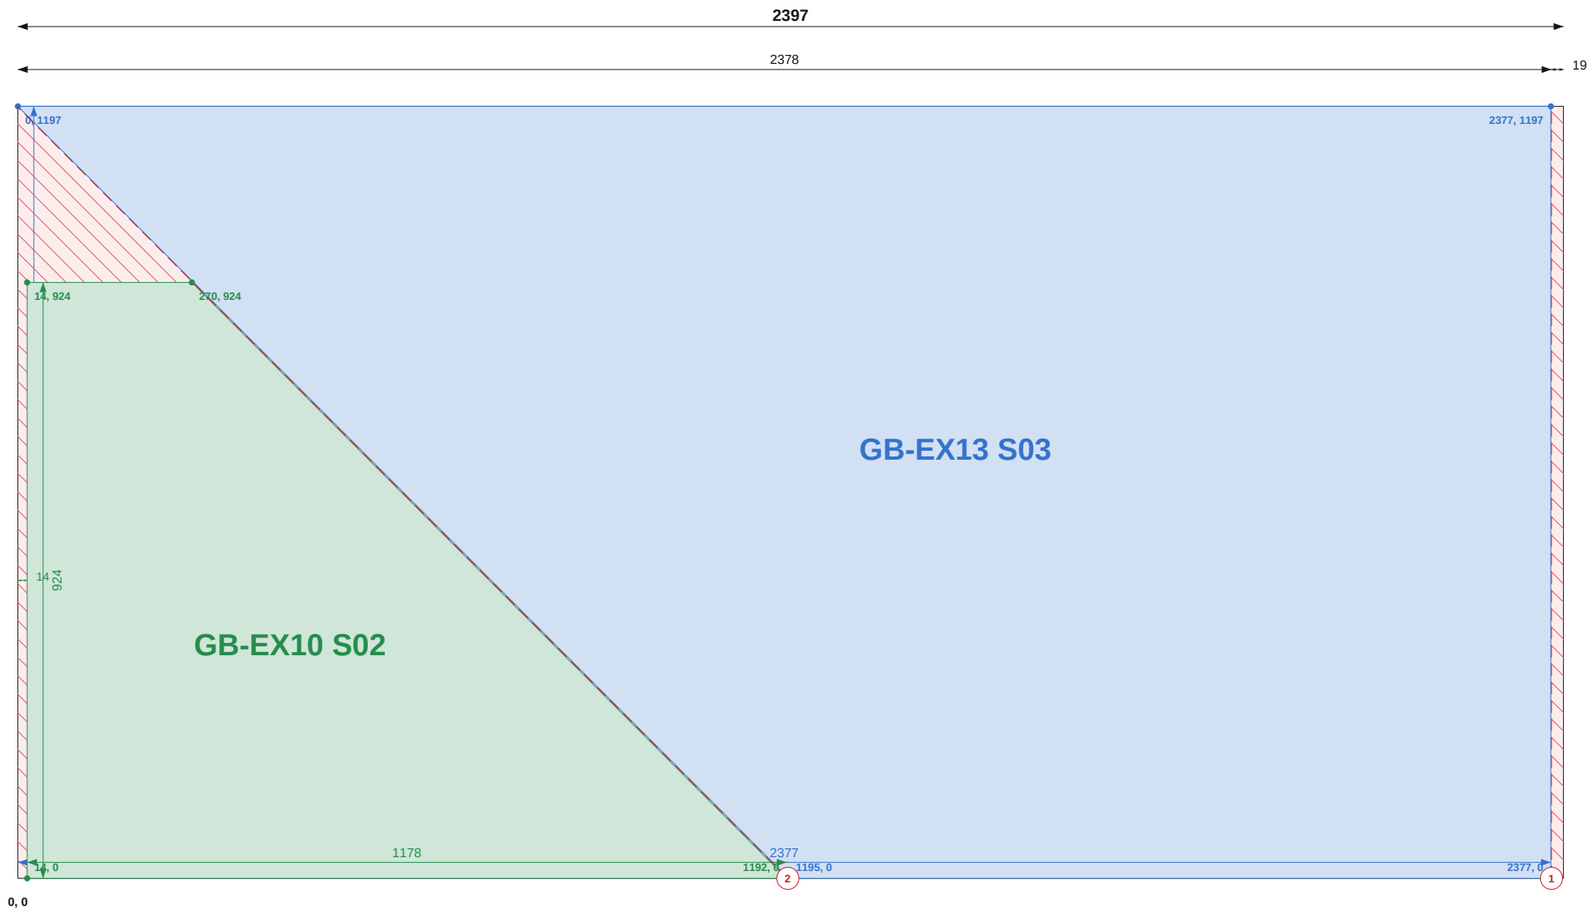


Top / left chains = saw cut positions (to cut centres). Coloured = part size and position.

## SHEET 8 OF 21

### THIS SHEET

| Item | Value |
|---|---|
| Parts | 2 |
| Used / waste | 97.3% / 0.08 m2 |
| Reusable offcuts | 0 |
| Saw cuts / shared | 2 / 1 |

### PIECES (POSITION = BOTTOM-LEFT CORNER)

| Label | Size | X, Y |
|---|---|---|
| GB-EX13 S03 | 1197 x 2377 rake to 1183 | 0, 0 |
| GB-EX10 S02 | 924 x 1178 rake to 257 | 14, 0 |

### NOTES

1. Cut from OSB/3 9mm 1197x2397, 2mm saw kerf. Viewed on the face; dimensions from the sheet's bottom-left corner (0,0). Red numbered lines = saw cuts in order, each edge to edge.
2. Coloured dimensions belong to the part of that colour: its width and height, and its position from the sheet edges. Raked parts: corner coordinates at each corner.
3. Red hatch = waste. Labels = panel + piece mark on the manufacture drawing.

### REVISIONS

| REV | DATE | DESCRIPTION |
|---|---|---|
| C01 | 14.09.26 | Construction issue |
| C02 | 14.09.26 | Roof trusses revised; SP diagonals added |
| C03 | 11.10.26 | FF windows coursed; steel + GP1 portal; steel drawings (ST) |
| C04 | 13.10.26 | Steel approved by the engineer: steel + steel timber drawings issued for construction |

TLS TIMBER FRAME
Design & Manufacture
Scan: 3D model + drawings

| CLIENT | PROJECT |
|---|---|
| MP Adams | MP Adams Plot 4, Eckington |

DRAWING TITLE


**OSB CUTTING - GABLES - SHEET 8 OF 21**

OSB/3 9mm 1197x2397 | Gables

| SCALE | SIZE | DATE | DRAWN |
|---|---|---|---|
| NTS | A3 | 13.10.26 | TS |

| STATUS | DRAWING No. | REV |
|---|---|---|
| CONSTRUCTION | P4-CP-OSB-03 / 08 | C04 |

Do not scale. All dimensions in mm. Check all dimensions on site.

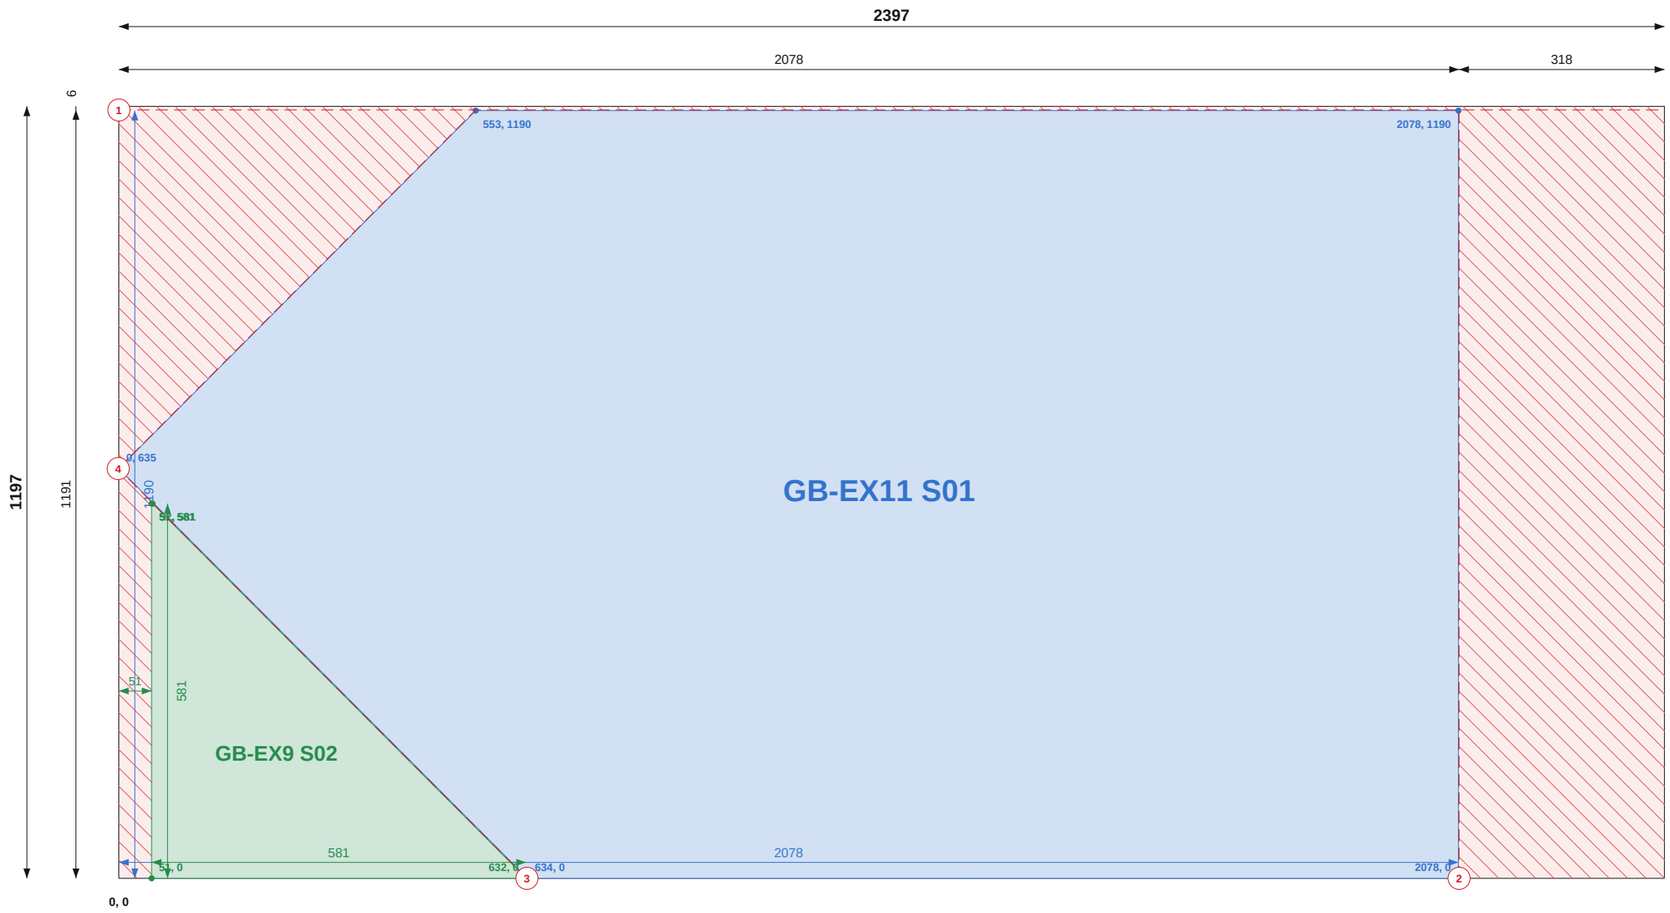


Top / left chains = saw cut positions (to cut centres). Coloured = part size and position.

## SHEET 9 OF 21

### THIS SHEET

| Item | Value |
|---|---|
| Parts | 2 |
| Used / waste | 79.7% / 0.58 m2 |
| Reusable offcuts | 1 |
| Saw cuts / shared | 4 / 2 |

### PIECES (POSITION = BOTTOM-LEFT CORNER)

| Label | Size | X, Y |
|---|---|---|
| GB-EX11 S01 | 1190 x 1525 rake to 1445 | 0, 0 |
| GB-EX9 S02 | 581 x 581 rake to 3 | 51, 0 |

### NOTES

1. Cut from OSB/3 9mm 1197x2397, 2mm saw kerf. Viewed on the face; dimensions from the sheet's bottom-left corner (0,0). Red numbered lines = saw cuts in order, each edge to edge.
2. Coloured dimensions belong to the part of that colour: its width and height, and its position from the sheet edges. Raked parts: corner coordinates at each corner.
3. Red hatch = waste. Labels = panel + piece mark on the manufacture drawing.

### REVISIONS

| REV | DATE | DESCRIPTION |
|---|---|---|
| C01 | 14.09.26 | Construction issue |
| C02 | 14.09.26 | Roof trusses revised; SP diagonals added |
| C03 | 11.10.26 | FF windows coursed; steel + GP1 portal; steel drawings (ST) |
| C04 | 13.10.26 | Steel approved by the engineer: steel + steel timber drawings issued for construction |

TLS TIMBER FRAME
Design & Manufacture
Scan: 3D model + drawings

| CLIENT | PROJECT |
|---|---|
| MP Adams | MP Adams Plot 4, Eckington |


DRAWING TITLE
**OSB CUTTING - GABLES - SHEET 9 OF 21**

OSB/3 9mm 1197x2397 | Gables

| SCALE | SIZE | DATE | DRAWN |
|---|---|---|---|
| NTS | A3 | 13.10.26 | TS |

| STATUS | DRAWING No. | REV |
|---|---|---|
| CONSTRUCTION | P4-CP-OSB-03 / 09 | C04 |

Do not scale. All dimensions in mm. Check all dimensions on site.

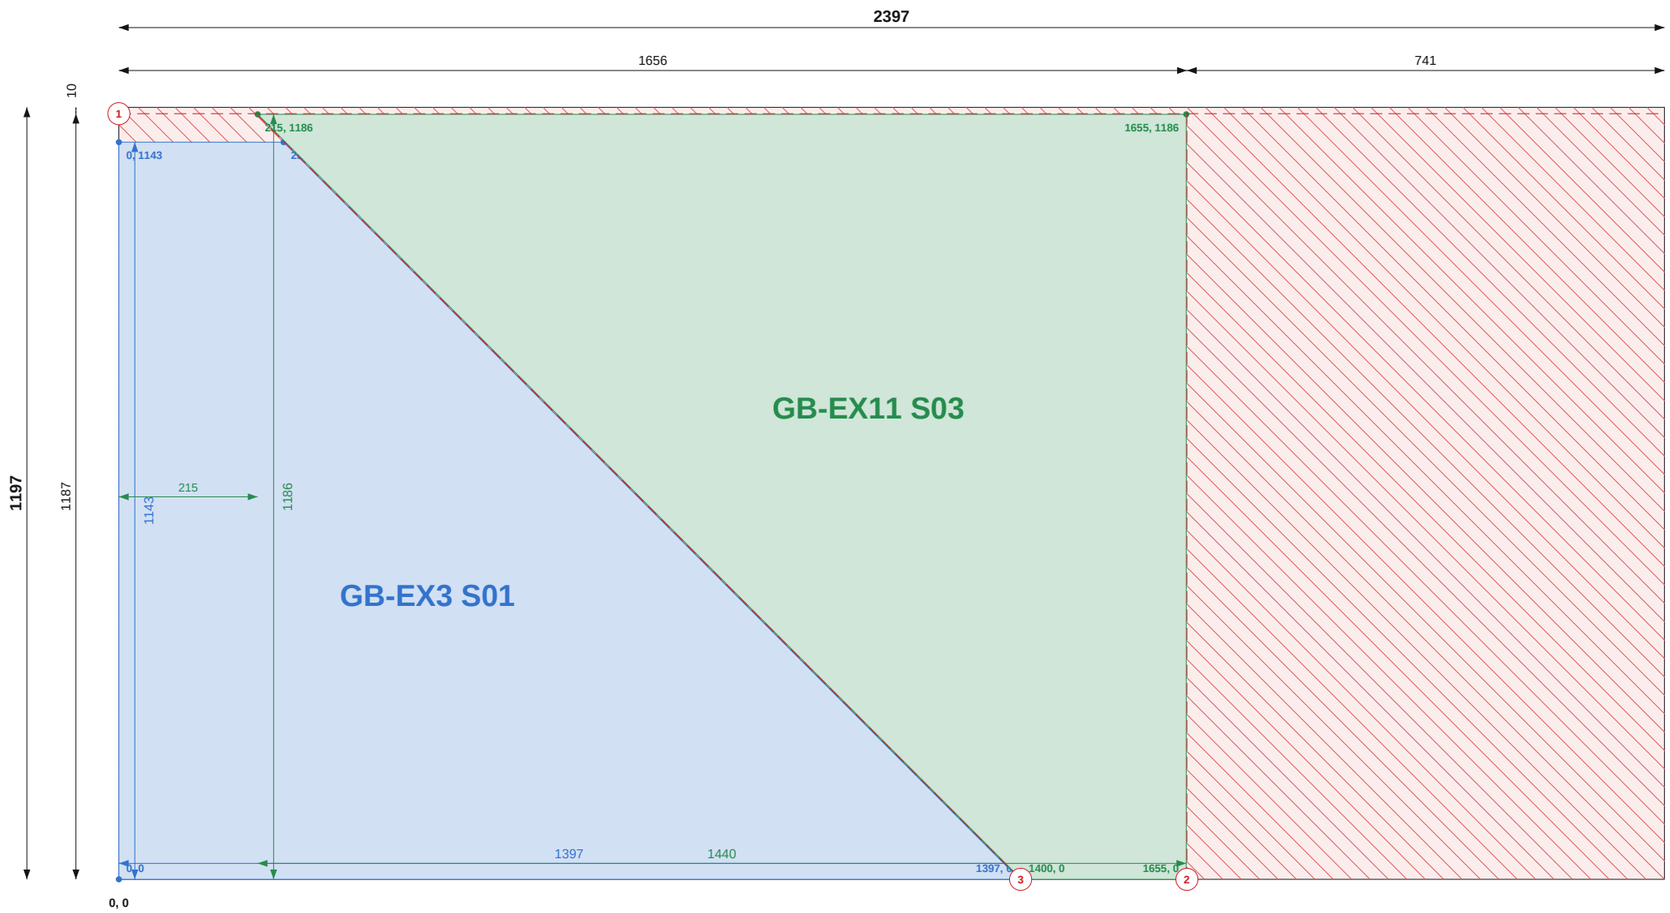


Top / left chains = saw cut positions (to cut centres). Coloured = part size and position.

## SHEET 10 OF 21

### THIS SHEET

| Item | Value |
|---|---|
| Parts | 2 |
| Used / waste | 68.0% / 0.92 m2 |
| Reusable offcuts | 1 |
| Saw cuts / shared | 3 / 1 |

### PIECES (POSITION = BOTTOM-LEFT CORNER)

| Label | Size | X, Y |
|---|---|---|
| GB-EX3 S01 | 1143 x 1397 rake to 257 | 0, 0 |
| GB-EX11 S03 | 1186 x 1440 rake to 257 | 215, 0 |

### NOTES

1. Cut from OSB/3 9mm 1197x2397, 2mm saw kerf. Viewed on the face; dimensions from the sheet's bottom-left corner (0,0). Red numbered lines = saw cuts in order, each edge to edge.
2. Coloured dimensions belong to the part of that colour: its width and height, and its position from the sheet edges. Raked parts: corner coordinates at each corner.
3. Red hatch = waste. Labels = panel + piece mark on the manufacture drawing.

### REVISIONS

| REV | DATE | DESCRIPTION |
|---|---|---|
| C01 | 14.09.26 | Construction issue |
| C02 | 14.09.26 | Roof trusses revised; SP diagonals added |
| C03 | 11.10.26 | FF windows coursed; steel + GP1 portal; steel drawings (ST) |
| C04 | 13.10.26 | Steel approved by the engineer: steel + steel timber drawings issued for construction |

TLS TIMBER FRAME
Design & Manufacture
Scan: 3D model + drawings

| CLIENT | PROJECT |
|---|---|
| MP Adams | MP Adams Plot 4, Eckington |

DRAWING TITLE


**OSB CUTTING - GABLES - SHEET 10 OF 21**

OSB/3 9mm 1197x2397 | Gables

| SCALE | SIZE | DATE | DRAWN |
|---|---|---|---|
| NTS | A3 | 13.10.26 | TS |

| STATUS | DRAWING No. | REV |
|---|---|---|
| CONSTRUCTION | P4-CP-OSB-03 / 10 | C04 |

Do not scale. All dimensions in mm. Check all dimensions on site.

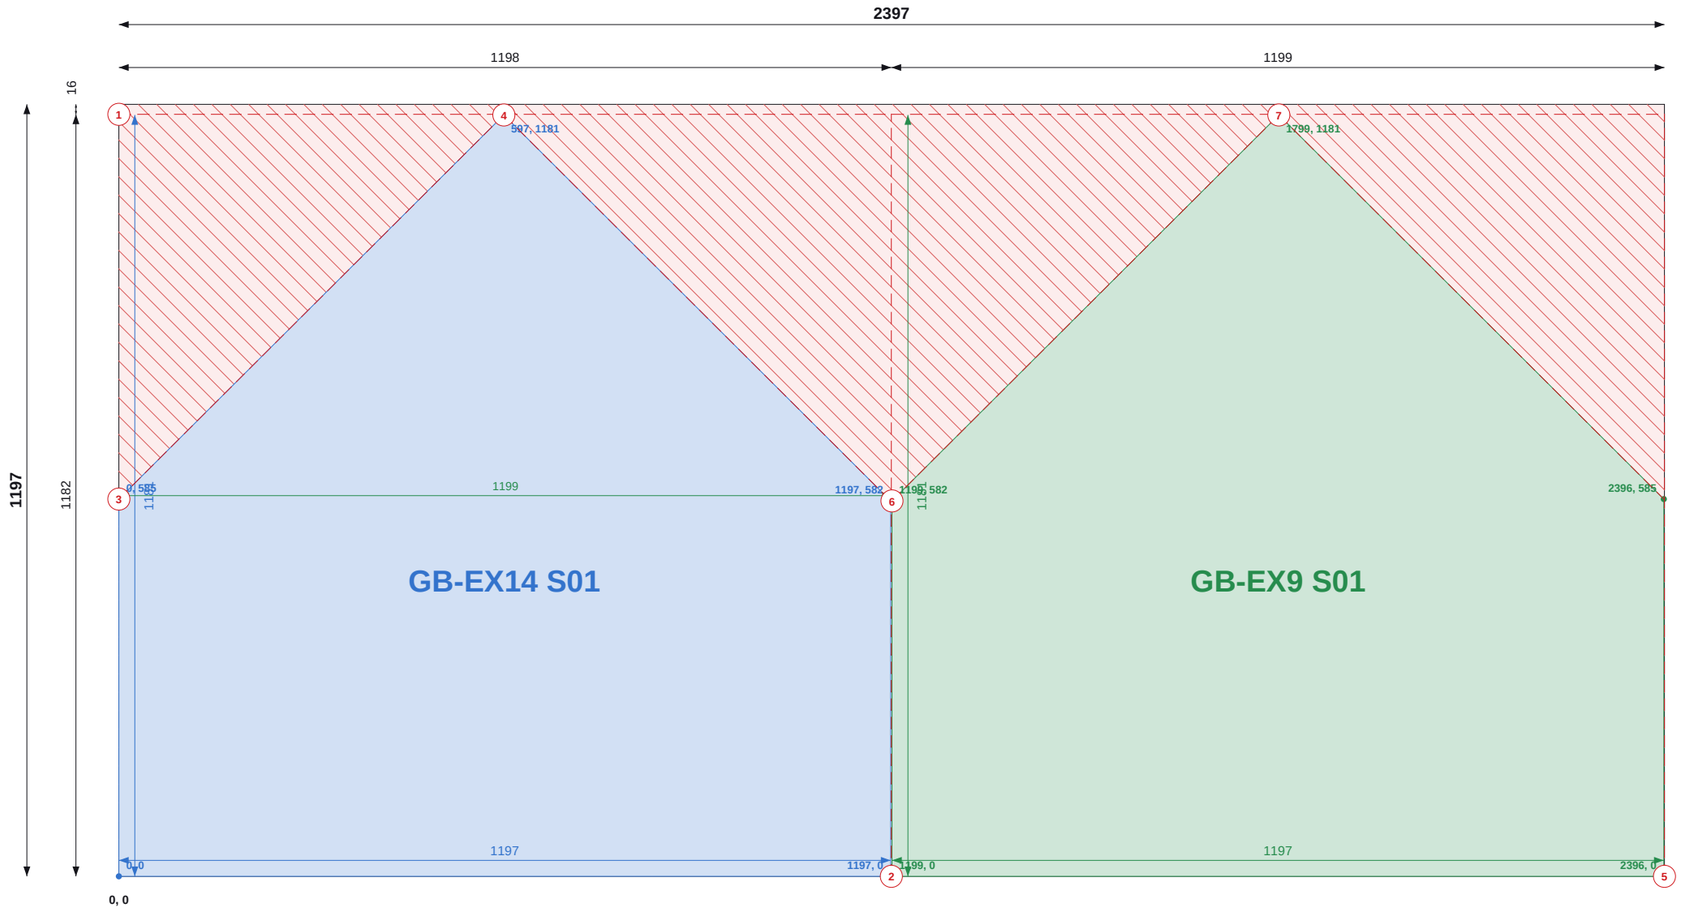


Top / left chains = saw cut positions (to cut centres). Coloured = part size and position.

## SHEET 11 OF 21

### THIS SHEET

| Item | Value |
|---|---|
| Parts | 2 |
| Used / waste | 73.6% / 0.76 m2 |
| Reusable offcuts | 0 |
| Saw cuts / shared | 7 / 5 |

### PIECES (POSITION = BOTTOM-LEFT CORNER)

| Label | Size | X, Y |
|---|---|---|
| GB-EX14 S01 | 1197 x 586 rake to 583 | 0, 0 |
| GB-EX9 S01 | 1197 x 586 rake to 583 | 1199, 0 |

### NOTES

1. Cut from OSB/3 9mm 1197x2397, 2mm saw kerf. Viewed on the face; dimensions from the sheet's bottom-left corner (0,0). Red numbered lines = saw cuts in order, each edge to edge.
2. Coloured dimensions belong to the part of that colour: its width and height, and its position from the sheet edges. Raked parts: corner coordinates at each corner.
3. Red hatch = waste. Labels = panel + piece mark on the manufacture drawing.

### REVISIONS

| REV | DATE | DESCRIPTION |
|---|---|---|
| C01 | 14.09.26 | Construction issue |
| C02 | 14.09.26 | Roof trusses revised; SP diagonals added |
| C03 | 11.10.26 | FF windows coursed; steel + GP1 portal; steel drawings (ST) |
| C04 | 13.10.26 | Steel approved by the engineer: steel + steel timber drawings issued for construction |

TLS TIMBER FRAME
Design & Manufacture
Scan: 3D model + drawings

| CLIENT | PROJECT |
|---|---|
| MP Adams | MP Adams Plot 4, Eckington |


DRAWING TITLE
**OSB CUTTING - GABLES - SHEET 11 OF 21**

OSB/3 9mm 1197x2397 | Gables

| SCALE | SIZE | DATE | DRAWN |
|---|---|---|---|
| NTS | A3 | 13.10.26 | TS |

| STATUS | DRAWING No. | REV |
|---|---|---|
| CONSTRUCTION | P4-CP-OSB-03 / 11 | C04 |

Do not scale. All dimensions in mm. Check all dimensions on site.

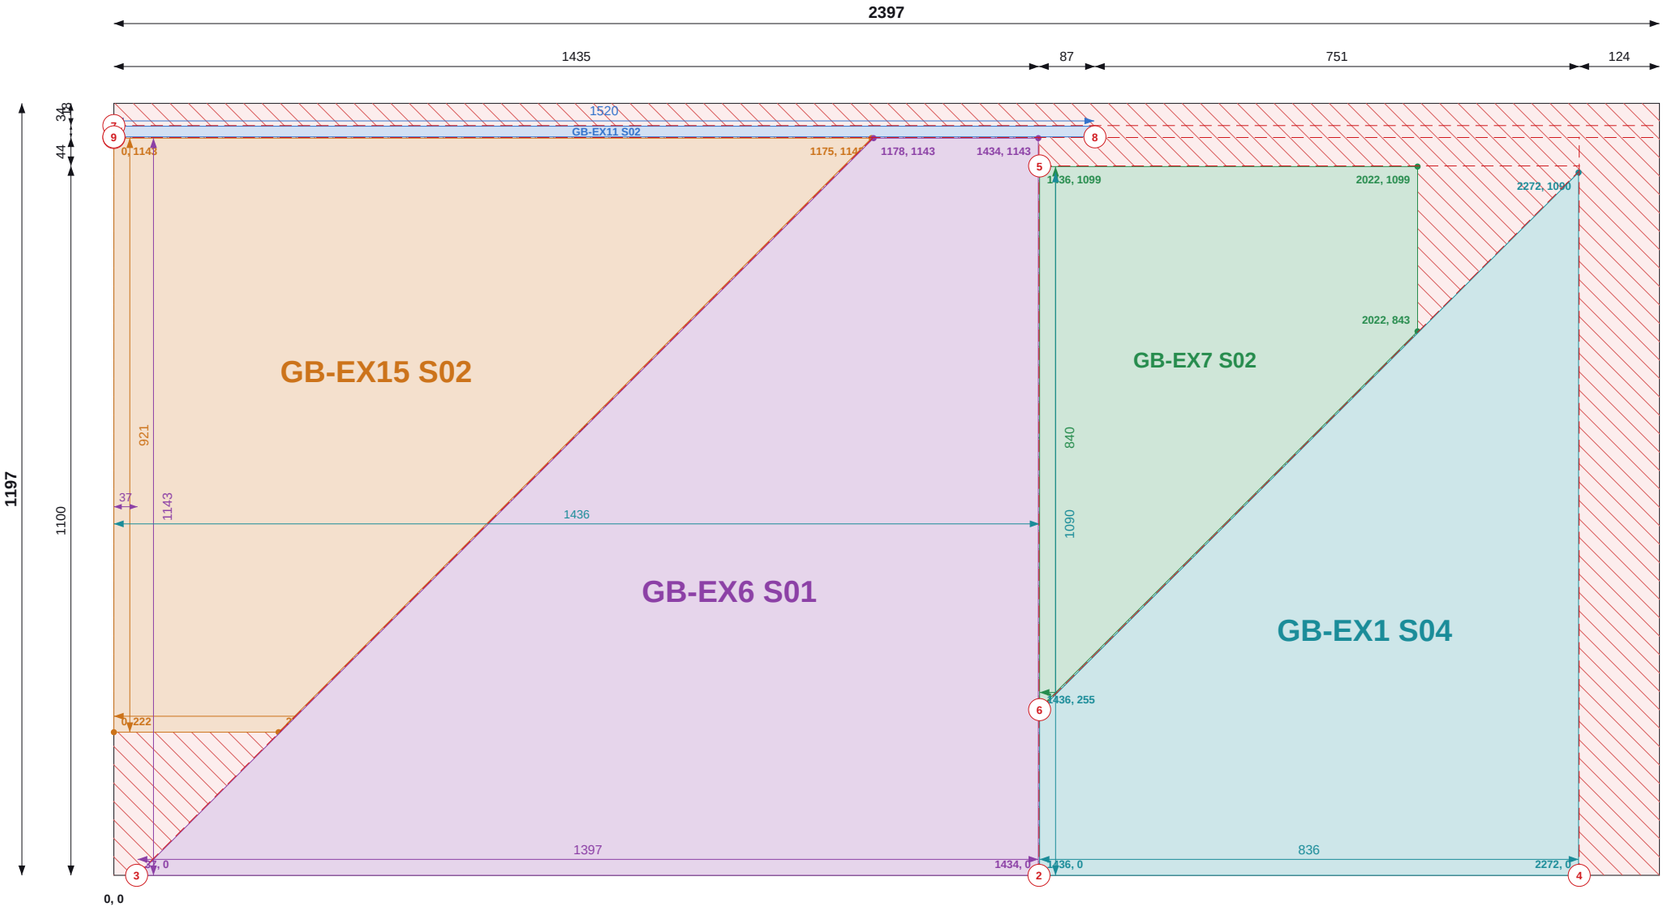


Top / left chains = saw cut positions (to cut centres). Coloured = part size and position.

Do not scale. All dimensions in mm. Check all dimensions on site.

## SHEET 12 OF 21

### THIS SHEET

| Item | Value |
|---|---|
| Parts | 5 |
| Used / waste | 87.5% / 0.36 m2 |
| Reusable offcuts | 0 |
| Saw cuts / shared | 9 / 5 |

### PIECES (POSITION = BOTTOM-LEFT CORNER)

| Label | Size | X, Y |
|---|---|---|
| GB-EX11 S02 | 16 x 1520 | 0, 1145 |
| GB-EX7 S02 | 586 x 840 rake to 257 | 1436, 259 |
| GB-EX15 S02 | 921 x 1175 rake to 257 | 0, 222 |
| GB-EX6 S01 | 1143 x 1397 rake to 257 | 37, 0 |
| GB-EX1 S04 | 836 x 1090 rake to 257 | 1436, 0 |

### NOTES

1. Cut from OSB/3 9mm 1197x2397, 2mm saw kerf. Viewed on the face; dimensions from the sheet's bottom-left corner (0,0). Red numbered lines = saw cuts in order, each edge to edge.
2. Coloured dimensions belong to the part of that colour: its width and height, and its position from the sheet edges. Raked parts: corner coordinates at each corner.
3. Red hatch = waste. Labels = panel + piece mark on the manufacture drawing.

### REVISIONS

| REV | DATE | DESCRIPTION |
|---|---|---|
| C01 | 14.09.26 | Construction issue |
| C02 | 14.09.26 | Roof trusses revised; SP diagonals added |
| C03 | 11.10.26 | FF windows coursed; steel + GP1 portal; steel drawings (ST) |
| C04 | 13.10.26 | Steel approved by the engineer: steel + steel timber drawings issued for construction |

TLS TIMBER FRAME
Design & Manufacture
Scan: 3D model + drawings


| CLIENT | PROJECT |
|---|---|
| MP Adams | MP Adams Plot 4, Eckington |

DRAWING TITLE
**OSB CUTTING - GABLES - SHEET 12 OF 21**

OSB/3 9mm 1197x2397 | Gables

| SCALE | SIZE | DATE | DRAWN |
|---|---|---|---|
| NTS | A3 | 13.10.26 | TS |

| STATUS | DRAWING No. | REV |
|---|---|---|
| CONSTRUCTION | P4-CP-OSB-03 / 12 | C04 |

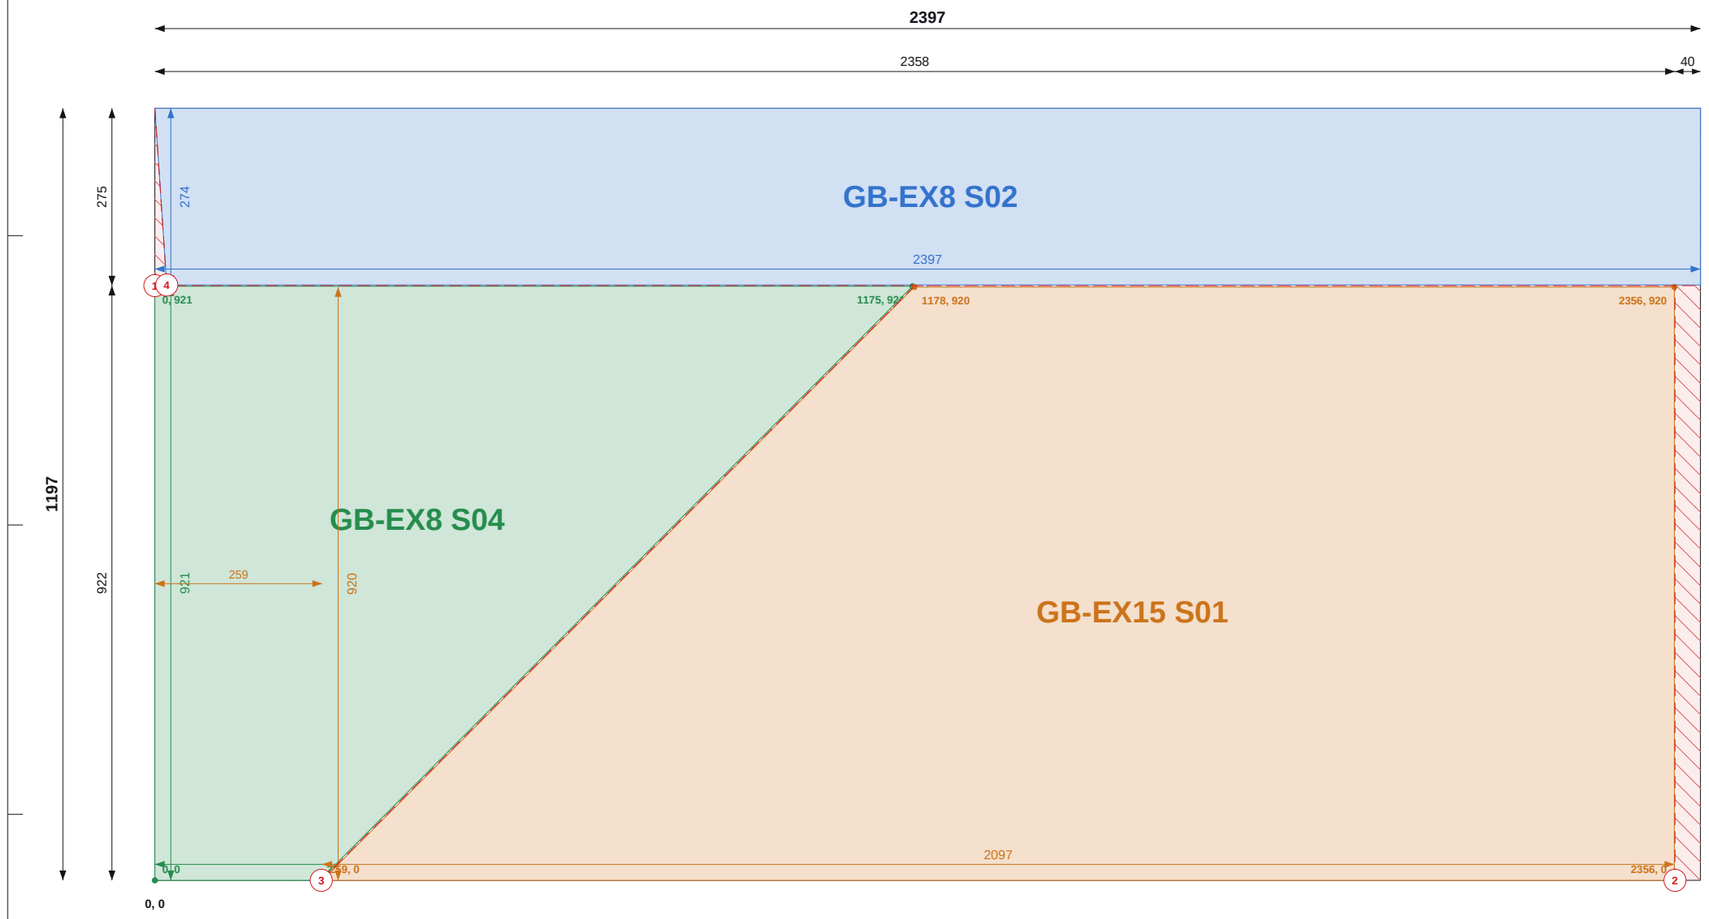


Top / left chains = saw cut positions (to cut centres). Coloured = part size and position.

## SHEET 13 OF 21

### THIS SHEET

| Item | Value |
|---|---|
| Parts | 3 |
| Used / waste | 98.3% / 0.05 m2 |
| Reusable offcuts | 0 |
| Saw cuts / shared | 4 / 3 |

### PIECES (POSITION = BOTTOM-LEFT CORNER)

| Label | Size | X, Y |
|---|---|---|
| GB-EX8 S02 | 274 x 2397 | 0, 923 |
| GB-EX8 S04 | 921 x 1175 rake to 257 | 0, 0 |
| GB-EX15 S01 | 920 x 2097 rake to 1180 | 259, 0 |

### NOTES

1. Cut from OSB/3 9mm 1197x2397, 2mm saw kerf. Viewed on the face; dimensions from the sheet's bottom-left corner (0,0). Red numbered lines = saw cuts in order, each edge to edge.
2. Coloured dimensions belong to the part of that colour: its width and height, and its position from the sheet edges. Raked parts: corner coordinates at each corner.
3. Red hatch = waste. Labels = panel + piece mark on the manufacture drawing.

### REVISIONS

| REV | DATE | DESCRIPTION |
|---|---|---|
| C01 | 14.09.26 | Construction issue |
| C02 | 14.09.26 | Roof trusses revised; SP diagonals added |
| C03 | 11.10.26 | FF windows coursed; steel + GP1 portal; steel drawings (ST) |
| C04 | 13.10.26 | Steel approved by the engineer: steel + steel timber drawings issued for construction |

TLS TIMBER FRAME
Design & Manufacture
Scan: 3D model + drawings

| CLIENT | PROJECT |
|---|---|
| MP Adams | MP Adams Plot 4, Eckington |

DRAWING TITLE


**OSB CUTTING - GABLES - SHEET 13 OF 21**

OSB/3 9mm 1197x2397 | Gables

| SCALE | SIZE | DATE | DRAWN |
|---|---|---|---|
| NTS | A3 | 13.10.26 | TS |

| STATUS | DRAWING No. | REV |
|---|---|---|
| CONSTRUCTION | P4-CP-OSB-03 / 13 | C04 |

Do not scale. All dimensions in mm. Check all dimensions on site.

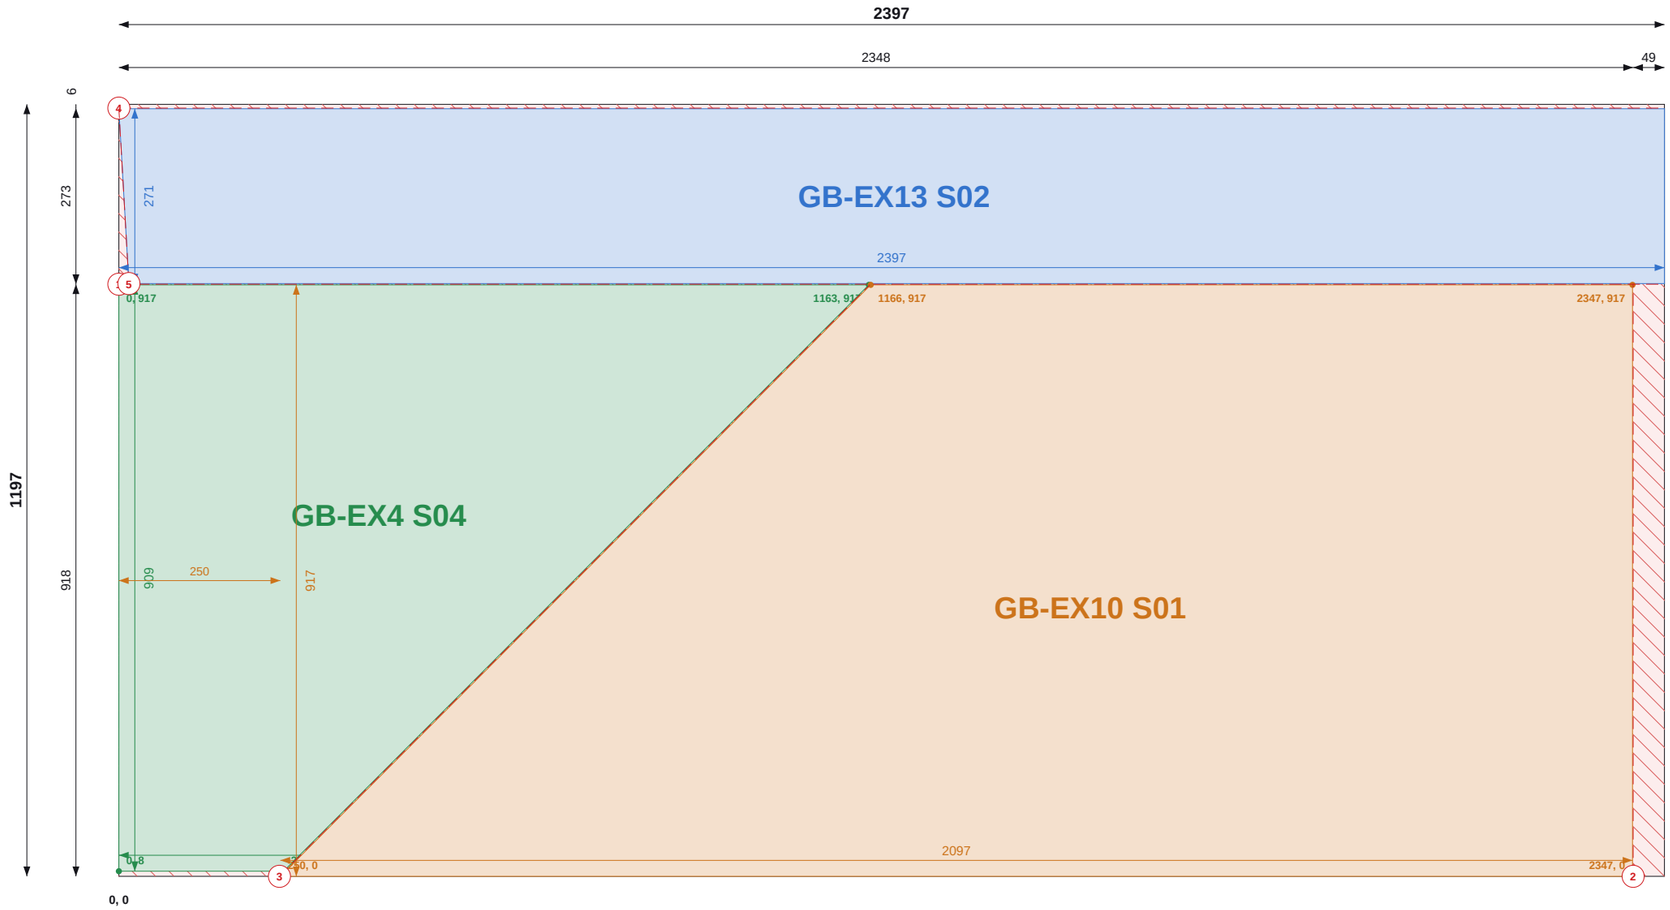


Top / left chains = saw cut positions (to cut centres). Coloured = part size and position.

## SHEET 14 OF 21

### THIS SHEET

| Item | Value |
|---|---|
| Parts | 3 |
| Used / waste | 97.4% / 0.07 m2 |
| Reusable offcuts | 0 |
| Saw cuts / shared | 5 / 3 |

### PIECES (POSITION = BOTTOM-LEFT CORNER)

| Label | Size | X, Y |
|---|---|---|
| GB-EX13 S02 | 271 x 2397 | 0, 919 |
| GB-EX4 S04 | 909 x 1163 rake to 257 | 0, 8 |
| GB-EX10 S01 | 917 x 2097 rake to 1183 | 250, 0 |

### NOTES

1. Cut from OSB/3 9mm 1197x2397, 2mm saw kerf. Viewed on the face; dimensions from the sheet's bottom-left corner (0,0). Red numbered lines = saw cuts in order, each edge to edge.
2. Coloured dimensions belong to the part of that colour: its width and height, and its position from the sheet edges. Raked parts: corner coordinates at each corner.
3. Red hatch = waste. Labels = panel + piece mark on the manufacture drawing.

### REVISIONS

| REV | DATE | DESCRIPTION |
|---|---|---|
| C01 | 14.09.26 | Construction issue |
| C02 | 14.09.26 | Roof trusses revised; SP diagonals added |
| C03 | 11.10.26 | FF windows coursed; steel + GP1 portal; steel drawings (ST) |
| C04 | 13.10.26 | Steel approved by the engineer: steel + steel timber drawings issued for construction |

TLS TIMBER FRAME
Design & Manufacture
Scan: 3D model + drawings

| CLIENT | PROJECT |
|---|---|
| MP Adams | MP Adams Plot 4, Eckington |


DRAWING TITLE
**OSB CUTTING - GABLES - SHEET 14 OF 21**

OSB/3 9mm 1197x2397 | Gables

| SCALE | SIZE | DATE | DRAWN |
|---|---|---|---|
| NTS | A3 | 13.10.26 | TS |

| STATUS | DRAWING No. | REV |
|---|---|---|
| CONSTRUCTION | P4-CP-OSB-03 / 14 | C04 |

Do not scale. All dimensions in mm. Check all dimensions on site.

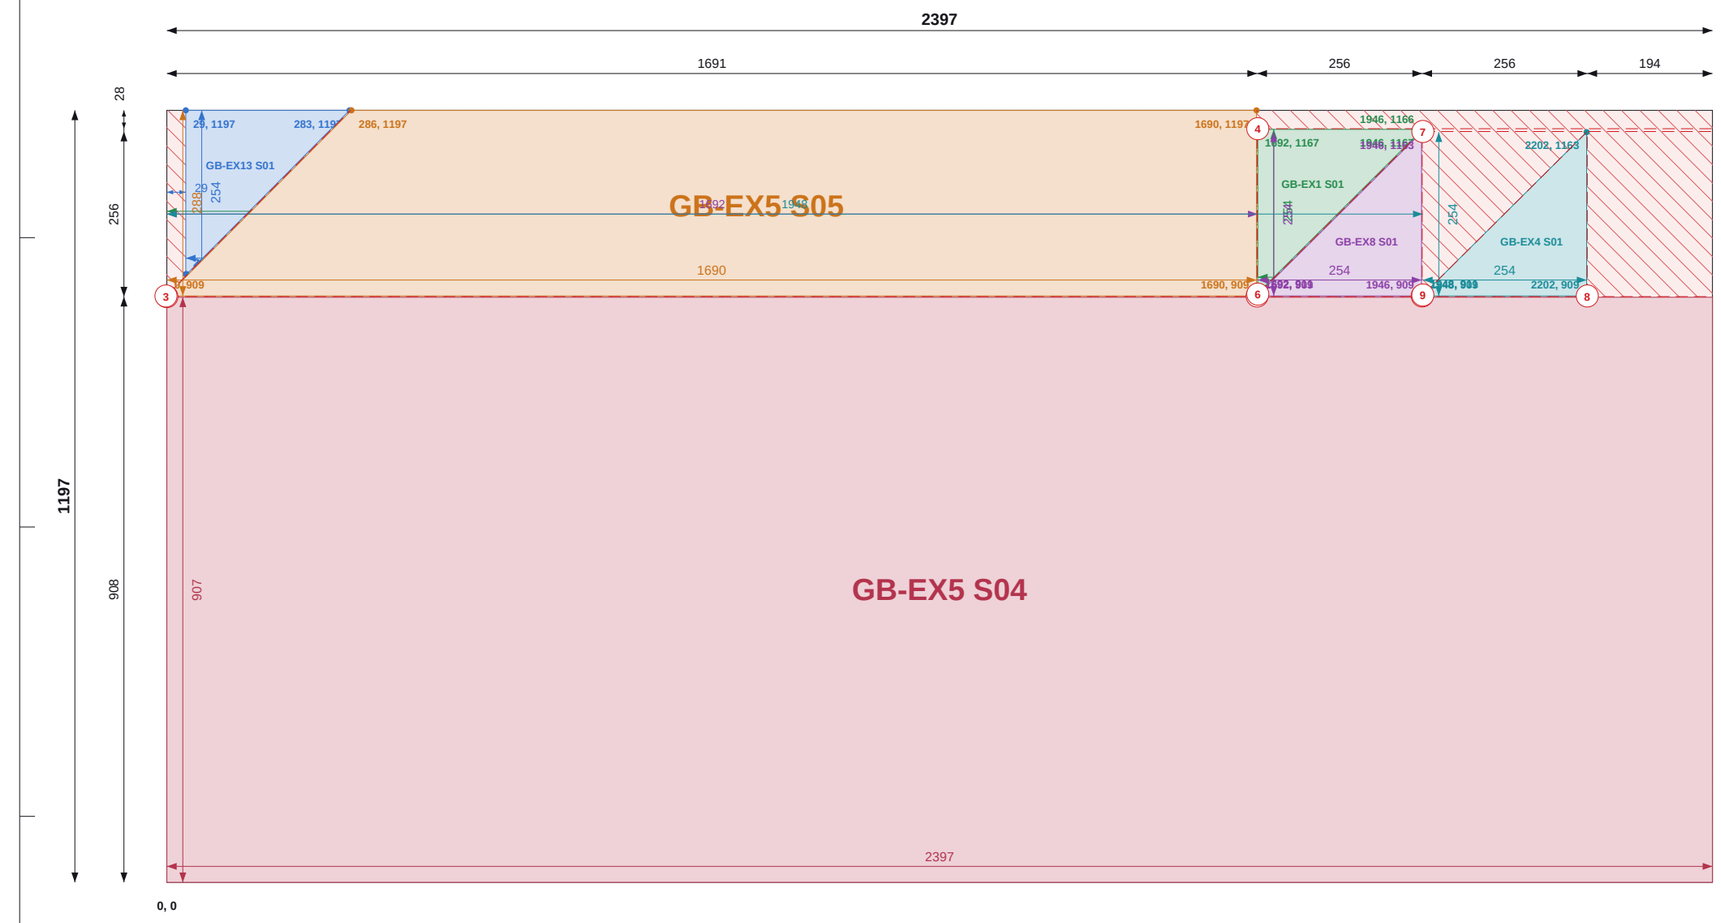


Top / left chains = saw cut positions (to cut centres). Coloured = part size and position.

## SHEET 15 OF 21

### THIS SHEET

| Item | Value |
|---|---|
| Parts | 6 |
| Used / waste | 95.8% / 0.12 m2 |
| Reusable offcuts | 0 |
| Saw cuts / shared | 9 / 6 |

### PIECES (POSITION = BOTTOM-LEFT CORNER)

| Label | Size | X, Y |
|---|---|---|
| GB-EX13 S01 | 254 x 254 rake to 3 | 29, 943 |
| GB-EX1 S01 | 254 x 254 rake to 3 | 1692, 913 |
| GB-EX5 S05 | 288 x 1690 rake to 1405 | 0, 909 |
| GB-EX8 S01 | 254 x 254 rake to 3 | 1692, 909 |
| GB-EX4 S01 | 254 x 254 rake to 3 | 1948, 909 |
| GB-EX5 S04 | 907 x 2397 | 0, 0 |

### NOTES

1. Cut from OSB/3 9mm 1197x2397, 2mm saw kerf. Viewed on the face; dimensions from the sheet's bottom-left corner (0,0). Red numbered lines = saw cuts in order, each edge to edge.
2. Coloured dimensions belong to the part of that colour: its width and height, and its position from the sheet edges. Raked parts: corner coordinates at each corner.
3. Red hatch = waste. Labels = panel + piece mark on the manufacture drawing.

### REVISIONS

| REV | DATE | DESCRIPTION |
|---|---|---|
| C01 | 14.09.26 | Construction issue |
| C02 | 14.09.26 | Roof trusses revised; SP diagonals added |
| C03 | 11.10.26 | FF windows coursed; steel + GP1 portal; steel drawings (ST) |
| C04 | 13.10.26 | Steel approved by the engineer: steel + steel timber drawings issued for construction |

TLS TIMBER FRAME
Design & Manufacture
Scan: 3D model + drawings

| CLIENT | PROJECT |
|---|---|
| MP Adams | MP Adams Plot 4, Eckington |

DRAWING TITLE

**OSB CUTTING - GABLES - SHEET 15 OF 21**

OSB/3 9mm 1197x2397 | Gables

| SCALE | SIZE | DATE | DRAWN |
|---|---|---|---|
| NTS | A3 | 13.10.26 | TS |

| STATUS | DRAWING No. | REV |
|---|---|---|
| CONSTRUCTION | P4-CP-OSB-03 / 15 | C04 |

Do not scale. All dimensions in mm. Check all dimensions on site.




Top / left chains = saw cut positions (to cut centres). Coloured = part size and position.

## SHEET 16 OF 21

### THIS SHEET

| Item | Value |
|---|---|
| Parts | 2 |
| Used / waste | 95.4% / 0.13 m2 |
| Reusable offcuts | 0 |
| Saw cuts / shared | 2 / 2 |

### PIECES (POSITION = BOTTOM-LEFT CORNER)

| Label | Size | X, Y |
|---|---|---|
| GB-EX9 S06 | 319 x 2397 | 0, 878 |
| GB-EX9 S04 | 876 x 2397 rake to 2104 | 0, 0 |

### NOTES

1. Cut from OSB/3 9mm 1197x2397, 2mm saw kerf. Viewed on the face; dimensions from the sheet's bottom-left corner (0,0). Red numbered lines = saw cuts in order, each edge to edge.
2. Coloured dimensions belong to the part of that colour: its width and height, and its position from the sheet edges. Raked parts: corner coordinates at each corner.
3. Red hatch = waste. Labels = panel + piece mark on the manufacture drawing.

### REVISIONS

| REV | DATE | DESCRIPTION |
|---|---|---|
| C01 | 14.09.26 | Construction issue |
| C02 | 14.09.26 | Roof trusses revised; SP diagonals added |
| C03 | 11.10.26 | FF windows coursed; steel + GP1 portal; steel drawings (ST) |
| C04 | 13.10.26 | Steel approved by the engineer: steel + steel timber drawings issued for construction |

TLS TIMBER FRAME
Design & Manufacture
Scan: 3D model + drawings

| CLIENT | PROJECT |
|---|---|
| MP Adams | MP Adams Plot 4, Eckington |

DRAWING TITLE

**OSB CUTTING - GABLES - SHEET 16 OF 21**

OSB/3 9mm 1197x2397 | Gables

| SCALE | SIZE | DATE | DRAWN |
|---|---|---|---|
| NTS | A3 | 13.10.26 | TS |

| STATUS | DRAWING No. | REV |
|---|---|---|
| CONSTRUCTION | P4-CP-OSB-03 / 16 | C04 |

Do not scale. All dimensions in mm. Check all dimensions on site.




Top / left chains = saw cut positions (to cut centres). Coloured = part size and position.

## SHEET 17 OF 21

### THIS SHEET

| Item | Value |
|---|---|
| Parts | 2 |
| Used / waste | 95.4% / 0.13 m2 |
| Reusable offcuts | 0 |
| Saw cuts / shared | 2 / 2 |

### PIECES (POSITION = BOTTOM-LEFT CORNER)

| Label | Size | X, Y |
|---|---|---|
| GB-EX14 S06 | 322 x 2397 | 0, 875 |
| GB-EX14 S04 | 873 x 2397 rake to 2104 | 0, 0 |

### NOTES

1. Cut from OSB/3 9mm 1197x2397, 2mm saw kerf. Viewed on the face; dimensions from the sheet's bottom-left corner (0,0). Red numbered lines = saw cuts in order, each edge to edge.
2. Coloured dimensions belong to the part of that colour: its width and height, and its position from the sheet edges. Raked parts: corner coordinates at each corner.
3. Red hatch = waste. Labels = panel + piece mark on the manufacture drawing.

### REVISIONS

| REV | DATE | DESCRIPTION |
|---|---|---|
| C01 | 14.09.26 | Construction issue |
| C02 | 14.09.26 | Roof trusses revised; SP diagonals added |
| C03 | 11.10.26 | FF windows coursed; steel + GP1 portal; steel drawings (ST) |
| C04 | 13.10.26 | Steel approved by the engineer: steel + steel timber drawings issued for construction |

TLS TIMBER FRAME
Design & Manufacture
Scan: 3D model + drawings

| CLIENT | PROJECT |
|---|---|
| MP Adams | MP Adams Plot 4, Eckington |


DRAWING TITLE
**OSB CUTTING - GABLES - SHEET 17 OF 21**

OSB/3 9mm 1197x2397 | Gables

| SCALE | SIZE | DATE | DRAWN |
|---|---|---|---|
| NTS | A3 | 13.10.26 | TS |

| STATUS | DRAWING No. | REV |
|---|---|---|
| CONSTRUCTION | P4-CP-OSB-03 / 17 | C04 |

Do not scale. All dimensions in mm. Check all dimensions on site.

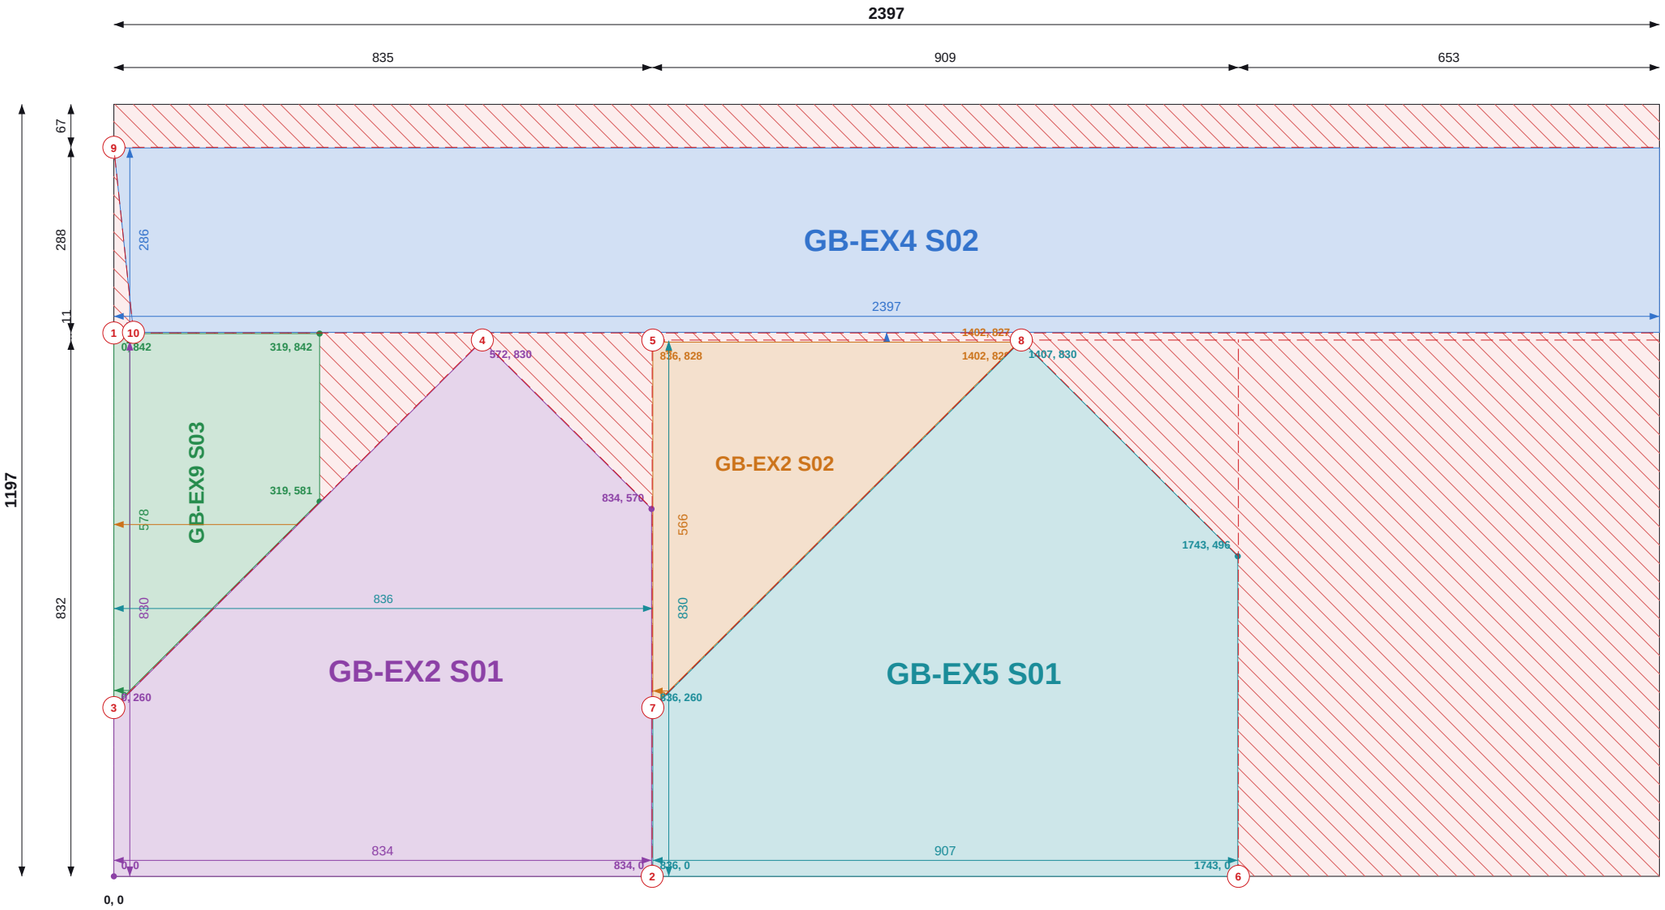


Top / left chains = saw cut positions (to cut centres). Coloured = part size and position.

Do not scale. All dimensions in mm. Check all dimensions on site.

## SHEET 18 OF 21

### THIS SHEET

| Item | Value |
|---|---|
| Parts | 5 |
| Used / waste | 69.9% / 0.86 m2 |
| Reusable offcuts | 1 |
| Saw cuts / shared | 10 / 7 |

### PIECES (POSITION = BOTTOM-LEFT CORNER)

| Label | Size | X, Y |
|---|---|---|
| GB-EX4 S02 | 286 x 2397 | 0, 844 |
| GB-EX9 S03 | 319 x 578 rake to 262 | 0, 263 |
| GB-EX2 S02 | 566 x 566 rake to 3 | 836, 263 |
| GB-EX2 S01 | 834 x 571 rake to 262 | 0, 0 |
| GB-EX5 S01 | 907 x 497 rake to 262 | 836, 0 |

### NOTES

1. Cut from OSB/3 9mm 1197x2397, 2mm saw kerf. Viewed on the face; dimensions from the sheet's bottom-left corner (0,0). Red numbered lines = saw cuts in order, each edge to edge.
2. Coloured dimensions belong to the part of that colour: its width and height, and its position from the sheet edges. Raked parts: corner coordinates at each corner.
3. Red hatch = waste. Labels = panel + piece mark on the manufacture drawing.

### REVISIONS

| REV | DATE | DESCRIPTION |
|---|---|---|
| C01 | 14.09.26 | Construction issue |
| C02 | 14.09.26 | Roof trusses revised; SP diagonals added |
| C03 | 11.10.26 | FF windows coursed; steel + GP1 portal; steel drawings (ST) |
| C04 | 13.10.26 | Steel approved by the engineer: steel + steel timber drawings issued for construction |

TLS TIMBER FRAME
Design & Manufacture
Scan: 3D model + drawings


| CLIENT | PROJECT |
|---|---|
| MP Adams | MP Adams Plot 4, Eckington |

DRAWING TITLE
**OSB CUTTING - GABLES - SHEET 18 OF 21**

OSB/3 9mm 1197x2397 | Gables

| SCALE | SIZE | DATE | DRAWN |
|---|---|---|---|
| NTS | A3 | 13.10.26 | TS |

| STATUS | DRAWING No. | REV |
|---|---|---|
| CONSTRUCTION | P4-CP-OSB-03 / 18 | C04 |

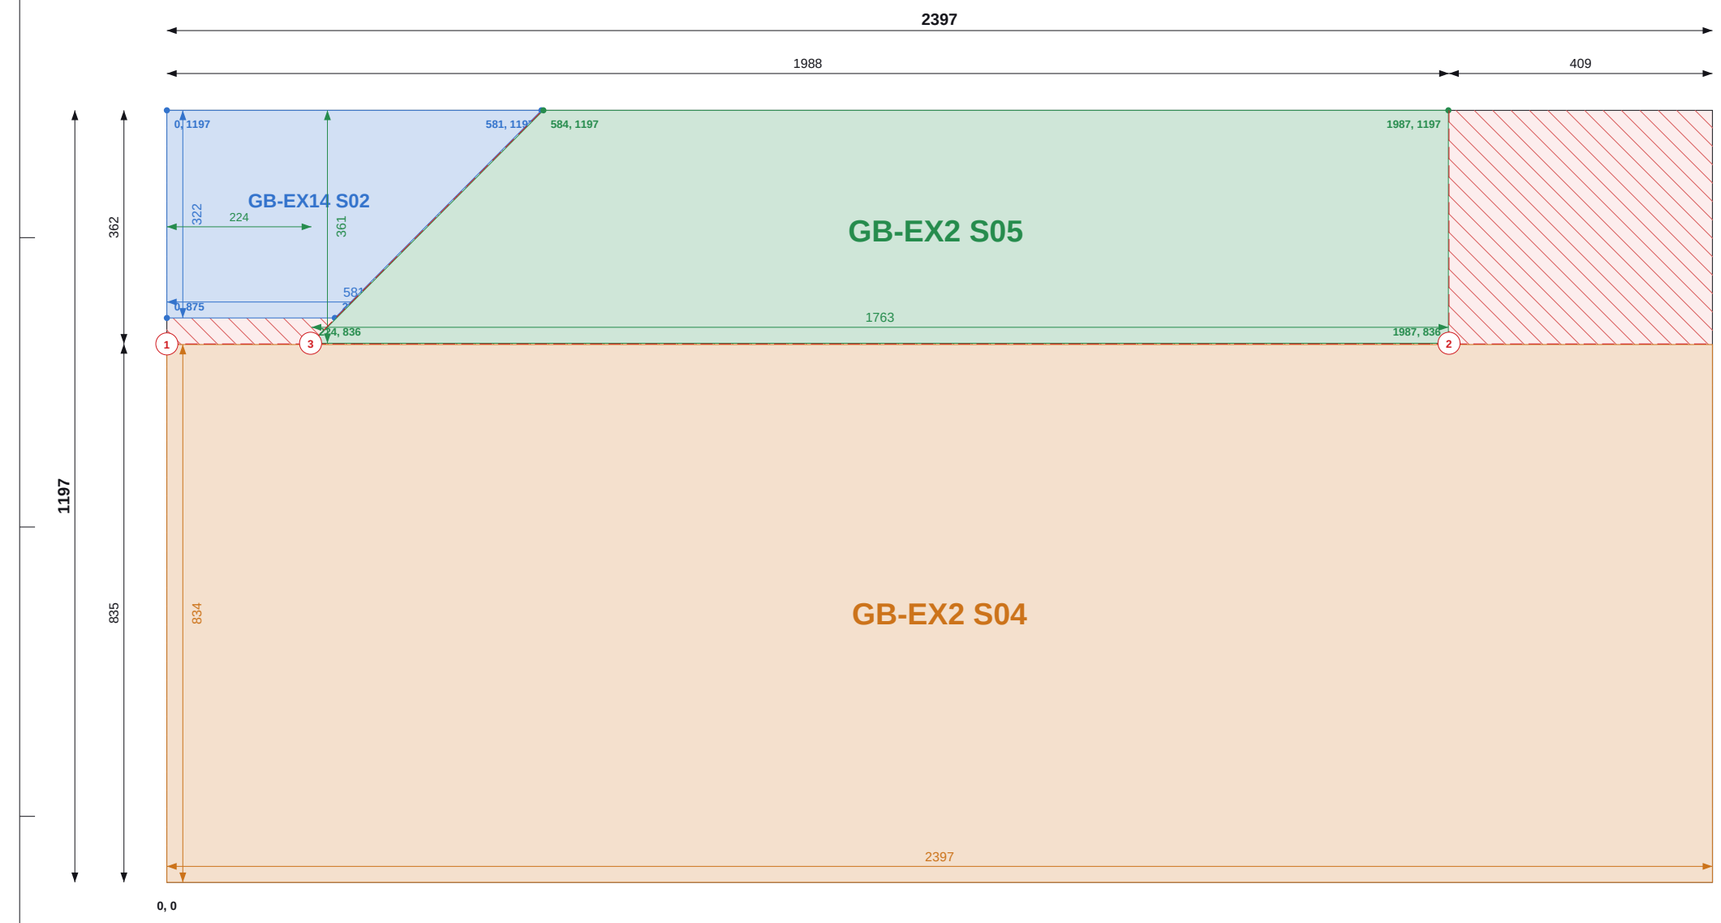


Top / left chains = saw cut positions (to cut centres). Coloured = part size and position.

Do not scale. All dimensions in mm. Check all dimensions on site.

## SHEET 19 OF 21

### THIS SHEET

| Item | Value |
|---|---|
| Parts | 3 |
| Used / waste | 94.3% / 0.16 m2 |
| Reusable offcuts | 1 |
| Saw cuts / shared | 3 / 2 |

### PIECES (POSITION = BOTTOM-LEFT CORNER)

| Label | Size | X, Y |
|---|---|---|
| GB-EX14 S02 | 322 x 581 rake to 262 | 0, 875 |
| GB-EX2 S05 | 361 x 1763 rake to 1405 | 224, 836 |
| GB-EX2 S04 | 834 x 2397 | 0, 0 |

### NOTES

1. Cut from OSB/3 9mm 1197x2397, 2mm saw kerf. Viewed on the face; dimensions from the sheet's bottom-left corner (0,0). Red numbered lines = saw cuts in order, each edge to edge.
2. Coloured dimensions belong to the part of that colour: its width and height, and its position from the sheet edges. Raked parts: corner coordinates at each corner.
3. Red hatch = waste. Labels = panel + piece mark on the manufacture drawing.

### REVISIONS

| REV | DATE | DESCRIPTION |
|---|---|---|
| C01 | 14.09.26 | Construction issue |
| C02 | 14.09.26 | Roof trusses revised; SP diagonals added |
| C03 | 11.10.26 | FF windows coursed; steel + GP1 portal; steel drawings (ST) |
| C04 | 13.10.26 | Steel approved by the engineer: steel + steel timber drawings issued for construction |

TLS TIMBER FRAME
Design & Manufacture
Scan: 3D model + drawings

| CLIENT | PROJECT |
|---|---|
| MP Adams | MP Adams Plot 4, Eckington |


DRAWING TITLE

**OSB CUTTING - GABLES - SHEET 19 OF 21**

OSB/3 9mm 1197x2397 | Gables

| SCALE | SIZE | DATE | DRAWN |
|---|---|---|---|
| NTS | A3 | 13.10.26 | TS |

| STATUS | DRAWING No. | REV |
|---|---|---|
| CONSTRUCTION | P4-CP-OSB-03 / 19 | C04 |

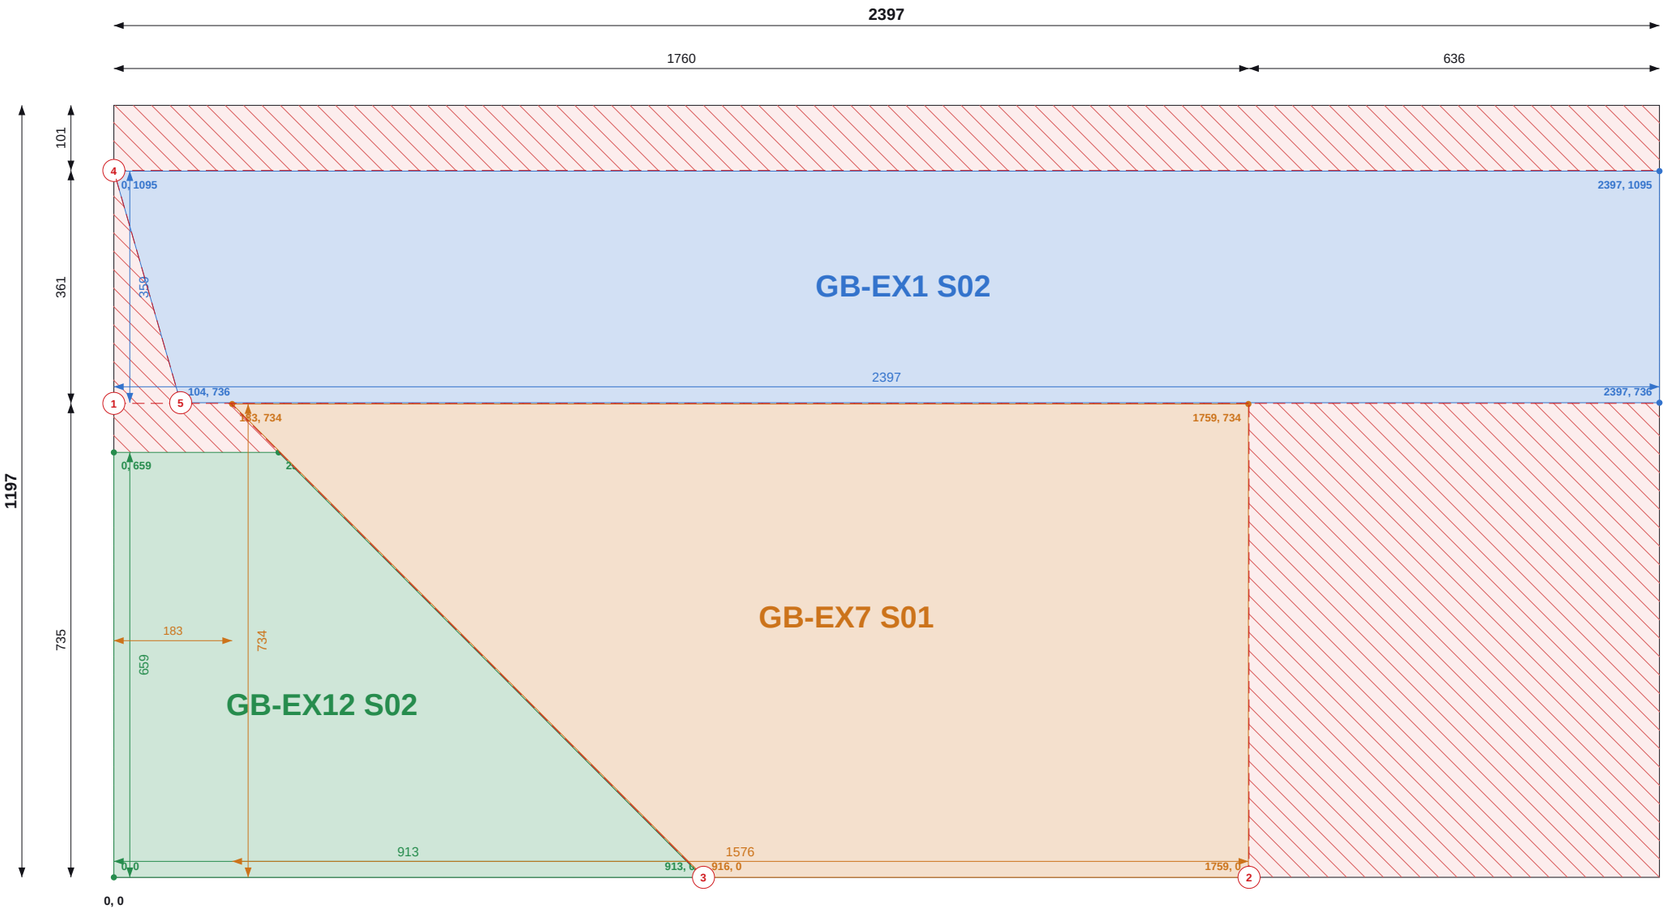


Top / left chains = saw cut positions (to cut centres). Coloured = part size and position.

## SHEET 20 OF 21

### THIS SHEET

| Item | Value |
|---|---|
| Parts | 3 |
| Used / waste | 73.7% / 0.75 m2 |
| Reusable offcuts | 1 |
| Saw cuts / shared | 5 / 3 |

### PIECES (POSITION = BOTTOM-LEFT CORNER)

| Label | Size | X, Y |
|---|---|---|
| GB-EX1 S02 | 359 x 2397 rake to 2294 | 0, 736 |
| GB-EX12 S02 | 659 x 913 rake to 257 | 0, 0 |
| GB-EX7 S01 | 734 x 1576 rake to 845 | 183, 0 |

### NOTES

1. Cut from OSB/3 9mm 1197x2397, 2mm saw kerf. Viewed on the face; dimensions from the sheet's bottom-left corner (0,0). Red numbered lines = saw cuts in order, each edge to edge.
2. Coloured dimensions belong to the part of that colour: its width and height, and its position from the sheet edges. Raked parts: corner coordinates at each corner.
3. Red hatch = waste. Labels = panel + piece mark on the manufacture drawing.

### REVISIONS

| REV | DATE | DESCRIPTION |
|---|---|---|
| C01 | 14.09.26 | Construction issue |
| C02 | 14.09.26 | Roof trusses revised; SP diagonals added |
| C03 | 11.10.26 | FF windows coursed; steel + GP1 portal; steel drawings (ST) |
| C04 | 13.10.26 | Steel approved by the engineer: steel + steel timber drawings issued for construction |

TLS TIMBER FRAME
Design & Manufacture
Scan: 3D model + drawings

| CLIENT | PROJECT |
|---|---|
| MP Adams | MP Adams Plot 4, Eckington |

DRAWING TITLE


**OSB CUTTING - GABLES - SHEET 20 OF 21**

OSB/3 9mm 1197x2397 | Gables

| SCALE | SIZE | DATE | DRAWN |
|---|---|---|---|
| NTS | A3 | 13.10.26 | TS |

| STATUS | DRAWING No. | REV |
|---|---|---|
| CONSTRUCTION | P4-CP-OSB-03 / 20 | C04 |

Do not scale. All dimensions in mm. Check all dimensions on site.

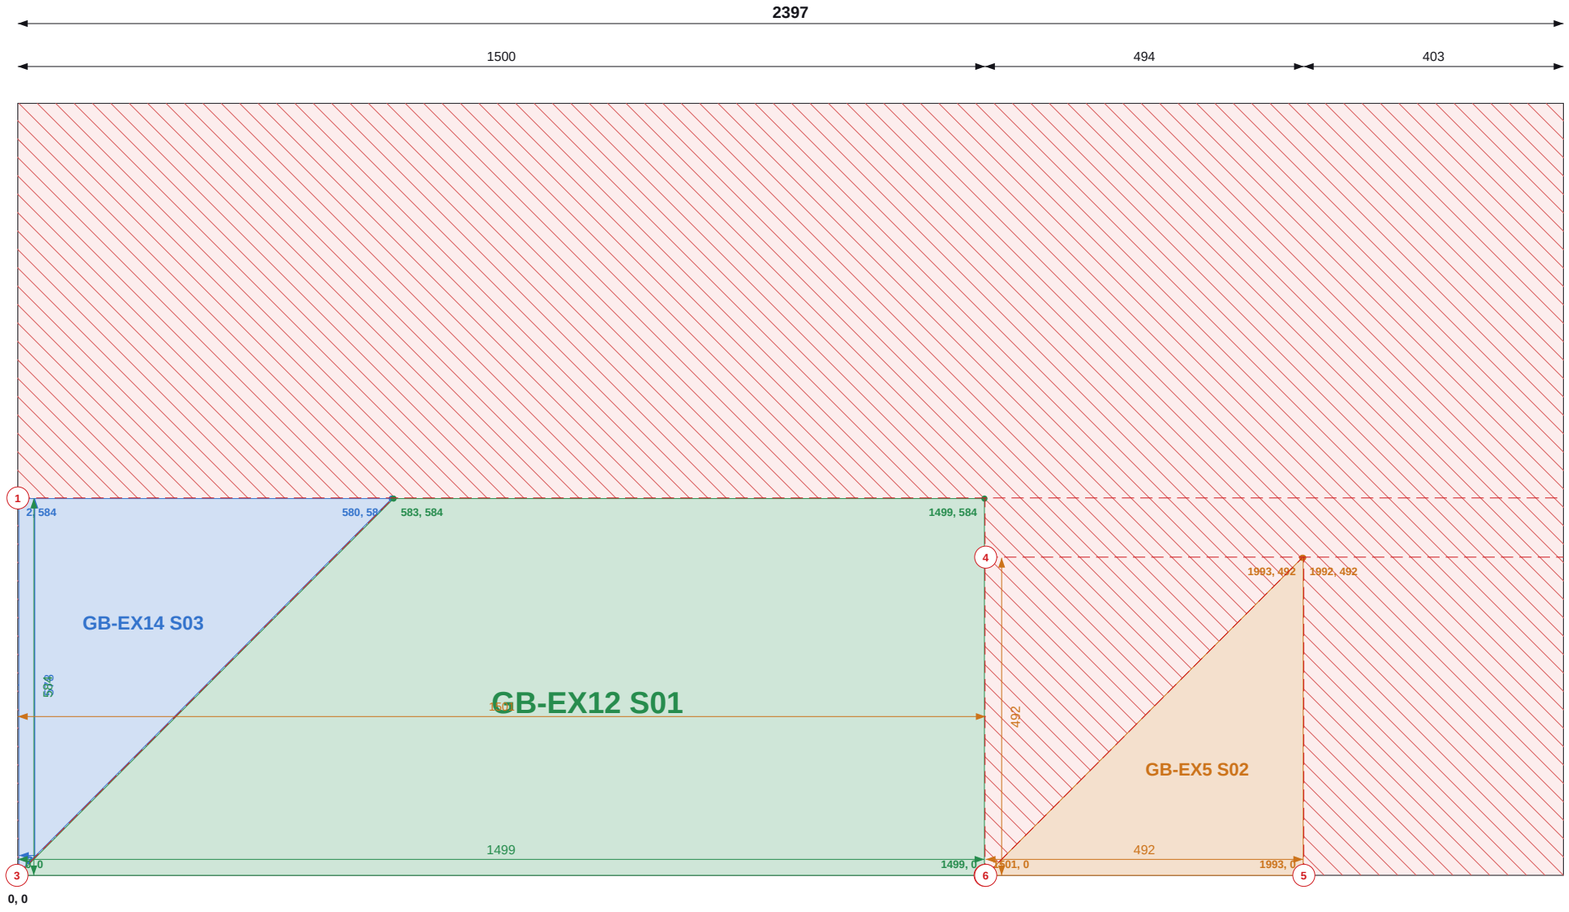


Top / left chains = saw cut positions (to cut centres). Coloured = part size and position.

## SHEET 21 OF 21

### THIS SHEET

| Item | Value |
|---|---|
| Parts | 3 |
| Used / waste | 34.7% / 1.87 m2 |
| Reusable offcuts | 2 |
| Saw cuts / shared | 6 / 3 |

### PIECES (POSITION = BOTTOM-LEFT CORNER)

| Label | Size | X, Y |
|---|---|---|
| GB-EX14 S03 | 578 x 578 rake to 3 | 2, 6 |
| GB-EX12 S01 | 584 x 1499 rake to 917 | 0, 0 |
| GB-EX5 S02 | 492 x 492 rake to 3 | 1501, 0 |

### NOTES

1. Cut from OSB/3 9mm 1197x2397, 2mm saw kerf. Viewed on the face; dimensions from the sheet's bottom-left corner (0,0). Red numbered lines = saw cuts in order, each edge to edge.
2. Coloured dimensions belong to the part of that colour: its width and height, and its position from the sheet edges. Raked parts: corner coordinates at each corner.
3. Red hatch = waste. Labels = panel + piece mark on the manufacture drawing.

### REVISIONS

| REV | DATE | DESCRIPTION |
|---|---|---|
| C01 | 14.09.26 | Construction issue |
| C02 | 14.09.26 | Roof trusses revised; SP diagonals added |
| C03 | 11.10.26 | FF windows coursed; steel + GP1 portal; steel drawings (ST) |
| C04 | 13.10.26 | Steel approved by the engineer: steel + steel timber drawings issued for construction |

TLS TIMBER FRAME
Design & Manufacture
Scan: 3D model + drawings

| CLIENT | PROJECT |
|---|---|
| MP Adams | MP Adams Plot 4, Eckington |

DRAWING TITLE
**OSB CUTTING - GABLES - SHEET 21 OF 21**

OSB/3 9mm 1197x2397 | Gables

| SCALE | SIZE | DATE | DRAWN |
|---|---|---|---|
| NTS | A3 | 13.10.26 | TS |

| STATUS | DRAWING No. | REV |
|---|---|---|
| CONSTRUCTION | P4-CP-OSB-03 / 21 | C04 |

Do not scale. All dimensions in mm. Check all dimensions on site.