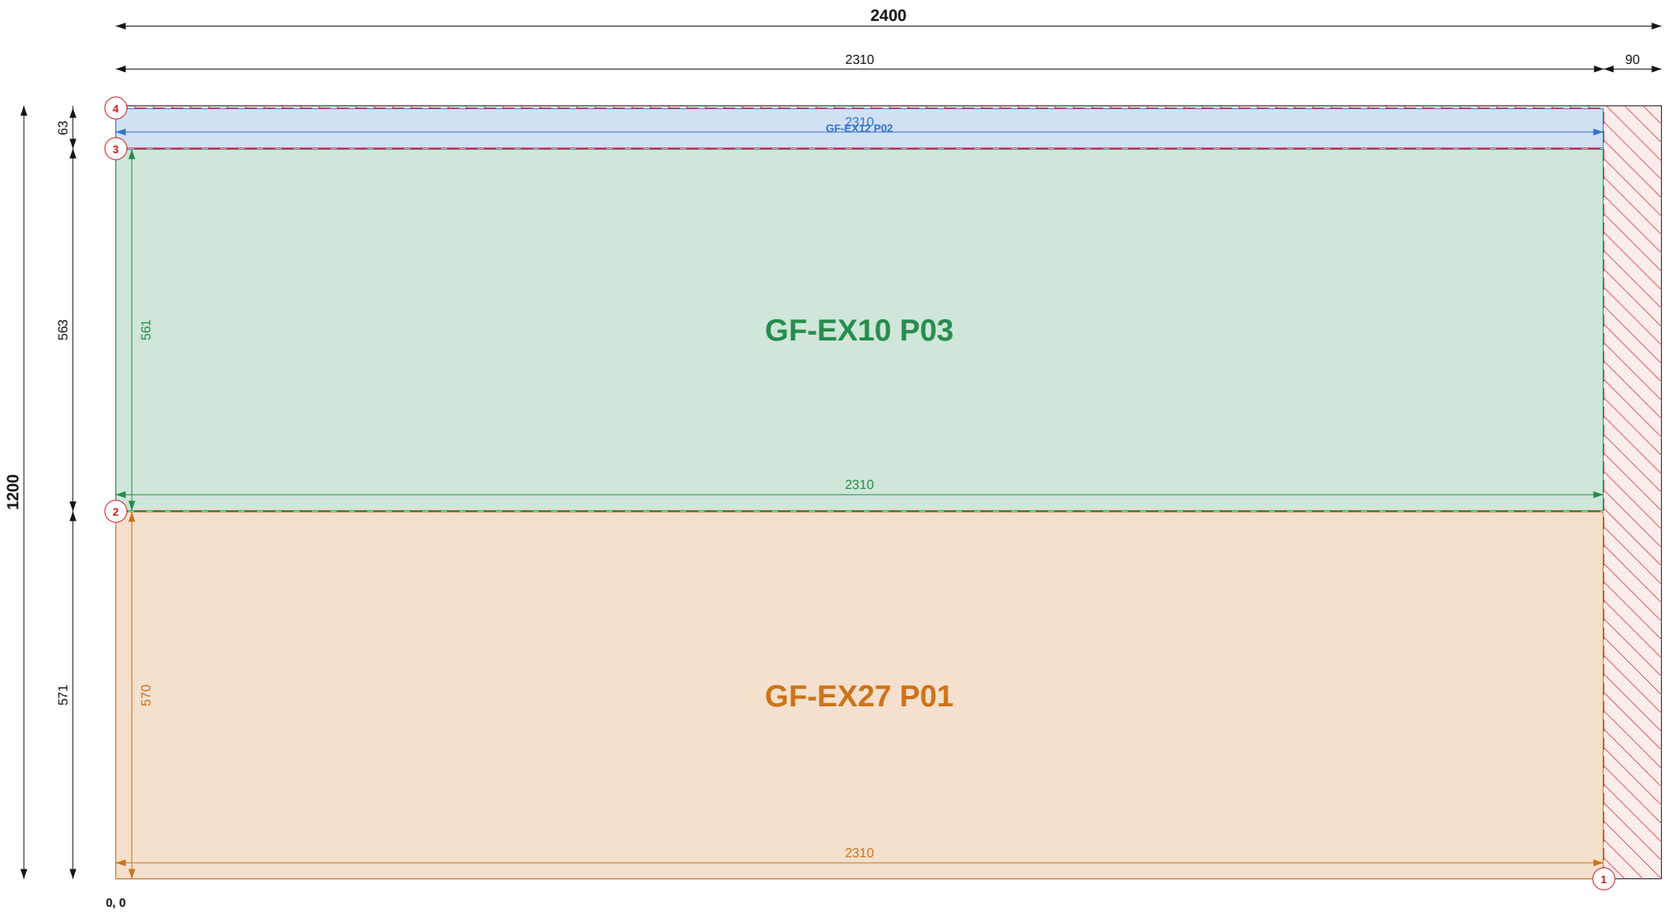


Top / left chains = saw cut positions (to cut centres). Coloured = part size and position.

SHEET 1 OF 33

THIS SHEET

Item	Value
Parts	3
Used / waste	95.6% / 0.13 m2
Reusable offcuts	0
Saw cuts / shared	4 / 2

PIECES (POSITION = BOTTOM-LEFT CORNER)

Label	Size	X, Y
GF-EX12 P02	61 x 2310	0, 1135
GF-EX10 P03	561 x 2310	0, 572
GF-EX27 P01	570 x 2310	0, 0

GROUND FLOOR TOTALS

Item	Value
Sheets / pieces	33 / 221
Yield / waste	91.6% / 8.00 m2
Saw cuts / shared / on stock edge	274 / 188 / 188

NOTES

1. Cut from PIR 120mm 1200x2400, 2mm saw kerf. Viewed on the face; dimensions from the sheet's bottom-left corner (0,0). Red numbered lines = saw cuts in order, each edge to edge.
2. Coloured dimensions belong to the part of that colour: its width and height, and its position from the sheet edges. Raked parts: corner coordinates at each corner.
3. Red hatch = waste. Labels = panel + piece mark on the manufacture drawing.

REVISIONS

REV	DATE	DESCRIPTION
C01	14.09.26	Construction issue
C02	14.09.26	Roof trusses revised; SP diagonals added
C03	11.10.26	FF windows coursed; steel + GP1 portal; steel drawings (ST)
C04	13.10.26	Steel approved by the engineer: steel + steel timber drawings issued for construction

TLS TIMBER FRAME
Design & Manufacture
Scan: 3D model + drawings

CLIENT	PROJECT
MP Adams	MP Adams Plot 4, Eckington

DRAWING TITLE


PIR CUTTING - GROUND FLOOR - SHEET 1 OF 33

PIR 120mm 1200x2400 | Ground Floor

SCALE	SIZE	DATE	DRAWN
NTS	A3	13.10.26	TS

STATUS	DRAWING No.	REV
CONSTRUCTION	P4-CP-PIR-01 / 01	C04

Do not scale. All dimensions in mm. Check all dimensions on site.

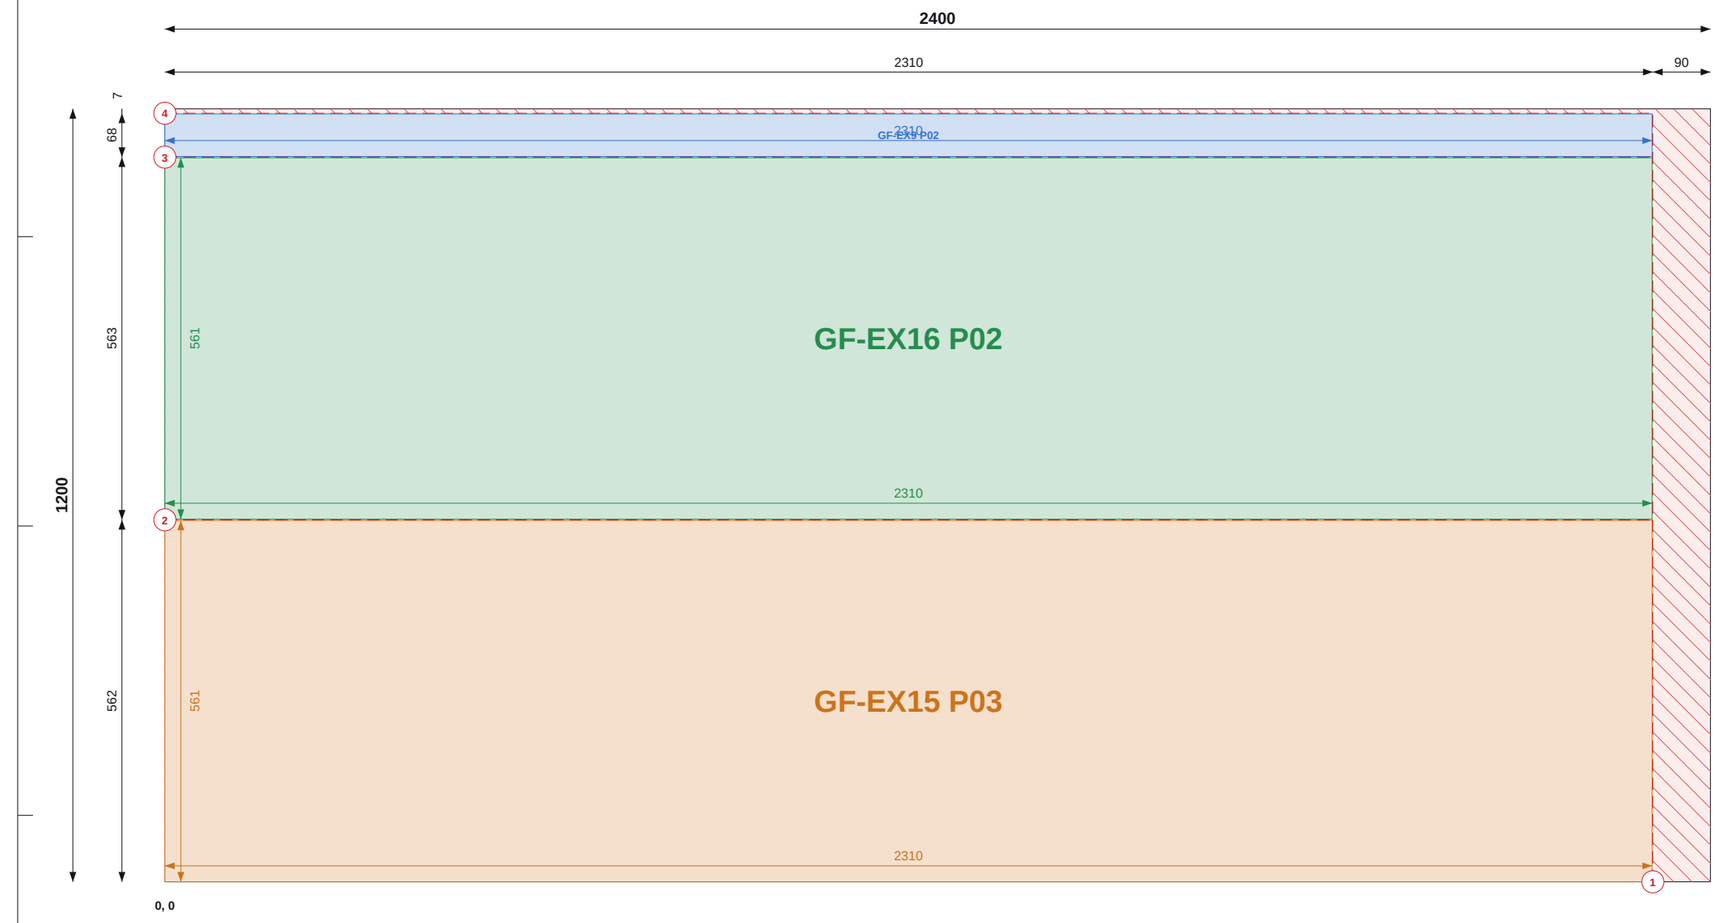

Top / left chains = saw cut positions (to cut centres). Coloured = part size and position.

SHEET 2 OF 33

THIS SHEET

Item	Value
Parts	3
Used / waste	95.3% / 0.14 m2
Reusable offcuts	0
Saw cuts / shared	4 / 2

PIECES (POSITION = BOTTOM-LEFT CORNER)

Label	Size	X, Y
GF-EX9 P02	66 x 2310	0, 1126
GF-EX16 P02	561 x 2310	0, 563
GF-EX15 P03	561 x 2310	0, 0

NOTES

1. Cut from PIR 120mm 1200x2400, 2mm saw kerf. Viewed on the face; dimensions from the sheet's bottom-left corner (0,0). Red numbered lines = saw cuts in order, each edge to edge.
2. Coloured dimensions belong to the part of that colour: its width and height, and its position from the sheet edges. Raked parts: corner coordinates at each corner.
3. Red hatch = waste. Labels = panel + piece mark on the manufacture drawing.

REVISIONS

REV	DATE	DESCRIPTION
C01	14.09.26	Construction issue
C02	14.09.26	Roof trusses revised; SP diagonals added
C03	11.10.26	FF windows coursed; steel + GP1 portal; steel drawings (ST)
C04	13.10.26	Steel approved by the engineer: steel + steel timber drawings issued for construction

TLS TIMBER FRAME DESIGN SUITE

TLS TIMBER FRAME
Design & Manufacture
Scan: 3D model + drawings

CLIENT	PROJECT
MP Adams	MP Adams Plot 4, Eckington

DRAWING TITLE


PIR CUTTING - GROUND FLOOR - SHEET 2 OF 33

PIR 120mm 1200x2400 | Ground Floor

SCALE	SIZE	DATE	DRAWN
NTS	A3	13.10.26	TS

STATUS	DRAWING No.	REV
CONSTRUCTION	P4-CP-PIR-01 / 02	C04

Do not scale. All dimensions in mm. Check all dimensions on site.

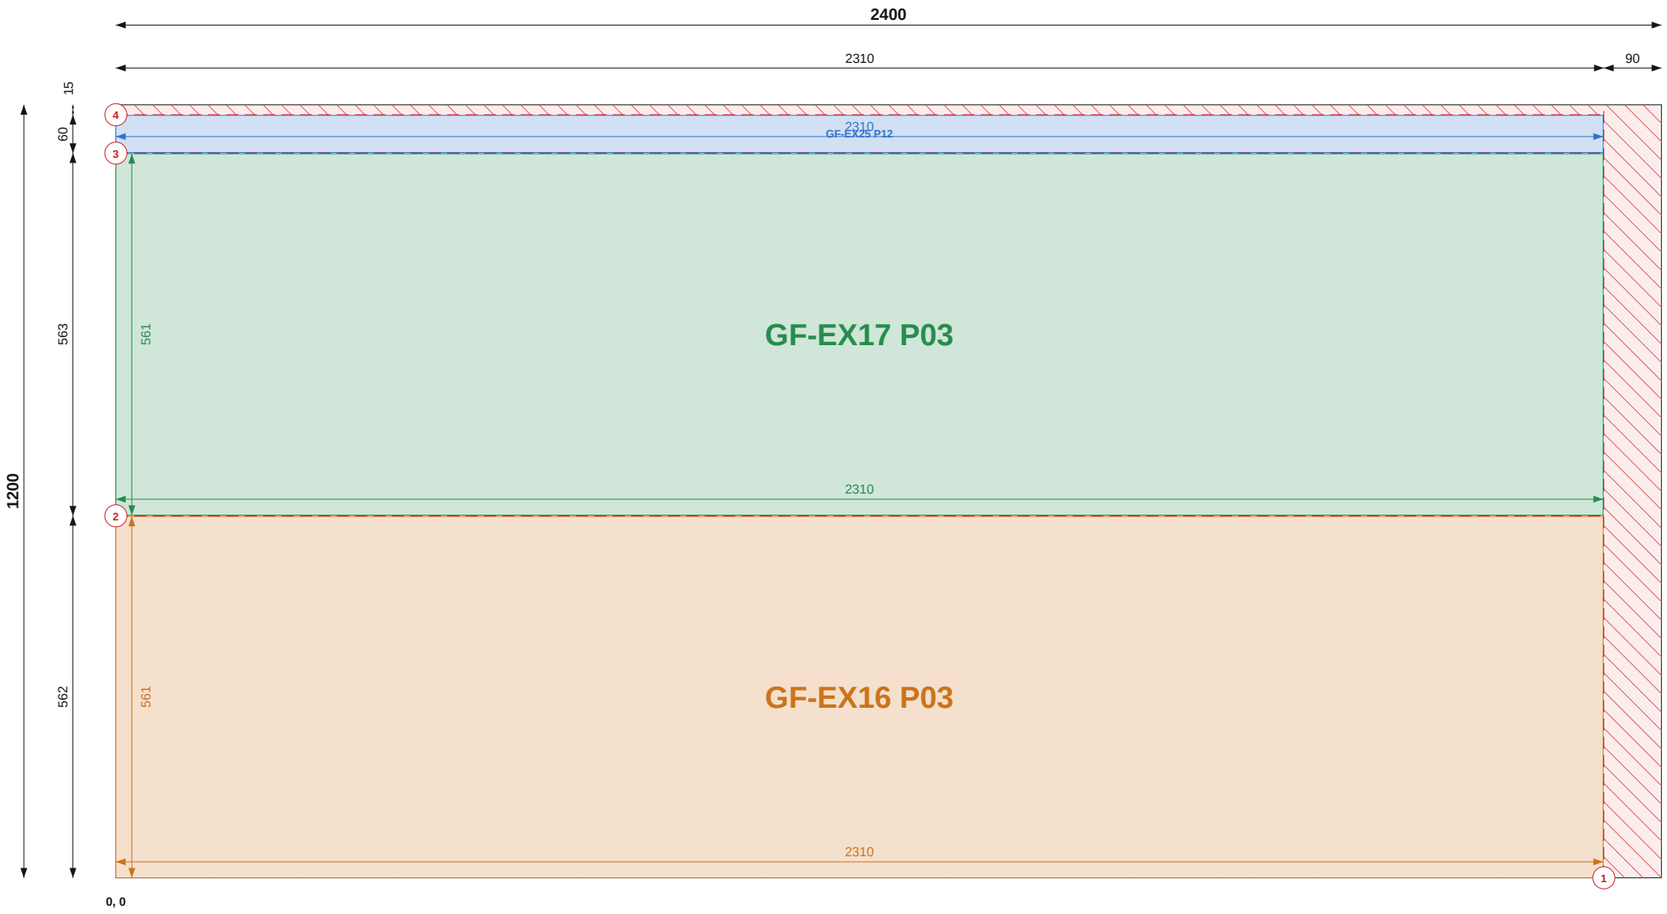

Top / left chains = saw cut positions (to cut centres). Coloured = part size and position.

SHEET 3 OF 33

THIS SHEET

Item	Value
Parts	3
Used / waste	94.6% / 0.16 m2
Reusable offcuts	0
Saw cuts / shared	4 / 2

PIECES (POSITION = BOTTOM-LEFT CORNER)

Label	Size	X, Y
GF-EX25 P12	58 x 2310	0, 1126
GF-EX17 P03	561 x 2310	0, 563
GF-EX16 P03	561 x 2310	0, 0

NOTES

1. Cut from PIR 120mm 1200x2400, 2mm saw kerf. Viewed on the face; dimensions from the sheet's bottom-left corner (0,0). Red numbered lines = saw cuts in order, each edge to edge.
2. Coloured dimensions belong to the part of that colour: its width and height, and its position from the sheet edges. Raked parts: corner coordinates at each corner.
3. Red hatch = waste. Labels = panel + piece mark on the manufacture drawing.

REVISIONS

REV	DATE	DESCRIPTION
C01	14.09.26	Construction issue
C02	14.09.26	Roof trusses revised; SP diagonals added
C03	11.10.26	FF windows coursed; steel + GP1 portal; steel drawings (ST)
C04	13.10.26	Steel approved by the engineer: steel + steel timber drawings issued for construction

TLS TIMBER FRAME
Design & Manufacture
Scan: 3D model + drawings

CLIENT	PROJECT
MP Adams	MP Adams Plot 4, Eckington

DRAWING TITLE


PIR CUTTING - GROUND FLOOR - SHEET 3 OF 33

PIR 120mm 1200x2400 | Ground Floor

SCALE	SIZE	DATE	DRAWN
NTS	A3	13.10.26	TS

STATUS	DRAWING No.	REV
CONSTRUCTION	P4-CP-PIR-01 / 03	C04

Do not scale. All dimensions in mm. Check all dimensions on site.

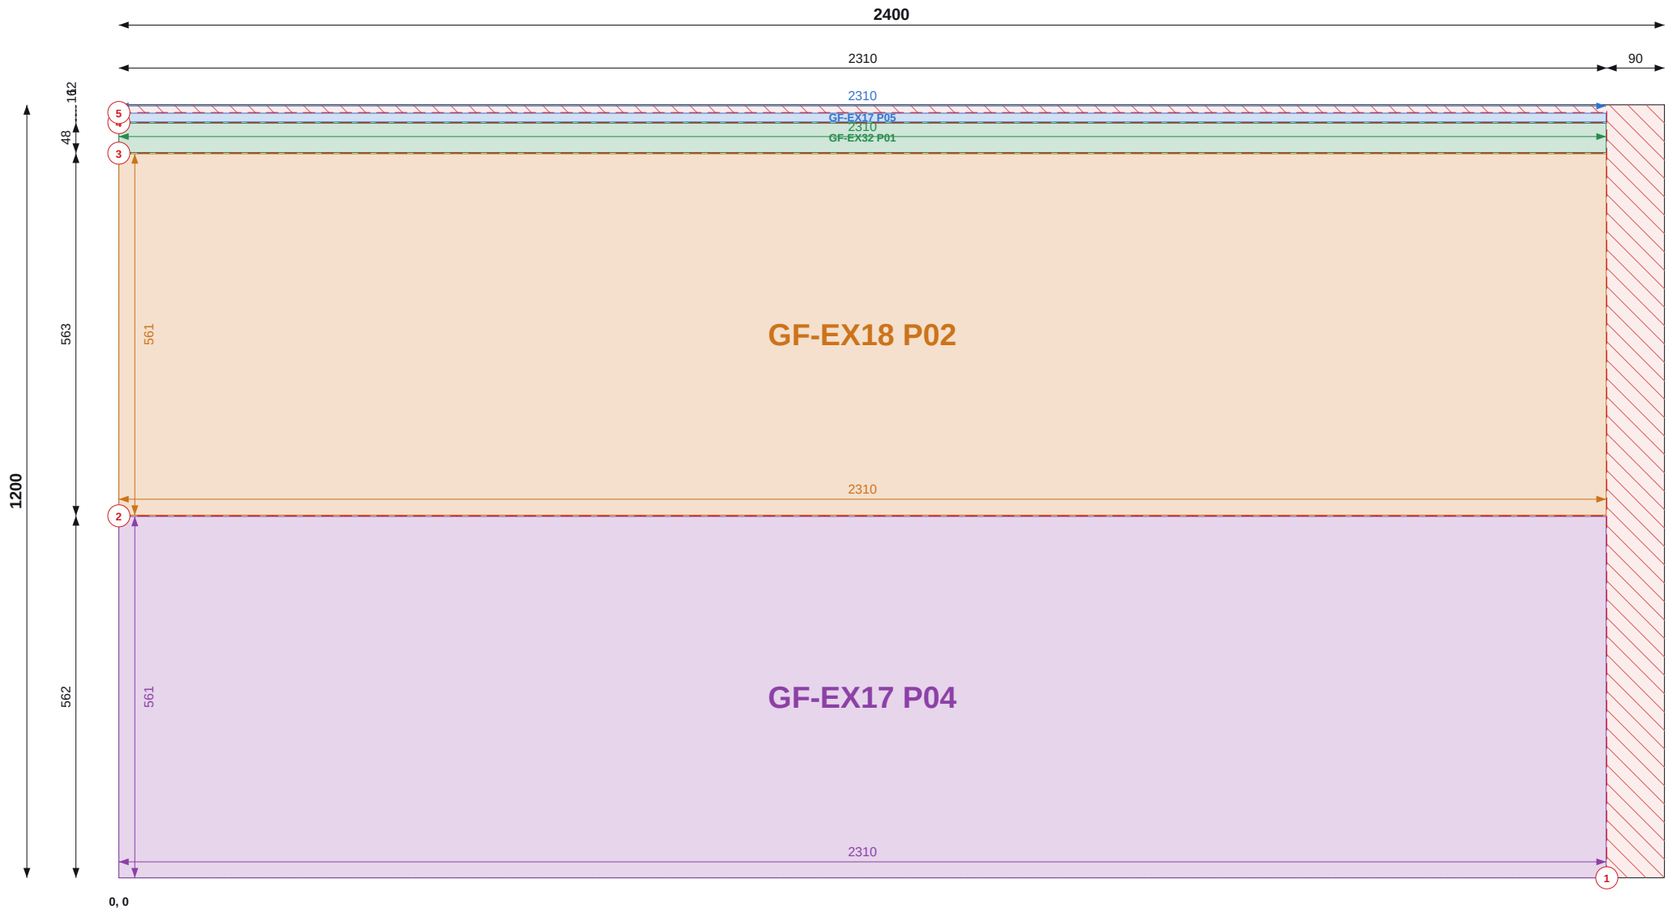

Top / left chains = saw cut positions (to cut centres). Coloured = part size and position.

SHEET 4 OF 33

THIS SHEET

Item	Value
Parts	4
Used / waste	94.7% / 0.15 m2
Reusable offcuts	0
Saw cuts / shared	5 / 3

PIECES (POSITION = BOTTOM-LEFT CORNER)

Label	Size	X, Y
GF-EX17 P05	14 x 2310	0, 1174
GF-EX32 P01	46 x 2310	0, 1126
GF-EX18 P02	561 x 2310	0, 563
GF-EX17 P04	561 x 2310	0, 0

NOTES

1. Cut from PIR 120mm 1200x2400, 2mm saw kerf. Viewed on the face; dimensions from the sheet's bottom-left corner (0,0). Red numbered lines = saw cuts in order, each edge to edge.
2. Coloured dimensions belong to the part of that colour: its width and height, and its position from the sheet edges. Raked parts: corner coordinates at each corner.
3. Red hatch = waste. Labels = panel + piece mark on the manufacture drawing.

REVISIONS

REV	DATE	DESCRIPTION
C01	14.09.26	Construction issue
C02	14.09.26	Roof trusses revised; SP diagonals added
C03	11.10.26	FF windows coursed; steel + GP1 portal; steel drawings (ST)
C04	13.10.26	Steel approved by the engineer: steel + steel timber drawings issued for construction

TLS TIMBER FRAME
Design & Manufacture
Scan: 3D model + drawings

CLIENT	PROJECT
MP Adams	MP Adams Plot 4, Eckington

DRAWING TITLE


PIR CUTTING - GROUND FLOOR - SHEET 4 OF 33

PIR 120mm 1200x2400 | Ground Floor

SCALE	SIZE	DATE	DRAWN
NTS	A3	13.10.26	TS

STATUS	DRAWING No.	REV
CONSTRUCTION	P4-CP-PIR-01 / 04	C04

Do not scale. All dimensions in mm. Check all dimensions on site.

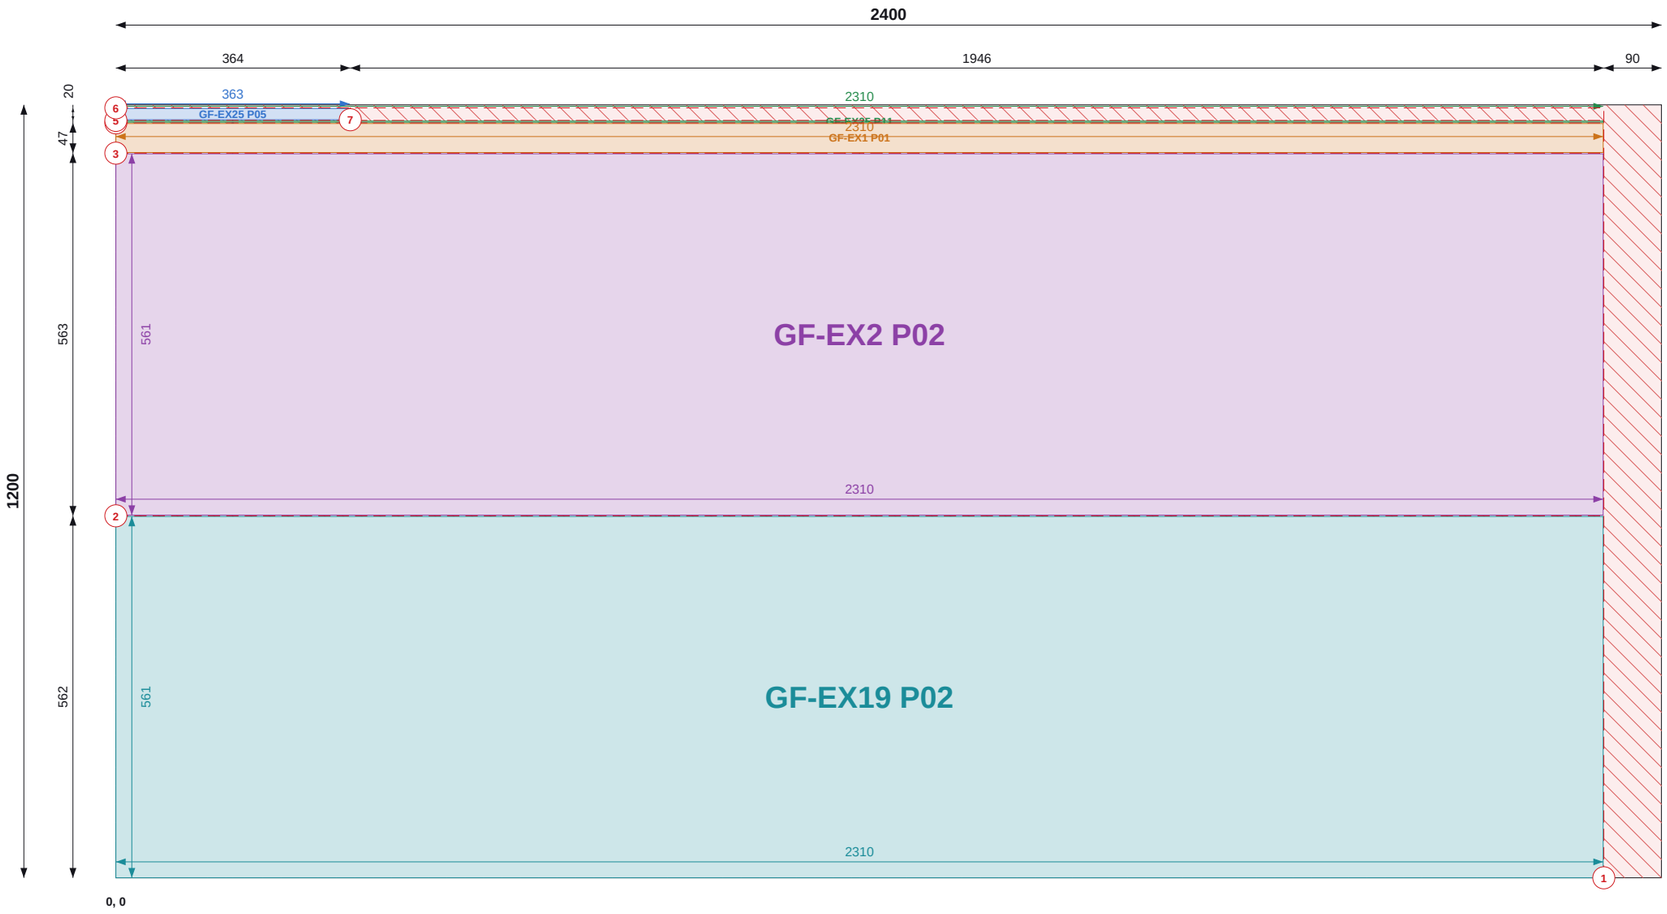

Top / left chains = saw cut positions (to cut centres). Coloured = part size and position.

SHEET 5 OF 33

THIS SHEET

Item	Value
Parts	5
Used / waste	94.0% / 0.17 m2
Reusable offcuts	0
Saw cuts / shared	7 / 4

PIECES (POSITION = BOTTOM-LEFT CORNER)

Label	Size	X, Y
GF-EX25 P05	363 x 18	0, 1177
GF-EX25 P11	2 x 2310	0, 1173
GF-EX1 P01	45 x 2310	0, 1126
GF-EX2 P02	561 x 2310	0, 563
GF-EX19 P02	561 x 2310	0, 0

NOTES

1. Cut from PIR 120mm 1200x2400, 2mm saw kerf. Viewed on the face; dimensions from the sheet's bottom-left corner (0,0). Red numbered lines = saw cuts in order, each edge to edge.
2. Coloured dimensions belong to the part of that colour: its width and height, and its position from the sheet edges. Raked parts: corner coordinates at each corner.
3. Red hatch = waste. Labels = panel + piece mark on the manufacture drawing.

REVISIONS

REV	DATE	DESCRIPTION
C01	14.09.26	Construction issue
C02	14.09.26	Roof trusses revised; SP diagonals added
C03	11.10.26	FF windows coursed; steel + GP1 portal; steel drawings (ST)
C04	13.10.26	Steel approved by the engineer: steel + steel timber drawings issued for construction

TLS TIMBER FRAME DESIGN SUITE

TLS TIMBER FRAME
Design & Manufacture
Scan: 3D model + drawings

CLIENT	PROJECT
MP Adams	MP Adams Plot 4, Eckington

DRAWING TITLE


PIR CUTTING - GROUND FLOOR - SHEET 5 OF 33

PIR 120mm 1200x2400 | Ground Floor

SCALE	SIZE	DATE	DRAWN
NTS	A3	13.10.26	TS

STATUS	DRAWING No.	REV
CONSTRUCTION	P4-CP-PIR-01 / 05	C04

Do not scale. All dimensions in mm. Check all dimensions on site.

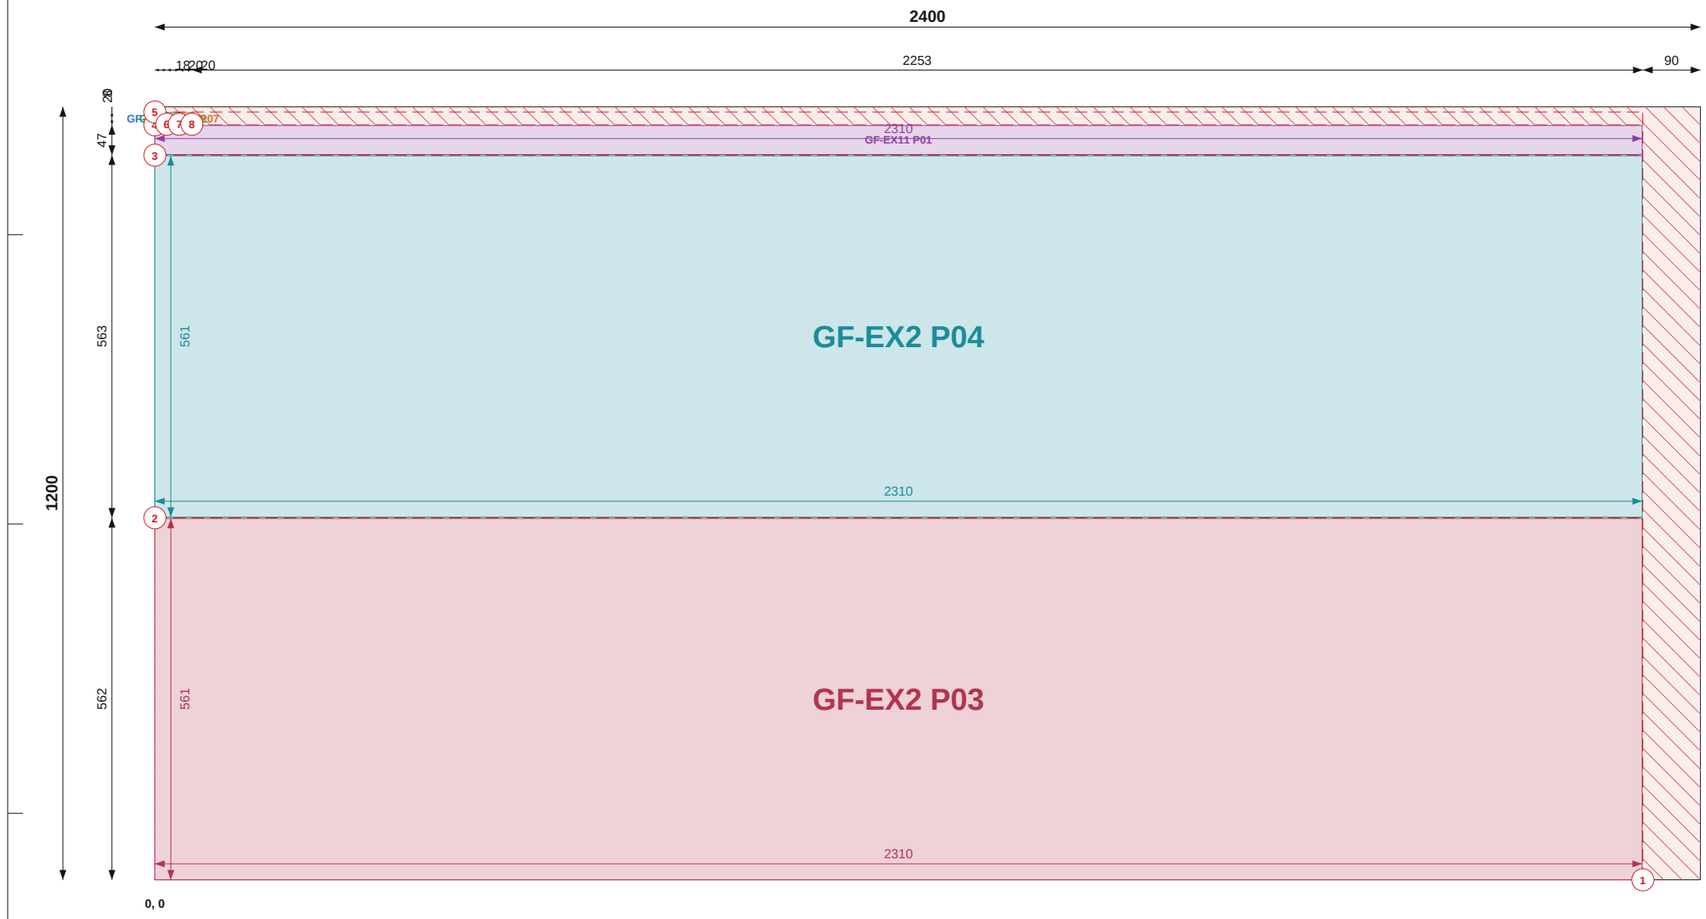

Top / left chains = saw cut positions (to cut centres). Coloured = part size and position.

SHEET 6 OF 33

THIS SHEET

Item	Value
Parts	6
Used / waste	93.6% / 0.18 m2
Reusable offcuts	0
Saw cuts / shared	8 / 5

PIECES (POSITION = BOTTOM-LEFT CORNER)

Label	Size	X, Y
GF-EX25 P10	18 x 18	0, 1173
GF-EX32 P02	18 x 18	20, 1173
GF-EX32 P07	18 x 18	39, 1173
GF-EX11 P01	45 x 2310	0, 1126
GF-EX2 P04	561 x 2310	0, 563
GF-EX2 P03	561 x 2310	0, 0

NOTES

1. Cut from PIR 120mm 1200x2400, 2mm saw kerf. Viewed on the face; dimensions from the sheet's bottom-left corner (0,0). Red numbered lines = saw cuts in order, each edge to edge.
2. Coloured dimensions belong to the part of that colour: its width and height, and its position from the sheet edges. Raked parts: corner coordinates at each corner.
3. Red hatch = waste. Labels = panel + piece mark on the manufacture drawing.

REVISIONS

REV	DATE	DESCRIPTION
C01	14.09.26	Construction issue
C02	14.09.26	Roof trusses revised; SP diagonals added
C03	11.10.26	FF windows coursed; steel + GP1 portal; steel drawings (ST)
C04	13.10.26	Steel approved by the engineer: steel + steel timber drawings issued for construction

TLS TIMBER FRAME
Design & Manufacture
Scan: 3D model + drawings

CLIENT	PROJECT
MP Adams	MP Adams Plot 4, Eckington

DRAWING TITLE


PIR CUTTING - GROUND FLOOR - SHEET 6 OF 33

PIR 120mm 1200x2400 | Ground Floor

SCALE	SIZE	DATE	DRAWN
NTS	A3	13.10.26	TS

STATUS	DRAWING No.	REV
CONSTRUCTION	P4-CP-PIR-01 / 06	C04

Do not scale. All dimensions in mm. Check all dimensions on site.

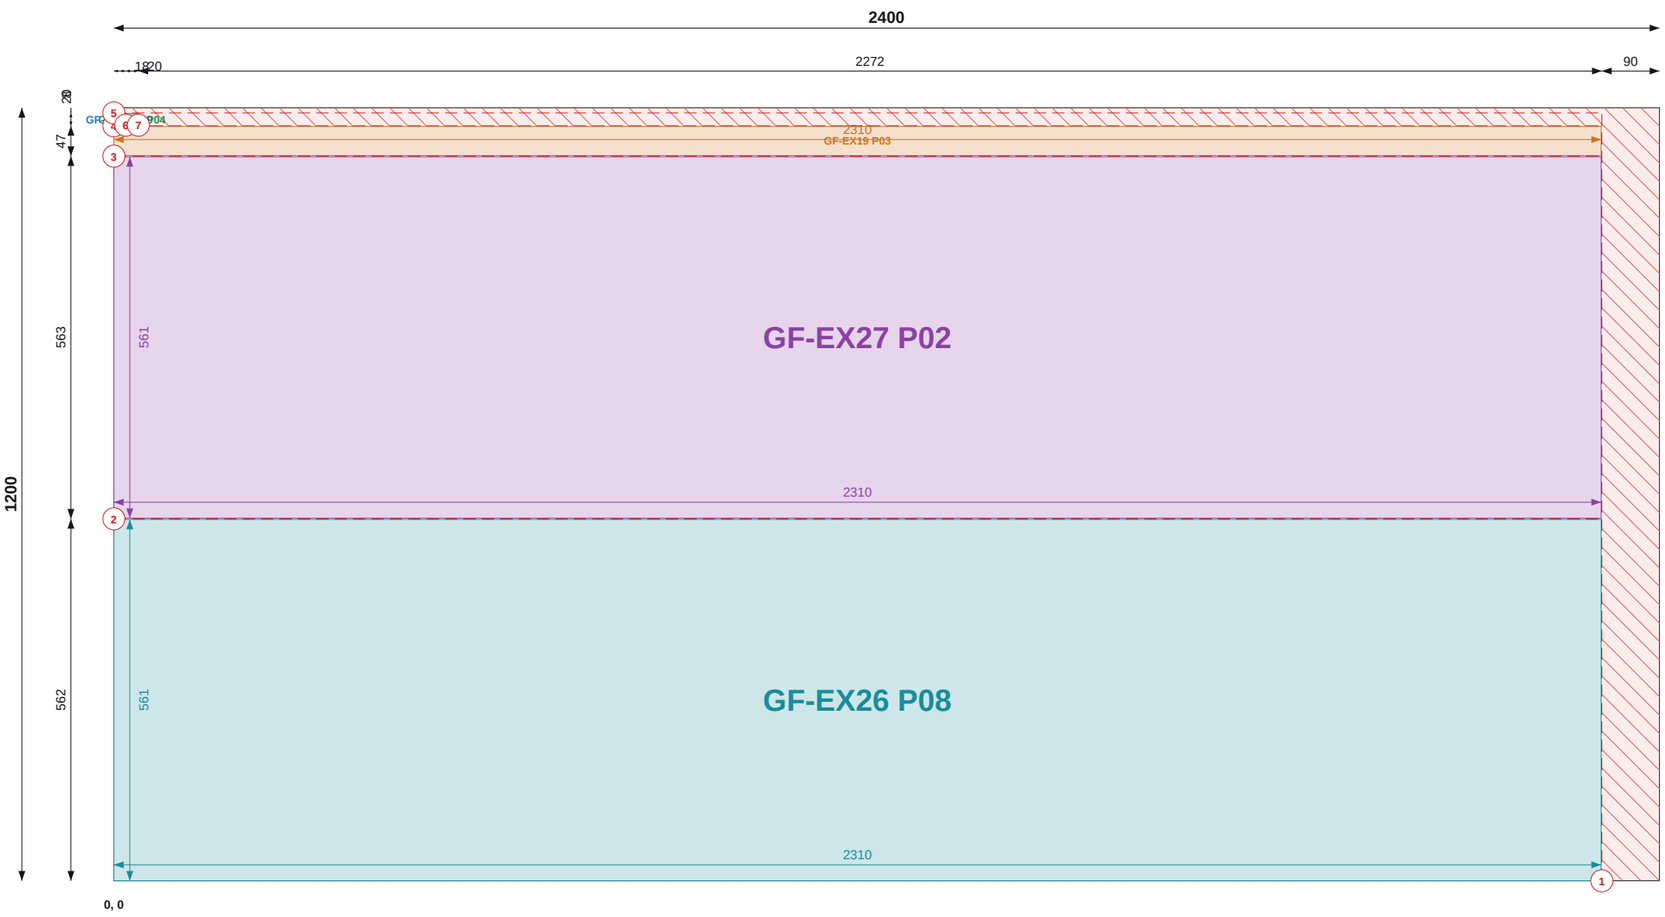

Top / left chains = saw cut positions (to cut centres). Coloured = part size and position.

Do not scale. All dimensions in mm. Check all dimensions on site.

SHEET 7 OF 33

THIS SHEET

Item	Value
Parts	5
Used / waste	93.6% / 0.18 m2
Reusable offcuts	0
Saw cuts / shared	7 / 4

PIECES (POSITION = BOTTOM-LEFT CORNER)

Label	Size	X, Y
GF-EX22 P09	18 x 18	0, 1173
GF-EX25 P04	18 x 18	20, 1173
GF-EX19 P03	45 x 2310	0, 1126
GF-EX27 P02	561 x 2310	0, 563
GF-EX26 P08	561 x 2310	0, 0

NOTES

1. Cut from PIR 120mm 1200x2400, 2mm saw kerf. Viewed on the face; dimensions from the sheet's bottom-left corner (0,0). Red numbered lines = saw cuts in order, each edge to edge.
2. Coloured dimensions belong to the part of that colour: its width and height, and its position from the sheet edges. Raked parts: corner coordinates at each corner.
3. Red hatch = waste. Labels = panel + piece mark on the manufacture drawing.

REVISIONS

REV	DATE	DESCRIPTION
C01	14.09.26	Construction issue
C02	14.09.26	Roof trusses revised; SP diagonals added
C03	11.10.26	FF windows coursed; steel + GP1 portal; steel drawings (ST)
C04	13.10.26	Steel approved by the engineer: steel + steel timber drawings issued for construction

TLS TIMBER FRAME
Design & Manufacture
Scan: 3D model + drawings

CLIENT	PROJECT
MP Adams	MP Adams Plot 4, Eckington


DRAWING TITLE

PIR CUTTING - GROUND FLOOR - SHEET 7 OF 33

PIR 120mm 1200x2400 | Ground Floor

SCALE	SIZE	DATE	DRAWN
NTS	A3	13.10.26	TS

STATUS	DRAWING No.	REV
CONSTRUCTION	P4-CP-PIR-01 / 07	C04

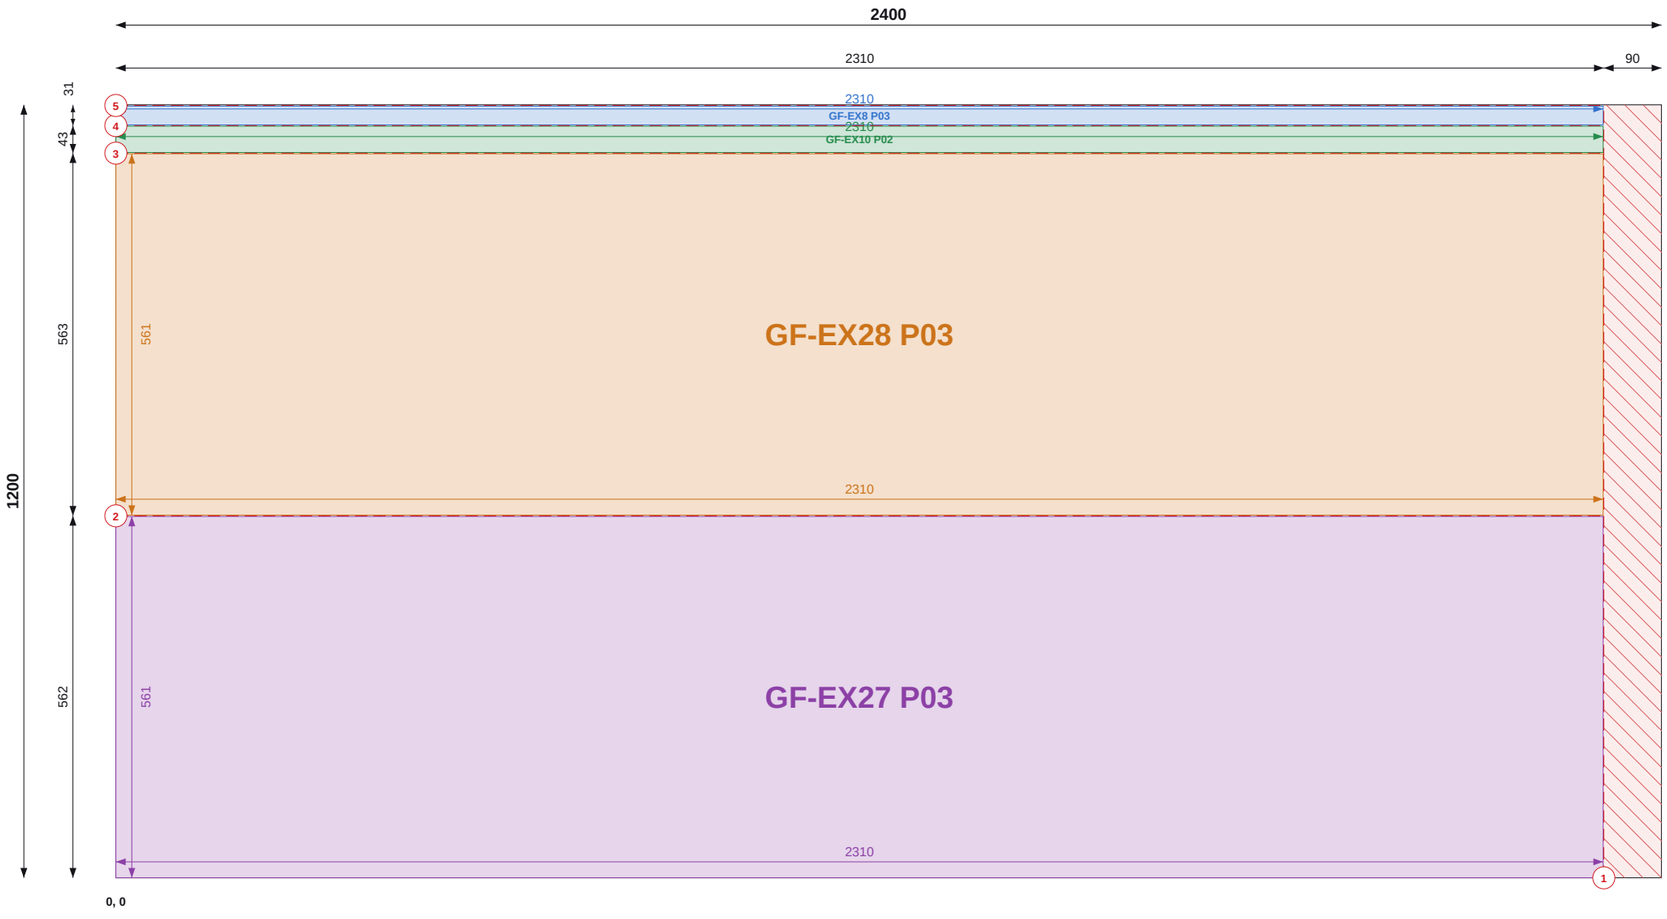

Top / left chains = saw cut positions (to cut centres). Coloured = part size and position.

SHEET 8 OF 33

THIS SHEET

Item	Value
Parts	4
Used / waste	95.6% / 0.13 m2
Reusable offcuts	0
Saw cuts / shared	5 / 3

PIECES (POSITION = BOTTOM-LEFT CORNER)

Label	Size	X, Y
GF-EX8 P03	29 x 2310	0, 1169
GF-EX10 P02	41 x 2310	0, 1126
GF-EX28 P03	561 x 2310	0, 563
GF-EX27 P03	561 x 2310	0, 0

NOTES

1. Cut from PIR 120mm 1200x2400, 2mm saw kerf. Viewed on the face; dimensions from the sheet's bottom-left corner (0,0). Red numbered lines = saw cuts in order, each edge to edge.
2. Coloured dimensions belong to the part of that colour: its width and height, and its position from the sheet edges. Raked parts: corner coordinates at each corner.
3. Red hatch = waste. Labels = panel + piece mark on the manufacture drawing.

REVISIONS

REV	DATE	DESCRIPTION
C01	14.09.26	Construction issue
C02	14.09.26	Roof trusses revised; SP diagonals added
C03	11.10.26	FF windows coursed; steel + GP1 portal; steel drawings (ST)
C04	13.10.26	Steel approved by the engineer: steel + steel timber drawings issued for construction

TLS TIMBER FRAME
Design & Manufacture
Scan: 3D model + drawings

CLIENT	PROJECT
MP Adams	MP Adams Plot 4, Eckington

DRAWING TITLE


PIR CUTTING - GROUND FLOOR - SHEET 8 OF 33

PIR 120mm 1200x2400 | Ground Floor

SCALE	SIZE	DATE	DRAWN
NTS	A3	13.10.26	TS

STATUS	DRAWING No.	REV
CONSTRUCTION	P4-CP-PIR-01 / 08	C04

Do not scale. All dimensions in mm. Check all dimensions on site.

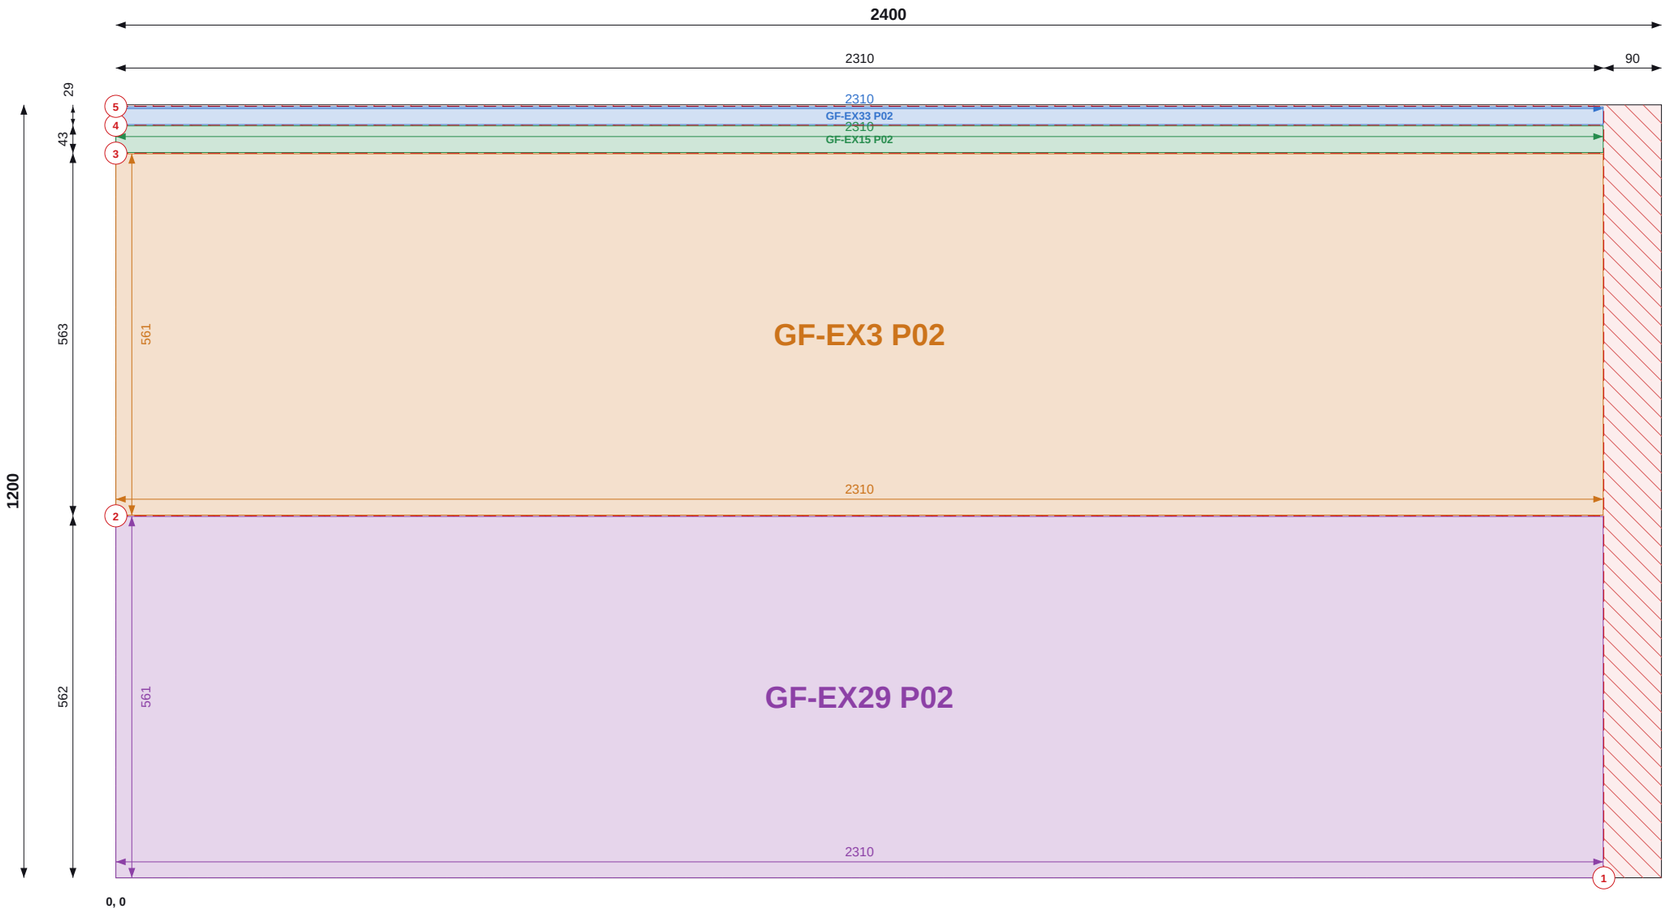

Top / left chains = saw cut positions (to cut centres). Coloured = part size and position.

SHEET 9 OF 33

THIS SHEET

Item	Value
Parts	4
Used / waste	95.5% / 0.13 m2
Reusable offcuts	0
Saw cuts / shared	5 / 3

PIECES (POSITION = BOTTOM-LEFT CORNER)

Label	Size	X, Y
GF-EX33 P02	27 x 2310	0, 1169
GF-EX15 P02	41 x 2310	0, 1126
GF-EX3 P02	561 x 2310	0, 563
GF-EX29 P02	561 x 2310	0, 0

NOTES

1. Cut from PIR 120mm 1200x2400, 2mm saw kerf. Viewed on the face; dimensions from the sheet's bottom-left corner (0,0). Red numbered lines = saw cuts in order, each edge to edge.
2. Coloured dimensions belong to the part of that colour: its width and height, and its position from the sheet edges. Raked parts: corner coordinates at each corner.
3. Red hatch = waste. Labels = panel + piece mark on the manufacture drawing.

REVISIONS

REV	DATE	DESCRIPTION
C01	14.09.26	Construction issue
C02	14.09.26	Roof trusses revised; SP diagonals added
C03	11.10.26	FF windows coursed; steel + GP1 portal; steel drawings (ST)
C04	13.10.26	Steel approved by the engineer: steel + steel timber drawings issued for construction

TLS TIMBER FRAME
Design & Manufacture
Scan: 3D model + drawings

CLIENT	PROJECT
MP Adams	MP Adams Plot 4, Eckington

DRAWING TITLE


PIR CUTTING - GROUND FLOOR - SHEET 9 OF 33

PIR 120mm 1200x2400 | Ground Floor

SCALE	SIZE	DATE	DRAWN
NTS	A3	13.10.26	TS

STATUS	DRAWING No.	REV
CONSTRUCTION	P4-CP-PIR-01 / 09	C04

Do not scale. All dimensions in mm. Check all dimensions on site.

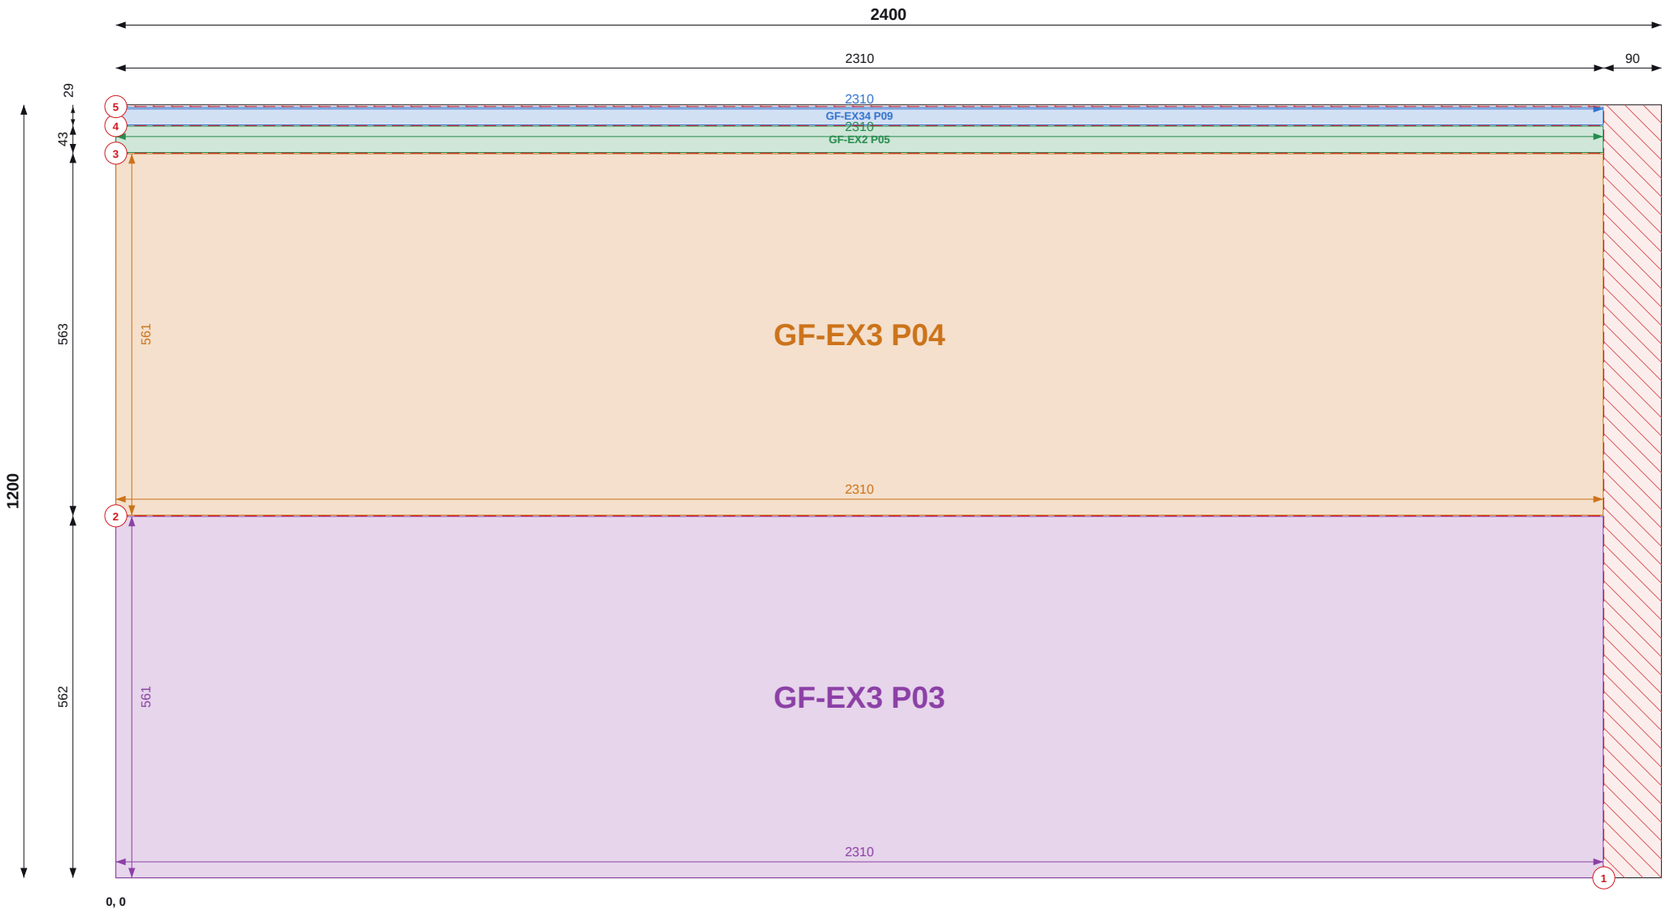

Top / left chains = saw cut positions (to cut centres). Coloured = part size and position.

SHEET 10 OF 33

THIS SHEET

Item	Value
Parts	4
Used / waste	95.4% / 0.13 m2
Reusable offcuts	0
Saw cuts / shared	5 / 3

PIECES (POSITION = BOTTOM-LEFT CORNER)

Label	Size	X, Y
GF-EX34 P09	27 x 2310	0, 1169
GF-EX2 P05	41 x 2310	0, 1126
GF-EX3 P04	561 x 2310	0, 563
GF-EX3 P03	561 x 2310	0, 0

NOTES

1. Cut from PIR 120mm 1200x2400, 2mm saw kerf. Viewed on the face; dimensions from the sheet's bottom-left corner (0,0). Red numbered lines = saw cuts in order, each edge to edge.
2. Coloured dimensions belong to the part of that colour: its width and height, and its position from the sheet edges. Raked parts: corner coordinates at each corner.
3. Red hatch = waste. Labels = panel + piece mark on the manufacture drawing.

REVISIONS

REV	DATE	DESCRIPTION
C01	14.09.26	Construction issue
C02	14.09.26	Roof trusses revised; SP diagonals added
C03	11.10.26	FF windows coursed; steel + GP1 portal; steel drawings (ST)
C04	13.10.26	Steel approved by the engineer: steel + steel timber drawings issued for construction

TLS TIMBER FRAME DESIGN SUITE

TLS TIMBER FRAME

Design & Manufacture

Scan: 3D model + drawings

CLIENT	PROJECT
MP Adams	MP Adams Plot 4, Eckington

DRAWING TITLE


PIR CUTTING - GROUND FLOOR - SHEET 10 OF 33

PIR 120mm 1200x2400 | Ground Floor

SCALE	SIZE	DATE	DRAWN
NTS	A3	13.10.26	TS

STATUS	DRAWING No.	REV
CONSTRUCTION	P4-CP-PIR-01 / 10	C04

Do not scale. All dimensions in mm. Check all dimensions on site.

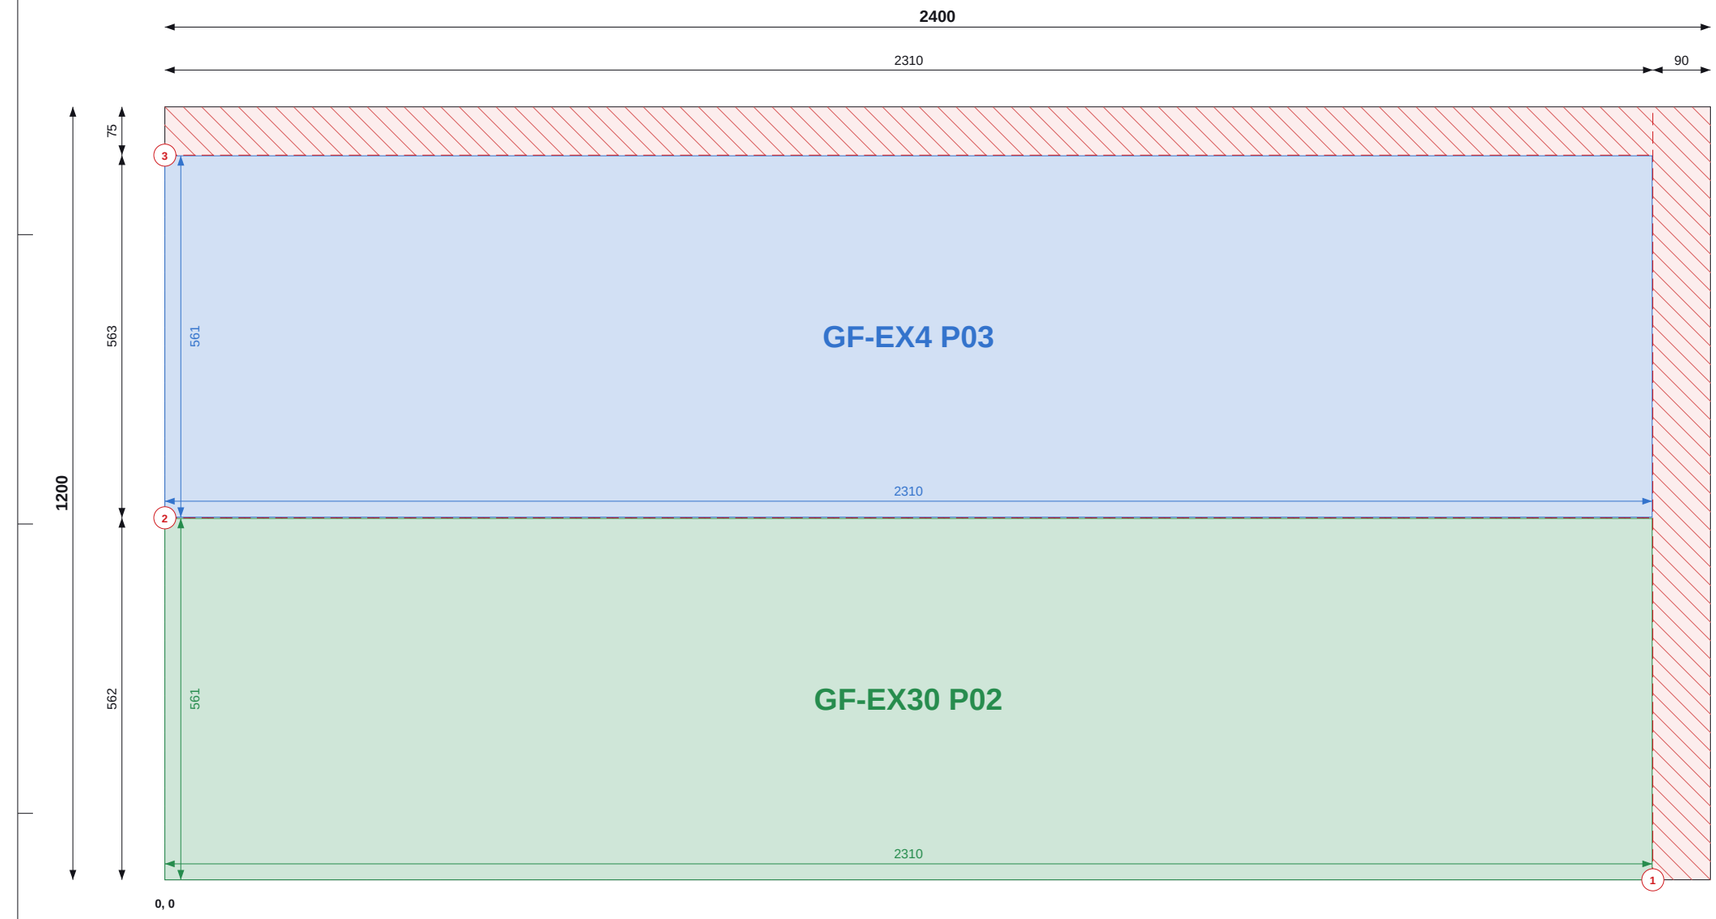

Top / left chains = saw cut positions (to cut centres). Coloured = part size and position.

Do not scale. All dimensions in mm. Check all dimensions on site.

SHEET 11 OF 33

THIS SHEET

Item	Value
Parts	2
Used / waste	90.0% / 0.29 m2
Reusable offcuts	0
Saw cuts / shared	3 / 1

PIECES (POSITION = BOTTOM-LEFT CORNER)

Label	Size	X, Y
GF-EX4 P03	561 x 2310	0, 563
GF-EX30 P02	561 x 2310	0, 0

NOTES

1. Cut from PIR 120mm 1200x2400, 2mm saw kerf. Viewed on the face; dimensions from the sheet's bottom-left corner (0,0). Red numbered lines = saw cuts in order, each edge to edge.
2. Coloured dimensions belong to the part of that colour: its width and height, and its position from the sheet edges. Raked parts: corner coordinates at each corner.
3. Red hatch = waste. Labels = panel + piece mark on the manufacture drawing.

REVISIONS

REV	DATE	DESCRIPTION
C01	14.09.26	Construction issue
C02	14.09.26	Roof trusses revised; SP diagonals added
C03	11.10.26	FF windows coursed; steel + GP1 portal; steel drawings (ST)
C04	13.10.26	Steel approved by the engineer: steel + steel timber drawings issued for construction

TLS TIMBER FRAME
Design & Manufacture
Scan: 3D model + drawings

CLIENT	PROJECT
MP Adams	MP Adams Plot 4, Eckington


DRAWING TITLE

PIR CUTTING - GROUND FLOOR - SHEET 11 OF 33

PIR 120mm 1200x2400 | Ground Floor

SCALE	SIZE	DATE	DRAWN
NTS	A3	13.10.26	TS

STATUS	DRAWING No.	REV
CONSTRUCTION	P4-CP-PIR-01 / 11	C04

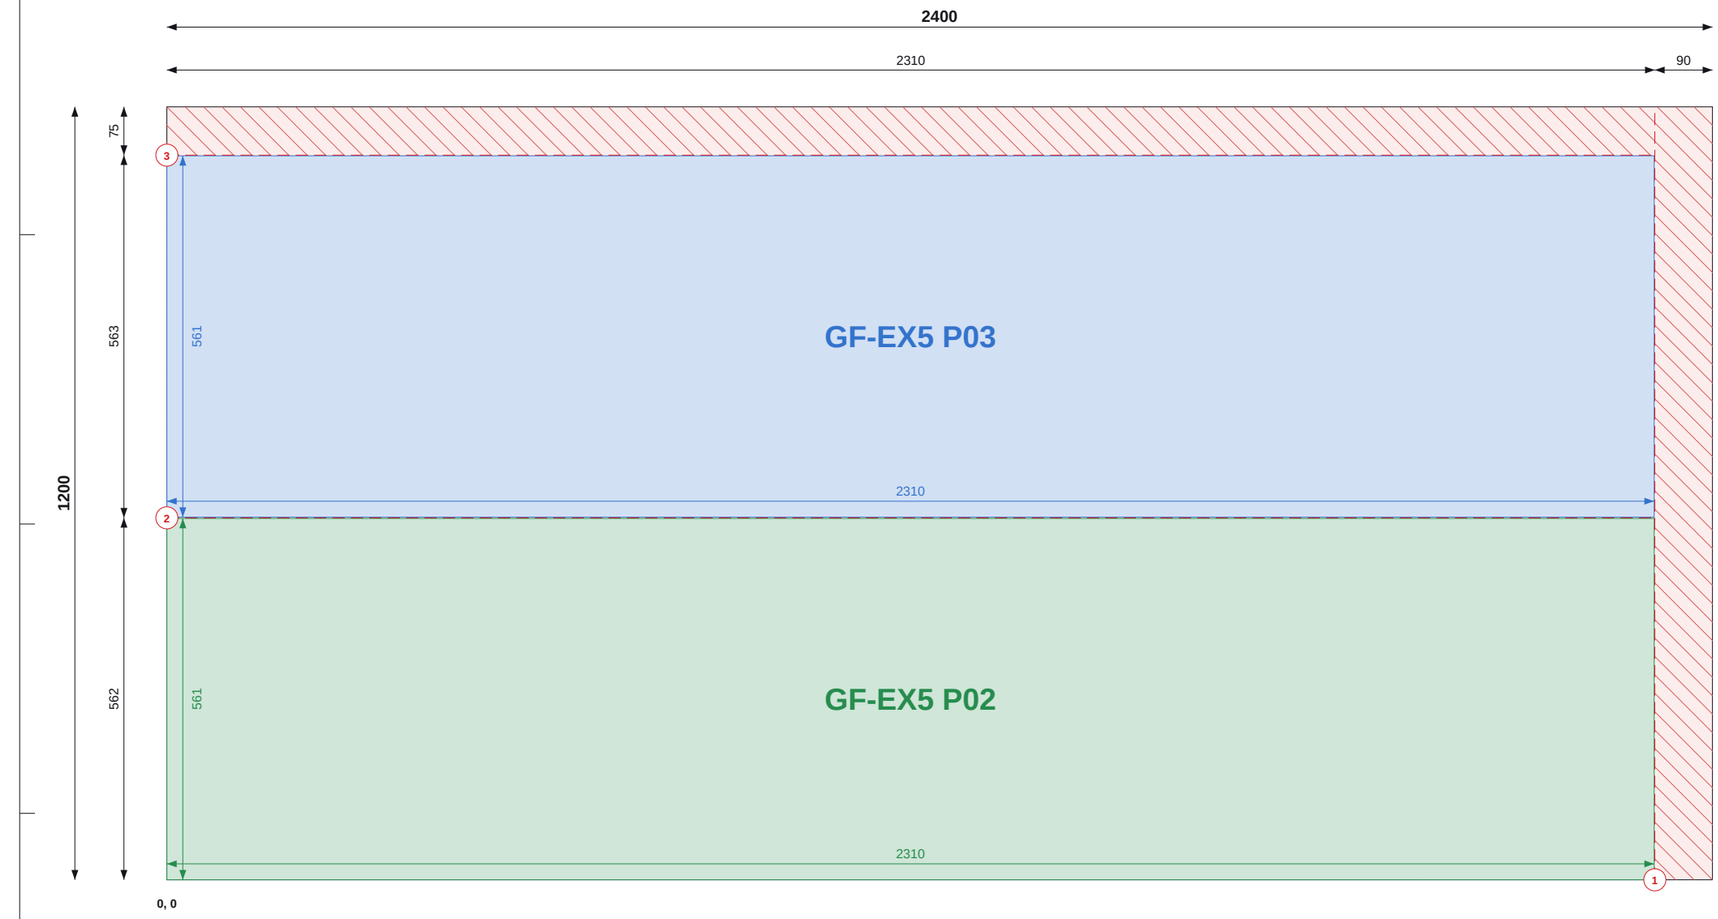

Top / left chains = saw cut positions (to cut centres). Coloured = part size and position.

Do not scale. All dimensions in mm. Check all dimensions on site.

SHEET 12 OF 33

THIS SHEET

Item	Value
Parts	2
Used / waste	90.0% / 0.29 m2
Reusable offcuts	0
Saw cuts / shared	3 / 1

PIECES (POSITION = BOTTOM-LEFT CORNER)

Label	Size	X, Y
GF-EX5 P03	561 x 2310	0, 563
GF-EX5 P02	561 x 2310	0, 0

NOTES

1. Cut from PIR 120mm 1200x2400, 2mm saw kerf. Viewed on the face; dimensions from the sheet's bottom-left corner (0,0). Red numbered lines = saw cuts in order, each edge to edge.
2. Coloured dimensions belong to the part of that colour: its width and height, and its position from the sheet edges. Raked parts: corner coordinates at each corner.
3. Red hatch = waste. Labels = panel + piece mark on the manufacture drawing.

REVISIONS

REV	DATE	DESCRIPTION
C01	14.09.26	Construction issue
C02	14.09.26	Roof trusses revised; SP diagonals added
C03	11.10.26	FF windows coursed; steel + GP1 portal; steel drawings (ST)
C04	13.10.26	Steel approved by the engineer: steel + steel timber drawings issued for construction

TLS TIMBER FRAME
Design & Manufacture
Scan: 3D model + drawings

CLIENT	PROJECT
MP Adams	MP Adams Plot 4, Eckington


DRAWING TITLE

PIR CUTTING - GROUND FLOOR - SHEET 12 OF 33

PIR 120mm 1200x2400 | Ground Floor

SCALE	SIZE	DATE	DRAWN
NTS	A3	13.10.26	TS

STATUS	DRAWING No.	REV
CONSTRUCTION	P4-CP-PIR-01 / 12	C04

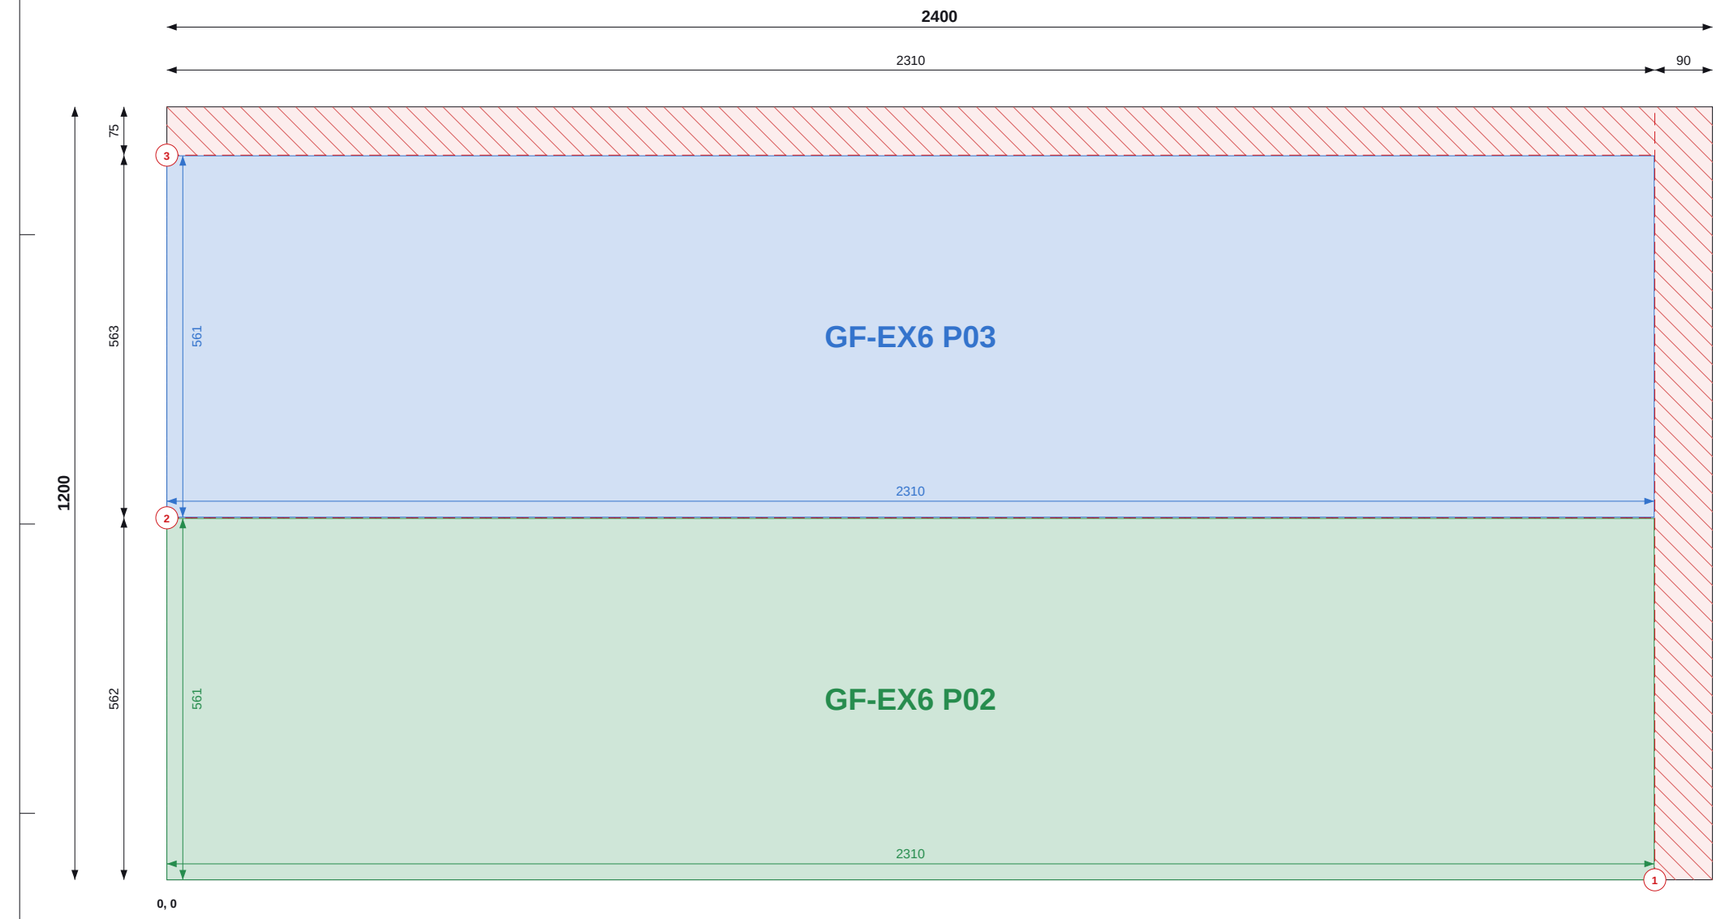

Top / left chains = saw cut positions (to cut centres). Coloured = part size and position.

SHEET 13 OF 33

THIS SHEET

Item	Value
Parts	2
Used / waste	90.0% / 0.29 m2
Reusable offcuts	0
Saw cuts / shared	3 / 1

PIECES (POSITION = BOTTOM-LEFT CORNER)

Label	Size	X, Y
GF-EX6 P03	561 x 2310	0, 563
GF-EX6 P02	561 x 2310	0, 0

NOTES

1. Cut from PIR 120mm 1200x2400, 2mm saw kerf. Viewed on the face; dimensions from the sheet's bottom-left corner (0,0). Red numbered lines = saw cuts in order, each edge to edge.
2. Coloured dimensions belong to the part of that colour: its width and height, and its position from the sheet edges. Raked parts: corner coordinates at each corner.
3. Red hatch = waste. Labels = panel + piece mark on the manufacture drawing.

REVISIONS

REV	DATE	DESCRIPTION
C01	14.09.26	Construction issue
C02	14.09.26	Roof trusses revised; SP diagonals added
C03	11.10.26	FF windows coursed; steel + GP1 portal; steel drawings (ST)
C04	13.10.26	Steel approved by the engineer: steel + steel timber drawings issued for construction

TLS TIMBER FRAME
Design & Manufacture
Scan: 3D model + drawings

CLIENT	PROJECT
MP Adams	MP Adams Plot 4, Eckington

DRAWING TITLE


PIR CUTTING - GROUND FLOOR - SHEET 13 OF 33

PIR 120mm 1200x2400 | Ground Floor

SCALE	SIZE	DATE	DRAWN
NTS	A3	13.10.26	TS

STATUS	DRAWING No.	REV
CONSTRUCTION	P4-CP-PIR-01 / 13	C04

Do not scale. All dimensions in mm. Check all dimensions on site.

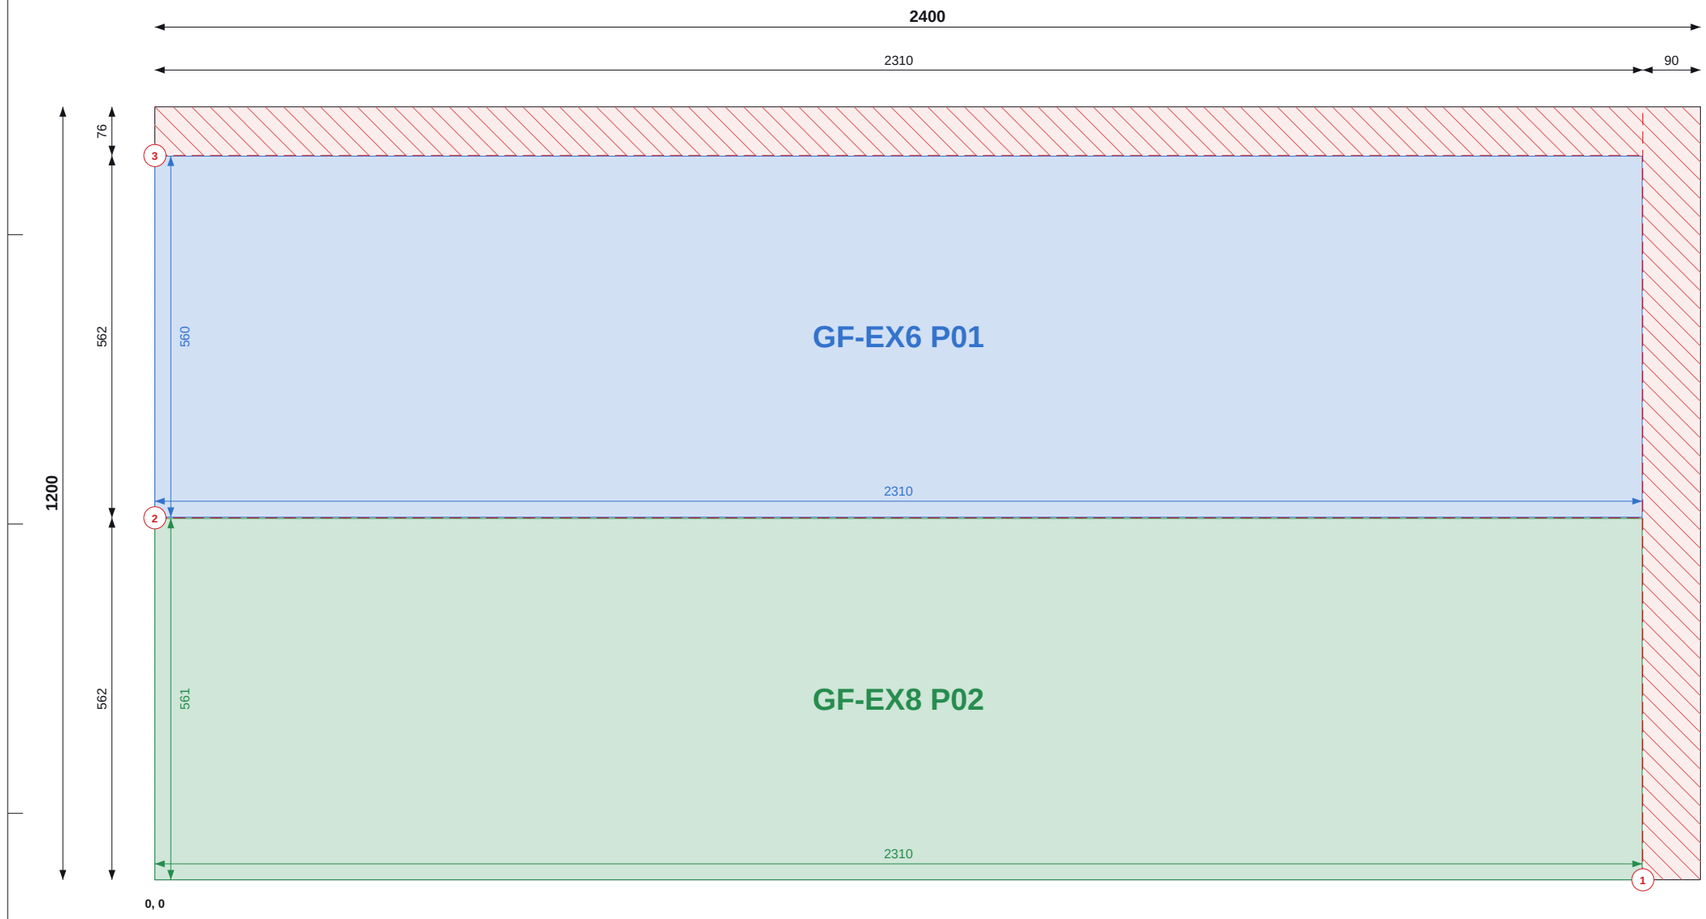

Top / left chains = saw cut positions (to cut centres). Coloured = part size and position.

SHEET 14 OF 33

THIS SHEET

Item	Value
Parts	2
Used / waste	89.9% / 0.29 m2
Reusable offcuts	0
Saw cuts / shared	3 / 1

PIECES (POSITION = BOTTOM-LEFT CORNER)

Label	Size	X, Y
GF-EX6 P01	560 x 2310	0, 563
GF-EX8 P02	561 x 2310	0, 0

NOTES

1. Cut from PIR 120mm 1200x2400, 2mm saw kerf. Viewed on the face; dimensions from the sheet's bottom-left corner (0,0). Red numbered lines = saw cuts in order, each edge to edge.
2. Coloured dimensions belong to the part of that colour: its width and height, and its position from the sheet edges. Raked parts: corner coordinates at each corner.
3. Red hatch = waste. Labels = panel + piece mark on the manufacture drawing.

REVISIONS

REV	DATE	DESCRIPTION
C01	14.09.26	Construction issue
C02	14.09.26	Roof trusses revised; SP diagonals added
C03	11.10.26	FF windows coursed; steel + GP1 portal; steel drawings (ST)
C04	13.10.26	Steel approved by the engineer: steel + steel timber drawings issued for construction

TLS TIMBER FRAME
Design & Manufacture
Scan: 3D model + drawings

CLIENT	PROJECT
MP Adams	MP Adams Plot 4, Eckington

DRAWING TITLE


PIR CUTTING - GROUND FLOOR - SHEET 14 OF 33

PIR 120mm 1200x2400 | Ground Floor

SCALE	SIZE	DATE	DRAWN
NTS	A3	13.10.26	TS

STATUS	DRAWING No.	REV
CONSTRUCTION	P4-CP-PIR-01 / 14	C04

Do not scale. All dimensions in mm. Check all dimensions on site.

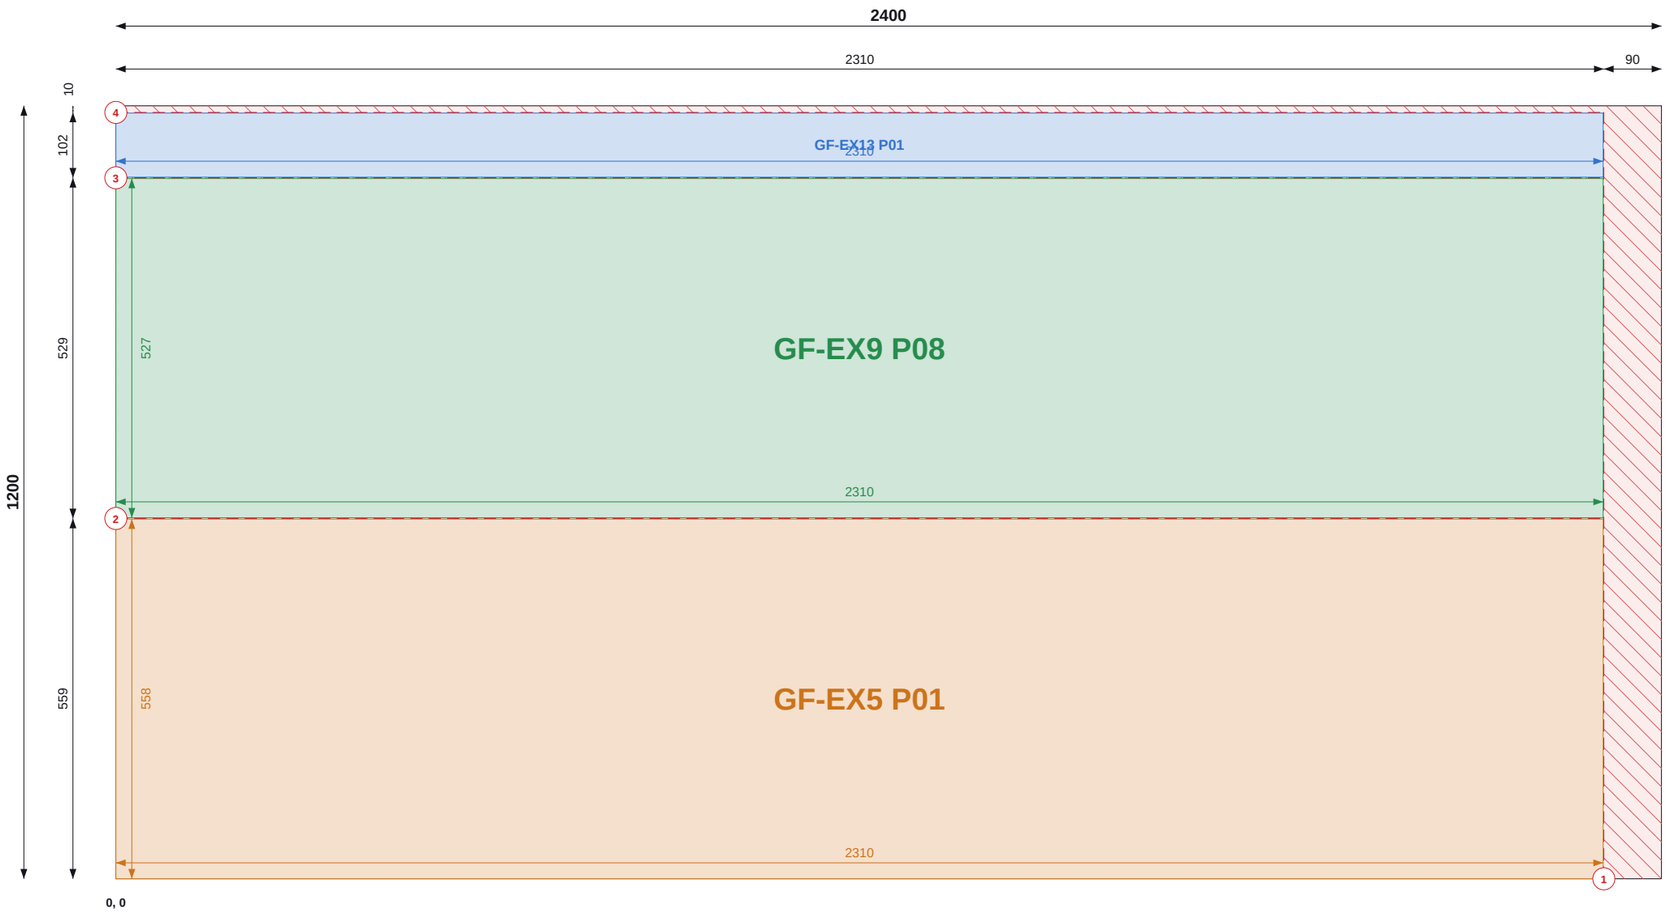

Top / left chains = saw cut positions (to cut centres). Coloured = part size and position.

SHEET 15 OF 33

THIS SHEET

Item	Value
Parts	3
Used / waste	95.0% / 0.14 m2
Reusable offcuts	0
Saw cuts / shared	4 / 2

PIECES (POSITION = BOTTOM-LEFT CORNER)

Label	Size	X, Y
GF-EX13 P01	99 x 2310	0, 1089
GF-EX9 P08	527 x 2310	0, 560
GF-EX5 P01	558 x 2310	0, 0

NOTES

1. Cut from PIR 120mm 1200x2400, 2mm saw kerf. Viewed on the face; dimensions from the sheet's bottom-left corner (0,0). Red numbered lines = saw cuts in order, each edge to edge.
2. Coloured dimensions belong to the part of that colour: its width and height, and its position from the sheet edges. Raked parts: corner coordinates at each corner.
3. Red hatch = waste. Labels = panel + piece mark on the manufacture drawing.

REVISIONS

REV	DATE	DESCRIPTION
C01	14.09.26	Construction issue
C02	14.09.26	Roof trusses revised; SP diagonals added
C03	11.10.26	FF windows coursed; steel + GP1 portal; steel drawings (ST)
C04	13.10.26	Steel approved by the engineer: steel + steel timber drawings issued for construction

TLS TIMBER FRAME DESIGN SUITE

TLS TIMBER FRAME

Design & Manufacture

Scan: 3D model + drawings

CLIENT	PROJECT
MP Adams	MP Adams Plot 4, Eckington

DRAWING TITLE


PIR CUTTING - GROUND FLOOR - SHEET 15 OF 33

PIR 120mm 1200x2400 | Ground Floor

SCALE	SIZE	DATE	DRAWN
NTS	A3	13.10.26	TS

STATUS	DRAWING No.	REV
CONSTRUCTION	P4-CP-PIR-01 / 15	C04

Do not scale. All dimensions in mm. Check all dimensions on site.

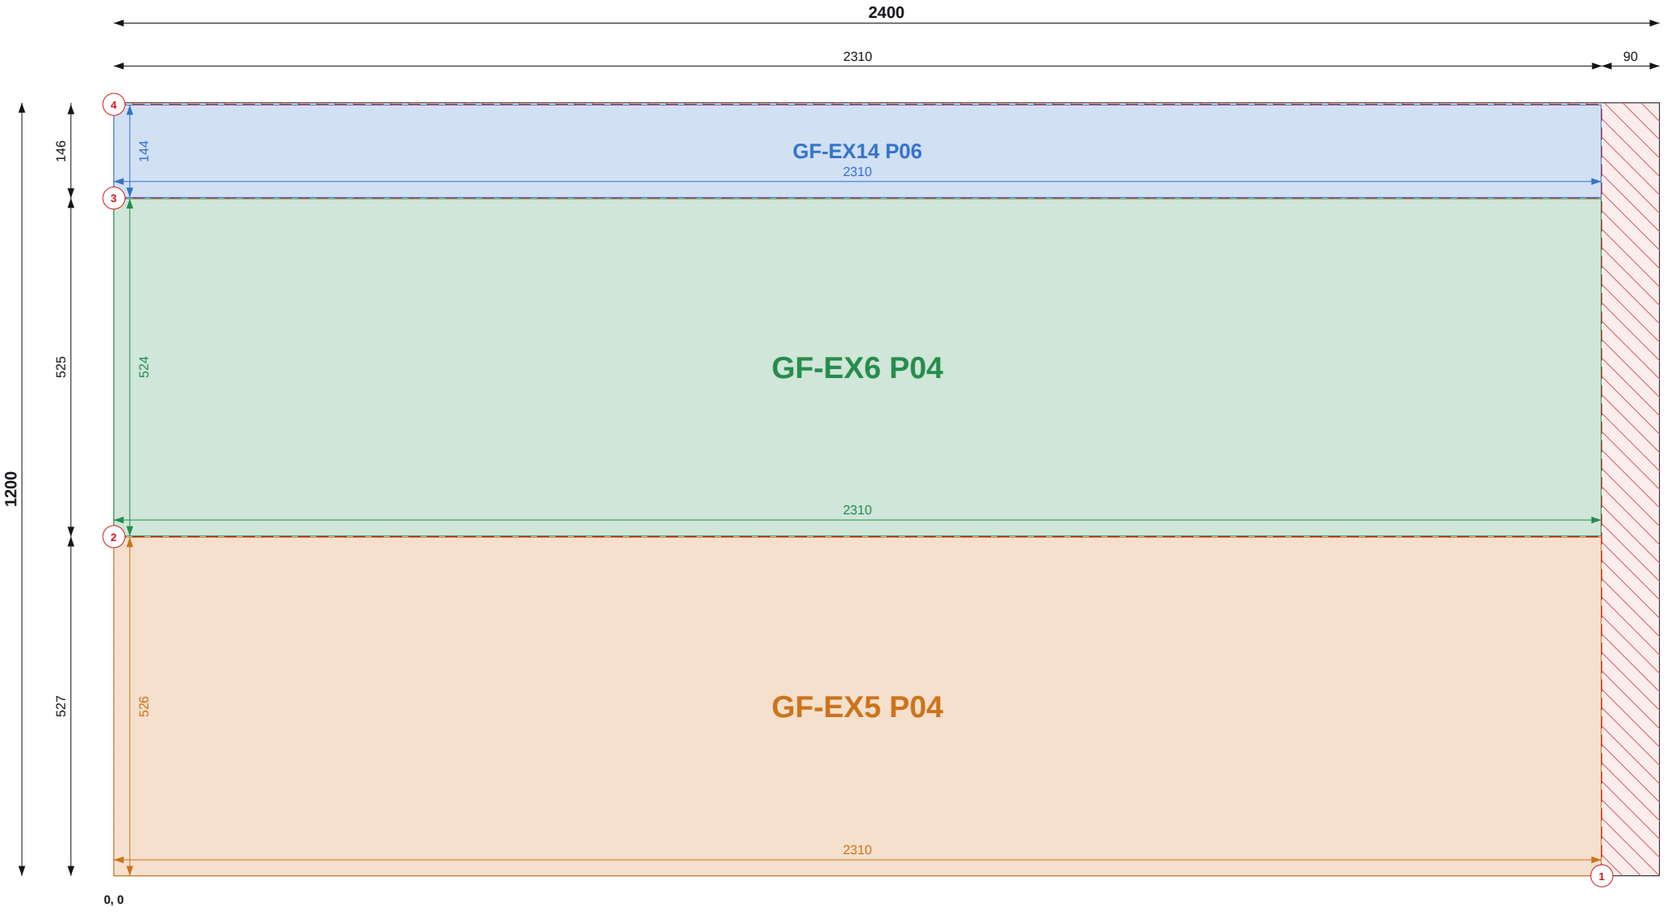

Top / left chains = saw cut positions (to cut centres). Coloured = part size and position.

SHEET 16 OF 33

THIS SHEET

Item	Value
Parts	3
Used / waste	95.6% / 0.13 m2
Reusable offcuts	0
Saw cuts / shared	4 / 2

PIECES (POSITION = BOTTOM-LEFT CORNER)

Label	Size	X, Y
GF-EX14 P06	144 x 2310	0, 1053
GF-EX6 P04	524 x 2310	0, 528
GF-EX5 P04	526 x 2310	0, 0

NOTES

1. Cut from PIR 120mm 1200x2400, 2mm saw kerf. Viewed on the face; dimensions from the sheet's bottom-left corner (0,0). Red numbered lines = saw cuts in order, each edge to edge.
2. Coloured dimensions belong to the part of that colour: its width and height, and its position from the sheet edges. Raked parts: corner coordinates at each corner.
3. Red hatch = waste. Labels = panel + piece mark on the manufacture drawing.

REVISIONS

REV	DATE	DESCRIPTION
C01	14.09.26	Construction issue
C02	14.09.26	Roof trusses revised; SP diagonals added
C03	11.10.26	FF windows coursed; steel + GP1 portal; steel drawings (ST)
C04	13.10.26	Steel approved by the engineer: steel + steel timber drawings issued for constructio

TLS TIMBER FRAME
Design & Manufacture
Scan: 3D model + drawings

CLIENT	PROJECT
MP Adams	MP Adams Plot 4, Eckington

DRAWING TITLE


PIR CUTTING - GROUND FLOOR - SHEET 16 OF 33

PIR 120mm 1200x2400 | Ground Floor

SCALE	SIZE	DATE	DRAWN
NTS	A3	13.10.26	TS

STATUS	DRAWING No.	REV
CONSTRUCTION	P4-CP-PIR-01 / 16	C04

Do not scale. All dimensions in mm. Check all dimensions on site.

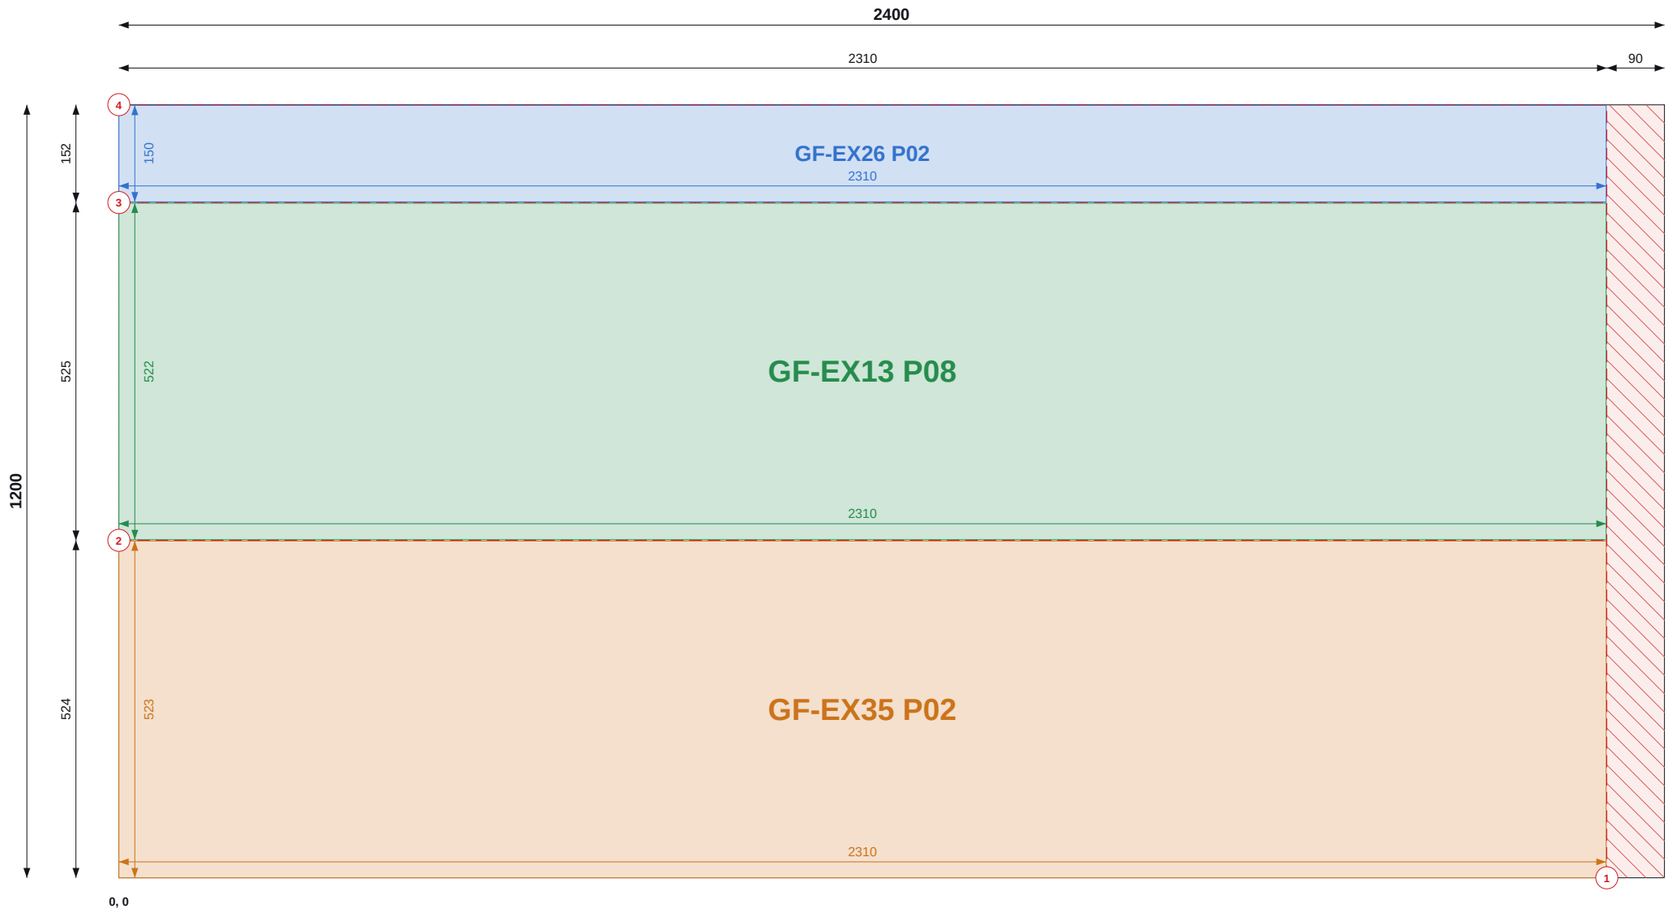

Top / left chains = saw cut positions (to cut centres). Coloured = part size and position.

SHEET 17 OF 33

THIS SHEET

Item	Value
Parts	3
Used / waste	95.9% / 0.12 m2
Reusable offcuts	0
Saw cuts / shared	4 / 2

PIECES (POSITION = BOTTOM-LEFT CORNER)

Label	Size	X, Y
GF-EX26 P02	150 x 2310	0, 1049
GF-EX13 P08	522 x 2310	0, 525
GF-EX35 P02	523 x 2310	0, 0

NOTES

1. Cut from PIR 120mm 1200x2400, 2mm saw kerf. Viewed on the face; dimensions from the sheet's bottom-left corner (0,0). Red numbered lines = saw cuts in order, each edge to edge.
2. Coloured dimensions belong to the part of that colour: its width and height, and its position from the sheet edges. Raked parts: corner coordinates at each corner.
3. Red hatch = waste. Labels = panel + piece mark on the manufacture drawing.

REVISIONS

REV	DATE	DESCRIPTION
C01	14.09.26	Construction issue
C02	14.09.26	Roof trusses revised; SP diagonals added
C03	11.10.26	FF windows coursed; steel + GP1 portal; steel drawings (ST)
C04	13.10.26	Steel approved by the engineer: steel + steel timber drawings issued for construction

TLS TIMBER FRAME
Design & Manufacture
Scan: 3D model + drawings

CLIENT	PROJECT
MP Adams	MP Adams Plot 4, Eckington

DRAWING TITLE


PIR CUTTING - GROUND FLOOR - SHEET 17 OF 33

PIR 120mm 1200x2400 | Ground Floor

SCALE	SIZE	DATE	DRAWN
NTS	A3	13.10.26	TS

STATUS	DRAWING No.	REV
CONSTRUCTION	P4-CP-PIR-01 / 17	C04

Do not scale. All dimensions in mm. Check all dimensions on site.

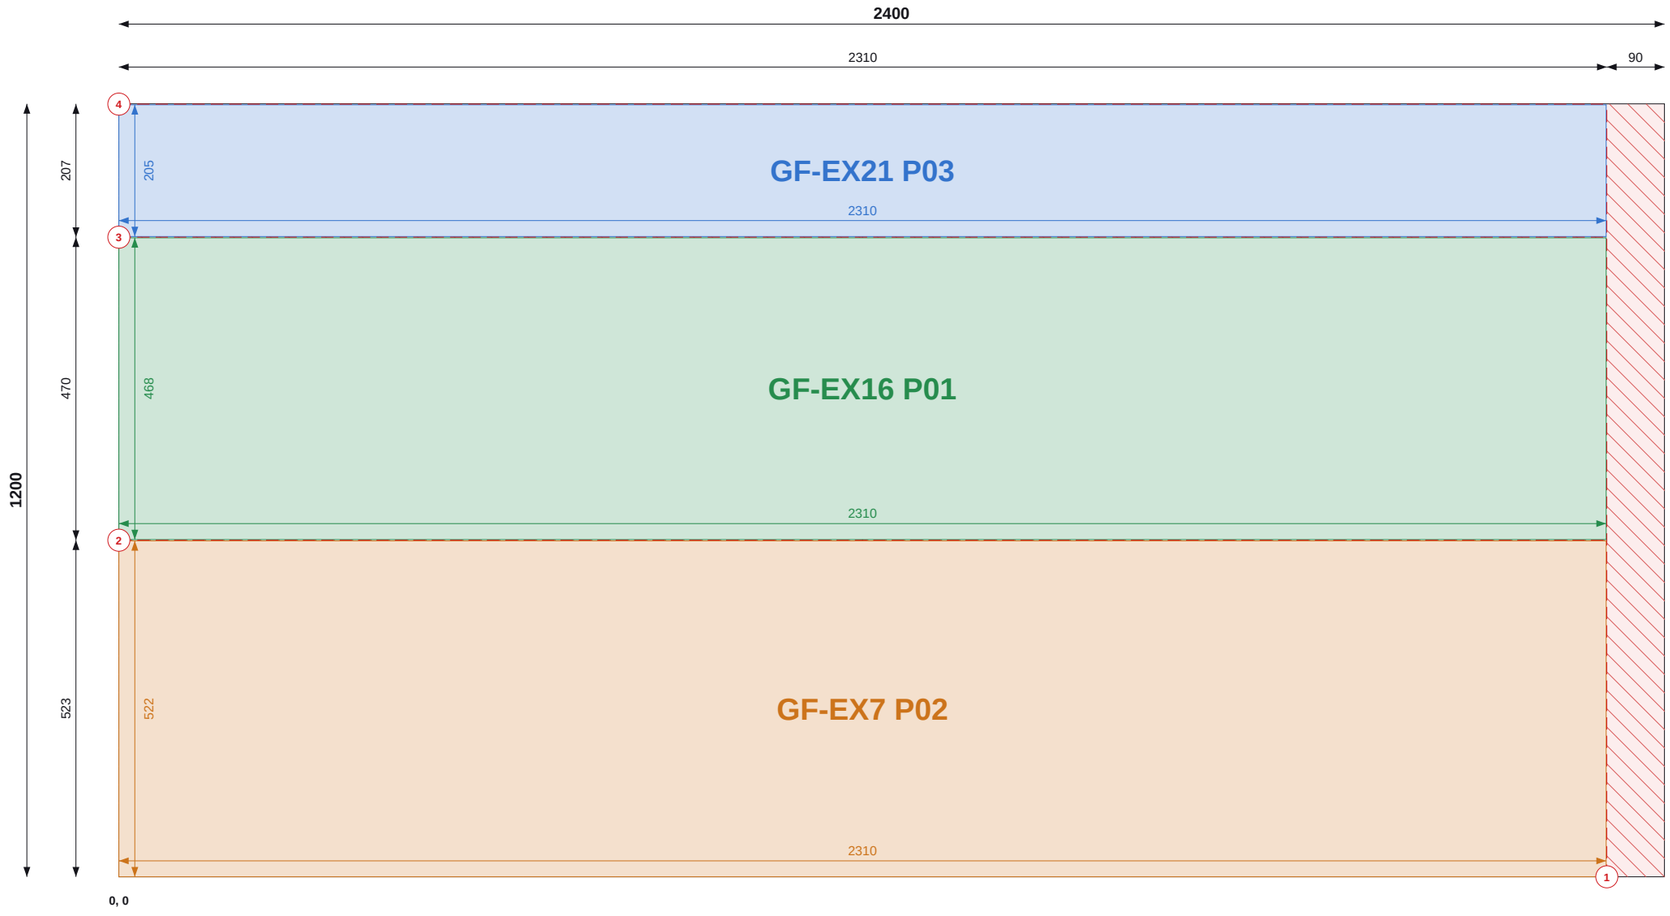

Top / left chains = saw cut positions (to cut centres). Coloured = part size and position.

Do not scale. All dimensions in mm. Check all dimensions on site.

SHEET 18 OF 33

THIS SHEET

Item	Value
Parts	3
Used / waste	95.8% / 0.12 m2
Reusable offcuts	0
Saw cuts / shared	4 / 2

PIECES (POSITION = BOTTOM-LEFT CORNER)

Label	Size	X, Y
GF-EX21 P03	205 x 2310	0, 994
GF-EX16 P01	468 x 2310	0, 524
GF-EX7 P02	522 x 2310	0, 0

NOTES

1. Cut from PIR 120mm 1200x2400, 2mm saw kerf. Viewed on the face; dimensions from the sheet's bottom-left corner (0,0). Red numbered lines = saw cuts in order, each edge to edge.
2. Coloured dimensions belong to the part of that colour: its width and height, and its position from the sheet edges. Raked parts: corner coordinates at each corner.
3. Red hatch = waste. Labels = panel + piece mark on the manufacture drawing.

REVISIONS

REV	DATE	DESCRIPTION
C01	14.09.26	Construction issue
C02	14.09.26	Roof trusses revised; SP diagonals added
C03	11.10.26	FF windows coursed; steel + GP1 portal; steel drawings (ST)
C04	13.10.26	Steel approved by the engineer: steel + steel timber drawings issued for constructio

TLS TIMBER FRAME
Design & Manufacture
Scan: 3D model + drawings

CLIENT	PROJECT
MP Adams	MP Adams Plot 4, Eckington


DRAWING TITLE

PIR CUTTING - GROUND FLOOR - SHEET 18 OF 33

PIR 120mm 1200x2400 | Ground Floor

SCALE	SIZE	DATE	DRAWN
NTS	A3	13.10.26	TS

STATUS	DRAWING No.	REV
CONSTRUCTION	P4-CP-PIR-01 / 18	C04

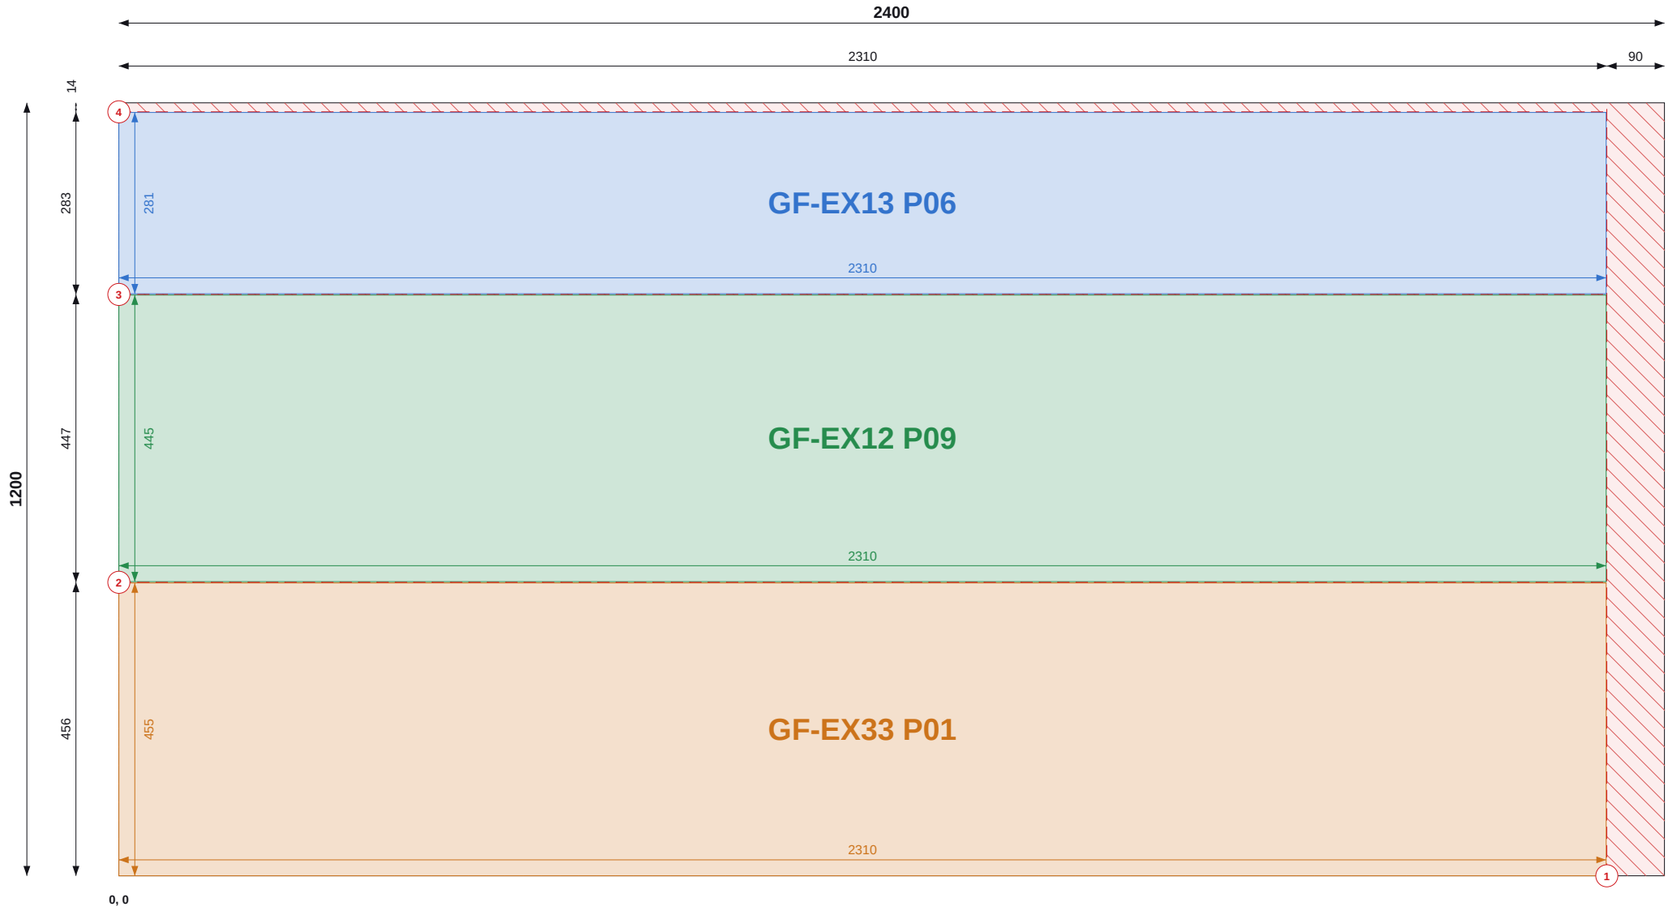

Top / left chains = saw cut positions (to cut centres). Coloured = part size and position.

Do not scale. All dimensions in mm. Check all dimensions on site.

SHEET 19 OF 33

THIS SHEET

Item	Value
Parts	3
Used / waste	94.7% / 0.15 m2
Reusable offcuts	0
Saw cuts / shared	4 / 2

PIECES (POSITION = BOTTOM-LEFT CORNER)

Label	Size	X, Y
GF-EX13 P06	281 x 2310	0, 904
GF-EX12 P09	445 x 2310	0, 457
GF-EX33 P01	455 x 2310	0, 0

NOTES

1. Cut from PIR 120mm 1200x2400, 2mm saw kerf. Viewed on the face; dimensions from the sheet's bottom-left corner (0,0). Red numbered lines = saw cuts in order, each edge to edge.
2. Coloured dimensions belong to the part of that colour: its width and height, and its position from the sheet edges. Raked parts: corner coordinates at each corner.
3. Red hatch = waste. Labels = panel + piece mark on the manufacture drawing.

REVISIONS

REV	DATE	DESCRIPTION
C01	14.09.26	Construction issue
C02	14.09.26	Roof trusses revised; SP diagonals added
C03	11.10.26	FF windows coursed; steel + GP1 portal; steel drawings (ST)
C04	13.10.26	Steel approved by the engineer: steel + steel timber drawings issued for construction

TLS TIMBER FRAME
Design & Manufacture
Scan: 3D model + drawings

CLIENT	PROJECT
MP Adams	MP Adams Plot 4, Eckington


DRAWING TITLE

PIR CUTTING - GROUND FLOOR - SHEET 19 OF 33

PIR 120mm 1200x2400 | Ground Floor

SCALE	SIZE	DATE	DRAWN
NTS	A3	13.10.26	TS

STATUS	DRAWING No.	REV
CONSTRUCTION	P4-CP-PIR-01 / 19	C04

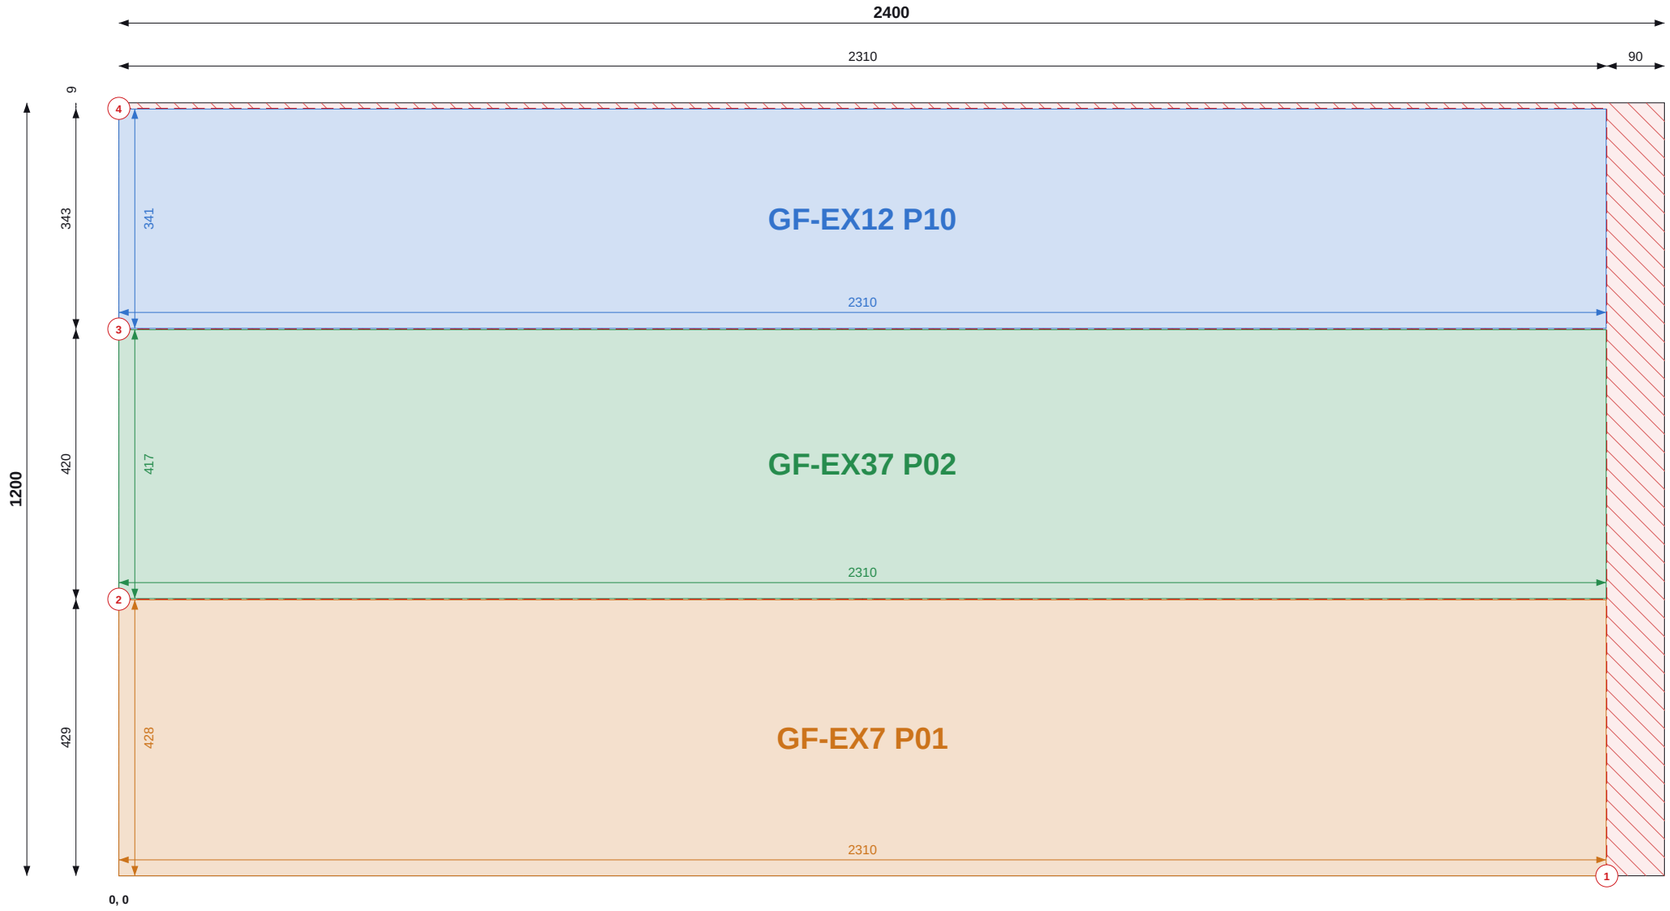

Top / left chains = saw cut positions (to cut centres). Coloured = part size and position.

Do not scale. All dimensions in mm. Check all dimensions on site.

SHEET 20 OF 33

THIS SHEET

Item	Value
Parts	3
Used / waste	95.1% / 0.14 m2
Reusable offcuts	0
Saw cuts / shared	4 / 2

PIECES (POSITION = BOTTOM-LEFT CORNER)

Label	Size	X, Y
GF-EX12 P10	341 x 2310	0, 850
GF-EX37 P02	417 x 2310	0, 430
GF-EX7 P01	428 x 2310	0, 0

NOTES

1. Cut from PIR 120mm 1200x2400, 2mm saw kerf. Viewed on the face; dimensions from the sheet's bottom-left corner (0,0). Red numbered lines = saw cuts in order, each edge to edge.
2. Coloured dimensions belong to the part of that colour: its width and height, and its position from the sheet edges. Raked parts: corner coordinates at each corner.
3. Red hatch = waste. Labels = panel + piece mark on the manufacture drawing.

REVISIONS

REV	DATE	DESCRIPTION
C01	14.09.26	Construction issue
C02	14.09.26	Roof trusses revised; SP diagonals added
C03	11.10.26	FF windows coursed; steel + GP1 portal; steel drawings (ST)
C04	13.10.26	Steel approved by the engineer: steel + steel timber drawings issued for construction

TLS TIMBER FRAME
Design & Manufacture
Scan: 3D model + drawings

CLIENT	PROJECT
MP Adams	MP Adams Plot 4, Eckington


DRAWING TITLE

PIR CUTTING - GROUND FLOOR - SHEET 20 OF 33

PIR 120mm 1200x2400 | Ground Floor

SCALE	SIZE	DATE	DRAWN
NTS	A3	13.10.26	TS

STATUS	DRAWING No.	REV
CONSTRUCTION	P4-CP-PIR-01 / 20	C04

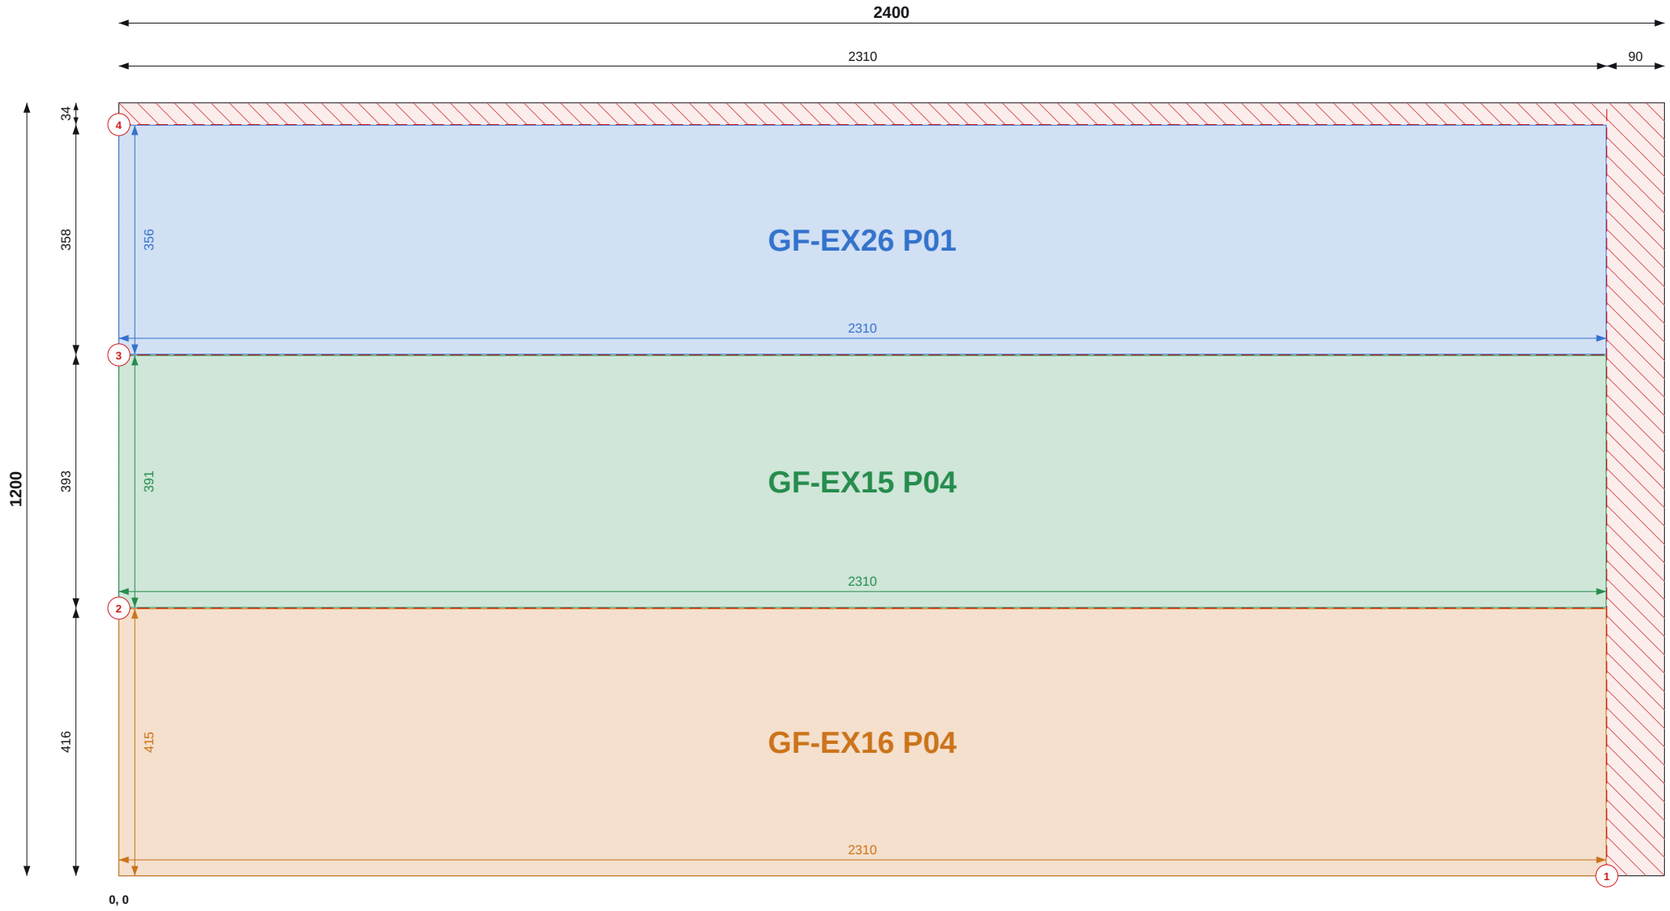

Top / left chains = saw cut positions (to cut centres). Coloured = part size and position.

SHEET 21 OF 33

THIS SHEET

Item	Value
Parts	3
Used / waste	93.1% / 0.20 m2
Reusable offcuts	0
Saw cuts / shared	4 / 2

PIECES (POSITION = BOTTOM-LEFT CORNER)

Label	Size	X, Y
GF-EX26 P01	356 x 2310	0, 810
GF-EX15 P04	391 x 2310	0, 417
GF-EX16 P04	415 x 2310	0, 0

NOTES

1. Cut from PIR 120mm 1200x2400, 2mm saw kerf. Viewed on the face; dimensions from the sheet's bottom-left corner (0,0). Red numbered lines = saw cuts in order, each edge to edge.
2. Coloured dimensions belong to the part of that colour: its width and height, and its position from the sheet edges. Raked parts: corner coordinates at each corner.
3. Red hatch = waste. Labels = panel + piece mark on the manufacture drawing.

REVISIONS

REV	DATE	DESCRIPTION
C01	14.09.26	Construction issue
C02	14.09.26	Roof trusses revised; SP diagonals added
C03	11.10.26	FF windows coursed; steel + GP1 portal; steel drawings (ST)
C04	13.10.26	Steel approved by the engineer: steel + steel timber drawings issued for construction

TLS TIMBER FRAME
Design & Manufacture
Scan: 3D model + drawings

CLIENT	PROJECT
MP Adams	MP Adams Plot 4, Eckington

DRAWING TITLE


PIR CUTTING - GROUND FLOOR - SHEET 21 OF 33

PIR 120mm 1200x2400 | Ground Floor

SCALE	SIZE	DATE	DRAWN
NTS	A3	13.10.26	TS

STATUS	DRAWING No.	REV
CONSTRUCTION	P4-CP-PIR-01 / 21	C04

Do not scale. All dimensions in mm. Check all dimensions on site.

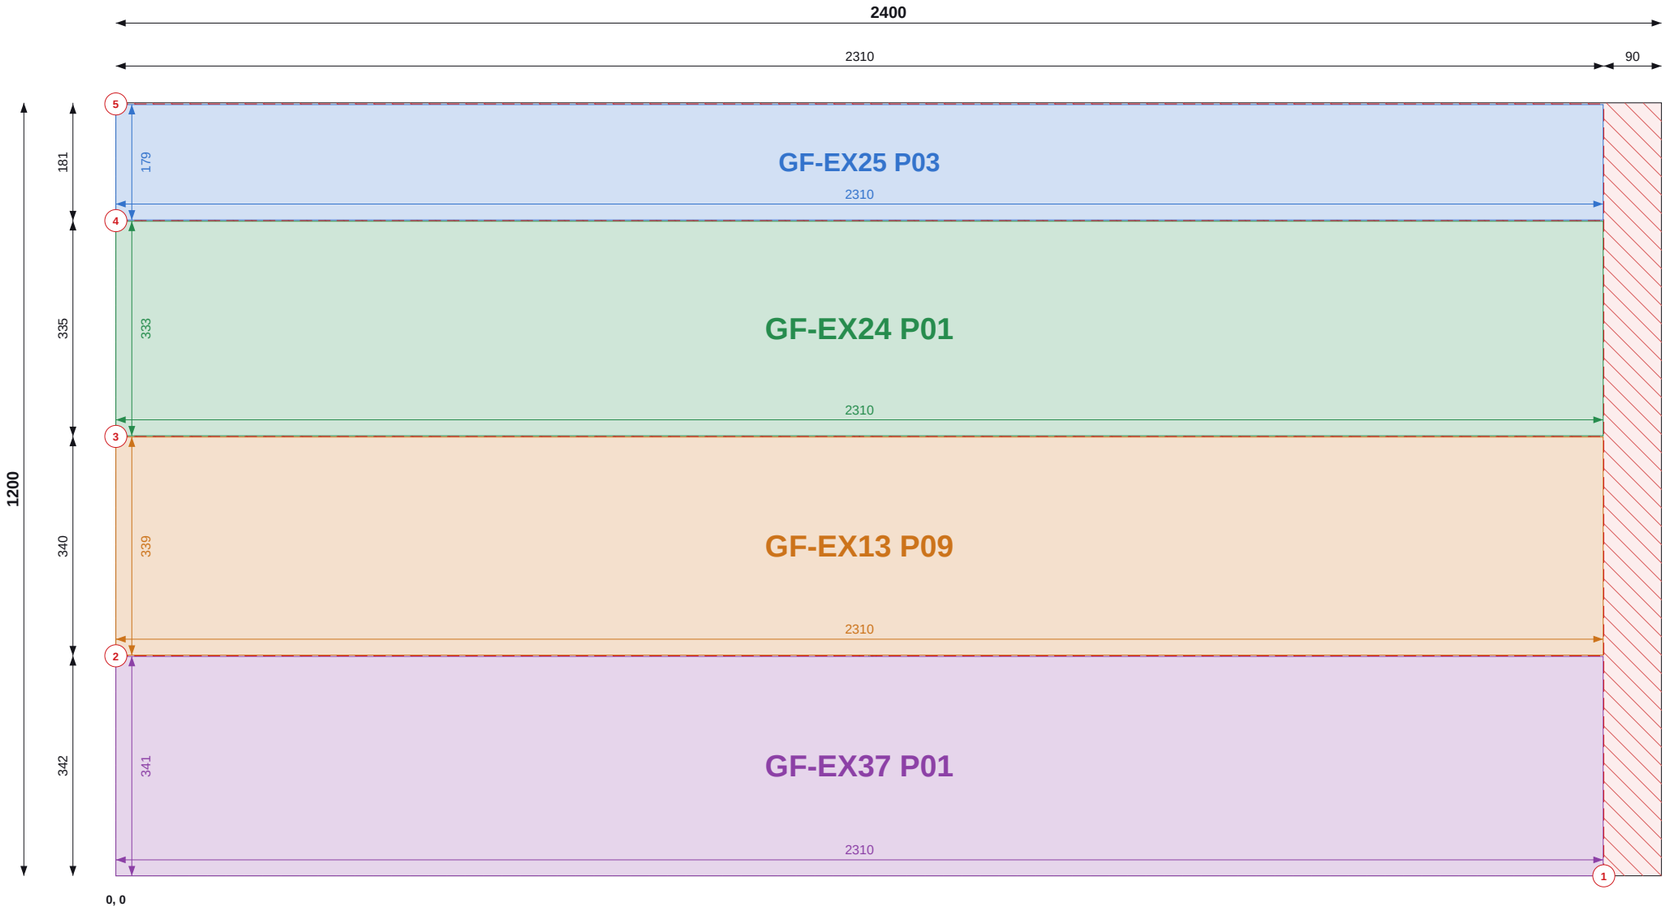

Top / left chains = saw cut positions (to cut centres). Coloured = part size and position.

SHEET 22 OF 33

THIS SHEET

Item	Value
Parts	4
Used / waste	95.5% / 0.13 m2
Reusable offcuts	0
Saw cuts / shared	5 / 3

PIECES (POSITION = BOTTOM-LEFT CORNER)

Label	Size	X, Y
GF-EX25 P03	179 x 2310	0, 1018
GF-EX24 P01	333 x 2310	0, 683
GF-EX13 P09	339 x 2310	0, 343
GF-EX37 P01	341 x 2310	0, 0

NOTES

1. Cut from PIR 120mm 1200x2400, 2mm saw kerf. Viewed on the face; dimensions from the sheet's bottom-left corner (0,0). Red numbered lines = saw cuts in order, each edge to edge.
2. Coloured dimensions belong to the part of that colour: its width and height, and its position from the sheet edges. Raked parts: corner coordinates at each corner.
3. Red hatch = waste. Labels = panel + piece mark on the manufacture drawing.

REVISIONS

REV	DATE	DESCRIPTION
C01	14.09.26	Construction issue
C02	14.09.26	Roof trusses revised; SP diagonals added
C03	11.10.26	FF windows coursed; steel + GP1 portal; steel drawings (ST)
C04	13.10.26	Steel approved by the engineer: steel + steel timber drawings issued for construction

TLS TIMBER FRAME
Design & Manufacture
Scan: 3D model + drawings

CLIENT	PROJECT
MP Adams	MP Adams Plot 4, Eckington


DRAWING TITLE
PIR CUTTING - GROUND FLOOR - SHEET 22 OF 33

PIR 120mm 1200x2400 | Ground Floor

SCALE	SIZE	DATE	DRAWN
NTS	A3	13.10.26	TS

STATUS	DRAWING No.	REV
CONSTRUCTION	P4-CP-PIR-01 / 22	C04

Do not scale. All dimensions in mm. Check all dimensions on site.

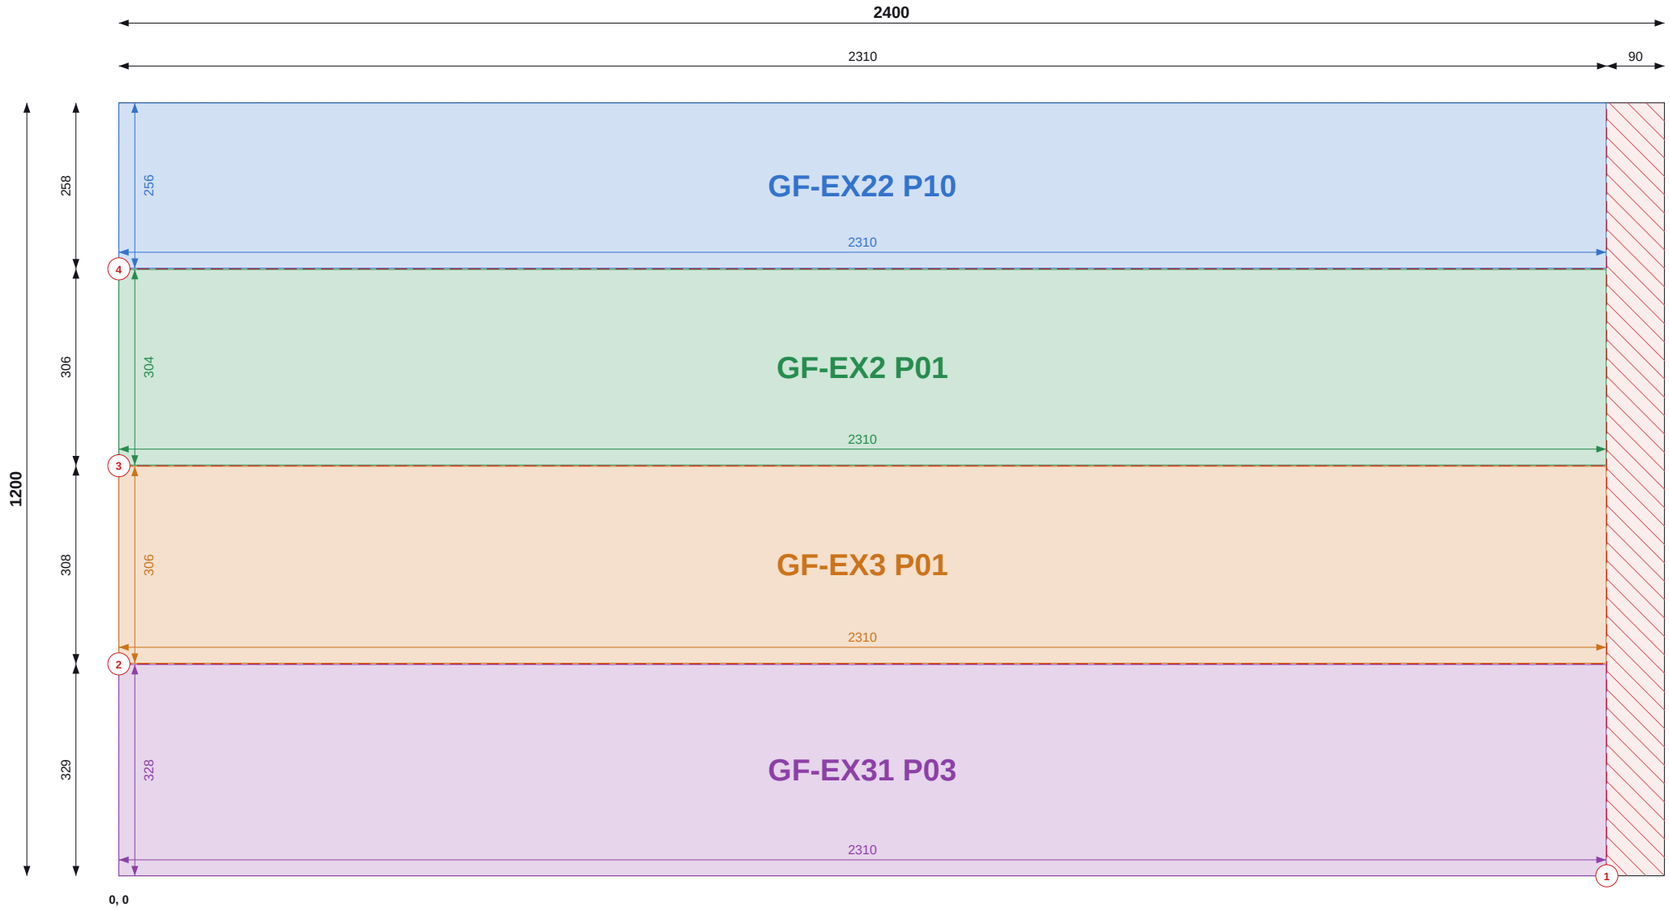

Top / left chains = saw cut positions (to cut centres). Coloured = part size and position.

SHEET 23 OF 33

THIS SHEET

Item	Value
Parts	4
Used / waste	95.7% / 0.12 m2
Reusable offcuts	0
Saw cuts / shared	4 / 3

PIECES (POSITION = BOTTOM-LEFT CORNER)

Label	Size	X, Y
GF-EX22 P10	256 x 2310	0, 943
GF-EX2 P01	304 x 2310	0, 638
GF-EX3 P01	306 x 2310	0, 330
GF-EX31 P03	328 x 2310	0, 0

NOTES

1. Cut from PIR 120mm 1200x2400, 2mm saw kerf. Viewed on the face; dimensions from the sheet's bottom-left corner (0,0). Red numbered lines = saw cuts in order, each edge to edge.
2. Coloured dimensions belong to the part of that colour: its width and height, and its position from the sheet edges. Raked parts: corner coordinates at each corner.
3. Red hatch = waste. Labels = panel + piece mark on the manufacture drawing.

REVISIONS

REV	DATE	DESCRIPTION
C01	14.09.26	Construction issue
C02	14.09.26	Roof trusses revised; SP diagonals added
C03	11.10.26	FF windows coursed; steel + GP1 portal; steel drawings (ST)
C04	13.10.26	Steel approved by the engineer: steel + steel timber drawings issued for construction

TLS TIMBER FRAME
Design & Manufacture
Scan: 3D model + drawings

CLIENT	PROJECT
MP Adams	MP Adams Plot 4, Eckington

DRAWING TITLE


PIR CUTTING - GROUND FLOOR - SHEET 23 OF 33

PIR 120mm 1200x2400 | Ground Floor

SCALE	SIZE	DATE	DRAWN
NTS	A3	13.10.26	TS

STATUS	DRAWING No.	REV
CONSTRUCTION	P4-CP-PIR-01 / 23	C04

Do not scale. All dimensions in mm. Check all dimensions on site.

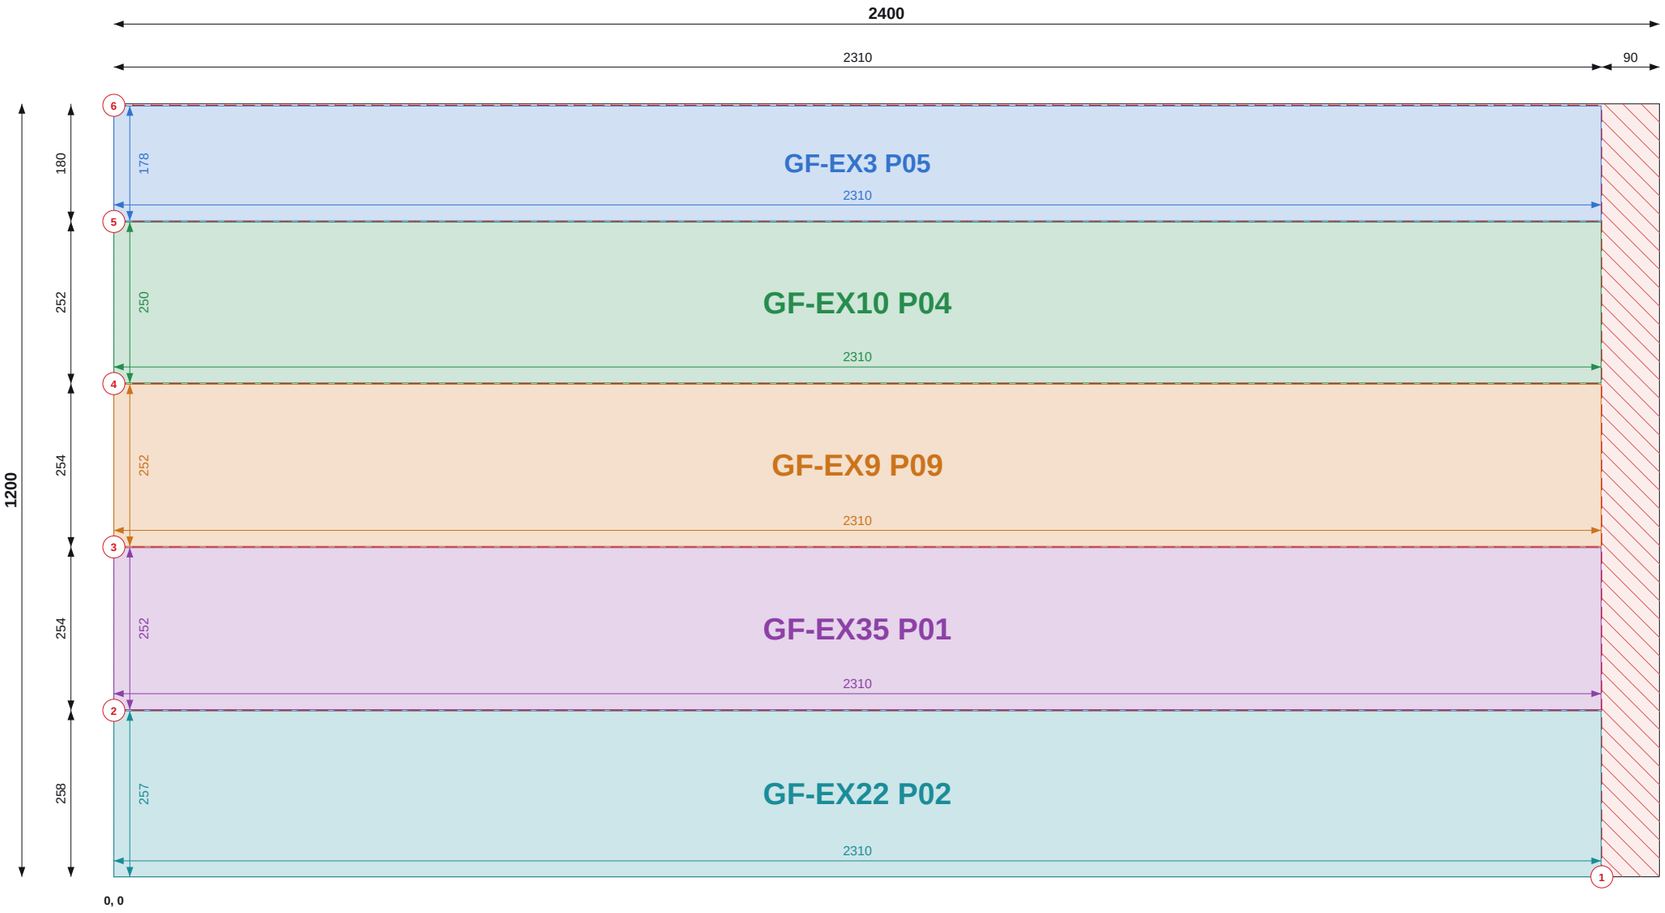

Top / left chains = saw cut positions (to cut centres). Coloured = part size and position.

Do not scale. All dimensions in mm. Check all dimensions on site.

SHEET 24 OF 33

THIS SHEET

Item	Value
Parts	5
Used / waste	95.3% / 0.13 m2
Reusable offcuts	0
Saw cuts / shared	6 / 4

PIECES (POSITION = BOTTOM-LEFT CORNER)

Label	Size	X, Y
GF-EX3 P05	178 x 2310	0, 1018
GF-EX10 P04	250 x 2310	0, 767
GF-EX9 P09	252 x 2310	0, 513
GF-EX35 P01	252 x 2310	0, 259
GF-EX22 P02	257 x 2310	0, 0

NOTES

1. Cut from PIR 120mm 1200x2400, 2mm saw kerf. Viewed on the face; dimensions from the sheet's bottom-left corner (0,0). Red numbered lines = saw cuts in order, each edge to edge.
2. Coloured dimensions belong to the part of that colour: its width and height, and its position from the sheet edges. Raked parts: corner coordinates at each corner.
3. Red hatch = waste. Labels = panel + piece mark on the manufacture drawing.

REVISIONS

REV	DATE	DESCRIPTION
C01	14.09.26	Construction issue
C02	14.09.26	Roof trusses revised; SP diagonals added
C03	11.10.26	FF windows coursed; steel + GP1 portal; steel drawings (ST)
C04	13.10.26	Steel approved by the engineer: steel + steel timber drawings issued for constructio

TLS TIMBER FRAME
Design & Manufacture
Scan: 3D model + drawings


CLIENT	PROJECT
MP Adams	MP Adams Plot 4, Eckington

DRAWING TITLE
PIR CUTTING - GROUND FLOOR - SHEET 24 OF 33

PIR 120mm 1200x2400 | Ground Floor

SCALE	SIZE	DATE	DRAWN
NTS	A3	13.10.26	TS

STATUS	DRAWING No.	REV
CONSTRUCTION	P4-CP-PIR-01 / 24	C04

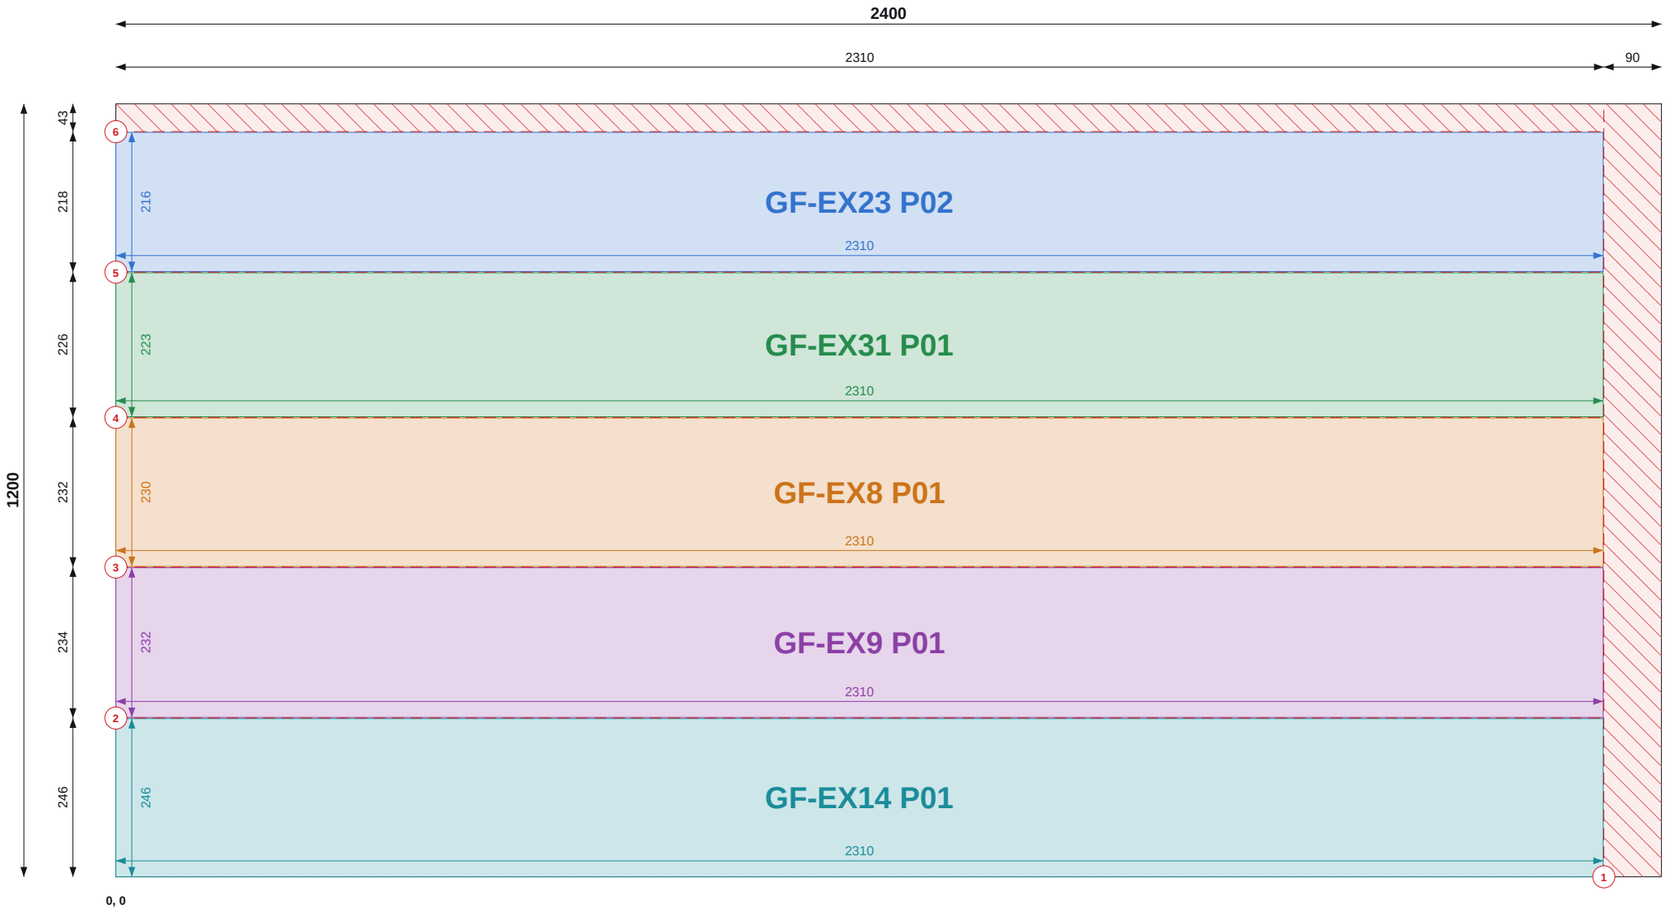

Top / left chains = saw cut positions (to cut centres). Coloured = part size and position.

SHEET 25 OF 33

THIS SHEET

Item	Value
Parts	5
Used / waste	92.0% / 0.23 m2
Reusable offcuts	0
Saw cuts / shared	6 / 4

PIECES (POSITION = BOTTOM-LEFT CORNER)

Label	Size	X, Y
GF-EX23 P02	216 x 2310	0, 940
GF-EX31 P01	223 x 2310	0, 714
GF-EX8 P01	230 x 2310	0, 482
GF-EX9 P01	232 x 2310	0, 248
GF-EX14 P01	246 x 2310	0, 0

NOTES

1. Cut from PIR 120mm 1200x2400, 2mm saw kerf. Viewed on the face; dimensions from the sheet's bottom-left corner (0,0). Red numbered lines = saw cuts in order, each edge to edge.
2. Coloured dimensions belong to the part of that colour: its width and height, and its position from the sheet edges. Raked parts: corner coordinates at each corner.
3. Red hatch = waste. Labels = panel + piece mark on the manufacture drawing.

REVISIONS

REV	DATE	DESCRIPTION
C01	14.09.26	Construction issue
C02	14.09.26	Roof trusses revised; SP diagonals added
C03	11.10.26	FF windows coursed; steel + GP1 portal; steel drawings (ST)
C04	13.10.26	Steel approved by the engineer: steel + steel timber drawings issued for constructio

TLS TIMBER FRAME

Design & Manufacture

Scan: 3D model + drawings

CLIENT	PROJECT
MP Adams	MP Adams Plot 4, Eckington

DRAWING TITLE


PIR CUTTING - GROUND FLOOR - SHEET 25 OF 33

PIR 120mm 1200x2400 | Ground Floor

SCALE	SIZE	DATE	DRAWN
NTS	A3	13.10.26	TS

STATUS	DRAWING No.	REV
CONSTRUCTION	P4-CP-PIR-01 / 25	C04

Do not scale. All dimensions in mm. Check all dimensions on site.

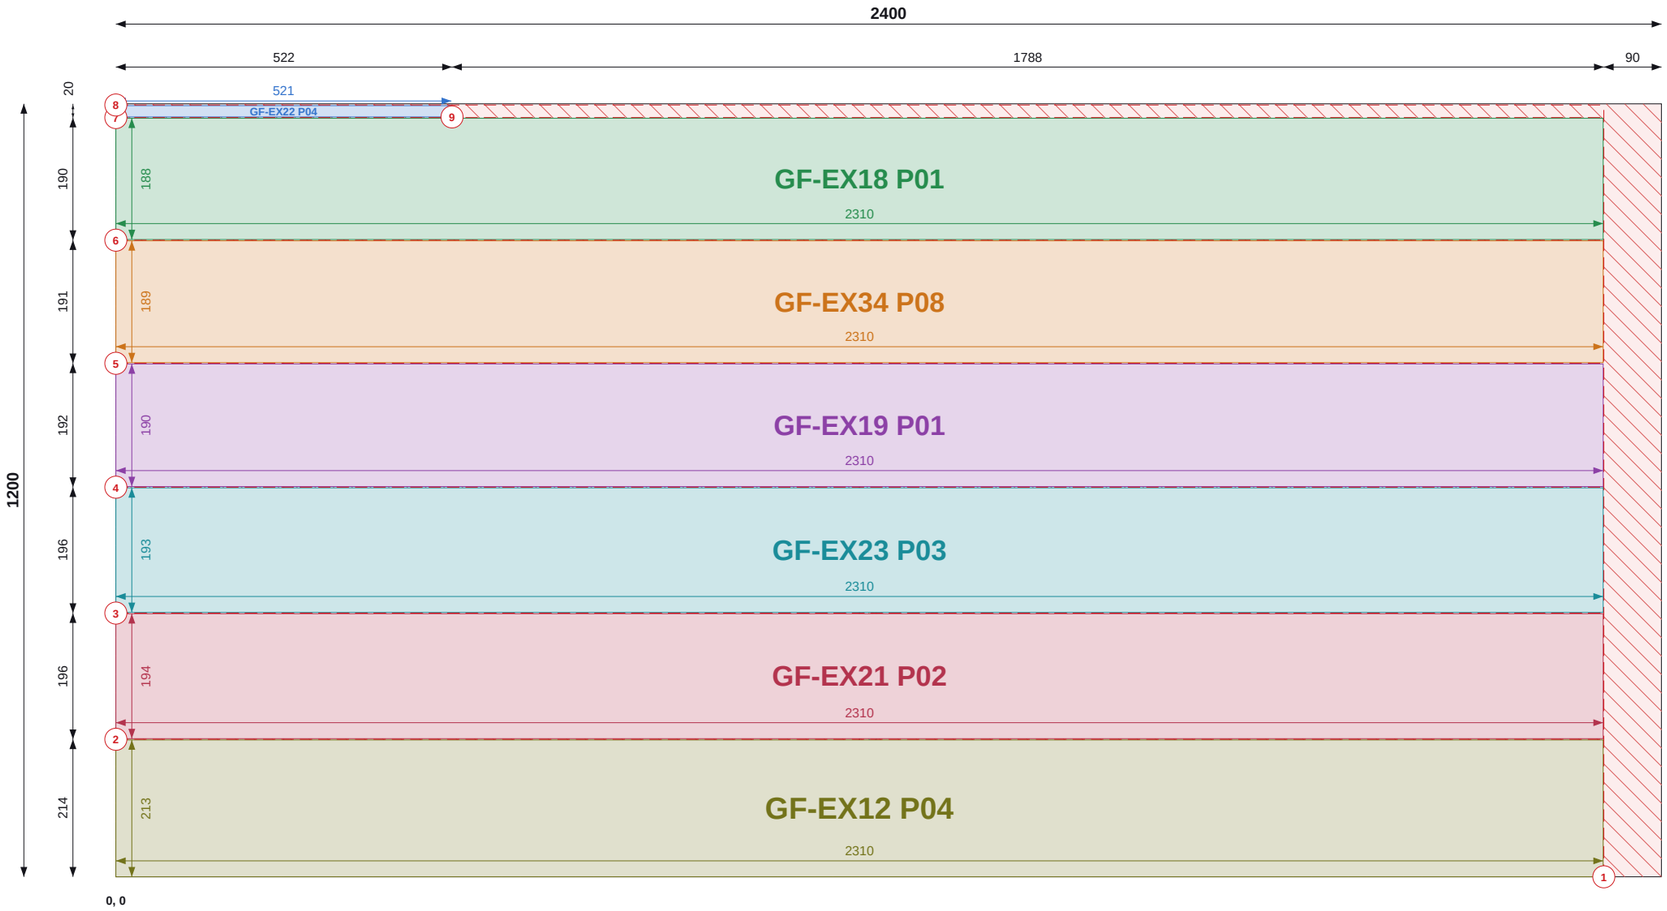

Top / left chains = saw cut positions (to cut centres). Coloured = part size and position.

SHEET 26 OF 33

THIS SHEET

Item	Value
Parts	7
Used / waste	94.0% / 0.17 m2
Reusable offcuts	0
Saw cuts / shared	9 / 6

PIECES (POSITION = BOTTOM-LEFT CORNER)

Label	Size	X, Y
GF-EX22 P04	521 x 18	0, 1180
GF-EX18 P01	188 x 2310	0, 989
GF-EX34 P08	189 x 2310	0, 798
GF-EX19 P01	190 x 2310	0, 606
GF-EX23 P03	193 x 2310	0, 410
GF-EX21 P02	194 x 2310	0, 215
GF-EX12 P04	213 x 2310	0, 0

NOTES

1. Cut from PIR 120mm 1200x2400, 2mm saw kerf. Viewed on the face; dimensions from the sheet's bottom-left corner (0,0). Red numbered lines = saw cuts in order, each edge to edge.
2. Coloured dimensions belong to the part of that colour: its width and height, and its position from the sheet edges. Raked parts: corner coordinates at each corner.
3. Red hatch = waste. Labels = panel + piece mark on the manufacture drawing.

REVISIONS

REV	DATE	DESCRIPTION
C01	14.09.26	Construction issue
C02	14.09.26	Roof trusses revised; SP diagonals added
C03	11.10.26	FF windows coursed; steel + GP1 portal; steel drawings (ST)
C04	13.10.26	Steel approved by the engineer: steel + steel timber drawings issued for construction

TLS

TLS TIMBER FRAME

Design & Manufacture

Scan: 3D model + drawings

CLIENT	PROJECT
MP Adams	MP Adams Plot 4, Eckington

DRAWING TITLE


PIR CUTTING - GROUND FLOOR - SHEET 26 OF 33

PIR 120mm 1200x2400 | Ground Floor

SCALE	SIZE	DATE	DRAWN
NTS	A3	13.10.26	TS

STATUS	DRAWING No.	REV
CONSTRUCTION	P4-CP-PIR-01 / 26	C04

Do not scale. All dimensions in mm. Check all dimensions on site.

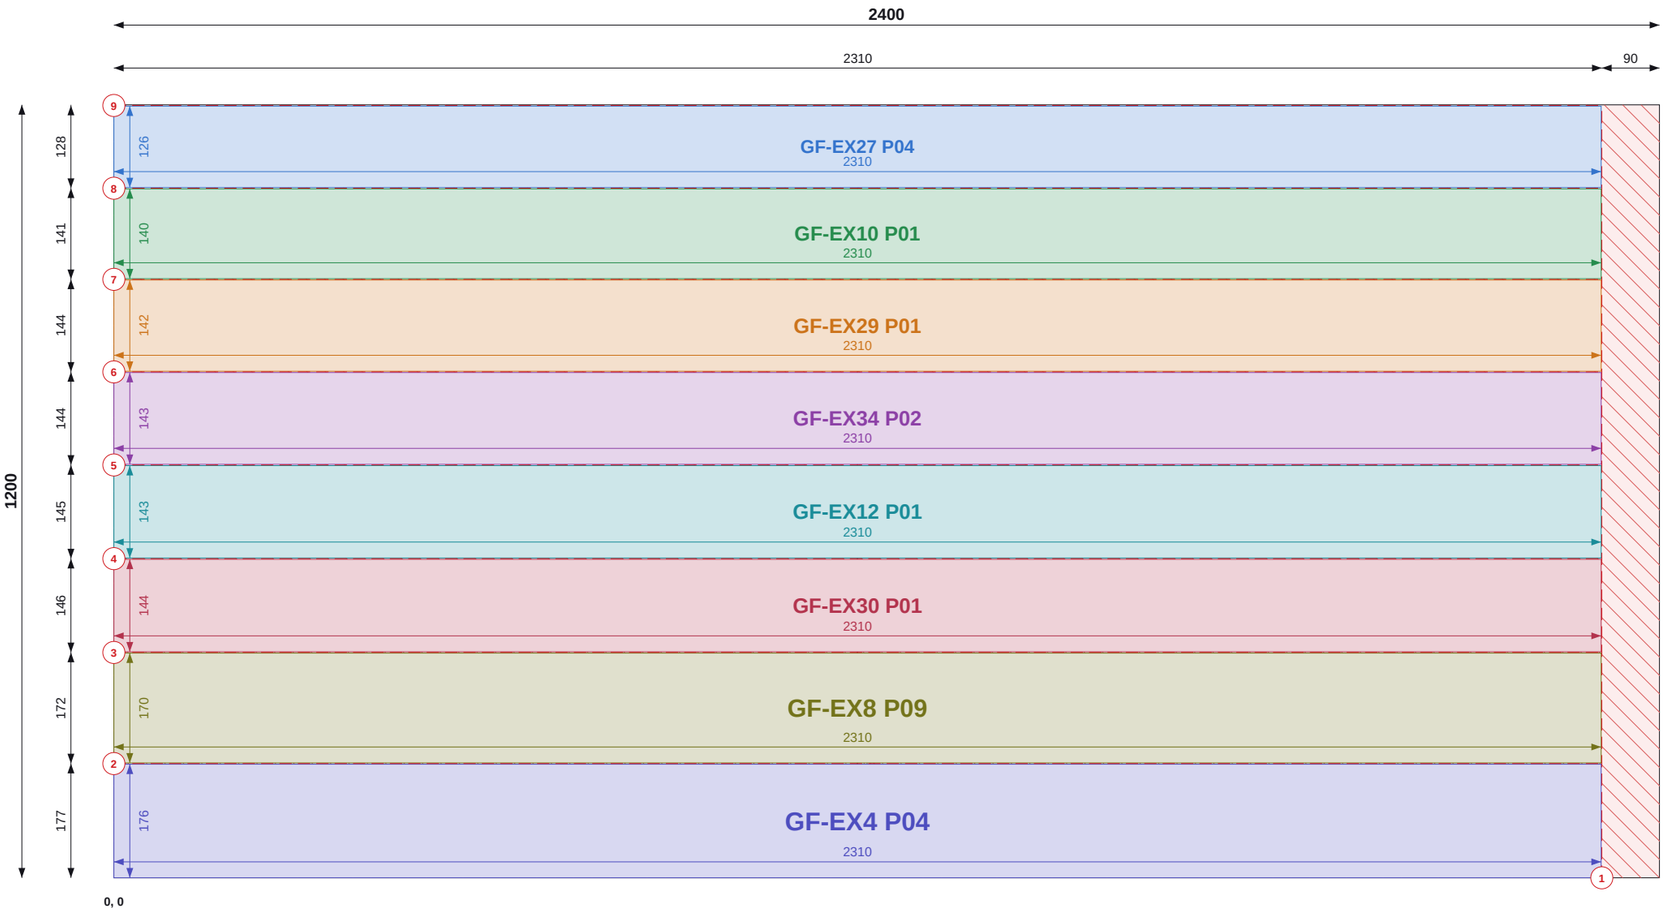

Top / left chains = saw cut positions (to cut centres). Coloured = part size and position.

Do not scale. All dimensions in mm. Check all dimensions on site.

SHEET 27 OF 33

THIS SHEET

Item	Value
Parts	8
Used / waste	94.9% / 0.15 m2
Reusable offcuts	0
Saw cuts / shared	9 / 7

PIECES (POSITION = BOTTOM-LEFT CORNER)

Label	Size	X, Y
GF-EX27 P04	126 x 2310	0, 1072
GF-EX10 P01	140 x 2310	0, 930
GF-EX29 P01	142 x 2310	0, 786
GF-EX34 P02	143 x 2310	0, 642
GF-EX12 P01	143 x 2310	0, 496
GF-EX30 P01	144 x 2310	0, 351
GF-EX8 P09	170 x 2310	0, 178
GF-EX4 P04	176 x 2310	0, 0

NOTES

1. Cut from PIR 120mm 1200x2400, 2mm saw kerf. Viewed on the face; dimensions from the sheet's bottom-left corner (0,0). Red numbered lines = saw cuts in order, each edge to edge.
2. Coloured dimensions belong to the part of that colour: its width and height, and its position from the sheet edges. Raked parts: corner coordinates at each corner.
3. Red hatch = waste. Labels = panel + piece mark on the manufacture drawing.

REVISIONS

REV	DATE	DESCRIPTION
C01	14.09.26	Construction issue
C02	14.09.26	Roof trusses revised; SP diagonals added
C03	11.10.26	FF windows coursed; steel + GP1 portal; steel drawings (ST)
C04	13.10.26	Steel approved by the engineer: steel + steel timber drawings issued for construction

TLS

TLS TIMBER FRAME

Design & Manufacture

Scan: 3D model + drawings

CLIENT	PROJECT
MP Adams	MP Adams Plot 4, Eckington


DRAWING TITLE

PIR CUTTING - GROUND FLOOR - SHEET 27 OF 33

PIR 120mm 1200x2400 | Ground Floor

SCALE	SIZE	DATE	DRAWN
NTS	A3	13.10.26	TS

STATUS	DRAWING No.	REV
CONSTRUCTION	P4-CP-PIR-01 / 27	C04

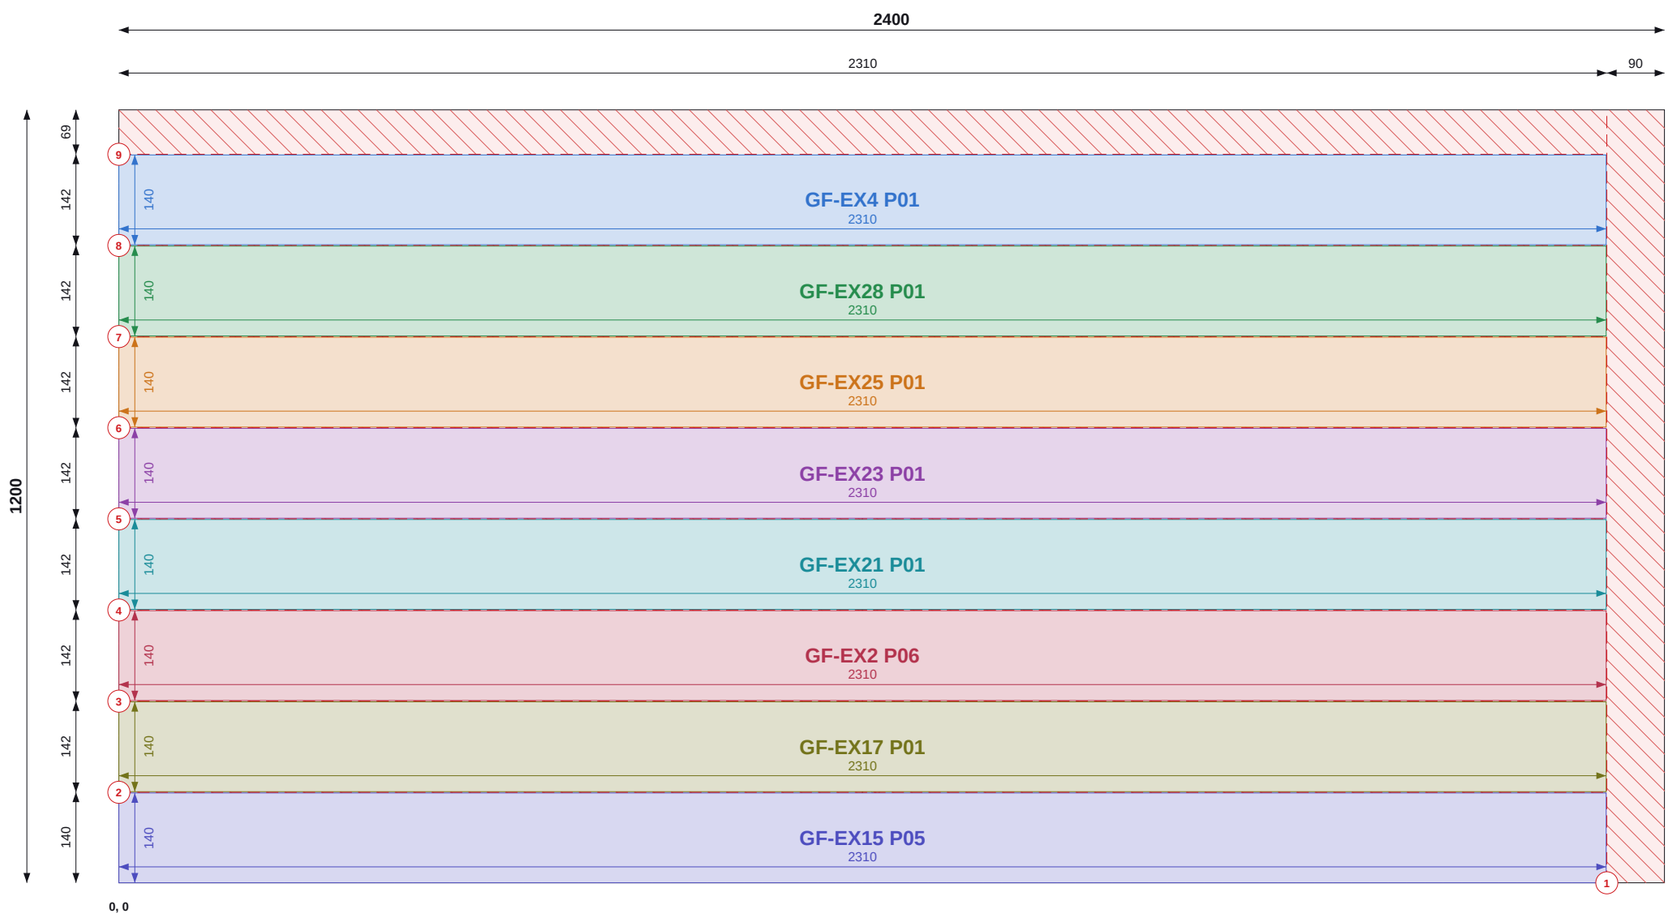

Top / left chains = saw cut positions (to cut centres). Coloured = part size and position.

SHEET 28 OF 33

THIS SHEET

Item	Value
Parts	8
Used / waste	89.5% / 0.30 m2
Reusable offcuts	0
Saw cuts / shared	9 / 7

PIECES (POSITION = BOTTOM-LEFT CORNER)

Label	Size	X, Y
GF-EX4 P01	140 x 2310	0, 991
GF-EX28 P01	140 x 2310	0, 849
GF-EX25 P01	140 x 2310	0, 708
GF-EX23 P01	140 x 2310	0, 566
GF-EX21 P01	140 x 2310	0, 425
GF-EX2 P06	140 x 2310	0, 283
GF-EX17 P01	140 x 2310	0, 142
GF-EX15 P05	140 x 2310	0, 0

NOTES

1. Cut from PIR 120mm 1200x2400, 2mm saw kerf. Viewed on the face; dimensions from the sheet's bottom-left corner (0,0). Red numbered lines = saw cuts in order, each edge to edge.
2. Coloured dimensions belong to the part of that colour: its width and height, and its position from the sheet edges. Raked parts: corner coordinates at each corner.
3. Red hatch = waste. Labels = panel + piece mark on the manufacture drawing.

REVISIONS

REV	DATE	DESCRIPTION
C01	14.09.26	Construction issue
C02	14.09.26	Roof trusses revised; SP diagonals added
C03	11.10.26	FF windows coursed; steel + GP1 portal; steel drawings (ST)
C04	13.10.26	Steel approved by the engineer: steel + steel timber drawings issued for construction

TLS TIMBER FRAME
Design & Manufacture
Scan: 3D model + drawings


CLIENT	PROJECT
MP Adams	MP Adams Plot 4, Eckington

DRAWING TITLE
PIR CUTTING - GROUND FLOOR - SHEET 28 OF 33
PIR 120mm 1200x2400 | Ground Floor

SCALE	SIZE	DATE	DRAWN
NTS	A3	13.10.26	TS

STATUS	DRAWING No.	REV
CONSTRUCTION	P4-CP-PIR-01 / 28	C04

Do not scale. All dimensions in mm. Check all dimensions on site.

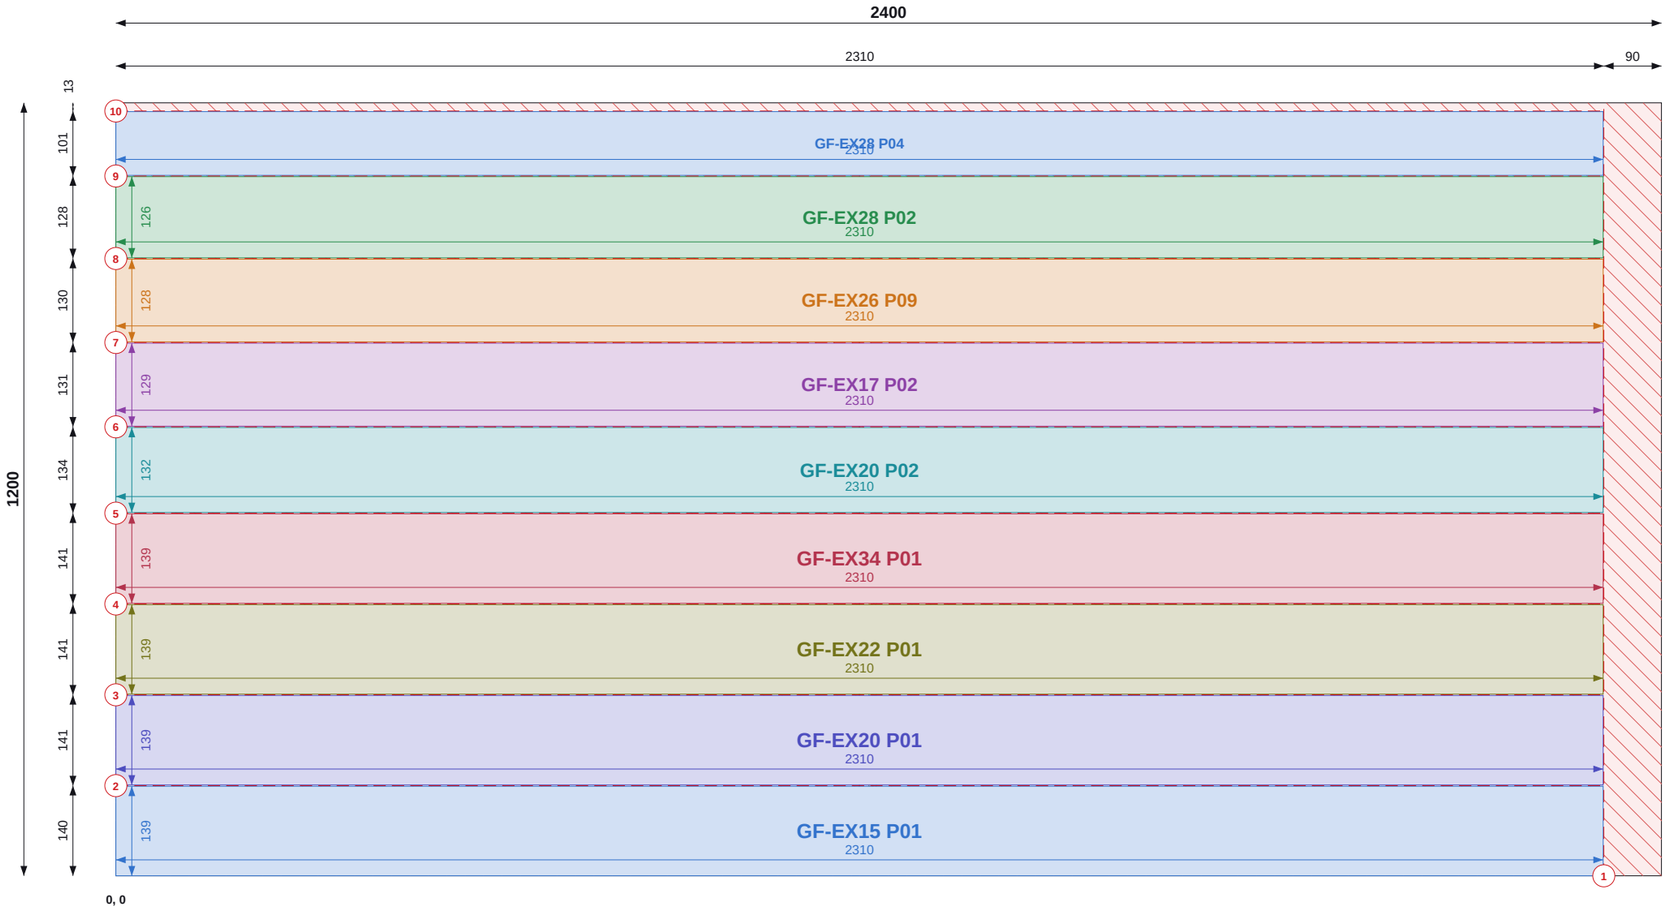

Top / left chains = saw cut positions (to cut centres). Coloured = part size and position.

Do not scale. All dimensions in mm. Check all dimensions on site.

SHEET 29 OF 33

THIS SHEET

Item	Value
Parts	9
Used / waste	93.9% / 0.18 m2
Reusable offcuts	0
Saw cuts / shared	10 / 8

PIECES (POSITION = BOTTOM-LEFT CORNER)

Label	Size	X, Y
GF-EX28 P04	99 x 2310	0, 1087
GF-EX28 P02	126 x 2310	0, 959
GF-EX26 P09	128 x 2310	0, 829
GF-EX17 P02	129 x 2310	0, 698
GF-EX20 P02	132 x 2310	0, 564
GF-EX34 P01	139 x 2310	0, 423
GF-EX22 P01	139 x 2310	0, 282
GF-EX20 P01	139 x 2310	0, 141
GF-EX15 P01	139 x 2310	0, 0

NOTES

1. Cut from PIR 120mm 1200x2400, 2mm saw kerf. Viewed on the face; dimensions from the sheet's bottom-left corner (0,0). Red numbered lines = saw cuts in order, each edge to edge.
2. Coloured dimensions belong to the part of that colour: its width and height, and its position from the sheet edges. Raked parts: corner coordinates at each corner.
3. Red hatch = waste. Labels = panel + piece mark on the manufacture drawing.

REVISIONS

REV	DATE	DESCRIPTION
C01	14.09.26	Construction issue
C02	14.09.26	Roof trusses revised; SP diagonals added
C03	11.10.26	FF windows coursed; steel + GP1 portal; steel drawings (ST)
C04	13.10.26	Steel approved by the engineer: steel + steel timber drawings issued for construction

TLS TIMBER FRAME
Design & Manufacture
Scan: 3D model + drawings


CLIENT	PROJECT
MP Adams	MP Adams Plot 4, Eckington

DRAWING TITLE
PIR CUTTING - GROUND FLOOR - SHEET 29 OF 33

PIR 120mm 1200x2400 | Ground Floor

SCALE	SIZE	DATE	DRAWN
NTS	A3	13.10.26	TS

STATUS	DRAWING No.	REV
CONSTRUCTION	P4-CP-PIR-01 / 29	C04

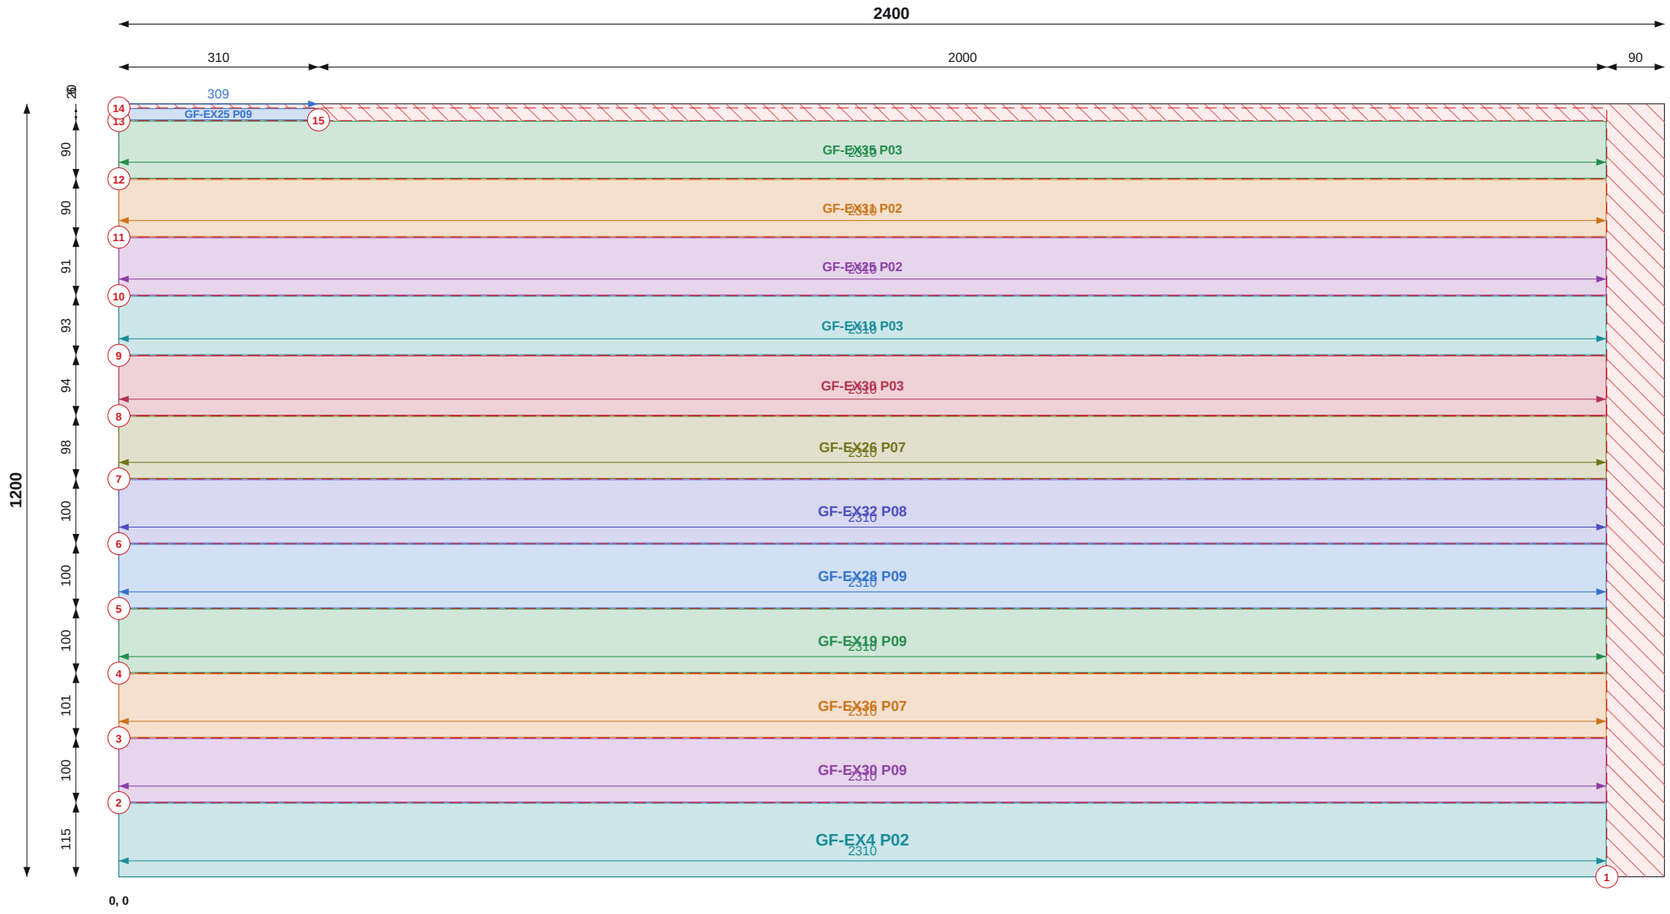

Top / left chains = saw cut positions (to cut centres). Coloured = part size and position.

Do not scale. All dimensions in mm. Check all dimensions on site.

SHEET 30 OF 33

THIS SHEET

Item	Value
Parts	13
Used / waste	92.5% / 0.22 m2
Reusable offcuts	0
Saw cuts / shared	15 / 12

PIECES (POSITION = BOTTOM-LEFT CORNER)

Label	Size	X, Y
GF-EX25 P09	309 x 18	0, 1175
GF-EX35 P03	89 x 2310	0, 1085
GF-EX31 P02	89 x 2310	0, 994
GF-EX25 P02	89 x 2310	0, 903
GF-EX18 P03	91 x 2310	0, 811
GF-EX30 P03	92 x 2310	0, 717
GF-EX26 P07	96 x 2310	0, 619
GF-EX32 P08	98 x 2310	0, 518
GF-EX28 P09	98 x 2310	0, 418
GF-EX19 P09	98 x 2310	0, 317
GF-EX36 P07	99 x 2310	0, 217
GF-EX30 P09	99 x 2310	0, 116
GF-EX4 P02	114 x 2310	0, 0

NOTES

1. Cut from PIR 120mm 1200x2400, 2mm saw kerf. Viewed on the face; dimensions from the sheet's bottom-left corner (0,0). Red numbered lines = saw cuts in order, each edge to edge.
2. Coloured dimensions belong to the part of that colour: its width and height, and its position from the sheet edges. Raked parts: corner coordinates at each corner.
3. Red hatch = waste. Labels = panel + piece mark on the manufacture drawing.

REVISIONS

REV	DATE	DESCRIPTION
C01	14.09.26	Construction issue
C02	14.09.26	Roof trusses revised; SP diagonals added
C03	11.10.26	FF windows coursed; steel + GP1 portal; steel drawings (ST)
C04	13.10.26	Steel approved by the engineer: steel + steel timber drawings issued for construction

TLS TIMBER FRAME DESIGN SUITE

TLS TIMBER FRAME

Design & Manufacture

Scan: 3D model + drawings

CLIENT	PROJECT
MP Adams	MP Adams Plot 4, Eckington


DRAWING TITLE

PIR CUTTING - GROUND FLOOR - SHEET 30 OF 33

PIR 120mm 1200x2400 | Ground Floor

SCALE	SIZE	DATE	DRAWN
NTS	A3	13.10.26	TS

STATUS	DRAWING No.	REV
CONSTRUCTION	P4-CP-PIR-01 / 30	C04

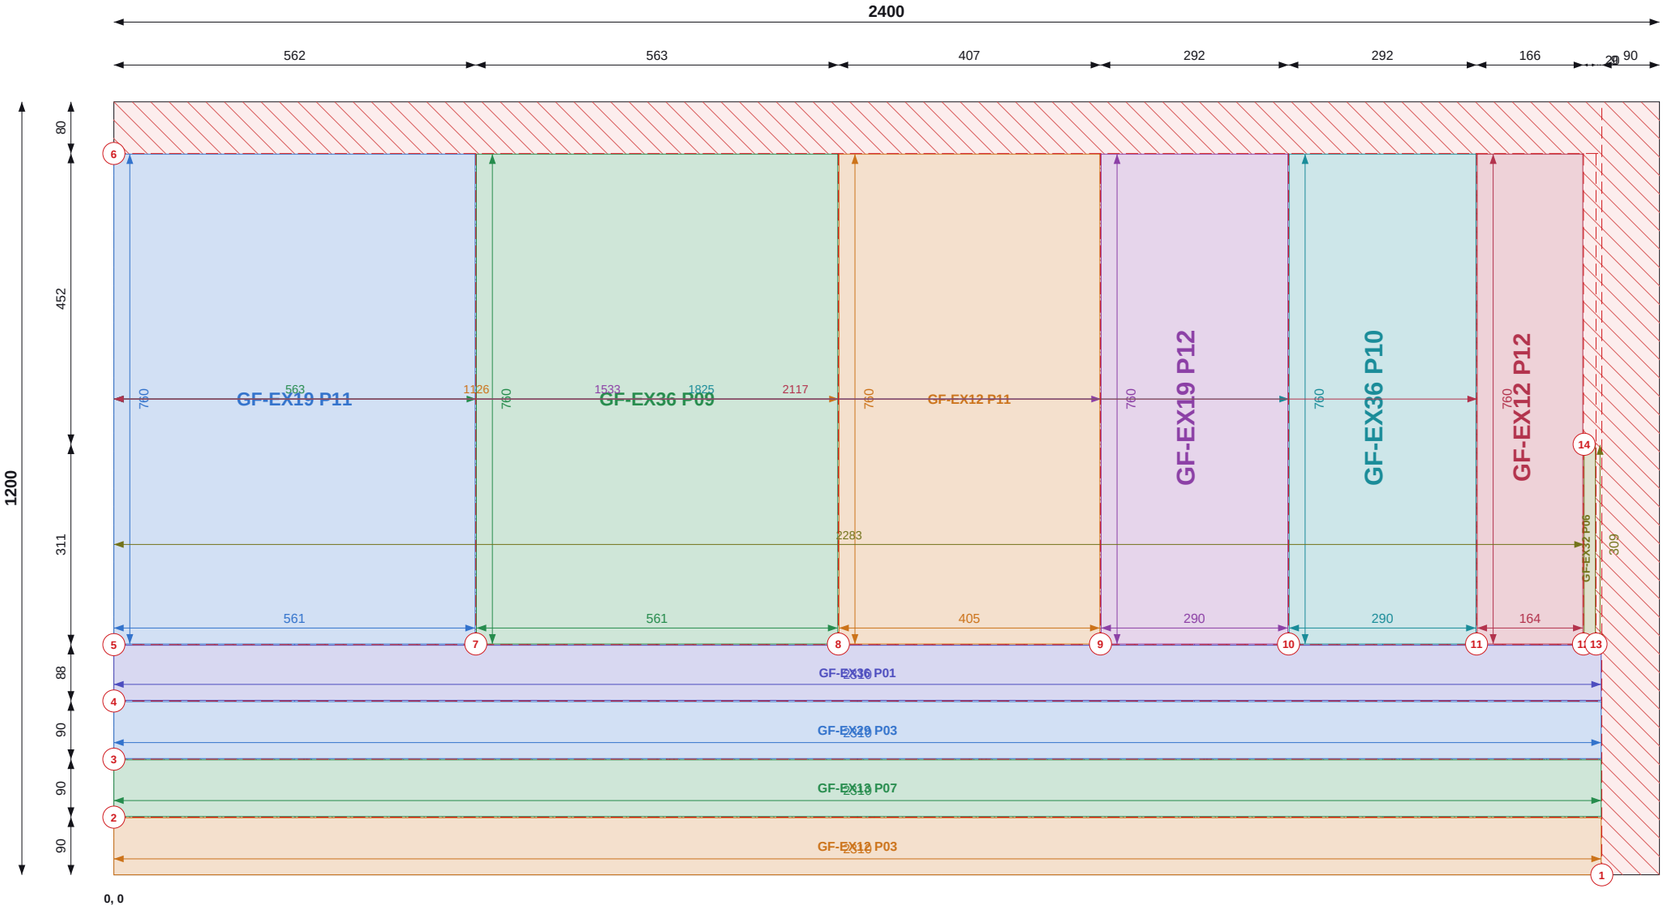

Top / left chains = saw cut positions (to cut centres). Coloured = part size and position.

SHEET 31 OF 33

THIS SHEET

Item	Value
Parts	11
Used / waste	88.3% / 0.34 m2
Reusable offcuts	0
Saw cuts / shared	14 / 10

PIECES (POSITION = BOTTOM-LEFT CORNER)

Label	Size	X, Y
GF-EX19 P11	561 x 760	0, 358
GF-EX36 P09	561 x 760	563, 358
GF-EX12 P11	405 x 760	1126, 358
GF-EX19 P12	290 x 760	1533, 358
GF-EX36 P10	290 x 760	1825, 358
GF-EX12 P12	164 x 760	2117, 358
GF-EX32 P06	309 x 18	2283, 358
GF-EX36 P01	86 x 2310	0, 271
GF-EX29 P03	88 x 2310	0, 181
GF-EX13 P07	88 x 2310	0, 90
GF-EX12 P03	88 x 2310	0, 0

NOTES

1. Cut from PIR 120mm 1200x2400, 2mm saw kerf. Viewed on the face; dimensions from the sheet's bottom-left corner (0,0). Red numbered lines = saw cuts in order, each edge to edge.
2. Coloured dimensions belong to the part of that colour: its width and height, and its position from the sheet edges. Raked parts: corner coordinates at each corner.
3. Red hatch = waste. Labels = panel + piece mark on the manufacture drawing.

REVISIONS

REV	DATE	DESCRIPTION
C01	14.09.26	Construction issue
C02	14.09.26	Roof trusses revised; SP diagonals added
C03	11.10.26	FF windows coursed; steel + GP1 portal; steel drawings (ST)
C04	13.10.26	Steel approved by the engineer: steel + steel timber drawings issued for construction

TLS

TLS TIMBER FRAME

Design & Manufacture

Scan: 3D model + drawings

CLIENT	PROJECT
MP Adams	MP Adams Plot 4, Eckington

DRAWING TITLE


PIR CUTTING - GROUND FLOOR - SHEET 31 OF 33

PIR 120mm 1200x2400 | Ground Floor

SCALE	SIZE	DATE	DRAWN
NTS	A3	13.10.26	TS

STATUS	DRAWING No.	REV
CONSTRUCTION	P4-CP-PIR-01 / 31	C04

Do not scale. All dimensions in mm. Check all dimensions on site.

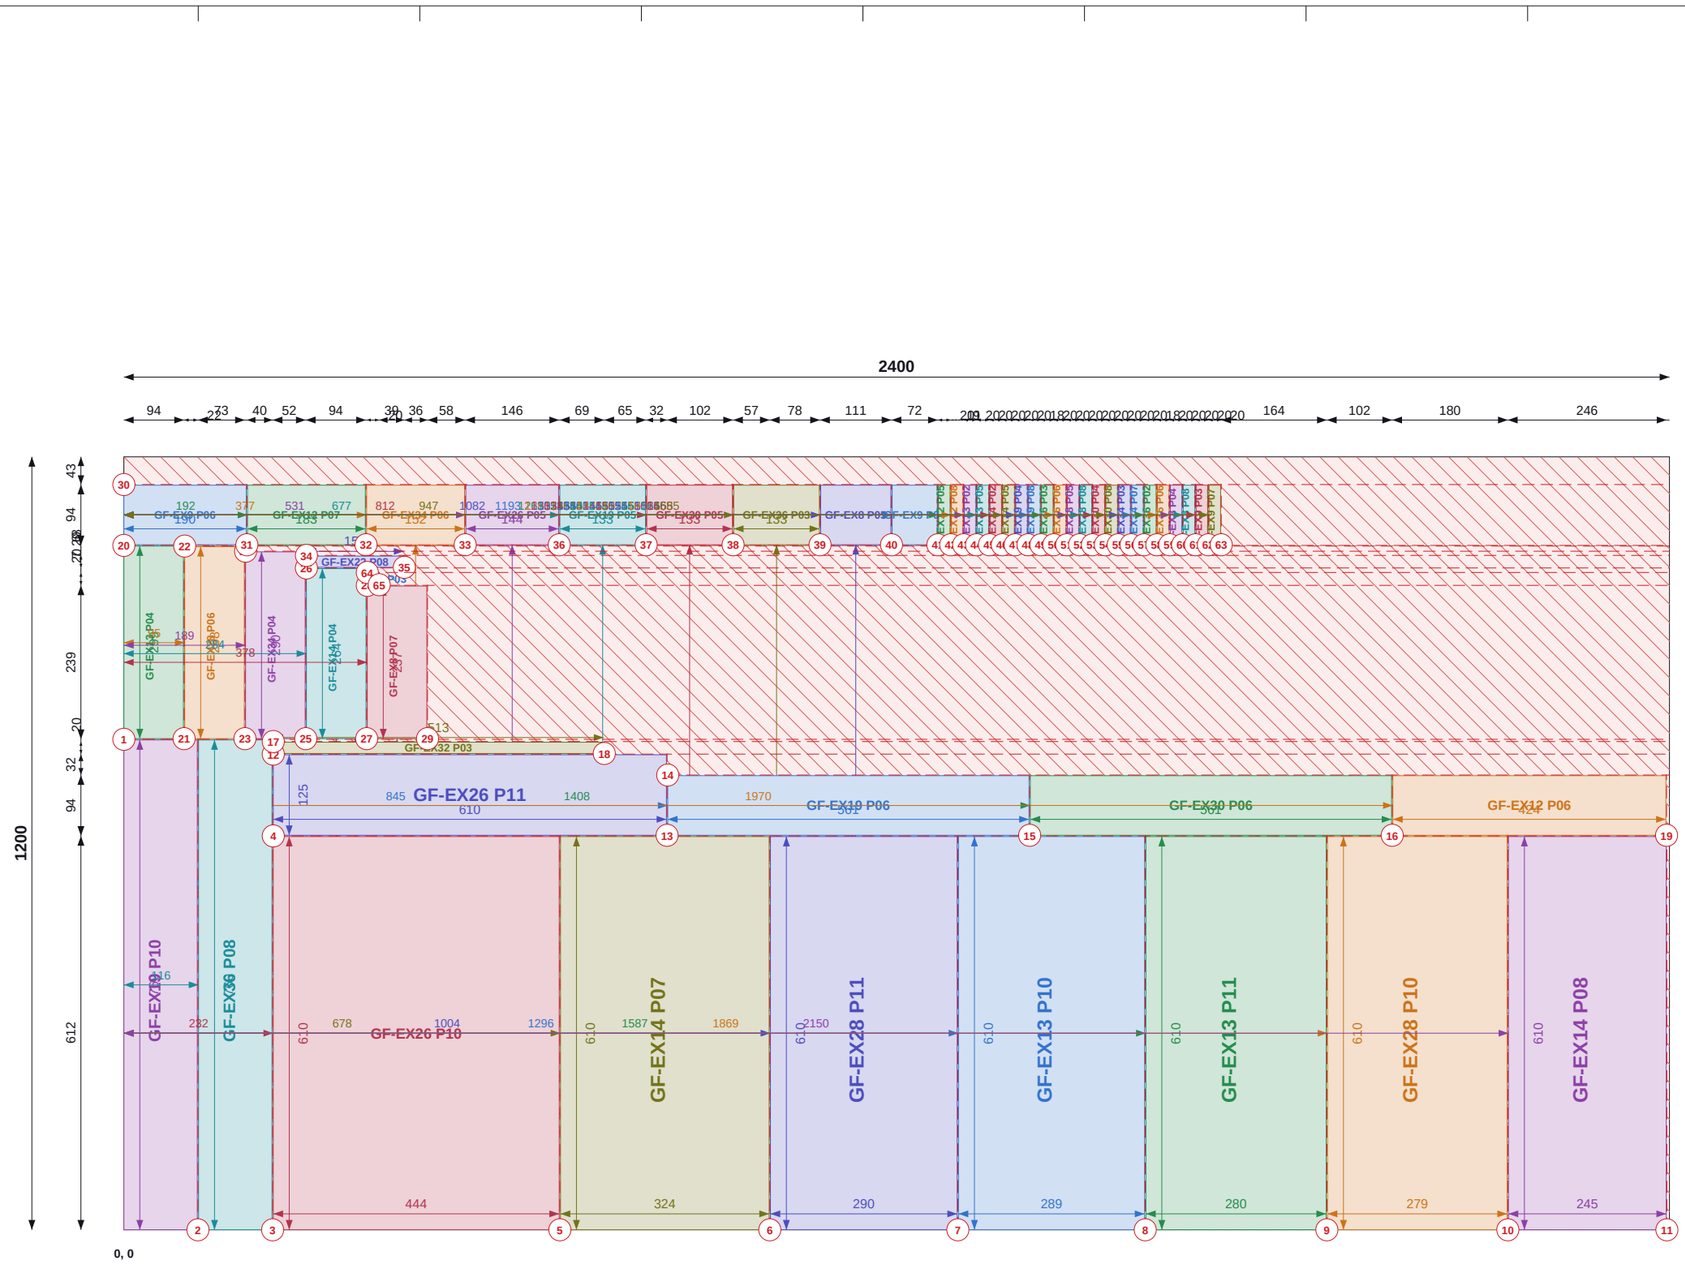

Top / left chains = saw cut positions (to cut centres). Coloured = part size and position.

SHEET 32 OF 33

THIS SHEET

Item	Value
Parts	52
Used / waste	69.4% / 0.88 m2
Reusable offcuts	0
Saw cuts / shared	65 / 51

PIECES (POSITION = BOTTOM-LEFT CORNER)

Label	Size	X, Y
GF-EX9 P06	190 x 93	0, 1064
GF-EX12 P07	183 x 93	192, 1064
GF-EX34 P06	152 x 93	377, 1064
GF-EX26 P05	144 x 93	531, 1064
GF-EX19 P05	133 x 93	677, 1064
GF-EX30 P05	133 x 93	812, 1064
GF-EX36 P03	133 x 93	947, 1064
GF-EX8 P05	109 x 93	1082, 1064
GF-EX9 P04	70 x 93	1193, 1064
GF-EX12 P05	18 x 93	1265, 1064
GF-EX12 P08	18 x 93	1285, 1064
GF-EX13 P02	18 x 93	1305, 1064
GF-EX13 P05	18 x 93	1325, 1064
GF-EX14 P02	18 x 93	1345, 1064
GF-EX14 P05	18 x 93	1365, 1064
GF-EX19 P04	18 x 93	1385, 1064
GF-EX19 P08	18 x 93	1405, 1064
GF-EX26 P03	18 x 93	1425, 1064
GF-EX26 P06	18 x 93	1445, 1064
GF-EX28 P05	18 x 93	1465, 1064
GF-EX28 P08	18 x 93	1485, 1064
GF-EX30 P04	18 x 93	1505, 1064
GF-EX30 P08	18 x 93	1525, 1064
GF-EX34 P03	18 x 93	1545, 1064
GF-EX34 P07	18 x 93	1565, 1064
GF-EX36 P02	18 x 93	1585, 1064
GF-EX36 P06	18 x 93	1605, 1064
GF-EX8 P04	18 x 93	1625, 1064
GF-EX8 P08	18 x 93	1645, 1064
GF-EX9 P03	18 x 93	1665, 1064
GF-EX9 P07	18 x 93	1685, 1064
GF-EX22 P08	151 x 18	284, 1028
GF-EX22 P03	18 x 18	378, 1001
GF-EX13 P04	299 x 93	0, 762
GF-EX28 P06	298 x 93	95, 762
GF-EX34 P04	290 x 93	189, 762
GF-EX14 P04	264 x 93	284, 762
GF-EX8 P07	237 x 93	378, 762
GF-EX32 P03	513 x 18	232, 740
GF-EX26 P11	125 x 610	232, 612
GF-EX19 P06	561 x 93	845, 612
GF-EX30 P06	561 x 93	1408, 612
GF-EX12 P06	424 x 93	1970, 612
GF-EX19 P10	114 x 760	0, 0
GF-EX36 P08	114 x 760	116, 0
GF-EX26 P10	444 x 610	232, 0
GF-EX14 P07	324 x 610	678, 0
GF-EX28 P11	290 x 610	1004, 0
GF-EX13 P10	289 x 610	1296, 0
GF-EX13 P11	280 x 610	1587, 0
GF-EX28 P10	279 x 610	1869, 0
GF-EX14 P08	245 x 610	2150, 0

NOTES

1. Cut from PIR 120mm 1200x2400, 2mm saw kerf. Viewed on the face; dimensions from the sheet's bottom-left corner (0,0). Red numbered lines = saw cuts in order, each edge to edge.
2. Coloured dimensions belong to the part of that colour: its width and height, and its position from the sheet edges. Raked parts: corner coordinates at each corner.
3. Red hatch = waste. Labels = panel + piece mark on the manufacture drawing.

REVISIONS

REV	DATE	DESCRIPTION
C01	14.09.26	Construction issue
C02	14.09.26	Roof trusses revised; SP diagonals added
C03	11.10.26	FF windows coursed; steel + GP1 portal; steel drawings (ST)
C04	13.10.26	Steel approved by the engineer: steel + steel timber drawings issued for construction

TLS TIMBER FRAME
Design & Manufacture
Scan: 3D model + drawings

CLIENT	PROJECT
MP Adams	MP Adams Plot 4, Eckington


DRAWING TITLE
PIR CUTTING - GROUND FLOOR - SHEET 32 OF 33

PIR 120mm 1200x2400 | Ground Floor

SCALE	SIZE	DATE	DRAWN
NTS	A3	13.10.26	TS

STATUS	DRAWING No.	REV
CONSTRUCTION	P4-CP-PIR-01 / 32	C04

Do not scale. All dimensions in mm. Check all dimensions on site.

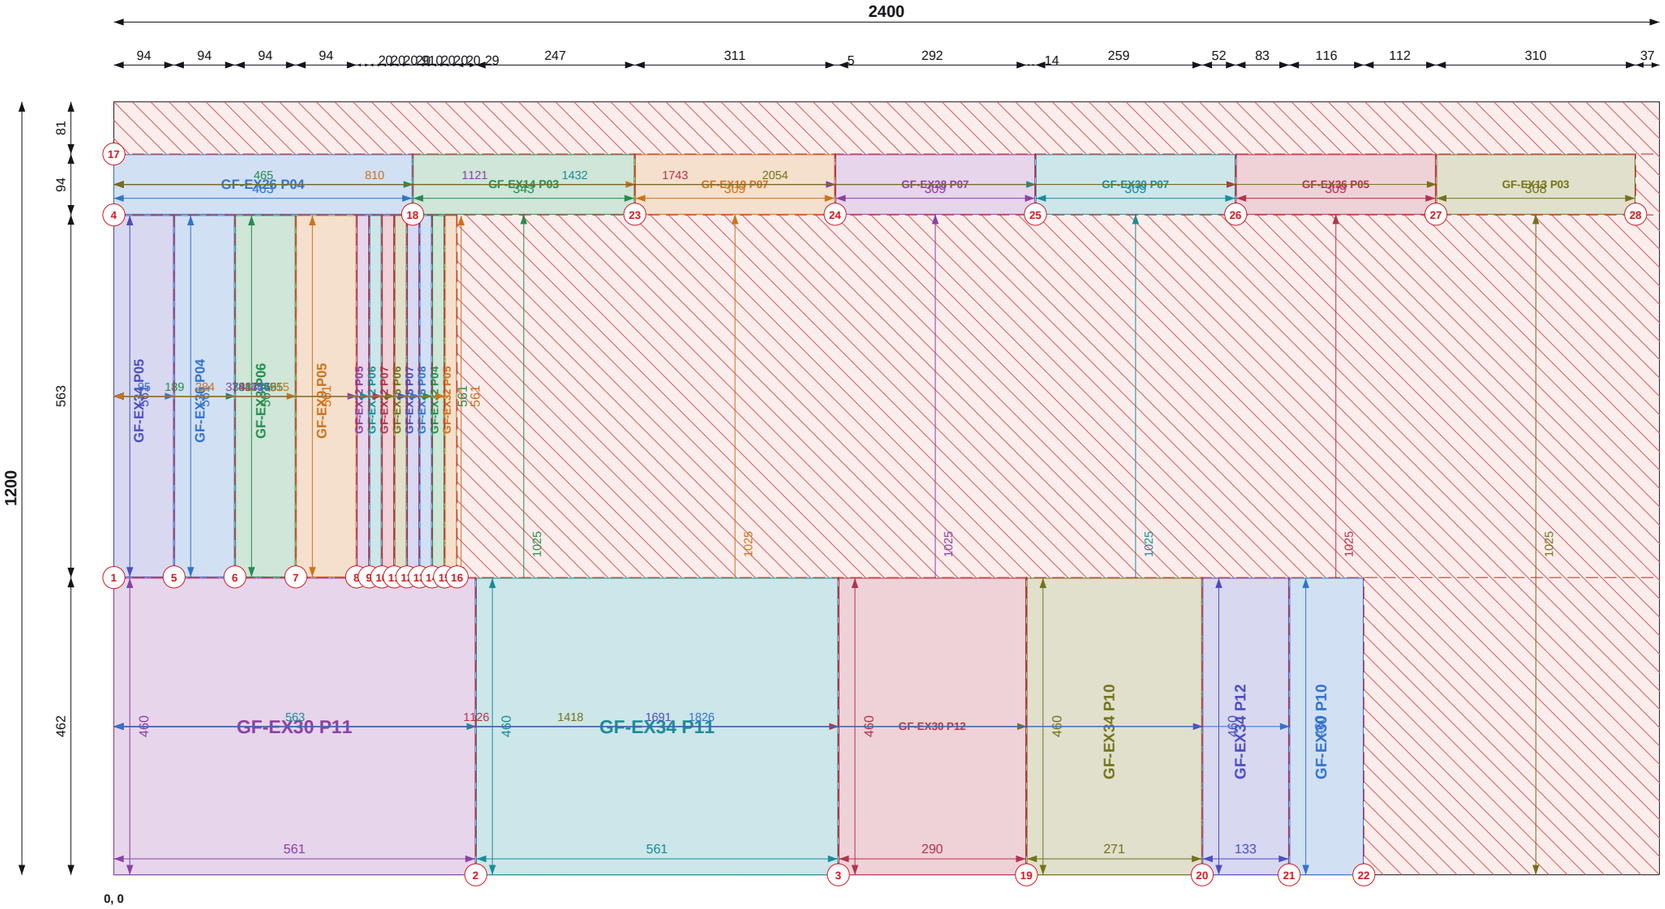

Top / left chains = saw cut positions (to cut centres). Coloured = part size and position.

Do not scale. All dimensions in mm. Check all dimensions on site.

SHEET 33 OF 33

THIS SHEET

Item	Value
Parts	25
Used / waste	48.3% / 1.49 m2
Reusable offcuts	2
Saw cuts / shared	28 / 24

PIECES (POSITION = BOTTOM-LEFT CORNER)

Label	Size	X, Y
GF-EX26 P04	463 x 93	0, 1025
GF-EX14 P03	343 x 93	465, 1025
GF-EX19 P07	309 x 93	810, 1025
GF-EX28 P07	309 x 93	1121, 1025
GF-EX30 P07	309 x 93	1432, 1025
GF-EX36 P05	309 x 93	1743, 1025
GF-EX13 P03	308 x 93	2054, 1025
GF-EX34 P05	561 x 93	0, 462
GF-EX36 P04	561 x 93	95, 462
GF-EX8 P06	561 x 93	189, 462
GF-EX9 P05	561 x 93	284, 462
GF-EX22 P05	561 x 18	378, 462
GF-EX22 P06	561 x 18	398, 462
GF-EX22 P07	561 x 18	417, 462
GF-EX25 P06	561 x 18	437, 462
GF-EX25 P07	561 x 18	456, 462
GF-EX25 P08	561 x 18	476, 462
GF-EX32 P04	561 x 18	495, 462
GF-EX32 P05	561 x 18	515, 462
GF-EX30 P11	561 x 460	0, 0
GF-EX34 P11	561 x 460	563, 0
GF-EX30 P12	290 x 460	1126, 0
GF-EX34 P10	271 x 460	1418, 0
GF-EX34 P12	133 x 460	1691, 0
GF-EX30 P10	114 x 460	1826, 0

NOTES

1. Cut from PIR 120mm 1200x2400, 2mm saw kerf. Viewed on the face; dimensions from the sheet's bottom-left corner (0,0). Red numbered lines = saw cuts in order, each edge to edge.
2. Coloured dimensions belong to the part of that colour: its width and height, and its position from the sheet edges. Raked parts: corner coordinates at each corner.
3. Red hatch = waste. Labels = panel + piece mark on the manufacture drawing.

REVISIONS

REV	DATE	DESCRIPTION
C01	14.09.26	Construction issue
C02	14.09.26	Roof trusses revised; SP diagonals added
C03	11.10.26	FF windows coursed; steel + GP1 portal; steel drawings (ST)
C04	13.10.26	Steel approved by the engineer: steel + steel timber drawings issued for construction

TLS TIMBER FRAME
Design & Manufacture
Scan: 3D model + drawings

CLIENT	PROJECT
MP Adams	MP Adams Plot 4, Eckington


DRAWING TITLE

PIR CUTTING - GROUND FLOOR - SHEET 33 OF 33

PIR 120mm 1200x2400 | Ground Floor

SCALE	SIZE	DATE	DRAWN
NTS	A3	13.10.26	TS

STATUS	DRAWING No.	REV
CONSTRUCTION	P4-CP-PIR-01 / 33	C04

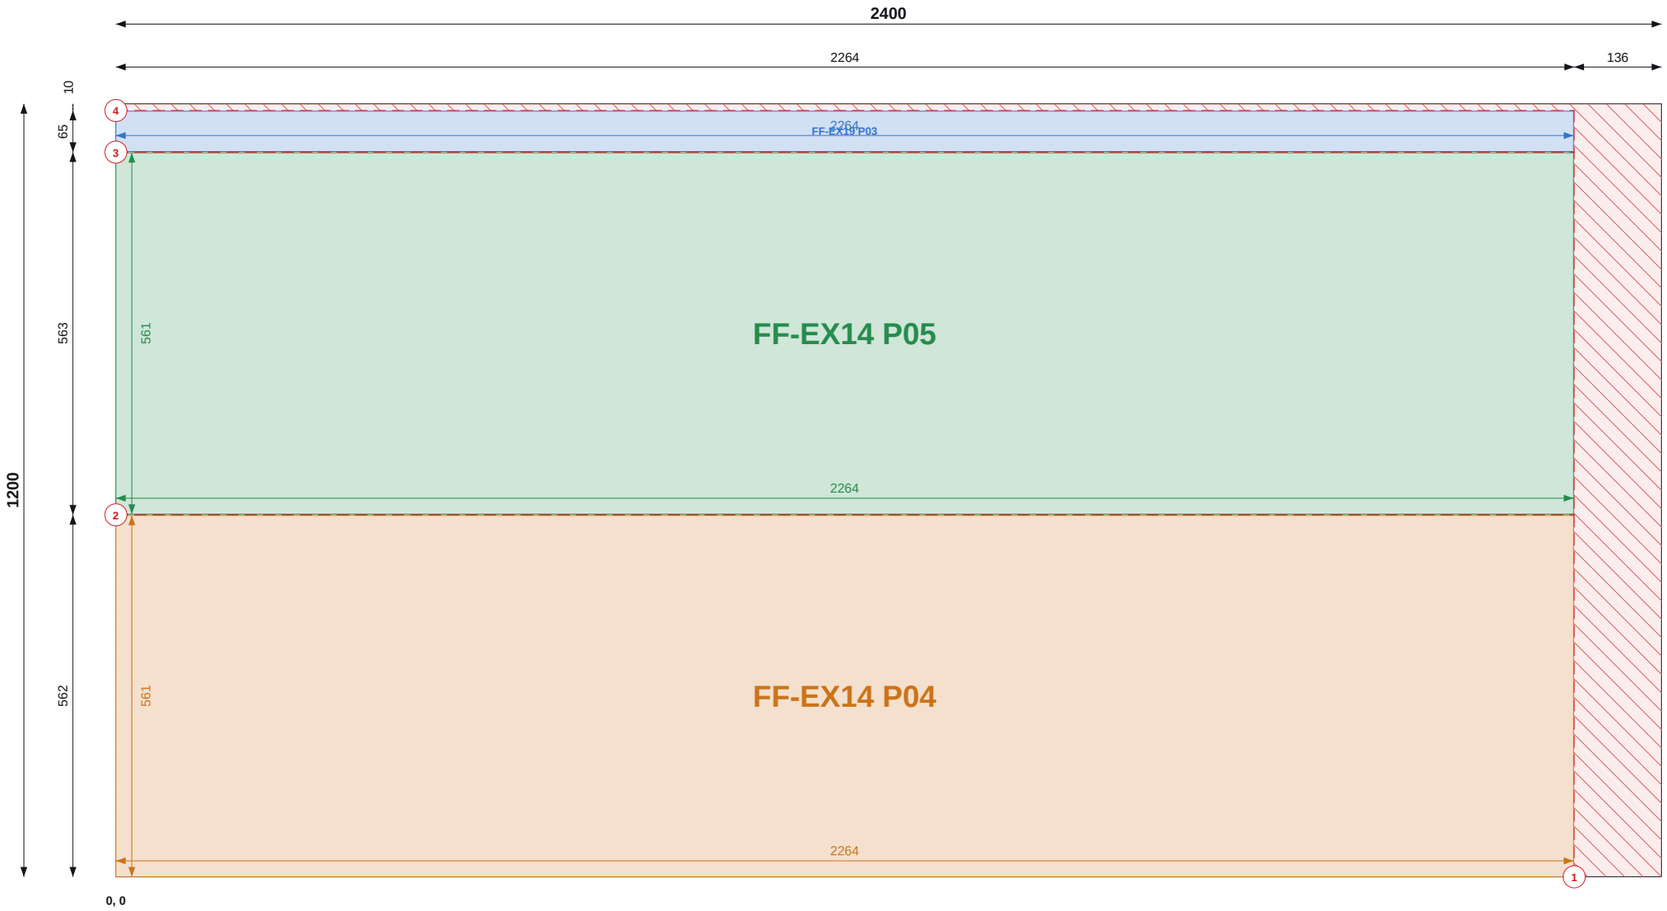

Top / left chains = saw cut positions (to cut centres). Coloured = part size and position.

SHEET 1 OF 23

THIS SHEET

Item	Value
Parts	3
Used / waste	93.1% / 0.20 m2
Reusable offcuts	0
Saw cuts / shared	4 / 2

PIECES (POSITION = BOTTOM-LEFT CORNER)

Label	Size	X, Y
FF-EX19 P03	63 x 2264	0, 1126
FF-EX14 P05	561 x 2264	0, 563
FF-EX14 P04	561 x 2264	0, 0

FIRST FLOOR TOTALS

Item	Value
Sheets / pieces	23 / 148
Yield / waste	89.6% / 6.92 m2
Saw cuts / shared / on stock edge	177 / 125 / 134

NOTES

1. Cut from PIR 120mm 1200x2400, 2mm saw kerf. Viewed on the face; dimensions from the sheet's bottom-left corner (0,0). Red numbered lines = saw cuts in order, each edge to edge.
2. Coloured dimensions belong to the part of that colour: its width and height, and its position from the sheet edges. Raked parts: corner coordinates at each corner.
3. Red hatch = waste. Labels = panel + piece mark on the manufacture drawing.

REVISIONS

REV	DATE	DESCRIPTION
C01	14.09.26	Construction issue
C02	14.09.26	Roof trusses revised; SP diagonals added
C03	11.10.26	FF windows coursed; steel + GP1 portal; steel drawings (ST)
C04	13.10.26	Steel approved by the engineer: steel + steel timber drawings issued for construction

TLS TIMBER FRAME
Design & Manufacture
Scan: 3D model + drawings

CLIENT	PROJECT
MP Adams	MP Adams Plot 4, Eckington


DRAWING TITLE
PIR CUTTING - FIRST FLOOR - SHEET 1 OF 23

PIR 120mm 1200x2400 | First Floor

SCALE	SIZE	DATE	DRAWN
NTS	A3	13.10.26	TS

STATUS	DRAWING No.	REV
CONSTRUCTION	P4-CP-PIR-02 / 01	C04

Do not scale. All dimensions in mm. Check all dimensions on site.

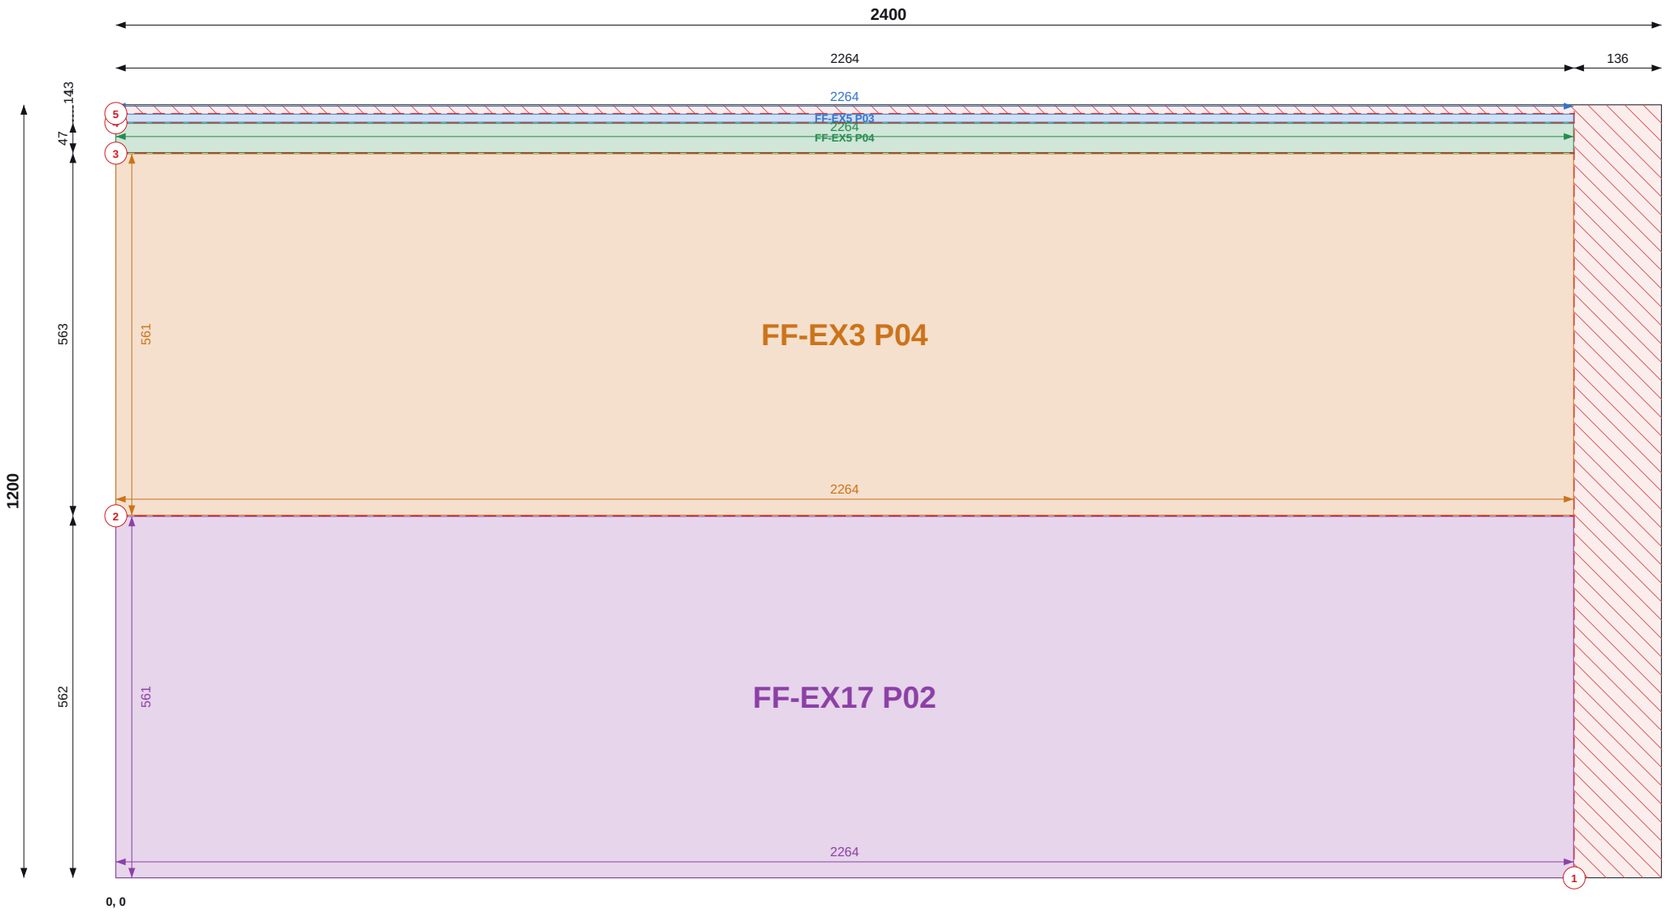

Top / left chains = saw cut positions (to cut centres). Coloured = part size and position.

SHEET 2 OF 23

THIS SHEET

Item	Value
Parts	4
Used / waste	92.7% / 0.21 m2
Reusable offcuts	0
Saw cuts / shared	5 / 3

PIECES (POSITION = BOTTOM-LEFT CORNER)

Label	Size	X, Y
FF-EX5 P03	12 x 2264	0, 1173
FF-EX5 P04	45 x 2264	0, 1126
FF-EX3 P04	561 x 2264	0, 563
FF-EX17 P02	561 x 2264	0, 0

NOTES

1. Cut from PIR 120mm 1200x2400, 2mm saw kerf. Viewed on the face; dimensions from the sheet's bottom-left corner (0,0). Red numbered lines = saw cuts in order, each edge to edge.
2. Coloured dimensions belong to the part of that colour: its width and height, and its position from the sheet edges. Raked parts: corner coordinates at each corner.
3. Red hatch = waste. Labels = panel + piece mark on the manufacture drawing.

REVISIONS

REV	DATE	DESCRIPTION
C01	14.09.26	Construction issue
C02	14.09.26	Roof trusses revised; SP diagonals added
C03	11.10.26	FF windows coursed; steel + GP1 portal; steel drawings (ST)
C04	13.10.26	Steel approved by the engineer: steel + steel timber drawings issued for construction

TLS TIMBER FRAME
Design & Manufacture
Scan: 3D model + drawings

CLIENT	PROJECT
MP Adams	MP Adams Plot 4, Eckington

DRAWING TITLE


PIR CUTTING - FIRST FLOOR - SHEET 2 OF 23

PIR 120mm 1200x2400 | First Floor

SCALE	SIZE	DATE	DRAWN
NTS	A3	13.10.26	TS

STATUS	DRAWING No.	REV
CONSTRUCTION	P4-CP-PIR-02 / 02	C04

Do not scale. All dimensions in mm. Check all dimensions on site.

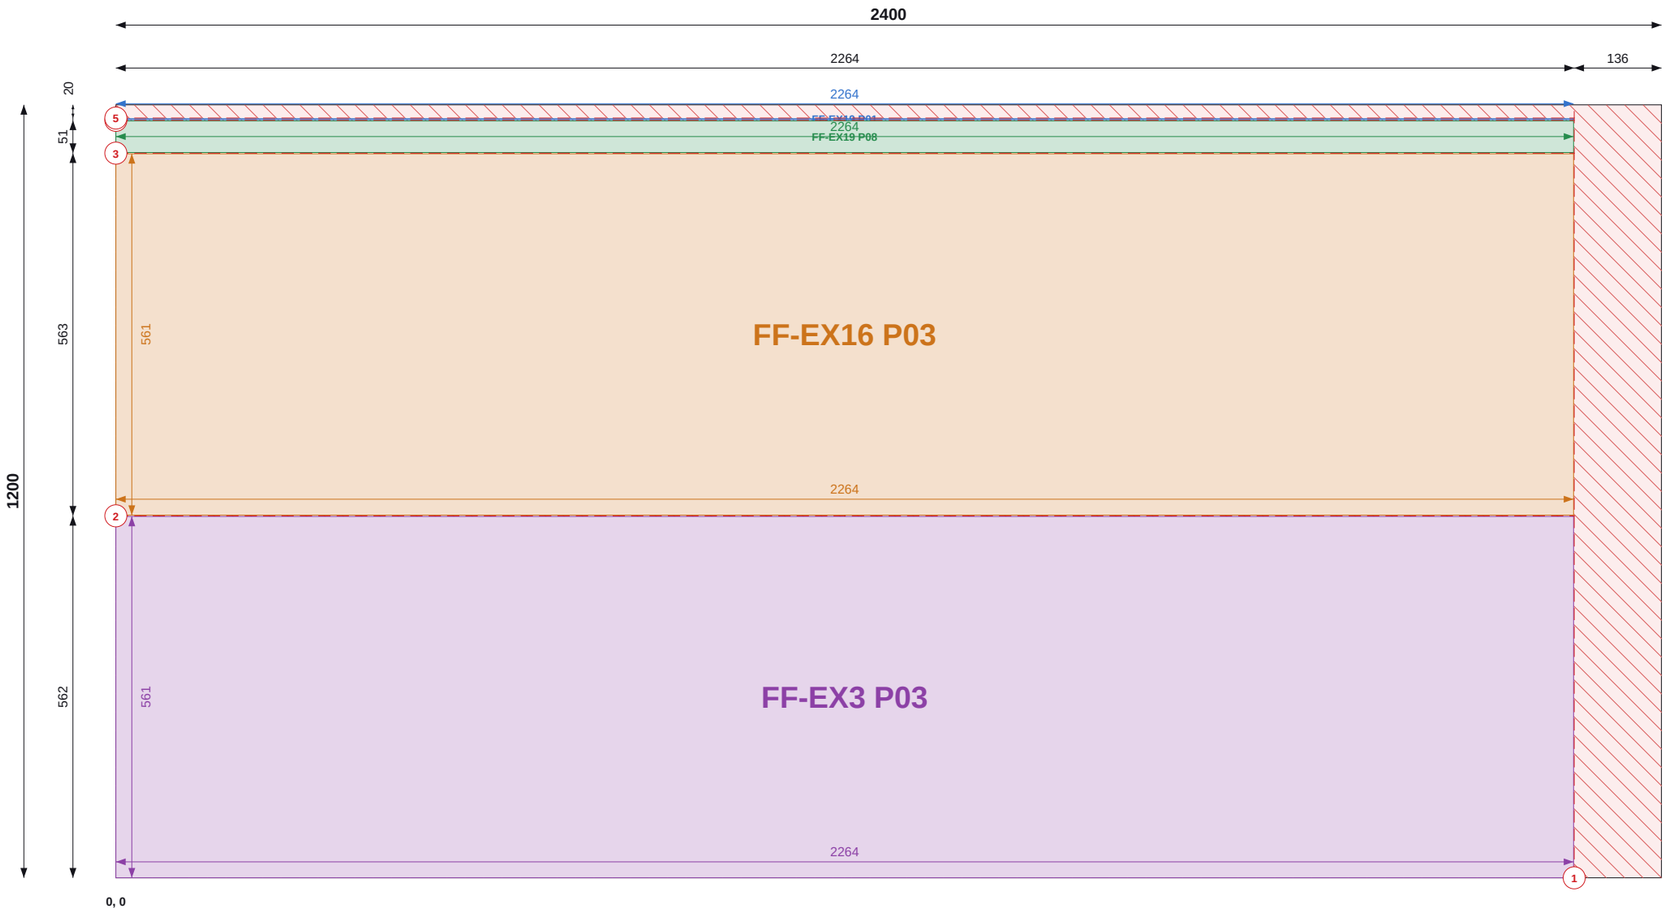

Top / left chains = saw cut positions (to cut centres). Coloured = part size and position.

SHEET 3 OF 23

THIS SHEET

Item	Value
Parts	4
Used / waste	92.2% / 0.23 m2
Reusable offcuts	0
Saw cuts / shared	5 / 3

PIECES (POSITION = BOTTOM-LEFT CORNER)

Label	Size	X, Y
FF-EX19 P01	1 x 2264	0, 1177
FF-EX19 P08	49 x 2264	0, 1126
FF-EX16 P03	561 x 2264	0, 563
FF-EX3 P03	561 x 2264	0, 0

NOTES

1. Cut from PIR 120mm 1200x2400, 2mm saw kerf. Viewed on the face; dimensions from the sheet's bottom-left corner (0,0). Red numbered lines = saw cuts in order, each edge to edge.
2. Coloured dimensions belong to the part of that colour: its width and height, and its position from the sheet edges. Raked parts: corner coordinates at each corner.
3. Red hatch = waste. Labels = panel + piece mark on the manufacture drawing.

REVISIONS

REV	DATE	DESCRIPTION
C01	14.09.26	Construction issue
C02	14.09.26	Roof trusses revised; SP diagonals added
C03	11.10.26	FF windows coursed; steel + GP1 portal; steel drawings (ST)
C04	13.10.26	Steel approved by the engineer: steel + steel timber drawings issued for construction

TLS TIMBER FRAME
Design & Manufacture
Scan: 3D model + drawings

CLIENT	PROJECT
MP Adams	MP Adams Plot 4, Eckington

DRAWING TITLE


PIR CUTTING - FIRST FLOOR - SHEET 3 OF 23

PIR 120mm 1200x2400 | First Floor

SCALE	SIZE	DATE	DRAWN
NTS	A3	13.10.26	TS

STATUS	DRAWING No.	REV
CONSTRUCTION	P4-CP-PIR-02 / 03	C04

Do not scale. All dimensions in mm. Check all dimensions on site.

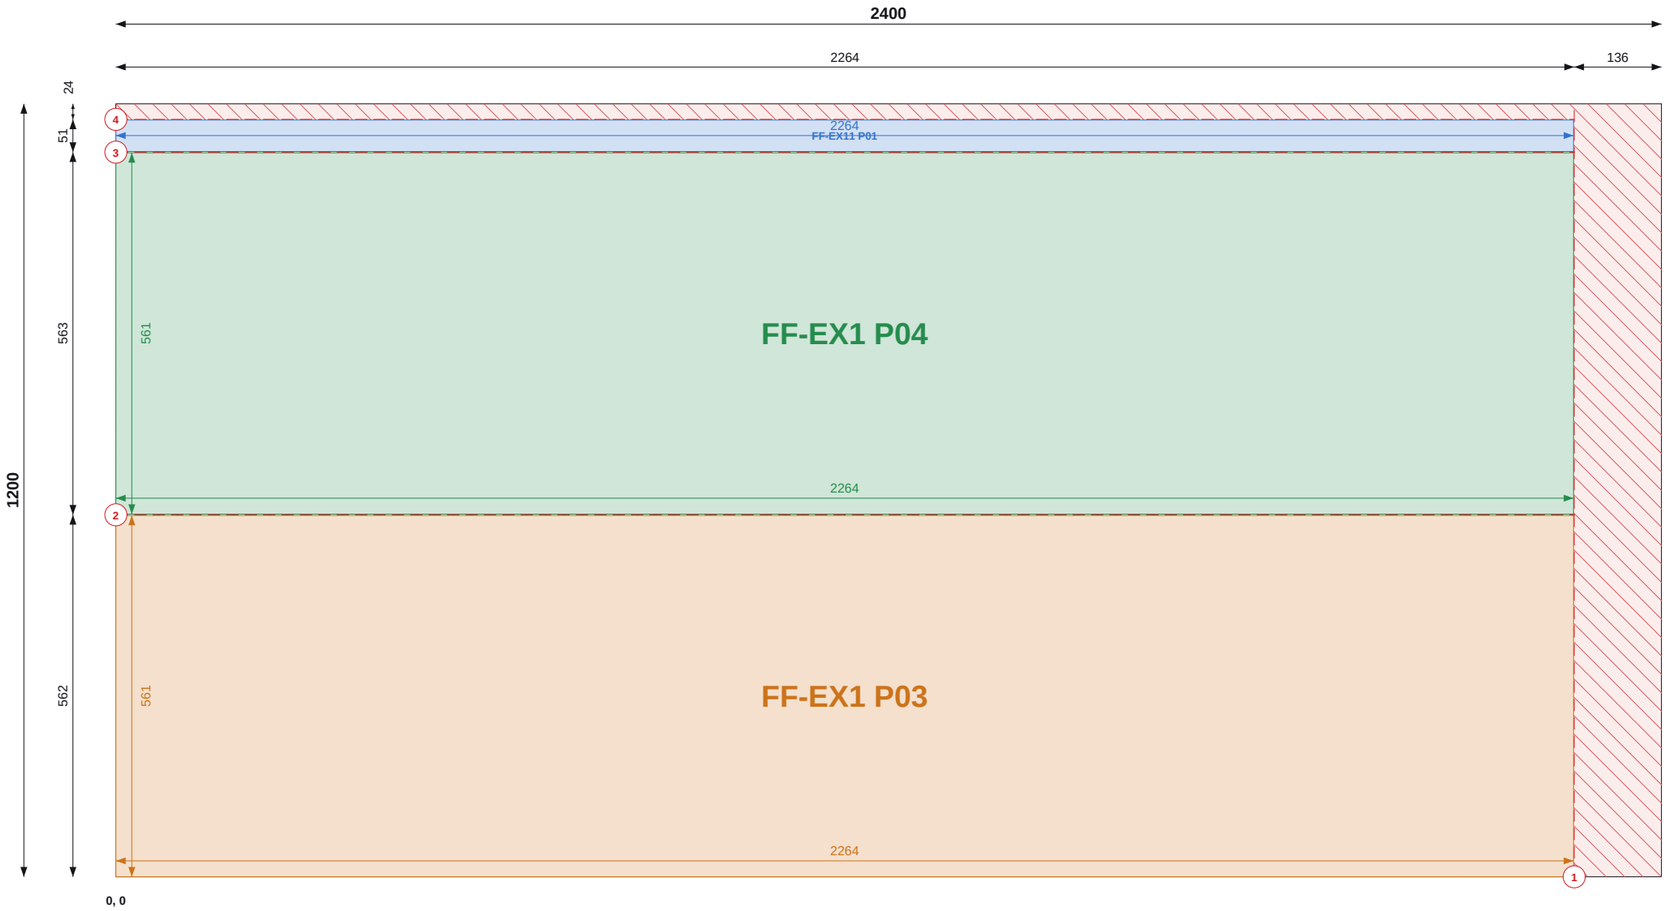

Top / left chains = saw cut positions (to cut centres). Coloured = part size and position.

SHEET 4 OF 23

THIS SHEET

Item	Value
Parts	3
Used / waste	92.0% / 0.23 m2
Reusable offcuts	0
Saw cuts / shared	4 / 2

PIECES (POSITION = BOTTOM-LEFT CORNER)

Label	Size	X, Y
FF-EX11 P01	49 x 2264	0, 1126
FF-EX1 P04	561 x 2264	0, 563
FF-EX1 P03	561 x 2264	0, 0

NOTES

1. Cut from PIR 120mm 1200x2400, 2mm saw kerf. Viewed on the face; dimensions from the sheet's bottom-left corner (0,0). Red numbered lines = saw cuts in order, each edge to edge.
2. Coloured dimensions belong to the part of that colour: its width and height, and its position from the sheet edges. Raked parts: corner coordinates at each corner.
3. Red hatch = waste. Labels = panel + piece mark on the manufacture drawing.

REVISIONS

REV	DATE	DESCRIPTION
C01	14.09.26	Construction issue
C02	14.09.26	Roof trusses revised; SP diagonals added
C03	11.10.26	FF windows coursed; steel + GP1 portal; steel drawings (ST)
C04	13.10.26	Steel approved by the engineer: steel + steel timber drawings issued for construction

TLS TIMBER FRAME
Design & Manufacture
Scan: 3D model + drawings

CLIENT	PROJECT
MP Adams	MP Adams Plot 4, Eckington

DRAWING TITLE


PIR CUTTING - FIRST FLOOR - SHEET 4 OF 23

PIR 120mm 1200x2400 | First Floor

SCALE	SIZE	DATE	DRAWN
NTS	A3	13.10.26	TS

STATUS	DRAWING No.	REV
CONSTRUCTION	P4-CP-PIR-02 / 04	C04

Do not scale. All dimensions in mm. Check all dimensions on site.

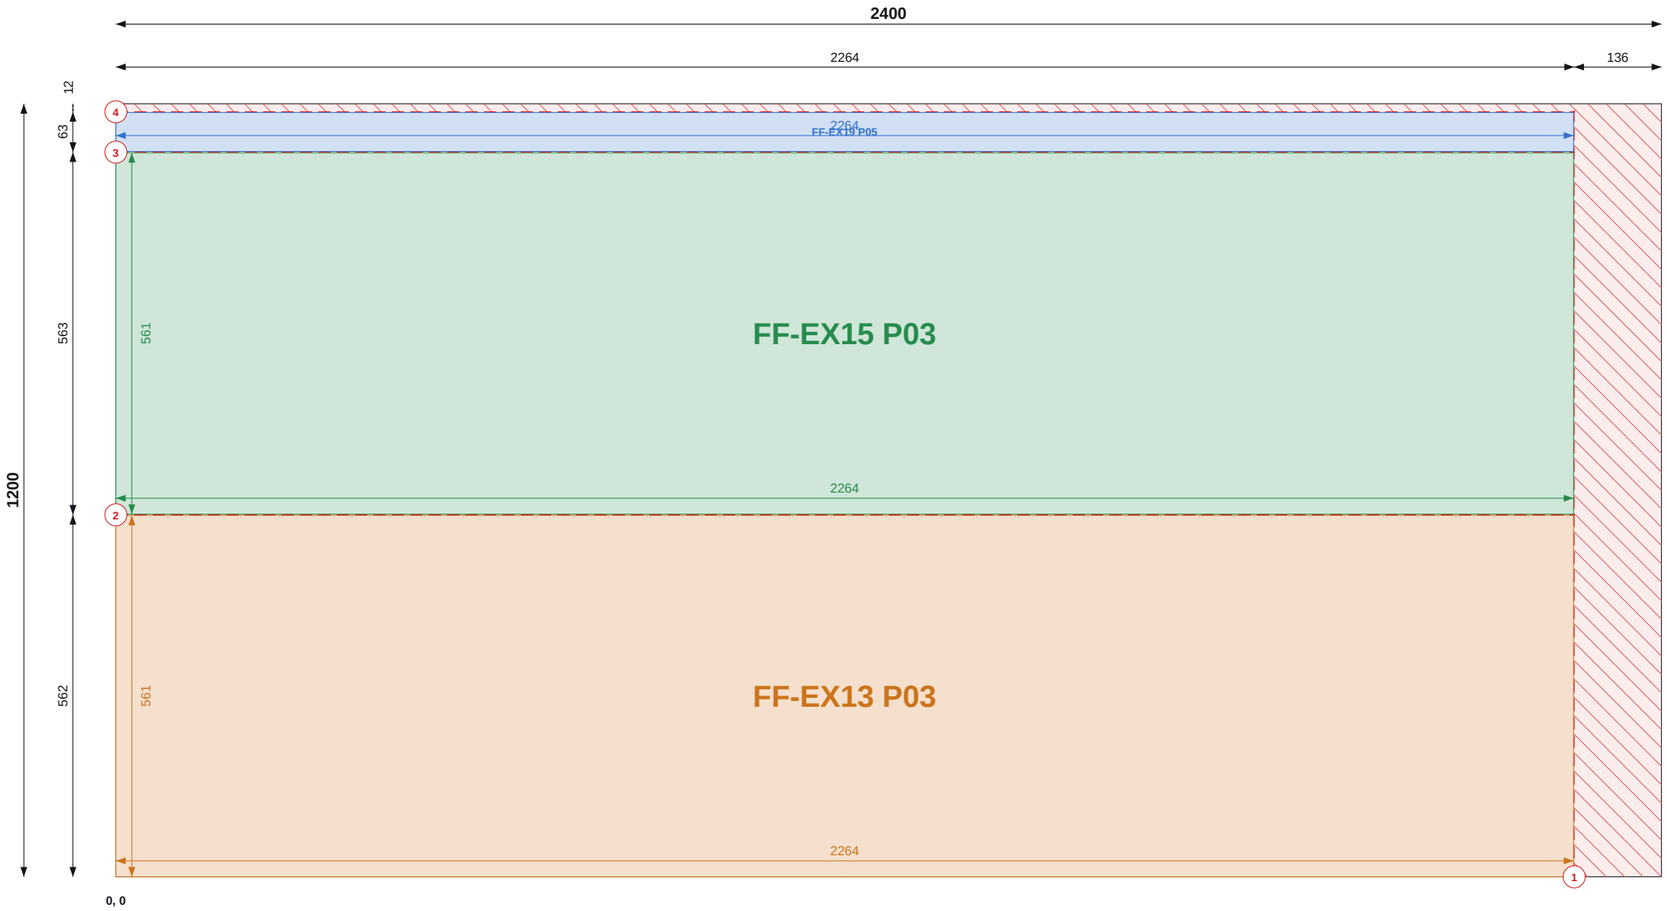

Top / left chains = saw cut positions (to cut centres). Coloured = part size and position.

SHEET 5 OF 23

THIS SHEET

Item	Value
Parts	3
Used / waste	92.9% / 0.20 m2
Reusable offcuts	0
Saw cuts / shared	4 / 2

PIECES (POSITION = BOTTOM-LEFT CORNER)

Label	Size	X, Y
FF-EX19 P05	61 x 2264	0, 1126
FF-EX15 P03	561 x 2264	0, 563
FF-EX13 P03	561 x 2264	0, 0

NOTES

1. Cut from PIR 120mm 1200x2400, 2mm saw kerf. Viewed on the face; dimensions from the sheet's bottom-left corner (0,0). Red numbered lines = saw cuts in order, each edge to edge.
2. Coloured dimensions belong to the part of that colour: its width and height, and its position from the sheet edges. Raked parts: corner coordinates at each corner.
3. Red hatch = waste. Labels = panel + piece mark on the manufacture drawing.

REVISIONS

REV	DATE	DESCRIPTION
C01	14.09.26	Construction issue
C02	14.09.26	Roof trusses revised; SP diagonals added
C03	11.10.26	FF windows coursed; steel + GP1 portal; steel drawings (ST)
C04	13.10.26	Steel approved by the engineer: steel + steel timber drawings issued for construction

TLS TIMBER FRAME
Design & Manufacture
Scan: 3D model + drawings

CLIENT	PROJECT
MP Adams	MP Adams Plot 4, Eckington


DRAWING TITLE
PIR CUTTING - FIRST FLOOR - SHEET 5 OF 23

PIR 120mm 1200x2400 | First Floor

SCALE	SIZE	DATE	DRAWN
NTS	A3	13.10.26	TS

STATUS	DRAWING No.	REV
CONSTRUCTION	P4-CP-PIR-02 / 05	C04

Do not scale. All dimensions in mm. Check all dimensions on site.

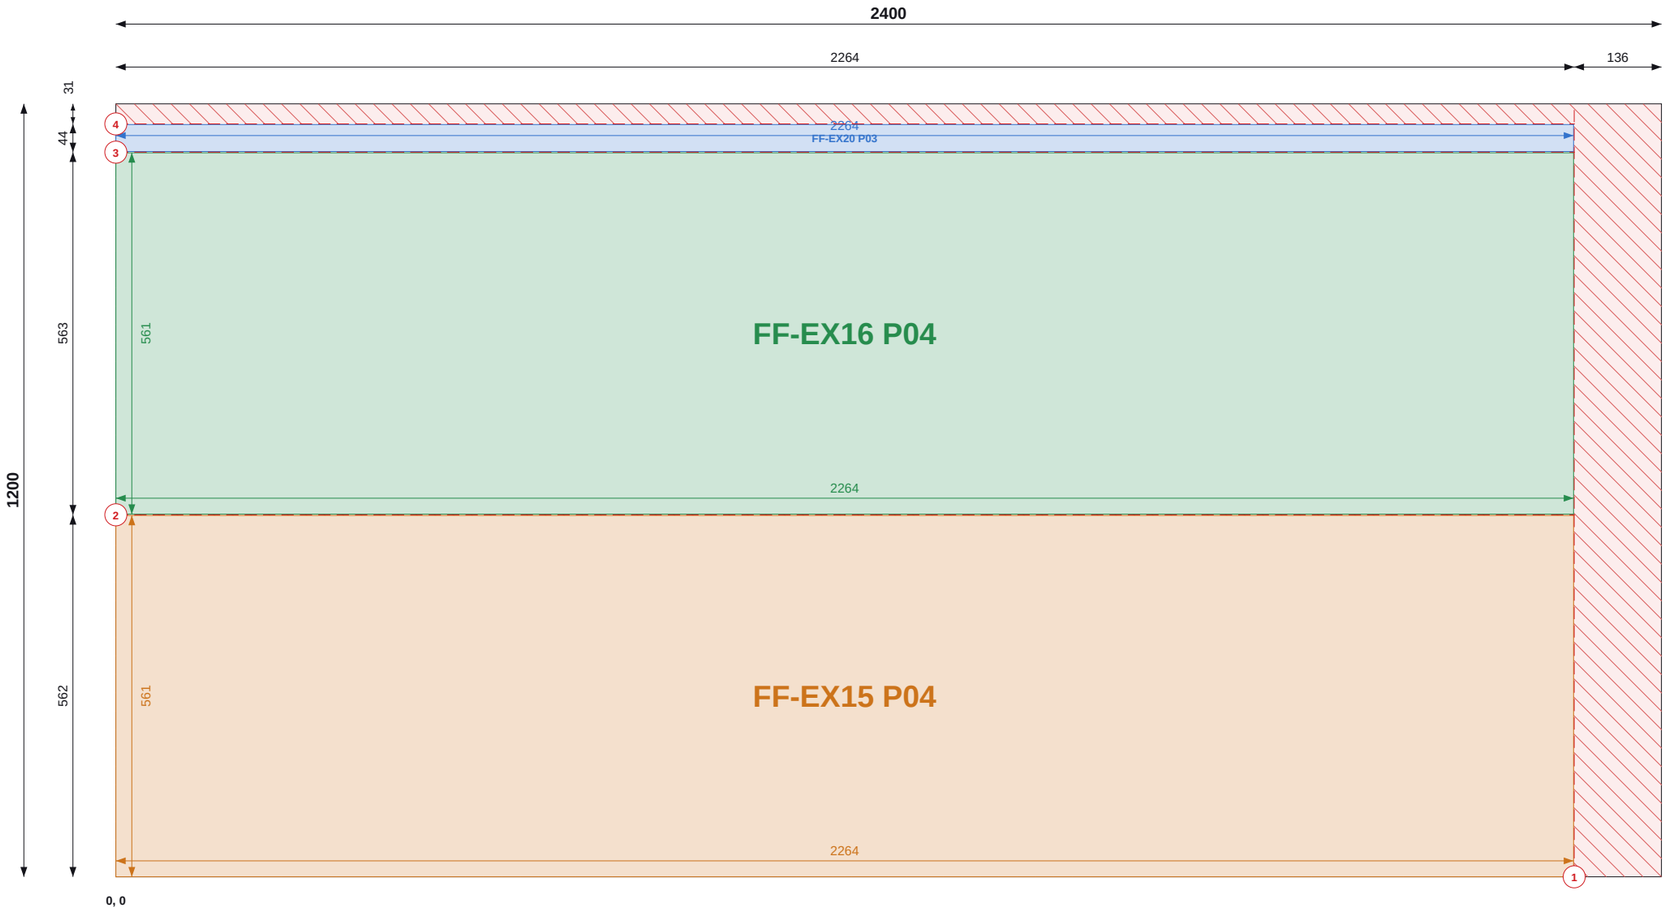

Top / left chains = saw cut positions (to cut centres). Coloured = part size and position.

SHEET 6 OF 23

THIS SHEET

Item	Value
Parts	3
Used / waste	91.5% / 0.25 m2
Reusable offcuts	0
Saw cuts / shared	4 / 2

PIECES (POSITION = BOTTOM-LEFT CORNER)

Label	Size	X, Y
FF-EX20 P03	42 x 2264	0, 1126
FF-EX16 P04	561 x 2264	0, 563
FF-EX15 P04	561 x 2264	0, 0

NOTES

1. Cut from PIR 120mm 1200x2400, 2mm saw kerf. Viewed on the face; dimensions from the sheet's bottom-left corner (0,0). Red numbered lines = saw cuts in order, each edge to edge.
2. Coloured dimensions belong to the part of that colour: its width and height, and its position from the sheet edges. Raked parts: corner coordinates at each corner.
3. Red hatch = waste. Labels = panel + piece mark on the manufacture drawing.

REVISIONS

REV	DATE	DESCRIPTION
C01	14.09.26	Construction issue
C02	14.09.26	Roof trusses revised; SP diagonals added
C03	11.10.26	FF windows coursed; steel + GP1 portal; steel drawings (ST)
C04	13.10.26	Steel approved by the engineer: steel + steel timber drawings issued for construction

TLS TIMBER FRAME
Design & Manufacture
Scan: 3D model + drawings

CLIENT	PROJECT
MP Adams	MP Adams Plot 4, Eckington

DRAWING TITLE


PIR CUTTING - FIRST FLOOR - SHEET 6 OF 23

PIR 120mm 1200x2400 | First Floor

SCALE	SIZE	DATE	DRAWN
NTS	A3	13.10.26	TS

STATUS	DRAWING No.	REV
CONSTRUCTION	P4-CP-PIR-02 / 06	C04

Do not scale. All dimensions in mm. Check all dimensions on site.

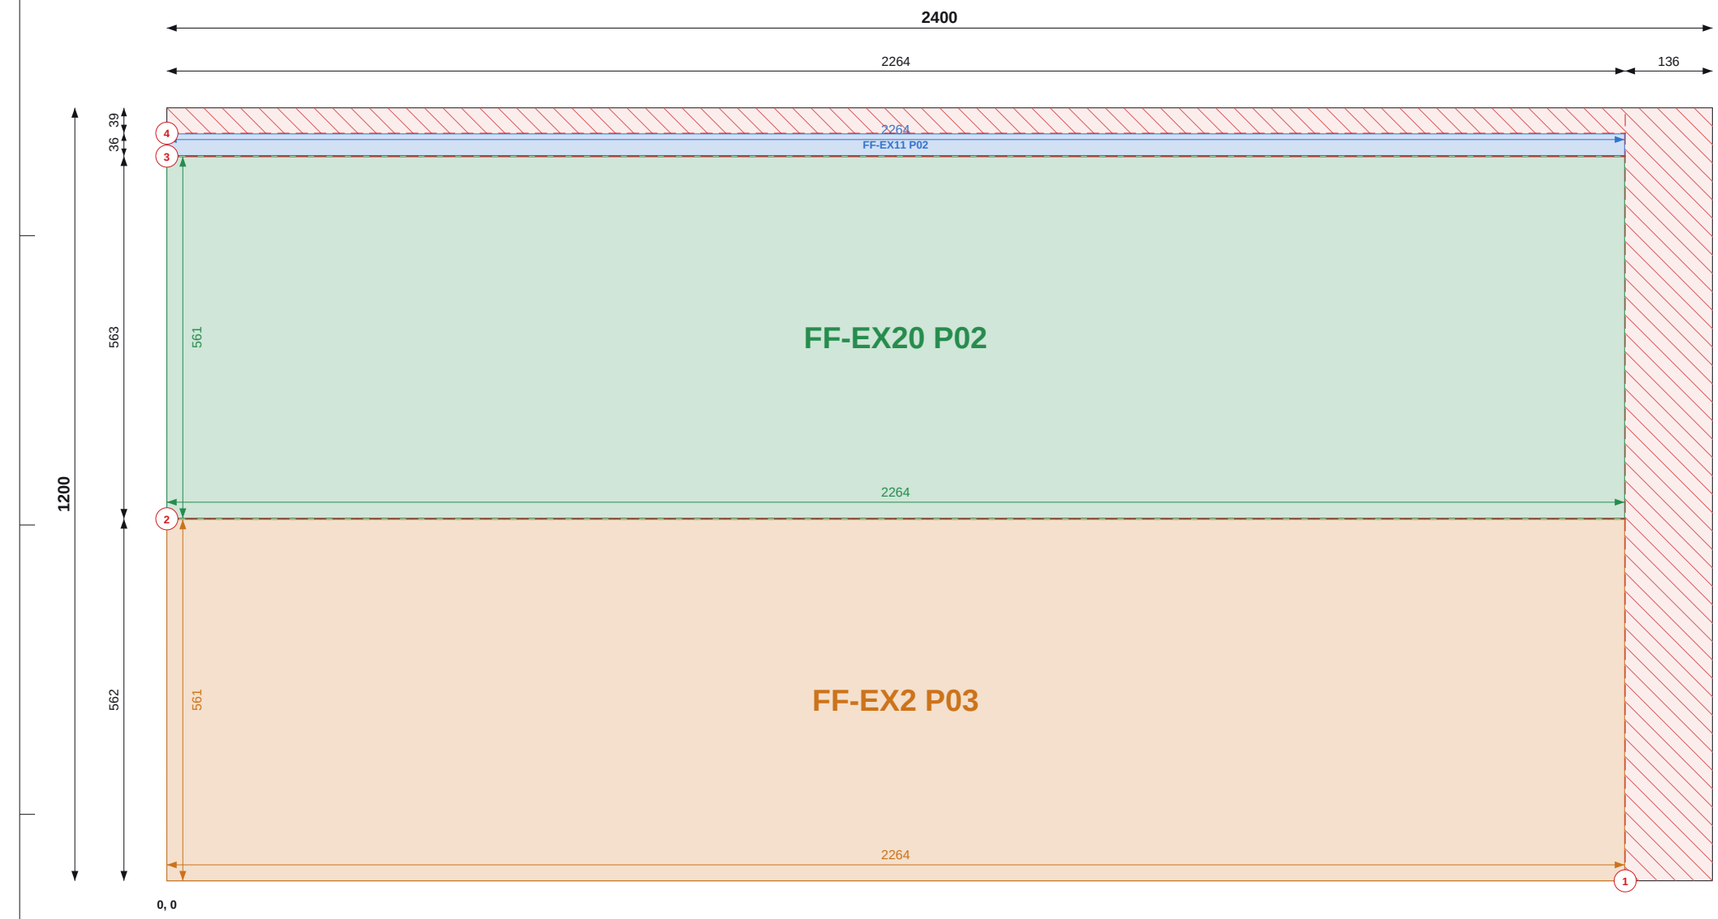

Top / left chains = saw cut positions (to cut centres). Coloured = part size and position.

SHEET 7 OF 23

THIS SHEET

Item	Value
Parts	3
Used / waste	90.8% / 0.26 m2
Reusable offcuts	0
Saw cuts / shared	4 / 2

PIECES (POSITION = BOTTOM-LEFT CORNER)

Label	Size	X, Y
FF-EX11 P02	34 x 2264	0, 1126
FF-EX20 P02	561 x 2264	0, 563
FF-EX2 P03	561 x 2264	0, 0

NOTES

1. Cut from PIR 120mm 1200x2400, 2mm saw kerf. Viewed on the face; dimensions from the sheet's bottom-left corner (0,0). Red numbered lines = saw cuts in order, each edge to edge.
2. Coloured dimensions belong to the part of that colour: its width and height, and its position from the sheet edges. Raked parts: corner coordinates at each corner.
3. Red hatch = waste. Labels = panel + piece mark on the manufacture drawing.

REVISIONS

REV	DATE	DESCRIPTION
C01	14.09.26	Construction issue
C02	14.09.26	Roof trusses revised; SP diagonals added
C03	11.10.26	FF windows coursed; steel + GP1 portal; steel drawings (ST)
C04	13.10.26	Steel approved by the engineer: steel + steel timber drawings issued for construction

TLS TIMBER FRAME
Design & Manufacture
Scan: 3D model + drawings

CLIENT	PROJECT
MP Adams	MP Adams Plot 4, Eckington

DRAWING TITLE


PIR CUTTING - FIRST FLOOR - SHEET 7 OF 23

PIR 120mm 1200x2400 | First Floor

SCALE	SIZE	DATE	DRAWN
NTS	A3	13.10.26	TS

STATUS	DRAWING No.	REV
CONSTRUCTION	P4-CP-PIR-02 / 07	C04

Do not scale. All dimensions in mm. Check all dimensions on site.

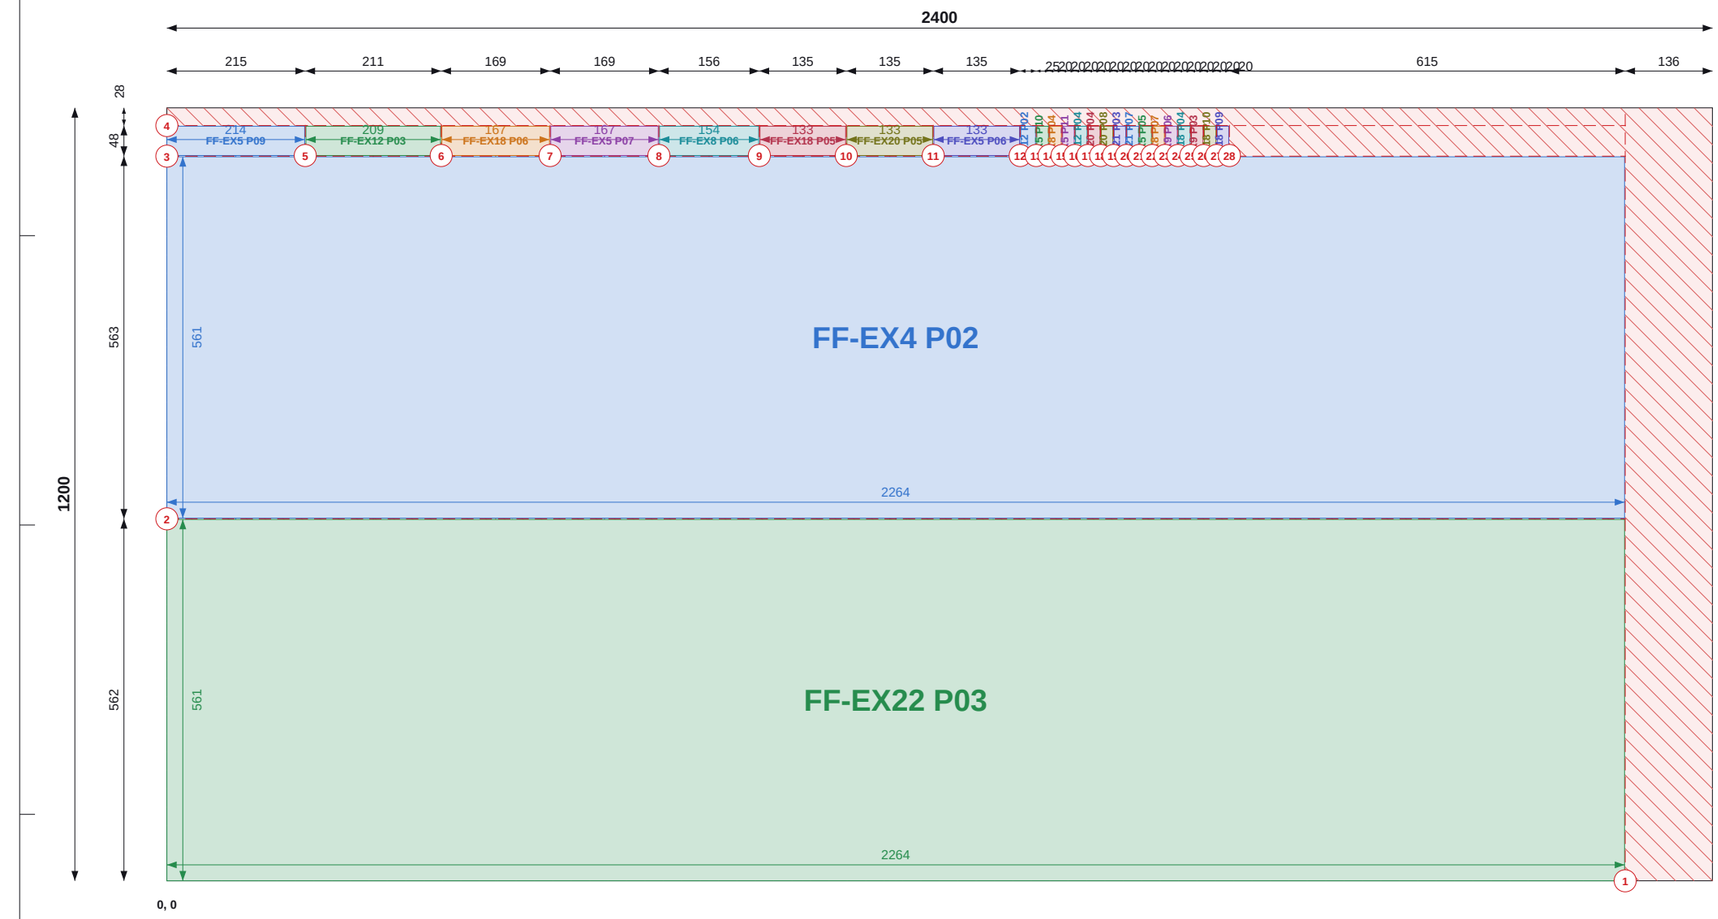

Top / left chains = saw cut positions (to cut centres). Coloured = part size and position.

Do not scale. All dimensions in mm. Check all dimensions on site.

SHEET 8 OF 23

THIS SHEET

Item	Value
Parts	26
Used / waste	90.7% / 0.27 m2
Reusable offcuts	0
Saw cuts / shared	28 / 25

PIECES (POSITION = BOTTOM-LEFT CORNER)

Label	Size	X, Y
FF-EX5 P09	214 x 46	0, 1126
FF-EX12 P03	209 x 46	216, 1126
FF-EX18 P06	167 x 46	427, 1126
FF-EX5 P07	167 x 46	596, 1126
FF-EX8 P06	154 x 46	765, 1126
FF-EX18 P05	133 x 46	921, 1126
FF-EX20 P05	133 x 46	1056, 1126
FF-EX5 P06	133 x 46	1191, 1126
FF-EX12 P02	23 x 46	1326, 1126
FF-EX5 P10	18 x 46	1351, 1126
FF-EX8 P04	18 x 46	1371, 1126
FF-EX5 P11	18 x 46	1391, 1126
FF-EX12 P04	18 x 46	1411, 1126
FF-EX20 P04	18 x 46	1431, 1126
FF-EX20 P08	18 x 46	1451, 1126
FF-EX21 P03	18 x 46	1471, 1126
FF-EX21 P07	18 x 46	1491, 1126
FF-EX5 P05	18 x 46	1511, 1126
FF-EX8 P07	18 x 46	1531, 1126
FF-EX9 P06	18 x 46	1551, 1126
FF-EX18 P04	18 x 46	1571, 1126
FF-EX9 P03	18 x 46	1591, 1126
FF-EX18 P10	18 x 46	1611, 1126
FF-EX18 P09	18 x 46	1631, 1126
FF-EX4 P02	561 x 2264	0, 563
FF-EX22 P03	561 x 2264	0, 0

NOTES

1. Cut from PIR 120mm 1200x2400, 2mm saw kerf. Viewed on the face; dimensions from the sheet's bottom-left corner (0,0). Red numbered lines = saw cuts in order, each edge to edge.
2. Coloured dimensions belong to the part of that colour: its width and height, and its position from the sheet edges. Raked parts: corner coordinates at each corner.
3. Red hatch = waste. Labels = panel + piece mark on the manufacture drawing.

REVISIONS

REV	DATE	DESCRIPTION
C01	14.09.26	Construction issue
C02	14.09.26	Roof trusses revised; SP diagonals added
C03	11.10.26	FF windows coursed; steel + GP1 portal; steel drawings (ST)
C04	13.10.26	Steel approved by the engineer: steel + steel timber drawings issued for construction

TLS TIMBER FRAME
Design & Manufacture
Scan: 3D model + drawings


CLIENT	PROJECT
MP Adams	MP Adams Plot 4, Eckington

DRAWING TITLE
PIR CUTTING - FIRST FLOOR - SHEET 8 OF 23

PIR 120mm 1200x2400 | First Floor

SCALE	SIZE	DATE	DRAWN
NTS	A3	13.10.26	TS

STATUS	DRAWING No.	REV
CONSTRUCTION	P4-CP-PIR-02 / 08	C04

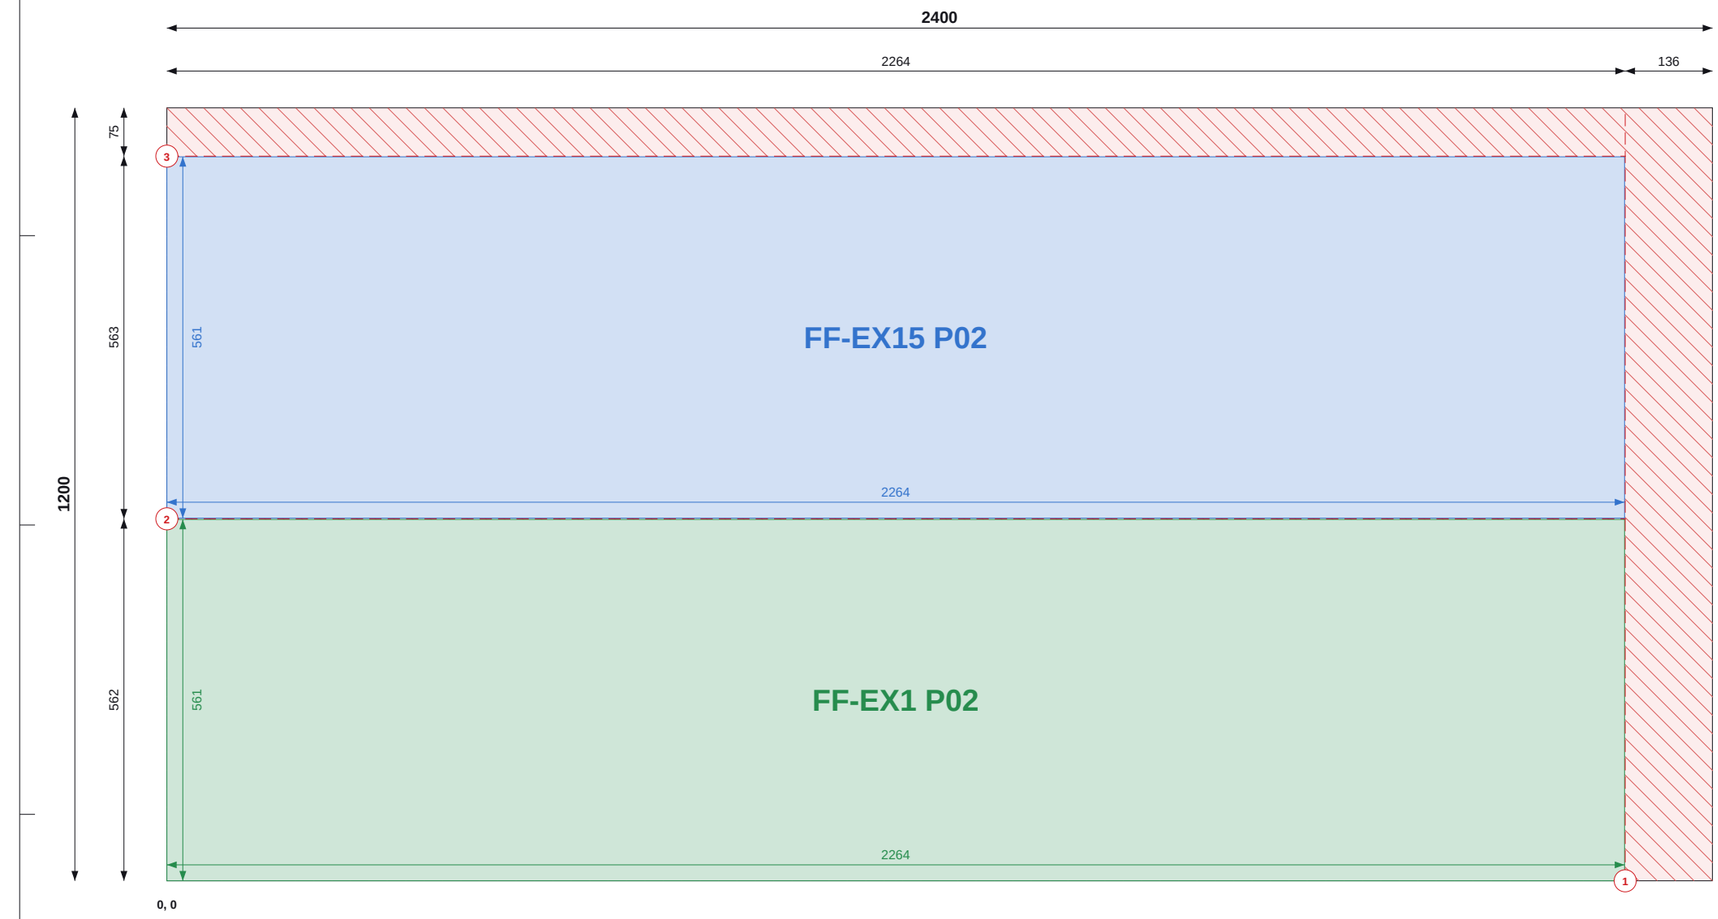

Top / left chains = saw cut positions (to cut centres). Coloured = part size and position.

SHEET 9 OF 23

THIS SHEET

Item	Value
Parts	2
Used / waste	88.2% / 0.34 m2
Reusable offcuts	0
Saw cuts / shared	3 / 1

PIECES (POSITION = BOTTOM-LEFT CORNER)

Label	Size	X, Y
FF-EX15 P02	561 x 2264	0, 563
FF-EX1 P02	561 x 2264	0, 0

NOTES

1. Cut from PIR 120mm 1200x2400, 2mm saw kerf. Viewed on the face; dimensions from the sheet's bottom-left corner (0,0). Red numbered lines = saw cuts in order, each edge to edge.
2. Coloured dimensions belong to the part of that colour: its width and height, and its position from the sheet edges. Raked parts: corner coordinates at each corner.
3. Red hatch = waste. Labels = panel + piece mark on the manufacture drawing.

REVISIONS

REV	DATE	DESCRIPTION
C01	14.09.26	Construction issue
C02	14.09.26	Roof trusses revised; SP diagonals added
C03	11.10.26	FF windows coursed; steel + GP1 portal; steel drawings (ST)
C04	13.10.26	Steel approved by the engineer: steel + steel timber drawings issued for construction

TLS TIMBER FRAME
Design & Manufacture
Scan: 3D model + drawings

CLIENT	PROJECT
MP Adams	MP Adams Plot 4, Eckington


DRAWING TITLE
PIR CUTTING - FIRST FLOOR - SHEET 9 OF 23

PIR 120mm 1200x2400 | First Floor

SCALE	SIZE	DATE	DRAWN
NTS	A3	13.10.26	TS

STATUS	DRAWING No.	REV
CONSTRUCTION	P4-CP-PIR-02 / 09	C04

Do not scale. All dimensions in mm. Check all dimensions on site.

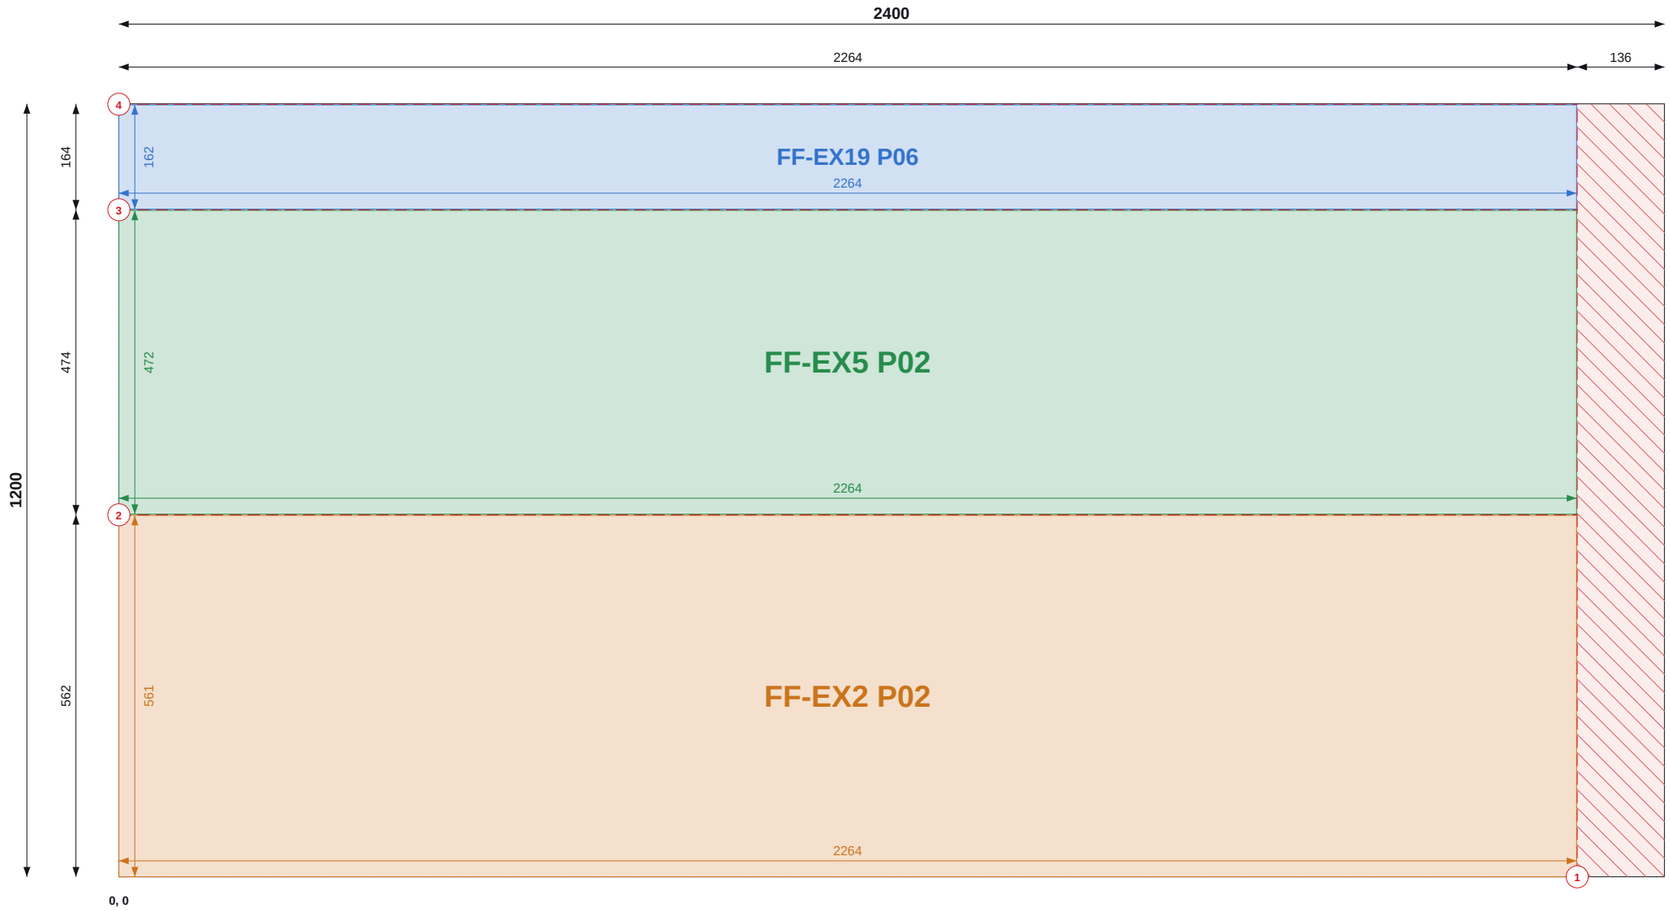

Top / left chains = saw cut positions (to cut centres). Coloured = part size and position.

SHEET 10 OF 23

THIS SHEET

Item	Value
Parts	3
Used / waste	93.9% / 0.18 m2
Reusable offcuts	0
Saw cuts / shared	4 / 2

PIECES (POSITION = BOTTOM-LEFT CORNER)

Label	Size	X, Y
FF-EX19 P06	162 x 2264	0, 1037
FF-EX5 P02	472 x 2264	0, 563
FF-EX2 P02	561 x 2264	0, 0

NOTES

1. Cut from PIR 120mm 1200x2400, 2mm saw kerf. Viewed on the face; dimensions from the sheet's bottom-left corner (0,0). Red numbered lines = saw cuts in order, each edge to edge.
2. Coloured dimensions belong to the part of that colour: its width and height, and its position from the sheet edges. Raked parts: corner coordinates at each corner.
3. Red hatch = waste. Labels = panel + piece mark on the manufacture drawing.

REVISIONS

REV	DATE	DESCRIPTION
C01	14.09.26	Construction issue
C02	14.09.26	Roof trusses revised; SP diagonals added
C03	11.10.26	FF windows coursed; steel + GP1 portal; steel drawings (ST)
C04	13.10.26	Steel approved by the engineer: steel + steel timber drawings issued for construction

TLS TIMBER FRAME
Design & Manufacture
Scan: 3D model + drawings

CLIENT	PROJECT
MP Adams	MP Adams Plot 4, Eckington


DRAWING TITLE
PIR CUTTING - FIRST FLOOR - SHEET 10 OF 23

PIR 120mm 1200x2400 | First Floor

SCALE	SIZE	DATE	DRAWN
NTS	A3	13.10.26	TS

STATUS	DRAWING No.	REV
CONSTRUCTION	P4-CP-PIR-02 / 10	C04

Do not scale. All dimensions in mm. Check all dimensions on site.

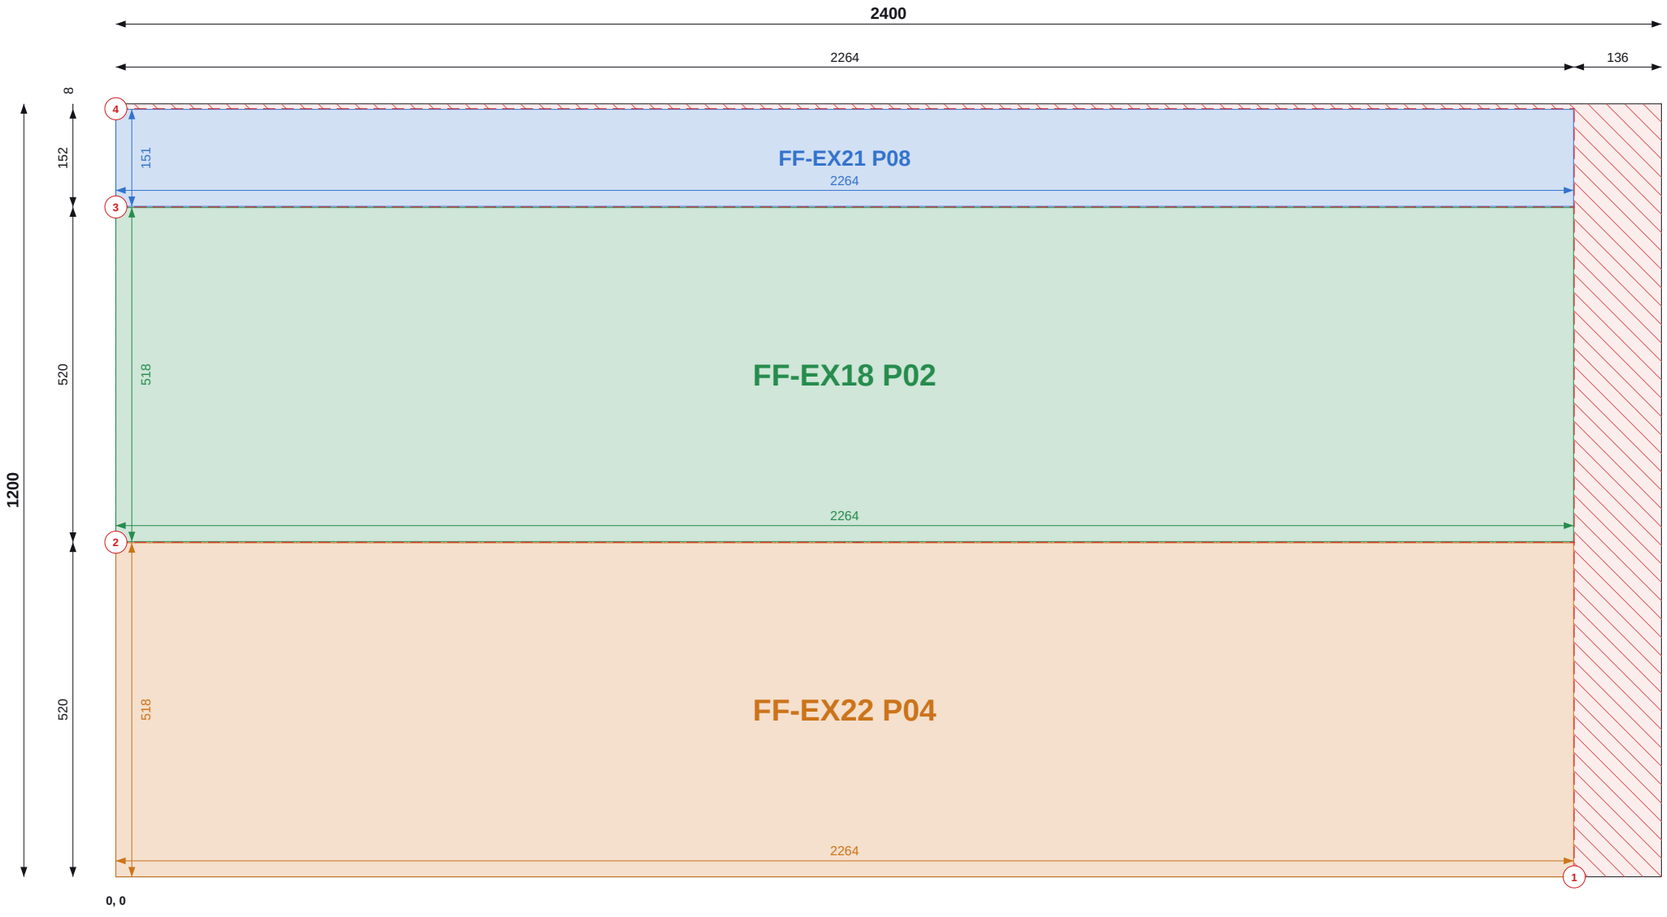

Top / left chains = saw cut positions (to cut centres). Coloured = part size and position.

SHEET 11 OF 23

THIS SHEET

Item	Value
Parts	3
Used / waste	93.3% / 0.19 m2
Reusable offcuts	0
Saw cuts / shared	4 / 2

PIECES (POSITION = BOTTOM-LEFT CORNER)

Label	Size	X, Y
FF-EX21 P08	151 x 2264	0, 1041
FF-EX18 P02	518 x 2264	0, 520
FF-EX22 P04	518 x 2264	0, 0

NOTES

1. Cut from PIR 120mm 1200x2400, 2mm saw kerf. Viewed on the face; dimensions from the sheet's bottom-left corner (0,0). Red numbered lines = saw cuts in order, each edge to edge.
2. Coloured dimensions belong to the part of that colour: its width and height, and its position from the sheet edges. Raked parts: corner coordinates at each corner.
3. Red hatch = waste. Labels = panel + piece mark on the manufacture drawing.

REVISIONS

REV	DATE	DESCRIPTION
C01	14.09.26	Construction issue
C02	14.09.26	Roof trusses revised; SP diagonals added
C03	11.10.26	FF windows coursed; steel + GP1 portal; steel drawings (ST)
C04	13.10.26	Steel approved by the engineer: steel + steel timber drawings issued for construction

TLS TIMBER FRAME
Design & Manufacture
Scan: 3D model + drawings

CLIENT	PROJECT
MP Adams	MP Adams Plot 4, Eckington

DRAWING TITLE


PIR CUTTING - FIRST FLOOR - SHEET 11 OF 23

PIR 120mm 1200x2400 | First Floor

SCALE	SIZE	DATE	DRAWN
NTS	A3	13.10.26	TS

STATUS	DRAWING No.	REV
CONSTRUCTION	P4-CP-PIR-02 / 11	C04

Do not scale. All dimensions in mm. Check all dimensions on site.

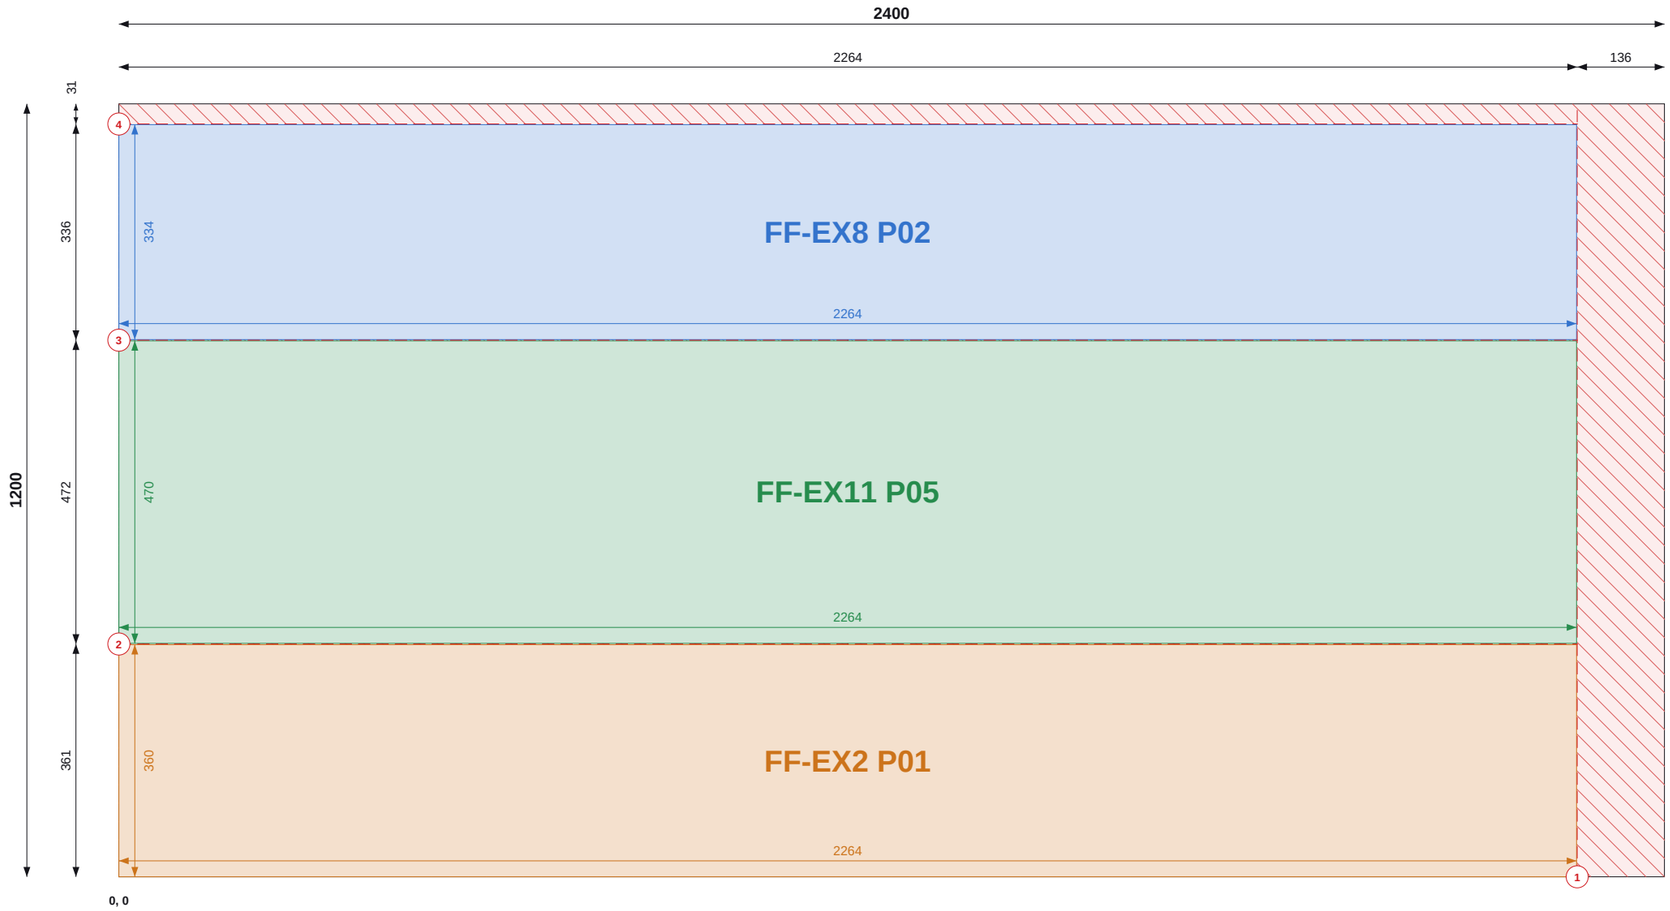

Top / left chains = saw cut positions (to cut centres). Coloured = part size and position.

SHEET 12 OF 23

THIS SHEET

Item	Value
Parts	3
Used / waste	91.5% / 0.25 m2
Reusable offcuts	0
Saw cuts / shared	4 / 2

PIECES (POSITION = BOTTOM-LEFT CORNER)

Label	Size	X, Y
FF-EX8 P02	334 x 2264	0, 834
FF-EX11 P05	470 x 2264	0, 362
FF-EX2 P01	360 x 2264	0, 0

NOTES

1. Cut from PIR 120mm 1200x2400, 2mm saw kerf. Viewed on the face; dimensions from the sheet's bottom-left corner (0,0). Red numbered lines = saw cuts in order, each edge to edge.
2. Coloured dimensions belong to the part of that colour: its width and height, and its position from the sheet edges. Raked parts: corner coordinates at each corner.
3. Red hatch = waste. Labels = panel + piece mark on the manufacture drawing.

REVISIONS

REV	DATE	DESCRIPTION
C01	14.09.26	Construction issue
C02	14.09.26	Roof trusses revised; SP diagonals added
C03	11.10.26	FF windows coursed; steel + GP1 portal; steel drawings (ST)
C04	13.10.26	Steel approved by the engineer: steel + steel timber drawings issued for construction

TLS TIMBER FRAME
Design & Manufacture
Scan: 3D model + drawings

CLIENT	PROJECT
MP Adams	MP Adams Plot 4, Eckington


DRAWING TITLE
PIR CUTTING - FIRST FLOOR - SHEET 12 OF 23

PIR 120mm 1200x2400 | First Floor

SCALE	SIZE	DATE	DRAWN
NTS	A3	13.10.26	TS

STATUS	DRAWING No.	REV
CONSTRUCTION	P4-CP-PIR-02 / 12	C04

Do not scale. All dimensions in mm. Check all dimensions on site.

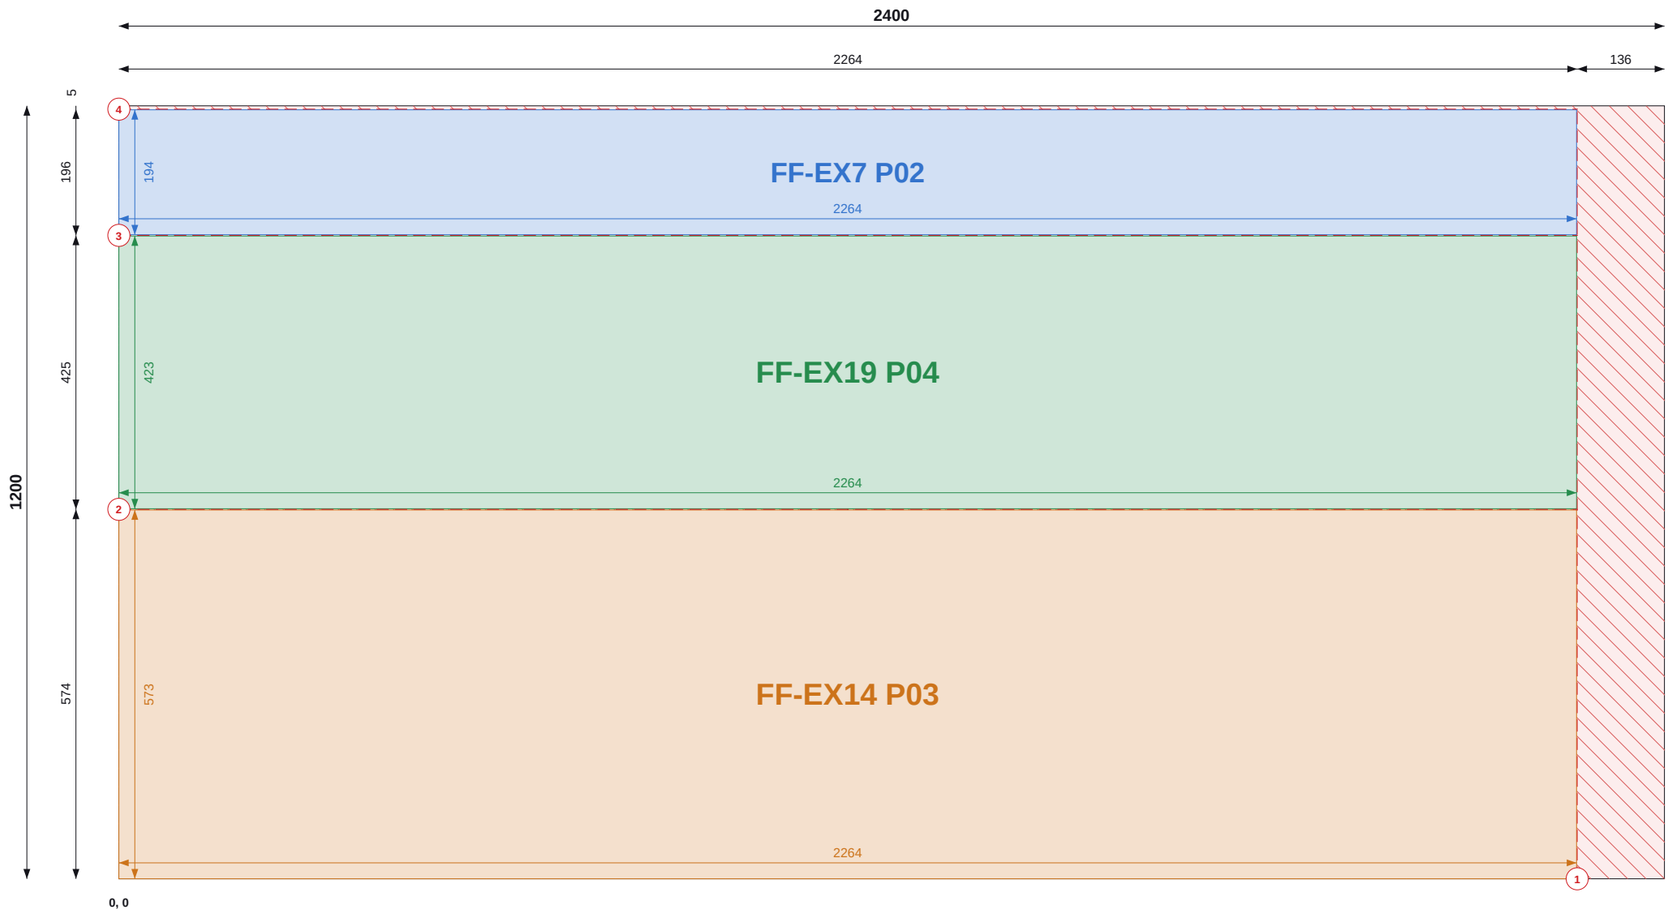

Top / left chains = saw cut positions (to cut centres). Coloured = part size and position.

SHEET 13 OF 23

THIS SHEET

Item	Value
Parts	3
Used / waste	93.5% / 0.19 m2
Reusable offcuts	0
Saw cuts / shared	4 / 2

PIECES (POSITION = BOTTOM-LEFT CORNER)

Label	Size	X, Y
FF-EX7 P02	194 x 2264	0, 1000
FF-EX19 P04	423 x 2264	0, 575
FF-EX14 P03	573 x 2264	0, 0

NOTES

1. Cut from PIR 120mm 1200x2400, 2mm saw kerf. Viewed on the face; dimensions from the sheet's bottom-left corner (0,0). Red numbered lines = saw cuts in order, each edge to edge.
2. Coloured dimensions belong to the part of that colour: its width and height, and its position from the sheet edges. Raked parts: corner coordinates at each corner.
3. Red hatch = waste. Labels = panel + piece mark on the manufacture drawing.

REVISIONS

REV	DATE	DESCRIPTION
C01	14.09.26	Construction issue
C02	14.09.26	Roof trusses revised; SP diagonals added
C03	11.10.26	FF windows coursed; steel + GP1 portal; steel drawings (ST)
C04	13.10.26	Steel approved by the engineer: steel + steel timber drawings issued for constructio

TLS TIMBER FRAME
Design & Manufacture
Scan: 3D model + drawings

CLIENT	PROJECT
MP Adams	MP Adams Plot 4, Eckington

DRAWING TITLE


PIR CUTTING - FIRST FLOOR - SHEET 13 OF 23

PIR 120mm 1200x2400 | First Floor

SCALE	SIZE	DATE	DRAWN
NTS	A3	13.10.26	TS

STATUS	DRAWING No.	REV
CONSTRUCTION	P4-CP-PIR-02 / 13	C04

Do not scale. All dimensions in mm. Check all dimensions on site.

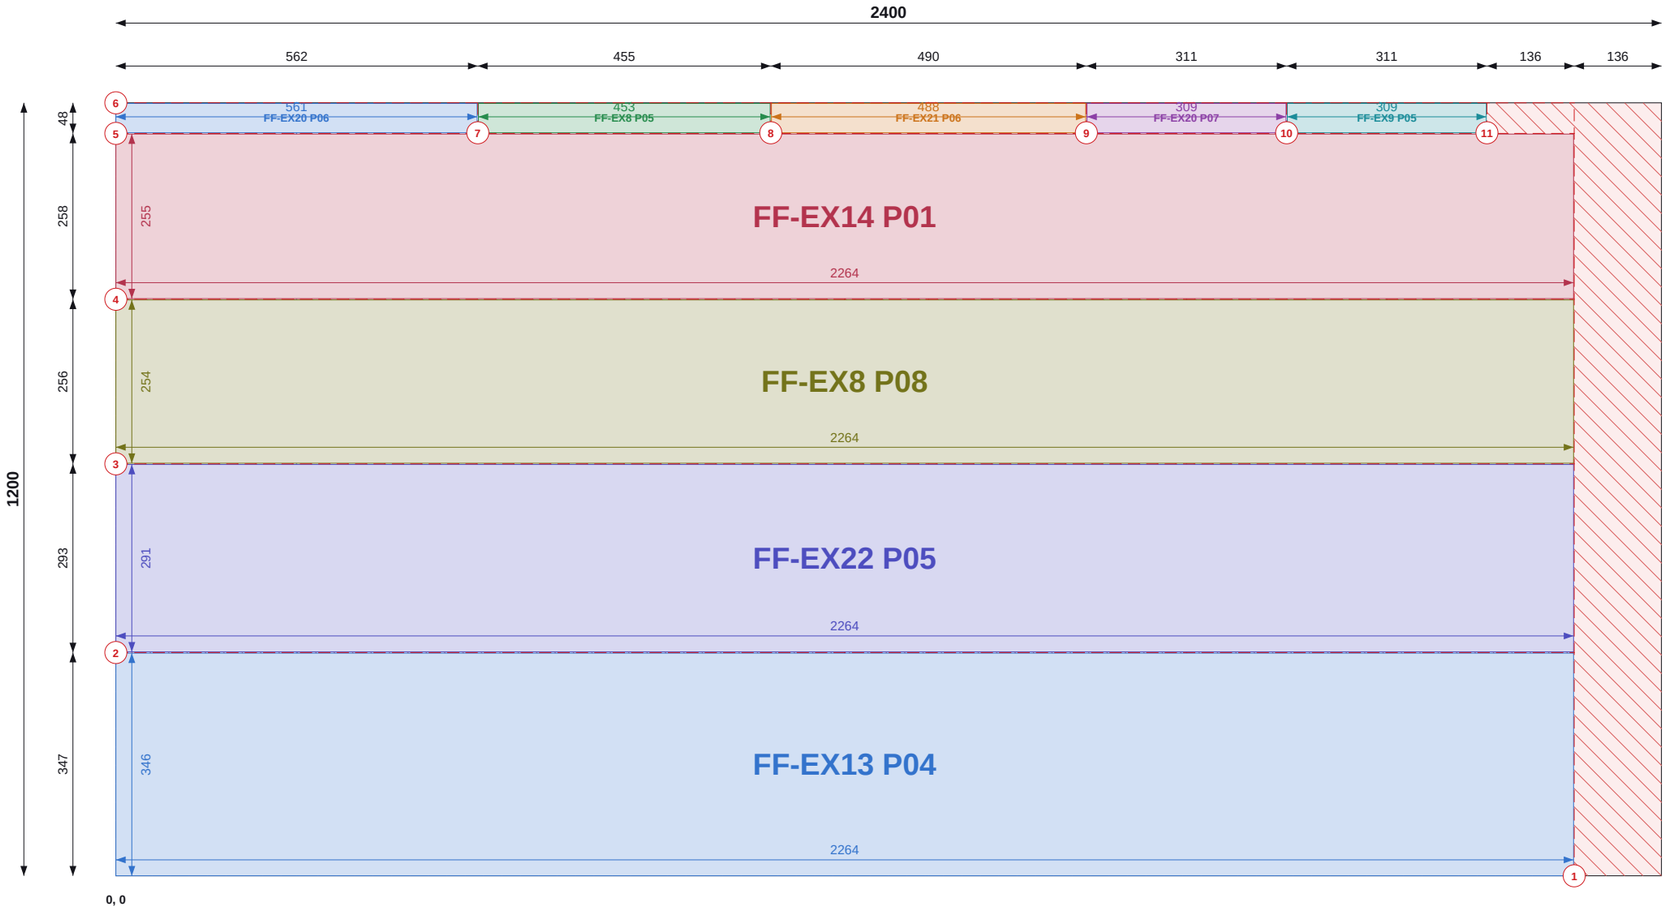

Top / left chains = saw cut positions (to cut centres). Coloured = part size and position.

Do not scale. All dimensions in mm. Check all dimensions on site.

SHEET 14 OF 23

THIS SHEET

Item	Value
Parts	9
Used / waste	93.4% / 0.19 m2
Reusable offcuts	0
Saw cuts / shared	11 / 8

PIECES (POSITION = BOTTOM-LEFT CORNER)

Label	Size	X, Y
FF-EX20 P06	561 x 46	0, 1154
FF-EX8 P05	453 x 46	563, 1154
FF-EX21 P06	488 x 46	1018, 1154
FF-EX20 P07	309 x 46	1508, 1154
FF-EX9 P05	309 x 46	1819, 1154
FF-EX14 P01	255 x 2264	0, 896
FF-EX8 P08	254 x 2264	0, 641
FF-EX22 P05	291 x 2264	0, 348
FF-EX13 P04	346 x 2264	0, 0

NOTES

1. Cut from PIR 120mm 1200x2400, 2mm saw kerf. Viewed on the face; dimensions from the sheet's bottom-left corner (0,0). Red numbered lines = saw cuts in order, each edge to edge.
2. Coloured dimensions belong to the part of that colour: its width and height, and its position from the sheet edges. Raked parts: corner coordinates at each corner.
3. Red hatch = waste. Labels = panel + piece mark on the manufacture drawing.

REVISIONS

REV	DATE	DESCRIPTION
C01	14.09.26	Construction issue
C02	14.09.26	Roof trusses revised; SP diagonals added
C03	11.10.26	FF windows coursed; steel + GP1 portal; steel drawings (ST)
C04	13.10.26	Steel approved by the engineer: steel + steel timber drawings issued for construction

TLS

TLS TIMBER FRAME

Design & Manufacture

Scan: 3D model + drawings

CLIENT	PROJECT
MP Adams	MP Adams Plot 4, Eckington


DRAWING TITLE

PIR CUTTING - FIRST FLOOR - SHEET 14 OF 23

PIR 120mm 1200x2400 | First Floor

SCALE	SIZE	DATE	DRAWN
NTS	A3	13.10.26	TS

STATUS	DRAWING No.	REV
CONSTRUCTION	P4-CP-PIR-02 / 14	C04

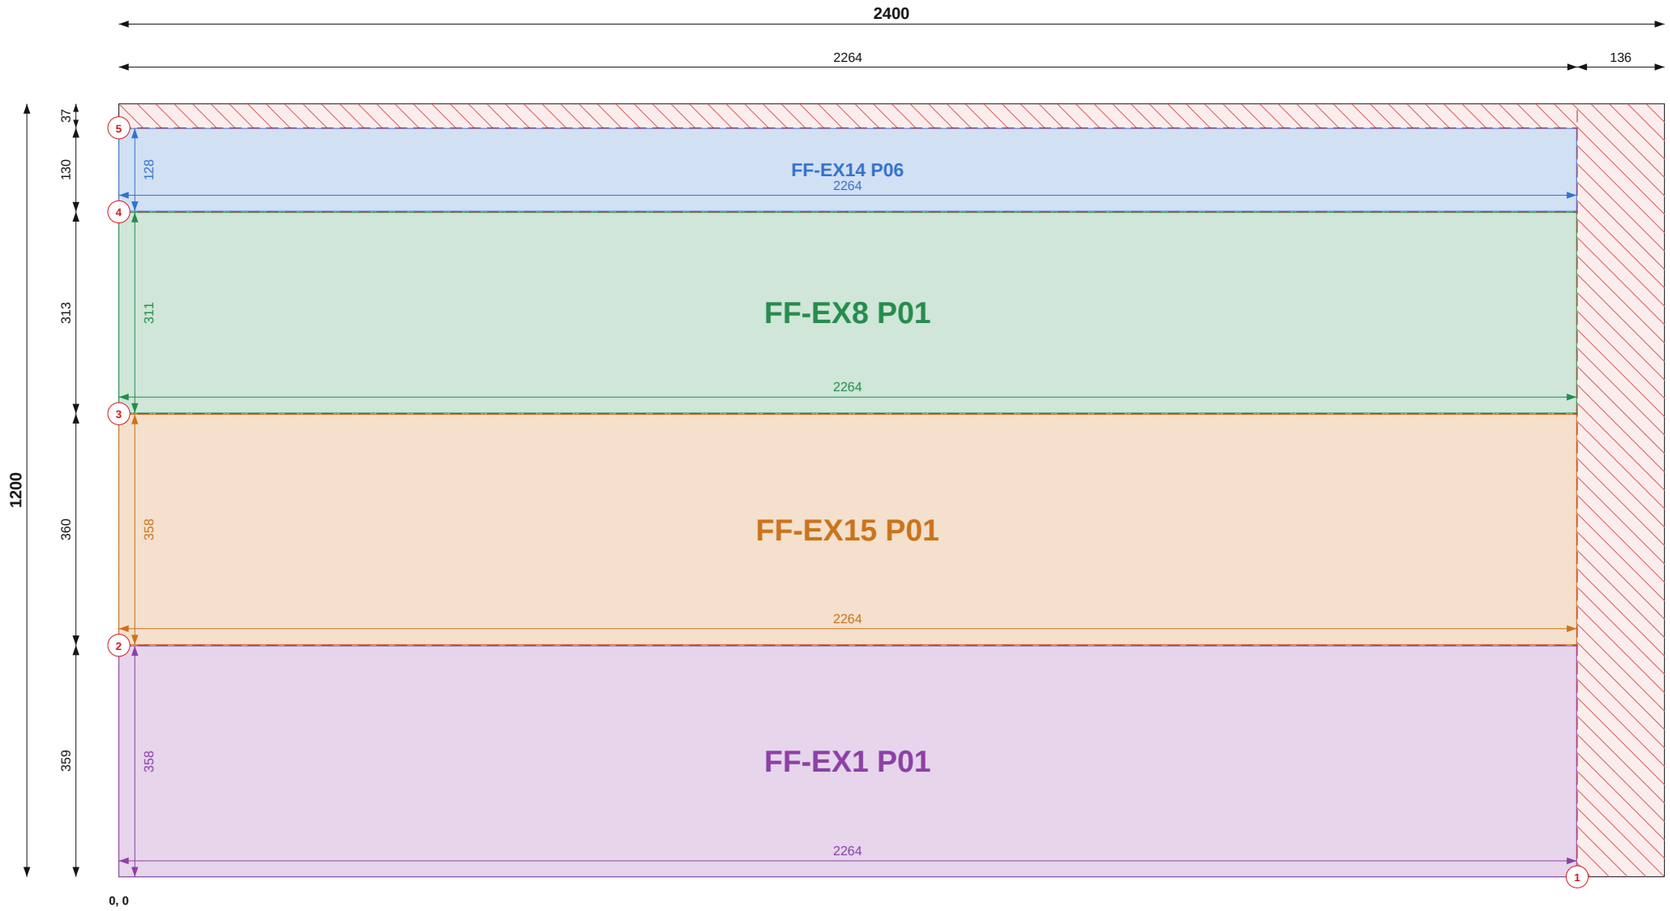

Top / left chains = saw cut positions (to cut centres). Coloured = part size and position.

SHEET 15 OF 23

THIS SHEET

Item	Value
Parts	4
Used / waste	90.8% / 0.26 m2
Reusable offcuts	0
Saw cuts / shared	5 / 3

PIECES (POSITION = BOTTOM-LEFT CORNER)

Label	Size	X, Y
FF-EX14 P06	128 x 2264	0, 1033
FF-EX8 P01	311 x 2264	0, 720
FF-EX15 P01	358 x 2264	0, 360
FF-EX1 P01	358 x 2264	0, 0

NOTES

1. Cut from PIR 120mm 1200x2400, 2mm saw kerf. Viewed on the face; dimensions from the sheet's bottom-left corner (0,0). Red numbered lines = saw cuts in order, each edge to edge.
2. Coloured dimensions belong to the part of that colour: its width and height, and its position from the sheet edges. Raked parts: corner coordinates at each corner.
3. Red hatch = waste. Labels = panel + piece mark on the manufacture drawing.

REVISIONS

REV	DATE	DESCRIPTION
C01	14.09.26	Construction issue
C02	14.09.26	Roof trusses revised; SP diagonals added
C03	11.10.26	FF windows coursed; steel + GP1 portal; steel drawings (ST)
C04	13.10.26	Steel approved by the engineer: steel + steel timber drawings issued for construction

TLS TIMBER FRAME
Design & Manufacture
Scan: 3D model + drawings

CLIENT	PROJECT
MP Adams	MP Adams Plot 4, Eckington

DRAWING TITLE


PIR CUTTING - FIRST FLOOR - SHEET 15 OF 23

PIR 120mm 1200x2400 | First Floor

SCALE	SIZE	DATE	DRAWN
NTS	A3	13.10.26	TS

STATUS	DRAWING No.	REV
CONSTRUCTION	P4-CP-PIR-02 / 15	C04

Do not scale. All dimensions in mm. Check all dimensions on site.

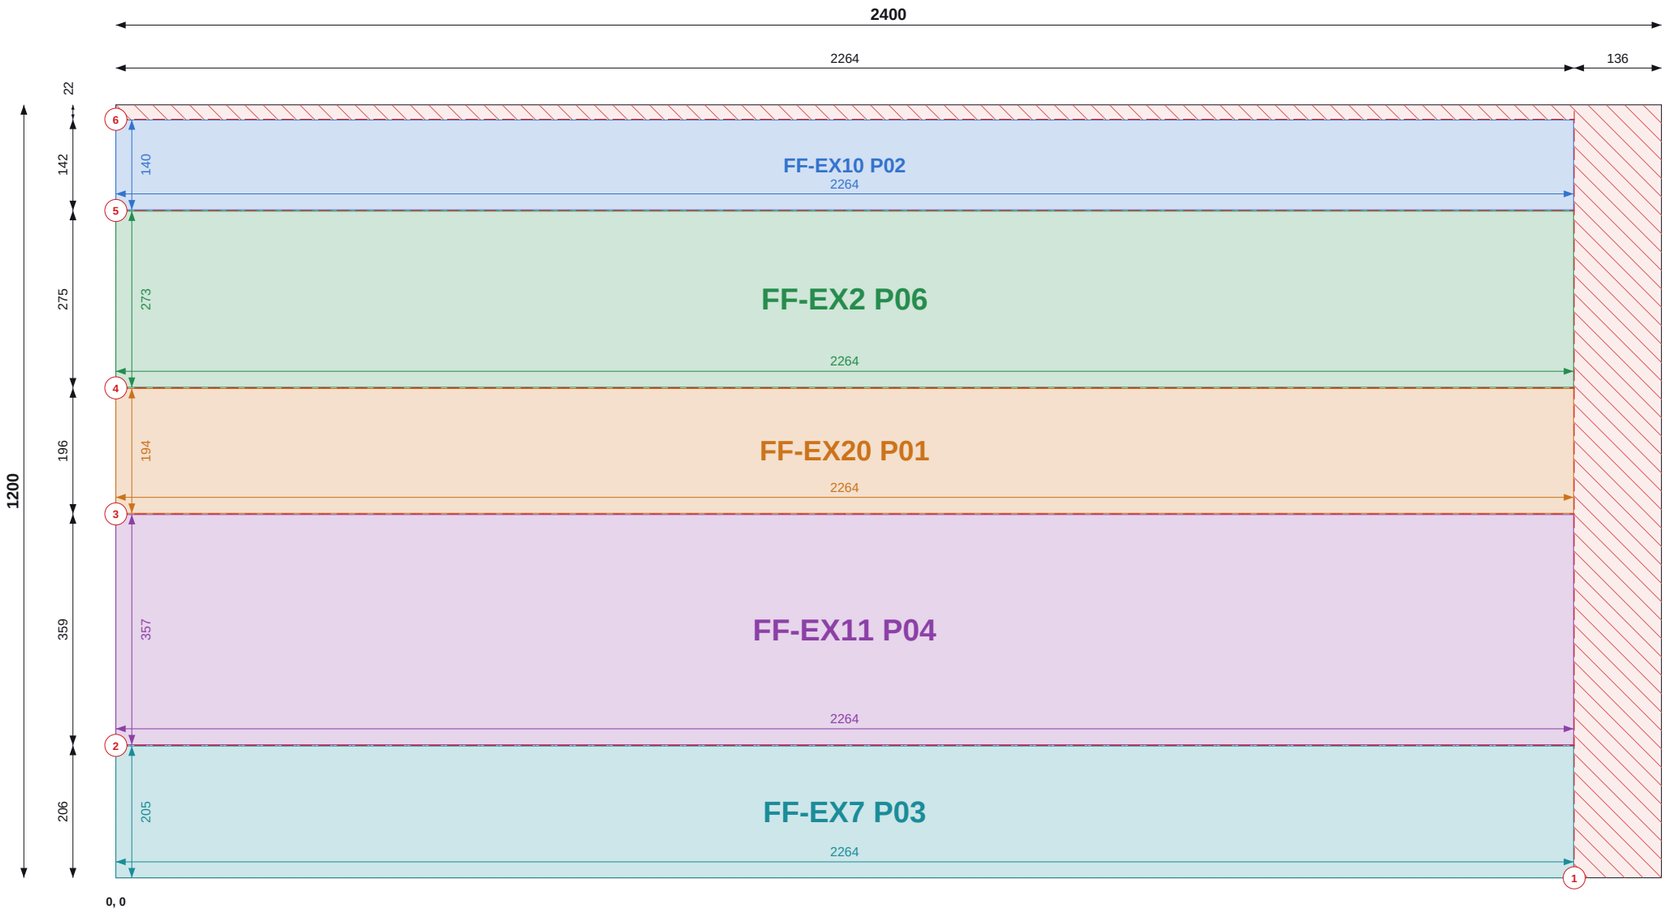

Top / left chains = saw cut positions (to cut centres). Coloured = part size and position.

SHEET 16 OF 23

THIS SHEET

Item	Value
Parts	5
Used / waste	91.8% / 0.23 m2
Reusable offcuts	0
Saw cuts / shared	6 / 4

PIECES (POSITION = BOTTOM-LEFT CORNER)

Label	Size	X, Y
FF-EX10 P02	140 x 2264	0, 1037
FF-EX2 P06	273 x 2264	0, 762
FF-EX20 P01	194 x 2264	0, 566
FF-EX11 P04	357 x 2264	0, 207
FF-EX7 P03	205 x 2264	0, 0

NOTES

1. Cut from PIR 120mm 1200x2400, 2mm saw kerf. Viewed on the face; dimensions from the sheet's bottom-left corner (0,0). Red numbered lines = saw cuts in order, each edge to edge.
2. Coloured dimensions belong to the part of that colour: its width and height, and its position from the sheet edges. Raked parts: corner coordinates at each corner.
3. Red hatch = waste. Labels = panel + piece mark on the manufacture drawing.

REVISIONS

REV	DATE	DESCRIPTION
C01	14.09.26	Construction issue
C02	14.09.26	Roof trusses revised; SP diagonals added
C03	11.10.26	FF windows coursed; steel + GP1 portal; steel drawings (ST)
C04	13.10.26	Steel approved by the engineer: steel + steel timber drawings issued for construction

TLS TIMBER FRAME DESIGN SUITE

TLS TIMBER FRAME

Design & Manufacture

Scan: 3D model + drawings

CLIENT	PROJECT
MP Adams	MP Adams Plot 4, Eckington

DRAWING TITLE


PIR CUTTING - FIRST FLOOR - SHEET 16 OF 23

PIR 120mm 1200x2400 | First Floor

SCALE	SIZE	DATE	DRAWN
NTS	A3	13.10.26	TS

STATUS	DRAWING No.	REV
CONSTRUCTION	P4-CP-PIR-02 / 16	C04

Do not scale. All dimensions in mm. Check all dimensions on site.

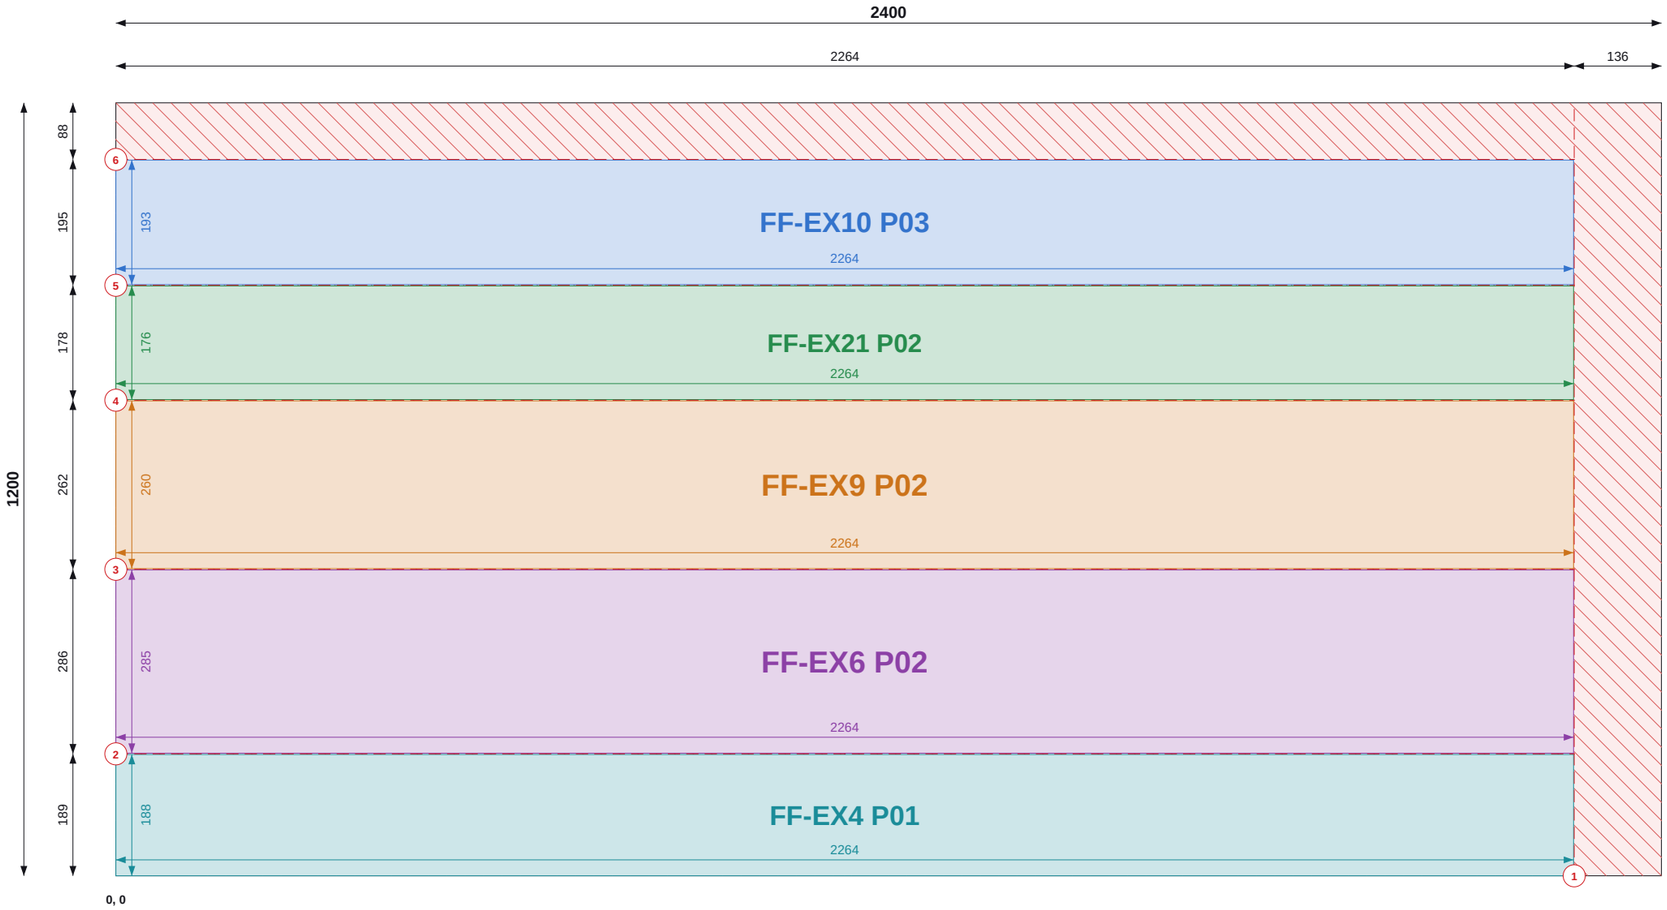

Top / left chains = saw cut positions (to cut centres). Coloured = part size and position.

Do not scale. All dimensions in mm. Check all dimensions on site.

SHEET 17 OF 23

THIS SHEET

Item	Value
Parts	5
Used / waste	86.7% / 0.38 m2
Reusable offcuts	0
Saw cuts / shared	6 / 4

PIECES (POSITION = BOTTOM-LEFT CORNER)

Label	Size	X, Y
FF-EX10 P03	193 x 2264	0, 918
FF-EX21 P02	176 x 2264	0, 739
FF-EX9 P02	260 x 2264	0, 477
FF-EX6 P02	285 x 2264	0, 190
FF-EX4 P01	188 x 2264	0, 0

NOTES

1. Cut from PIR 120mm 1200x2400, 2mm saw kerf. Viewed on the face; dimensions from the sheet's bottom-left corner (0,0). Red numbered lines = saw cuts in order, each edge to edge.
2. Coloured dimensions belong to the part of that colour: its width and height, and its position from the sheet edges. Raked parts: corner coordinates at each corner.
3. Red hatch = waste. Labels = panel + piece mark on the manufacture drawing.

REVISIONS

REV	DATE	DESCRIPTION
C01	14.09.26	Construction issue
C02	14.09.26	Roof trusses revised; SP diagonals added
C03	11.10.26	FF windows coursed; steel + GP1 portal; steel drawings (ST)
C04	13.10.26	Steel approved by the engineer: steel + steel timber drawings issued for construction

TLS TIMBER FRAME
Design & Manufacture
Scan: 3D model + drawings

CLIENT	PROJECT
MP Adams	MP Adams Plot 4, Eckington


DRAWING TITLE

PIR CUTTING - FIRST FLOOR - SHEET 17 OF 23

PIR 120mm 1200x2400 | First Floor

SCALE	SIZE	DATE	DRAWN
NTS	A3	13.10.26	TS

STATUS	DRAWING No.	REV
CONSTRUCTION	P4-CP-PIR-02 / 17	C04

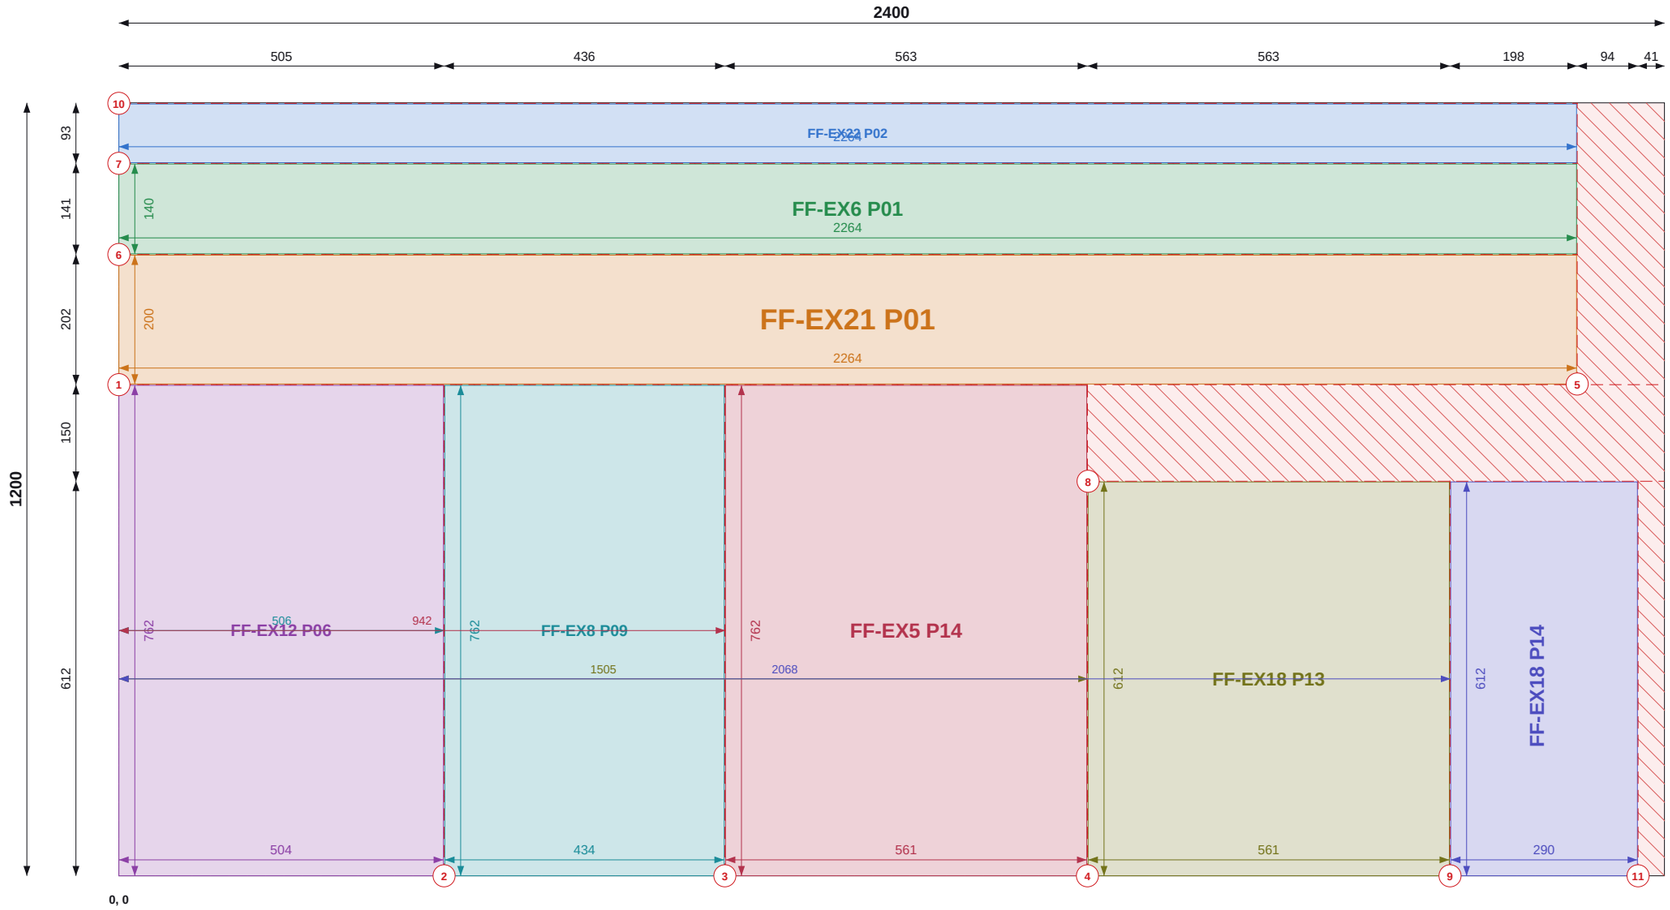

Top / left chains = saw cut positions (to cut centres). Coloured = part size and position.

Do not scale. All dimensions in mm. Check all dimensions on site.

SHEET 18 OF 23

THIS SHEET

Item	Value
Parts	8
Used / waste	91.6% / 0.24 m2
Reusable offcuts	0
Saw cuts / shared	11 / 7

PIECES (POSITION = BOTTOM-LEFT CORNER)

Label	Size	X, Y
FF-EX22 P02	91 x 2264	0, 1107
FF-EX6 P01	140 x 2264	0, 966
FF-EX21 P01	200 x 2264	0, 764
FF-EX12 P06	504 x 762	0, 0
FF-EX8 P09	434 x 762	506, 0
FF-EX5 P14	561 x 762	942, 0
FF-EX18 P13	561 x 612	1505, 0
FF-EX18 P14	290 x 612	2068, 0

NOTES

1. Cut from PIR 120mm 1200x2400, 2mm saw kerf. Viewed on the face; dimensions from the sheet's bottom-left corner (0,0). Red numbered lines = saw cuts in order, each edge to edge.
2. Coloured dimensions belong to the part of that colour: its width and height, and its position from the sheet edges. Raked parts: corner coordinates at each corner.
3. Red hatch = waste. Labels = panel + piece mark on the manufacture drawing.

REVISIONS

REV	DATE	DESCRIPTION
C01	14.09.26	Construction issue
C02	14.09.26	Roof trusses revised; SP diagonals added
C03	11.10.26	FF windows coursed; steel + GP1 portal; steel drawings (ST)
C04	13.10.26	Steel approved by the engineer: steel + steel timber drawings issued for construction

TLS TIMBER FRAME
Design & Manufacture
Scan: 3D model + drawings

CLIENT	PROJECT
MP Adams	MP Adams Plot 4, Eckington


DRAWING TITLE

PIR CUTTING - FIRST FLOOR - SHEET 18 OF 23

PIR 120mm 1200x2400 | First Floor

SCALE	SIZE	DATE	DRAWN
NTS	A3	13.10.26	TS

STATUS	DRAWING No.	REV
CONSTRUCTION	P4-CP-PIR-02 / 18	C04

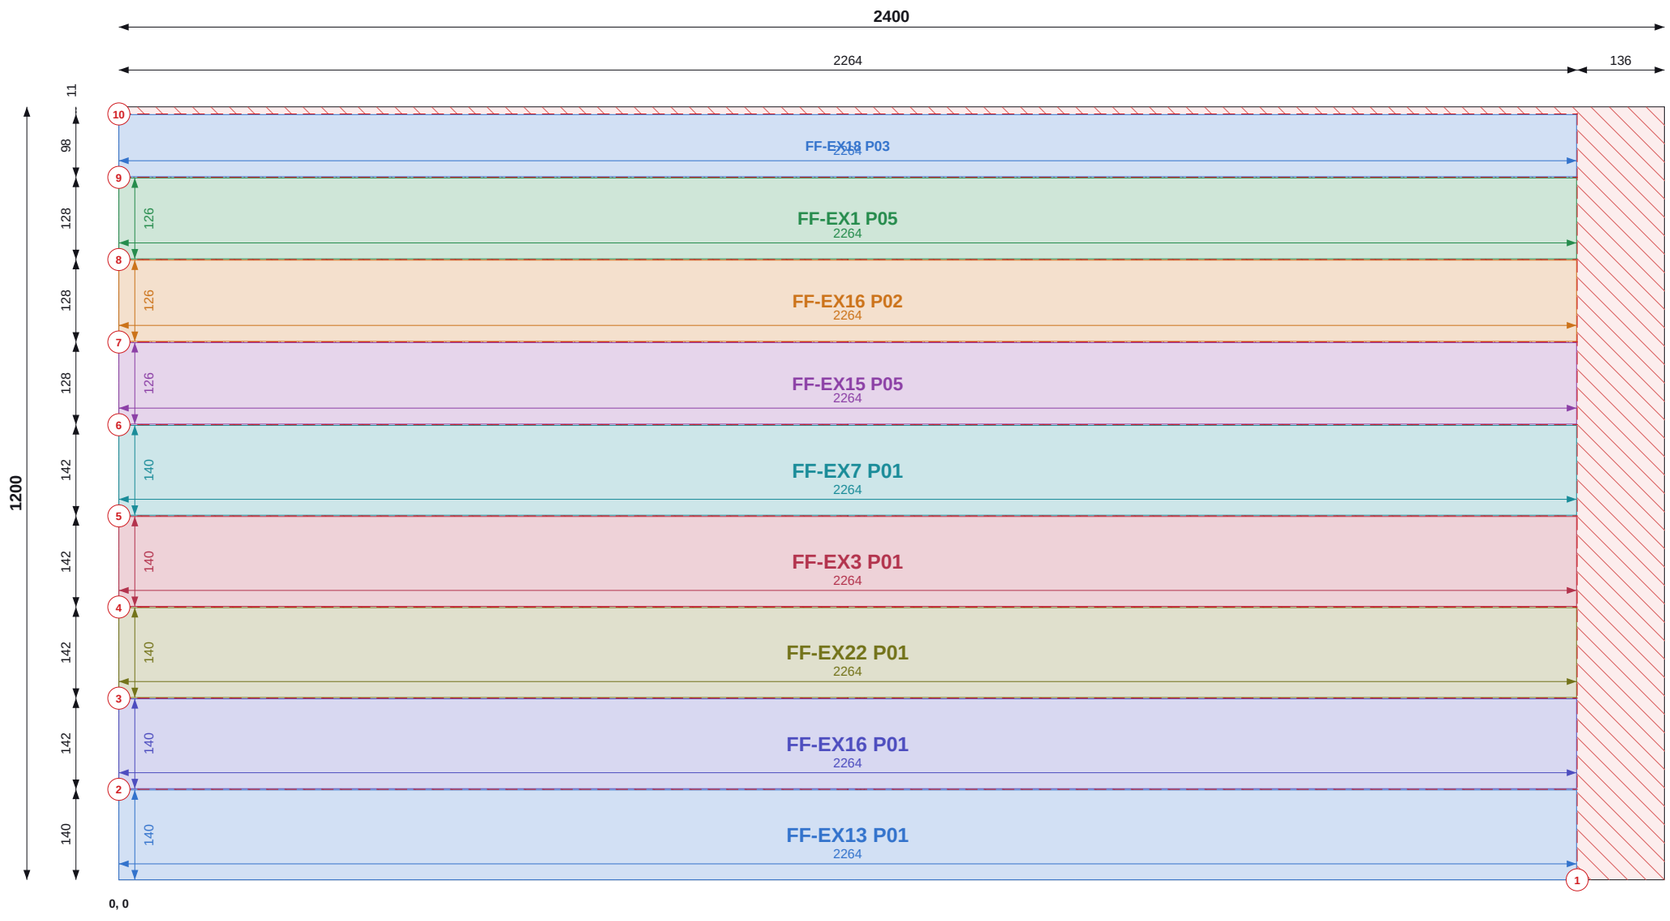

Top / left chains = saw cut positions (to cut centres). Coloured = part size and position.

SHEET 19 OF 23

THIS SHEET

Item	Value
Parts	9
Used / waste	92.1% / 0.23 m2
Reusable offcuts	0
Saw cuts / shared	10 / 8

PIECES (POSITION = BOTTOM-LEFT CORNER)

Label	Size	X, Y
FF-EX18 P03	96 x 2264	0, 1092
FF-EX1 P05	126 x 2264	0, 964
FF-EX16 P02	126 x 2264	0, 836
FF-EX15 P05	126 x 2264	0, 708
FF-EX7 P01	140 x 2264	0, 566
FF-EX3 P01	140 x 2264	0, 424
FF-EX22 P01	140 x 2264	0, 283
FF-EX16 P01	140 x 2264	0, 142
FF-EX13 P01	140 x 2264	0, 0

NOTES

1. Cut from PIR 120mm 1200x2400, 2mm saw kerf. Viewed on the face; dimensions from the sheet's bottom-left corner (0,0). Red numbered lines = saw cuts in order, each edge to edge.
2. Coloured dimensions belong to the part of that colour: its width and height, and its position from the sheet edges. Raked parts: corner coordinates at each corner.
3. Red hatch = waste. Labels = panel + piece mark on the manufacture drawing.

REVISIONS

REV	DATE	DESCRIPTION
C01	14.09.26	Construction issue
C02	14.09.26	Roof trusses revised; SP diagonals added
C03	11.10.26	FF windows coursed; steel + GP1 portal; steel drawings (ST)
C04	13.10.26	Steel approved by the engineer: steel + steel timber drawings issued for construction

TLS TIMBER FRAME DESIGN SUITE

TLS TIMBER FRAME
Design & Manufacture
Scan: 3D model + drawings

CLIENT	PROJECT
MP Adams	MP Adams Plot 4, Eckington

DRAWING TITLE


PIR CUTTING - FIRST FLOOR - SHEET 19 OF 23

PIR 120mm 1200x2400 | First Floor

SCALE	SIZE	DATE	DRAWN
NTS	A3	13.10.26	TS

STATUS	DRAWING No.	REV
CONSTRUCTION	P4-CP-PIR-02 / 19	C04

Do not scale. All dimensions in mm. Check all dimensions on site.

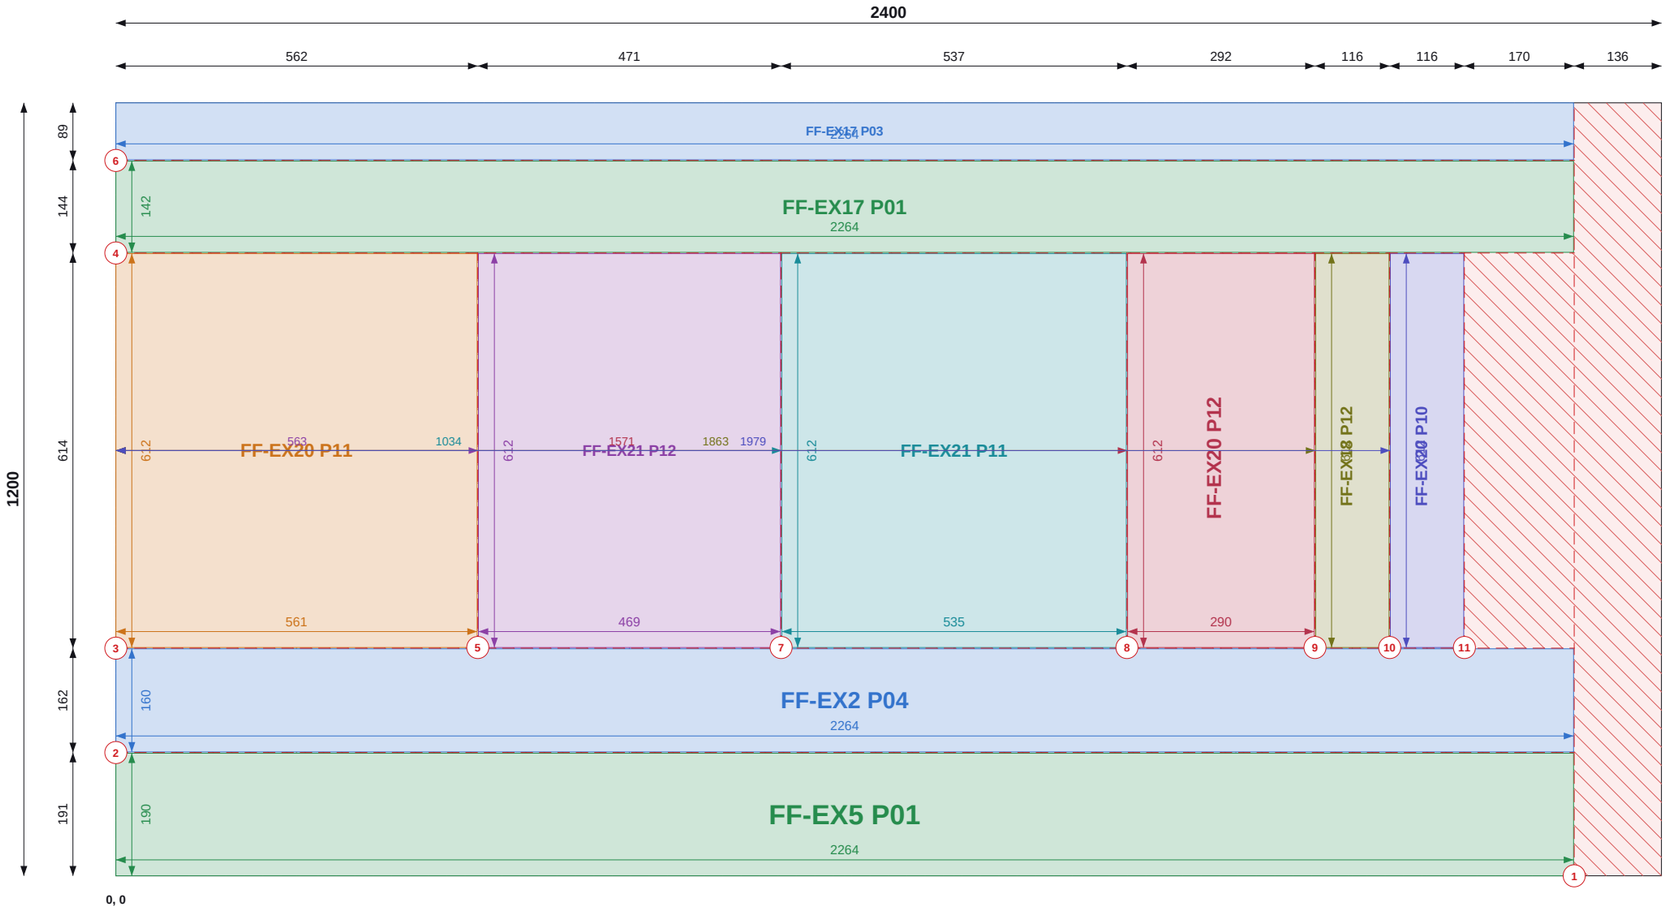

Top / left chains = saw cut positions (to cut centres). Coloured = part size and position.

Do not scale. All dimensions in mm. Check all dimensions on site.

SHEET 20 OF 23

THIS SHEET

Item	Value
Parts	10
Used / waste	89.8% / 0.29 m2
Reusable offcuts	0
Saw cuts / shared	11 / 9

PIECES (POSITION = BOTTOM-LEFT CORNER)

Label	Size	X, Y
FF-EX17 P03	88 x 2264	0, 1112
FF-EX17 P01	142 x 2264	0, 968
FF-EX20 P11	561 x 612	0, 354
FF-EX21 P12	469 x 612	563, 354
FF-EX21 P11	535 x 612	1034, 354
FF-EX20 P12	290 x 612	1571, 354
FF-EX18 P12	114 x 612	1863, 354
FF-EX20 P10	114 x 612	1979, 354
FF-EX2 P04	160 x 2264	0, 192
FF-EX5 P01	190 x 2264	0, 0

NOTES

1. Cut from PIR 120mm 1200x2400, 2mm saw kerf. Viewed on the face; dimensions from the sheet's bottom-left corner (0,0). Red numbered lines = saw cuts in order, each edge to edge.
2. Coloured dimensions belong to the part of that colour: its width and height, and its position from the sheet edges. Raked parts: corner coordinates at each corner.
3. Red hatch = waste. Labels = panel + piece mark on the manufacture drawing.

REVISIONS

REV	DATE	DESCRIPTION
C01	14.09.26	Construction issue
C02	14.09.26	Roof trusses revised; SP diagonals added
C03	11.10.26	FF windows coursed; steel + GP1 portal; steel drawings (ST)
C04	13.10.26	Steel approved by the engineer: steel + steel timber drawings issued for construction

TLS TIMBER FRAME
Design & Manufacture
Scan: 3D model + drawings


CLIENT	PROJECT
MP Adams	MP Adams Plot 4, Eckington

DRAWING TITLE
PIR CUTTING - FIRST FLOOR - SHEET 20 OF 23

PIR 120mm 1200x2400 | First Floor

SCALE	SIZE	DATE	DRAWN
NTS	A3	13.10.26	TS

STATUS	DRAWING No.	REV
CONSTRUCTION	P4-CP-PIR-02 / 20	C04

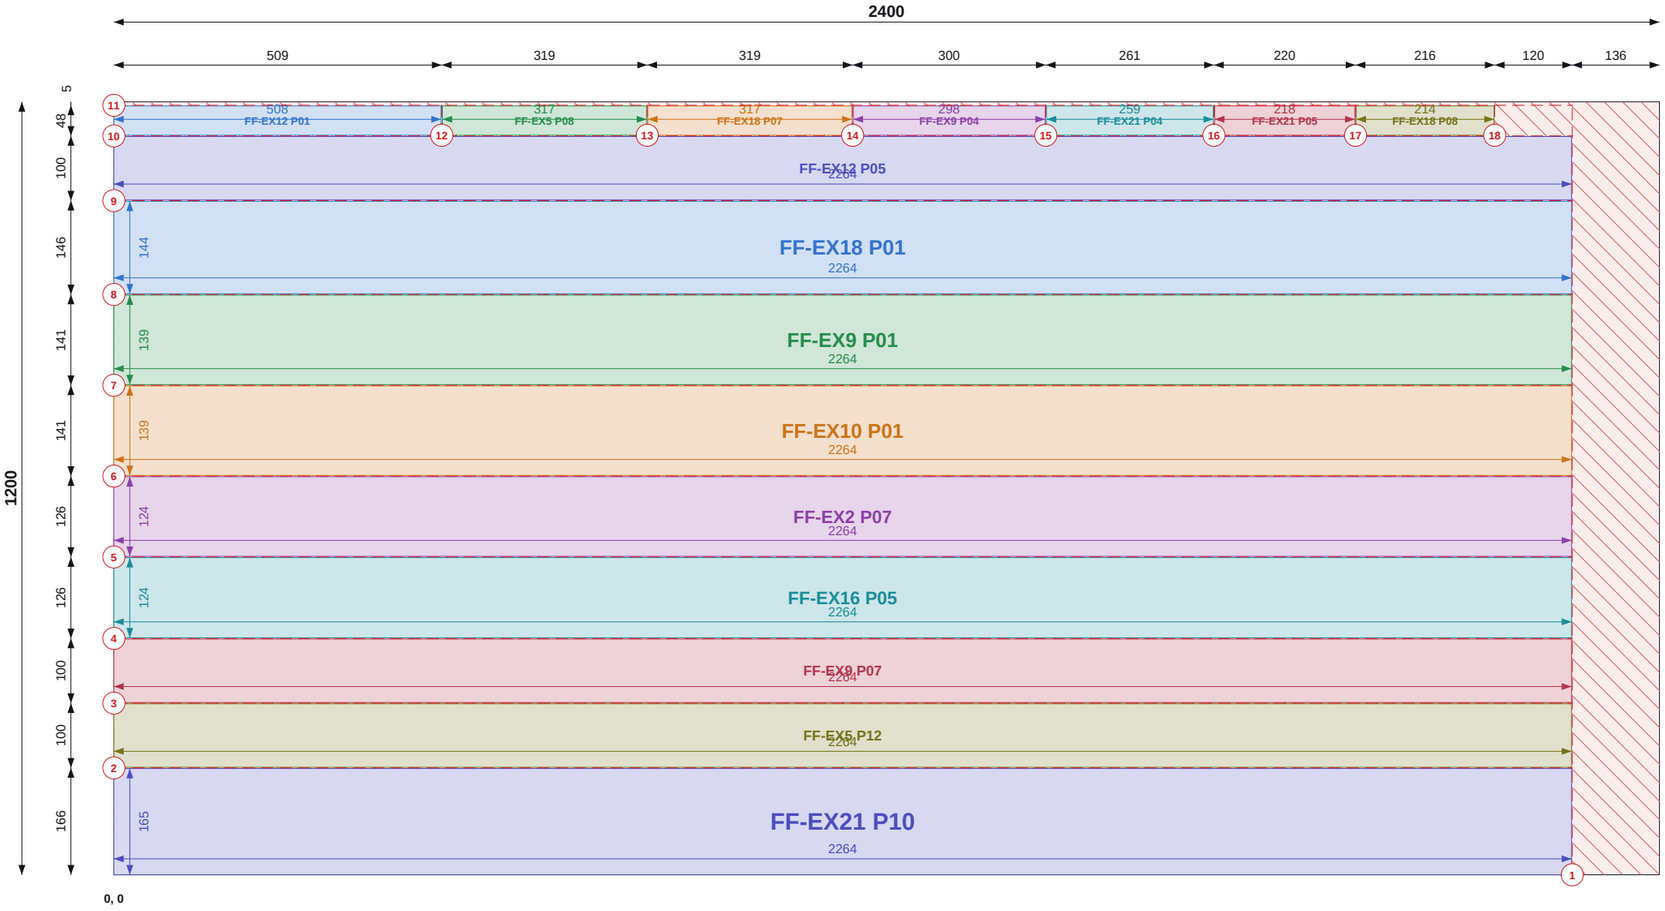

Top / left chains = saw cut positions (to cut centres). Coloured = part size and position.

SHEET 21 OF 23

THIS SHEET

Item	Value
Parts	16
Used / waste	92.2% / 0.22 m2
Reusable offcuts	0
Saw cuts / shared	18 / 15

PIECES (POSITION = BOTTOM-LEFT CORNER)

Label	Size	X, Y
FF-EX12 P01	508 x 46	0, 1148
FF-EX5 P08	317 x 46	510, 1148
FF-EX18 P07	317 x 46	829, 1148
FF-EX9 P04	298 x 46	1148, 1148
FF-EX21 P04	259 x 46	1448, 1148
FF-EX21 P05	218 x 46	1709, 1148
FF-EX18 P08	214 x 46	1929, 1148
FF-EX12 P05	99 x 2264	0, 1048
FF-EX18 P01	144 x 2264	0, 902
FF-EX9 P01	139 x 2264	0, 761
FF-EX10 P01	139 x 2264	0, 620
FF-EX2 P07	124 x 2264	0, 494
FF-EX16 P05	124 x 2264	0, 368
FF-EX9 P07	98 x 2264	0, 268
FF-EX5 P12	98 x 2264	0, 167
FF-EX21 P10	165 x 2264	0, 0

NOTES

1. Cut from PIR 120mm 1200x2400, 2mm saw kerf. Viewed on the face; dimensions from the sheet's bottom-left corner (0,0). Red numbered lines = saw cuts in order, each edge to edge.
2. Coloured dimensions belong to the part of that colour: its width and height, and its position from the sheet edges. Raked parts: corner coordinates at each corner.
3. Red hatch = waste. Labels = panel + piece mark on the manufacture drawing.

REVISIONS

REV	DATE	DESCRIPTION
C01	14.09.26	Construction issue
C02	14.09.26	Roof trusses revised; SP diagonals added
C03	11.10.26	FF windows coursed; steel + GP1 portal; steel drawings (ST)
C04	13.10.26	Steel approved by the engineer: steel + steel timber drawings issued for constructio

TLS TIMBER FRAME
Design & Manufacture
Scan: 3D model + drawings

CLIENT	PROJECT
MP Adams	MP Adams Plot 4, Eckington

DRAWING TITLE


PIR CUTTING - FIRST FLOOR - SHEET 21 OF 23

PIR 120mm 1200x2400 | First Floor

SCALE	SIZE	DATE	DRAWN
NTS	A3	13.10.26	TS

STATUS	DRAWING No.	REV
CONSTRUCTION	P4-CP-PIR-02 / 21	C04

Do not scale. All dimensions in mm. Check all dimensions on site.

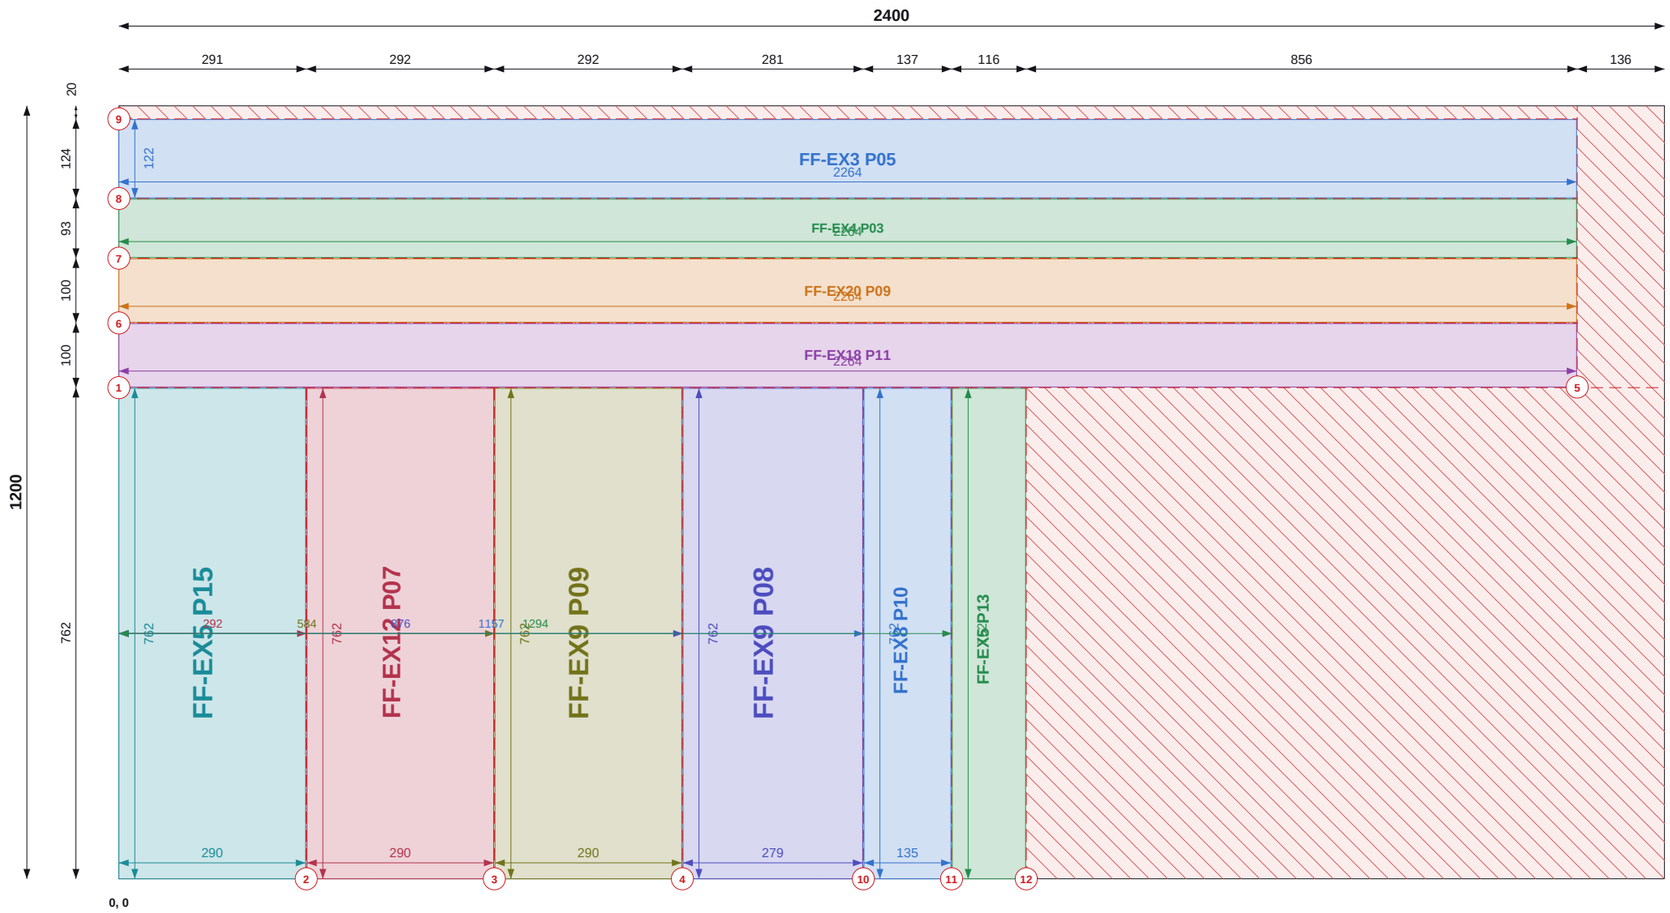

Top / left chains = saw cut positions (to cut centres). Coloured = part size and position.

Do not scale. All dimensions in mm. Check all dimensions on site.

SHEET 22 OF 23

THIS SHEET

Item	Value
Parts	10
Used / waste	69.1% / 0.89 m2
Reusable offcuts	1
Saw cuts / shared	12 / 9

PIECES (POSITION = BOTTOM-LEFT CORNER)

Label	Size	X, Y
FF-EX3 P05	122 x 2264	0, 1057
FF-EX4 P03	91 x 2264	0, 965
FF-EX20 P09	99 x 2264	0, 864
FF-EX18 P11	99 x 2264	0, 764
FF-EX5 P15	290 x 762	0, 0
FF-EX12 P07	290 x 762	292, 0
FF-EX9 P09	290 x 762	584, 0
FF-EX9 P08	279 x 762	876, 0
FF-EX8 P10	135 x 762	1157, 0
FF-EX5 P13	114 x 762	1294, 0

NOTES

1. Cut from PIR 120mm 1200x2400, 2mm saw kerf. Viewed on the face; dimensions from the sheet's bottom-left corner (0,0). Red numbered lines = saw cuts in order, each edge to edge.
2. Coloured dimensions belong to the part of that colour: its width and height, and its position from the sheet edges. Raked parts: corner coordinates at each corner.
3. Red hatch = waste. Labels = panel + piece mark on the manufacture drawing.

REVISIONS

REV	DATE	DESCRIPTION
C01	14.09.26	Construction issue
C02	14.09.26	Roof trusses revised; SP diagonals added
C03	11.10.26	FF windows coursed; steel + GP1 portal; steel drawings (ST)
C04	13.10.26	Steel approved by the engineer: steel + steel timber drawings issued for construction

TLS TIMBER FRAME
Design & Manufacture
Scan: 3D model + drawings

CLIENT	PROJECT
MP Adams	MP Adams Plot 4, Eckington


DRAWING TITLE

PIR CUTTING - FIRST FLOOR - SHEET 22 OF 23

PIR 120mm 1200x2400 | First Floor

SCALE	SIZE	DATE	DRAWN
NTS	A3	13.10.26	TS

STATUS	DRAWING No.	REV
CONSTRUCTION	P4-CP-PIR-02 / 22	C04

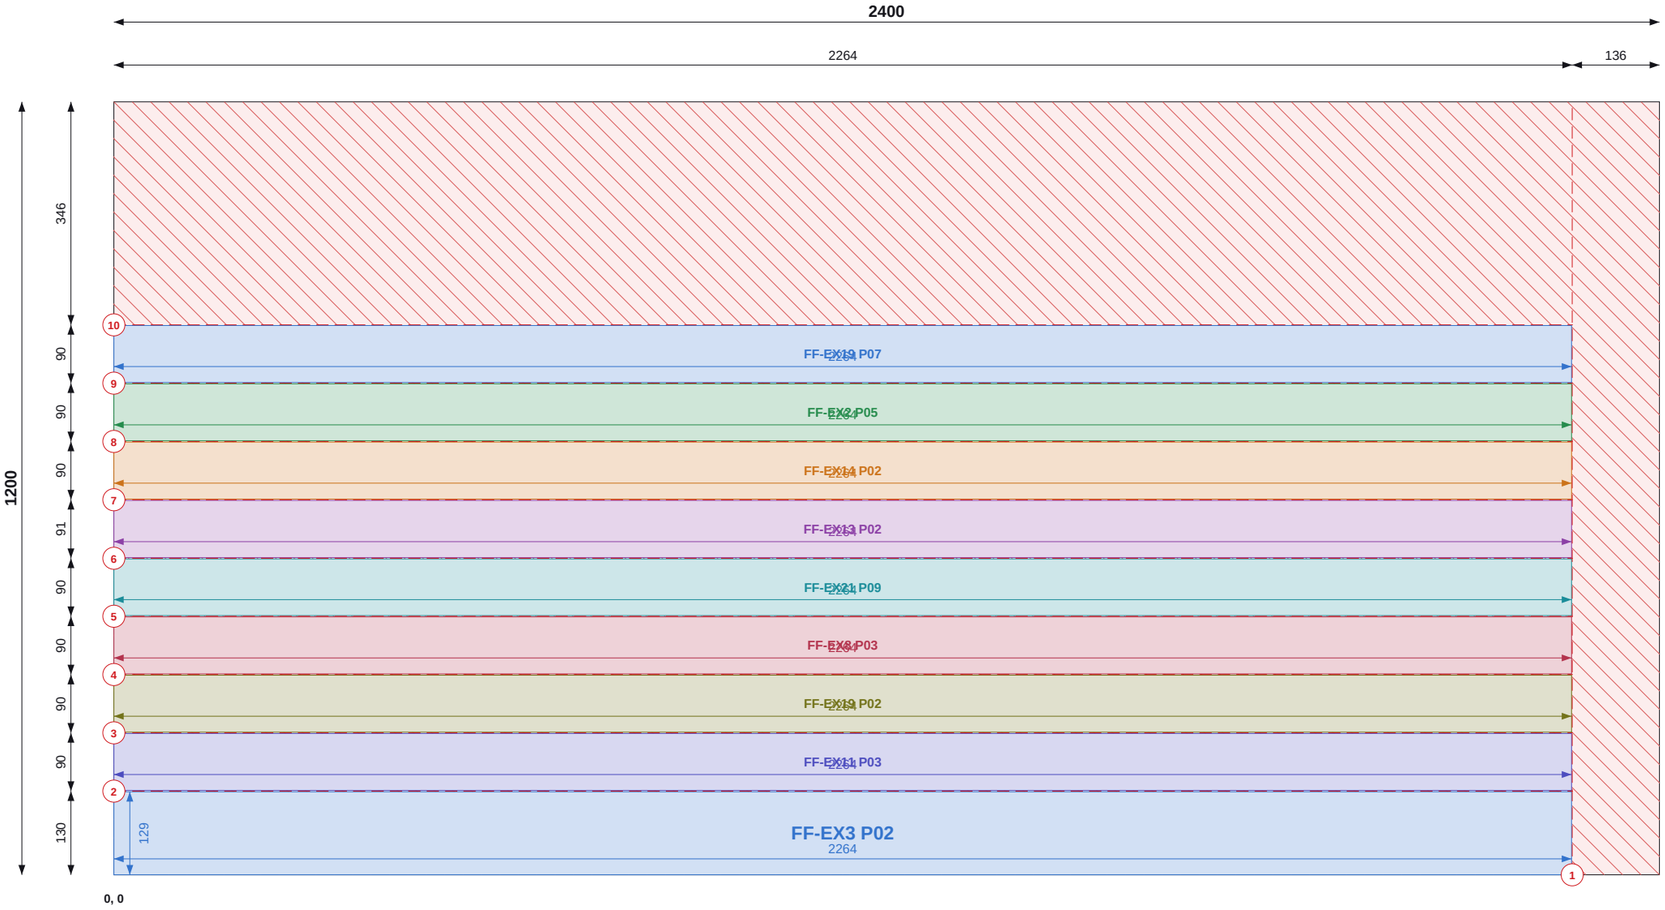

Top / left chains = saw cut positions (to cut centres). Coloured = part size and position.

Do not scale. All dimensions in mm. Check all dimensions on site.

SHEET 23 OF 23

THIS SHEET

Item	Value
Parts	9
Used / waste	65.8% / 0.99 m2
Reusable offcuts	1
Saw cuts / shared	10 / 8

PIECES (POSITION = BOTTOM-LEFT CORNER)

Label	Size	X, Y
FF-EX19 P07	89 x 2264	0, 764
FF-EX2 P05	89 x 2264	0, 674
FF-EX14 P02	89 x 2264	0, 583
FF-EX13 P02	89 x 2264	0, 492
FF-EX21 P09	88 x 2264	0, 402
FF-EX8 P03	88 x 2264	0, 312
FF-EX19 P02	88 x 2264	0, 221
FF-EX11 P03	88 x 2264	0, 131
FF-EX3 P02	129 x 2264	0, 0

NOTES

1. Cut from PIR 120mm 1200x2400, 2mm saw kerf. Viewed on the face; dimensions from the sheet's bottom-left corner (0,0). Red numbered lines = saw cuts in order, each edge to edge.
2. Coloured dimensions belong to the part of that colour: its width and height, and its position from the sheet edges. Raked parts: corner coordinates at each corner.
3. Red hatch = waste. Labels = panel + piece mark on the manufacture drawing.

REVISIONS

REV	DATE	DESCRIPTION
C01	14.09.26	Construction issue
C02	14.09.26	Roof trusses revised; SP diagonals added
C03	11.10.26	FF windows coursed; steel + GP1 portal; steel drawings (ST)
C04	13.10.26	Steel approved by the engineer: steel + steel timber drawings issued for construction

TLS TIMBER FRAME DESIGN SUITE

TLS TIMBER FRAME

Design & Manufacture

Scan: 3D model + drawings

CLIENT	PROJECT
MP Adams	MP Adams Plot 4, Eckington


DRAWING TITLE

PIR CUTTING - FIRST FLOOR - SHEET 23 OF 23

PIR 120mm 1200x2400 | First Floor

SCALE	SIZE	DATE	DRAWN
NTS	A3	13.10.26	TS

STATUS	DRAWING No.	REV
CONSTRUCTION	P4-CP-PIR-02 / 23	C04

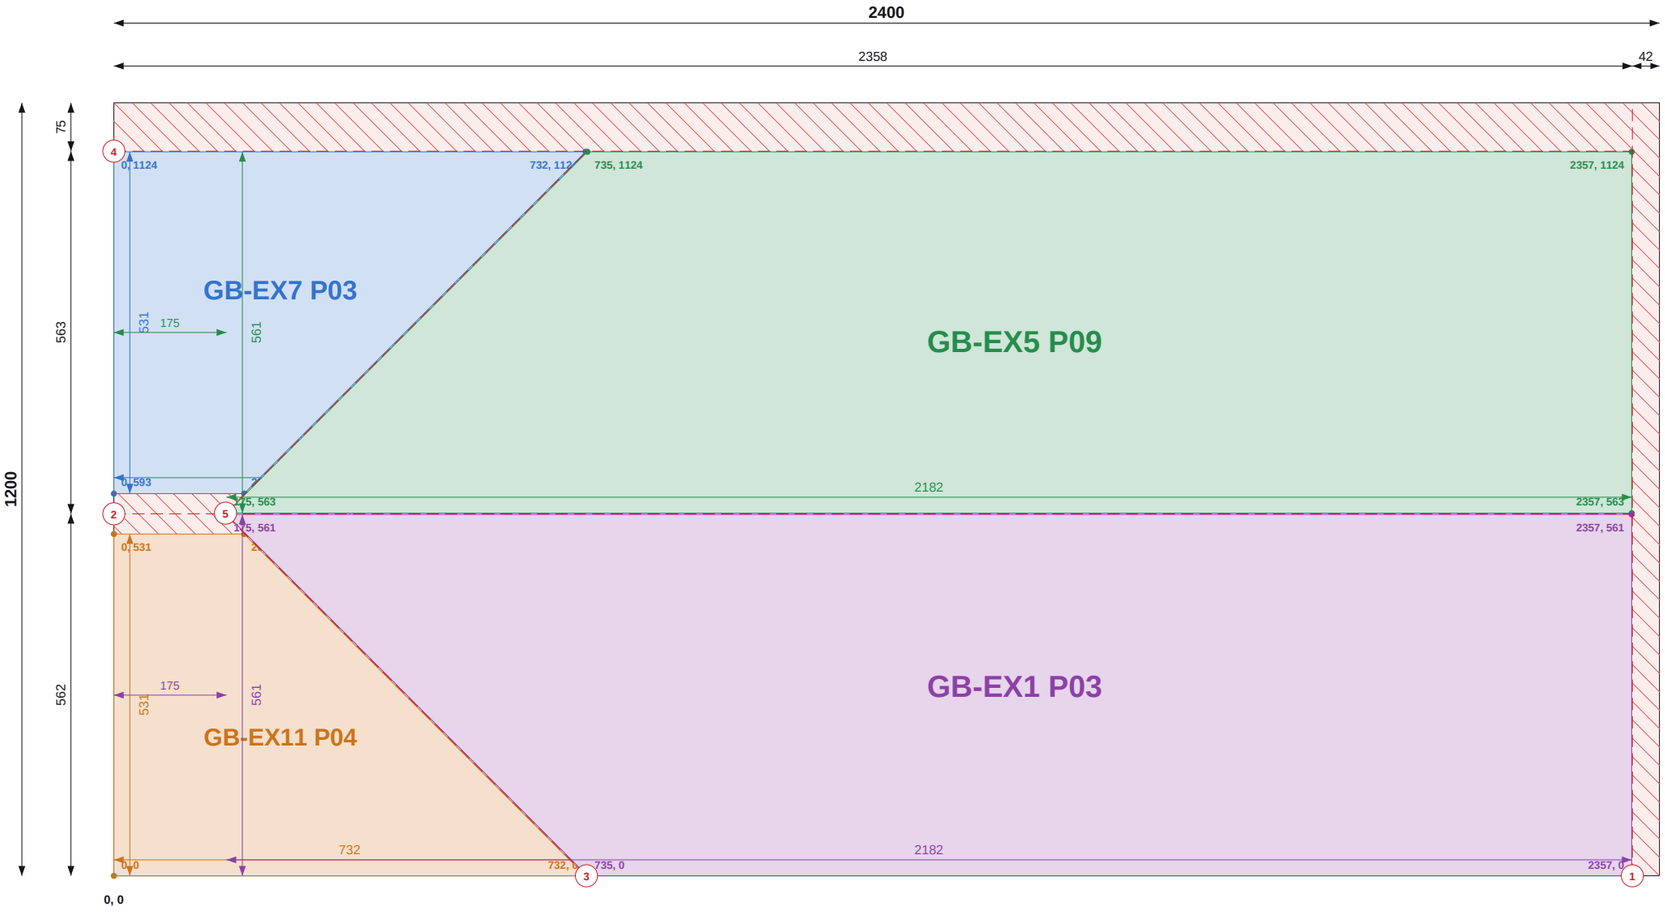

Top / left chains = saw cut positions (to cut centres). Coloured = part size and position.

Do not scale. All dimensions in mm. Check all dimensions on site.

SHEET 1 OF 18

THIS SHEET

Item	Value
Parts	4
Used / waste	91.3% / 0.25 m2
Reusable offcuts	0
Saw cuts / shared	5 / 3

PIECES (POSITION = BOTTOM-LEFT CORNER)

Label	Size	X, Y
GB-EX7 P03	531 x 732 rake to 203	0, 593
GB-EX5 P09	561 x 2182 rake to 1623	175, 563
GB-EX11 P04	531 x 732 rake to 203	0, 0
GB-EX1 P03	561 x 2182 rake to 1623	175, 0

GABLES TOTALS

Item	Value
Sheets / pieces	18 / 86
Yield / waste	83.1% / 8.77 m2
Saw cuts / shared / on stock edge	135 / 80 / 69

NOTES

1. Cut from PIR 120mm 1200x2400, 2mm saw kerf. Viewed on the face; dimensions from the sheet's bottom-left corner (0,0). Red numbered lines = saw cuts in order, each edge to edge.
2. Coloured dimensions belong to the part of that colour: its width and height, and its position from the sheet edges. Raked parts: corner coordinates at each corner.
3. Red hatch = waste. Labels = panel + piece mark on the manufacture drawing.

REVISIONS

REV	DATE	DESCRIPTION
C01	14.09.26	Construction issue
C02	14.09.26	Roof trusses revised; SP diagonals added
C03	11.10.26	FF windows coursed; steel + GP1 portal; steel drawings (ST)
C04	13.10.26	Steel approved by the engineer: steel + steel timber drawings issued for constructio

TLS

TLS TIMBER FRAME
Design & Manufacture
Scan: 3D model + drawings

CLIENT	PROJECT
MP Adams	MP Adams Plot 4, Eckington


DRAWING TITLE

PIR CUTTING - GABLES - SHEET 1 OF 18

PIR 120mm 1200x2400 | Gables

SCALE	SIZE	DATE	DRAWN
NTS	A3	13.10.26	TS

STATUS	DRAWING No.	REV
CONSTRUCTION	P4-CP-PIR-03 / 01	C04

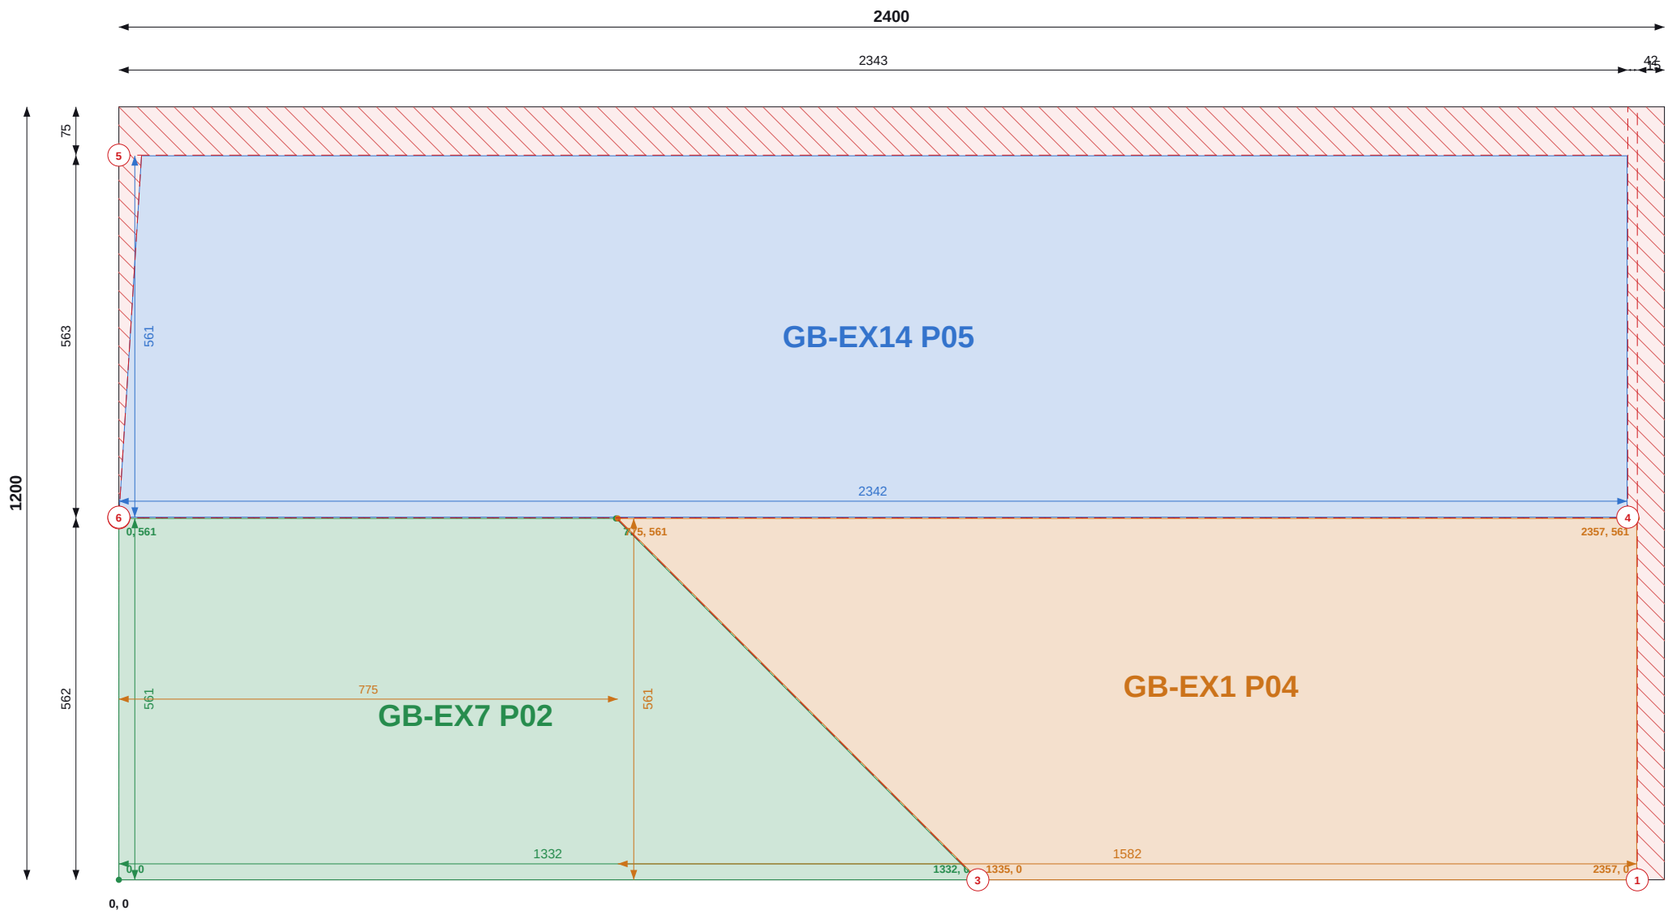

Top / left chains = saw cut positions (to cut centres). Coloured = part size and position.

SHEET 2 OF 18

THIS SHEET

Item	Value
Parts	3
Used / waste	91.1% / 0.26 m2
Reusable offcuts	0
Saw cuts / shared	6 / 3

PIECES (POSITION = BOTTOM-LEFT CORNER)

Label	Size	X, Y
GB-EX14 P05	561 x 2342	0, 563
GB-EX7 P02	561 x 1332 rake to 773	0, 0
GB-EX1 P04	561 x 1582 rake to 1023	775, 0

NOTES

1. Cut from PIR 120mm 1200x2400, 2mm saw kerf. Viewed on the face; dimensions from the sheet's bottom-left corner (0,0). Red numbered lines = saw cuts in order, each edge to edge.
2. Coloured dimensions belong to the part of that colour: its width and height, and its position from the sheet edges. Raked parts: corner coordinates at each corner.
3. Red hatch = waste. Labels = panel + piece mark on the manufacture drawing.

REVISIONS

REV	DATE	DESCRIPTION
C01	14.09.26	Construction issue
C02	14.09.26	Roof trusses revised; SP diagonals added
C03	11.10.26	FF windows coursed; steel + GP1 portal; steel drawings (ST)
C04	13.10.26	Steel approved by the engineer: steel + steel timber drawings issued for construction

TLS TIMBER FRAME
Design & Manufacture
Scan: 3D model + drawings


CLIENT	PROJECT
MP Adams	MP Adams Plot 4, Eckington

DRAWING TITLE
PIR CUTTING - GABLES - SHEET 2 OF 18
PIR 120mm 1200x2400 | Gables

SCALE	SIZE	DATE	DRAWN
NTS	A3	13.10.26	TS

STATUS	DRAWING No.	REV
CONSTRUCTION	P4-CP-PIR-03 / 02	C04

Do not scale. All dimensions in mm. Check all dimensions on site.

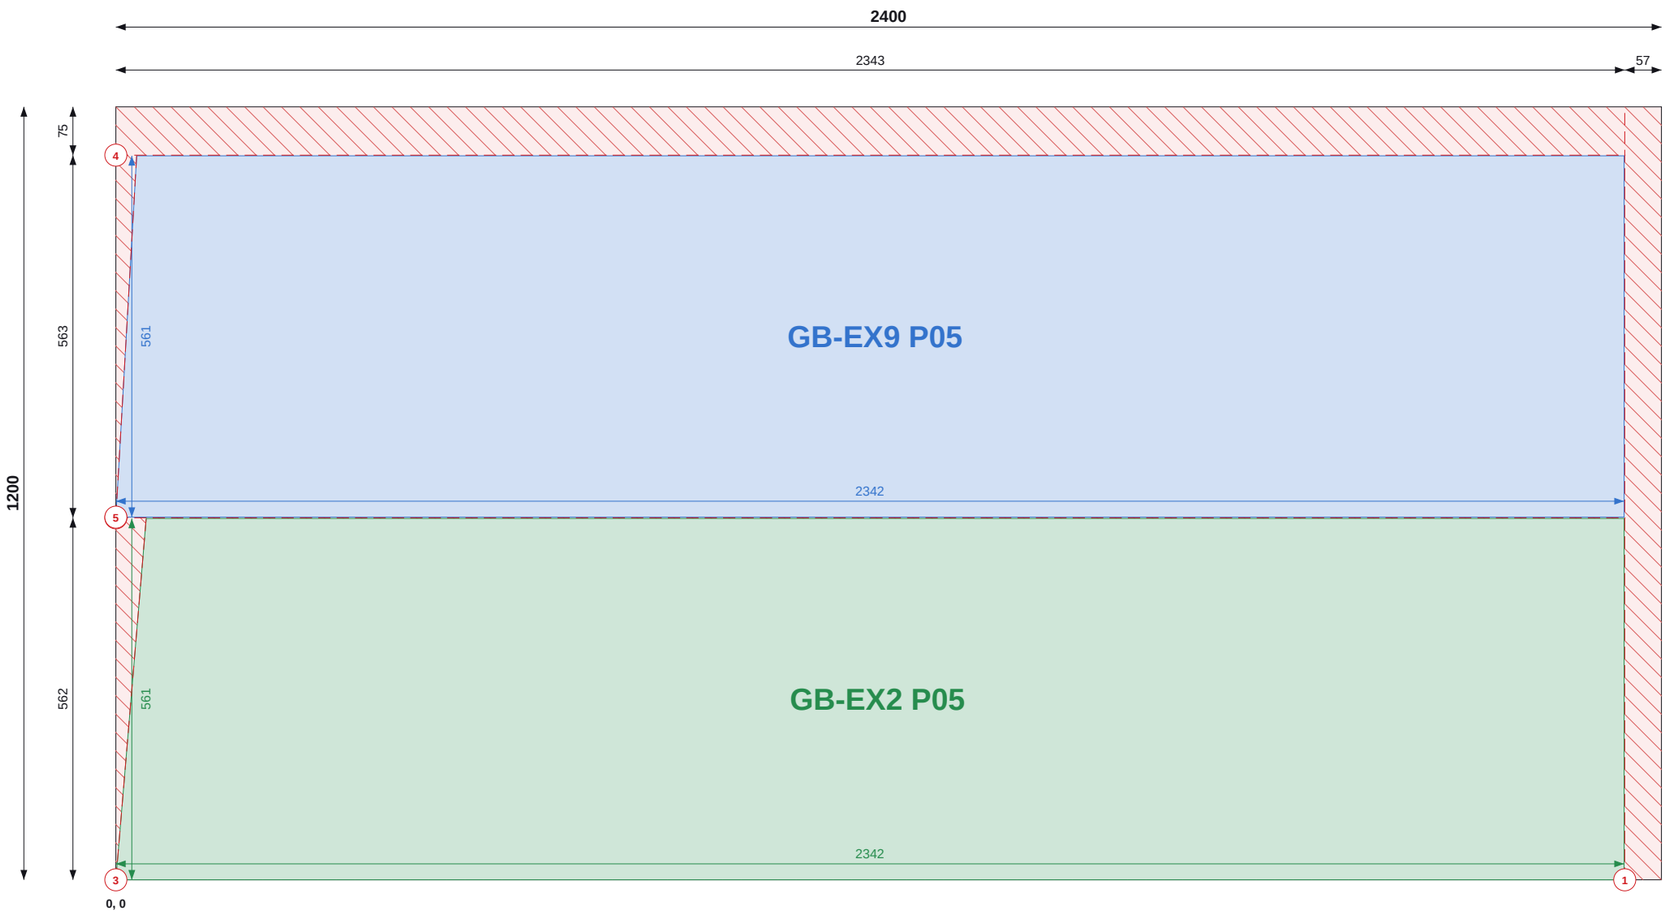

Top / left chains = saw cut positions (to cut centres). Coloured = part size and position.

SHEET 3 OF 18

THIS SHEET

Item	Value
Parts	2
Used / waste	90.5% / 0.27 m2
Reusable offcuts	0
Saw cuts / shared	5 / 3

PIECES (POSITION = BOTTOM-LEFT CORNER)

Label	Size	X, Y
GB-EX9 P05	561 x 2342	0, 563
GB-EX2 P05	561 x 2342	0, 0

NOTES

1. Cut from PIR 120mm 1200x2400, 2mm saw kerf. Viewed on the face; dimensions from the sheet's bottom-left corner (0,0). Red numbered lines = saw cuts in order, each edge to edge.
2. Coloured dimensions belong to the part of that colour: its width and height, and its position from the sheet edges. Raked parts: corner coordinates at each corner.
3. Red hatch = waste. Labels = panel + piece mark on the manufacture drawing.

REVISIONS

REV	DATE	DESCRIPTION
C01	14.09.26	Construction issue
C02	14.09.26	Roof trusses revised; SP diagonals added
C03	11.10.26	FF windows coursed; steel + GP1 portal; steel drawings (ST)
C04	13.10.26	Steel approved by the engineer: steel + steel timber drawings issued for constructio

TLS TIMBER FRAME
Design & Manufacture
Scan: 3D model + drawings

CLIENT	PROJECT
MP Adams	MP Adams Plot 4, Eckington


DRAWING TITLE
PIR CUTTING - GABLES - SHEET 3 OF 18

PIR 120mm 1200x2400 | Gables

SCALE	SIZE	DATE	DRAWN
NTS	A3	13.10.26	TS

STATUS	DRAWING No.	REV
CONSTRUCTION	P4-CP-PIR-03 / 03	C04

Do not scale. All dimensions in mm. Check all dimensions on site.

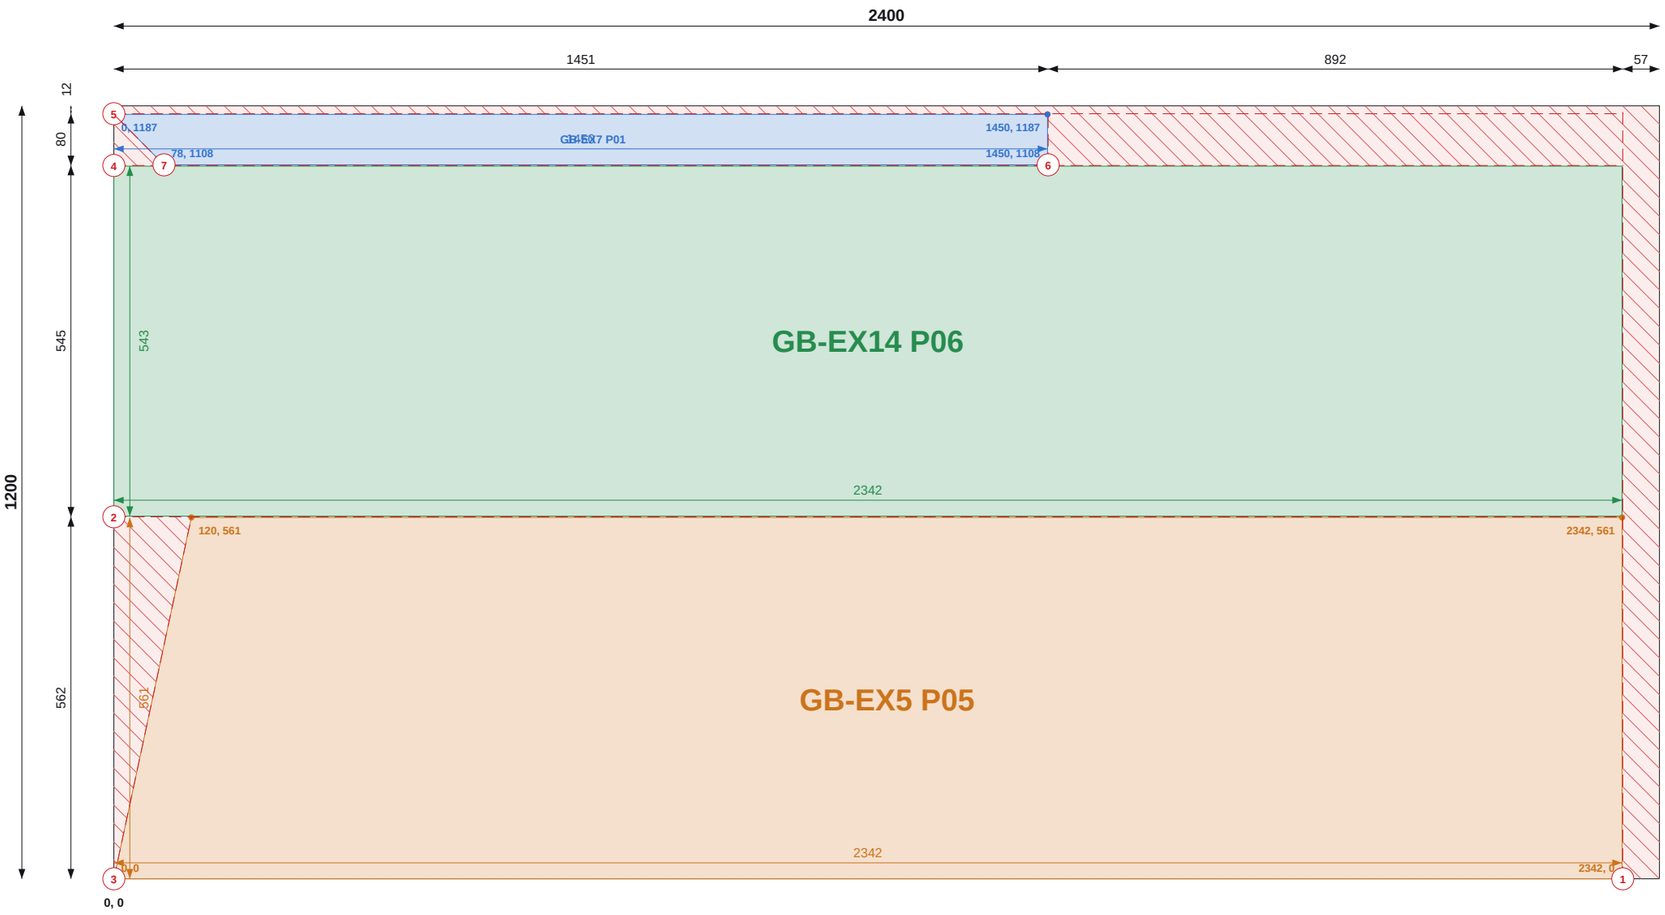

Top / left chains = saw cut positions (to cut centres). Coloured = part size and position.

SHEET 4 OF 18

THIS SHEET

Item	Value
Parts	3
Used / waste	92.5% / 0.22 m2
Reusable offcuts	0
Saw cuts / shared	7 / 4

PIECES (POSITION = BOTTOM-LEFT CORNER)

Label	Size	X, Y
GB-EX7 P01	78 x 1450 rake to 1373	0, 1108
GB-EX14 P06	543 x 2342	0, 563
GB-EX5 P05	561 x 2342 rake to 2222	0, 0

NOTES

1. Cut from PIR 120mm 1200x2400, 2mm saw kerf. Viewed on the face; dimensions from the sheet's bottom-left corner (0,0). Red numbered lines = saw cuts in order, each edge to edge.
2. Coloured dimensions belong to the part of that colour: its width and height, and its position from the sheet edges. Raked parts: corner coordinates at each corner.
3. Red hatch = waste. Labels = panel + piece mark on the manufacture drawing.

REVISIONS

REV	DATE	DESCRIPTION
C01	14.09.26	Construction issue
C02	14.09.26	Roof trusses revised; SP diagonals added
C03	11.10.26	FF windows coursed; steel + GP1 portal; steel drawings (ST)
C04	13.10.26	Steel approved by the engineer: steel + steel timber drawings issued for construction

TLS TIMBER FRAME
Design & Manufacture
Scan: 3D model + drawings

CLIENT	PROJECT
MP Adams	MP Adams Plot 4, Eckington

DRAWING TITLE


PIR CUTTING - GABLES - SHEET 4 OF 18

PIR 120mm 1200x2400 | Gables

SCALE	SIZE	DATE	DRAWN
NTS	A3	13.10.26	TS

STATUS	DRAWING No.	REV
CONSTRUCTION	P4-CP-PIR-03 / 04	C04

Do not scale. All dimensions in mm. Check all dimensions on site.

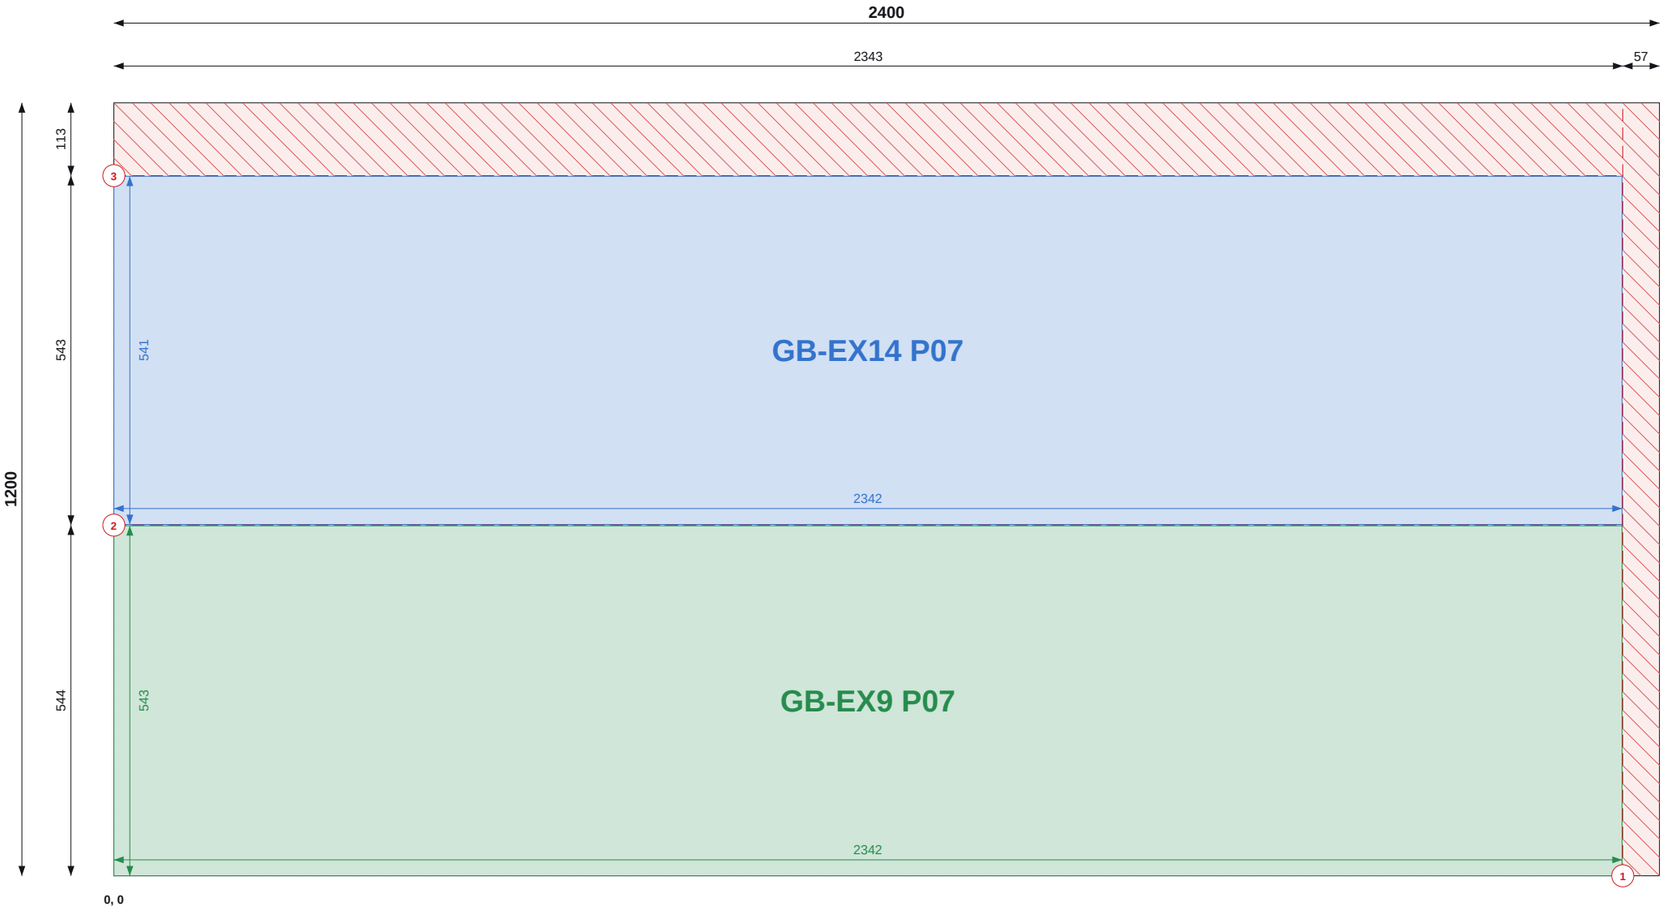

Top / left chains = saw cut positions (to cut centres). Coloured = part size and position.

SHEET 5 OF 18

THIS SHEET

Item	Value
Parts	2
Used / waste	88.2% / 0.34 m2
Reusable offcuts	0
Saw cuts / shared	3 / 1

PIECES (POSITION = BOTTOM-LEFT CORNER)

Label	Size	X, Y
GB-EX14 P07	541 x 2342	0, 545
GB-EX9 P07	543 x 2342	0, 0

NOTES

1. Cut from PIR 120mm 1200x2400, 2mm saw kerf. Viewed on the face; dimensions from the sheet's bottom-left corner (0,0). Red numbered lines = saw cuts in order, each edge to edge.
2. Coloured dimensions belong to the part of that colour: its width and height, and its position from the sheet edges. Raked parts: corner coordinates at each corner.
3. Red hatch = waste. Labels = panel + piece mark on the manufacture drawing.

REVISIONS

REV	DATE	DESCRIPTION
C01	14.09.26	Construction issue
C02	14.09.26	Roof trusses revised; SP diagonals added
C03	11.10.26	FF windows coursed; steel + GP1 portal; steel drawings (ST)
C04	13.10.26	Steel approved by the engineer: steel + steel timber drawings issued for constructio

TLS TIMBER FRAME
Design & Manufacture
Scan: 3D model + drawings

CLIENT	PROJECT
MP Adams	MP Adams Plot 4, Eckington


DRAWING TITLE
PIR CUTTING - GABLES - SHEET 5 OF 18

PIR 120mm 1200x2400 | Gables

SCALE	SIZE	DATE	DRAWN
NTS	A3	13.10.26	TS

STATUS	DRAWING No.	REV
CONSTRUCTION	P4-CP-PIR-03 / 05	C04

Do not scale. All dimensions in mm. Check all dimensions on site.

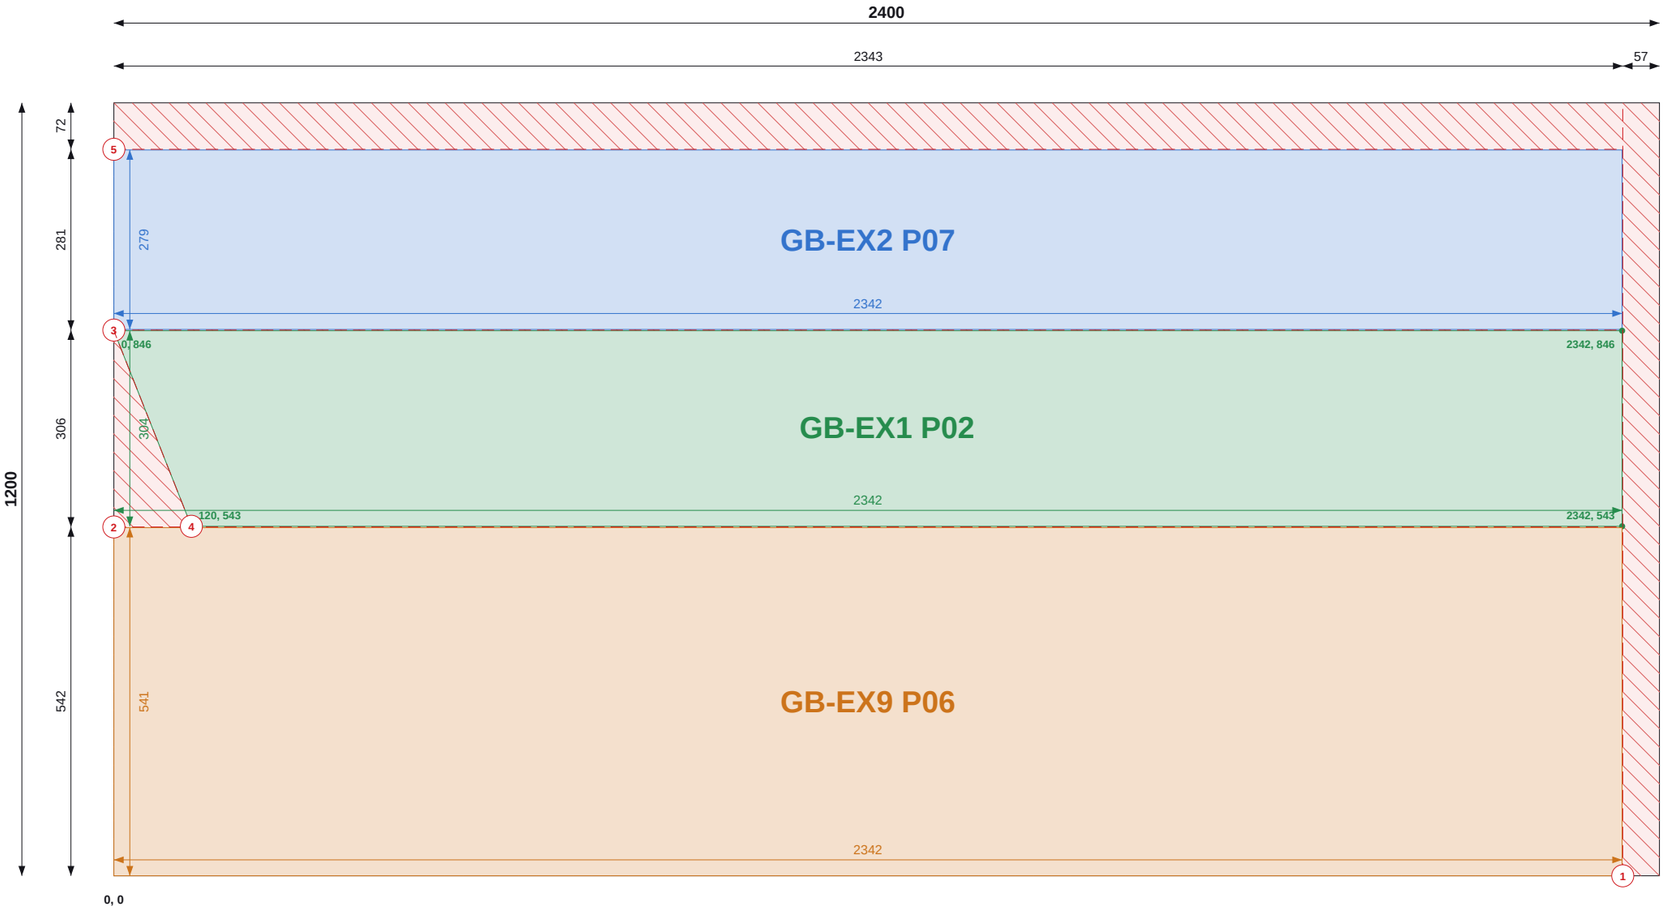

Top / left chains = saw cut positions (to cut centres). Coloured = part size and position.

SHEET 6 OF 18

THIS SHEET

Item	Value
Parts	3
Used / waste	90.7% / 0.27 m2
Reusable offcuts	0
Saw cuts / shared	5 / 3

PIECES (POSITION = BOTTOM-LEFT CORNER)

Label	Size	X, Y
GB-EX2 P07	279 x 2342	0, 848
GB-EX1 P02	304 x 2342 rake to 2222	0, 543
GB-EX9 P06	541 x 2342	0, 0

NOTES

1. Cut from PIR 120mm 1200x2400, 2mm saw kerf. Viewed on the face; dimensions from the sheet's bottom-left corner (0,0). Red numbered lines = saw cuts in order, each edge to edge.
2. Coloured dimensions belong to the part of that colour: its width and height, and its position from the sheet edges. Raked parts: corner coordinates at each corner.
3. Red hatch = waste. Labels = panel + piece mark on the manufacture drawing.

REVISIONS

REV	DATE	DESCRIPTION
C01	14.09.26	Construction issue
C02	14.09.26	Roof trusses revised; SP diagonals added
C03	11.10.26	FF windows coursed; steel + GP1 portal; steel drawings (ST)
C04	13.10.26	Steel approved by the engineer: steel + steel timber drawings issued for constructio

TLS TIMBER FRAME
Design & Manufacture
Scan: 3D model + drawings

CLIENT	PROJECT
MP Adams	MP Adams Plot 4, Eckington

DRAWING TITLE


PIR CUTTING - GABLES - SHEET 6 OF 18

PIR 120mm 1200x2400 | Gables

SCALE	SIZE	DATE	DRAWN
NTS	A3	13.10.26	TS

STATUS	DRAWING No.	REV
CONSTRUCTION	P4-CP-PIR-03 / 06	C04

Do not scale. All dimensions in mm. Check all dimensions on site.

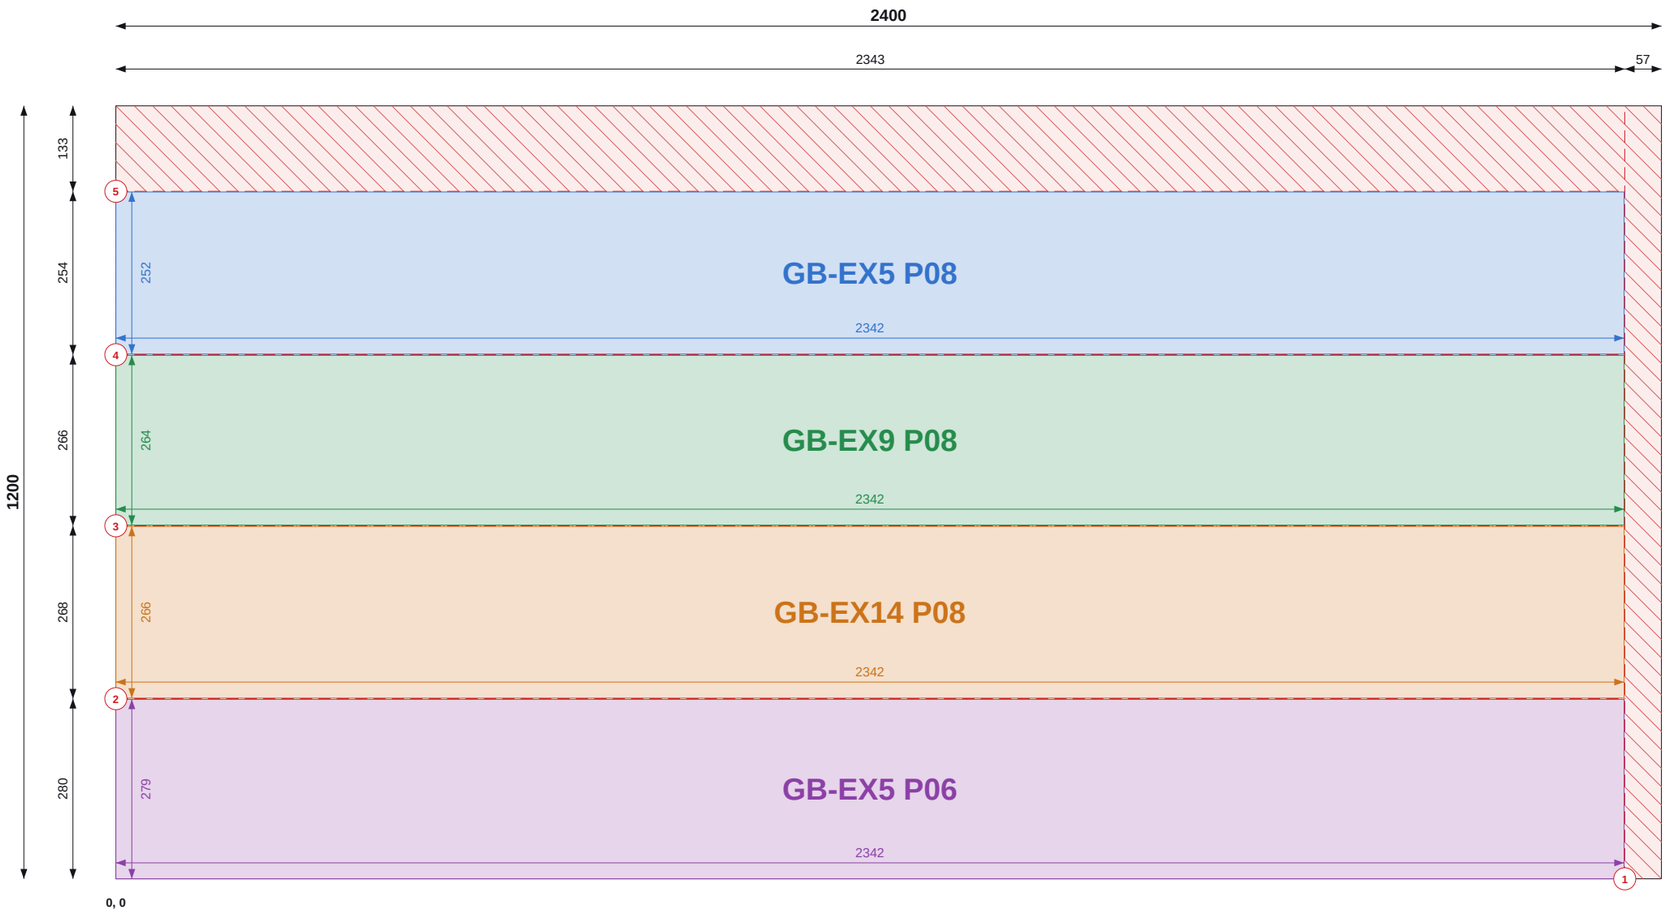

Top / left chains = saw cut positions (to cut centres). Coloured = part size and position.

SHEET 7 OF 18

THIS SHEET

Item	Value
Parts	4
Used / waste	86.2% / 0.40 m2
Reusable offcuts	0
Saw cuts / shared	5 / 3

PIECES (POSITION = BOTTOM-LEFT CORNER)

Label	Size	X, Y
GB-EX5 P08	252 x 2342	0, 815
GB-EX9 P08	264 x 2342	0, 549
GB-EX14 P08	266 x 2342	0, 281
GB-EX5 P06	279 x 2342	0, 0

NOTES

1. Cut from PIR 120mm 1200x2400, 2mm saw kerf. Viewed on the face; dimensions from the sheet's bottom-left corner (0,0). Red numbered lines = saw cuts in order, each edge to edge.
2. Coloured dimensions belong to the part of that colour: its width and height, and its position from the sheet edges. Raked parts: corner coordinates at each corner.
3. Red hatch = waste. Labels = panel + piece mark on the manufacture drawing.

REVISIONS

REV	DATE	DESCRIPTION
C01	14.09.26	Construction issue
C02	14.09.26	Roof trusses revised; SP diagonals added
C03	11.10.26	FF windows coursed; steel + GP1 portal; steel drawings (ST)
C04	13.10.26	Steel approved by the engineer: steel + steel timber drawings issued for construction

TLS TIMBER FRAME DESIGN SUITE

TLS TIMBER FRAME

Design & Manufacture

Scan: 3D model + drawings

CLIENT	PROJECT
MP Adams	MP Adams Plot 4, Eckington

DRAWING TITLE


PIR CUTTING - GABLES - SHEET 7 OF 18

PIR 120mm 1200x2400 | Gables

SCALE	SIZE	DATE	DRAWN
NTS	A3	13.10.26	TS

STATUS	DRAWING No.	REV
CONSTRUCTION	P4-CP-PIR-03 / 07	C04

Do not scale. All dimensions in mm. Check all dimensions on site.

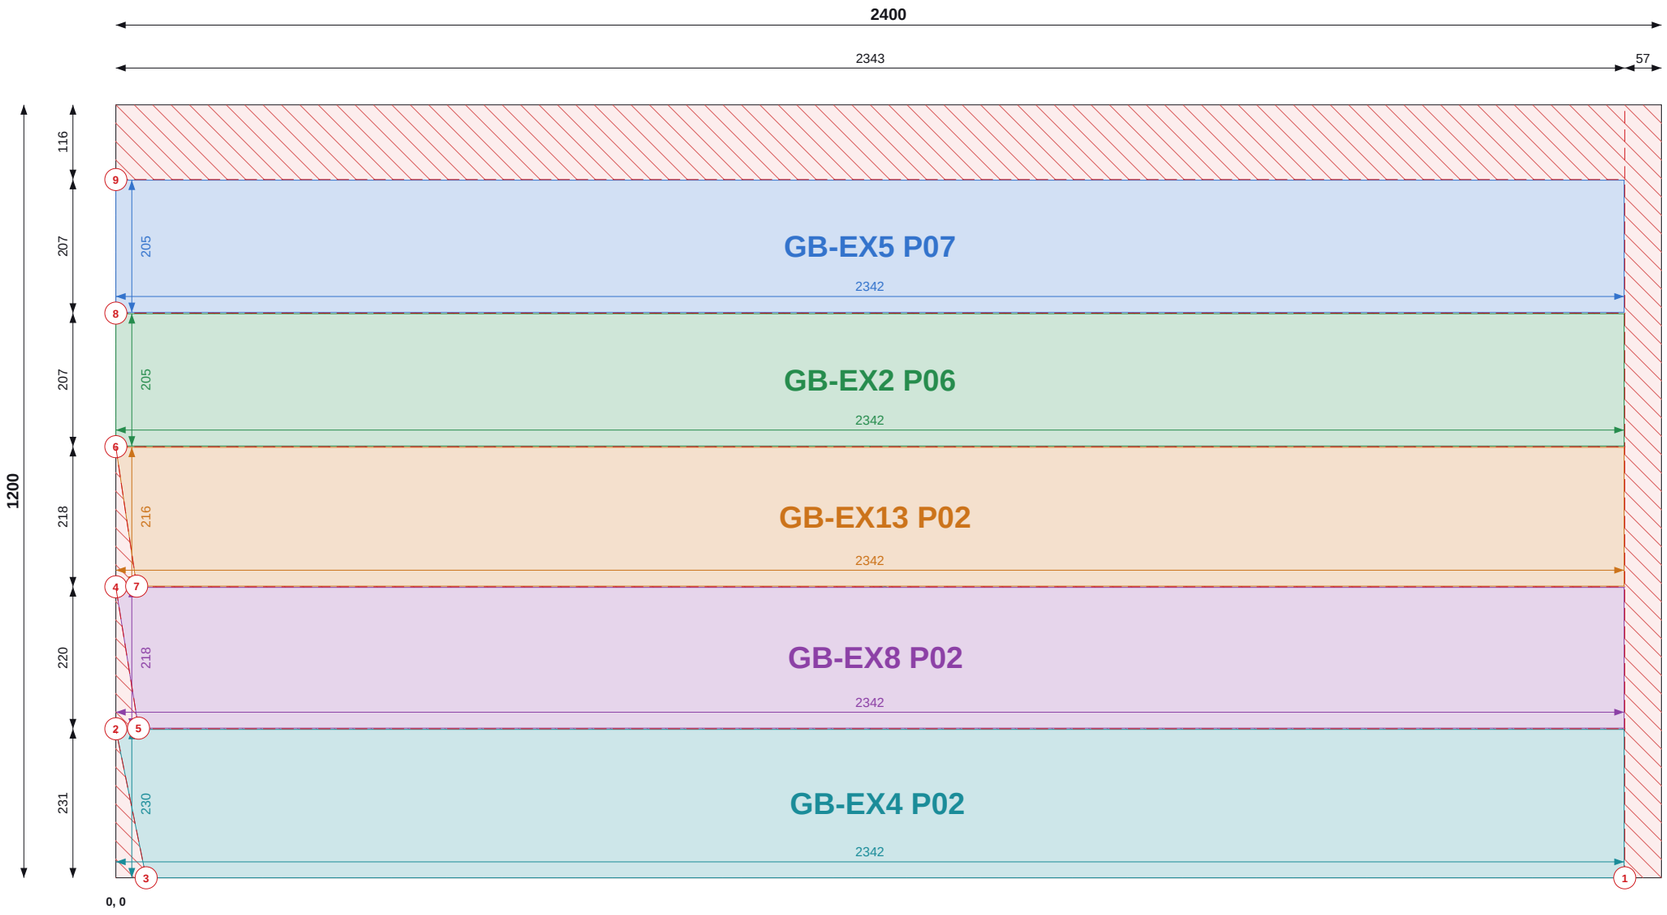

Top / left chains = saw cut positions (to cut centres). Coloured = part size and position.

SHEET 8 OF 18

THIS SHEET

Item	Value
Parts	5
Used / waste	87.0% / 0.37 m2
Reusable offcuts	0
Saw cuts / shared	9 / 7

PIECES (POSITION = BOTTOM-LEFT CORNER)

Label	Size	X, Y
GB-EX5 P07	205 x 2342	0, 878
GB-EX2 P06	205 x 2342	0, 670
GB-EX13 P02	216 x 2342	0, 453
GB-EX8 P02	218 x 2342	0, 232
GB-EX4 P02	230 x 2342	0, 0

NOTES

1. Cut from PIR 120mm 1200x2400, 2mm saw kerf. Viewed on the face; dimensions from the sheet's bottom-left corner (0,0). Red numbered lines = saw cuts in order, each edge to edge.
2. Coloured dimensions belong to the part of that colour: its width and height, and its position from the sheet edges. Raked parts: corner coordinates at each corner.
3. Red hatch = waste. Labels = panel + piece mark on the manufacture drawing.

REVISIONS

REV	DATE	DESCRIPTION
C01	14.09.26	Construction issue
C02	14.09.26	Roof trusses revised; SP diagonals added
C03	11.10.26	FF windows coursed; steel + GP1 portal; steel drawings (ST)
C04	13.10.26	Steel approved by the engineer: steel + steel timber drawings issued for constructio

TLS TIMBER FRAME
Design & Manufacture
Scan: 3D model + drawings

CLIENT	PROJECT
MP Adams	MP Adams Plot 4, Eckington

DRAWING TITLE


PIR CUTTING - GABLES - SHEET 8 OF 18

PIR 120mm 1200x2400 | Gables

SCALE	SIZE	DATE	DRAWN
NTS	A3	13.10.26	TS

STATUS	DRAWING No.	REV
CONSTRUCTION	P4-CP-PIR-03 / 08	C04

Do not scale. All dimensions in mm. Check all dimensions on site.

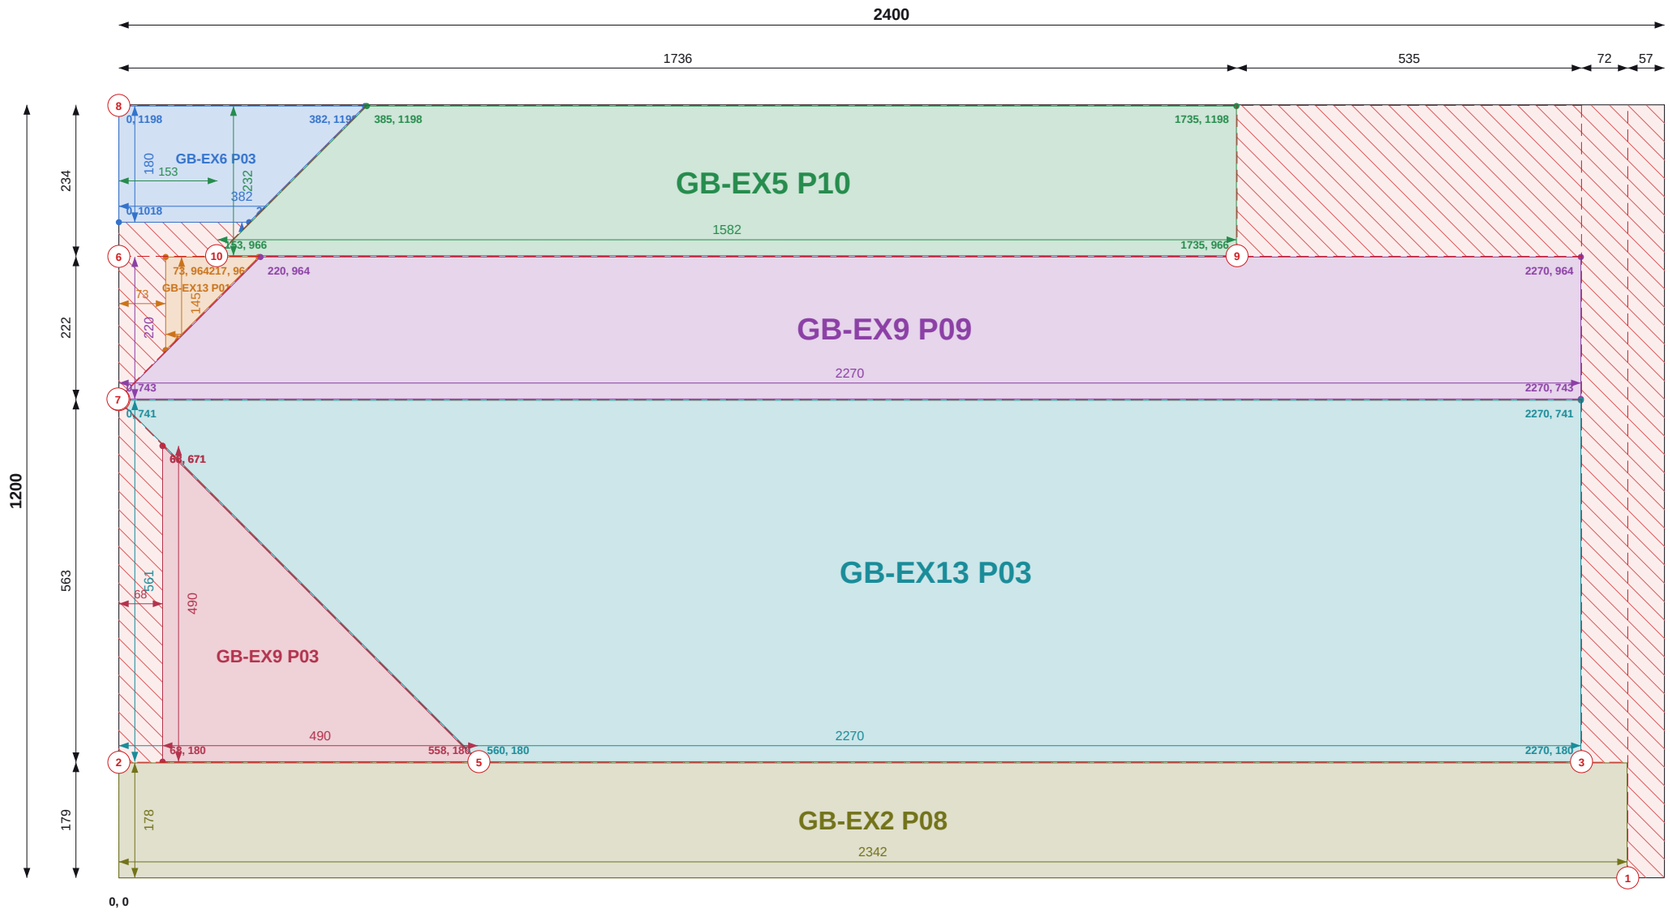

Top / left chains = saw cut positions (to cut centres). Coloured = part size and position.

Do not scale. All dimensions in mm. Check all dimensions on site.

SHEET 9 OF 18

THIS SHEET

Item	Value
Parts	7
Used / waste	88.0% / 0.35 m2
Reusable offcuts	0
Saw cuts / shared	10 / 6

PIECES (POSITION = BOTTOM-LEFT CORNER)

Label	Size	X, Y
GB-EX6 P03	180 x 382 rake to 203	0, 1018
GB-EX5 P10	232 x 1582 rake to 1351	153, 966
GB-EX13 P01	145 x 144 rake to 1	73, 819
GB-EX9 P09	220 x 2270 rake to 2051	0, 743
GB-EX13 P03	561 x 2270 rake to 1711	0, 180
GB-EX9 P03	490 x 490 rake to 1	68, 180
GB-EX2 P08	178 x 2342	0, 0

NOTES

1. Cut from PIR 120mm 1200x2400, 2mm saw kerf. Viewed on the face; dimensions from the sheet's bottom-left corner (0,0). Red numbered lines = saw cuts in order, each edge to edge.
2. Coloured dimensions belong to the part of that colour: its width and height, and its position from the sheet edges. Raked parts: corner coordinates at each corner.
3. Red hatch = waste. Labels = panel + piece mark on the manufacture drawing.

REVISIONS

REV	DATE	DESCRIPTION
C01	14.09.26	Construction issue
C02	14.09.26	Roof trusses revised; SP diagonals added
C03	11.10.26	FF windows coursed; steel + GP1 portal; steel drawings (ST)
C04	13.10.26	Steel approved by the engineer: steel + steel timber drawings issued for construction

TLS TIMBER FRAME
Design & Manufacture
Scan: 3D model + drawings

CLIENT	PROJECT
MP Adams	MP Adams Plot 4, Eckington


DRAWING TITLE

PIR CUTTING - GABLES - SHEET 9 OF 18

PIR 120mm 1200x2400 | Gables

SCALE	SIZE	DATE	DRAWN
NTS	A3	13.10.26	TS

STATUS	DRAWING No.	REV
CONSTRUCTION	P4-CP-PIR-03 / 09	C04

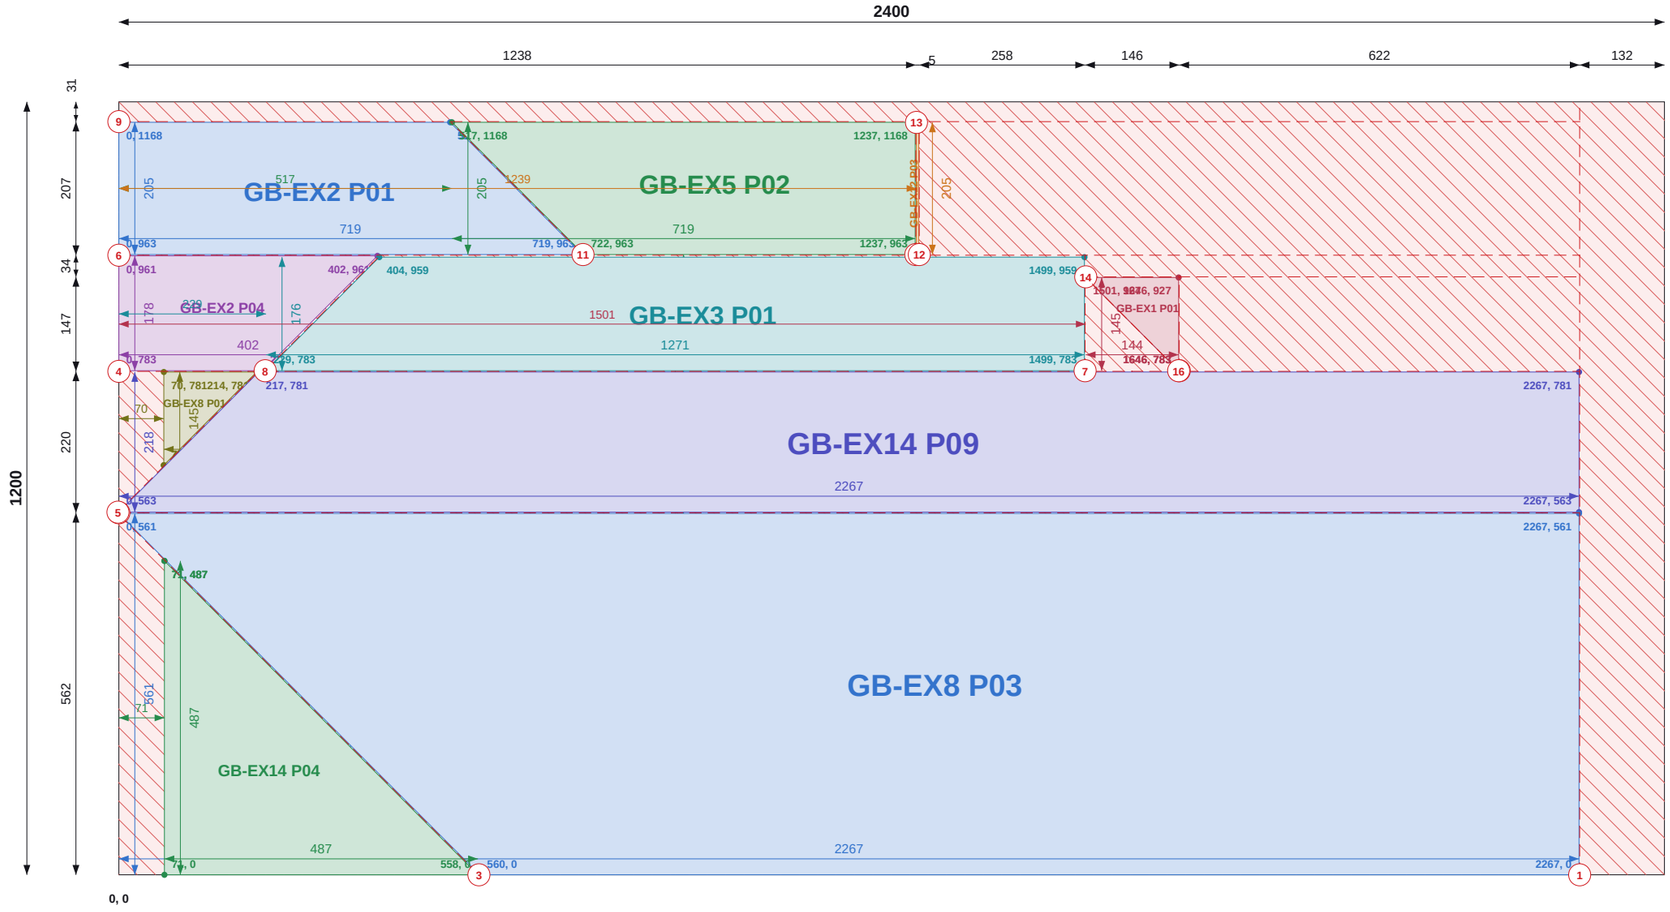

Top / left chains = saw cut positions (to cut centres). Coloured = part size and position.

Do not scale. All dimensions in mm. Check all dimensions on site.

SHEET 10 OF 18

THIS SHEET

Item	Value
Parts	10
Used / waste	77.9% / 0.64 m2
Reusable offcuts	0
Saw cuts / shared	16 / 11

PIECES (POSITION = BOTTOM-LEFT CORNER)

Label	Size	X, Y
GB-EX2 P01	205 x 719 rake to 516	0, 963
GB-EX5 P02	205 x 719 rake to 516	517, 963
GB-EX12 P03	3 x 205	1239, 963
GB-EX2 P04	178 x 402 rake to 225	0, 783
GB-EX3 P01	176 x 1271 rake to 1096	229, 783
GB-EX1 P01	145 x 144 rake to 1	1501, 783
GB-EX8 P01	145 x 144 rake to 1	70, 636
GB-EX14 P09	218 x 2267 rake to 2051	0, 563
GB-EX8 P03	561 x 2267 rake to 1708	0, 0
GB-EX14 P04	487 x 487 rake to 1	71, 0

NOTES

1. Cut from PIR 120mm 1200x2400, 2mm saw kerf. Viewed on the face; dimensions from the sheet's bottom-left corner (0,0). Red numbered lines = saw cuts in order, each edge to edge.
2. Coloured dimensions belong to the part of that colour: its width and height, and its position from the sheet edges. Raked parts: corner coordinates at each corner.
3. Red hatch = waste. Labels = panel + piece mark on the manufacture drawing.

REVISIONS

REV	DATE	DESCRIPTION
C01	14.09.26	Construction issue
C02	14.09.26	Roof trusses revised; SP diagonals added
C03	11.10.26	FF windows coursed; steel + GP1 portal; steel drawings (ST)
C04	13.10.26	Steel approved by the engineer: steel + steel timber drawings issued for constructio

TLS TIMBER FRAME
Design & Manufacture
Scan: 3D model + drawings


CLIENT	PROJECT
MP Adams	MP Adams Plot 4, Eckington

DRAWING TITLE
PIR CUTTING - GABLES - SHEET 10 OF 18

PIR 120mm 1200x2400 | Gables

SCALE	SIZE	DATE	DRAWN
NTS	A3	13.10.26	TS

STATUS	DRAWING No.	REV
CONSTRUCTION	P4-CP-PIR-03 / 10	C04

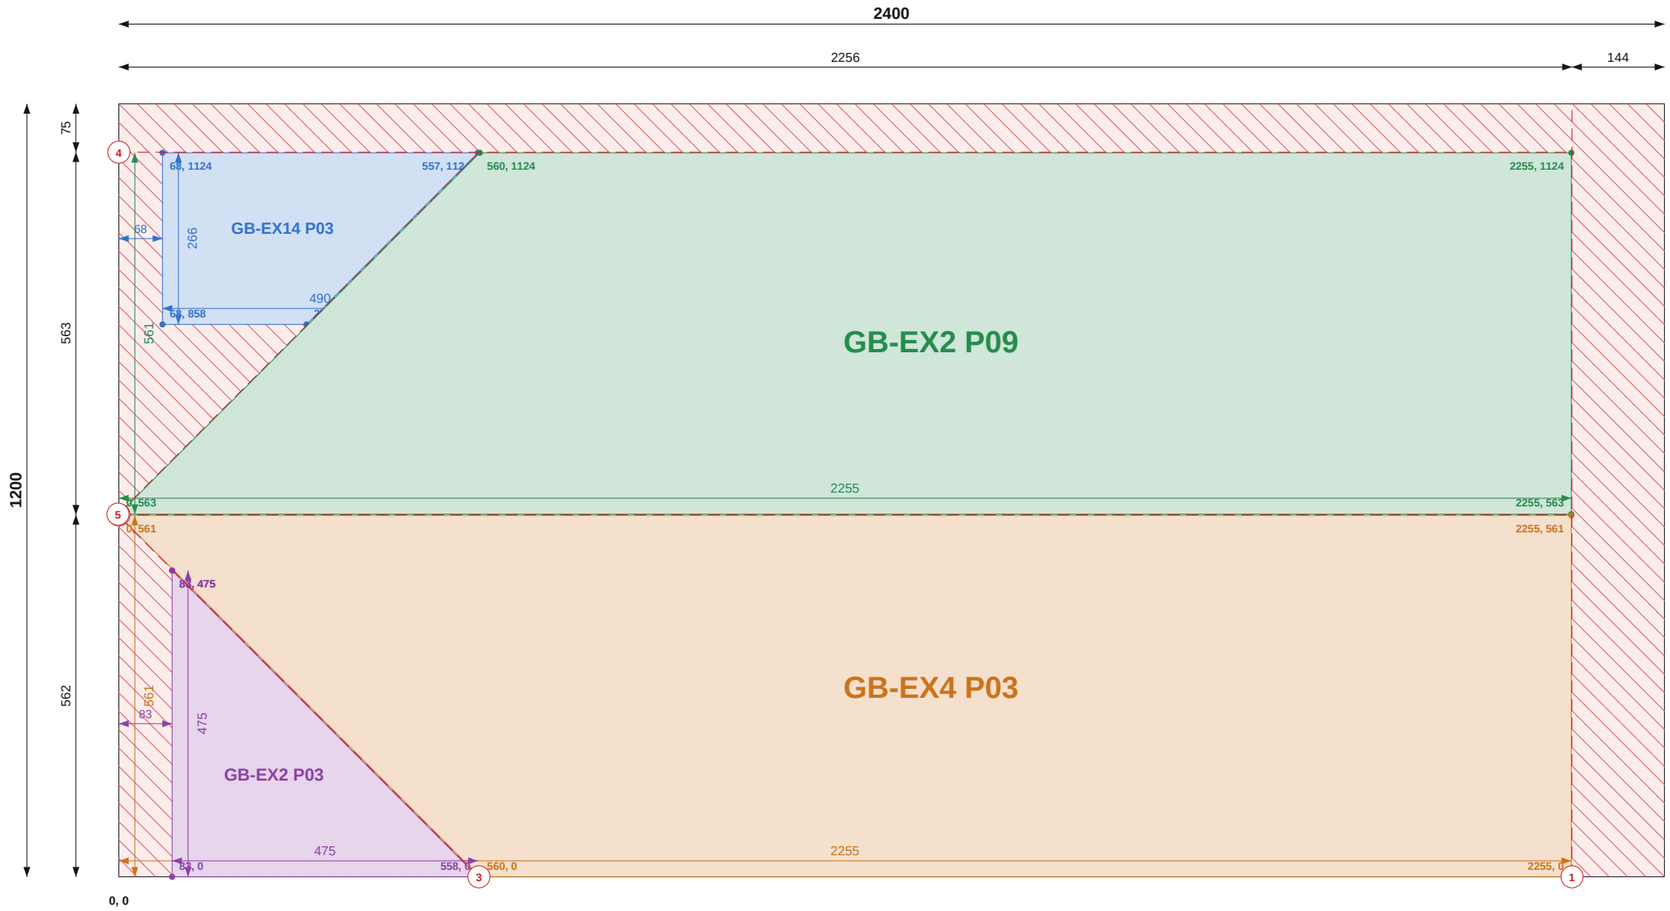

Top / left chains = saw cut positions (to cut centres). Coloured = part size and position.

SHEET 11 OF 18

THIS SHEET

Item	Value
Parts	4
Used / waste	84.2% / 0.46 m2
Reusable offcuts	0
Saw cuts / shared	5 / 3

PIECES (POSITION = BOTTOM-LEFT CORNER)

Label	Size	X, Y
GB-EX14 P03	266 x 490 rake to 225	68, 858
GB-EX2 P09	561 x 2255 rake to 1696	0, 563
GB-EX4 P03	561 x 2255 rake to 1696	0, 0
GB-EX2 P03	475 x 475 rake to 1	83, 0

NOTES

1. Cut from PIR 120mm 1200x2400, 2mm saw kerf. Viewed on the face; dimensions from the sheet's bottom-left corner (0,0). Red numbered lines = saw cuts in order, each edge to edge.
2. Coloured dimensions belong to the part of that colour: its width and height, and its position from the sheet edges. Raked parts: corner coordinates at each corner.
3. Red hatch = waste. Labels = panel + piece mark on the manufacture drawing.

REVISIONS

REV	DATE	DESCRIPTION
C01	14.09.26	Construction issue
C02	14.09.26	Roof trusses revised; SP diagonals added
C03	11.10.26	FF windows coursed; steel + GP1 portal; steel drawings (ST)
C04	13.10.26	Steel approved by the engineer: steel + steel timber drawings issued for construction

TLS TIMBER FRAME
Design & Manufacture
Scan: 3D model + drawings

CLIENT	PROJECT
MP Adams	MP Adams Plot 4, Eckington

DRAWING TITLE


PIR CUTTING - GABLES - SHEET 11 OF 18

PIR 120mm 1200x2400 | Gables

SCALE	SIZE	DATE	DRAWN
NTS	A3	13.10.26	TS

STATUS	DRAWING No.	REV
CONSTRUCTION	P4-CP-PIR-03 / 11	C04

Do not scale. All dimensions in mm. Check all dimensions on site.

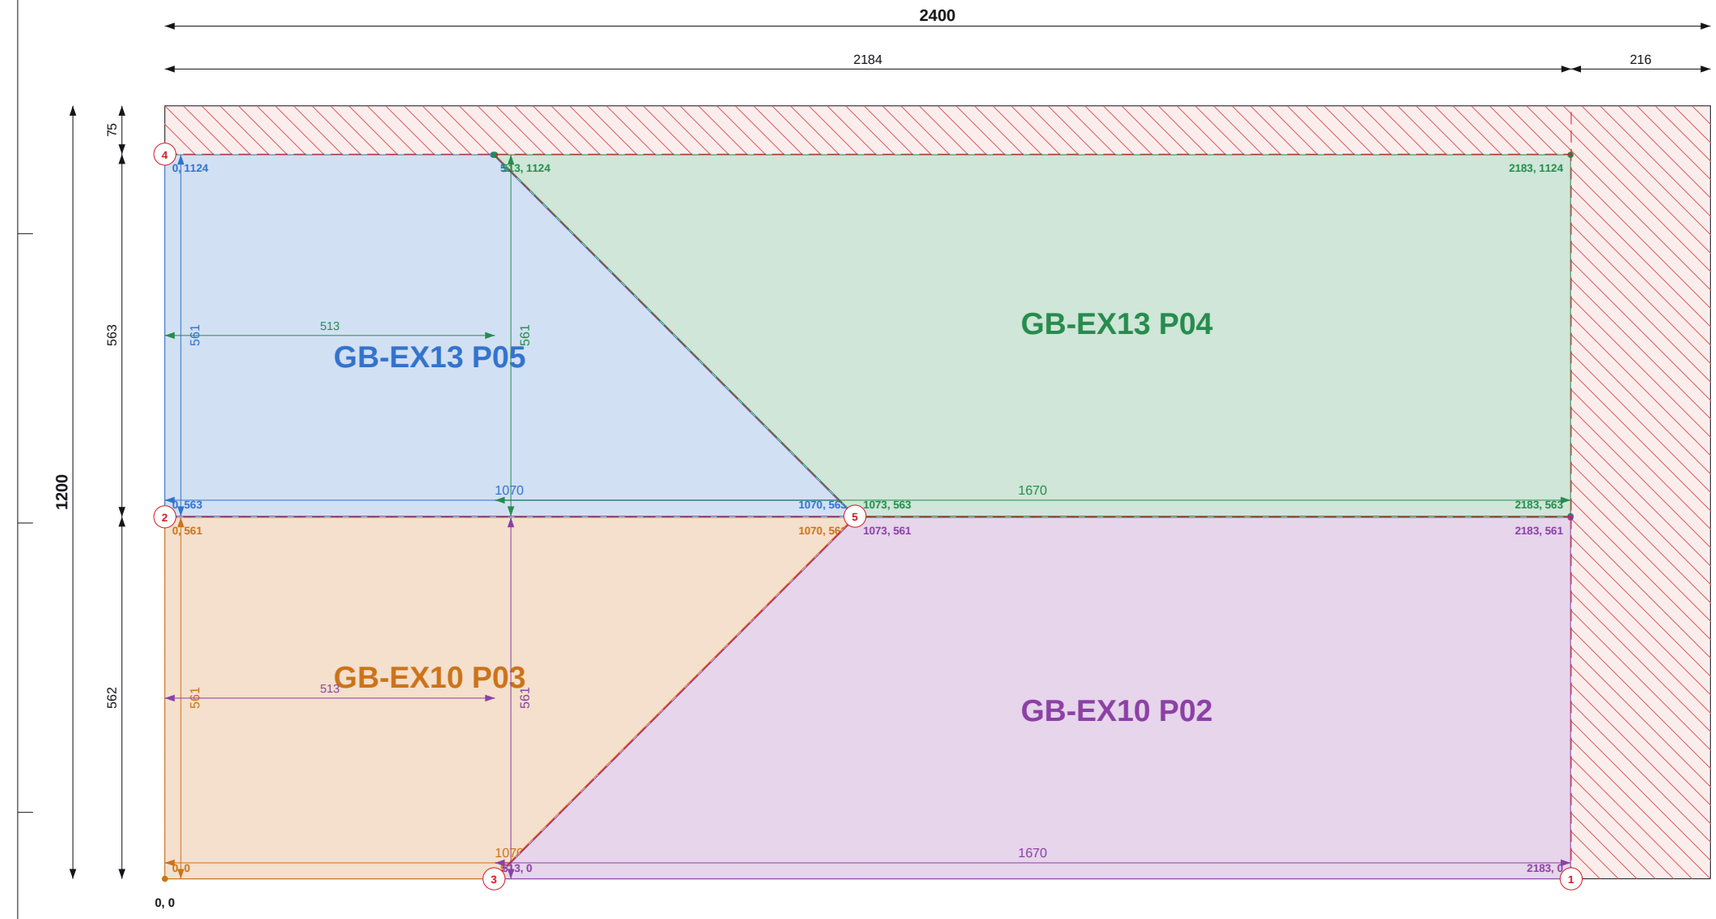

Top / left chains = saw cut positions (to cut centres). Coloured = part size and position.

Do not scale. All dimensions in mm. Check all dimensions on site.

SHEET 12 OF 18

THIS SHEET

Item	Value
Parts	4
Used / waste	84.9% / 0.43 m2
Reusable offcuts	0
Saw cuts / shared	5 / 3

PIECES (POSITION = BOTTOM-LEFT CORNER)

Label	Size	X, Y
GB-EX13 P05	561 x 1070 rake to 511	0, 563
GB-EX13 P04	561 x 1670 rake to 1111	513, 563
GB-EX10 P03	561 x 1070 rake to 511	0, 0
GB-EX10 P02	561 x 1670 rake to 1111	513, 0

NOTES

1. Cut from PIR 120mm 1200x2400, 2mm saw kerf. Viewed on the face; dimensions from the sheet's bottom-left corner (0,0). Red numbered lines = saw cuts in order, each edge to edge.
2. Coloured dimensions belong to the part of that colour: its width and height, and its position from the sheet edges. Raked parts: corner coordinates at each corner.
3. Red hatch = waste. Labels = panel + piece mark on the manufacture drawing.

REVISIONS

REV	DATE	DESCRIPTION
C01	14.09.26	Construction issue
C02	14.09.26	Roof trusses revised; SP diagonals added
C03	11.10.26	FF windows coursed; steel + GP1 portal; steel drawings (ST)
C04	13.10.26	Steel approved by the engineer: steel + steel timber drawings issued for construction

TLS TIMBER FRAME
Design & Manufacture
Scan: 3D model + drawings

CLIENT	PROJECT
MP Adams	MP Adams Plot 4, Eckington


DRAWING TITLE

PIR CUTTING - GABLES - SHEET 12 OF 18

PIR 120mm 1200x2400 | Gables

SCALE	SIZE	DATE	DRAWN
NTS	A3	13.10.26	TS

STATUS	DRAWING No.	REV
CONSTRUCTION	P4-CP-PIR-03 / 12	C04

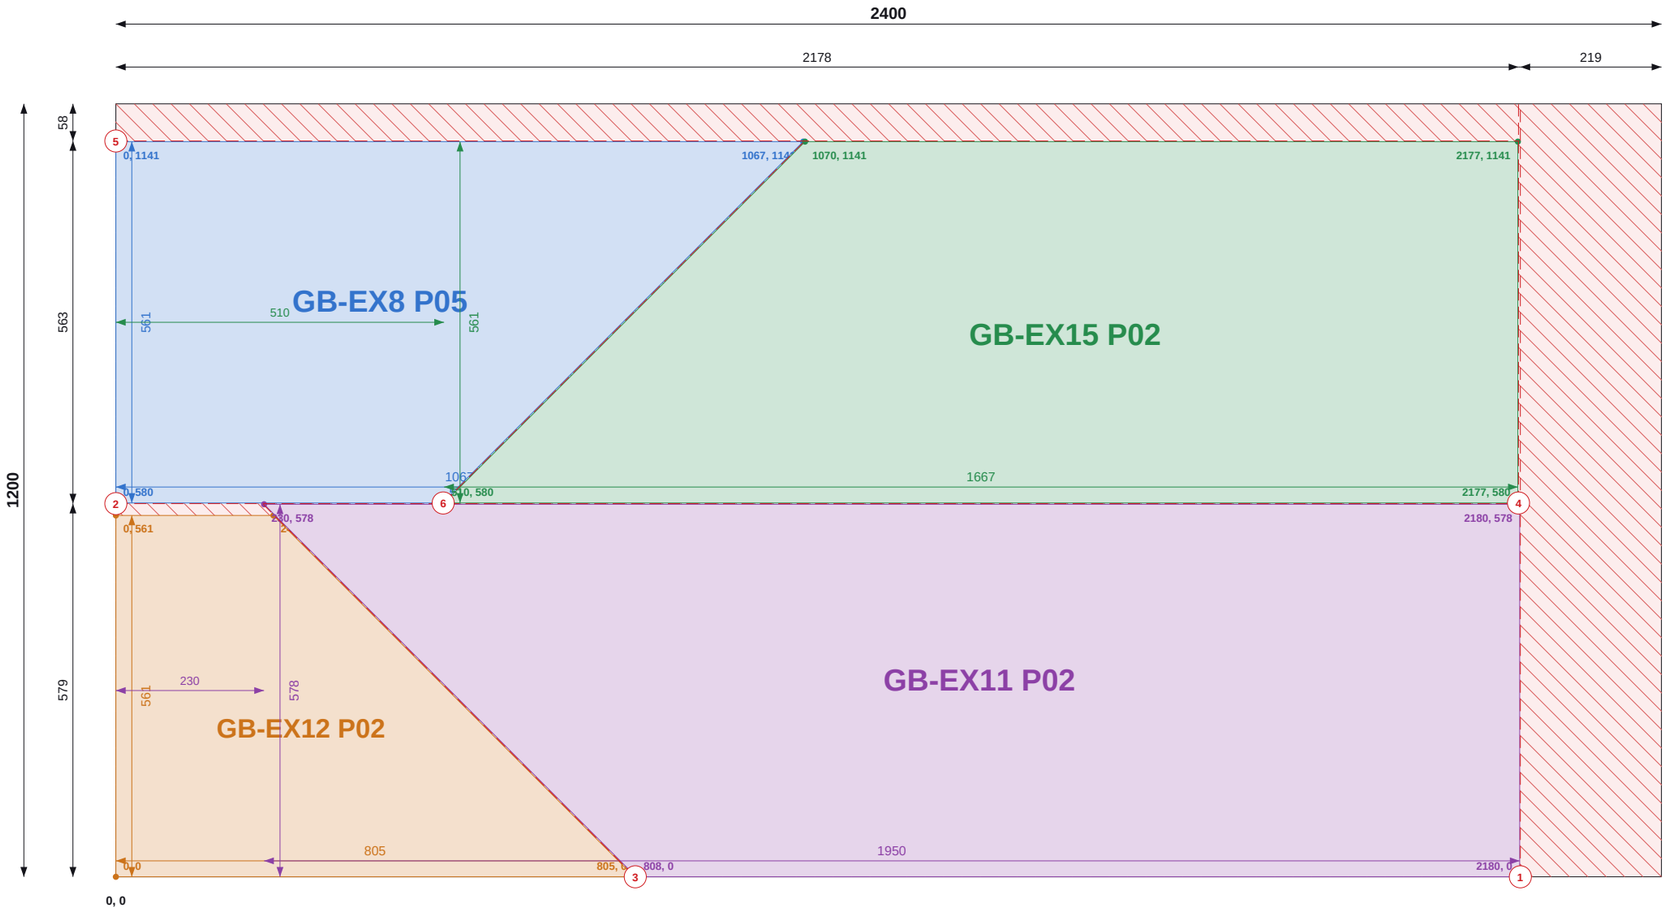

Top / left chains = saw cut positions (to cut centres). Coloured = part size and position.

Do not scale. All dimensions in mm. Check all dimensions on site.

SHEET 13 OF 18

THIS SHEET

Item	Value
Parts	4
Used / waste	85.9% / 0.41 m2
Reusable offcuts	0
Saw cuts / shared	6 / 3

PIECES (POSITION = BOTTOM-LEFT CORNER)

Label	Size	X, Y
GB-EX8 P05	561 x 1067 rake to 508	0, 580
GB-EX15 P02	561 x 1667 rake to 1108	510, 580
GB-EX12 P02	561 x 805 rake to 246	0, 0
GB-EX11 P02	578 x 1950 rake to 1373	230, 0

NOTES

1. Cut from PIR 120mm 1200x2400, 2mm saw kerf. Viewed on the face; dimensions from the sheet's bottom-left corner (0,0). Red numbered lines = saw cuts in order, each edge to edge.
2. Coloured dimensions belong to the part of that colour: its width and height, and its position from the sheet edges. Raked parts: corner coordinates at each corner.
3. Red hatch = waste. Labels = panel + piece mark on the manufacture drawing.

REVISIONS

REV	DATE	DESCRIPTION
C01	14.09.26	Construction issue
C02	14.09.26	Roof trusses revised; SP diagonals added
C03	11.10.26	FF windows coursed; steel + GP1 portal; steel drawings (ST)
C04	13.10.26	Steel approved by the engineer: steel + steel timber drawings issued for constructio

TLS

TLS TIMBER FRAME

Design & Manufacture

Scan: 3D model + drawings

CLIENT	PROJECT
MP Adams	MP Adams Plot 4, Eckington


DRAWING TITLE

PIR CUTTING - GABLES - SHEET 13 OF 18

PIR 120mm 1200x2400 | Gables

SCALE	SIZE	DATE	DRAWN
NTS	A3	13.10.26	TS

STATUS	DRAWING No.	REV
CONSTRUCTION	P4-CP-PIR-03 / 13	C04

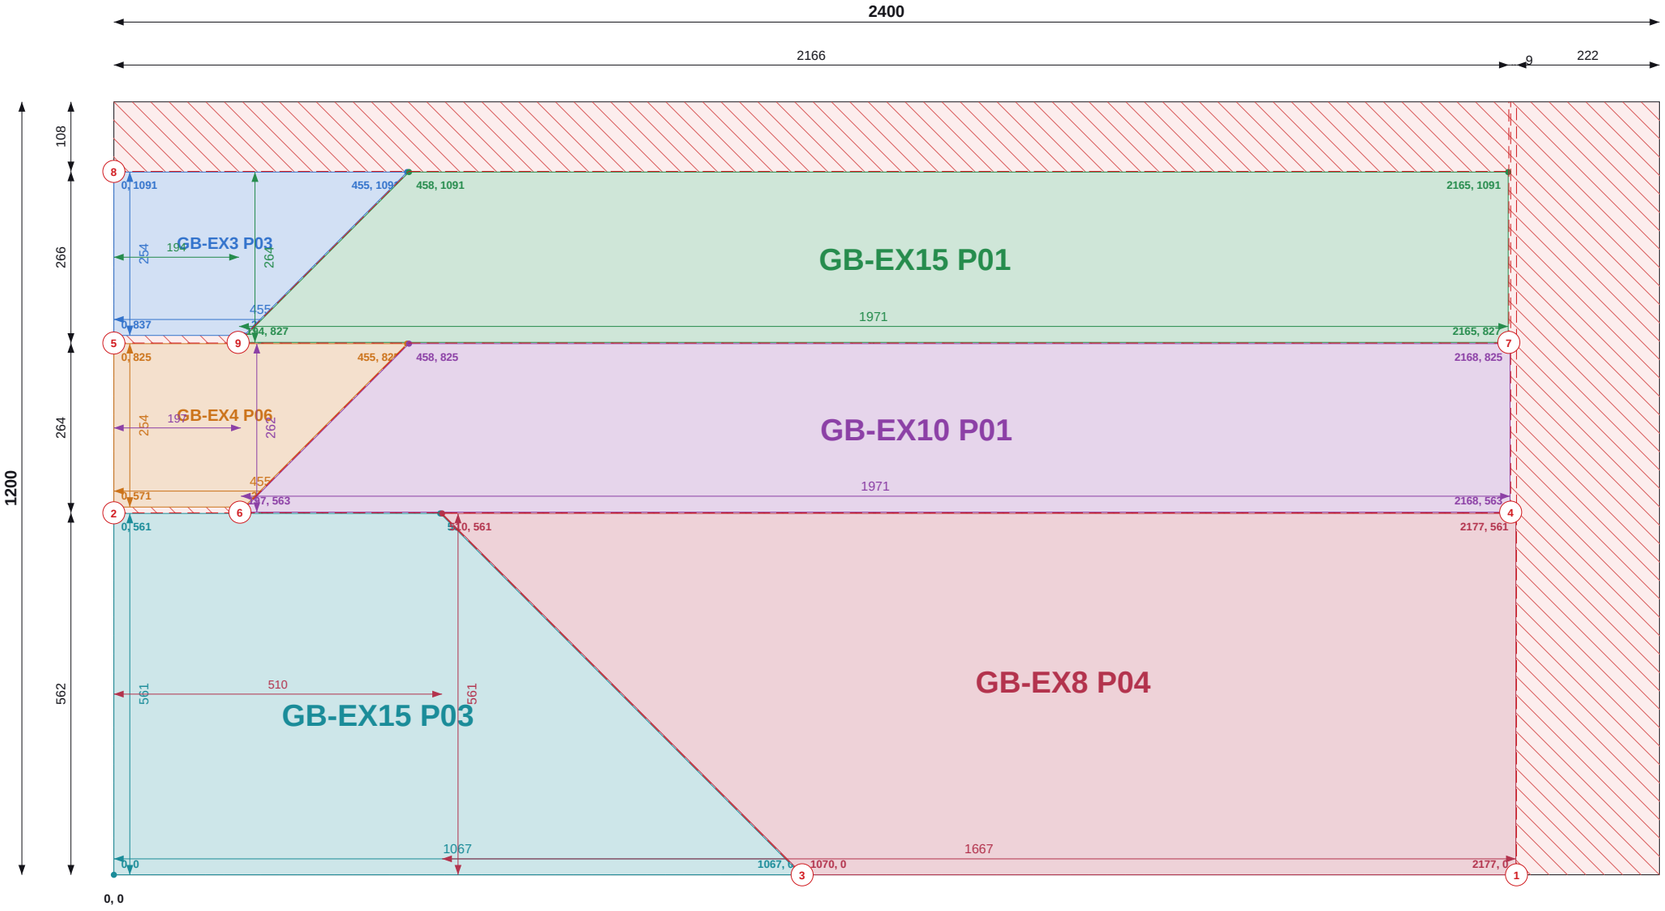

Top / left chains = saw cut positions (to cut centres). Coloured = part size and position.

Do not scale. All dimensions in mm. Check all dimensions on site.

SHEET 14 OF 18

THIS SHEET

Item	Value
Parts	6
Used / waste	81.7% / 0.53 m2
Reusable offcuts	0
Saw cuts / shared	9 / 5

PIECES (POSITION = BOTTOM-LEFT CORNER)

Label	Size	X, Y
GB-EX3 P03	254 x 455 rake to 203	0, 837
GB-EX15 P01	264 x 1971 rake to 1708	194, 827
GB-EX4 P06	254 x 455 rake to 203	0, 571
GB-EX10 P01	262 x 1971 rake to 1711	197, 563
GB-EX15 P03	561 x 1067 rake to 508	0, 0
GB-EX8 P04	561 x 1667 rake to 1108	510, 0

NOTES

1. Cut from PIR 120mm 1200x2400, 2mm saw kerf. Viewed on the face; dimensions from the sheet's bottom-left corner (0,0). Red numbered lines = saw cuts in order, each edge to edge.
2. Coloured dimensions belong to the part of that colour: its width and height, and its position from the sheet edges. Raked parts: corner coordinates at each corner.
3. Red hatch = waste. Labels = panel + piece mark on the manufacture drawing.

REVISIONS

REV	DATE	DESCRIPTION
C01	14.09.26	Construction issue
C02	14.09.26	Roof trusses revised; SP diagonals added
C03	11.10.26	FF windows coursed; steel + GP1 portal; steel drawings (ST)
C04	13.10.26	Steel approved by the engineer: steel + steel timber drawings issued for constructio

TLS TIMBER FRAME
Design & Manufacture
Scan: 3D model + drawings


CLIENT	PROJECT
MP Adams	MP Adams Plot 4, Eckington

DRAWING TITLE
PIR CUTTING - GABLES - SHEET 14 OF 18

PIR 120mm 1200x2400 | Gables

SCALE	SIZE	DATE	DRAWN
NTS	A3	13.10.26	TS

STATUS	DRAWING No.	REV
CONSTRUCTION	P4-CP-PIR-03 / 14	C04

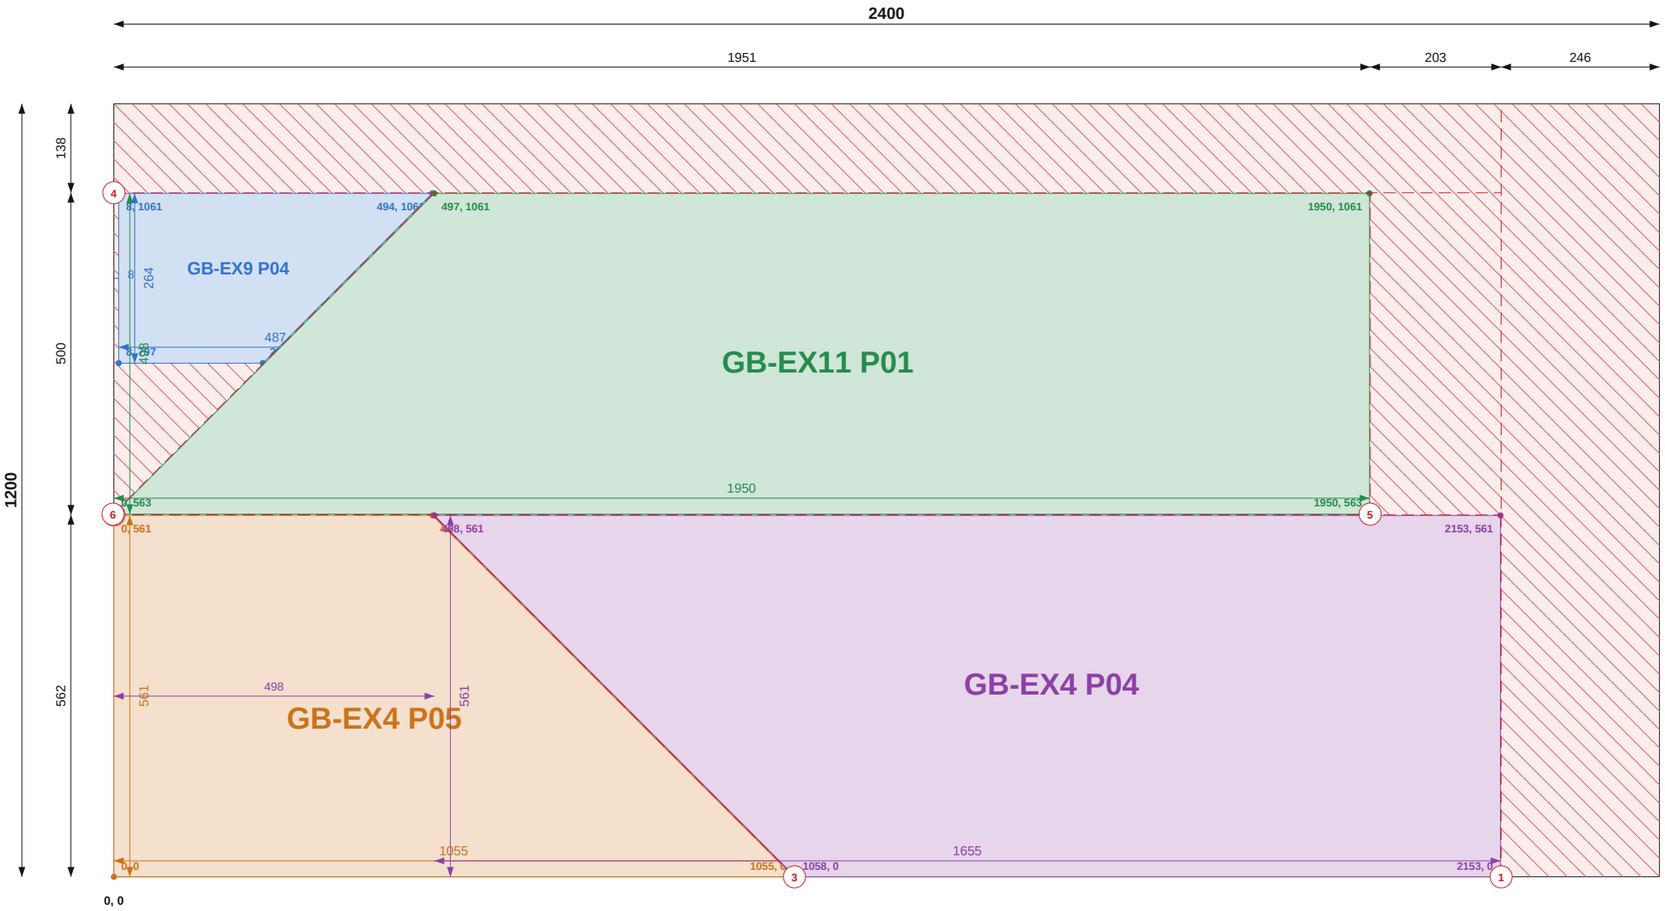

Top / left chains = saw cut positions (to cut centres). Coloured = part size and position.

SHEET 15 OF 18

THIS SHEET

Item	Value
Parts	4
Used / waste	74.6% / 0.73 m2
Reusable offcuts	0
Saw cuts / shared	6 / 3

PIECES (POSITION = BOTTOM-LEFT CORNER)

Label	Size	X, Y
GB-EX9 P04	264 x 487 rake to 225	8, 797
GB-EX11 P01	498 x 1950 rake to 1453	0, 563
GB-EX4 P05	561 x 1055 rake to 496	0, 0
GB-EX4 P04	561 x 1655 rake to 1096	498, 0

NOTES

1. Cut from PIR 120mm 1200x2400, 2mm saw kerf. Viewed on the face; dimensions from the sheet's bottom-left corner (0,0). Red numbered lines = saw cuts in order, each edge to edge.
2. Coloured dimensions belong to the part of that colour: its width and height, and its position from the sheet edges. Raked parts: corner coordinates at each corner.
3. Red hatch = waste. Labels = panel + piece mark on the manufacture drawing.

REVISIONS

REV	DATE	DESCRIPTION
C01	14.09.26	Construction issue
C02	14.09.26	Roof trusses revised; SP diagonals added
C03	11.10.26	FF windows coursed; steel + GP1 portal; steel drawings (ST)
C04	13.10.26	Steel approved by the engineer: steel + steel timber drawings issued for construction

TLS TIMBER FRAME
Design & Manufacture
Scan: 3D model + drawings

CLIENT	PROJECT
MP Adams	MP Adams Plot 4, Eckington

DRAWING TITLE


PIR CUTTING - GABLES - SHEET 15 OF 18

PIR 120mm 1200x2400 | Gables

SCALE	SIZE	DATE	DRAWN
NTS	A3	13.10.26	TS

STATUS	DRAWING No.	REV
CONSTRUCTION	P4-CP-PIR-03 / 15	C04

Do not scale. All dimensions in mm. Check all dimensions on site.

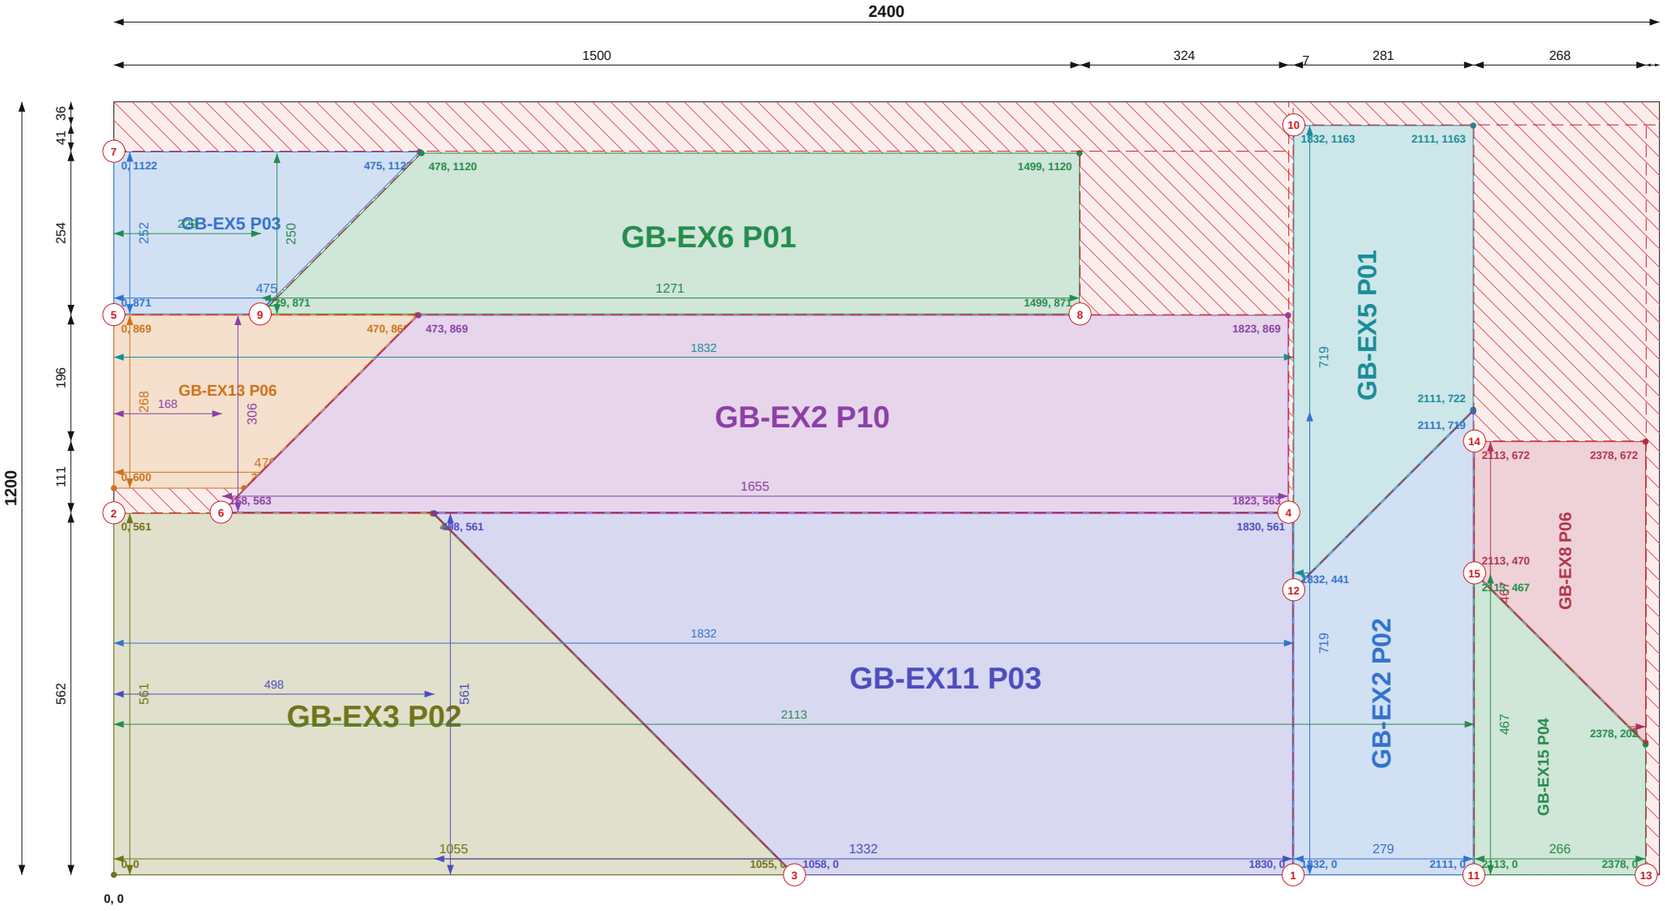

SHEET 16 OF 18

THIS SHEET

Item	Value
Parts	10
Used / waste	85.1% / 0.43 m2
Reusable offcuts	0
Saw cuts / shared	15 / 9

PIECES (POSITION = BOTTOM-LEFT CORNER)

Label	Size	X, Y
GB-EX5 P03	252 x 475 rake to 225	0, 871
GB-EX6 P01	250 x 1271 rake to 1023	229, 871
GB-EX13 P06	268 x 470 rake to 203	0, 600
GB-EX2 P10	306 x 1655 rake to 1351	168, 563
GB-EX5 P01	279 x 719 rake to 442	1832, 444
GB-EX8 P06	266 x 467 rake to 203	2113, 205
GB-EX3 P02	561 x 1055 rake to 496	0, 0
GB-EX11 P03	561 x 1332 rake to 773	498, 0
GB-EX2 P02	279 x 719 rake to 442	1832, 0
GB-EX15 P04	266 x 467 rake to 203	2113, 0

NOTES

1. Cut from PIR 120mm 1200x2400, 2mm saw kerf. Viewed on the face; dimensions from the sheet's bottom-left corner (0,0). Red numbered lines = saw cuts in order, each edge to edge.
2. Coloured dimensions belong to the part of that colour: its width and height, and its position from the sheet edges. Raked parts: corner coordinates at each corner.
3. Red hatch = waste. Labels = panel + piece mark on the manufacture drawing.

REVISIONS

REV	DATE	DESCRIPTION
C01	14.09.26	Construction issue
C02	14.09.26	Roof trusses revised; SP diagonals added
C03	11.10.26	FF windows coursed; steel + GP1 portal; steel drawings (ST)
C04	13.10.26	Steel approved by the engineer: steel + steel timber drawings issued for construction

TLS TIMBER FRAME
Design & Manufacture
Scan: 3D model + drawings

CLIENT	PROJECT
MP Adams	MP Adams Plot 4, Eckington


DRAWING TITLE
PIR CUTTING - GABLES - SHEET 16 OF 18

PIR 120mm 1200x2400 | Gables

SCALE	SIZE	DATE	DRAWN
NTS	A3	13.10.26	TS

STATUS	DRAWING No.	REV
CONSTRUCTION	P4-CP-PIR-03 / 16	C04

Do not scale. All dimensions in mm. Check all dimensions on site.

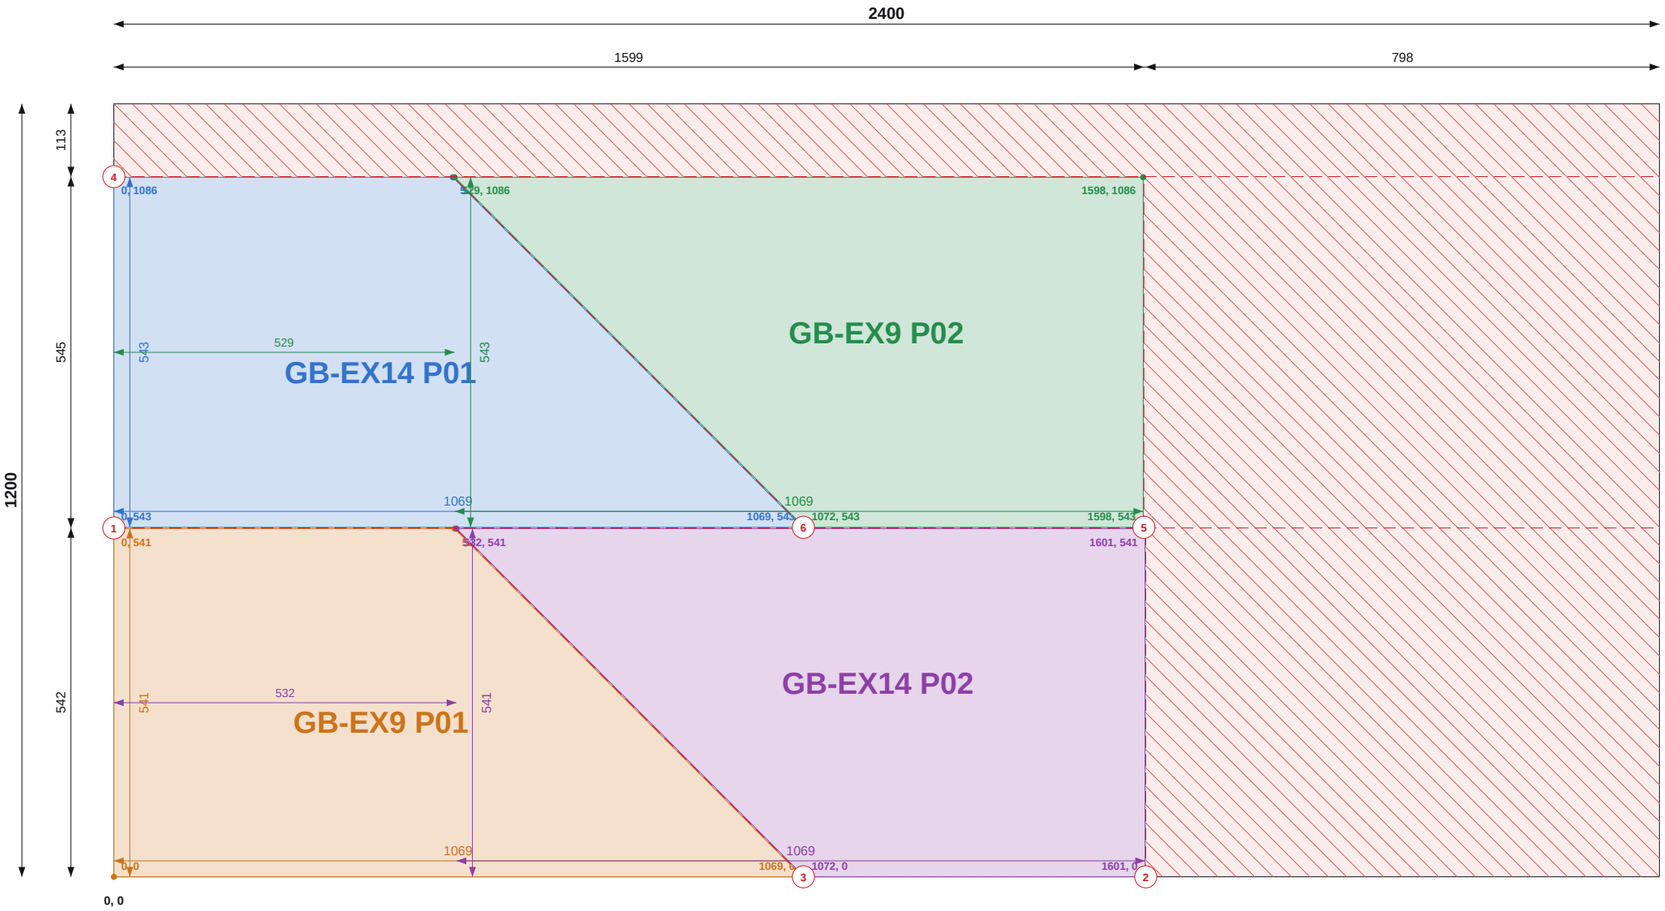

Top / left chains = saw cut positions (to cut centres). Coloured = part size and position.

Do not scale. All dimensions in mm. Check all dimensions on site.

SHEET 17 OF 18

THIS SHEET

Item	Value
Parts	4
Used / waste	60.1% / 1.15 m2
Reusable offcuts	2
Saw cuts / shared	6 / 3

PIECES (POSITION = BOTTOM-LEFT CORNER)

Label	Size	X, Y
GB-EX14 P01	543 x 1069 rake to 527	0, 543
GB-EX9 P02	543 x 1069 rake to 527	529, 543
GB-EX9 P01	541 x 1069 rake to 530	0, 0
GB-EX14 P02	541 x 1069 rake to 530	532, 0

NOTES

1. Cut from PIR 120mm 1200x2400, 2mm saw kerf. Viewed on the face; dimensions from the sheet's bottom-left corner (0,0). Red numbered lines = saw cuts in order, each edge to edge.
2. Coloured dimensions belong to the part of that colour: its width and height, and its position from the sheet edges. Raked parts: corner coordinates at each corner.
3. Red hatch = waste. Labels = panel + piece mark on the manufacture drawing.

REVISIONS

REV	DATE	DESCRIPTION
C01	14.09.26	Construction issue
C02	14.09.26	Roof trusses revised; SP diagonals added
C03	11.10.26	FF windows coursed; steel + GP1 portal; steel drawings (ST)
C04	13.10.26	Steel approved by the engineer: steel + steel timber drawings issued for construction

TLS TIMBER FRAME
Design & Manufacture
Scan: 3D model + drawings

CLIENT	PROJECT
MP Adams	MP Adams Plot 4, Eckington


DRAWING TITLE

PIR CUTTING - GABLES - SHEET 17 OF 18

PIR 120mm 1200x2400 | Gables

SCALE	SIZE	DATE	DRAWN
NTS	A3	13.10.26	TS

STATUS	DRAWING No.	REV
CONSTRUCTION	P4-CP-PIR-03 / 17	C04

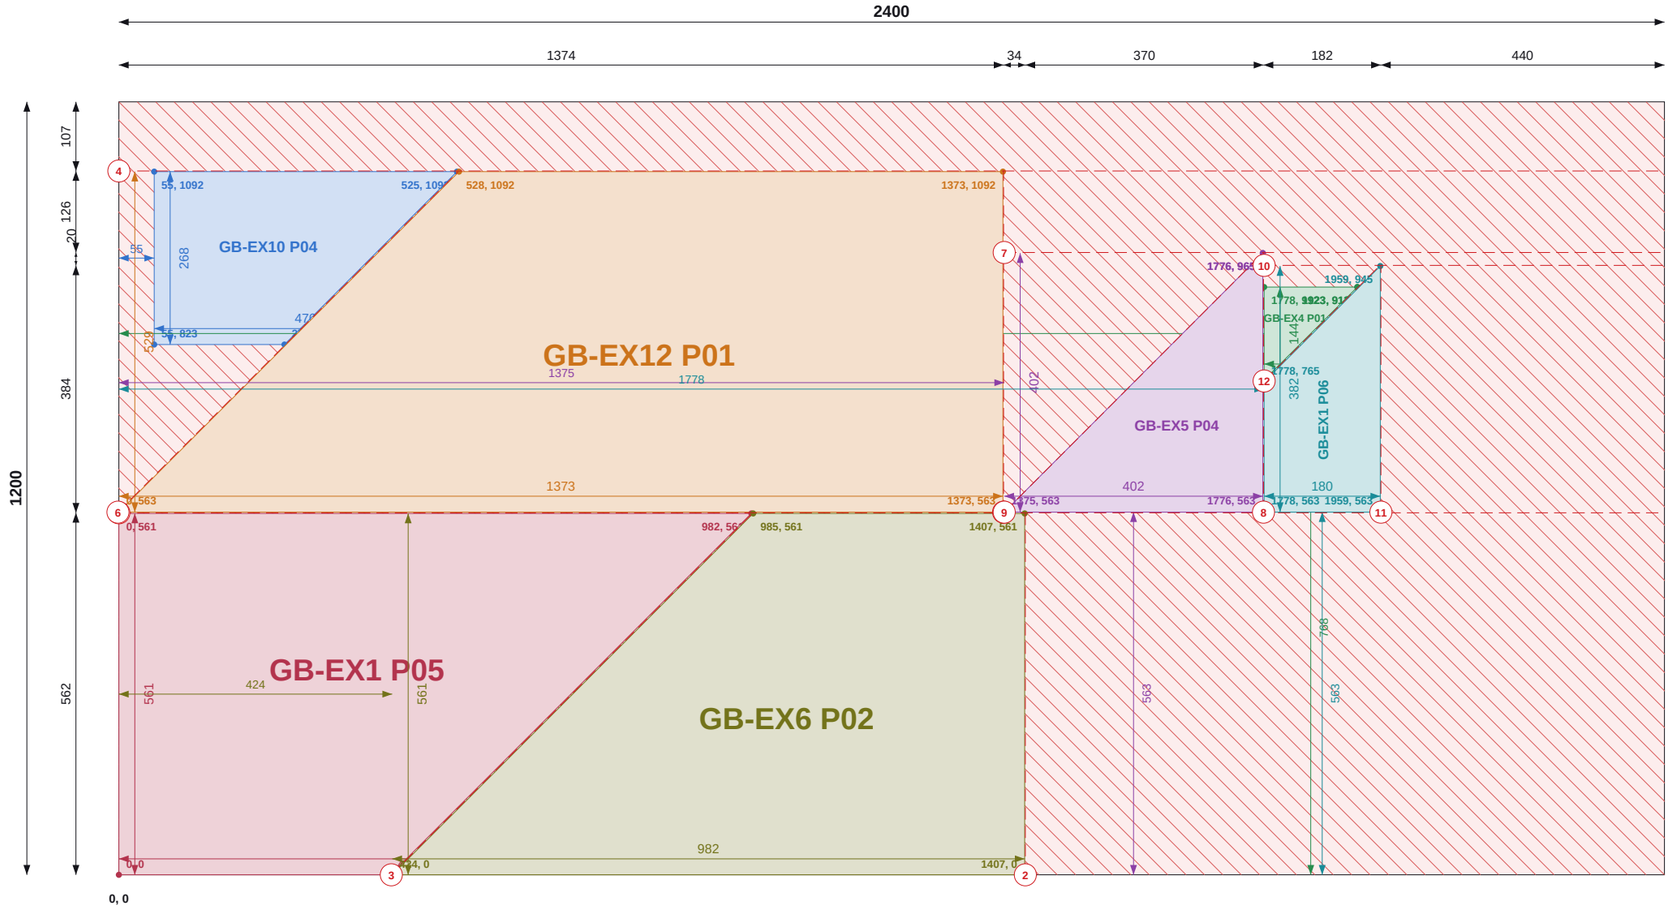

Top / left chains = saw cut positions (to cut centres). Coloured = part size and position.

Do not scale. All dimensions in mm. Check all dimensions on site.

SHEET 18 OF 18

THIS SHEET

Item	Value
Parts	7
Used / waste	55.8% / 1.27 m2
Reusable offcuts	2
Saw cuts / shared	12 / 7

PIECES (POSITION = BOTTOM-LEFT CORNER)

Label	Size	X, Y
GB-EX10 P04	268 x 470 rake to 203	55, 823
GB-EX4 P01	145 x 144 rake to 1	1778, 768
GB-EX12 P01	529 x 1373 rake to 846	0, 563
GB-EX5 P04	402 x 402 rake to 1	1375, 563
GB-EX1 P06	180 x 382 rake to 203	1778, 563
GB-EX1 P05	561 x 982 rake to 423	0, 0
GB-EX6 P02	561 x 982 rake to 423	424, 0

NOTES

1. Cut from PIR 120mm 1200x2400, 2mm saw kerf. Viewed on the face; dimensions from the sheet's bottom-left corner (0,0). Red numbered lines = saw cuts in order, each edge to edge.
2. Coloured dimensions belong to the part of that colour: its width and height, and its position from the sheet edges. Raked parts: corner coordinates at each corner.
3. Red hatch = waste. Labels = panel + piece mark on the manufacture drawing.

REVISIONS

REV	DATE	DESCRIPTION
C01	14.09.26	Construction issue
C02	14.09.26	Roof trusses revised; SP diagonals added
C03	11.10.26	FF windows coursed; steel + GP1 portal; steel drawings (ST)
C04	13.10.26	Steel approved by the engineer: steel + steel timber drawings issued for constructio

TLS TIMBER FRAME
Design & Manufacture
Scan: 3D model + drawings

CLIENT	PROJECT
MP Adams	MP Adams Plot 4, Eckington

DRAWING TITLE
PIR CUTTING - GABLES - SHEET 18 OF 18

PIR 120mm 1200x2400 | Gables

SCALE	SIZE	DATE	DRAWN
NTS	A3	13.10.26	TS

STATUS	DRAWING No.	REV
CONSTRUCTION	P4-CP-PIR-03 / 18	C04