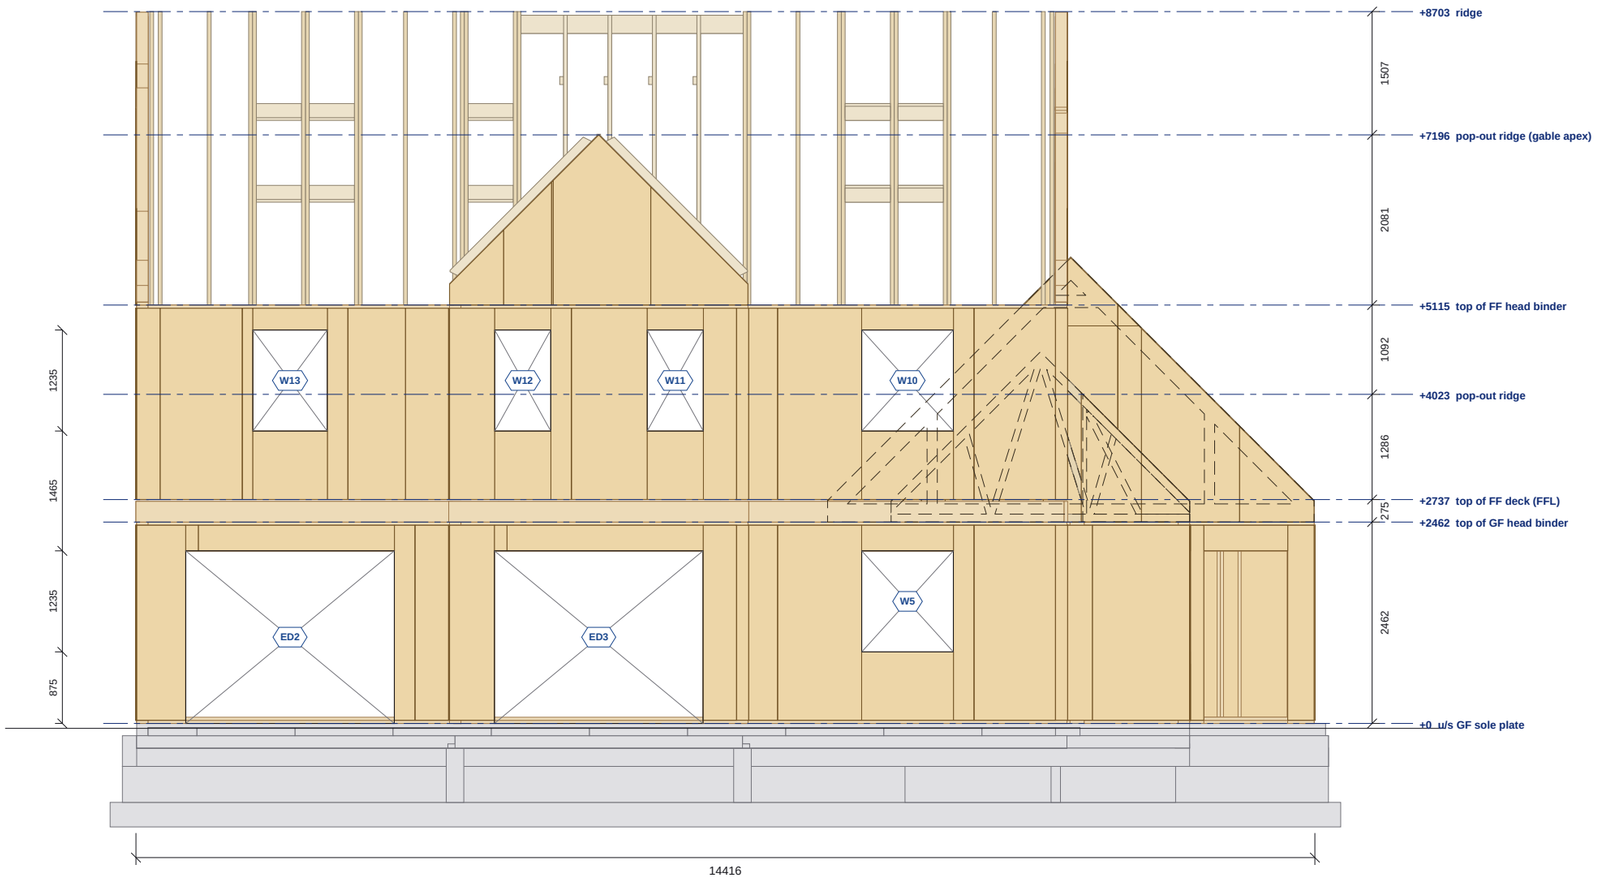



## REAR ELEVATION (NORTH)

Scale 1:75 @ A3 | Levels right: storey levels + visible ridges; left: sills and heads on this face

0 1 2 3 4 5m

Do not scale. All dimensions in mm. Check all dimensions on site.

## REAR ELEVATION (NORTH) SCHEDULE

### LEVELS ON THIS FACE

| Level | mm |
|---|---|
| u/s GF sole plate | +0 |
| top of GF head binder | +2462 |
| top of FF deck (FFL) | +2737 |
| pop-out ridge | +4023 |
| top of FF head binder | +5115 |
| pop-out ridge (gable apex) | +7196 |
| ridge | +8703 |

Above underside of the ground floor sole plate.

### OPENINGS ON THIS FACE

| Label | Level | Width | Height | Sill | Head |
|---|---|---|---|---|---|
| ED2 | GF | 2550 | 2110 | 0 | 2110 |
| ED3 | GF | 2550 | 2110 | 0 | 2110 |
| W5 | GF | 1120 | 1235 | 875 | 2110 |
| W10 | FF | 1120 | 1235 | 3575 | 4810 |
| W11 | FF | 685 | 1235 | 3575 | 4810 |
| W12 | FF | 685 | 1235 | 3575 | 4810 |
| W13 | FF | 910 | 1235 | 3575 | 4810 |

Sill and head levels above underside of the GF sole plate.

### NOTES

1. Construction elevation of the timber frame: OSB/3 face of external and gable panels, sole plates, head binders and edgebinders. Cladding, roof covering and windows by others, not shown.
2. Level lines shown are only those relevant to this face: storey levels, visible ridges and the sill / head levels of the openings on this face.
3. Roof trusses: edge-on trusses drawn at their centres; trusses behind gable / wall panels shown dashed (hidden detail, nearest truss of each type).
4. Levels above the underside of the ground floor sole plate (+0). Openings are structural openings; see P4-GA-01 / P4-GA-02 / P4-GA-03.

### REVISIONS

| REV | DATE | DESCRIPTION |
|---|---|---|
| C01 | 14.09.26 | Construction issue |
| C02 | 14.09.26 | Roof trusses revised; SP diagonals added |
| C03 | 11.10.26 | FF windows coursed; steel + GP1 portal; steel drawings (ST) |
| C04 | 13.10.26 | Steel approved by the engineer: steel + steel timber drawings issued for construction |

TLS TIMBER FRAME
Design & Manufacture
Scan: 3D model + drawings

| CLIENT | PROJECT |
|---|---|
| MP Adams | MP Adams Plot 4, Eckington |

DRAWING TITLE
**REAR ELEVATION (NORTH)**
Timber frame construction elevation

| SCALE | SIZE | DATE | DRAWN |
|---|---|---|---|
| 1:75 | A3 | 13.10.26 | TS |

| STATUS | DRAWING No. | REV |
|---|---|---|
| CONSTRUCTION | P4-EL-03 | C04 |