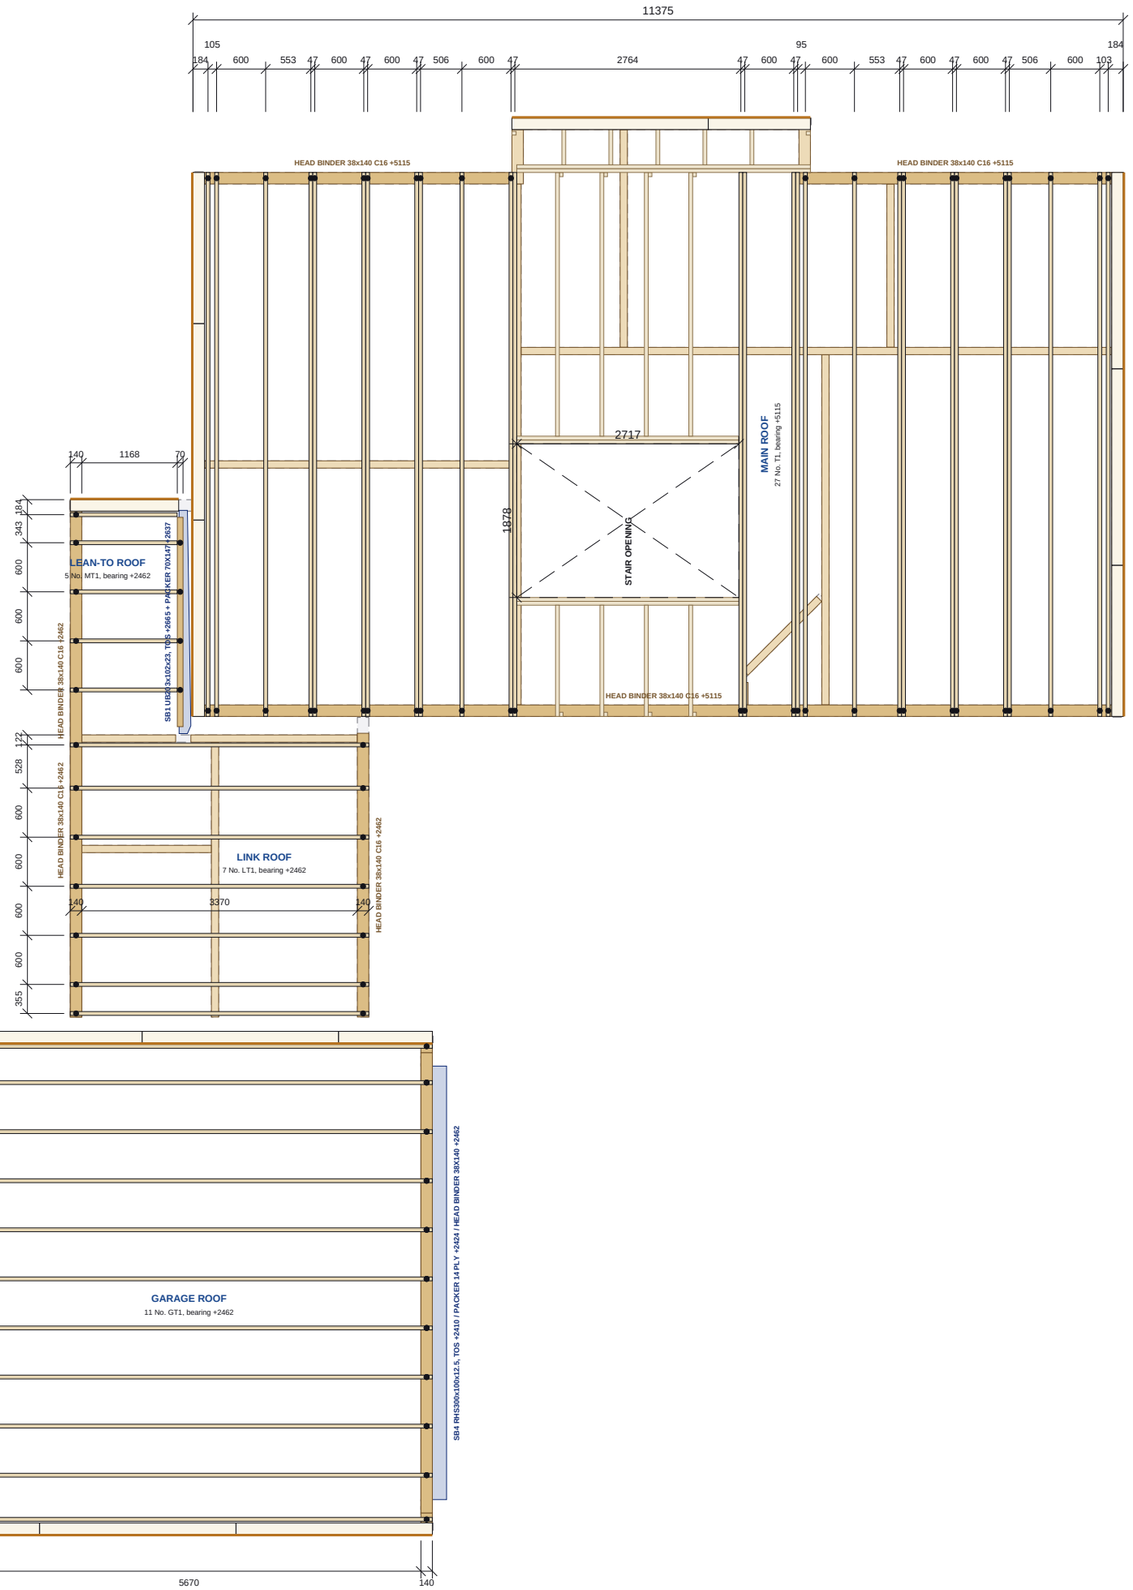


ROOF - CEILING LEVEL PLAN

Scale 1:75 @ A3 | Plan at +5415; first floor walls below grey dashed

Do not scale. All dimensions in mm. Check all dimensions on site.

CEILING LEVEL SCHEDULE

TRUSSES

Type	No.	Span	Height	Doubles
GT1	11	5950	3238	0
LT1	7	3650	2080	0
MT1	5	1306	1562	0
T1	27	6650	3588	9

Span over external frame faces; height from underside of bottom chord.

TRUSS BEARINGS

Roof	Bearing	Top	Runs
Main	HEAD BINDER 38x140 C16	+5115	3
Garage	SB4 RHS300x100x12.5 S355J2H	+2410	1
Garage	SB4 head binder 38x140 C16	+2462	1
Garage	SB4 packer 14mm marine ply 140	+2424	1
Garage	HEAD BINDER 38x140 C16	+2462	3
Link	HEAD BINDER 38x140 C16	+2462	2
Lean-to	SB1 UB203x102x23 S355JR	+2665	1
Lean-to	SB1 packer 70x147 C24	+2637	1
Lean-to	HEAD BINDER 38x140 C16	+2462	1

Top of bearing above slab; runs = separate lengths on plan. Dots on plan mark each truss bearing.

CEILING-LEVEL ROOF MEMBERS

Item	No.
Cut roof members bearing at ceiling level	29

Pop-out valley and junction framing, indicative.

NOTES

1. Lower roofs (garage roof, link roof and lean-to roof): trusses bear at +2462 above slab on the ground floor head binders and the steel / packers shown solid, set out as dimensioned; dots mark each truss bearing.
2. Ceiling level: attic truss bottom chords bear on the first floor head binder at +5115 above slab.
3. Truss bottom chords form the attic floor zone; double trusses trim the stair void and the pop-out junction.
4. Cut roof members at the pop-out valley shown at their low (ceiling-level) ends; see P4-RF-02.
5. Truss and roof member positions indicative; read with the truss manufacturer's layout and engineer's drawing 26-431-S-0010.

REVISIONS

REV	DATE	DESCRIPTION
C01	14.09.26	Construction issue
C02	14.09.26	Roof trusses revised; SP diagonals added
C03	11.10.26	FF windows coursed; steel + GP1 portal; steel drawings (ST)
C04	13.10.26	Steel approved by the engineer: steel + steel timber drawings issued for construction

TLS TIMBER FRAME DESIGN SUITE

TLS TIMBER FRAME

Design & Manufacture

Scan: 3D model + drawings

CLIENT	PROJECT
MP Adams	MP Adams Plot 4, Eckington

DRAWING TITLE

ROOF - CEILING LEVEL

Attic truss bottom chords and ceiling-level roof members

SCALE	SIZE	DATE	DRAWN
1:75	A3	13.10.26	TS

STATUS	DRAWING No.	REV
CONSTRUCTION	P4-RF-01	C04