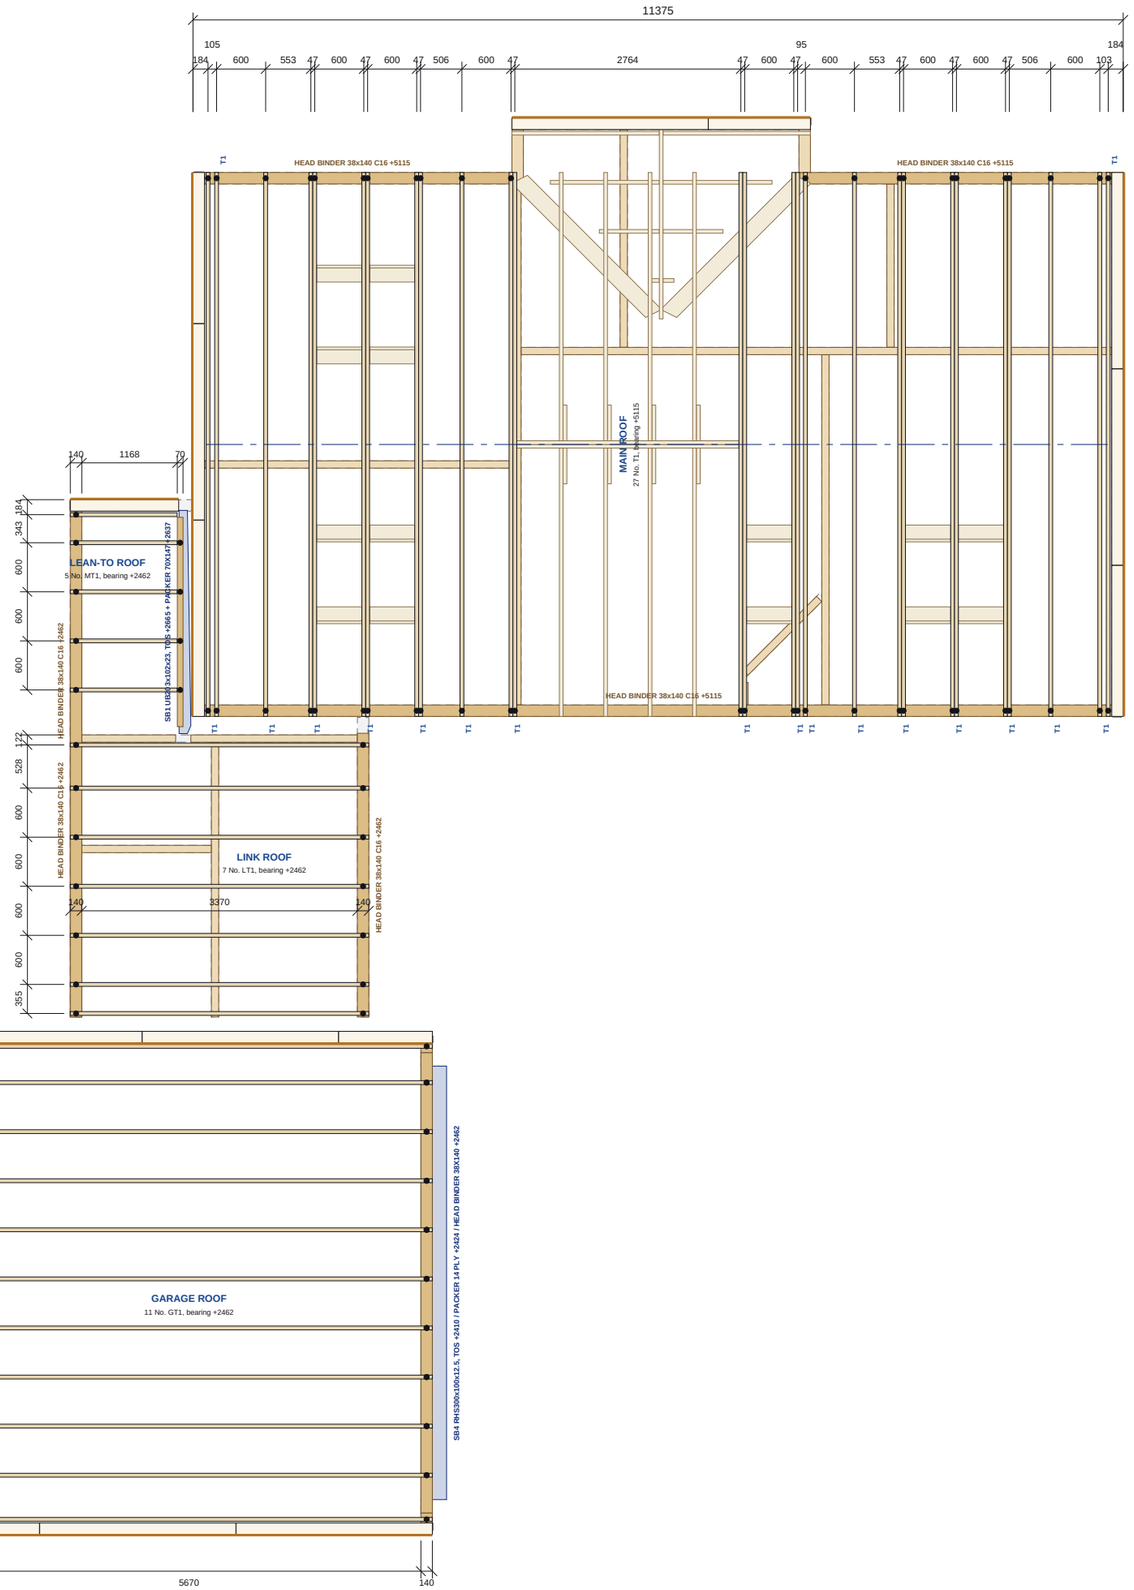


ROOF - TRUSS LAYOUT PLAN

Scale 1:75 @ A3 | Ridge lines blue dash-dot; first floor walls below grey dashed

Do not scale. All dimensions in mm. Check all dimensions on site.

ROOF SCHEDULE

TRUSSES

Type	No.	Span	Height	Doubles
GT1	11	5950	3238	0
LT1	7	3650	2080	0
MT1	5	1306	1562	0
T1	27	6650	3588	9

Span over external frame faces; height from underside of bottom chord.

TRUSS BEARINGS

Roof	Bearing	Top	Runs
Main	HEAD BINDER 38x140 C16	+5115	3
Garage	SB4 RHS300x100x12.5 S355J2H	+2410	1
Garage	SB4 head binder 38x140 C16	+2462	1
Garage	SB4 packer 14mm marine ply 140	+2424	1
Garage	HEAD BINDER 38x140 C16	+2462	3
Link	HEAD BINDER 38x140 C16	+2462	2
Lean-to	SB1 UB203x102x23 S355JR	+2665	1
Lean-to	SB1 packer 70x147 C24	+2637	1
Lean-to	HEAD BINDER 38x140 C16	+2462	1

Top of bearing above slab; runs = separate lengths on plan. Dots on plan mark each truss bearing.

CUT ROOF MEMBERS

Item	No.
Valley / rafter / ridge / purlin members (above ceiling)	53

Indicative, at the pop-out junction.

NOTES

1. Attic trusses T1 (main roof) and GT1 (garage roof); trussed rafters LT1 (link roof) and MT1 (lean-to roof) at the centres dimensioned; doubles where shown.
2. Lower roofs (garage roof, link roof and lean-to roof): trusses bear at +2462 above slab on the ground floor head binders and the steel / packers shown solid, set out as dimensioned; dots mark each truss bearing.
3. Cut roof members (valley, rafters, ridge and purlins) at the pop-out junction shown indicatively.
4. Gable panels see P4-GA-03. Truss and roof member positions indicative; read with the truss manufacturer's layout and engineer's drawing 26-431-S-0010.

REVISIONS

REV	DATE	DESCRIPTION
C01	14.09.26	Construction issue
C02	14.09.26	Roof trusses revised; SP diagonals added
C03	11.10.26	FF windows coursed; steel + GP1 portal; steel drawings (ST)
C04	13.10.26	Steel approved by the engineer: steel + steel timber drawings issued for construction

TLS TIMBER FRAME DESIGN SUITE

TLS TIMBER FRAME

Design & Manufacture

Scan: 3D model + drawings

CLIENT	PROJECT
MP Adams	MP Adams Plot 4, Eckington

DRAWING TITLE

ROOF - TRUSS LAYOUT

Attic trusses, cut roof members and set-out

SCALE	SIZE	DATE	DRAWN
1:75	A3	13.10.26	TS

STATUS	DRAWING No.	REV
CONSTRUCTION	P4-RF-02	C04