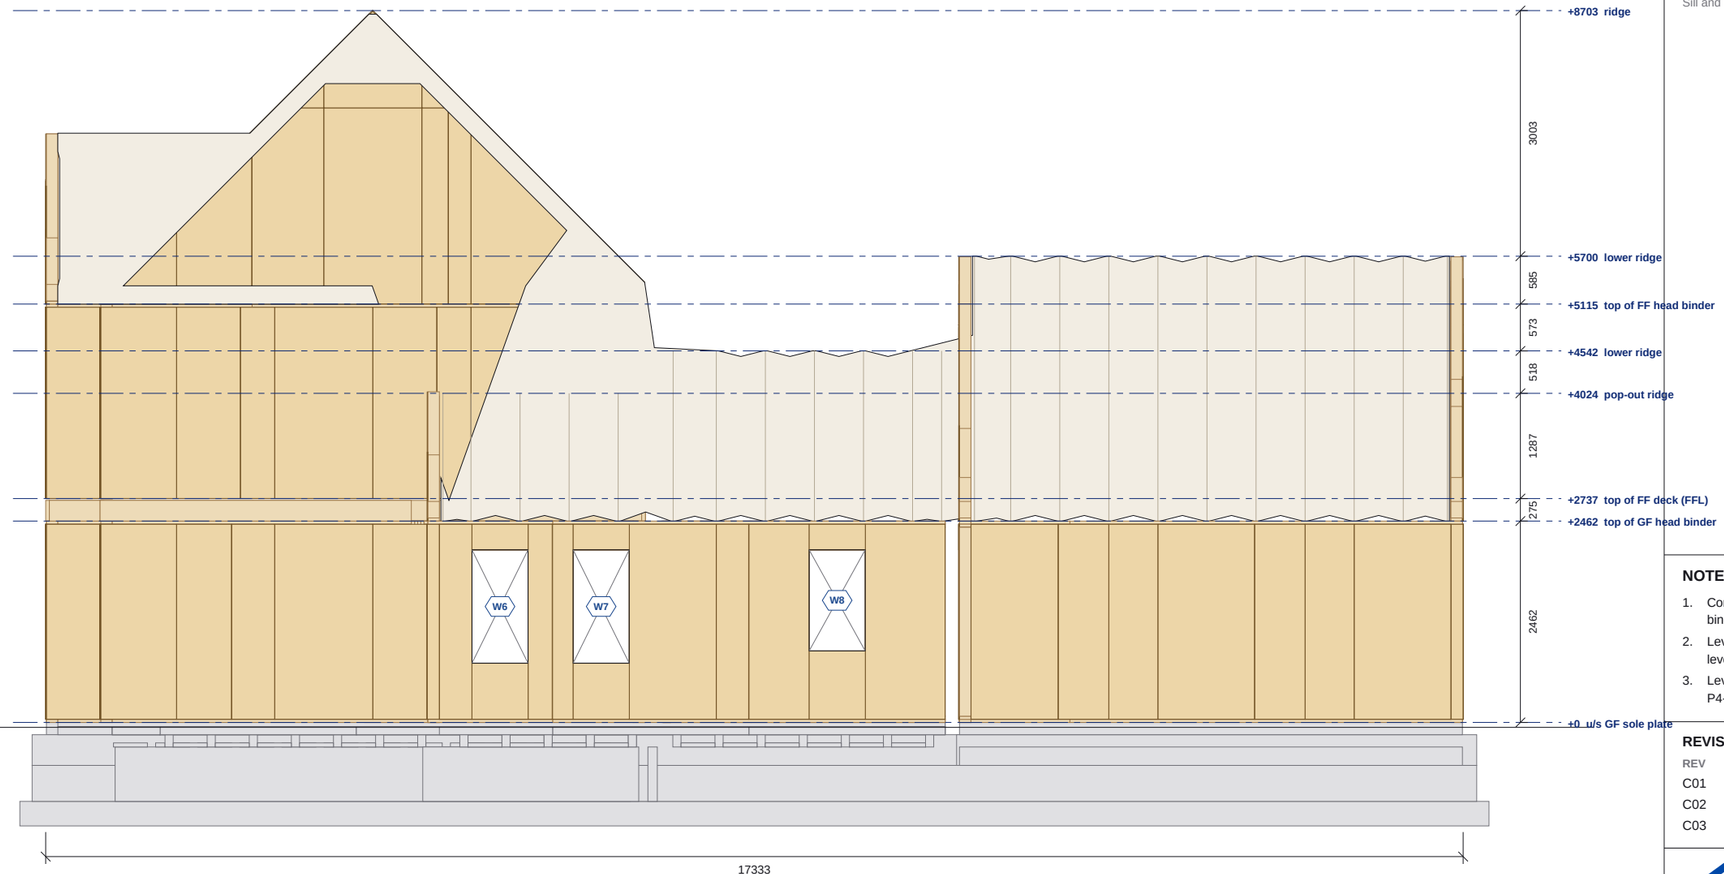


SIDE ELEVATION (WEST)

Scale 1:75 @ A3 | Levels right: storey levels + visible ridges; left: sills and heads on this face

0 1 2 3 4 5m

Do not scale. All dimensions in mm. Check all dimensions on site.

SIDE ELEVATION (WEST) SCHEDULE

LEVELS ON THIS FACE

Level	mm
u/s GF sole plate	+0
top of GF head binder	+2462
top of FF deck (FFL)	+2737
pop-out ridge	+4024
lower ridge	+4542
top of FF head binder	+5115
lower ridge	+5700
ridge	+8703

Above underside of the ground floor sole plate.

OPENINGS ON THIS FACE

Label	Level	Width	Height	Sill	Head
W6	GF	685	1385	725	2110
W7	GF	685	1385	725	2110
W8	GF	685	1235	875	2110

Sill and head levels above underside of the GF sole plate.

NOTES

1. Construction elevation of the timber frame: OSB/3 face of external and gable panels, sole plates, head binders and edgebinders. Cladding, roof covering and windows by others, not shown.
2. Level lines shown are only those relevant to this face: storey levels, visible ridges and the sill / head levels of the openings on this face.
3. Levels above the underside of the ground floor sole plate (+0). Openings are structural openings; see P4-GA-01 / P4-GA-02 / P4-GA-03.

REVISIONS

REV	DATE	DESCRIPTION
C01	14.09.26	Construction issue
C02	14.09.26	Roof trusses revised; SP diagonals added
C03	11.10.26	FF windows coursed; steel + GP1 portal; steel drawings (ST)

TLS TIMBER FRAME
Design & Manufacture
Scan: 3D model + drawings

CLIENT	PROJECT
MP Adams	MP Adams Plot 4, Eckington

DRAWING TITLE
SIDE ELEVATION (WEST)
Timber frame construction elevation

SCALE	SIZE	DATE	DRAWN
1:75	A3	11.10.26	TS

STATUS	DRAWING No.	REV
CONSTRUCTION	P4-EL-04	C03