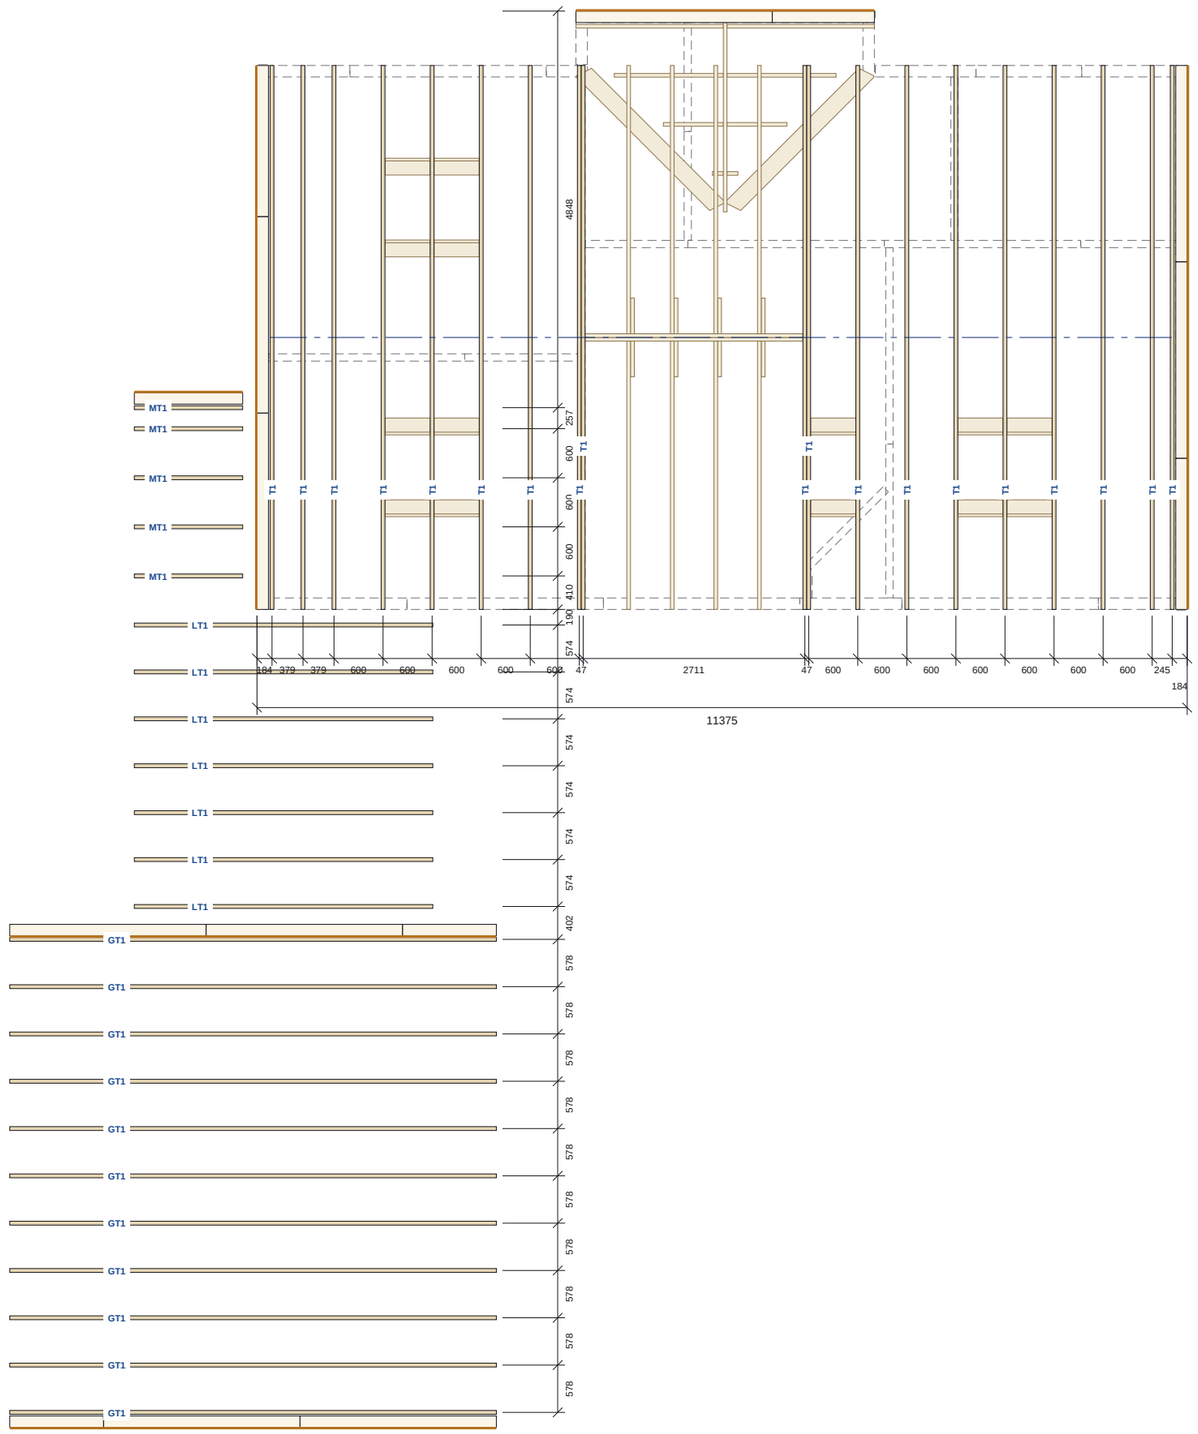


ROOF - TRUSS LAYOUT PLAN

Scale 1:75 @ A3 | Ridge lines blue dash-dot; first floor walls below grey dashed

0 1 2 3 4 5m

Do not scale. All dimensions in mm. Check all dimensions on site.

ROOF SCHEDULE

ATTIC TRUSSES

Type	No.	Span	Height	Doubles
GT1	11	5950	3230	0
LT1	7	3650	2080	0
MT1	5	1325	1580	0
T1	19	6650	3588	2

Span over external frame faces; height from underside of bottom chord.

CUT ROOF MEMBERS

Item	No.
Valley / rafter / ridge / purlin members (above ceiling)	53

Indicative, at the pop-out junction.

NOTES

1. Attic trusses T1 (main roof) and T2 (pop-out roof) at the centres dimensioned; doubles where shown.
2. Cut roof members (valley, rafters, ridge and purlins) at the pop-out junction shown indicatively.
3. Gable panels see P4-GA-03. Truss and roof member positions indicative; read with the truss manufacturer's layout and engineer's drawing 26-431-S-0010.

REVISIONS

REV	DATE	DESCRIPTION
C01	14.09.26	Construction issue

TLS TIMBER FRAME
Design & Manufacture
Scan: 3D model + drawings

CLIENT	PROJECT
MP Adams	MP Adams Plot 4, Eckington

DRAWING TITLE

ROOF - TRUSS LAYOUT

Attic trusses, cut roof members and set-out

SCALE	SIZE	DATE	DRAWN
1:75	A3	14.09.26	TS

STATUS	DRAWING No.	REV
CONSTRUCTION	P4-RF-02	C01